РАБОЧАЯ ДОКУМЕНТАЦИЯ

Архитектурные решения
(раздел АР)

Москва , 2026 год

Пояснительная записка

Общие данные:

1. Эскизный проект одноэтажной бани выполнен индивидуально
на основании исходных данных, представленных заказчиком.
2. Состав пирогов конструкций предусматривает его круглогодичную эксплуатацию.
3. Размеры строения 7х14,1 м
За относительную отметку ±0.000 уровень чистого пола теплых помещений.

Адрес строительства: Московская область

---

1. Рабочие чертежи разработаны на основании задания на проетирования (КР).

2. Объект строительства расположен в следующих климатических условиях:
- Нормативный вес снегового покрова для III района – Sg=1,5 кН/м2;
- Нормативное ветровое давление для I района – 23 кгс/м^2;
- Расчетная зимняя температура наружнего воздуха – минус 26 ^{0}С;
- Нормативная глубина промерзания – 1,4 м;
- Полезная нагрузка на покрытие – 150 кгс/м^2.

3. Общая характеристика:
- Уровень ответственности – нормальный.
- Класс сооружения – КС-2
- Класс функциональной пожарной опасности здания – Ф 1.4.
- Степень огнестойкости – III.
- Класс пожарной опасности строительных конструкций –К3.
- Зона влажности – нормальный.
- Расчетная температура наружного воздуха наиболее холодной пятидневки: -29°С.

4. Конструктивно строение представляет собой сооружение с плитным фундаментом, несущими стенами из газобетонного блока , кровлей по деревянным стропилам.

5. При проведении строительных работ необходимо осуществлять
технический надзор с ведением журнала работ. Осуществлять входной контроль материалов,
вести приемку по каждому этапу работ.

6. Описание конструкций строения:
- Фундамент – монолитная ж/б плита
- Несущие конструкции – Газобетонный блок 300мм, D500
- Стропильная система – из сеÎjq строганной доски сечением 45х190(h)мм сдвоенные доски
- Крыша – Вальмовая многоскатная;
- Кровля – Мягкая черепица.

7. Все деревянные конструкции обработать огне-биозащитными септиками в соответствии с СП 64.13330.2017

8. Кровельные работы выполнять в соответствии с требованиями фирмы производителя.

9. Все работы вести в строгом соответствии с требованиями СП 49.13330.2012 (Безопасность труда в строительстве).

10 При выполнении всех работ строго соблюдать меры противопожарной безопасности.

11. Возможна замена материалов аналогами.

*Решения, принятые в проекте и отображенные в чертежах, соответствуют требованиям экологических, санитарно -гигиенических, противопожарных и других норм, действующих на
территории Российской Федерации, и обеспечивают безопасную для жизни и здоровья людей эксплуатацию объекта при соблюдении предусмотренных рабочих чертежей и мероприятий.

						248_25		АР
						Московская область, КП Прибрежный, Летная 12		
Изм.	Колуч.	Лист	№Док.	Подп.	Дата			
						Индивидуальное строение_Баня	Стадия	Лист	Листов
ГАП		Алиев					Р	1	
Архитектор		Савельева							
						Пояснительная записка			

Согласовано

Взам. инв. №

Подп. и дата

Инв. № подл.

Ведомость чертежей

Лист	Наименование	Примечание
	Титульный лист	
1	Пояснительная записка	
2	Ведомость чертежей	
3	Эскизный план	
4	Аксонометрии плана	
5	Маркировочный план	
6	Размерный план	
7	План покрытий пола	
8	Сечения покрытий пола	
9	Сечения стен (лист 1)	
10	Сечения стен (лист 2)	
11	План электрооборудования	
12	План кровли	
13	Аксонометрия кровли	
14	Ведомость оконных проёмов	
15	Ведомость дверных проемов	
16	Разрез 1-1	
17	Разрез 2-2	
18	Аксонометрия разреза	
19	Цветовое решение; Фасад в осях Д-А	
20	Цветовое решение; Фасад в осях 5-1	
21	Цветовое решение; Фасад в осях А-Д	
22	Цветовое решение; Фасад в осях 1-5	
23	Визуализация №1	
24	Визуализация №2	
25	Визуализация №3	

Согласовано

Взам. инв. №

Подп. и дата

Инв. № подл.

Изм.	Колуч.	Лист	№Док.	Подп.	Дата				
						Индивидуальное строение_Баня	Стадия	Лист	Листов
						Ведомость чертежей			

Эскизный план

1:50

Экспликация помещений

№	Наименование	Площадь, кв. м.
1	Беседка	22,98
2	Комната отдыха	26,04
3	Прихожая	4,68
4	Душевая	6,21
5	Сауна	7,73
6	С/у	4,25
		71,89 м²

Наименование	Площадь, кв. м.
Площадь застройки	94,23

Изм.	Колич.	Лист	№Док.	Подп.	Дата			
						Индивидуальное строение_Баня	Стадия	Лист	Листов
						Эскизный план			

Согласовано

Взам. инв. №

Подп. и дата

Инв. № подл.

Аксонометрии плана

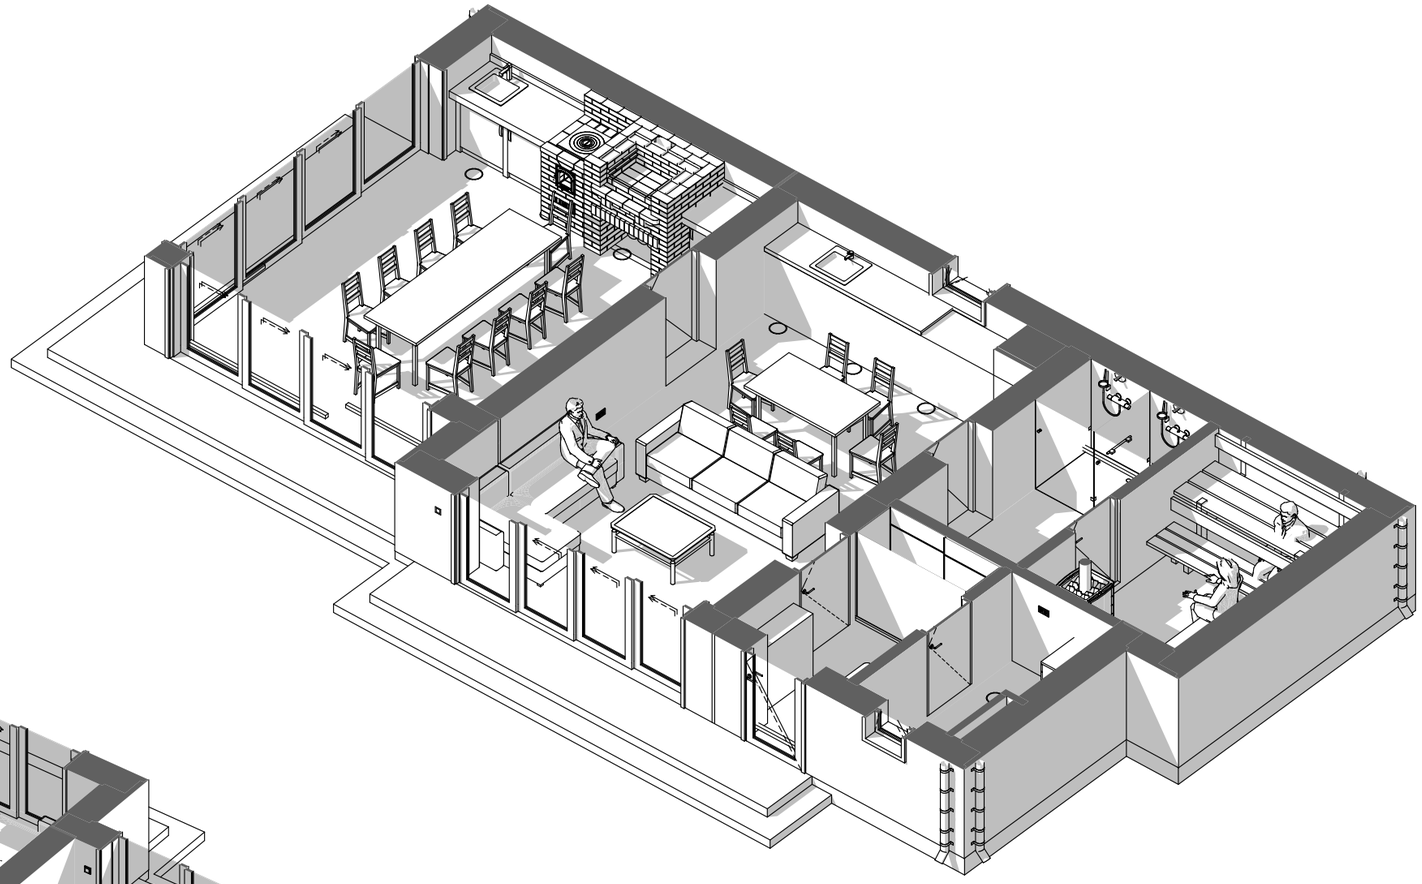

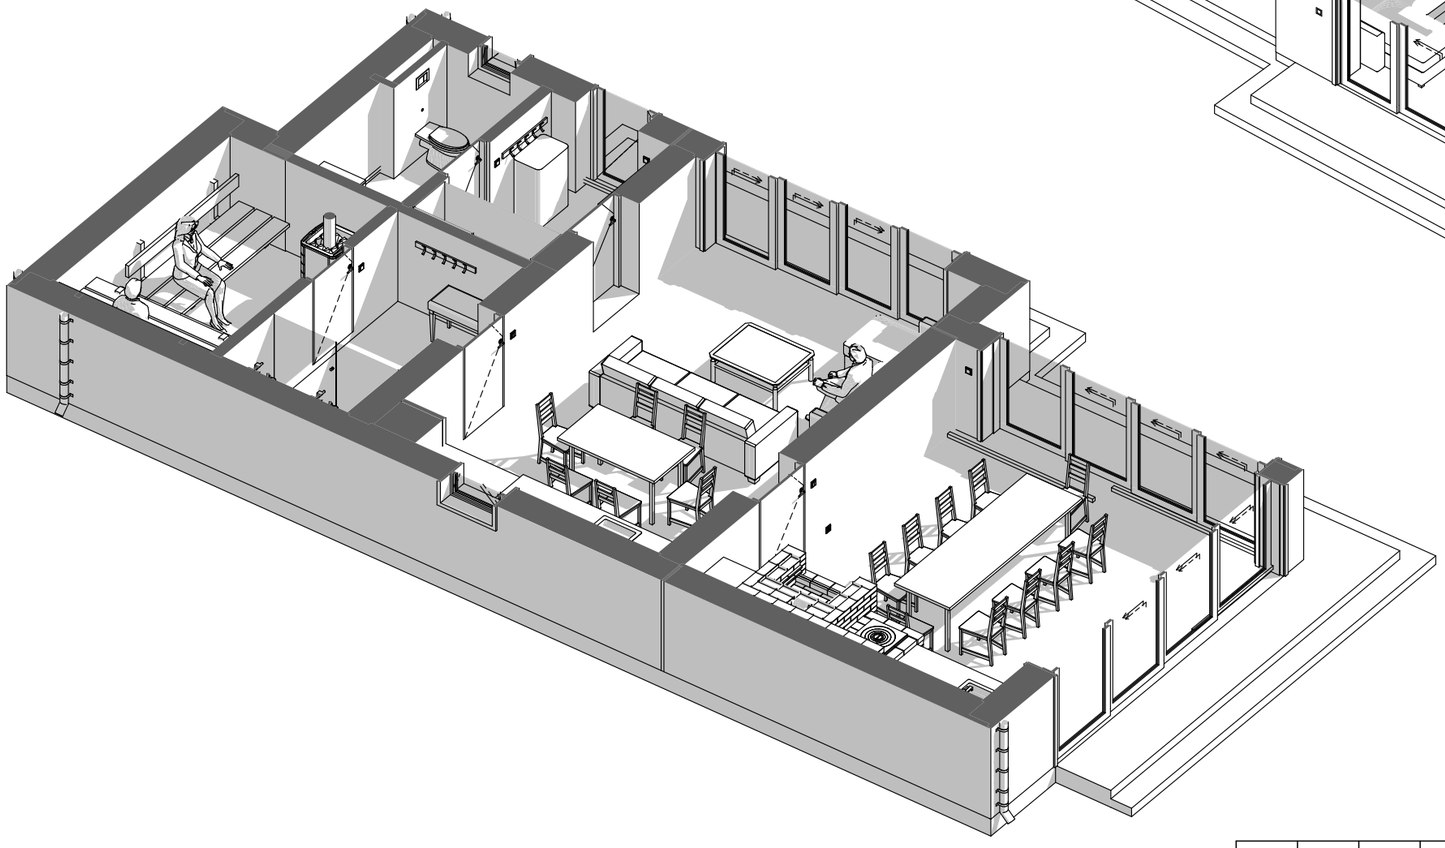

Изм.	Колуч.	Лист	№Док.	Подп.	Дата				
						Индивидуальное строение_Баня	Стадия	Лист	Листов
						Аксонометрии плана			

Согласовано

Взам. инв. №

Подп. и дата

Инв. № подл.

Маркировочный план 1:50

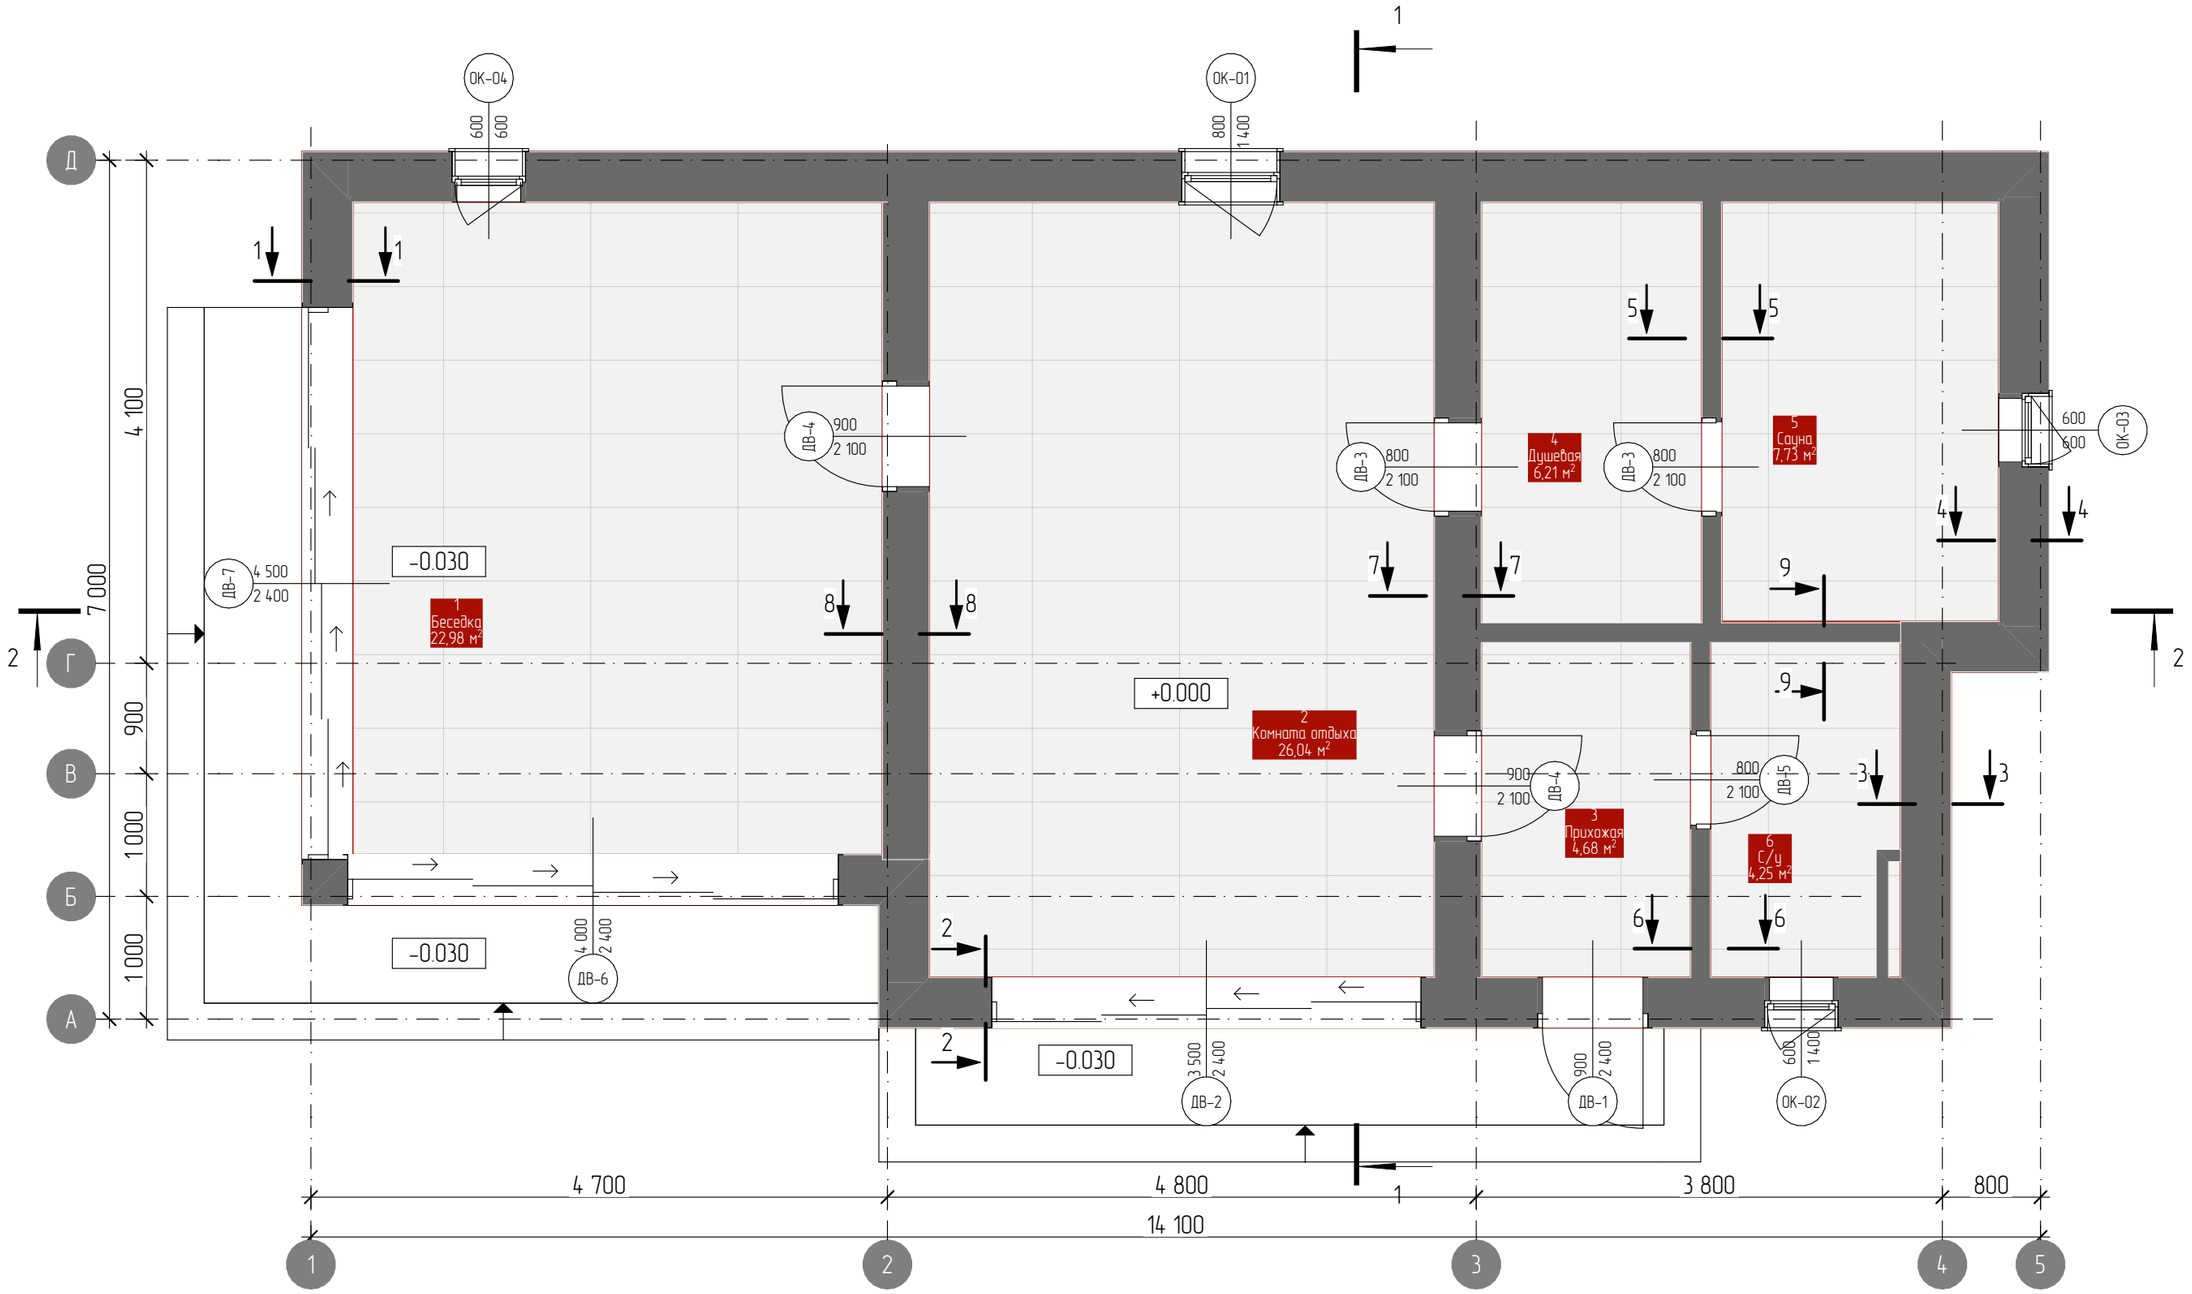

Примечание:

1. Ведомость оконных проемов см. лист 14
2. Ведомость дверных проемов см. лист 15
3. Сечения стен см листы 9,10
4. План покрытия пола см лист 7

Изм.	Колуч.	Лист	№Док.	Подп.	Дата

Индивидуальное строение_Баня	Стадия	Лист	Листов
Маркировочный план			

Согласовано

Взам. инв. №

Подп. и дата

Инв. № подл.

Размерный план 1:50

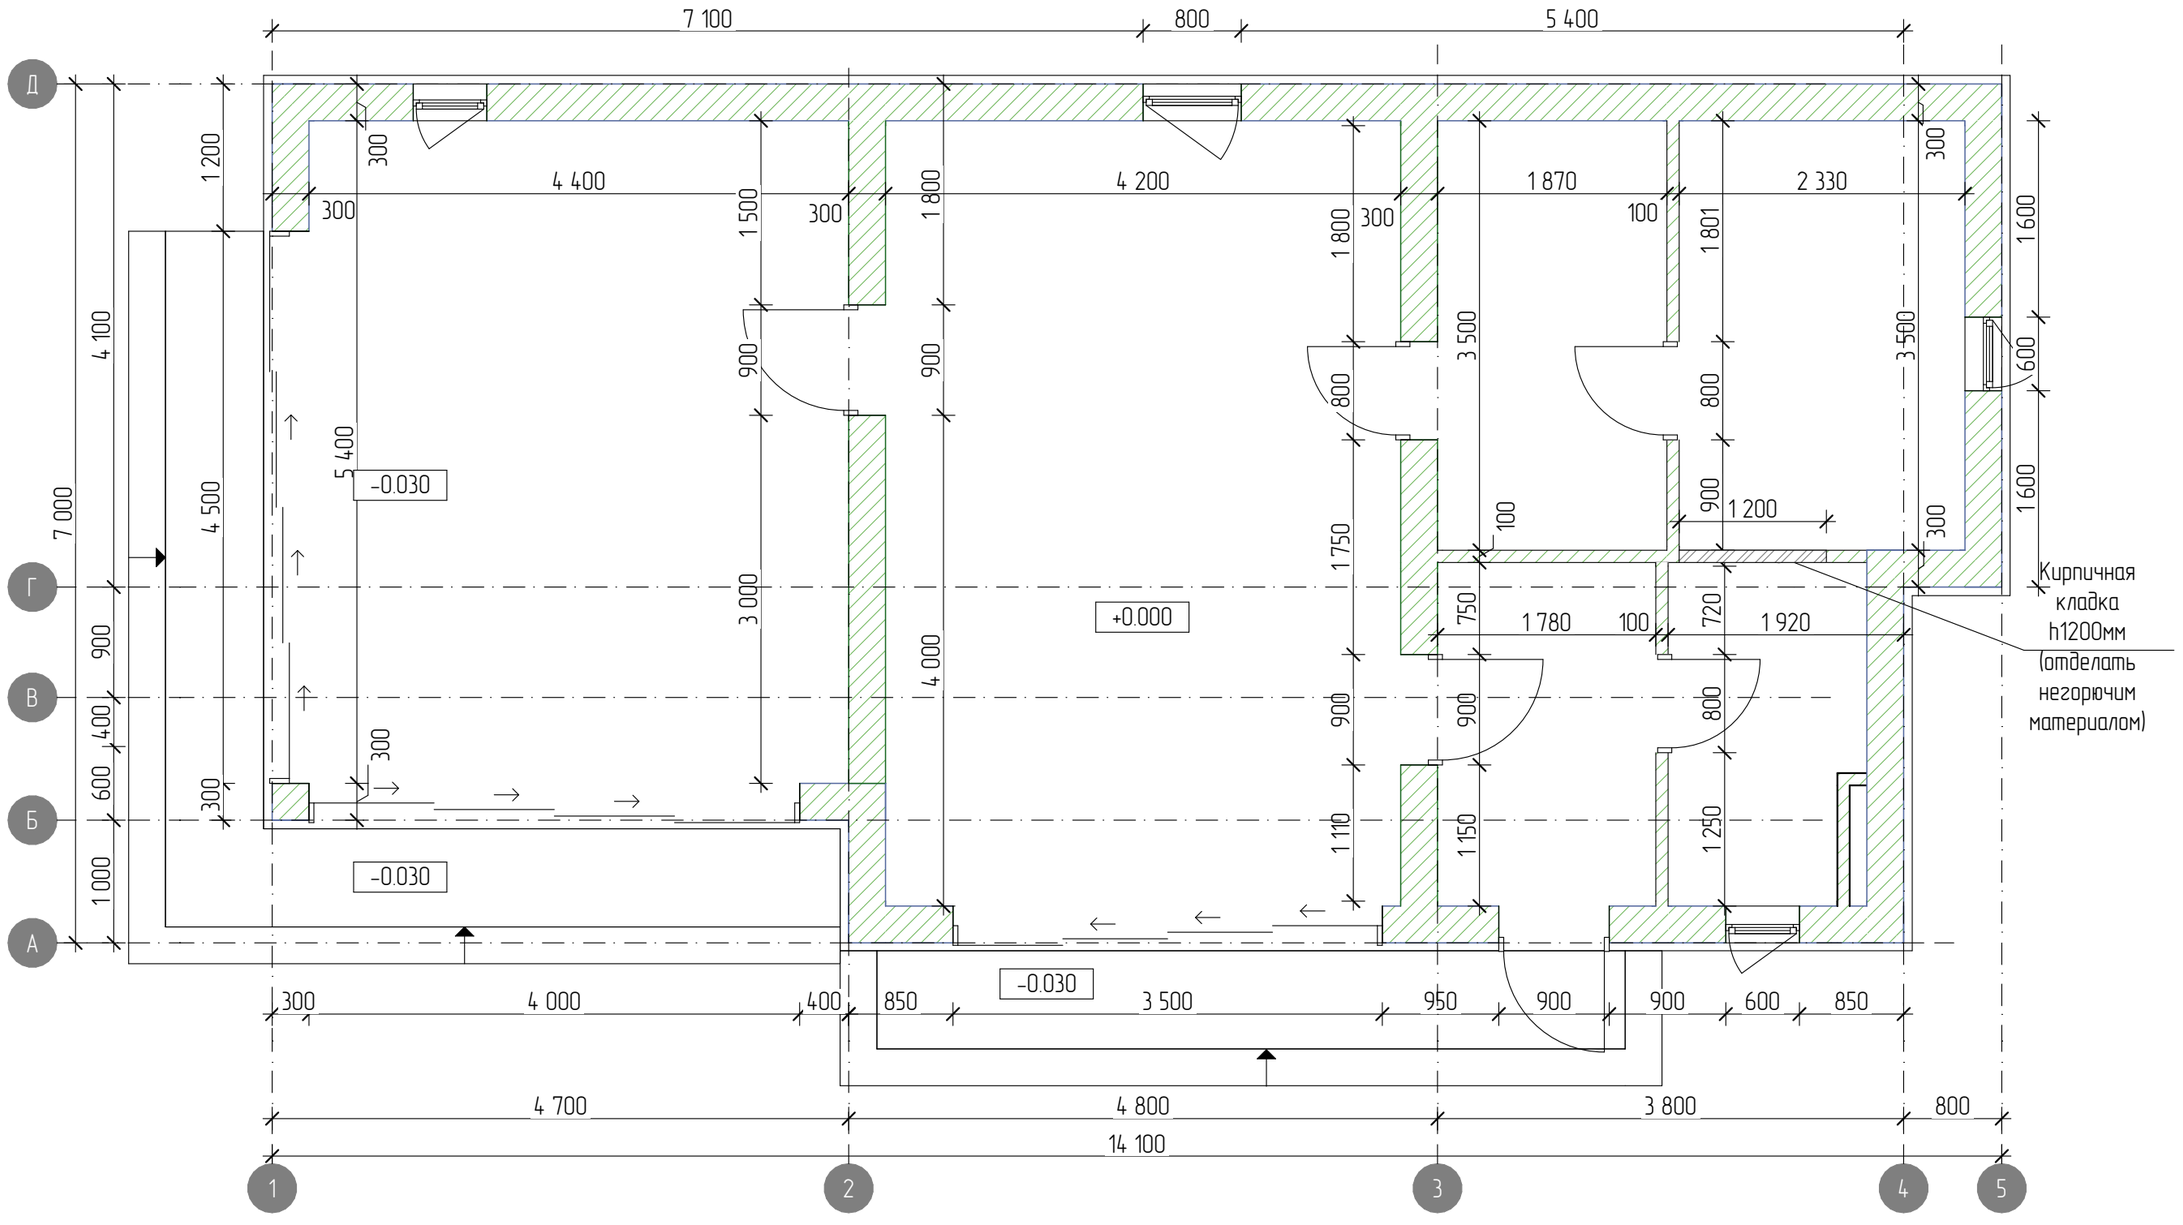

Примечание:

1. Размеры помещения даны без учёта внутренней и внешней отделки.
2. Ступени показаны условно.

Изм.	Колуч.	Лист	№Док.	Подп.	Дата	Индивидуальное строение_Баня	Стадия	Лист	Листов
						Размерный план			

Согласовано

Взам. инв. №

Подп. и дата

Инв. № подл.

План покрытия пола 1:50

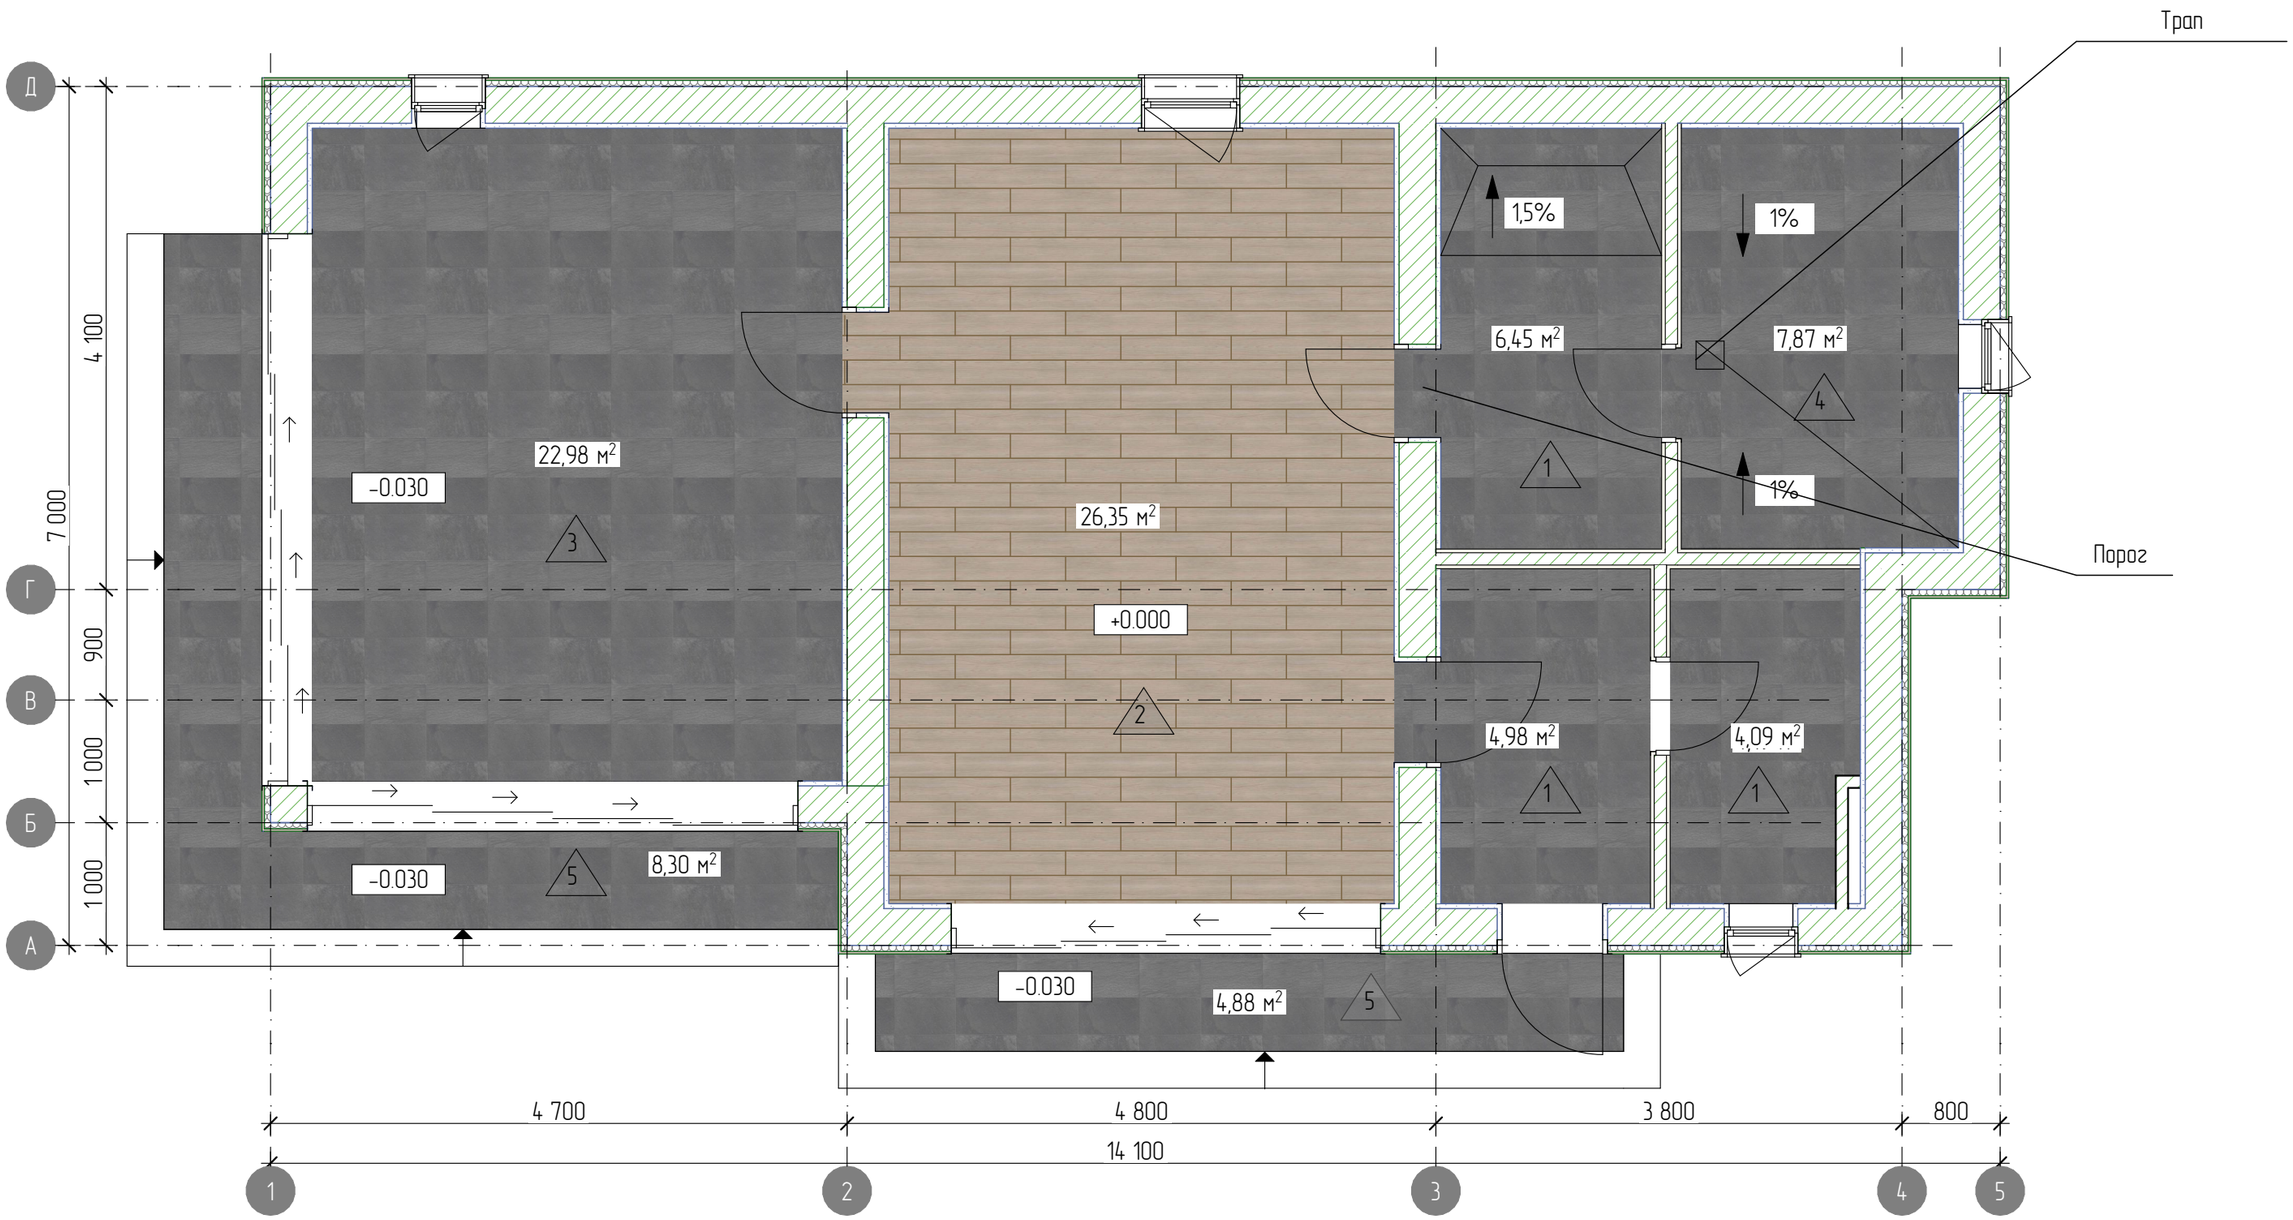

Примечание:

1. Сечения полов см. лист 8

Изм.	Колуч.	Лист	№Док.	Подп.	Дата	Индивидуальное строение_Баня	Стадия	Лист	Листов
						План покрытий пола			

Согласовано

Взам. инв. №

Подп. и дата

Инв. № подл.

Сечения покрытия пола

- Керамогранит 10 мм +клей 10мм
- ЦПС 50мм
- ЭППС 100мм
- Гидроизоляция наплавляемая 2 сл
- Битумный праймер
- Ж/б плита 200мм

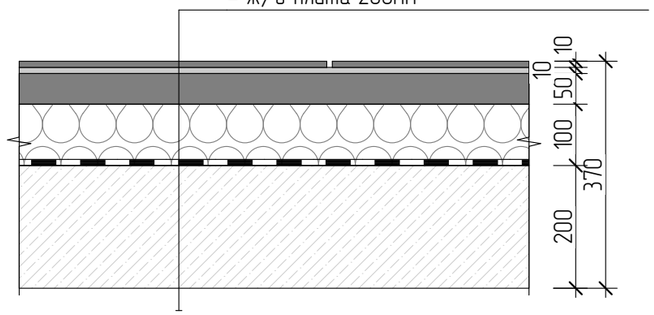

усл. обозначение на плане	1	Душевая, прихожая, с/у

- Виниловая плтка LVT
- Клей 10мм
- ЦПС 50мм
- ЭППС 100мм
- Гидроизоляция наплавляемая 2 сл
- Битумный праймер
- Ж/б плита 200мм

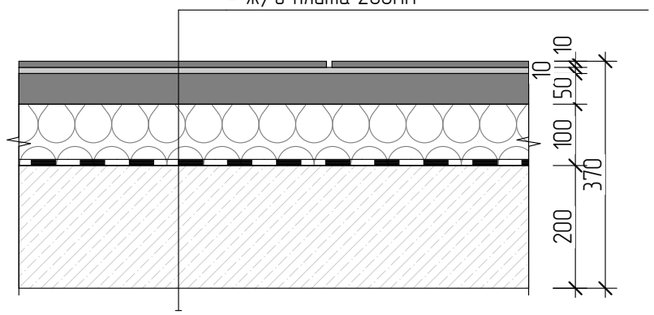

усл. обозначение на плане	2	Комната отдыха

- Керамогранит 10 мм +клей 10мм
- ЦПС 120мм с уклоном 1%
- Гидроизоляция наплавляемая 2 сл
- Битумный праймер
- Ж/б плита 200мм

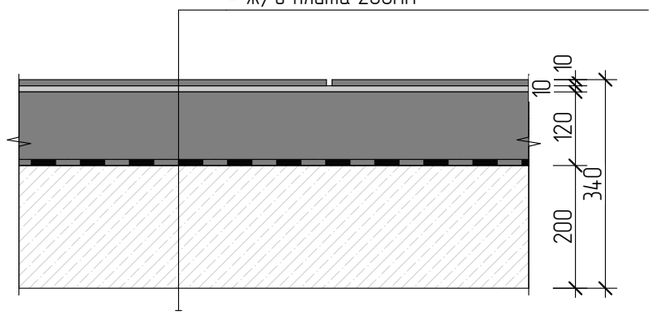

усл. обозначение на плане	4	Ступени

- Керамогранит 10 мм +клей 10мм
- ЦПС 120мм
- Гидроизоляция наплавляемая 2 сл
- Битумный праймер
- Ж/б плита 200мм

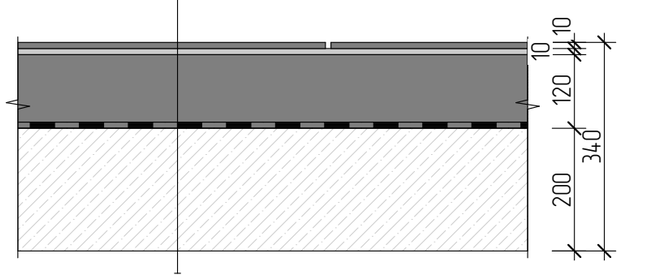

усл. обозначение на плане	3	Беседка

- Керамогранит 10 мм +клей 10мм
- ЦПС от 50 до 80мм
(с уклоном 1% в сторону лотка)
- Пароизоляционная мембрана
(алюминевая фольга)
- ЭППС 100мм
- Гидроизоляция наплавляемая 2 сл
- Битумный праймер
- Ж/б плита 200мм

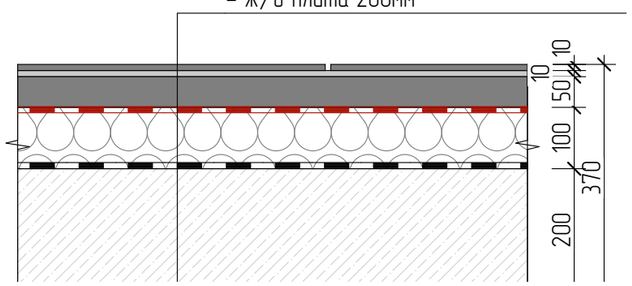

усл. обозначение на плане	4	Парная

Примечание:

1. Конструкция фундаментов разрабатывается проектом КЖ

Изм.	Колуч.	Лист	№Док.	Подп.	Дата

Индивидуальное строение_Баня	Стадия	Лист	Листов
Сечения покрытий пола			

Согласовано

Взам. инв. №

Подп. и дата

Инв. № подл.

Сечение 1-1

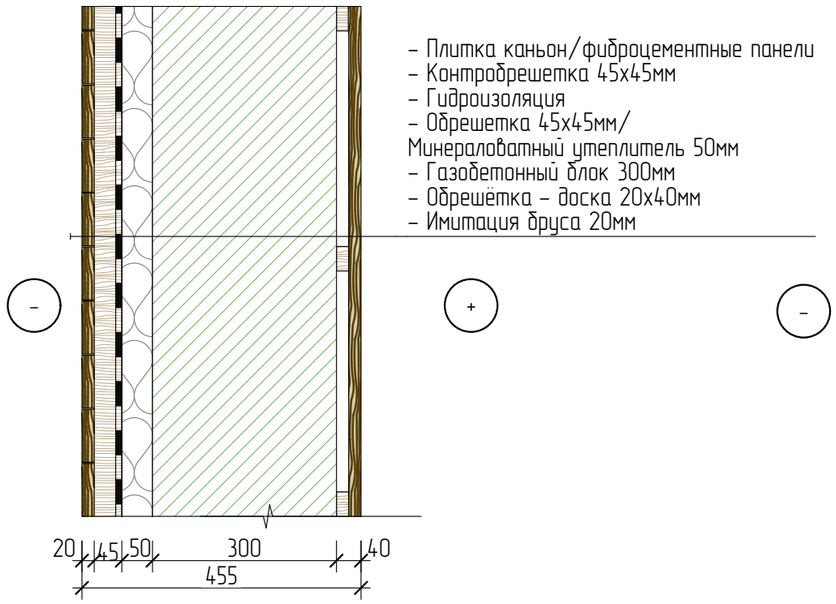

- Плитка каньон/фиброцементные панели
- Контробрешетка 45х45мм
- Гидроизоляция
- Обрешетка 45х45мм/
Минераловатный утеплитель 50мм
- Газобетонный блок 300мм
- Обрешётка – доска 20х40мм
- Имитация бруса 20мм

Сечение 2-2

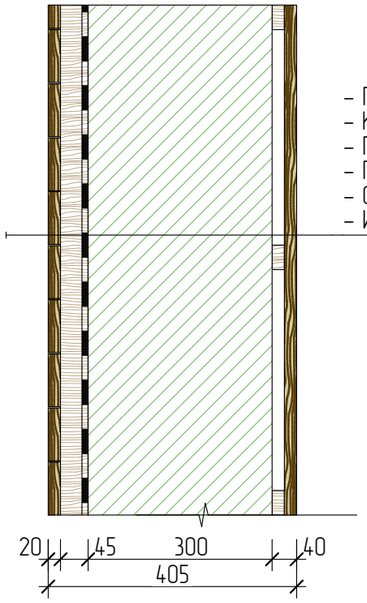

- Плитка каньон/фиброцементные панели
- Контробрешетка 45х45мм
- Гидроизоляция
- Газобетонный блок 300мм
- Обрешётка – доска 20х40мм
- Имитация бруса 20мм

Сечение 3-3

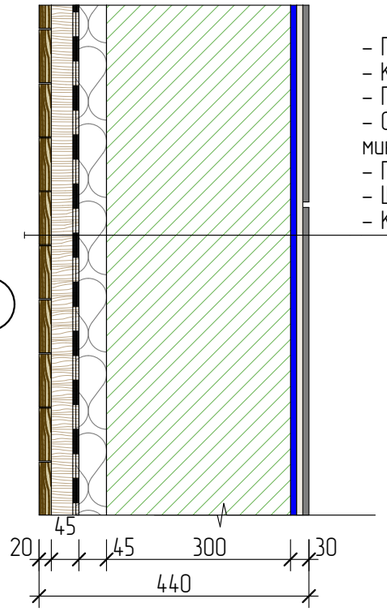

- Плитка каньон/фиброцементные панели
- Контробрешетка 45х45мм
- Гидроизоляция
- Обрешетка 45х45мм/
минераловатный утеплитель 150мм
- Газобетонный блок 300мм
- Штукатурка 9мм
- Клей+Керамогранит 20мм

Сечение 4-4

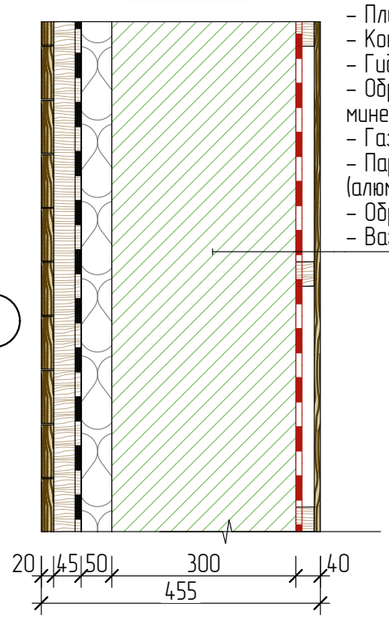

- Плитка каньон/фиброцементные панели
- Контробрешетка 45х45мм
- Гидроизоляция
- Обрешетка 45х45мм/
минераловатный утеплитель 50мм
- Газобетонный блок 300мм
- Пароизоляционная мембрана
(алюминиевая фольга)
- Обрешетка 20х40мм
- Вагонка 10мм

Сечение 5-5

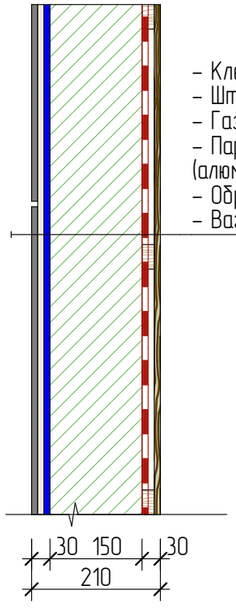

- Клей+керамогранит 20мм
- Штукатурка 9мм
- Газобетонный блок 300мм
- Пароизоляционная мембрана
(алюминиевая фольга)
- Обрешетка 20х40мм
- Вагонка 10мм

Изм.	Колуч.	Лист	№Док.	Подп.	Дата	Индивидуальное строение_Баня	Стадия	Лист	Листов
						Сечения стен (лист 1)			

Согласовано

Взам. инв. №

Подп. и дата

Инв. № подл.

Сечение 6-6

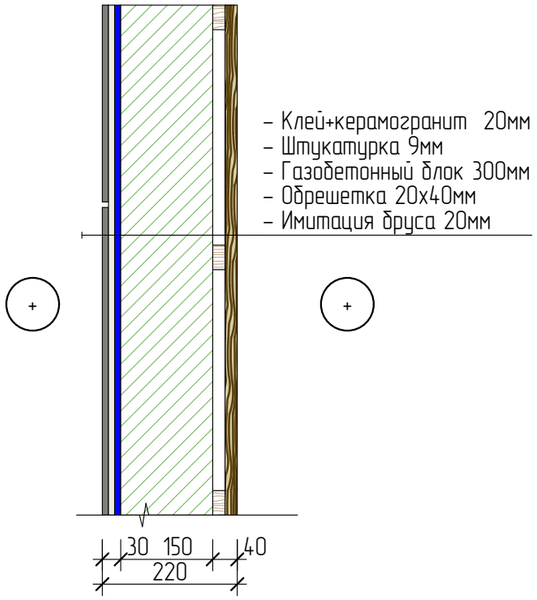

Сечение 7-7

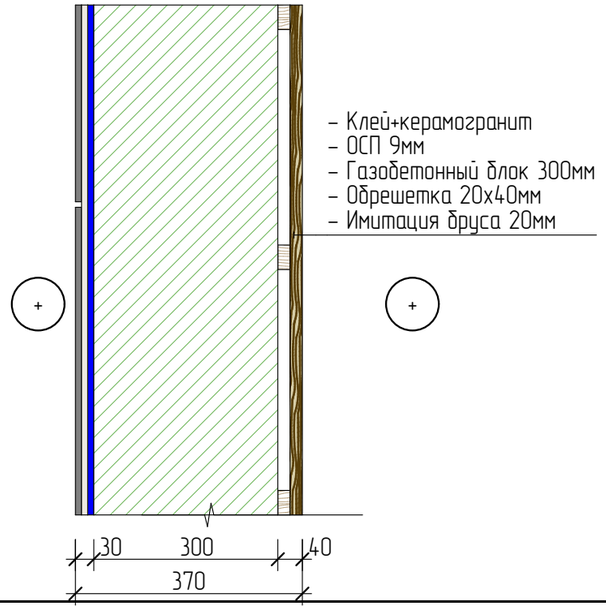

Сечение 8-8

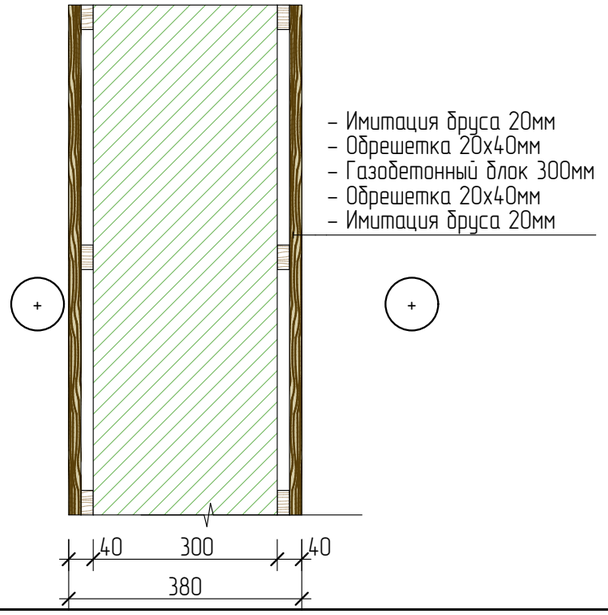

Сечение 9-9

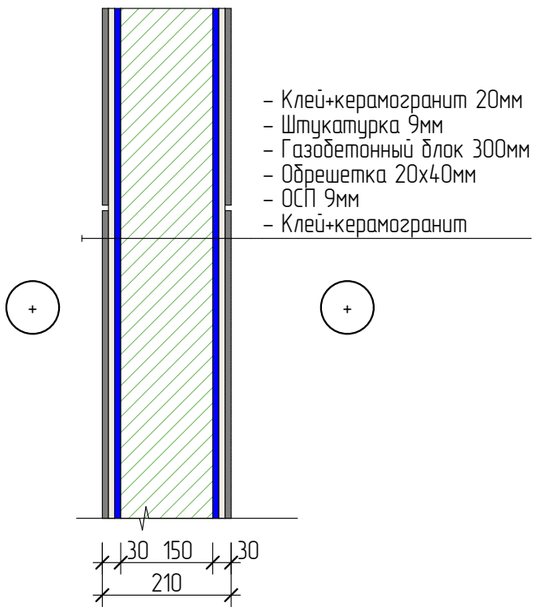

Согласовано

Взам. инв. №

Подп. и дата

Инв. № подл.

Изм.	Колуч.	Лист	№Док.	Подп.	Дата				
						Индивидуальное строение_Баня	Стадия	Лист	Листов
						Сечения стен (лист 2)			

План электрооборудования

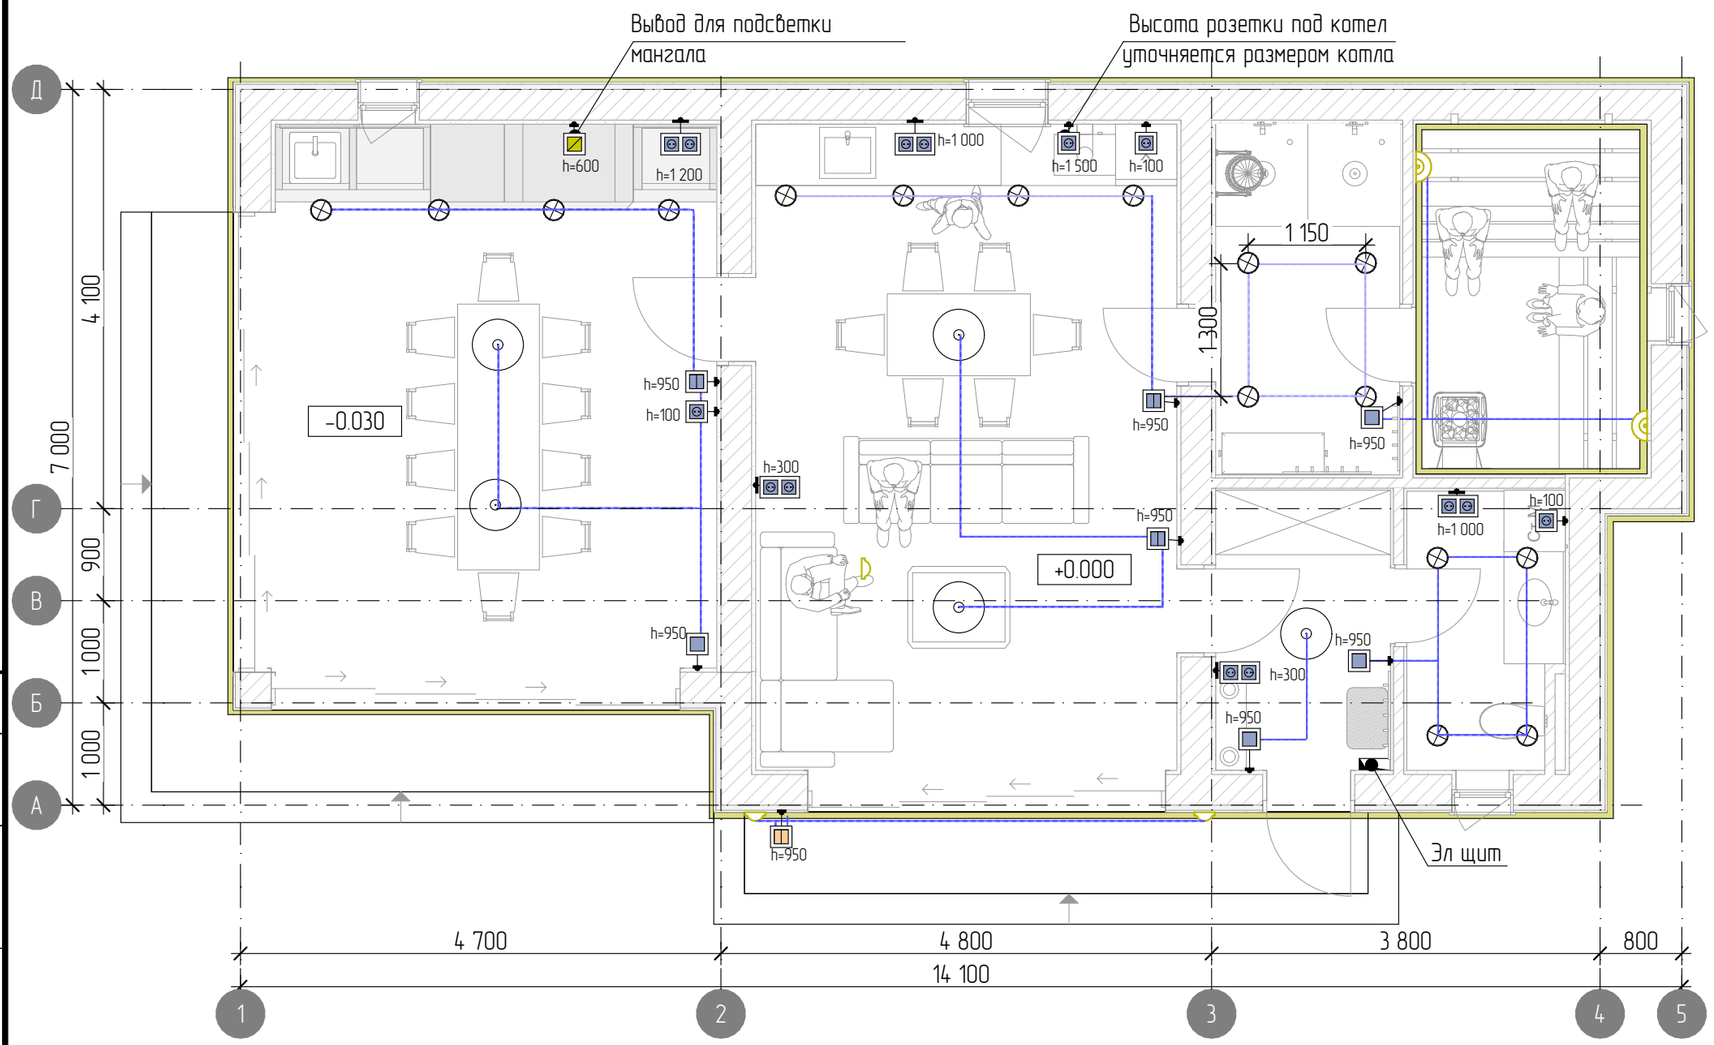

Электрооборудование		
Предпросмотр 2D-плана	ID Элемента	Количество
	Выключатель двухклавишный	3
	Выключатель одноклавишный	3
	Выключатель одноклавишный ip45	1
	Выключатель одноклавишный паралельный	1
	Навесной светильник	2
	Навесной фасадный светильник	2
	Розетка 220V двухрамная	5
	Розетка 220V однорамочная	4
	Светильник подвесной	5
	Светильник точечный	16
	Электрический вывод	1
	Уличная линейная подсветка встраиваемая в фасадный молдинг	43,18п.м.
	Линейная подсветка потолочная	11,4п.м.

Примечания:

1. Схема размещения розеток является рекомендательной и требует согласования с заказчиком по месту.
2. Все высоты даны от чистового пола, все указанные размеры даются до центра позиций.
3. Отметки розеток, выключателей, выводов и др. оборудования, являются предварительными и уточняются после выбора финишных материалов и мебели.
4. Размеры даны с учетом отделки.

Изм.	Колуч.	Лист	№Док.	Подп.	Дата			
						Индивидуальное строение_Баня	Стадия	Лист	Листов
						План электрооборудования			

Согласовано

Взам. инв. №

Подп. и дата

Инв. № подл.

План кровли

1:50

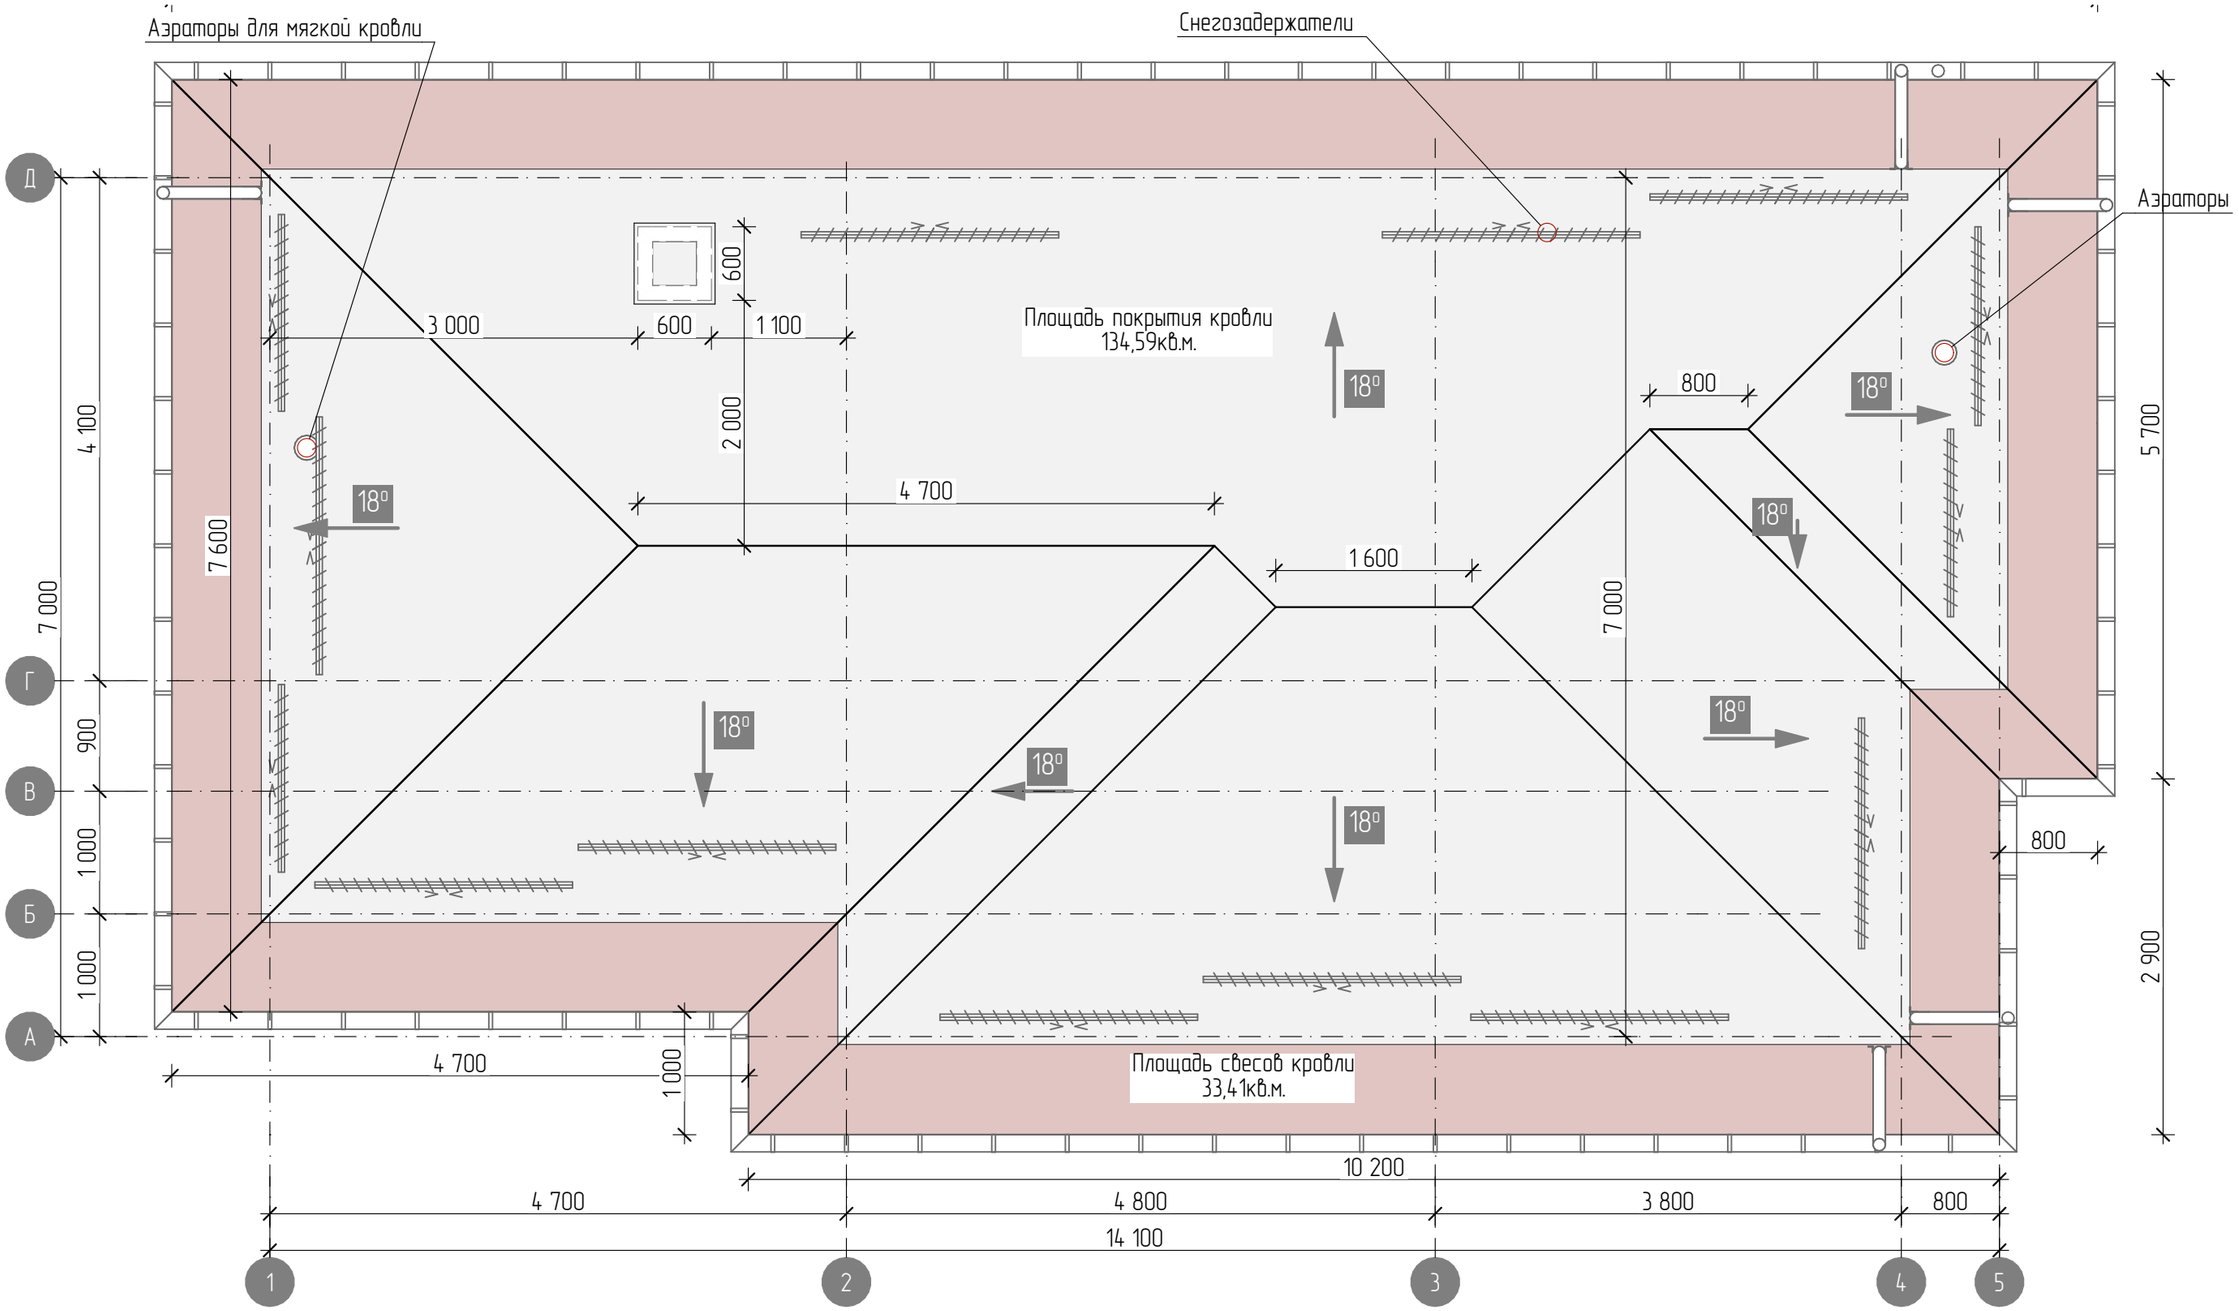

Общая площадь кровли 134,59 кв.м.

Примечания:

*- размеры привязки трубы печи показаны приблизительно, точную привязку определить после утверждения конкретной модели печи.

Изм.	Колуч.	Лист	№Док.	Подп.	Дата	Индивидуальное строение_Баня	Стадия	Лист	Листов
						План кровли			

Согласовано

Взам. инв. №

Подп. и дата

Инв. № подл.

Аксонометрия кровли

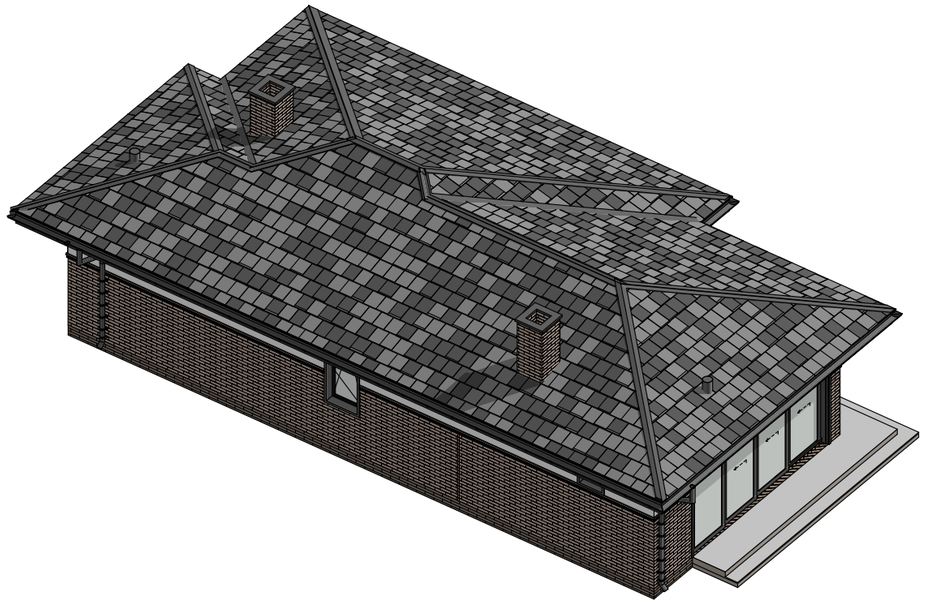

Узел по дымоходной трубе

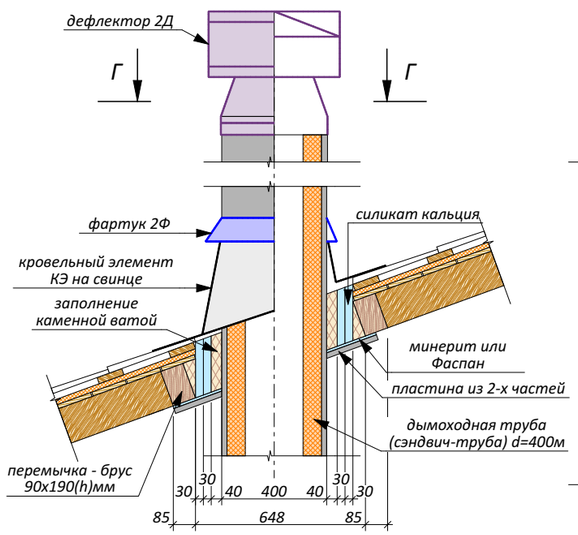

Г-Г

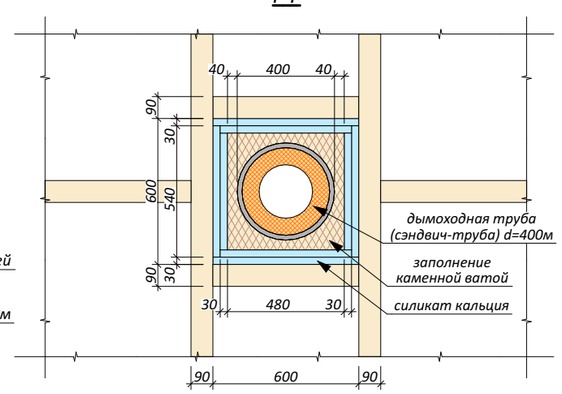

Изм.	Колуч.	Лист	№Док.	Подп.	Дата			
						Индивидуальное строение_Баня	Стадия	Лист	Листов
						Аксонометрия кровли			

Согласовано

Взам. инв. №

Подп. и дата

Инв. № подл.

Ведомость оконных проёмов				
Марка, поз.	Кол-во, шт.	Ориентация	Схема устройства (по размеру проёма)	Площадь Проема
ОК-01	1	Л (1)	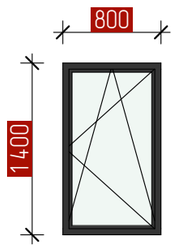	1,12
ОК-02	1	П (1)	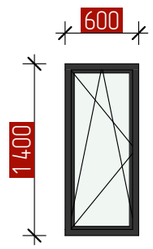	0,84
ОК-03	1	П (1)	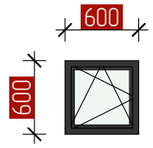 С жаропрочным стеклом	0,36

Ведомость оконных проёмов				
Марка, поз.	Кол-во, шт.	Ориентация	Схема устройства (по размеру проёма)	Площадь Проема
ОК-04	1	П (1)	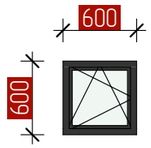 С автоматическим приводом	0,36
				2,68 м|

Примечание:

1. В таблице указаны проёмы, размеры изделий уточнить у производителя.
2. Предусмотреть на окнах москитные сетки

Изм.	Колуч.	Лист	№Док.	Подп.	Дата				
						Индивидуальное строение_Баня	Стадия	Лист	Листов
						Ведомость оконных проёмов			

Согласовано

Взам. инв. №

Подп. и дата

Инв. № подл.

АР Ведомость дверных проёмов

Марка, поз.	Кол-во, шт.	Ориентация	Схема устройства (по размеру проёма)	Площадь Проема
ДВ-1	1	П (1)	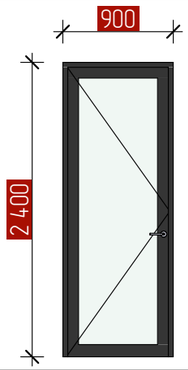	2,16
ДВ-2	1	Л (1)		8,40
ДВ-3	2	Л (2)	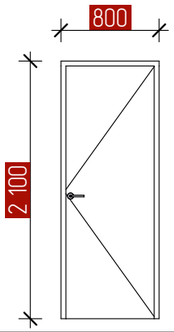	1,68
ДВ-4	2	Л (1) I ...	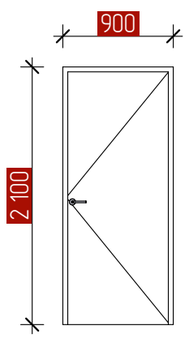	1,89

АР Ведомость дверных проёмов

Марка, поз.	Кол-во, шт.	Ориентация	Схема устройства (по размеру проёма)	Площадь Проема
ДВ-5	1	П (1)	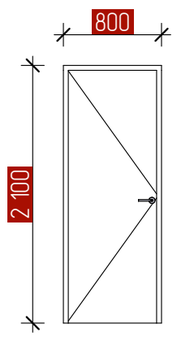	1,68
ДВ-6	1	П (1)		9,60
ДВ-7	1	Л (1)	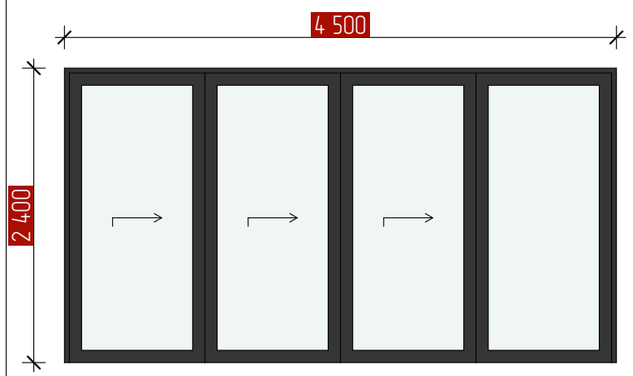	10,80
				39,78 м!

Примечание:

1. В таблице указаны проёмы, размеры изделий уточнить у производителя.

Изм.	Колуч.	Лист	№Док.	Подп.	Дата			
						Индивидуальное строение_Баня	Стадия	Лист	Листов
						Ведомость дверных проемов			

Согласовано

Взам. инв. №

Подп. и дата

Инв. № подл.

Разрез 1-1

1:50

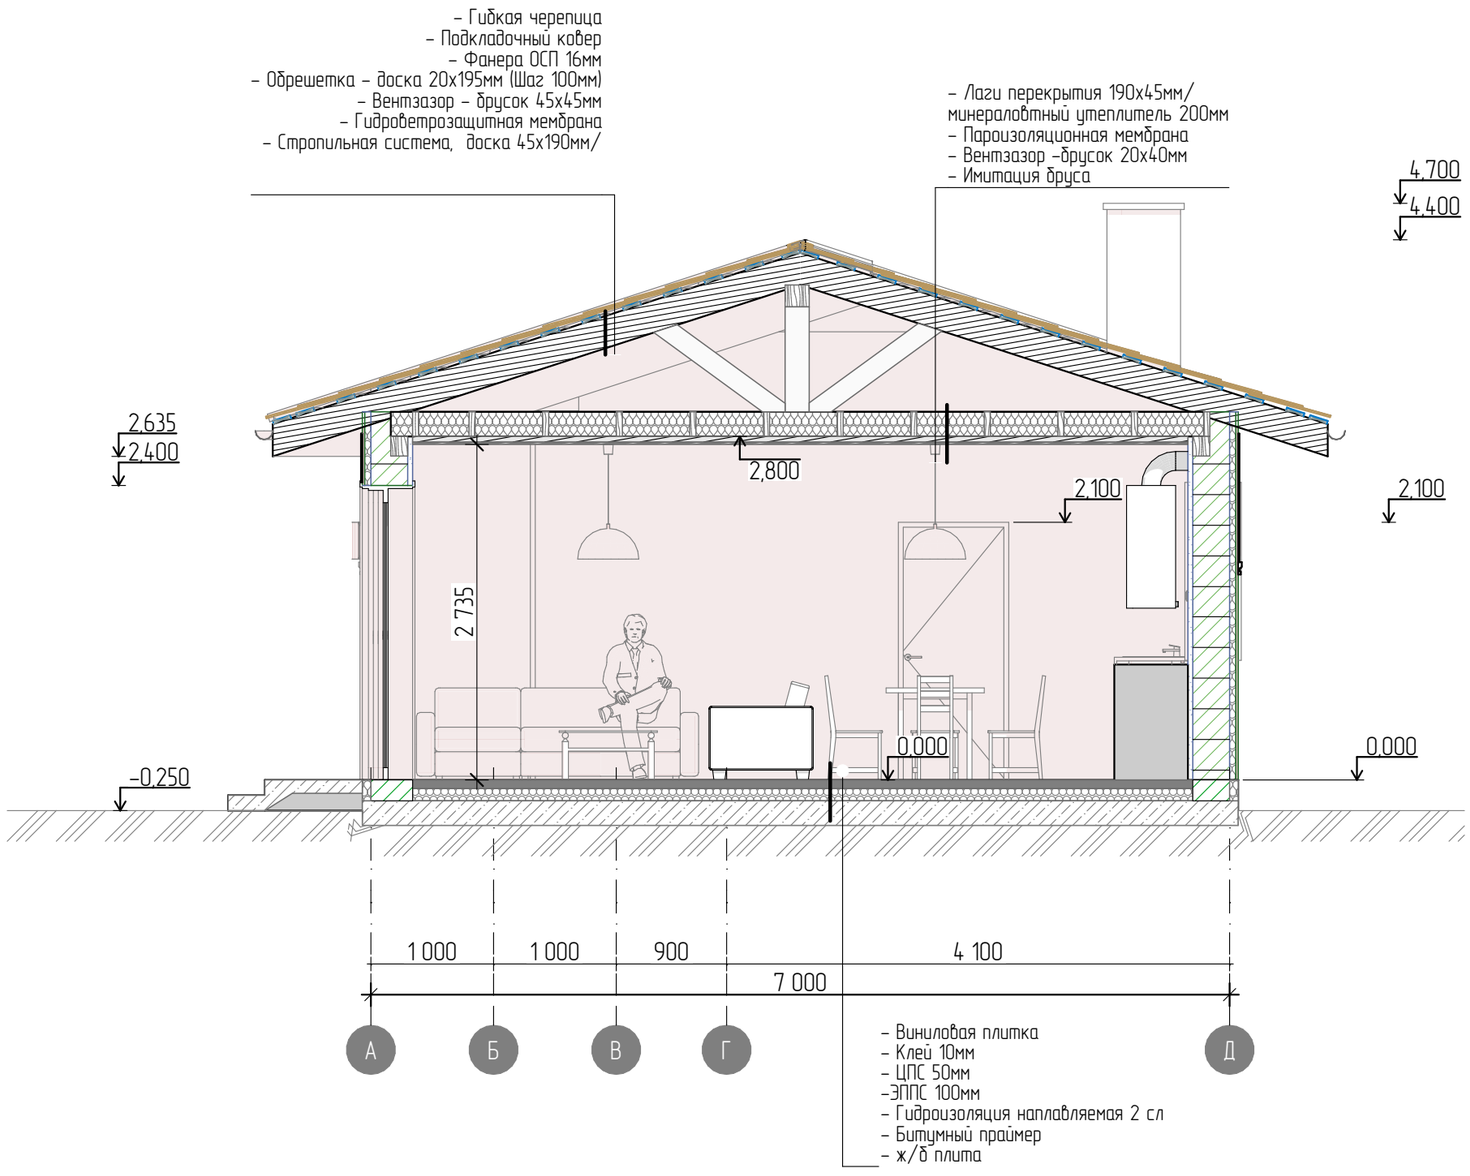

Изм.	Колуч.	Лист	№Док.	Подп.	Дата			
						Индивидуальное строение_Баня	Стадия	Лист	Листов
						Разрез 1-1			

Согласовано

Взам. инв. №

Подп. и дата

Инв. № подл.

Разрез 2-2

1:50

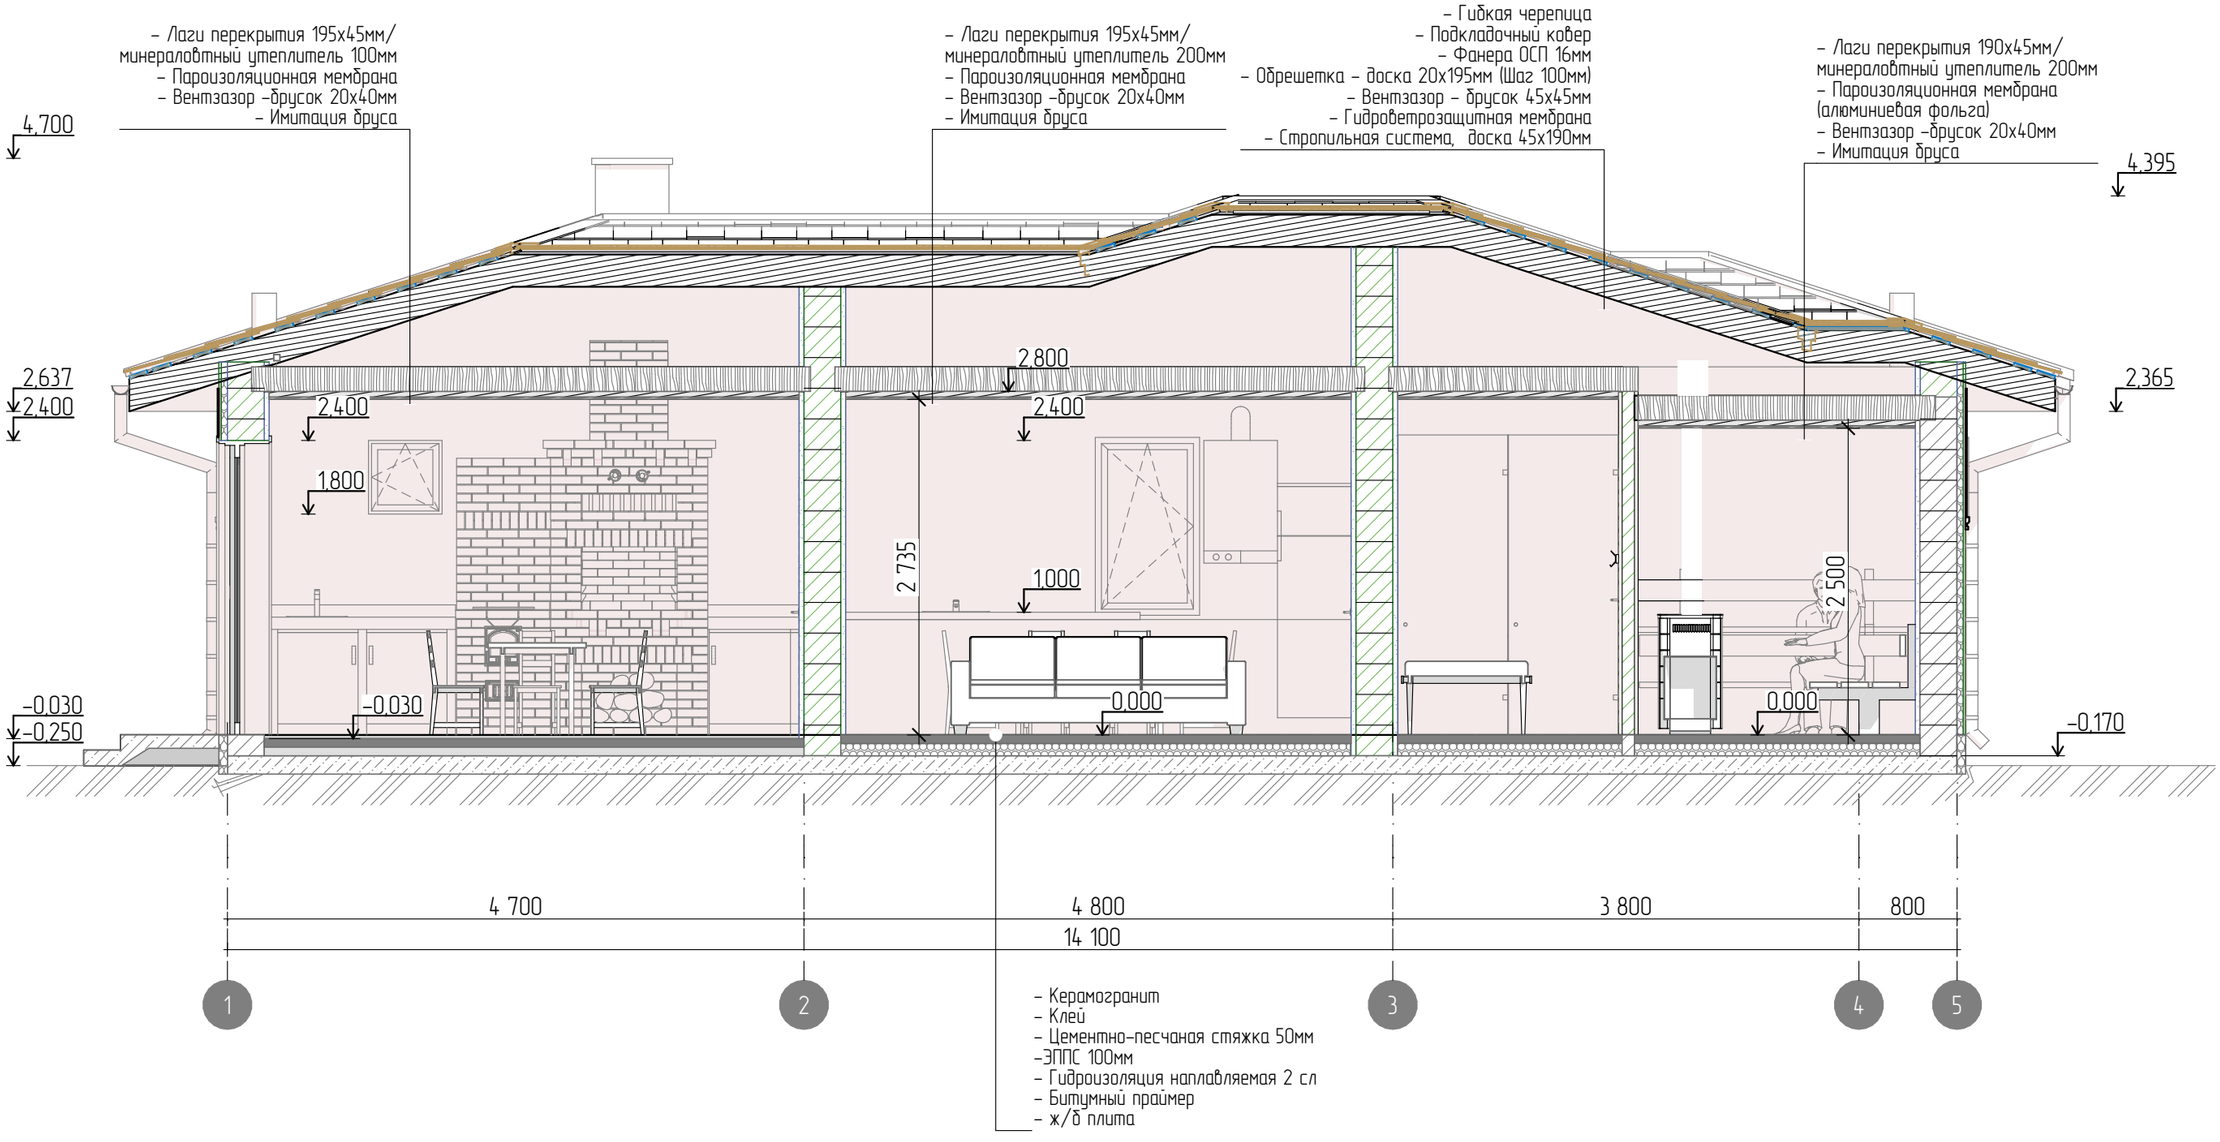

Изм.	Колуч.	Лист	№Док.	Подп.	Дата	Индивидуальное строение_Баня	Стадия	Лист	Листов
						Разрез 2-2			

Согласовано

Взам. инв. №

Подп. и дата

Инв. № подл.

Аксонометрия разреза

Изм.	Колуч.	Лист	№Док.	Подп.	Дата		
						Индивидуальное строение_Баня	Стадия / Лист / Листов
						Аксонометрия разреза	

Согласовано

Взам. инв. №

Подп. и дата

Инв. № подл.

Ф–1

1:50

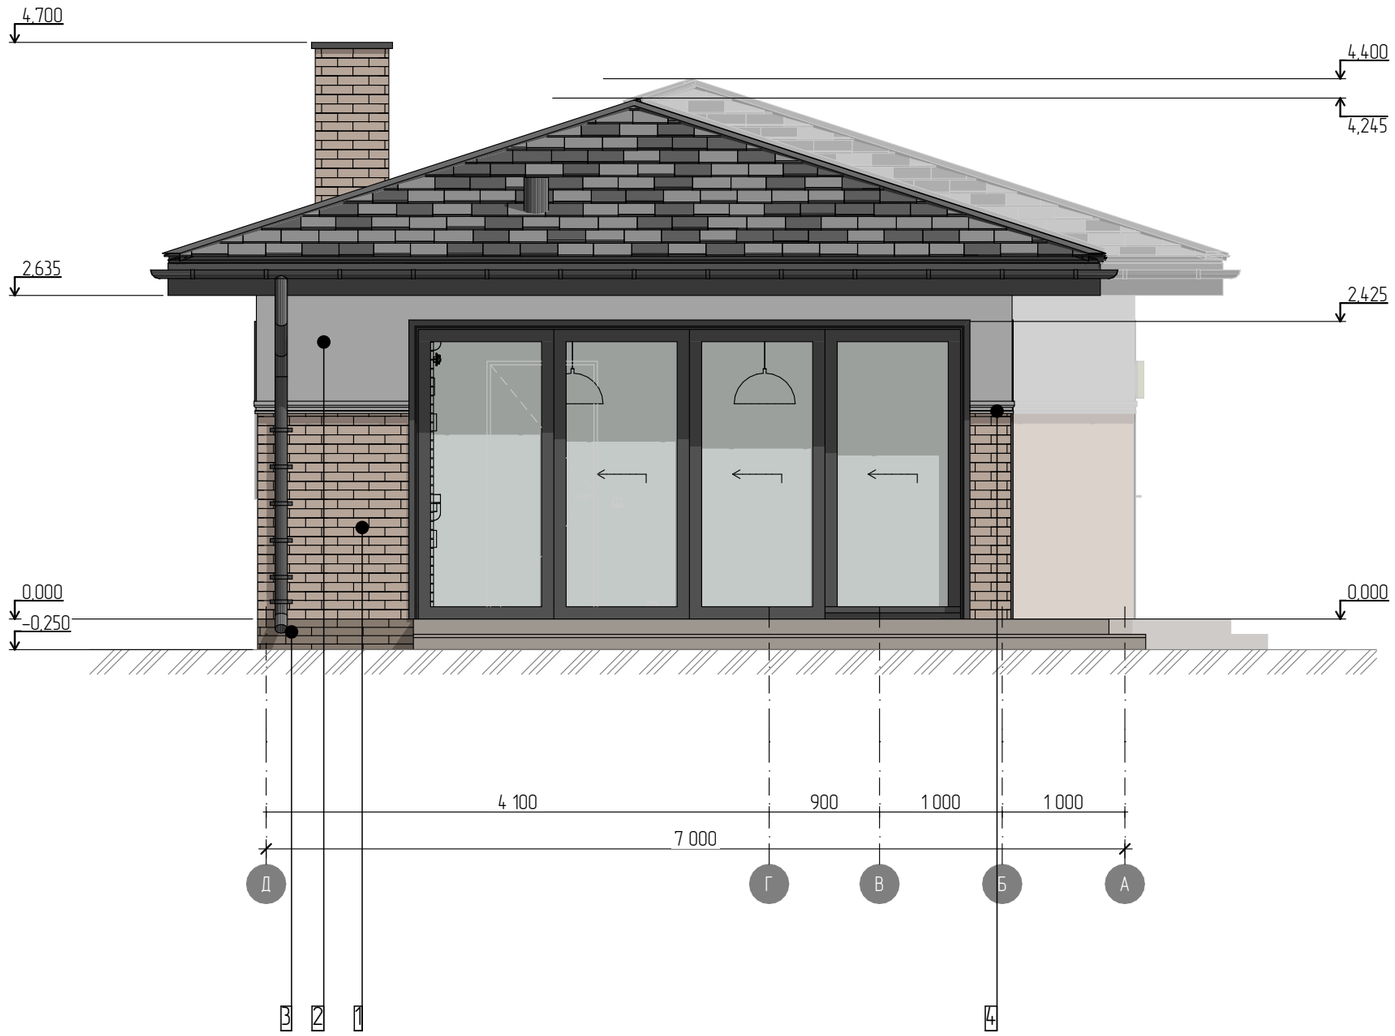

Примечание:

1. Цветовое решение фасада и материалов отделки показаны в проекте приблизительно.

Ведомость отделки фасада

Обозначение	Наименование	Кол–во	Примечание
1	Плитка фасадная каньон		Стены наружные
2	Фиброцементные панели		Стены наружные
3	Плитка фасадная Каньон		Цоколь
4	Молдинг фасадный из стеклофибробетона		Цоколь

Изм.	Колуч.	Лист	№Док.	Подп.	Дата

Индивидуальное строение_Баня

Стадия	Лист	Листов

Цветовое решение; Фасад в осях Д–А

Согласовано

Взам. инв. №

Подп. и дата

Инв. № подл.

Ф–2

1:50

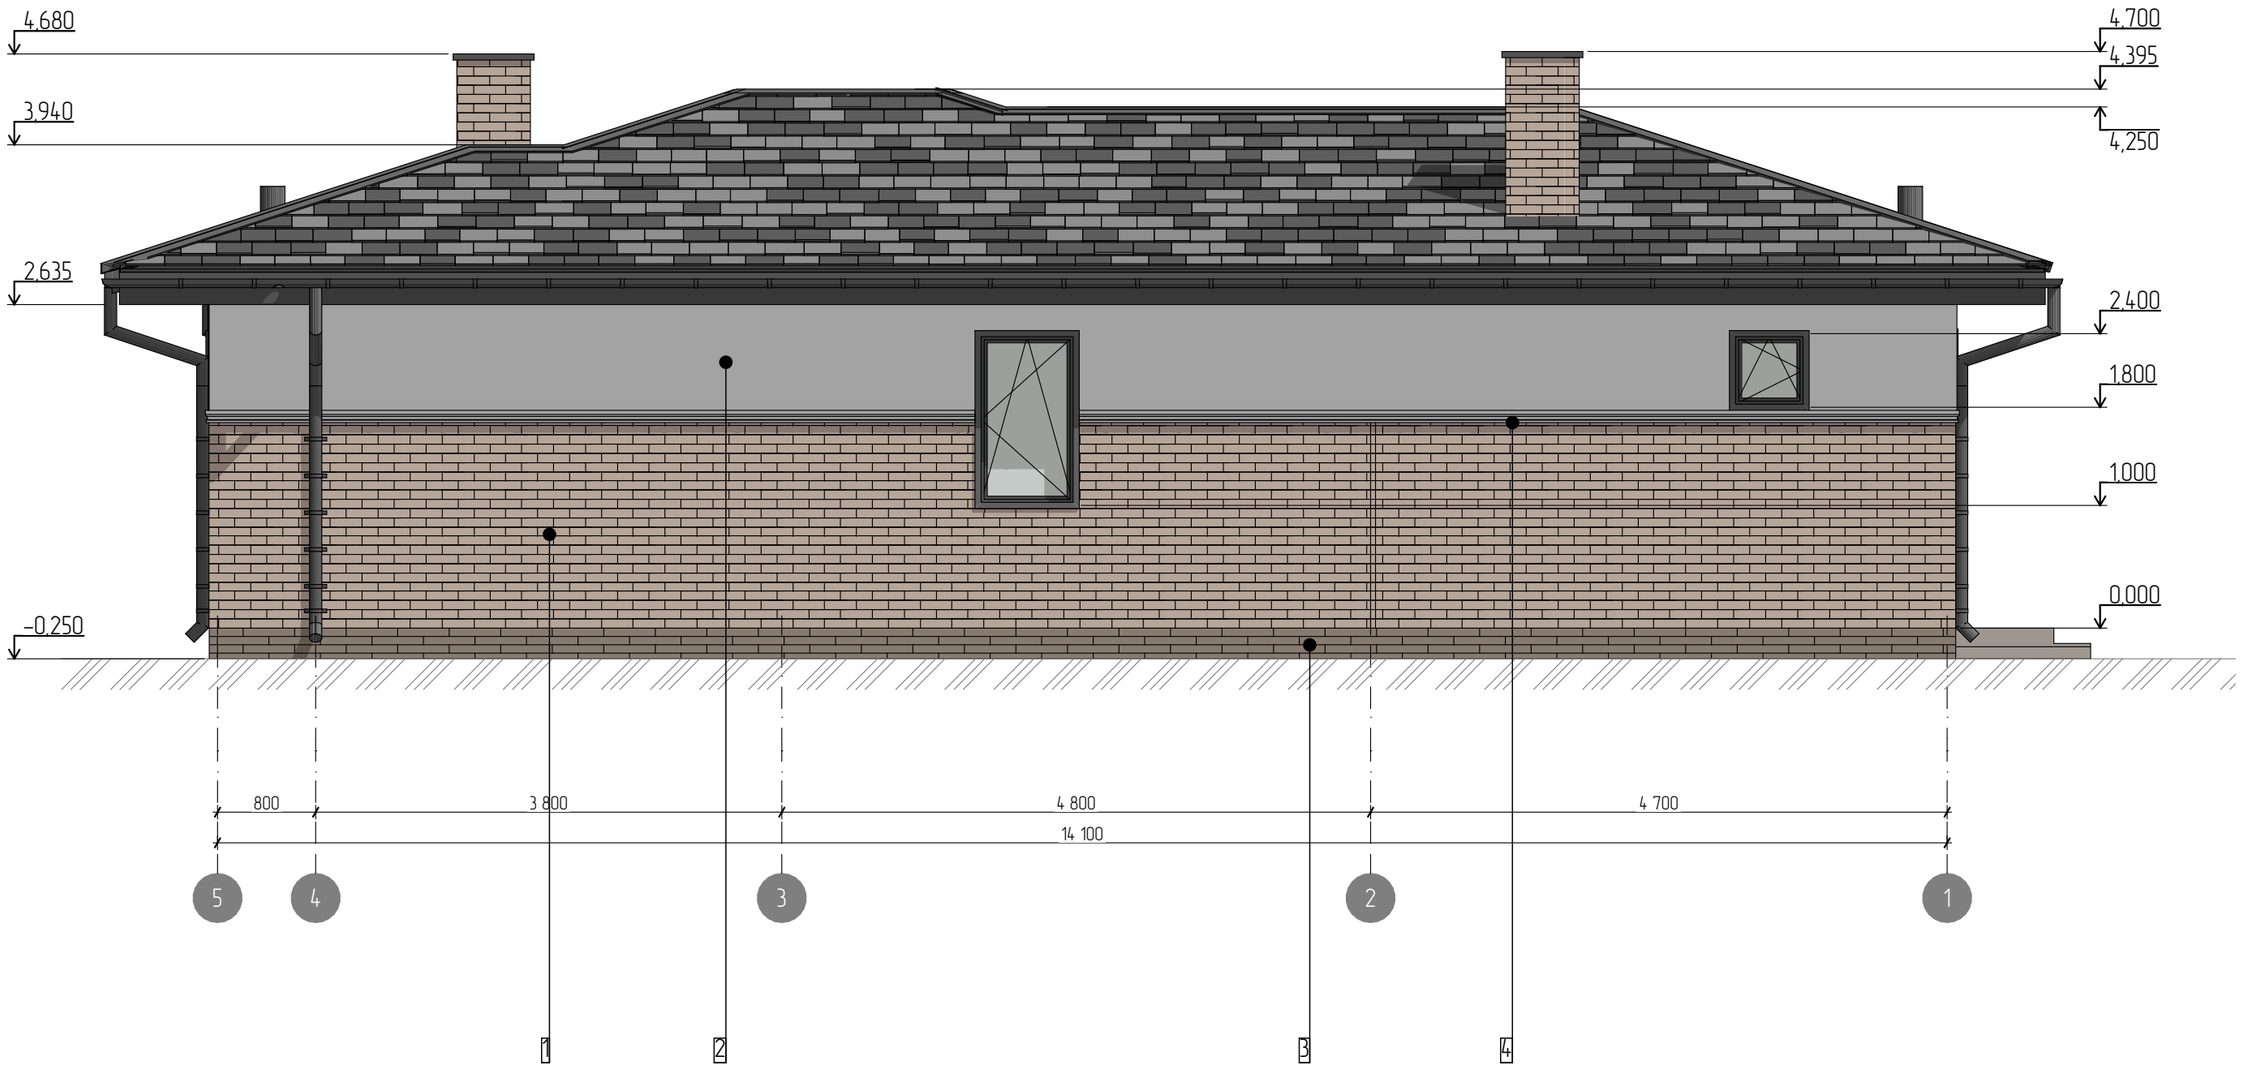

Примечание:

1. Цветовое решение фасада и материалов отделки показаны в проекте приблизительно.

Ведомость отделки фасада

Обозначение	Наименование	Кол–во	Примечание
1	Плитка фасадная каньон		Стены наружные
2	Фиброцементные панели		Стены наружные
3	Плитка фасадная Каньон		Цоколь
4	Молдинг фасадный из стеклофибробетона		Цоколь

Изм.	Колуч.	Лист	№Док.	Подп.	Дата

Индивидуальное строение_Баня

Стадия	Лист	Листов

Цветовое решение; Фасад в осях 5–1

Согласовано

Взам. инв. №

Подп. и дата

Инв. № подл.

Ф–3

1:50

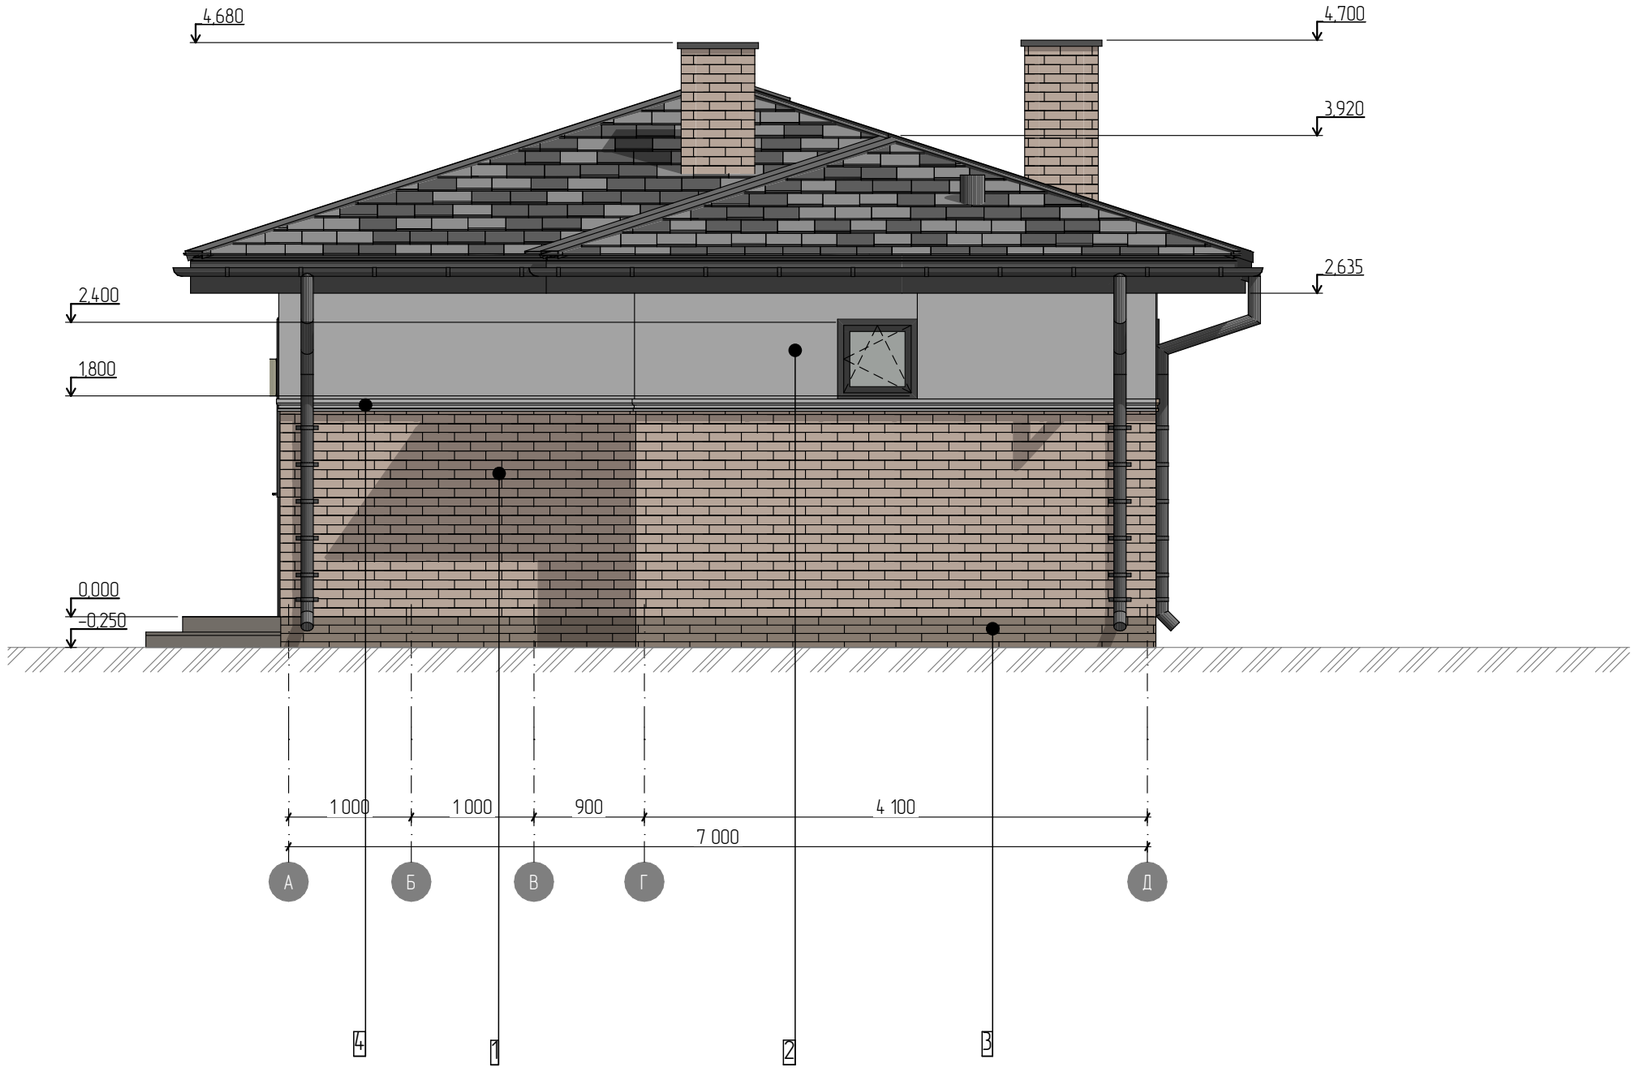

Примечание:

1. Цветовое решение фасада и материалов отделки показаны в проекте приблизительно.

Ведомость отделки фасада

Обозначение	Наименование	Кол–во	Примечание
1	Фиброцементные фасадные панели		Стены наружные
2	Планкен (вертикальная раскладка)		Парапет
3	Террасная доска – ДПК		Цоколь

Изм.	Колуч.	Лист	№Док.	Подп.	Дата			
						Индивидуальное строение_Баня	Стадия	Лист	Листов
						Цветовое решение; Фасад в осях А–Д			

Согласовано

Взам. инв. №

Подп. и дата

Инв. № подл.

Ф–4

1:50

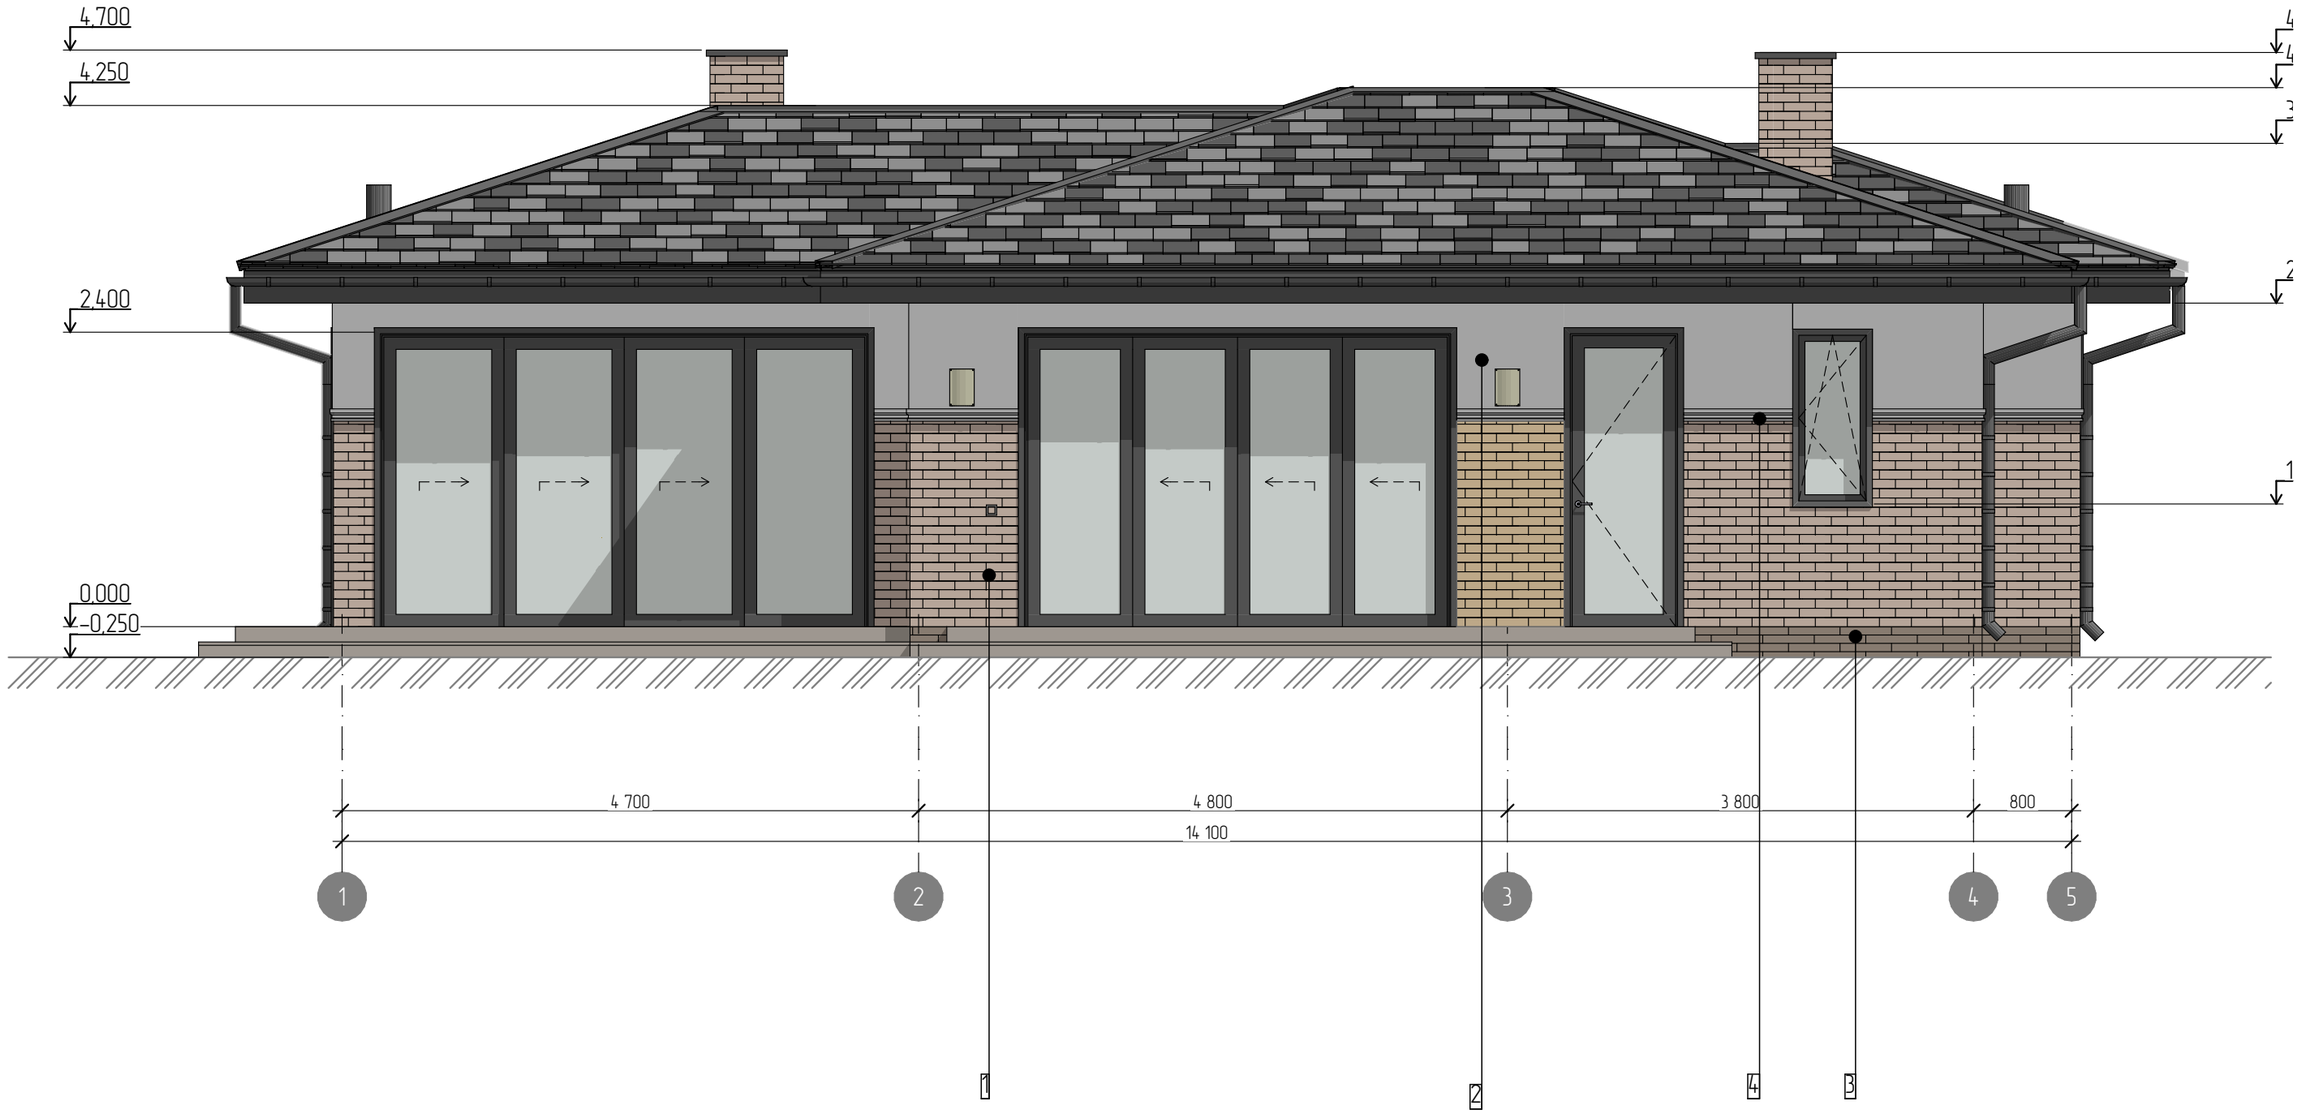

Примечание:

1. Цветовое решение фасада и материалов отделки показаны в проекте приблизительно.

Ведомость отделки фасада

Обозначение	Наименование	Кол–во	Примечание
1	Фиброцементные фасадные панели		Стены наружные
2	Планкен (вертикальная раскладка)		Стены наружные, парапет
3	Террасная доска – ДПК		Цоколь

Изм.	Колуч.	Лист	№Док.	Подп.	Дата			
						Индивидуальное строение_Баня	Стадия	Лист	Листов
						Цветовое решение; Фасад в осях 1–5			

Согласовано

Взам. инв. №

Подп. и дата

Инв. № подл.

Примечания:

Визуализации беседки являются приблизительными. Цвет отделки показан условно, визуализации даны для общего понимания внутреннего пространства и типа отделки.. Цвет и материал согласовывается с заказчиком в процессе реализации.

Изм.	Колуч.	Лист	№Док.	Подп.	Дата			
						Индивидуальное строение_Баня	Стадия	Лист	Листов
						Визуализация №1			

Согласовано

Взам. инв. №

Подп. и дата

Инв. № подл.

Согласовано

Взам. инв. №

Подп. и дата

Инв. № подл.

Изм.	Колуч.	Лист	№Док.	Подп.	Дата				
						Индивидуальное строение_Баня	Стадия	Лист	Листов
						Визуализация №2			

Изм.	Колуч.	Лист	№Док.	Подп.	Дата	

Индивидуальное строение_Баня	Стадия	Лист	Листов
Визуализация №3			

Согласовано

Взам. инв. №

Подп. и дата

Инв. № подл.