Рабочая документация



Архитектурные решения
(раздел АР)
Одноэтажное здание
(баня)
Основной комплект
чертежей (планы,
разрезы, фасады)

Архитектор _____ _____

Заказчик _____ _____

Москва
2026

Пояснительная записка

Общие данные:

1. Проект двухэтажной бани, выполнен индивидуально на основании исходных данных представленных заказчиком.
2. Состав пирогов конструкций предусматривает его круглогодичную эксплуатацию.

Размеры строения 8,00х7,20 м в осях

За относительную отметку ±0.000 принять уровень верха фундаментной плиты.

3. Адрес строительства:

Конструктивные решения:

1. Чертежи разработаны на основании задания на проектирование.

2. Объект строительства расположен в следующих климатических зонах:
- Нормальный вес снегового покрова для III района – Sg=1,5 кН/м2;
- Нормальное ветровое давление для I района – 23 кгс/м2;
- Расчётная зимняя температура для наружного воздуха – минус 26°С;
- Нормативная глубина промерзания грунта – 1,4 м;
- Полезная нагрузка на покрытие – 150 кгс/м2.

3. Общая характеристика:
- Уровень ответственности – нормальный.
- Класс сооружения – КС-2
- Категория здания по взрывопожарной и пожарной опасности – В.
- Класс функциональной пожарной опасности здания – Ф 1.4.
- Степень огнестойкости – III.
- Класс конструктивной пожарной опасности здания – С1
- Класс пожарной опасности строительных конструкций –К3.
- Зона влажности – нормальный.
- Расчётная температура наружного воздуха наиболее холодной пятидневки: -29°С.

4. Конструктивно, строение представляет собой сооружение сплитным монолитным фундаментом, несущими стенами из клееного бруса, кровлей по деревянным стропилам.

5. При проведении строительных работ необходимо осуществлять технический надзор с ведением журнала работ. Осуществлять входной контроль материалов, вести приёмку по каждому этапу работ.

6. Описание конструкций строения:
- Фундамент – железобетонная плита h=250мм
- Несущие конструкции – кленный брус 200х200мм
- Стропильная система – из строганой доски сечением 190(h)х45мм, уточняется в разделе КР
- Кровля – вальмовой;
- Покрытие кровли – металлочерепица;

Изм.	Колуч.	Лист	№Док.	Подп.	Дата	Двухэтажное здание (баня)	Стадия	Лист	Листов
Разраб.							АР		
ГАП									
Т. контр.									
Н. контр.						Пояснительная записка			
Утв.									

Состав чертежей

Лист	Наименование
1	Титульный
2	Пояснительная записка
3	Состав чертежей
4	Визуализация
5	Визуализация
6	Визуализация
7	Визуализация
8	Визуализация
9	Маркировочный план 1 этажа
10	Маркировочный план 2 этажа
11	Размерный план 1 этажа
12	Размерный план 2 этажа
13	Ведомость заполнения оконных проемов
14	3д-вид
15	3д-вид 1 этажа
16	3д-вид 2 этажа
17	План внутренней отделки 1 этажа
18	План внутренней отделки 2 этажа
19	План электрооборудования 1 этажа
20	План электрооборудования 2 этажа
21	План крыши
22	Разрез 1-1
23	Разрез 2-2
24	Фасад 1-2
25	Фасад А-Г, Фасад Г-А
26	Фасад 2-1

Изм.	Колуч.	Лист	№Док.	Подп.	Дата				
Разраб.						Двухэтажное здание (баня)	Стадия	Лист	Листов
ГАП							АР		
Т. контр.									
Н. контр.						Состав чертежей			
Утв.									



Изм.	Колуч.	Лист	№Док.	Подп.	Дата	Двухэтажное здание (баня)	Стадия	Лист	Листов
Разраб.							АР		
ГАП									
Т. контр.						Визуализация			
Н. контр.									
Утв.									



Изм.	Колуч.	Лист	№Док.	Подп.	Дата.	Двухэтажное здание (баня)	Стадия	Лист	Листов
Разраб.							АР		
ГАП									
Т. контр.									
Н. контр.						Визуализация			
Утв.									



Изм.	Колуч.	Лист	№Док.	Подп.	Дата.	Двухэтажное здание (баня)	Стадия	Лист	Листов
Разраб.							АР		
ГАП									
Т. контр.									
Н. контр.						Визуализация			
Утв.									

Маркировочный план 1 этажа




Экспликация 1-й этаж		
№	Название	Площадь, м2
Внешняя площадь		
1	Крыльцо	3,36
Внутренняя площадь		
1	Тамбур	3,46
2	Холл	2,03
3	Комната отдыха	17,15
4	С/у	1,88
5	Душевая	3,58
6	Парная	6,10
Общая площадь застройки		
		51,36

Примечание:
1. Вся индивидуальная мебель выполняется по отдельному проекту с детальной проработкой и калькуляцией. Чертежи предоставляет фирма-изготовитель столярных изделий.
2. Данный проект отдельно согласовывается с автором проекта и непосредственно с заказчиком.
3. Цветовое решение фасада и материалов отделки показаны в проекте приблизительно.
4. Количество ступений показано условно.
5.Расстояние и узлы крепления/проходок смотреть в техническом проекте для установки банной печи.

Изм.	Колуч.	Лист	№Док.	Подп.	Дата	Двухэтажное здание (баня)	Стадия	Лист	Листов
Разраб.							АР		
ГАП									
Т. контр.						Маркировочный план 1 этажа			
Н. контр.									
Утв.									

Маркировочный план 2 этажа

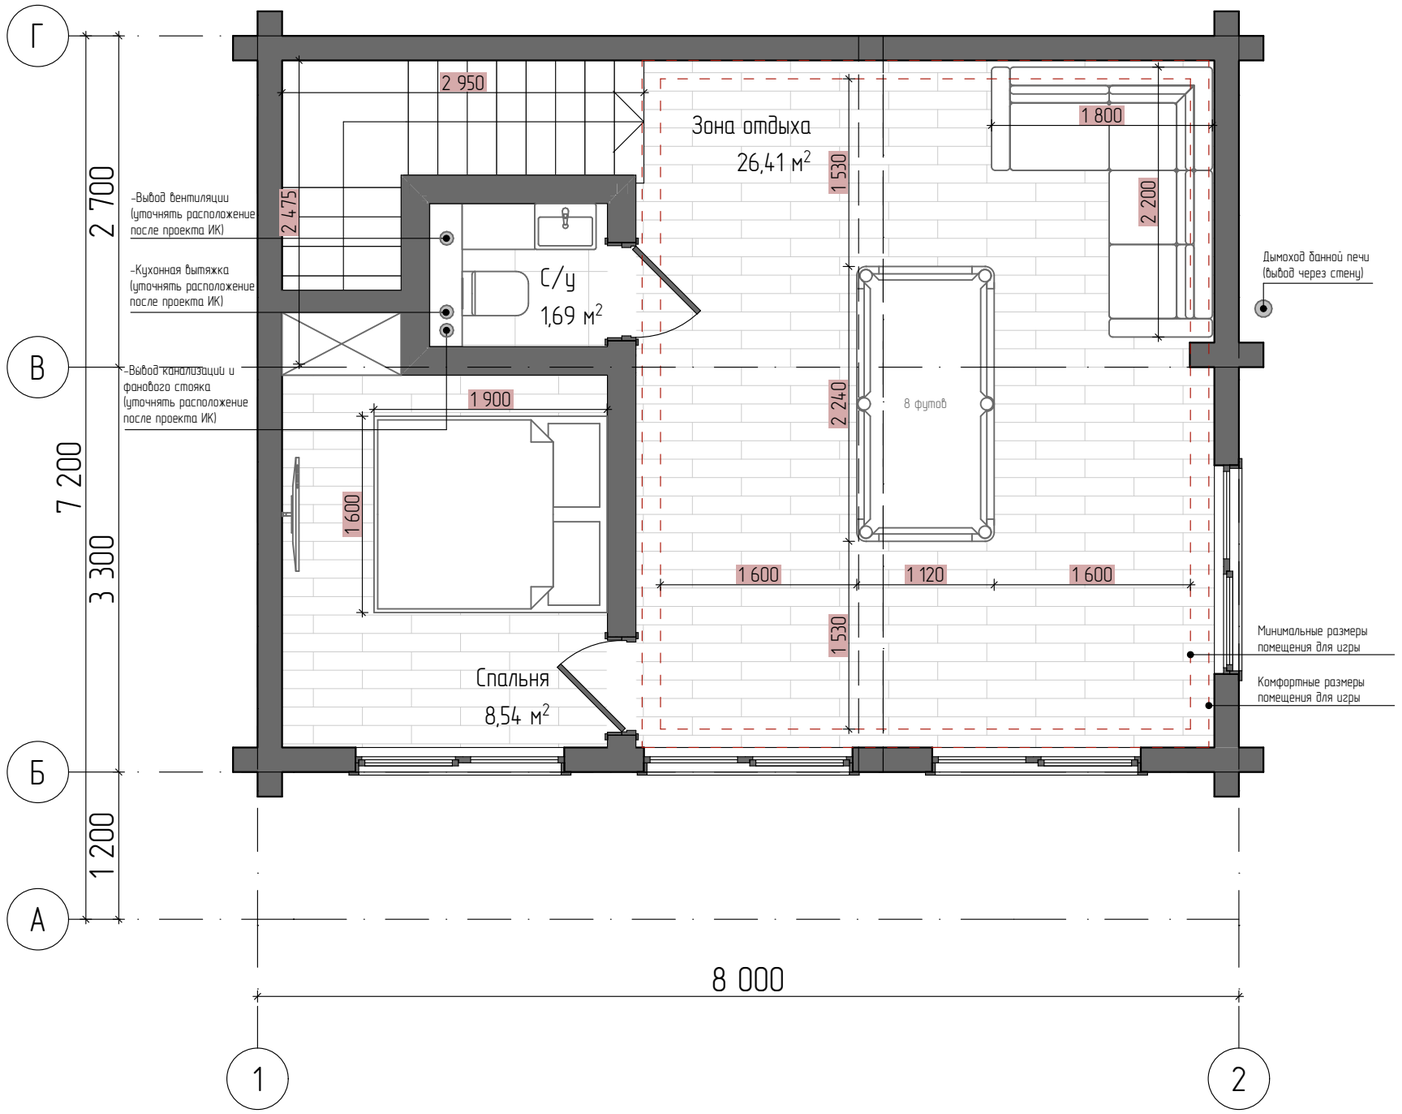


Экспликация 2-й этаж		
№	Название	Площадь
Внутренняя площадь		
1	Зона отдыха	26,41
2	С/у	1,69
3	Спальня	8,54
		36,64 м²

Примечание:

1. Вся индивидуальная мебель выполняется по отдельному проекту с детальной проработкой и калькуляцией. Чертежи предоставляет фирма-изготовитель столярных изделий.
2. Данный проект отдельно согласовывается с автором проекта и непосредственно с заказчиком.
3. Цветовое решение фасада и материалов отделки показаны в проекте приблизительно.
4. Количество ступений показано условно.
5. Расстояние и узлы крепления/проходок смотреть в техническом проекте для установки банной печи.

Изм.	Колуч.	Лист	№Док.	Подп.	Дата.	Двухэтажное здание (баня)	Стадия	Лист	Листов
Разраб.							АР		
ГАП									
Т. контр.						Маркировочный план 2 этажа			
Н. контр.									
Утв.									


Размерный план 1 этажа

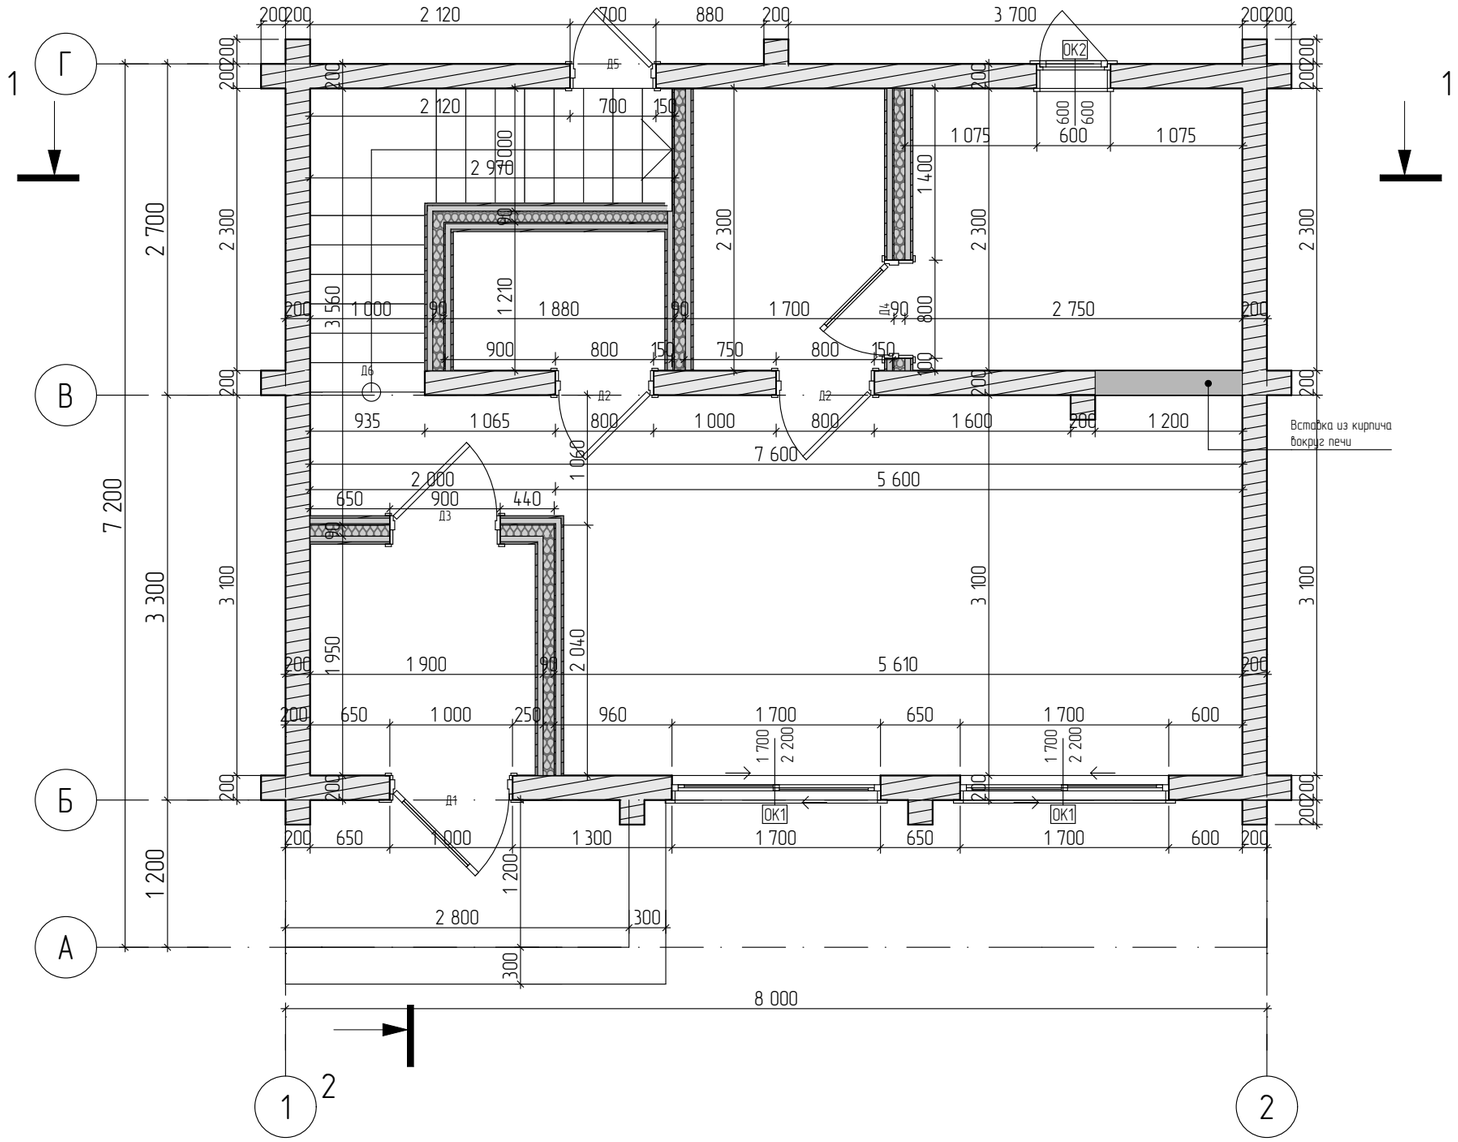

Примечание:
1. Размеры указаны без учета отделки.
2. Спецификацию оконных и дверных проёмов см. 8 лист.

Изм.	Колуч.	Лист	№Док.	Подп.	Дата	Двухэтажное здание (баня)	Стадия	Лист	Листов
Разраб.							АР		
ГАП									
Т. контр.									
Н. контр.						Размерный план 1 этажа			
Утв.									





Размерный план 2 этажа


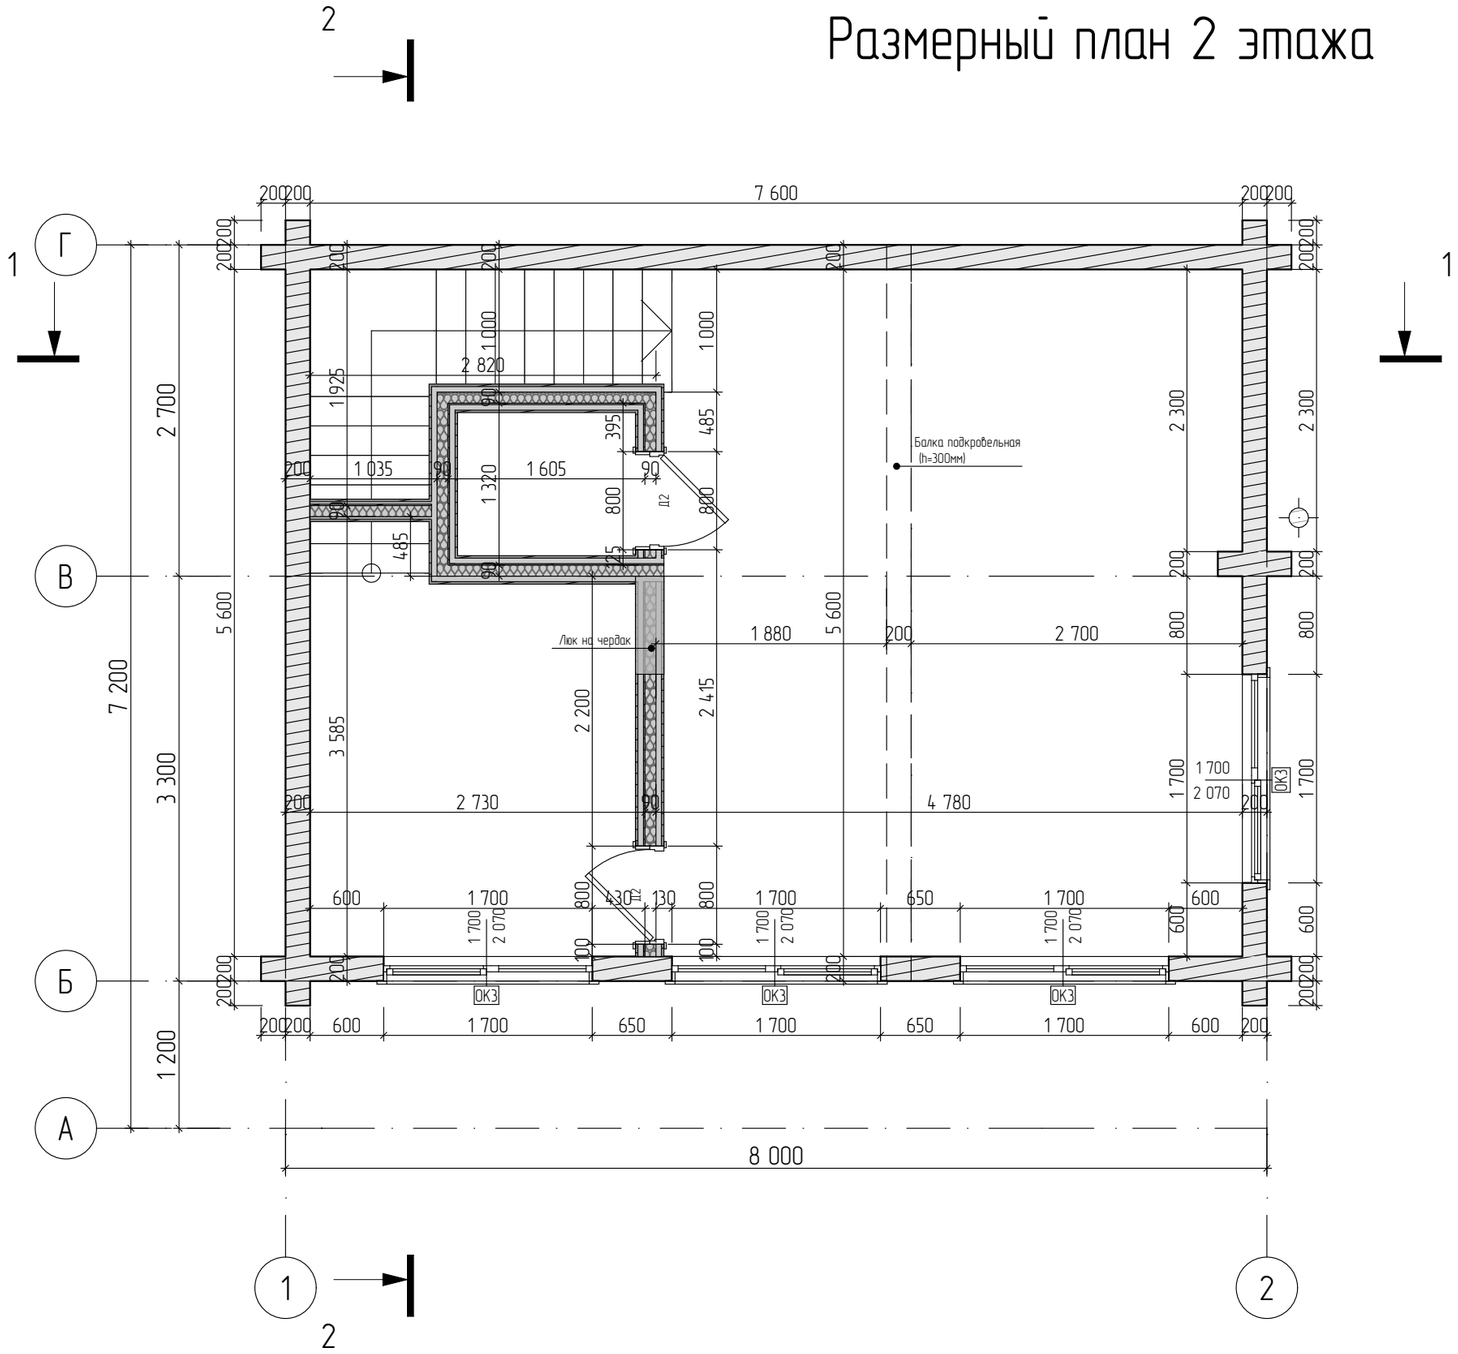


Примечание:
1. Размеры указаны без учета отделки.
2. Спецификацию оконных и дверных проёмов см. 8 лист.

Изм.	Колуч.	Лист	№Док.	Подп.	Дата.	Двухэтажное здание (баня)	Стадия	Лист	Листов
Разраб.							АР		
ГАП									
Т. контр.						Размерный план 2 этажа			
Н. контр.									
Утв.									

Ведомость заполнения оконных проемов

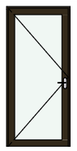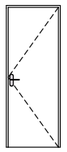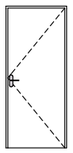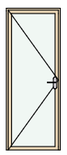Ведомость заполенения дверных проемов					
Название	Размер проема Ш х В, мм	Кол-во, шт	Вид	Ориентация	Площадь
Д1	1 000×2 200	1		Л	2,20
Д2	800×2 100	4		П	1,68
Д3	900×2 100	1		П	1,89
Д4	800×2 100	1		Л	1,68
Д5	700×1 600	1		Л	1,12
Д6	1 035×2 700	1			2,79
					16,40 м²

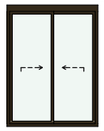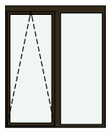
Ведомость заполнения оконных проемов					
Название	Размер проема Ш х В, мм	Кол-во, шт	Вид	Ориентация	Площадь
ОК1	1 700×2 270	2			3,86
ОК2	600×670	1		Л	0,40
ОК3	1 700×2 070	4			3,52
					22,20 м²

Примечание:


1. Изготовление окон и дверей определяется заказчиком, допускается изменение открывания окон и дверей;
2. При заказе оконных и дверных блоков необходим обмер по месту от изготовителя;
3. Оконные и дверные изделия изображены со стороны открывания.
4. В окнах предусмотреть теплоизоляцию компенсационного зазора 70мм

Изм.	Колуч.	Лист	№Док.	Подп.	Дата	Двухэтажное здание (баня)	Стадия	Лист	Листов
Разраб.							АР		
ГАП									
Т. контр.						Ведомость заполнения оконных проемов			
Н. контр.									
Утв.									

3д-вид

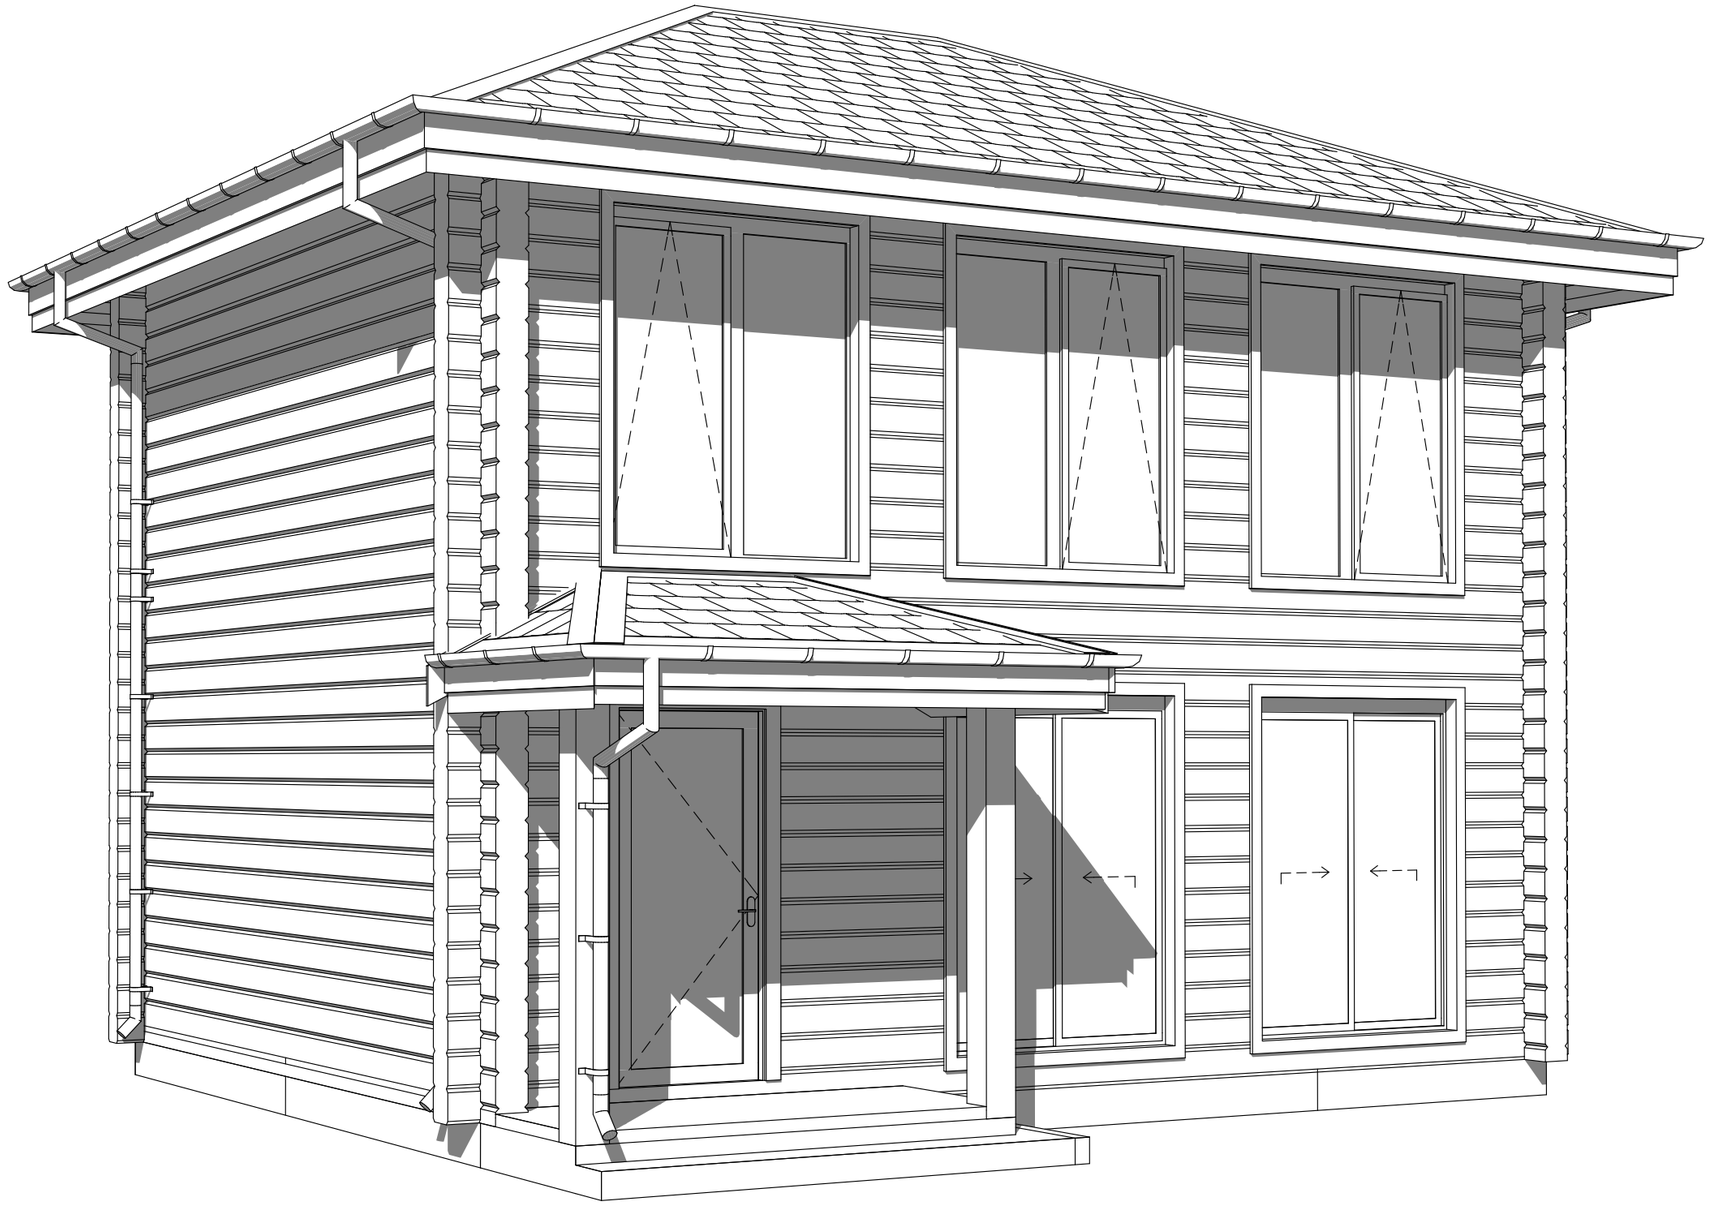

Изм.	Колуч.	Лист	№Док.	Подп.	Дата.	Двухэтажное здание (баня)	Стадия	Лист	Листов
Разраб.							АР		
ГАП									
Т. контр.									
Н. контр.						3д-вид			
Утв.									

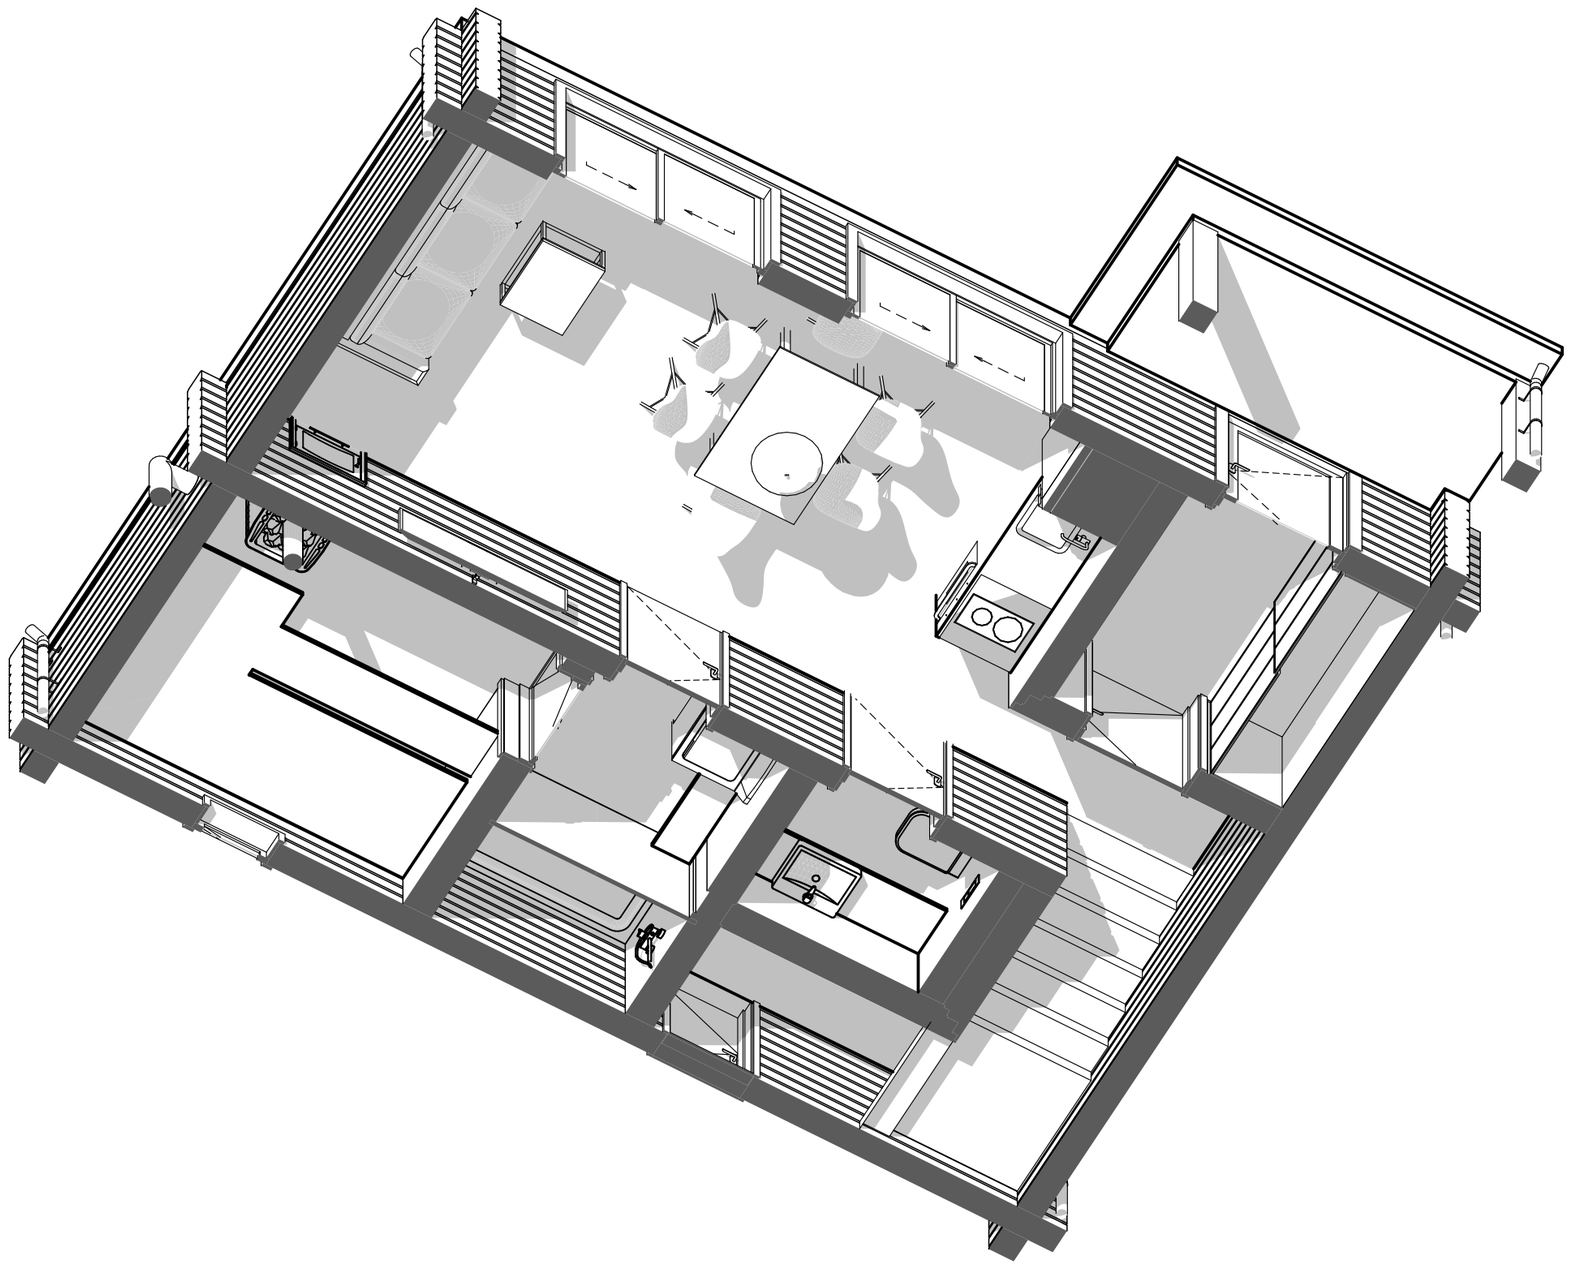

3д-бud 1 эпджд


Изм.	Кол.уч.	/lucm	№flok	Подп.	Дата

Разраб.			
ГАП			
Т. контр.			
Н. контр.			
Утб.			

Дцухэтпджное здание (бокд)

Стадия	/lucm	/lucmob
АР		

3д-бud 1 эпджд

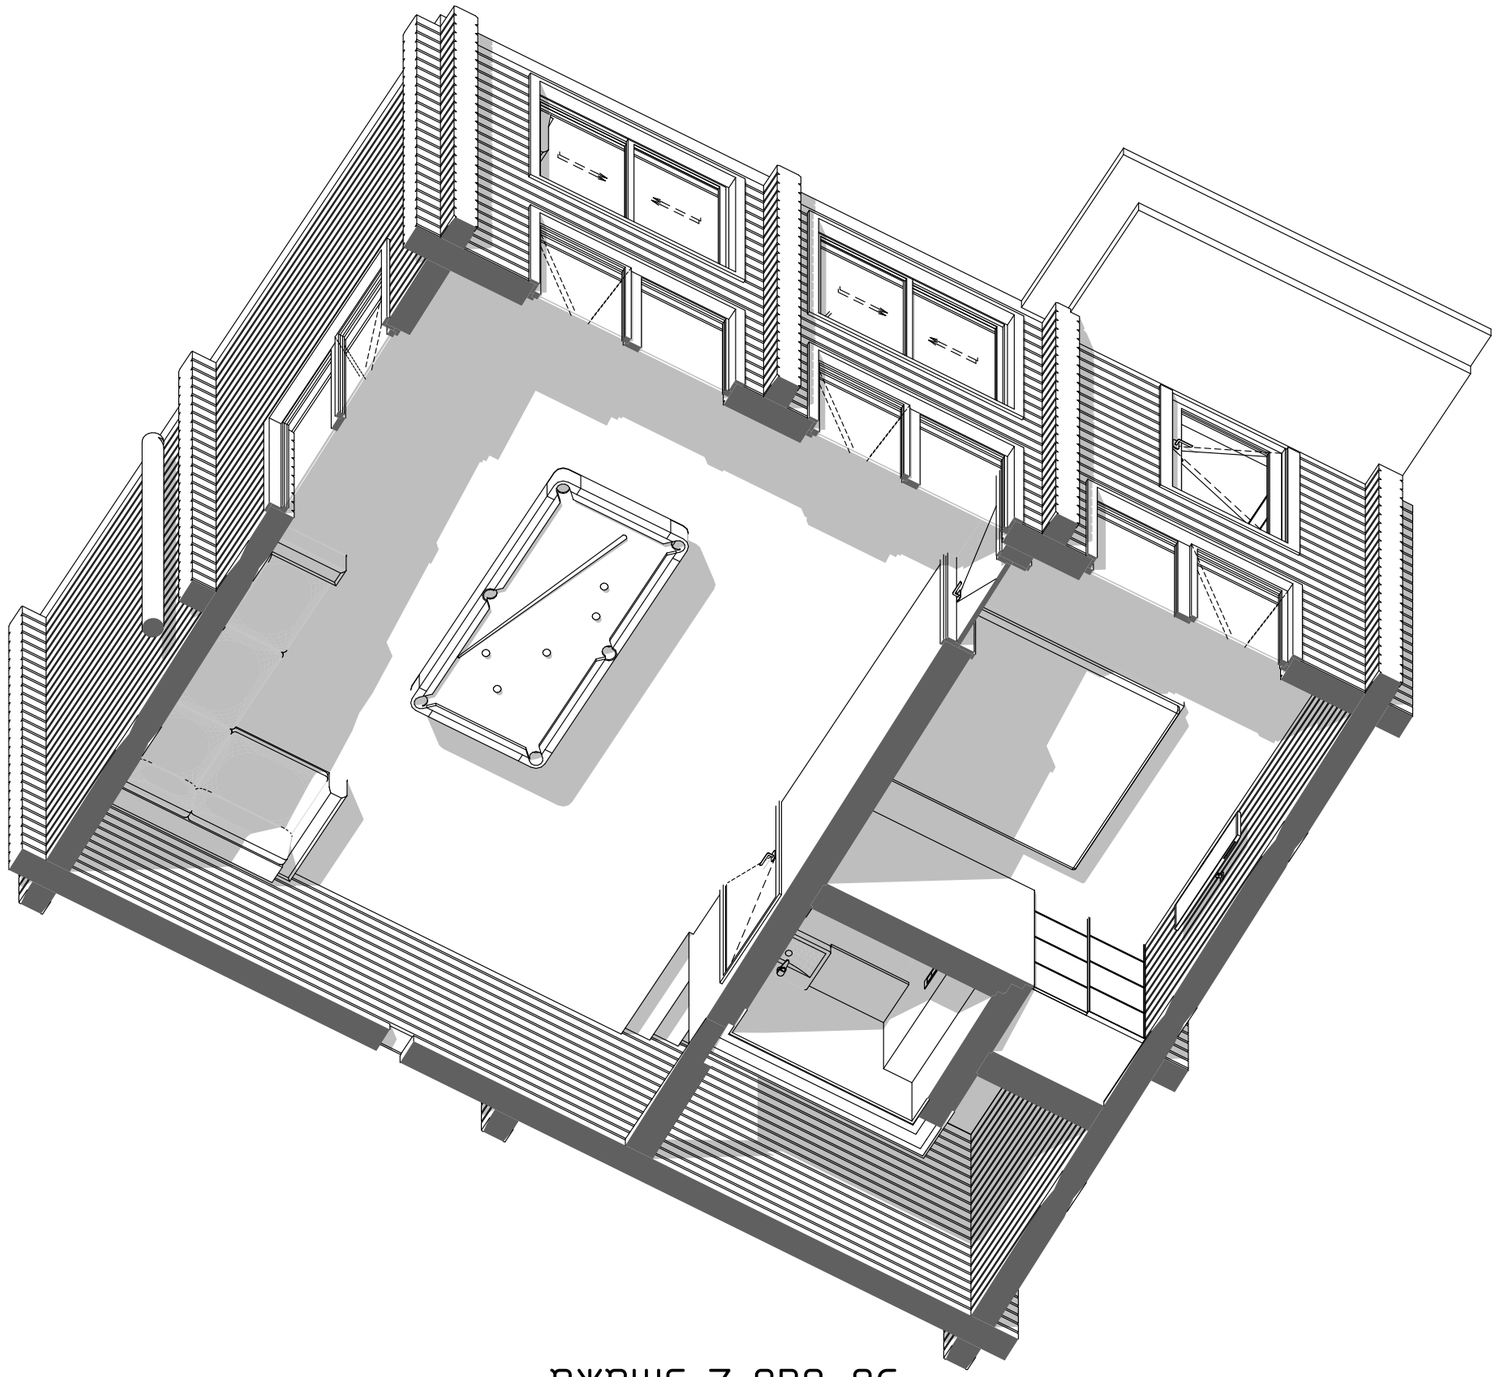

3д-бud 2 эπαжα

Изм.	Кол.уч.	/lucm	№док.	Подп.	Дата


Разраб.			
ГАП			
Т. контр.			
Н. контр.			
Утв.			

Дцухэтπажное зδанuе (δоκа)

Стадия	/lucm	/lucmoδ
АР		

3д-бud 2 эπαжα

План внутренней отделки 1 этажа

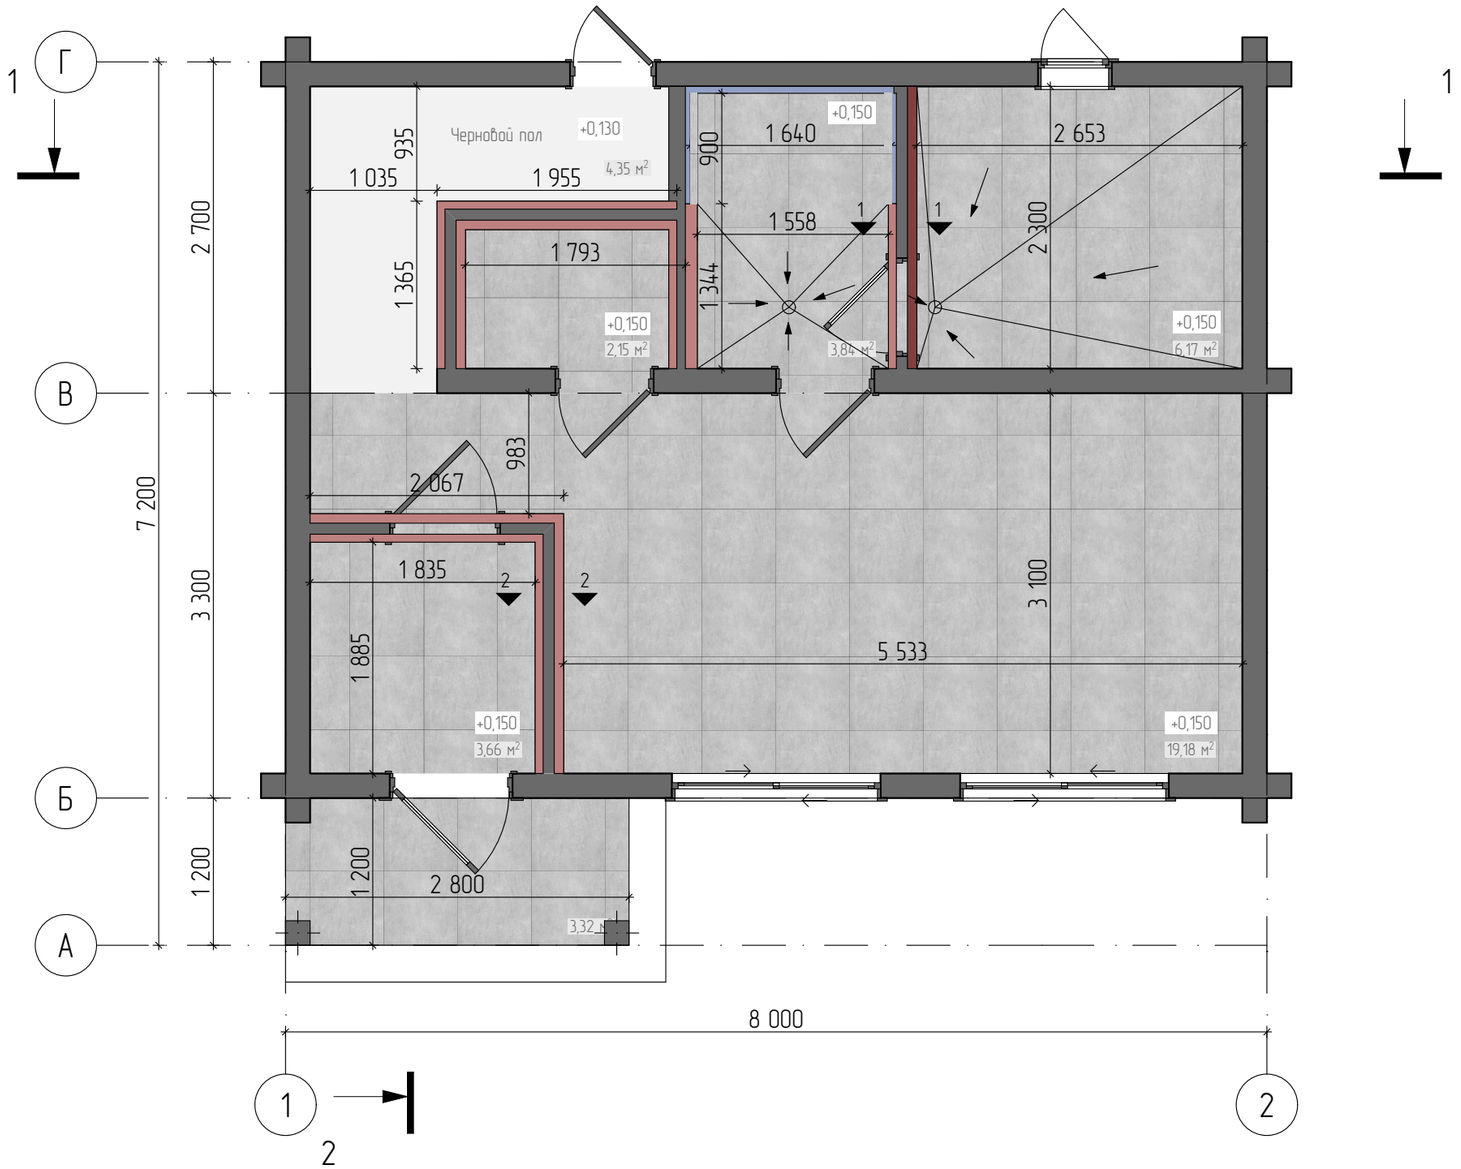

Отделка стен:


- Вагонка
  - Вентзазор – брусок 45х45мм
  - Пароизоляция (алюм.фольга)
  - ОСП 12мм
- Керамогранит 10мм
  - Клей
  - Руспанель 6мм
  - ОСП 9мм
  - Пароизоляция
- Имитация бруса
  - Вентзазор – брусок 45х45мм
  - Пароизоляция
  - ОСП 12 мм

Отделка пола:


- Керамогранит 10мм
  - Клей
  - ЦПС 80мм
  - ЭППС 50мм

(*предусмотреть разуклонку в мокрых зонах)

Сечение 1–1

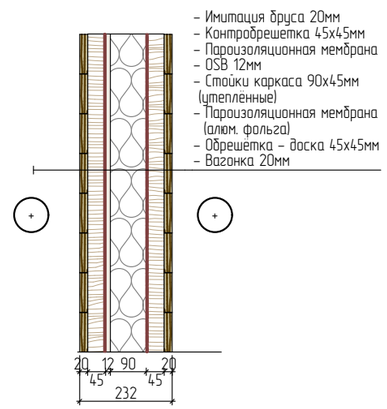


Сечение 2–2

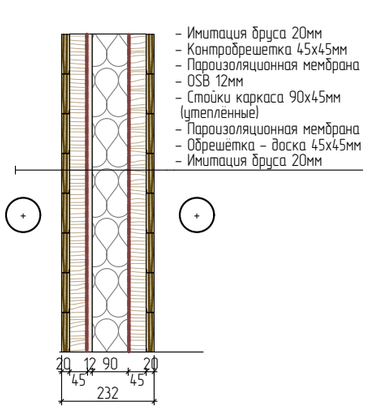

Изм.	Колуч.	Лист	№Док.	Подп.	Дата	Двухэтажное здание (баня)	Стадия	Лист	Листов
Разраб.							АР		
ГАП									
Т. контр.						План внутренней отделки 1 этажа			
Н. контр.									
Утв.									

План внутренней отделки 2 этажа

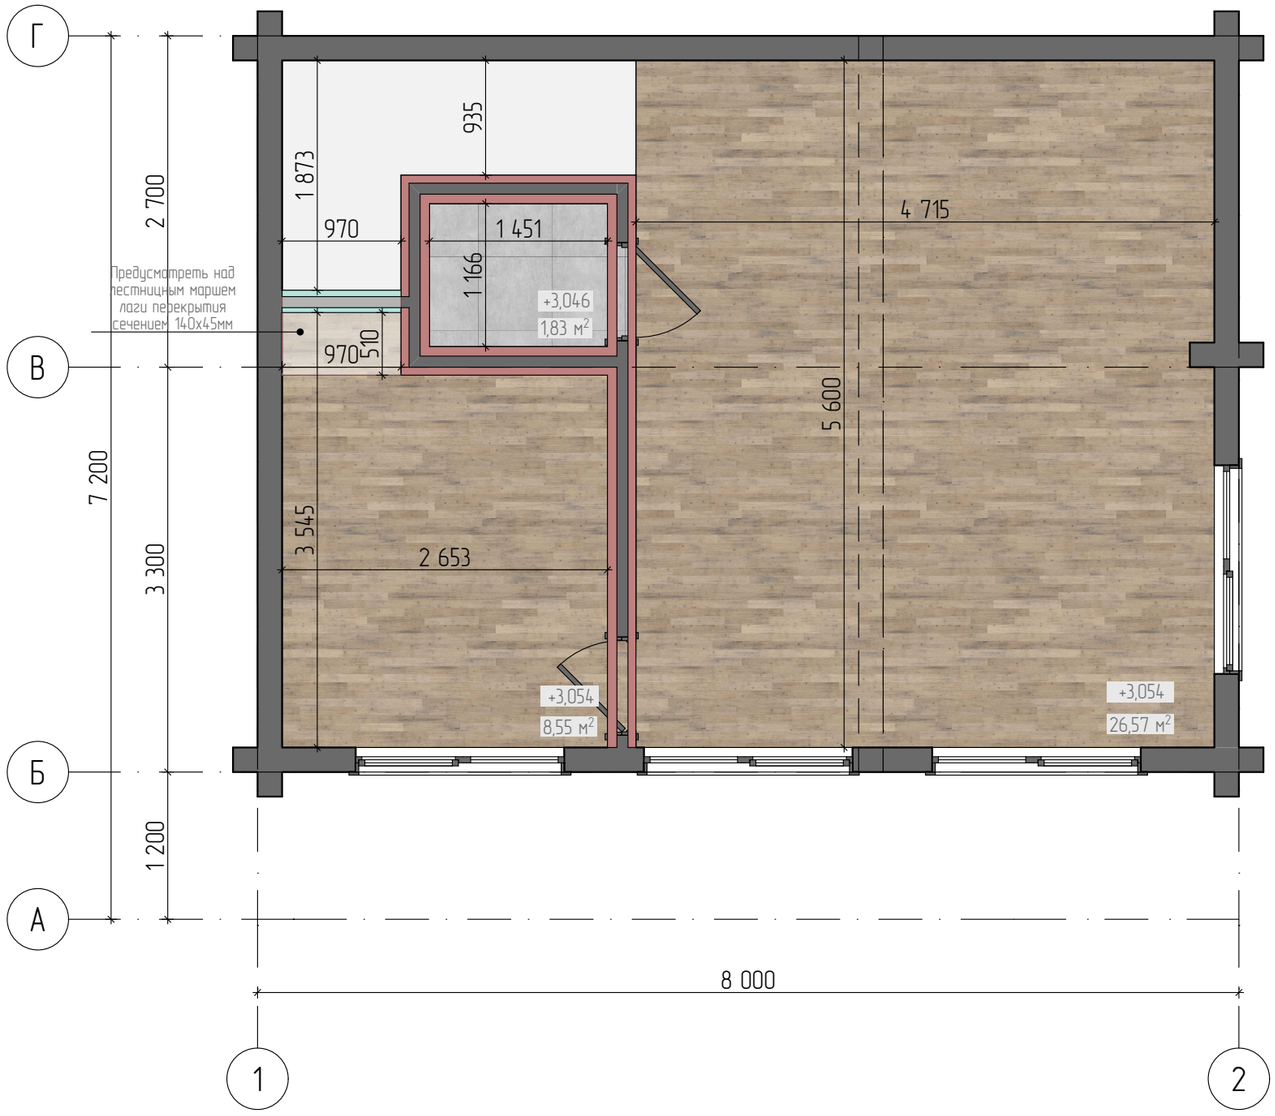

Отделка стен:


- Имитация бруса 20мм
  Вентзазор – брусок 45х45мм
  Пароизоляция
  ОСБ 12мм
- Имитация бруса 20мм
  Вентзазор – брусок 20х90мм
  Пароизоляция
  ОСБ 12мм

Отделка пола:

- Керамогранит 10мм
  Клей 10мм
  Руспанель 6мм
  ОСП 10мм
  ЦСП 20мм
  Пароизоляция
- Ламинат 10мм
  Подложка под ламинат 4мм
  ОСП 10мм
  ЦСП 20мм
  Вентзазор – брусок 20х40мм
  Пароизоляция

Изм.	Колуч.	Лист	№Док.	Подп.	Дата	Двухэтажное здание (баня)	Стадия	Лист	Листов
Разраб.							АР		
ГАП									
Т. контр.						План внутренней отделки 2 этажа			
Н. контр.									
Утв.									

План электрооборудования

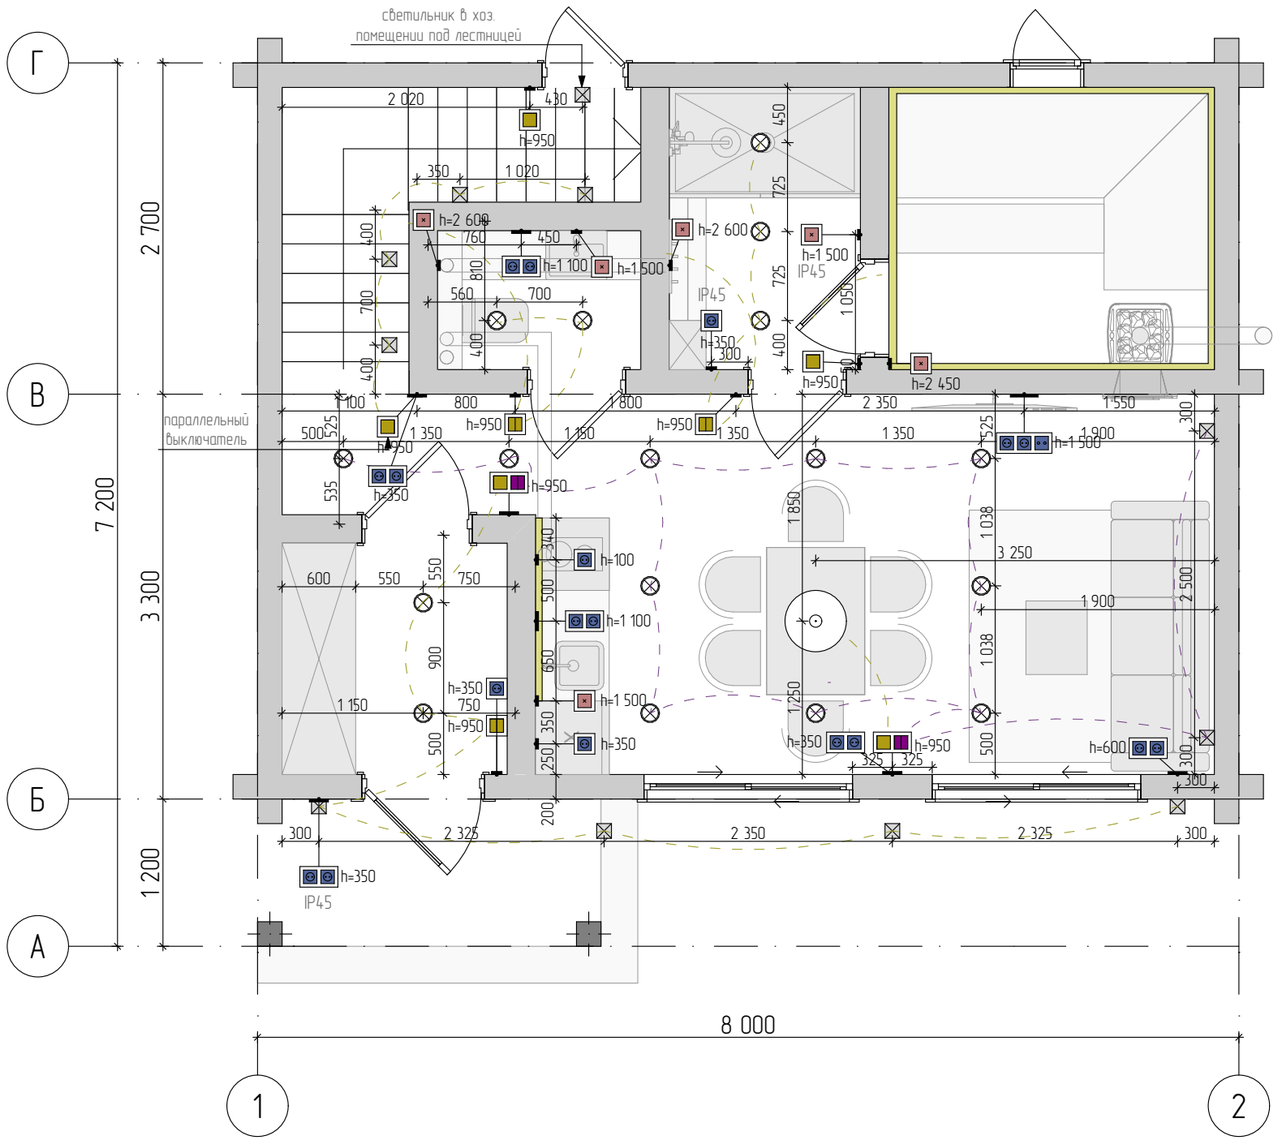


Спецификация электрооборудования		
2D-вид	Тип оборудования	Кол-тво, шт.
	Светильник подвесной	5
	Светильник точечный	30
	Светильник настенный	7
	Уличный светильник	4
	Выключатель двухклавишный (1 секция)	5
	Выключатель одно- и двухклавишный (2 секции)	4
	Выключатель одноклавишный (рамка 1 секция)	3
	Эл. вывод	7
	Розетка 220v (2 секции)	12
	Розетка 220v +тв розетка (3 секции)	2
	Розетка 220v (1 секция)	4
		83

Примечание:

1. Схема размещения розеток является рекомендательной и требует согласования с заказчиком по месту.
2. Все высоты даны от чистового пола 1 этажа.
3. Все указанные размеры даются до центра позиций.
4. Отметки розеток, выключателей, выводов и др. оборудования, являются предварительными и уточняются после выбора финишных материалов и мебели.
5. Размеры уточняются дополнительно

Изм.	Колуч.	Лист	№Док.	Подп.	Дата	Двухэтажное здание (баня)	Стадия	Лист	Листов
Разраб.							АР		
ГАП									
Т. контр.						План электрооборудования 1 этажа			
Н. контр.									
Утв.									

План электрооборудования

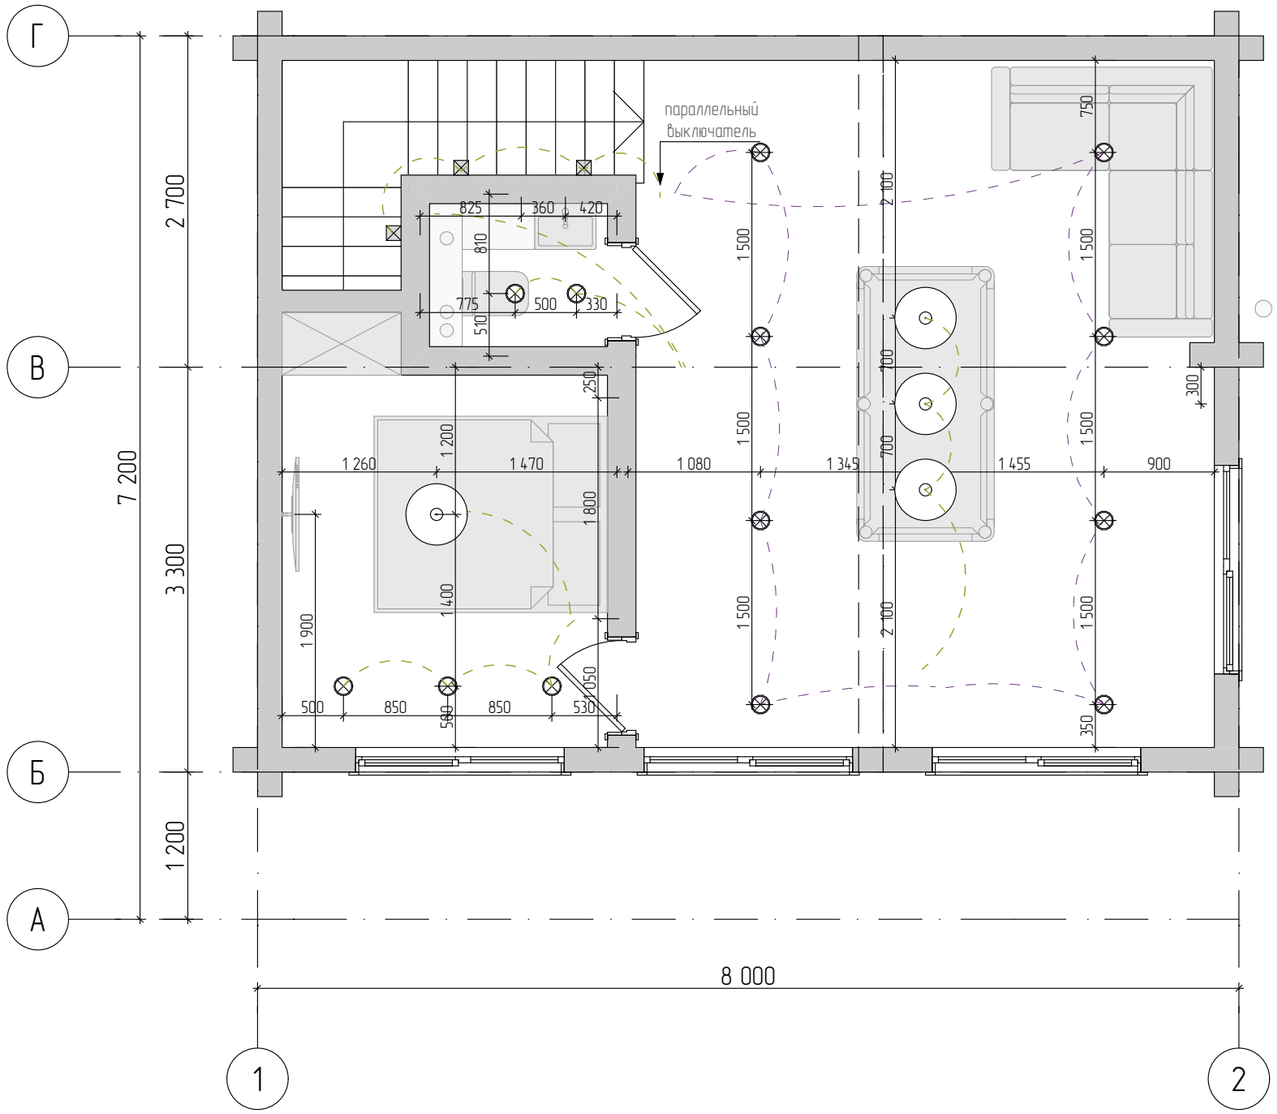


Спецификация электрооборудования		
2D-вид	Тип оборудования	Кол-тво, шт.
	Светильник подвесной	5
	Светильник точечный	30
	Светильник настенный	7
	Уличный светильник	4
	Выключатель двухклавишный (1 секции)	5
	Выключатель одно- и двухклавишный (2 секции)	4
	Выключатель одноклавишный (рамка 1 секции)	3
	Эл. вывод	7
	Розетка 220v (2 секции)	12
	Розетка 220v +тв розетка (3 секции)	2
	Розетка 220v (1 секции)	4
		83

Примечание:

1. Схема размещения розеток является рекомендательной и требует согласования с заказчиком по месту.
2. Все высоты даны от чистового пола 2 этажа.
3. Все указанные размеры даются до центра позиций.
4. Отметки розеток, выключателей, выводов и др. оборудования, являются предварительными и уточняются после выбора финишных материалов и мебели.
5. Размеры уточняются дополнительно

Изм.	Колуч.	Лист	№Док.	Подп.	Дата				
Разраб.						Двухэтажное здание (баня)	Стадия	Лист	Листов
ГАП							АР		
Т. контр.						План электрооборудования 2 этажа			
Н. контр.									
Утв.									


План крыши

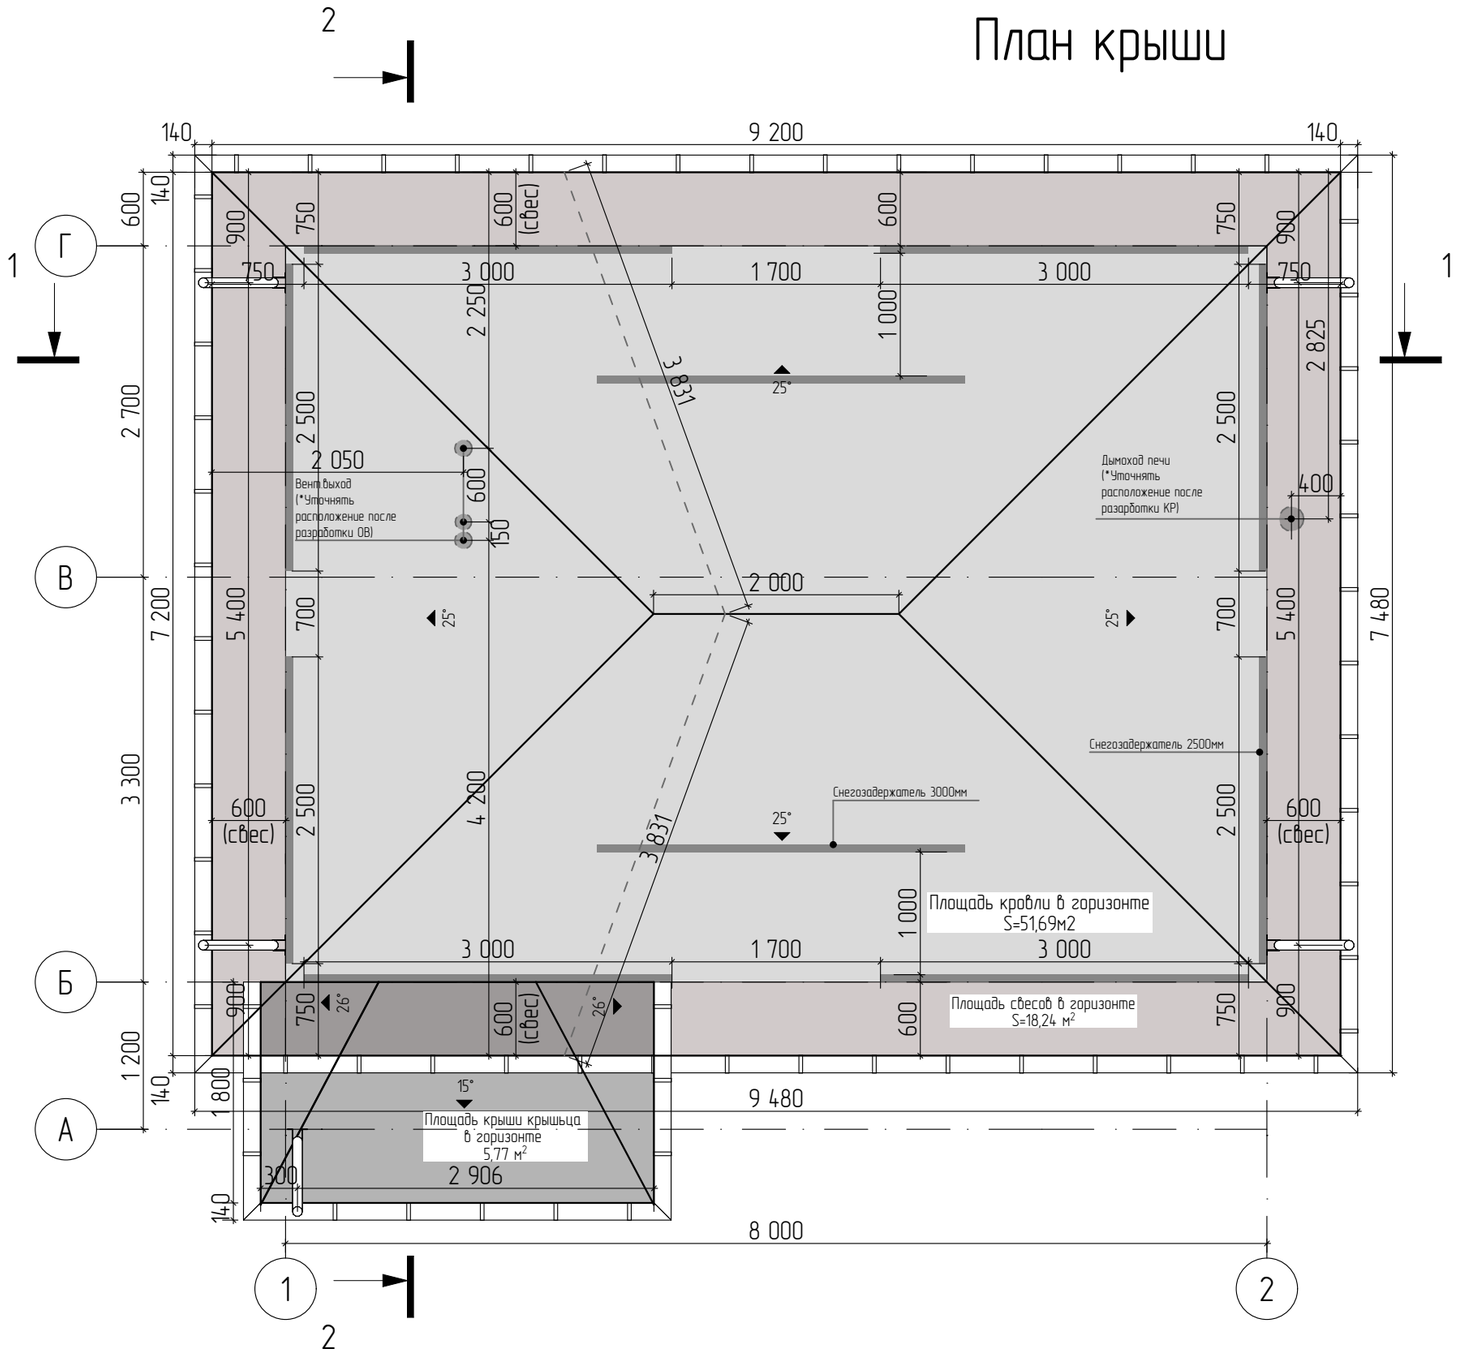

Примечание:
1. Фановый стояк располагать не менее чем в 1м от вытяжной вентиляции.


Изм.	Колуч.	Лист	№Док.	Подп.	Дата	Двухэтажное здание (баня)	Стадия	Лист	Листов
Разраб.							АР		
ГАП									
Т. контр.						План крыши			
Н. контр.									
Утв.									

Разрез 1-1

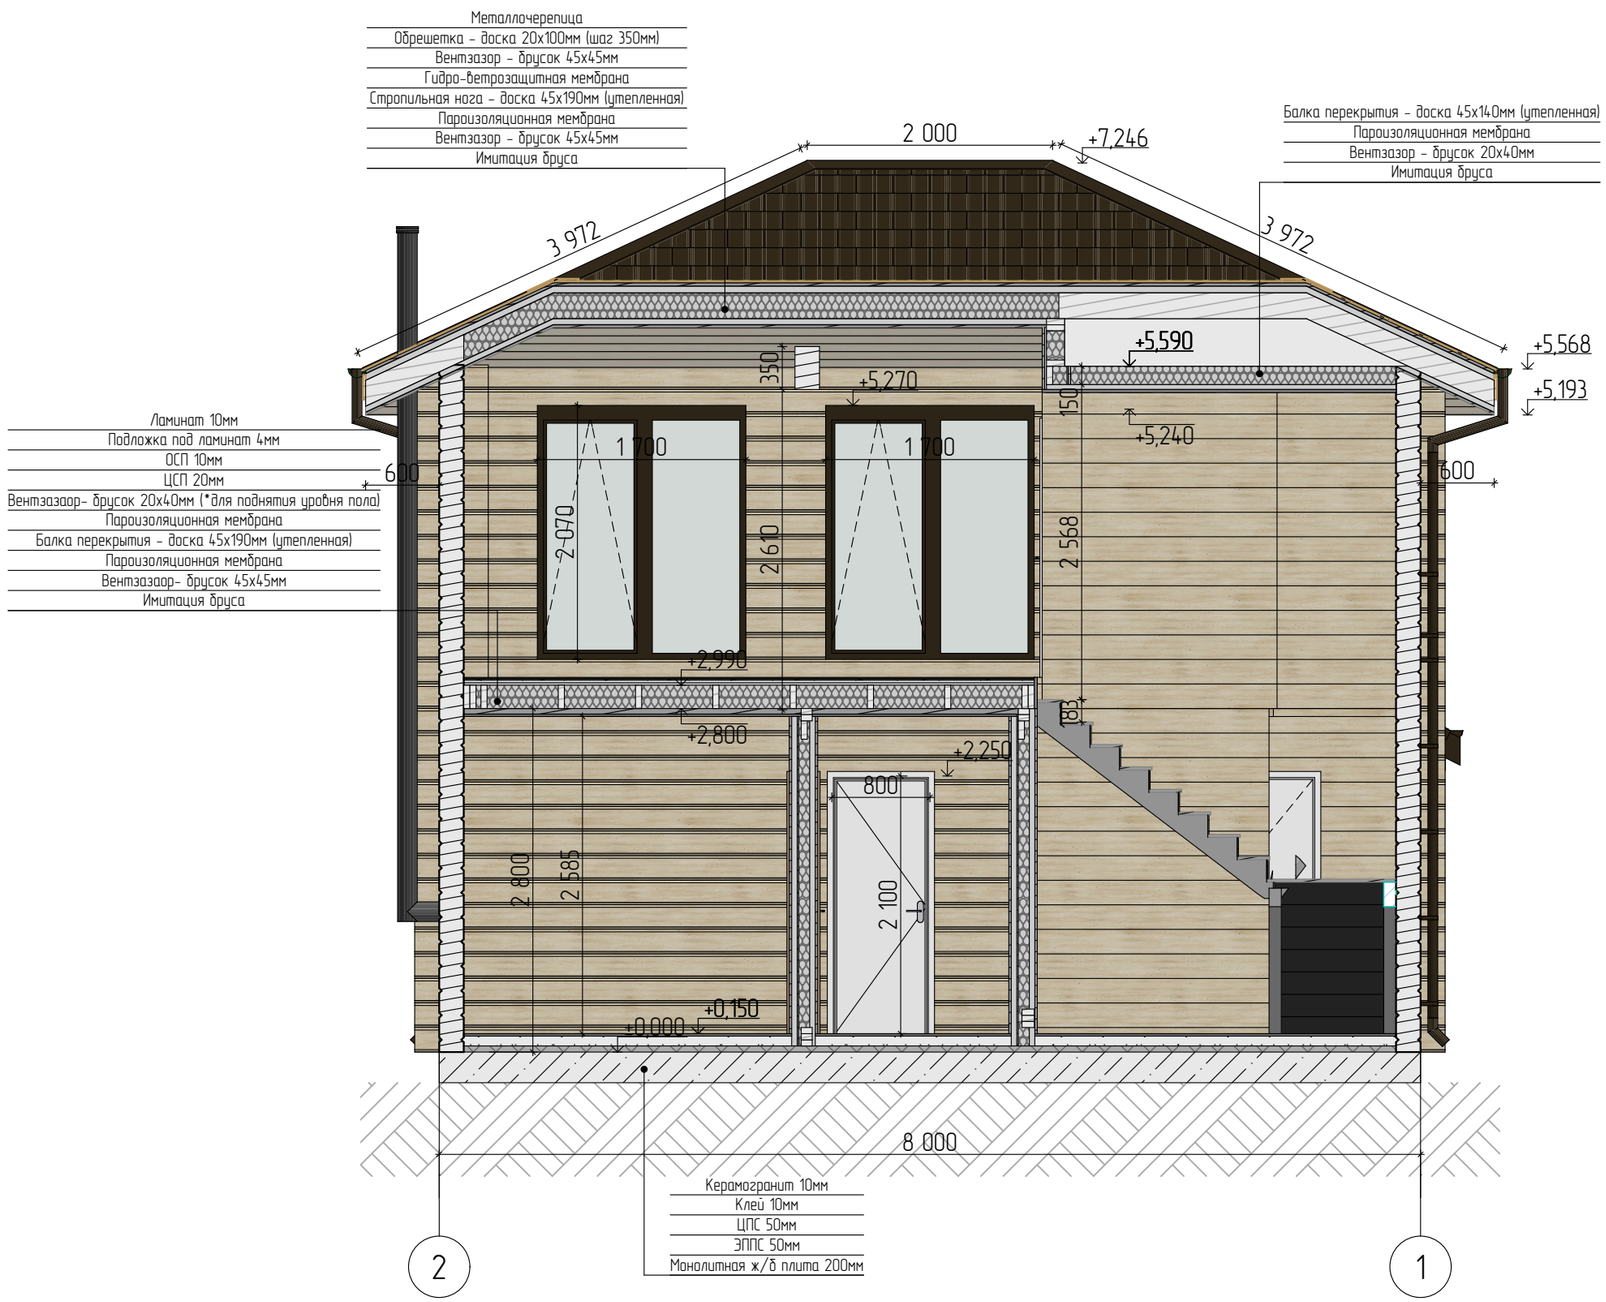

Изм.	Колуч.	Лист	№Док.	Подп.	Дата	Двухэтажное здание (баня)	Стадия	Лист	Листов
Разраб.							АР		
ГАП									
Т. контр.						Разрез 1-1			
Н. контр.									
Утв.									


Разрез 2-2

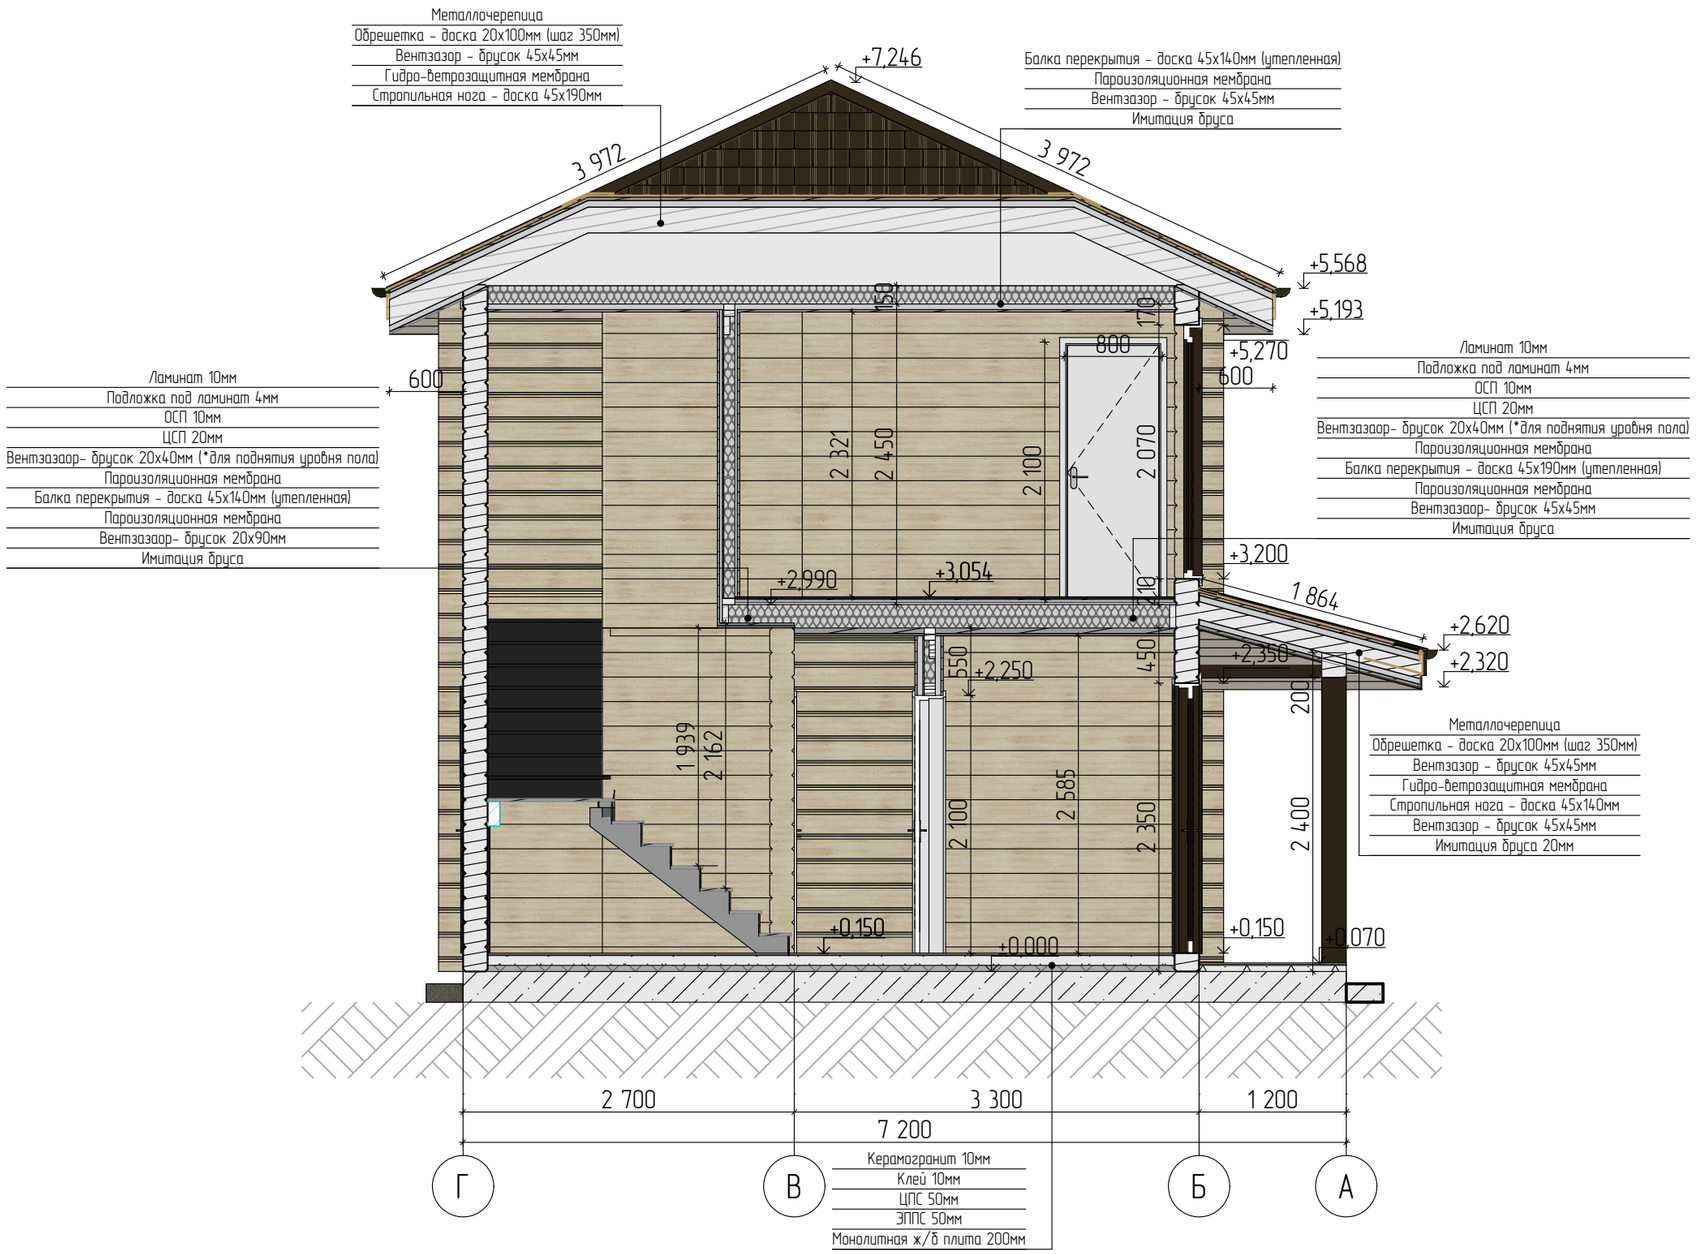

Изм.	Колуч.	Лист	№Док.	Подп.	Дата.	
Разраб.						
ГАП						
Т. контр.						
Н. контр.						
Утв.						

Двухэтажное здание (баня)	Стадия	Лист	Листов
	АР		
Разрез 2-2			

Фасад 1-2

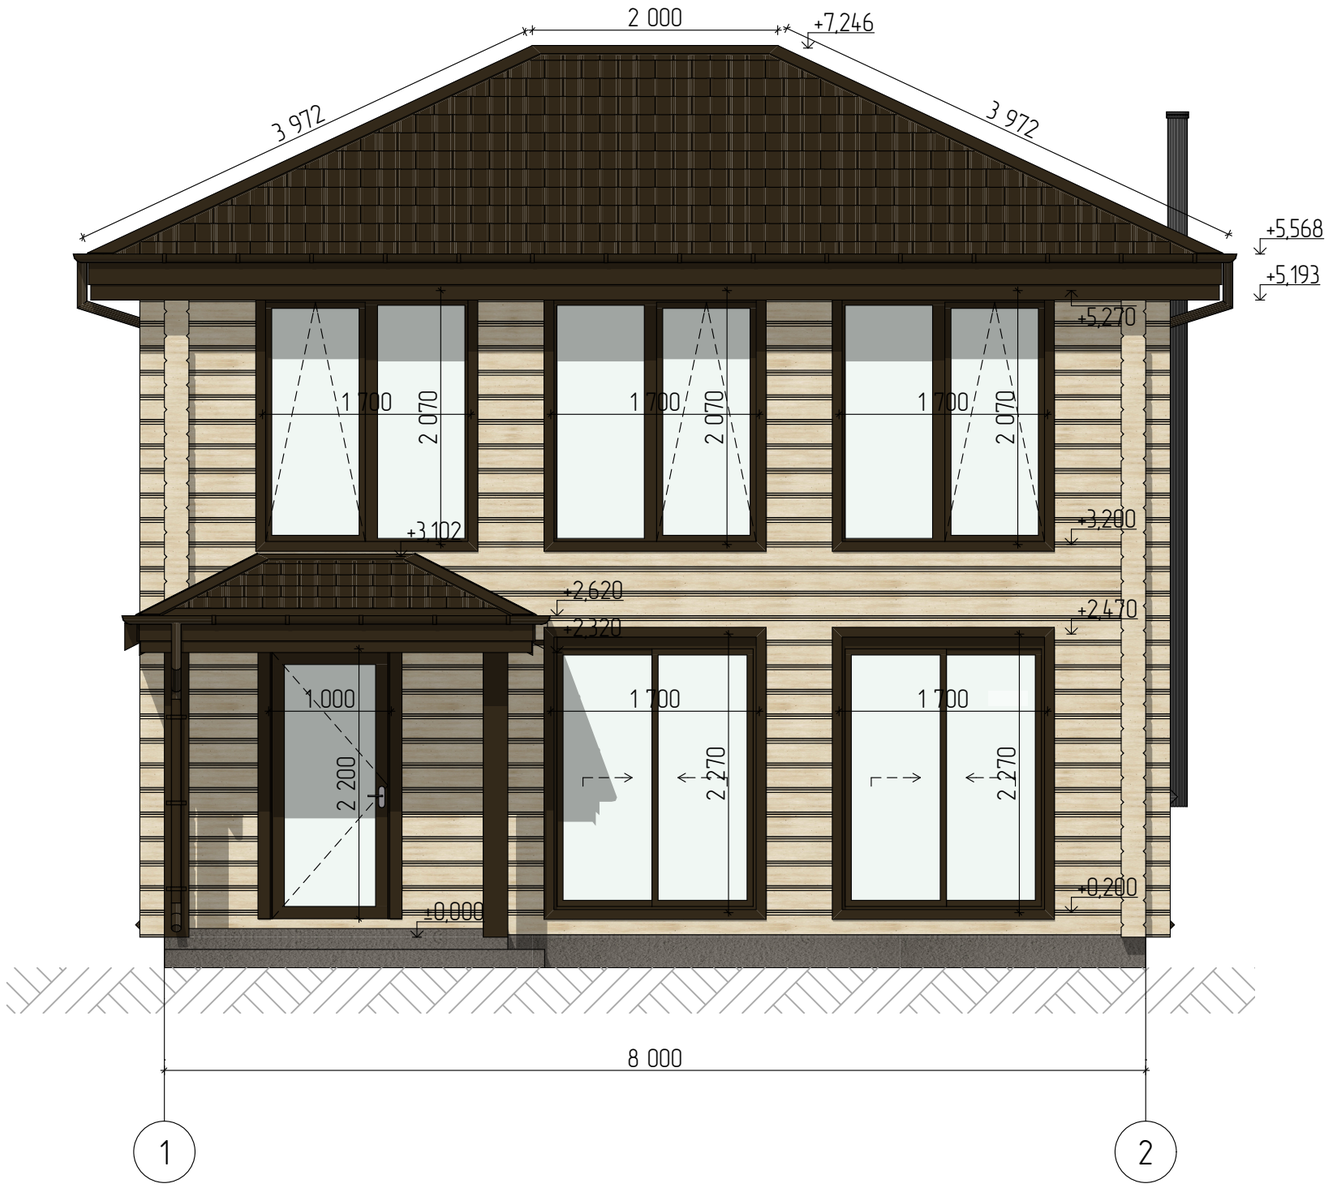


Условныеи обозначсение:


–Металлочерепица, лобовая доска, водосточная система, рамы, наличники

–Клееный брус

Изм.	Колуч.	Лист	№Док.	Подп.	Дата.	Двухэтажное здание (баня)	Стадия	Лист	Листов
Разраб.							АР		
ГАП									
Т. контр.									
Н. контр.						Фасад 1-2			
Утв.									


Фасад А-Г, Фасад Г-А

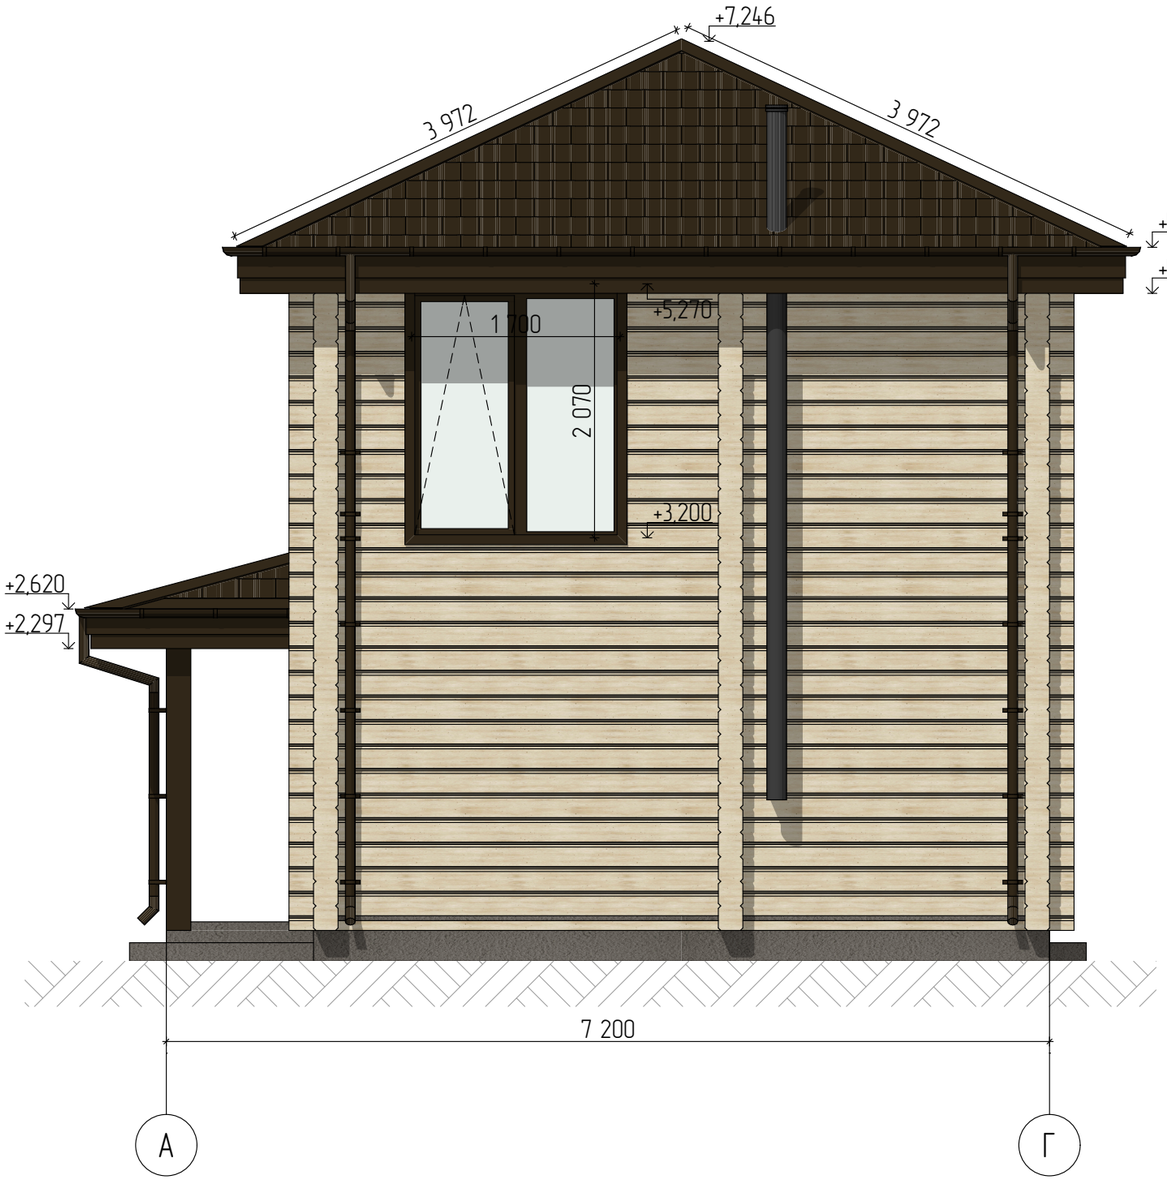

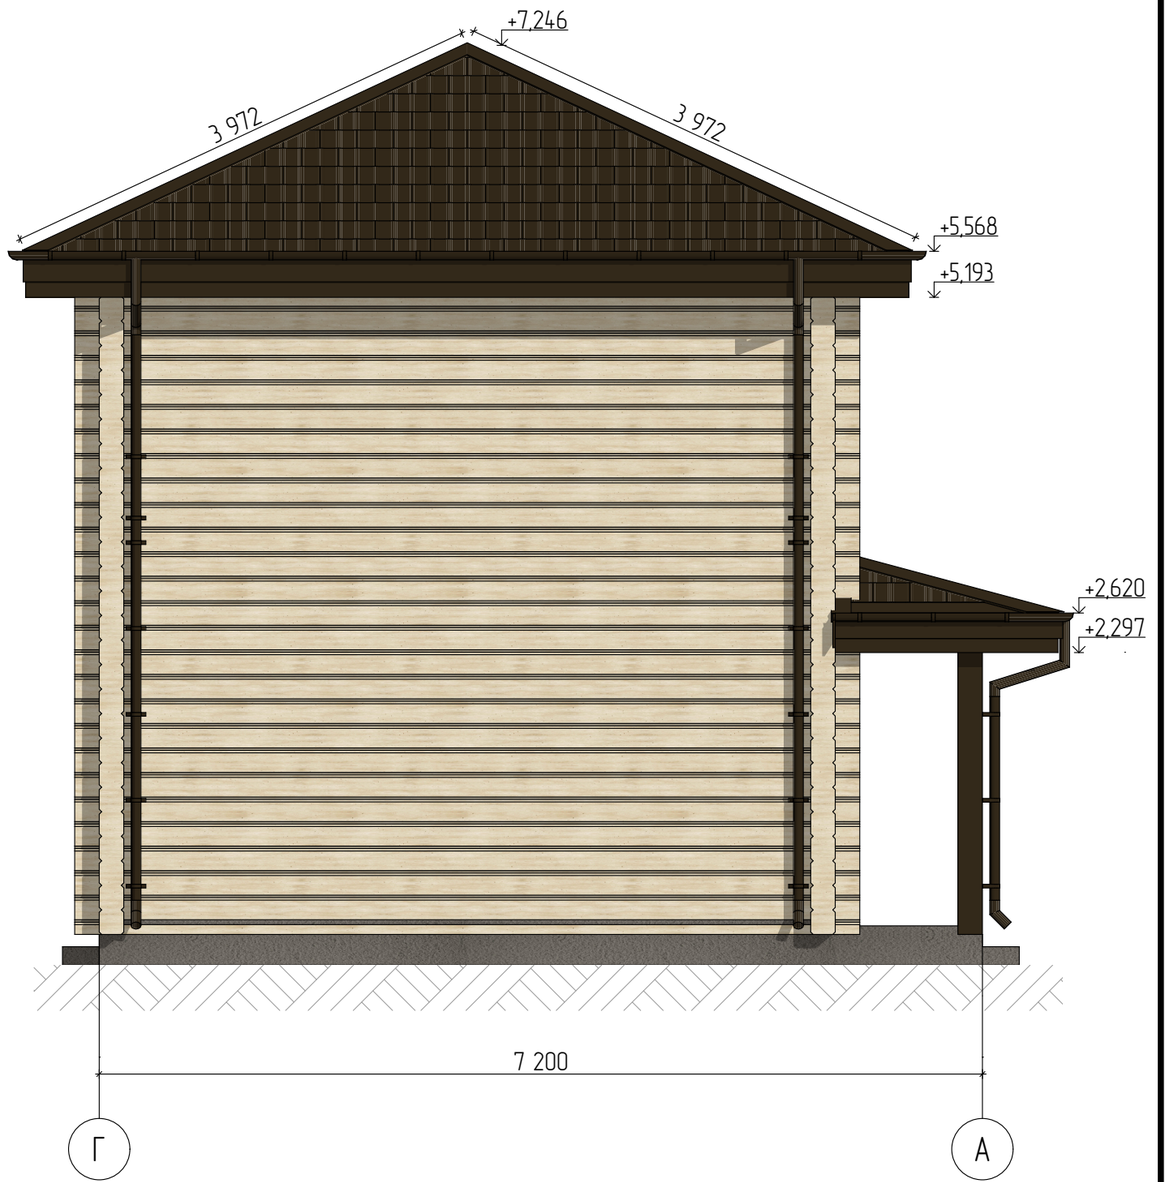

Изм.	Колуч.	Лист	№Док.	Подп.	Дата	Двухэтажное здание (баня)	Стадия	Лист	Листов
Разраб.							АР		
ГАП									
Т. контр.						Фасад А-Г, Фасад Г-А			
Н. контр.									
Утв.									

Фасад 2-1

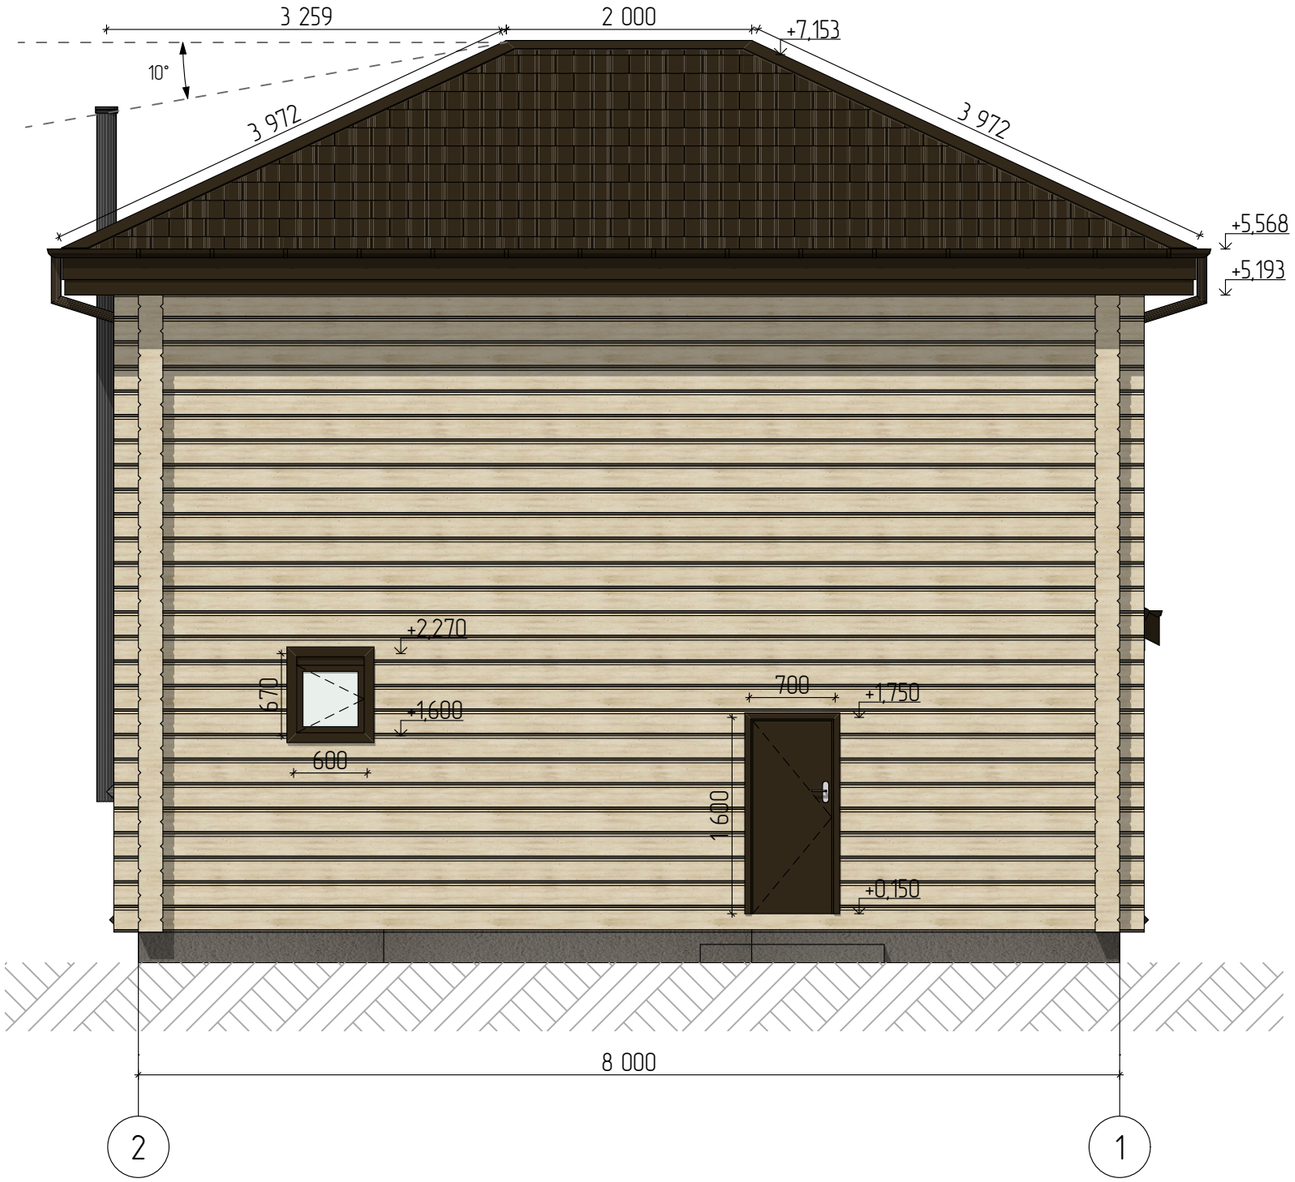

Условныеи обозначсение:

-Металлочерепица, лобовая доска, водосточная система, рамы, наличники

-Клееный брус

Изм.	Колуч.	Лист	№Док.	Подп.	Дата.	Двухэтажное здание (баня)	Стадия	Лист	Листов
Разраб.							АР		
ГАП									
Т. контр.									
Н. контр.						Фасад 2-1			
Утв.									