Рабочая документация

Архитектурные решения
(раздел АР)
Одноэтажное здание
(баня)
Основной комплект
чертежей (планы,
разрезы, фасады)

Архитектор _____ _____

Заказчик _____ _____

Москва
2026

Общие данные:

1. Проект двухэтажной бани, выполнен индивидуально на основании исходных данных представленных заказчиком.
2. Состав пирогов конструкций предусматривает его круглогодичную эксплуатацию.
Размеры строения 8,75х17,815м в осях
За относительную отметку ±0.000 принять уровень верха ж/б монолитной плиты.

3. Адрес строительства:

1. Чертежи разработаны на основании задания на проектирование.

2. Объект строительства расположен в следующих климатических зонах:
- Нормальный вес снегового покрова для III района - Sg=1,5 кН/м2;
- Нормальное ветровое давление для I района - 23 кгс/м2;
- Расчётная зимняя температура для наружного воздуха - минус 26°С;
- Нормативная глубина промерзания грунта - 1,4 м;
- Полезная нагрузка на покрытие - 150 кгс/м2.

3. Общая характеристика:
- Уровень ответственности - нормальный.
- Класс сооружения - КС-2
- Категория здания по взрывопожарной и пожарной опасности - В.
- Класс функциональной пожарной опасности здания - Ф 1.4.
- Степень огнестойкости - III.
- Класс конструктивной пожарной опасности здания - С1
- Класс пожарной опасности строительных конструкций -К3.
- Зона влажности - нормальный.
- Расчётная температура наружного воздуха наиболее холодной пятидневки: -29°С.

4. Конструктивно, строение представляет собой сооружение с плитным монолитным фундаментом, несущими каркасом из монолитных колонн с заполнением газоблоком, кровлей по деревянным стропилам.

5. При проведении строительных работ необходимо осуществлять технический надзор с ведением журнала работ.
Осуществлять входной контроль материалов, вести приёмку по каждому этапу работ.

6. Описание конструкций строения:
- Фундамент - Ж/б монолитная плита h=200мм с ребрами жесткост h=400мм
- Несущие конструкции - монолитные колонны с заполнением газоблоком
- Стропильная система - из строганой доски сечением 195(h)х40мм, уточняется в разделе КР
- Кровля - односкатная;
- Покрытие кровли - металлочерепица;

Изм.	Колуч.	Лист	№Док.	Подп.	Дата	Двухэтажное здание (баня)	Стадия	Лист	Листов
Разраб.							П		
Пров.									
Т. контр.									
Н. контр.						Пояснительная записка			
Утв.									

Лист	Наименование
1	Титульный
2	Пояснительная записка
3	Состав чертежей
4	Маркировочный план 1 этажа
5	Размерный план 1 этажа
6	3д-разрез 1 этажа
7	Маркировочный план 2 этажа
8	Размерный план 2 этажа
9	3д-разрез 2 этажа
10	Ведомость заполнения оконных проемов
11	Ведомость заполнения дверных проемов
12	3д-вид
13	Маркировочные план стен и пола 1 этажа
14	Маркировочные план стен и пола 2 этажа
15	Перечень ограждающих конструкций (лист 1)
16	Перечень ограждающих конструкций (лист 2)
17	План крыши
18	Разрез 1-1
19	Разрез 2-2; Разрез 3-3
20	Фасад 1-5
21	Фасад В-А
22	Фасад 5-1
23	Фасад А-В

Изм.	Колуч.	Лист	№Док.	Подп.	Дата	Двухэтажное здание (баня)	Стадия	Лист	Листов
Разраб.							П		
Пров.									
Т. контр.									
Н. контр.						Состав чертежей			
Утв.									

Изм.	Колуч.	Лист	№Док.	Подп.	Дата.			
Разраб.						Стадия	Лист	Листов
Пров.						П		
Т. контр.								
Н. контр.						Состав чертежей		
Утв.								

Изм.	Колуч.	Лист	№Док.	Подп.	Дата			
Разраб.								
Пров.								
Т. контр.						Состав чертежей		
Н. контр.								
Утв.								
							Стадия	Лист	Листов
							П		

Изм.	Колуч.	Лист	№Док.	Подп.	Дата			
Разраб.								
Пров.								
Т. контр.								
Н. контр.						Состав чертежей		
Утв.								
							Стадия	Лист	Листов
							П		

Маркировочный план 1 этажа

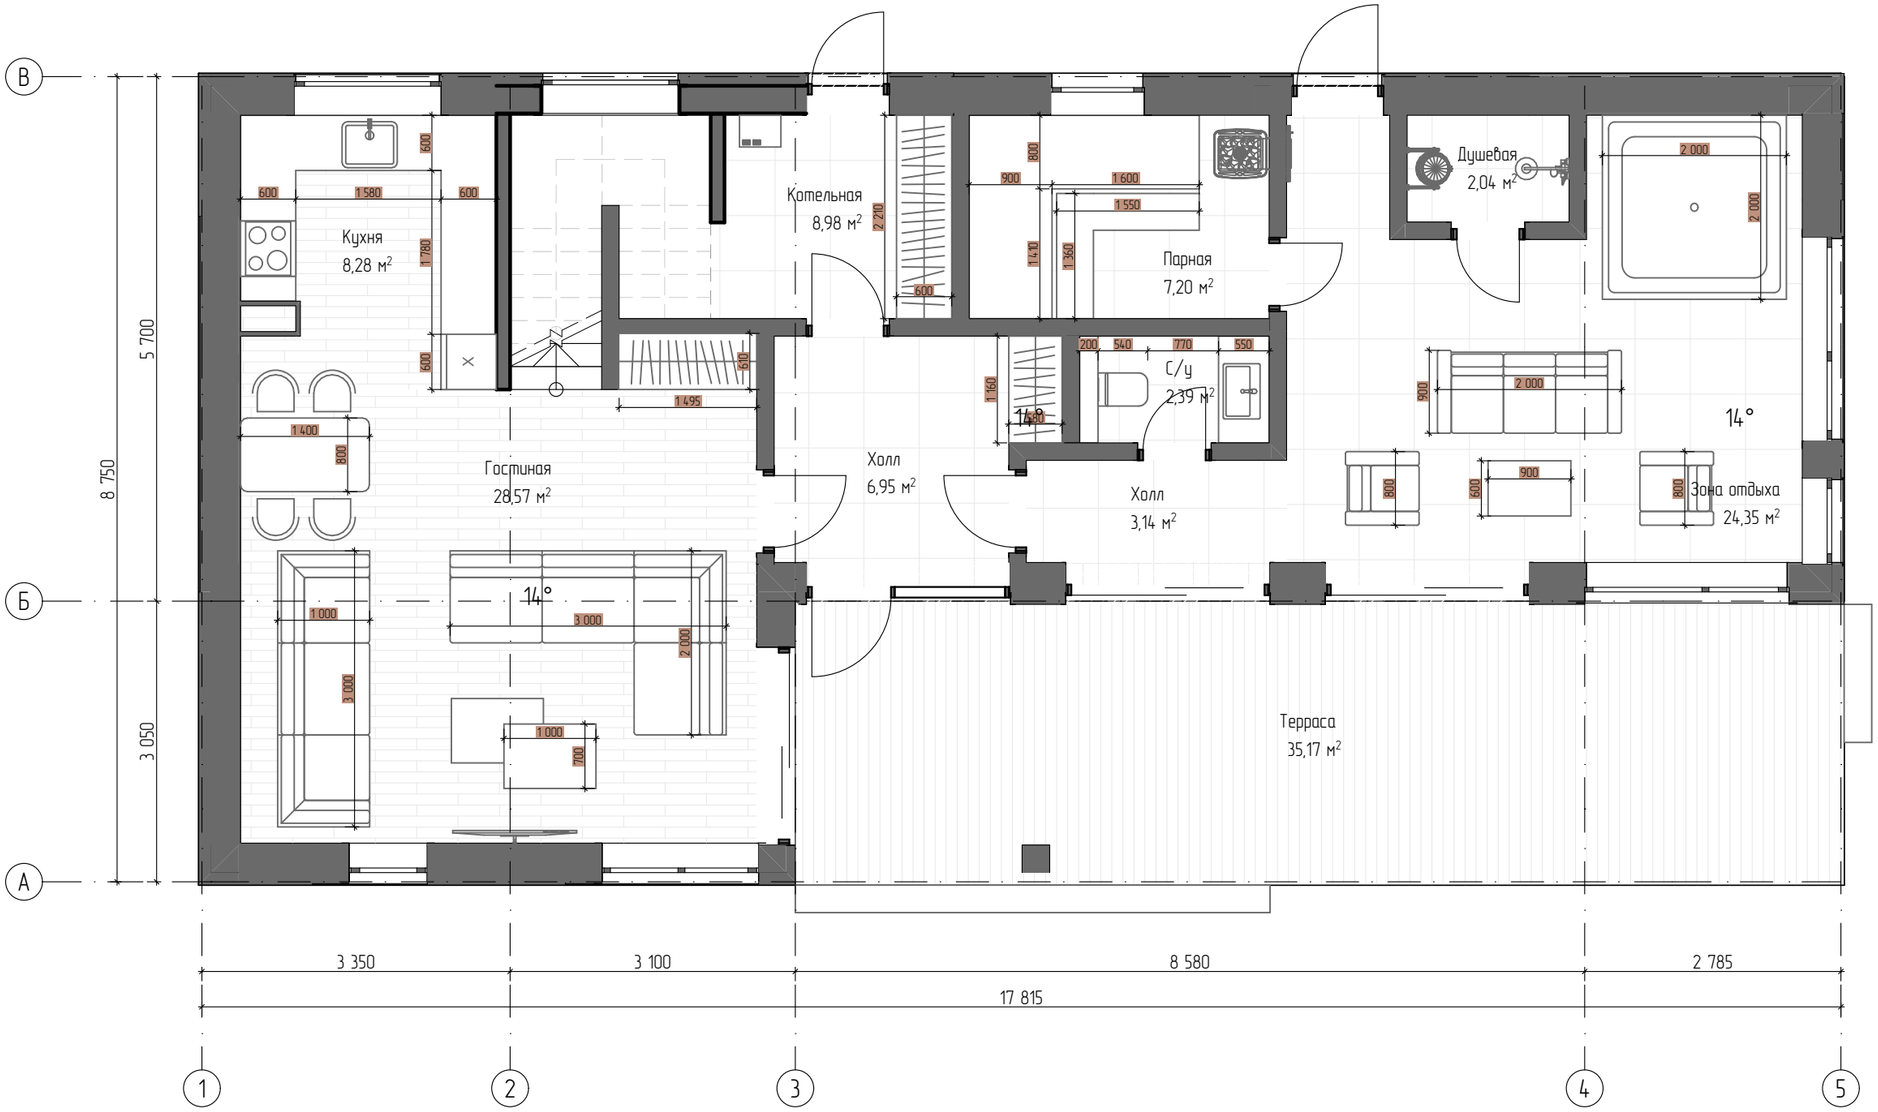

Экспликация помещений 1 этажа		
№	Название	Площадь, м2
Внешняя площадь		
1	Терраса	35,17
Внутренняя площадь		
1	Холл	6,95
2	Гостиная	28,57
3	Кухня	8,28
4	Котельная	8,98
5	Парная	7,20
6	Зона отдыха	24,35
7	Холл	3,14
8	С/у	2,39
9	Душевая	2,04
Общая площадь		
		155,88

1. Вся индивидуальная мебель выполняется по отдельному проекту с детальной проработкой и калькуляцией. Чертежи предоставляет фирма-изготовитель столярных изделий.
2. Цветовое решение материалов отделки показаны в проекте приблизительно.
3. количество ступений показано условно.

Изм.	Колуч.	Лист	№Док.	Подп.	Дата				
Разраб.						Двухэтажное здание (баня)	Стадия	Лист	Листов
Пров.							П		
Т. контр.						Маркировочный план 1 этажа			
Н. контр.									
Утв.									

Размерный план 1 этажа

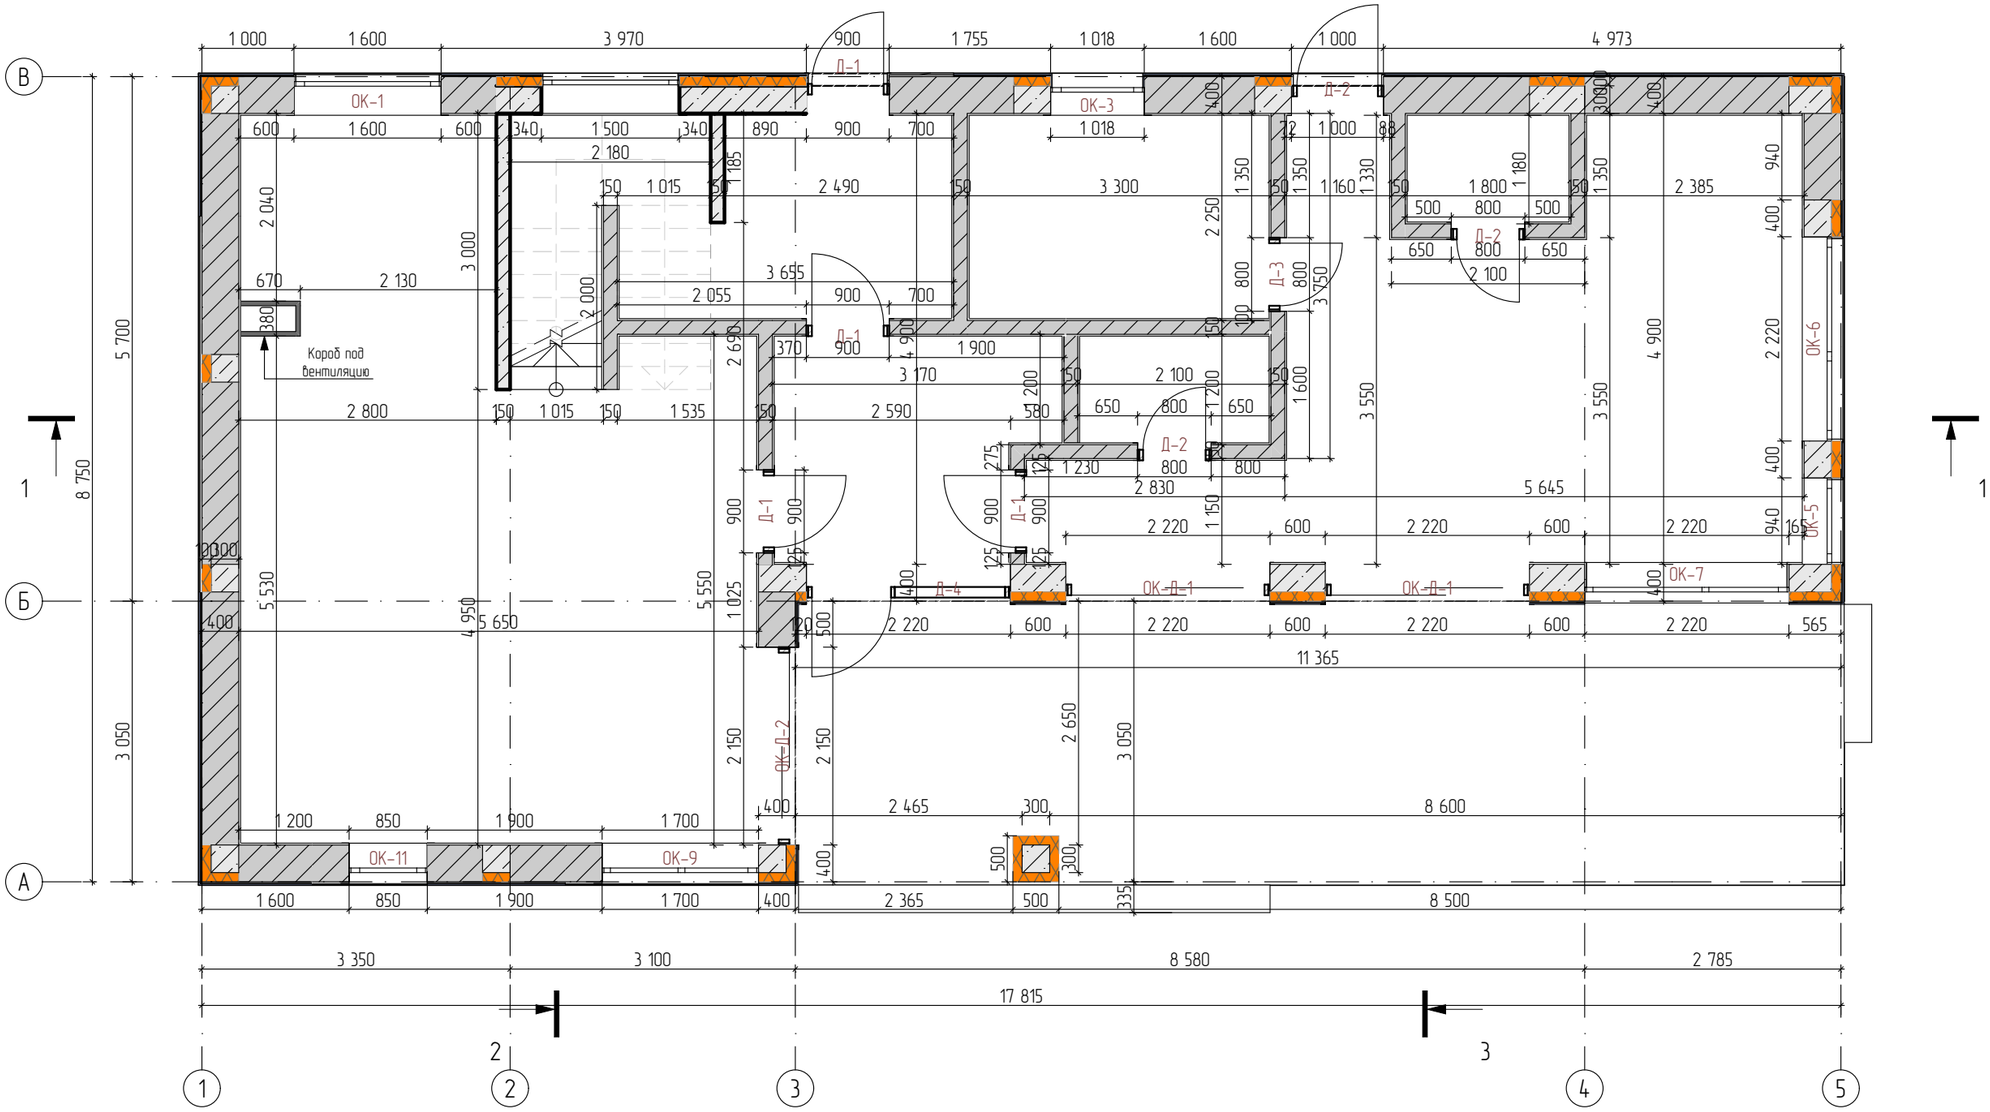

1. Размеры указаны без учета отделки.
2. Спецификацию оконных и дверных проёмов см. след. лист.

Изм.	Колуч.	Лист	№Док.	Подп.	Дата	Двухэтажное здание (баня)	Стадия	Лист	Листов
Разраб.							П		
Пров.									
Т. контр.									
Н. контр.						Размерный план 1 этажа			
Утв.									

3д-разрез 1 этажа

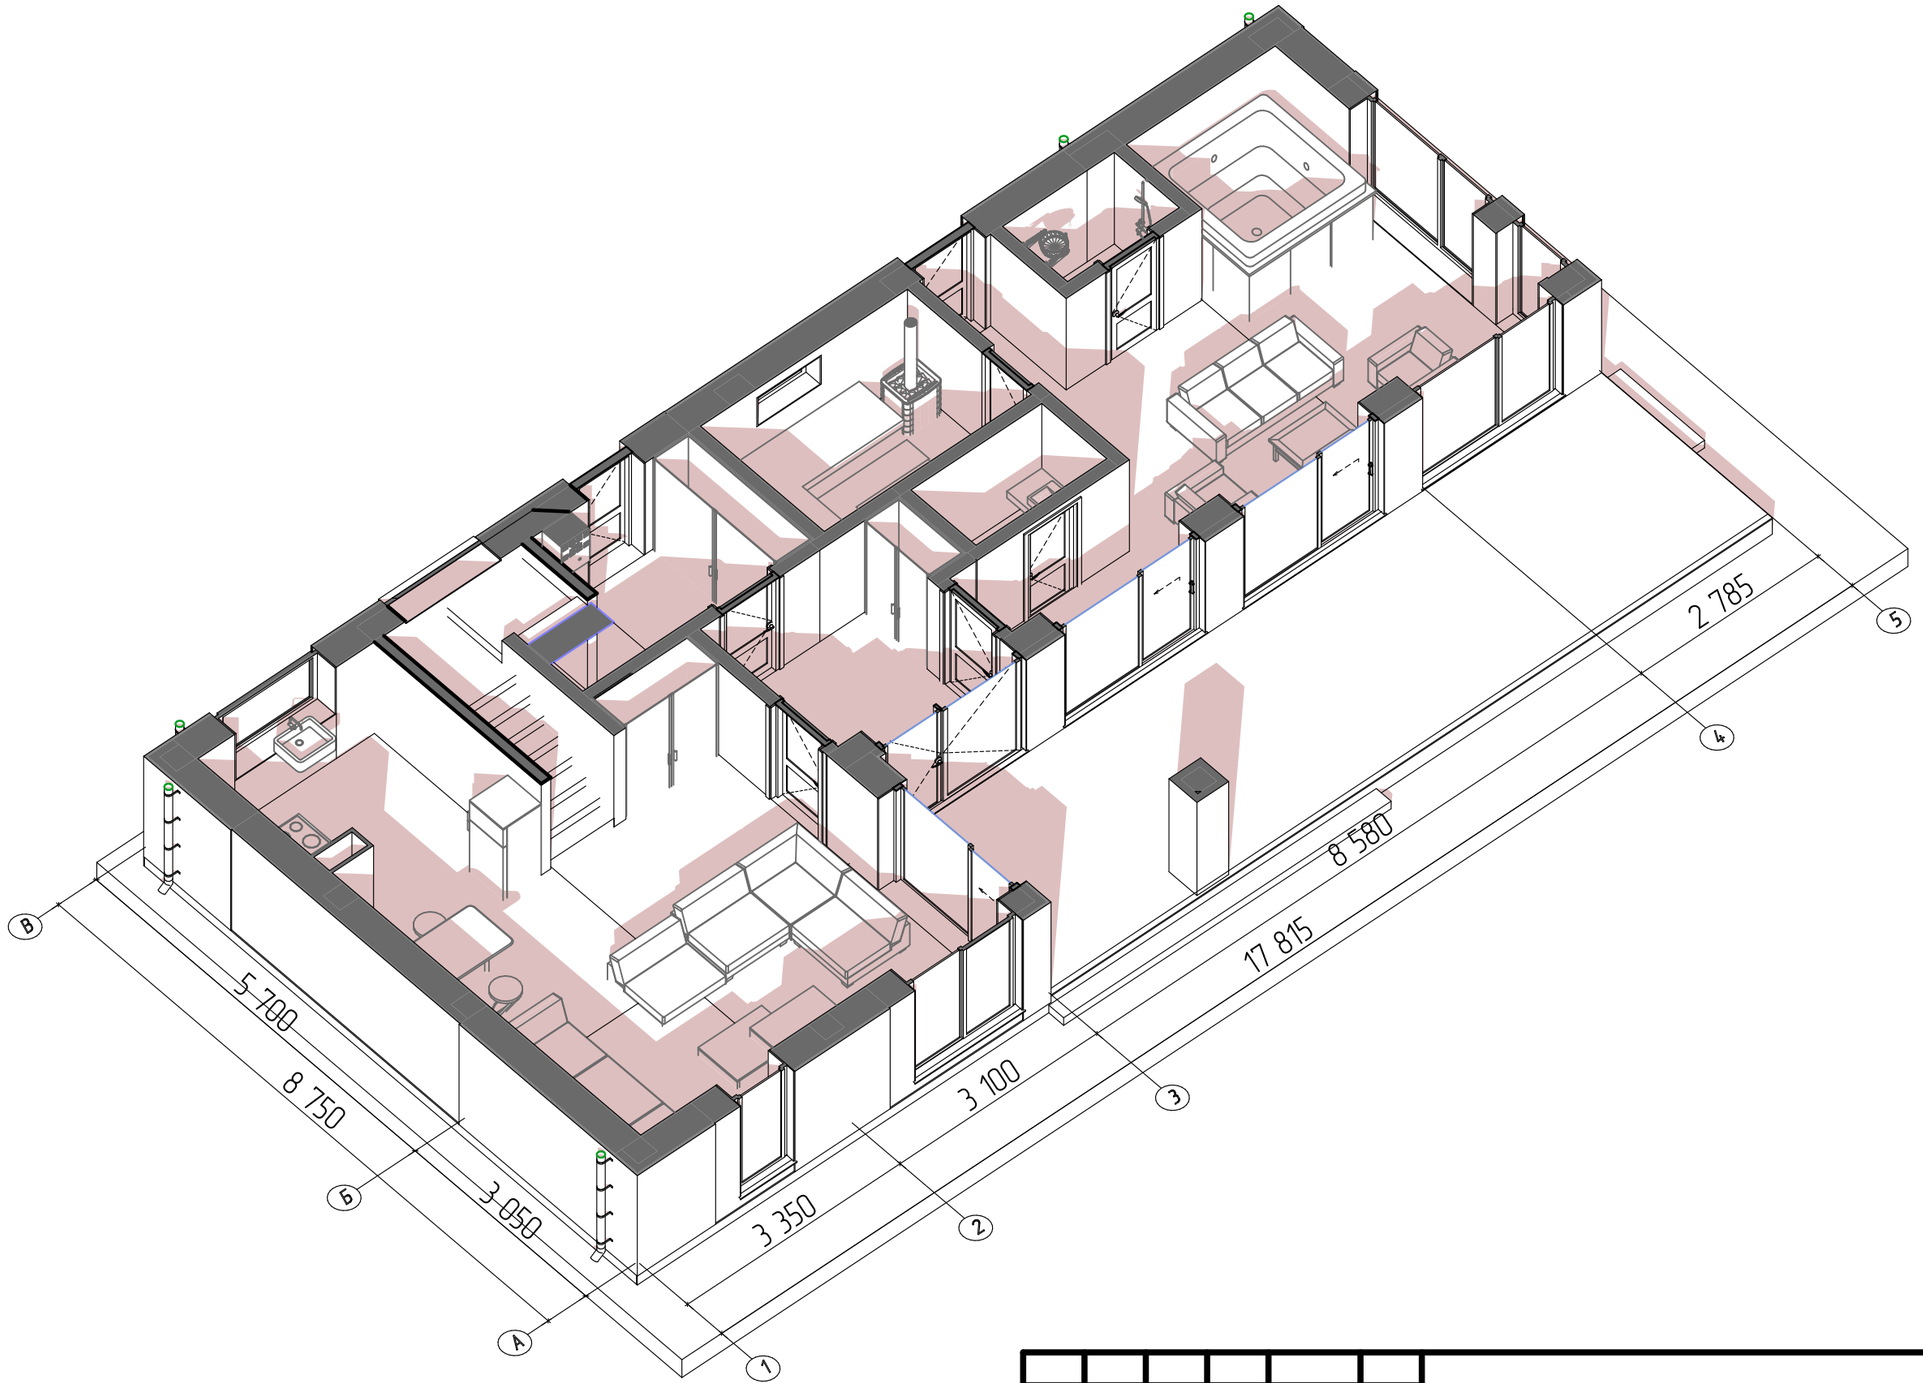

Изм.	Колуч.	Лист	№Док.	Подп.	Дата	Двухэтажное здание (баня)	Стадия	Лист	Листов
Разраб.							П		
Пров.									
Т. контр.									
Н. контр.						3д-разрез 1 этажа			
Утв.									

Маркировочный план 2 этажа

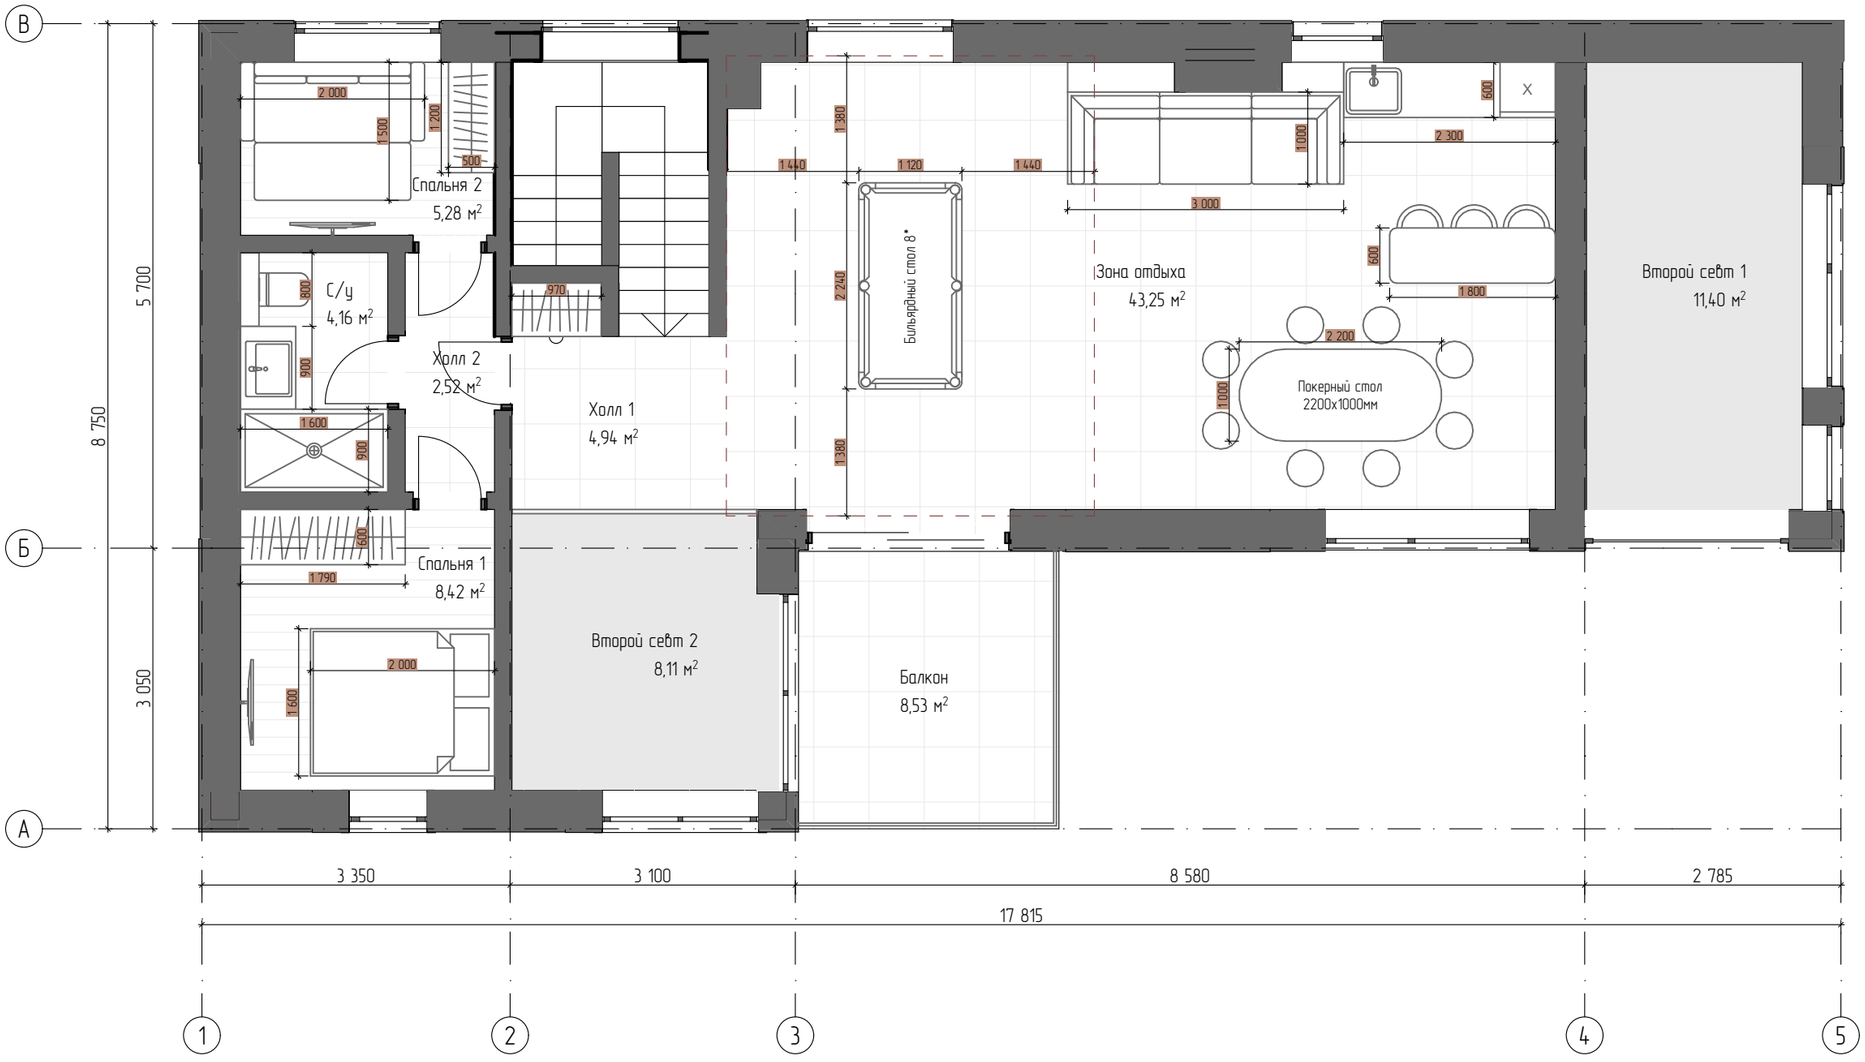

Экспликация 2-й этаж		
№	Название	Площадь, м2
Внешняя площадь		
1	Балкон	8,53
Внутренняя площадь		
1	Холл 1	4,94
2	Холл 2	2,52
3	Спальня 1	8,42
4	С/у	4,16
5	Спальня 2	5,28
6	Зона отдыха	43,25
Общая площадь		
		129,96

1. Вся индивидуальная мебель выполняется по отдельному проекту с детальной проработкой и калькуляцией. Чертежи предоставляет фирма-изготовитель столярных изделий.
2. Цветовое решение материалов отделки показаны в проекте приблизительно.

Изм.	Колуч.	Лист	№Док.	Подп.	Дата	Двухэтажное здание (баня)	Стадия	Лист	Листов
Разраб.							П		
Пров.									
Т. контр.									
Н. контр.						Маркировочный план 2 этажа			
Утв.									

Размерный план

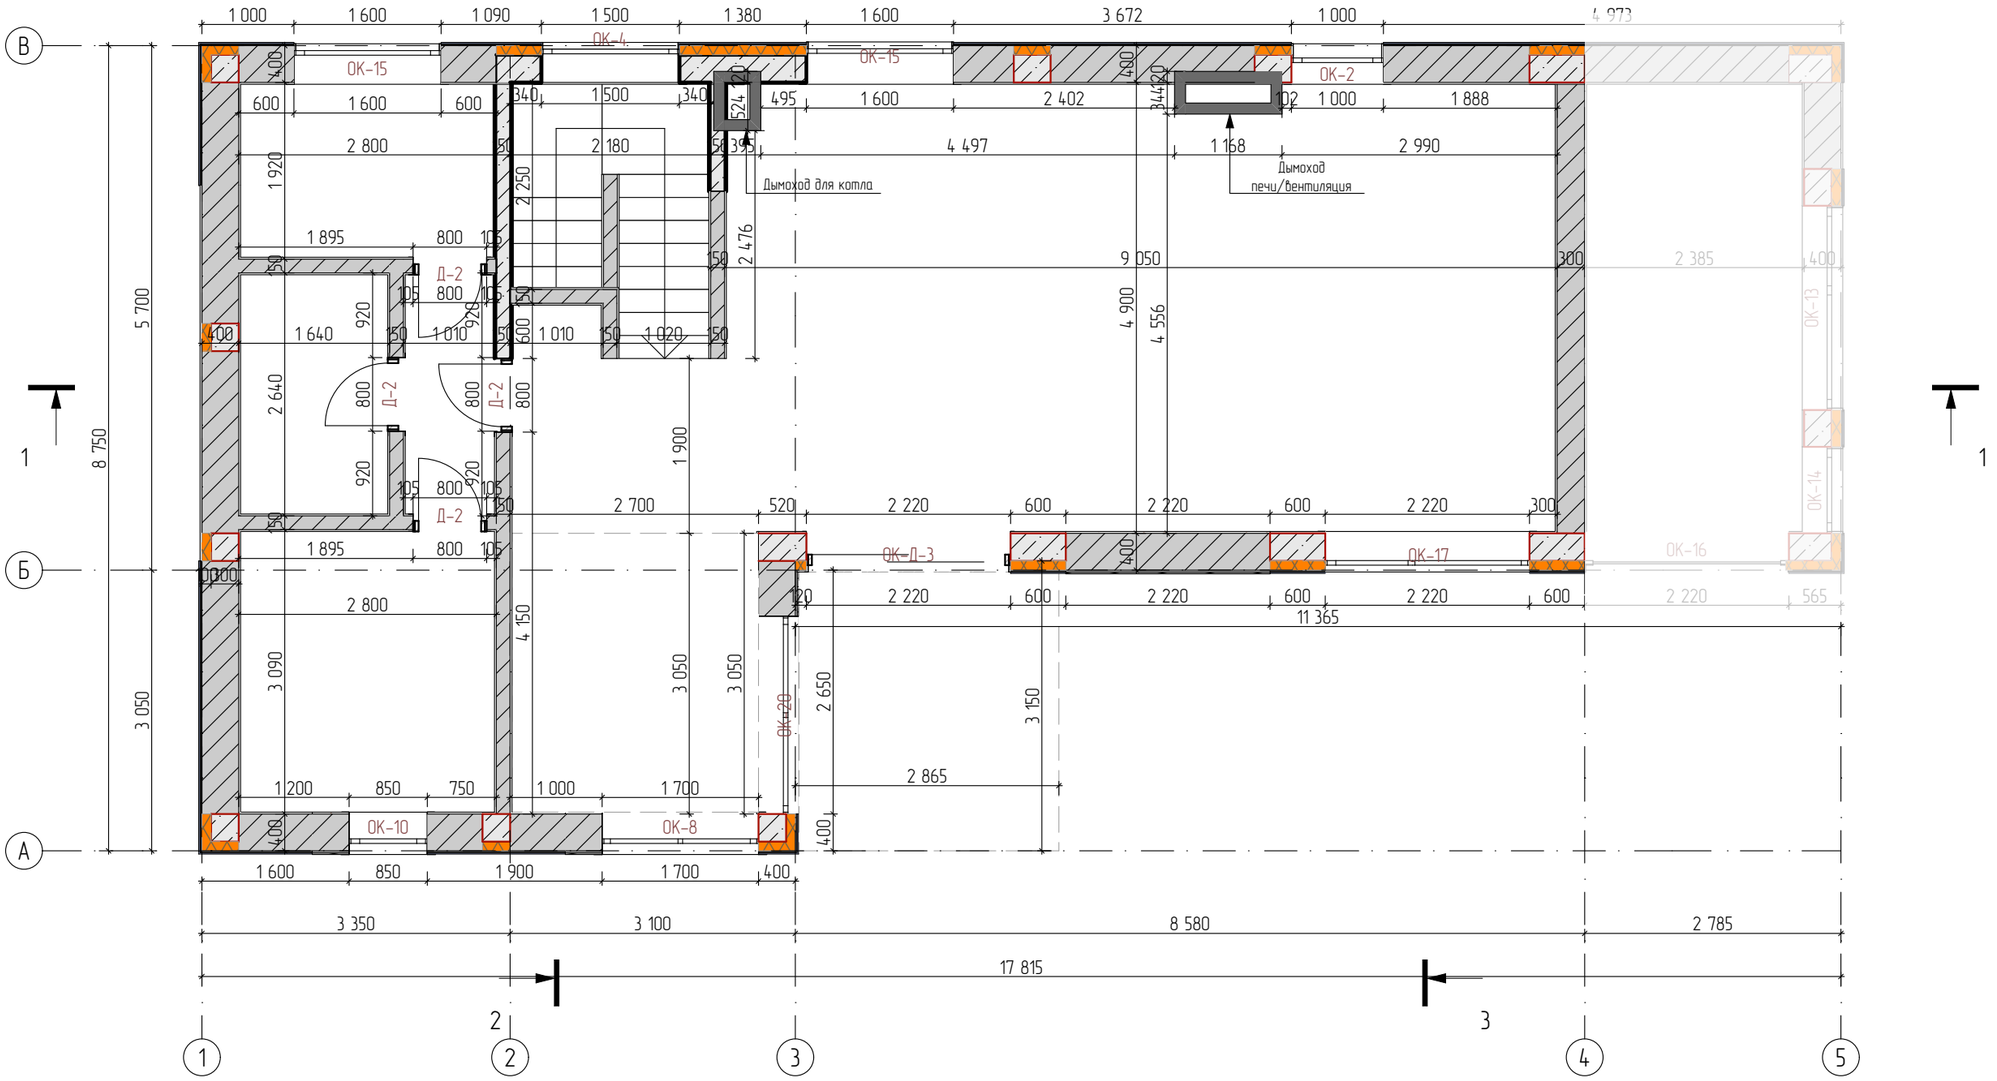

1. Размеры указаны без учета отделки.
2. Спецификацию оконных и дверных проёмов см. след. лист.

Изм.	Колуч.	Лист	№Док.	Подп.	Дата	Двухэтажное здание (баня)	Стадия	Лист	Листов
Разраб.							П		
Пров.									
Т. контр.						Размерный план 2 этажа			
Н. контр.									
Утв.									

3д-разрез 1 этажа

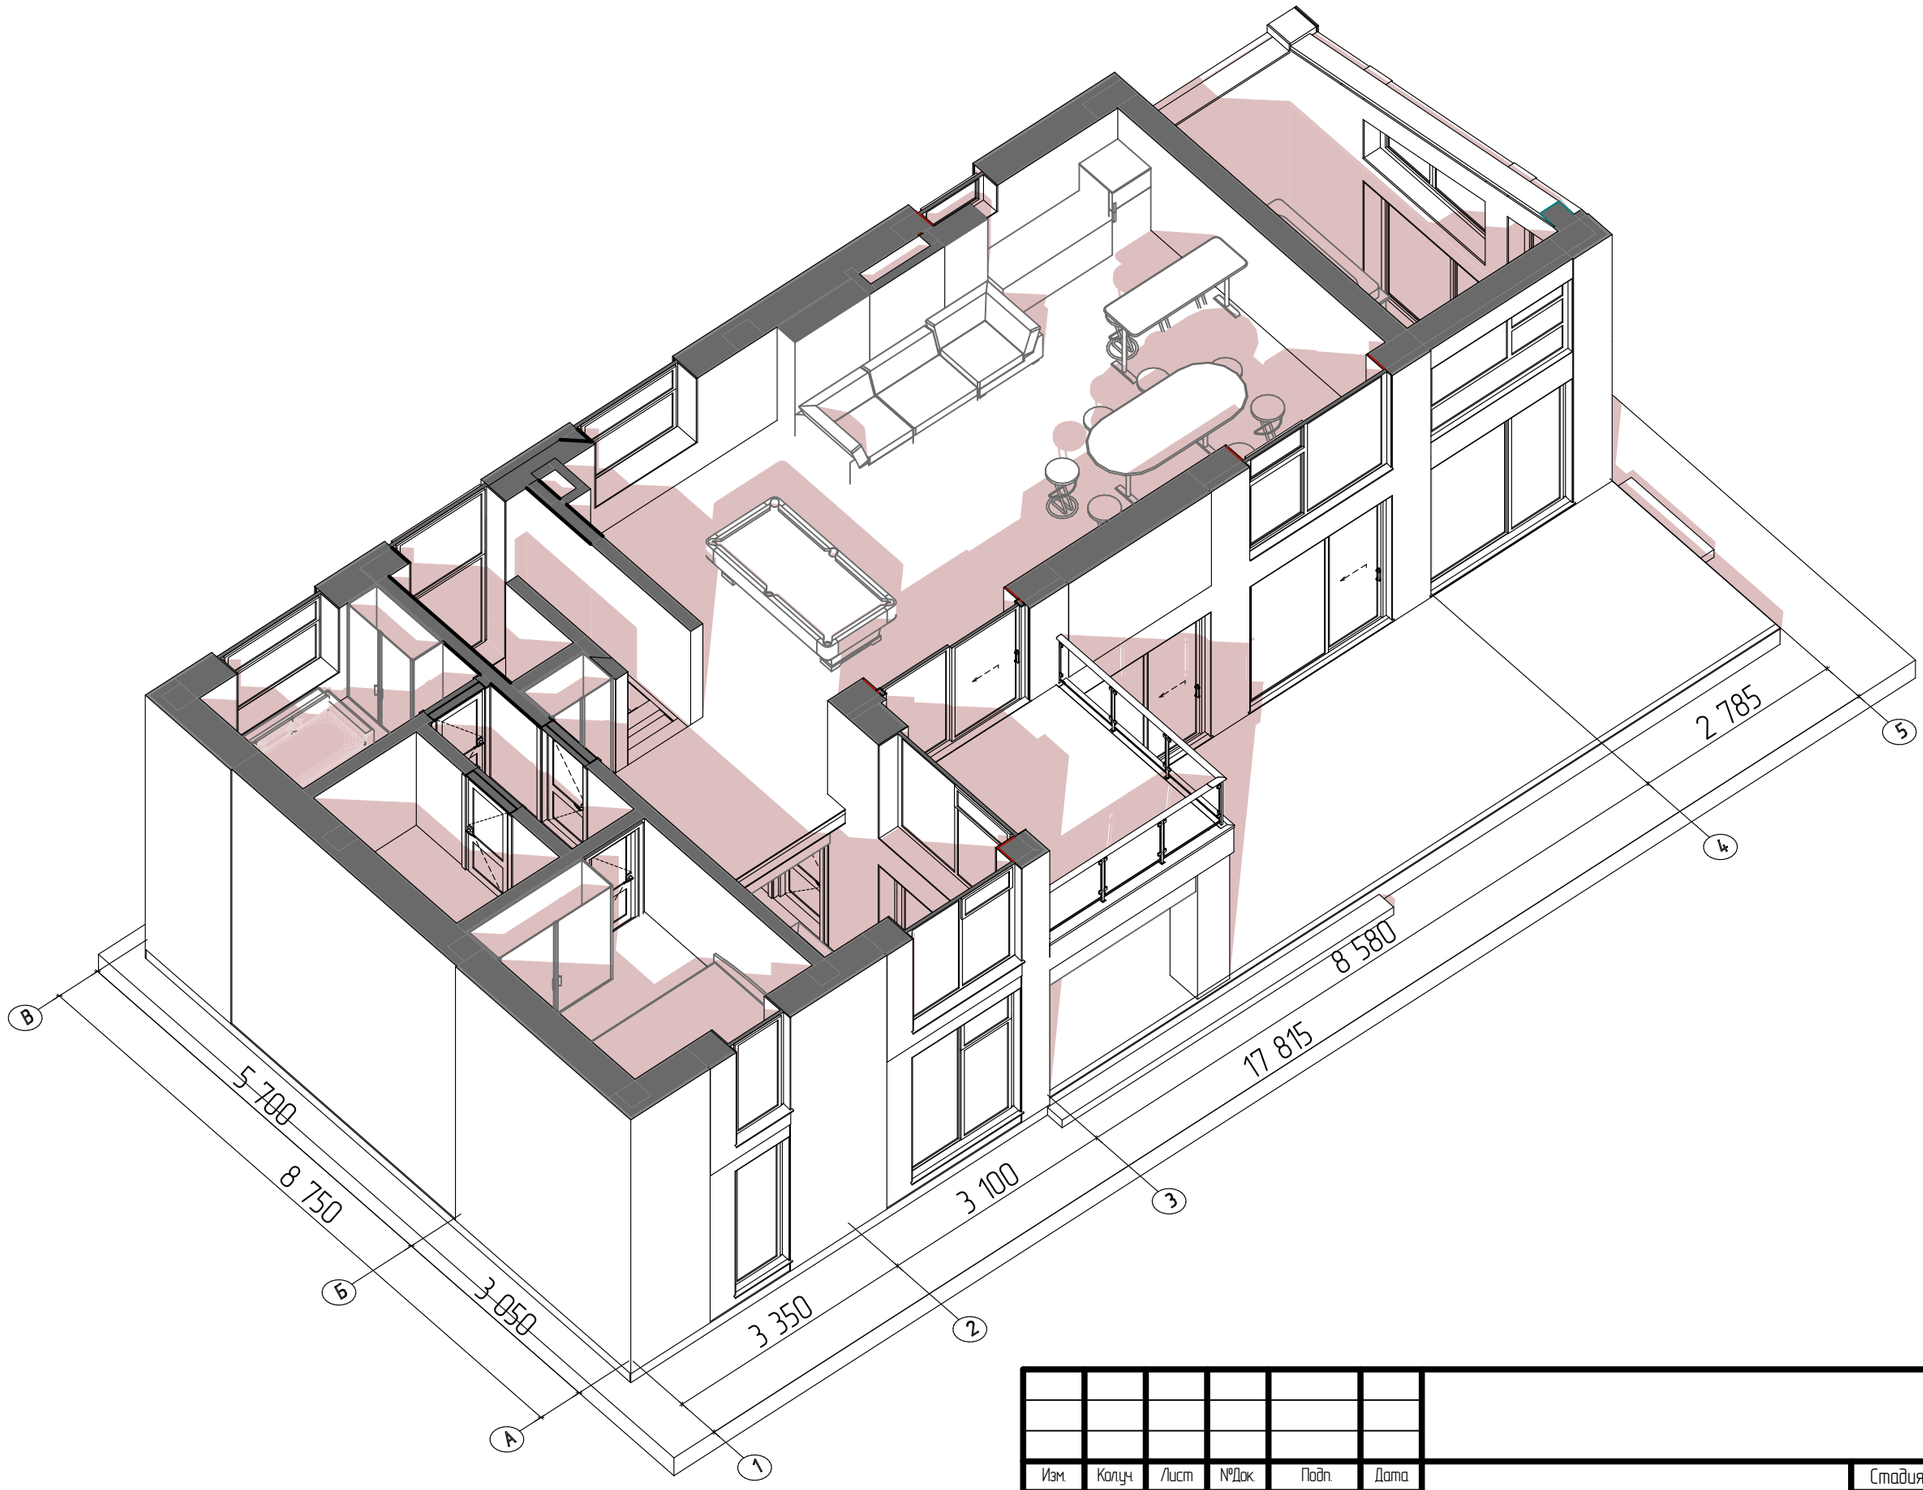

Изм.	Колуч.	Лист	№Док.	Подп.	Дата	Двухэтажное здание (баня)	Стадия	Лист	Листов
Разраб.							П		
Пров.									
Т. контр.									
Н. контр.						3д-разрез 2 этажа			
Утв.									

Ведомость заполнения оконных проемов

Ведомость заполнения оконных проемов				
Наименование	Размер проема Ш х В, мм	Кол-во, шт	Вид	Площадь
ОК-1	1 600×1 600	1	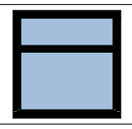	2,56
ОК-2	1 000×650	1		0,65
ОК-3	1 018×650	1		0,66
ОК-4	1 500×3 545	1	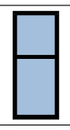	5,32
ОК-5	940×2 805	1	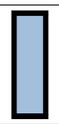	2,64
ОК-6	2 220×2 805	1	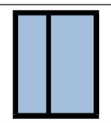	6,23
ОК-7	2 220×2 805	1	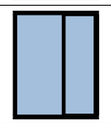	6,23
ОК-8	1 700×2 150	1		3,65
ОК-9	1 700×2 805	1	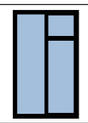	4,77

Ведомость заполнения оконных проемов				
Наименование	Размер проема Ш х В, мм	Кол-во, шт	Вид	Площадь
ОК-10	850×2 150	1	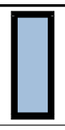	1,83
ОК-11	850×2 805	1	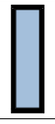	2,38
ОК-12	1 644×953	1	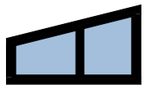	1,57
ОК-13	2 180×1 390	1	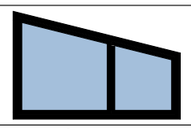	3,03
ОК-14	940×1 763	1	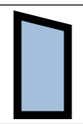	1,66
ОК-15	1 600×1 500	2	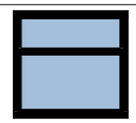	2,40
ОК-16	2 180×1 600	1	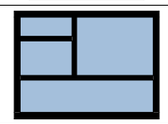	3,49
ОК-17	2 220×2 150	1		4,77
ОК-18	2 150×996	1		2,14

Ведомость заполнения оконных проемов				
Наименование	Размер проема Ш х В, мм	Кол-во, шт	Вид	Площадь
ОК-19	2 220×996	3		2,21
ОК-20	2 150×2 150	1	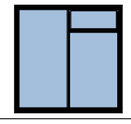	4,62
				69,63 м²

1. Изготовление окон и дверей определяется заказчиком, допускается изменение открывания окон и дверей;
2. При заказе оконных и дверных блоков необходим обмер по месту от изготовителя;
3. Оконные и дверные изделия изображены со стороны открывания.

Изм.	Колуч.	Лист	№Док.	Подп.	Дата	Двухэтажное здание (баня)	Стадия	Лист	Листов
Разраб.							П		
Пров.									
Т. контр.									
Н. контр.						Ведомость заполнения оконных проемов			
Утв.									

Ведомость заполнения дверных проемов

Ведомость заполенения дверных проемов				
Название	Размер проема Ш х В, мм	Кол-во, шт	Вид	Площадь
Д-1	900×2 100	4	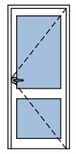	1,89
Д-2	800×2 100	6	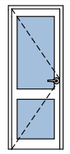	1,68
Д-2	1 000×2 100	1	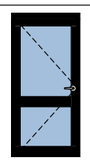	2,10
Д-3	800×2 100	1	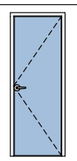	1,68
Д-4	2 220×2 805	1	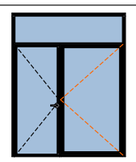	6,23
ОК-Д-1	2 220×2 805	2	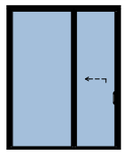	6,23
ОК-Д-2	2 150×2 805	1	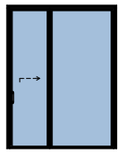	6,03
ОК-Д-3	2 220×2 150	1	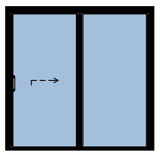	4,77
				50,91 м²

1. Изготовление окон и дверей определяется заказчиком, допускается изменение открывания окон и дверей;
2. При заказе оконных и дверных блоков необходим обмер по месту от изготовителя;
3. Оконные и дверные изделия изображены со стороны открывания.

Изм.	Колуч.	Лист	№Док.	Подп.	Дата	Двухэтажное здание (баня)	Стадия	Лист	Листов
Разраб.							П		
Пров.									
Т. контр.						Ведомость заполнения дверных проемов			
Н. контр.									
Утв.									

3д-вид

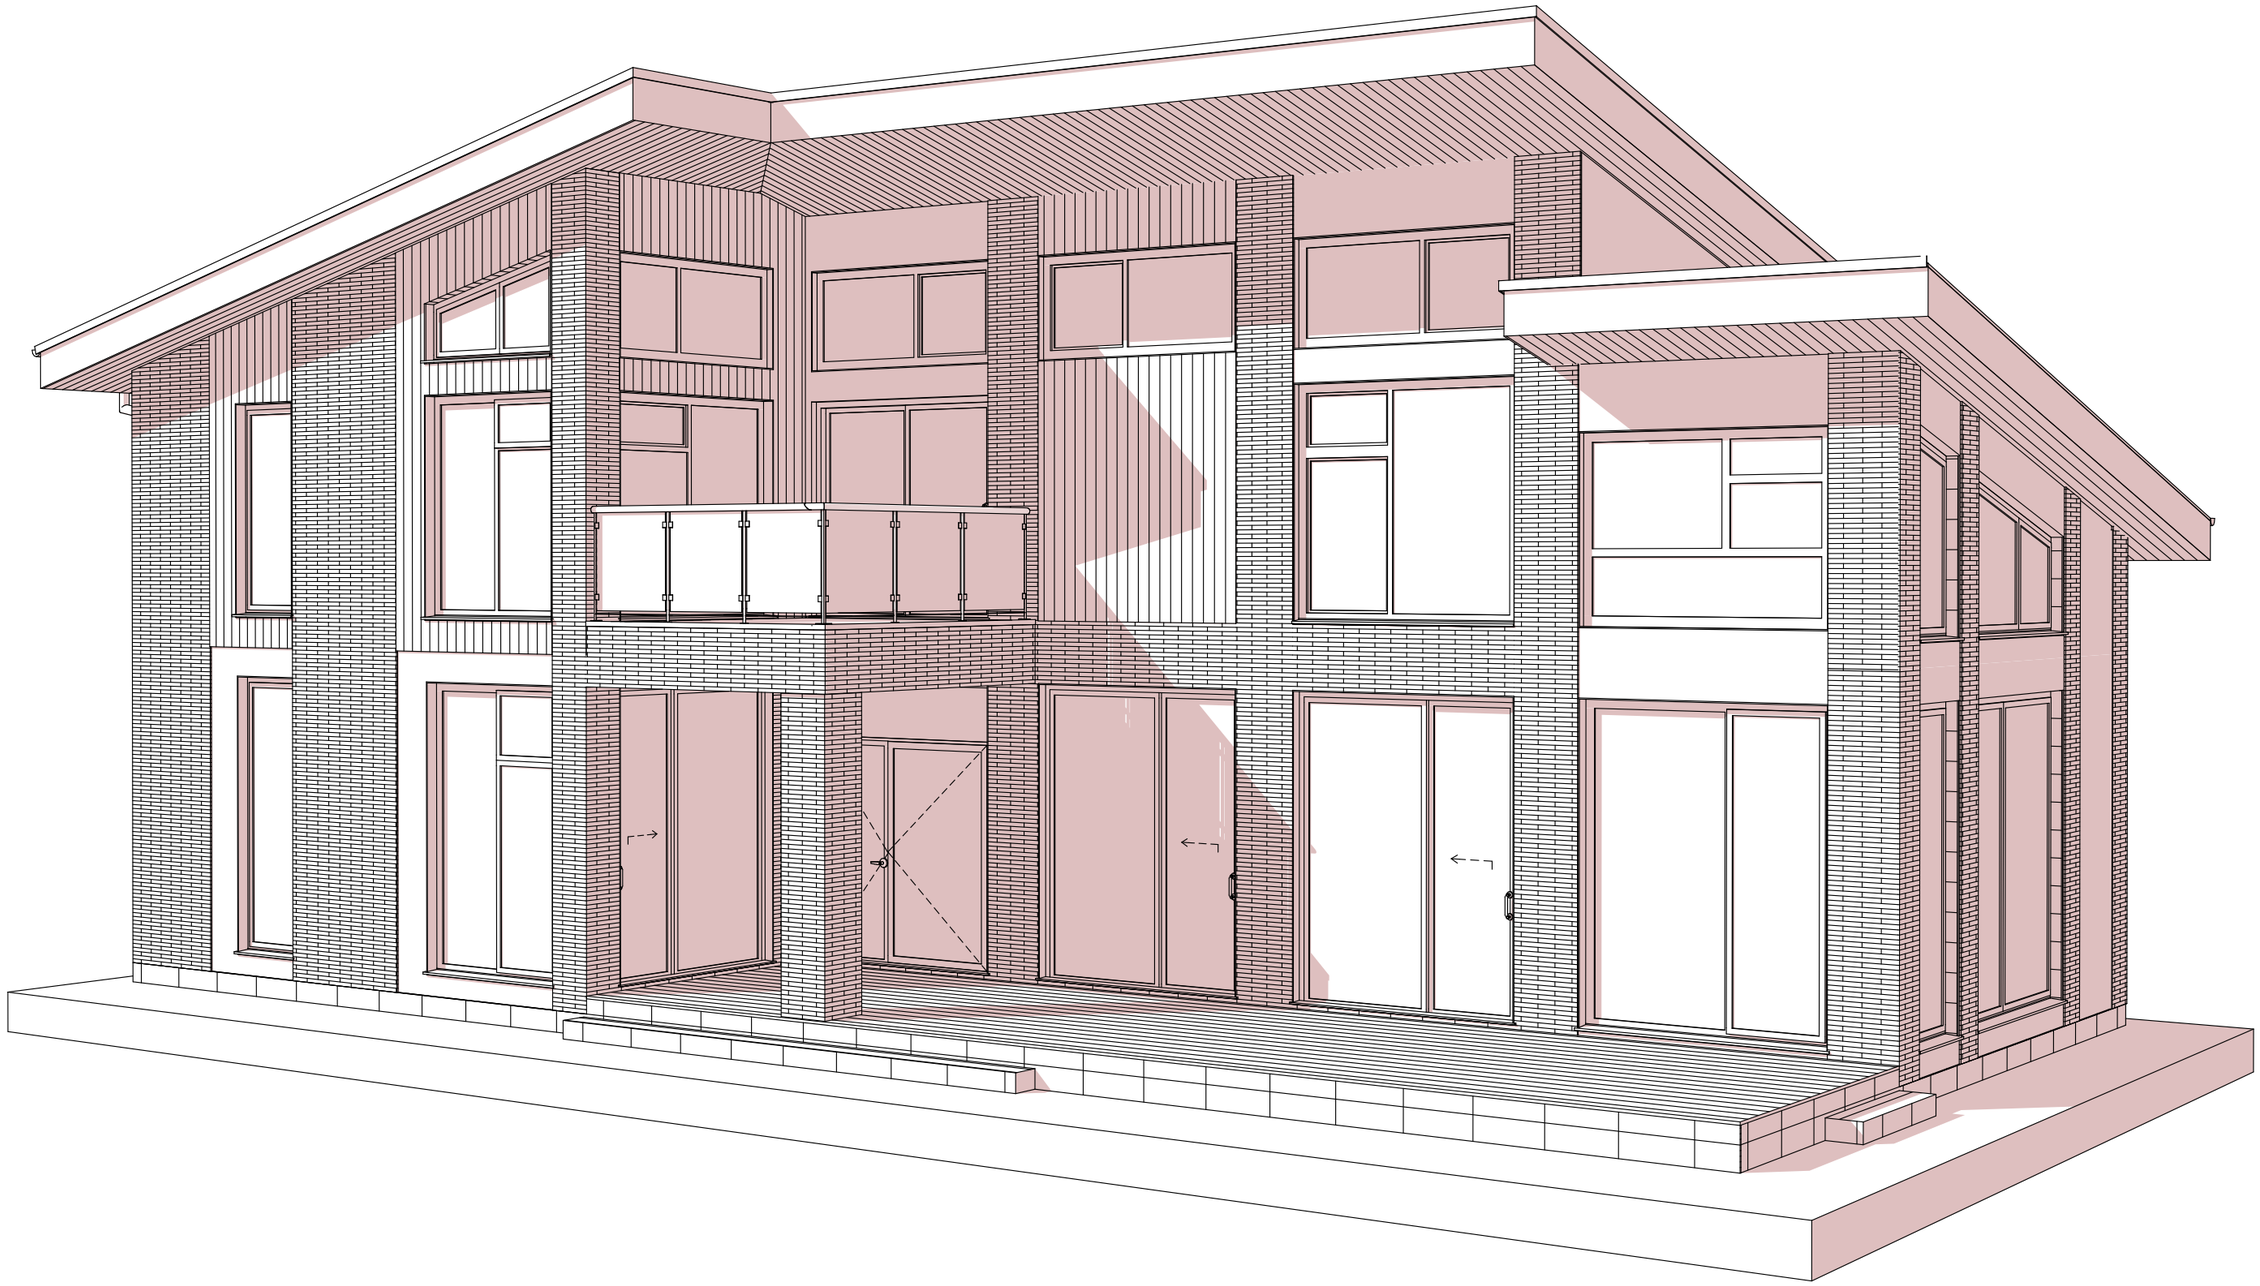

Изм.	Колуч.	Лист	№Док.	Подп.	Дата	Двухэтажное здание (баня)	Стадия	Лист	Листов
Разраб.							П		
Пров.									
Т. контр.						3д-вид			
Н. контр.									
Утв.									

Маркировочные план стен и пола 1 этажа

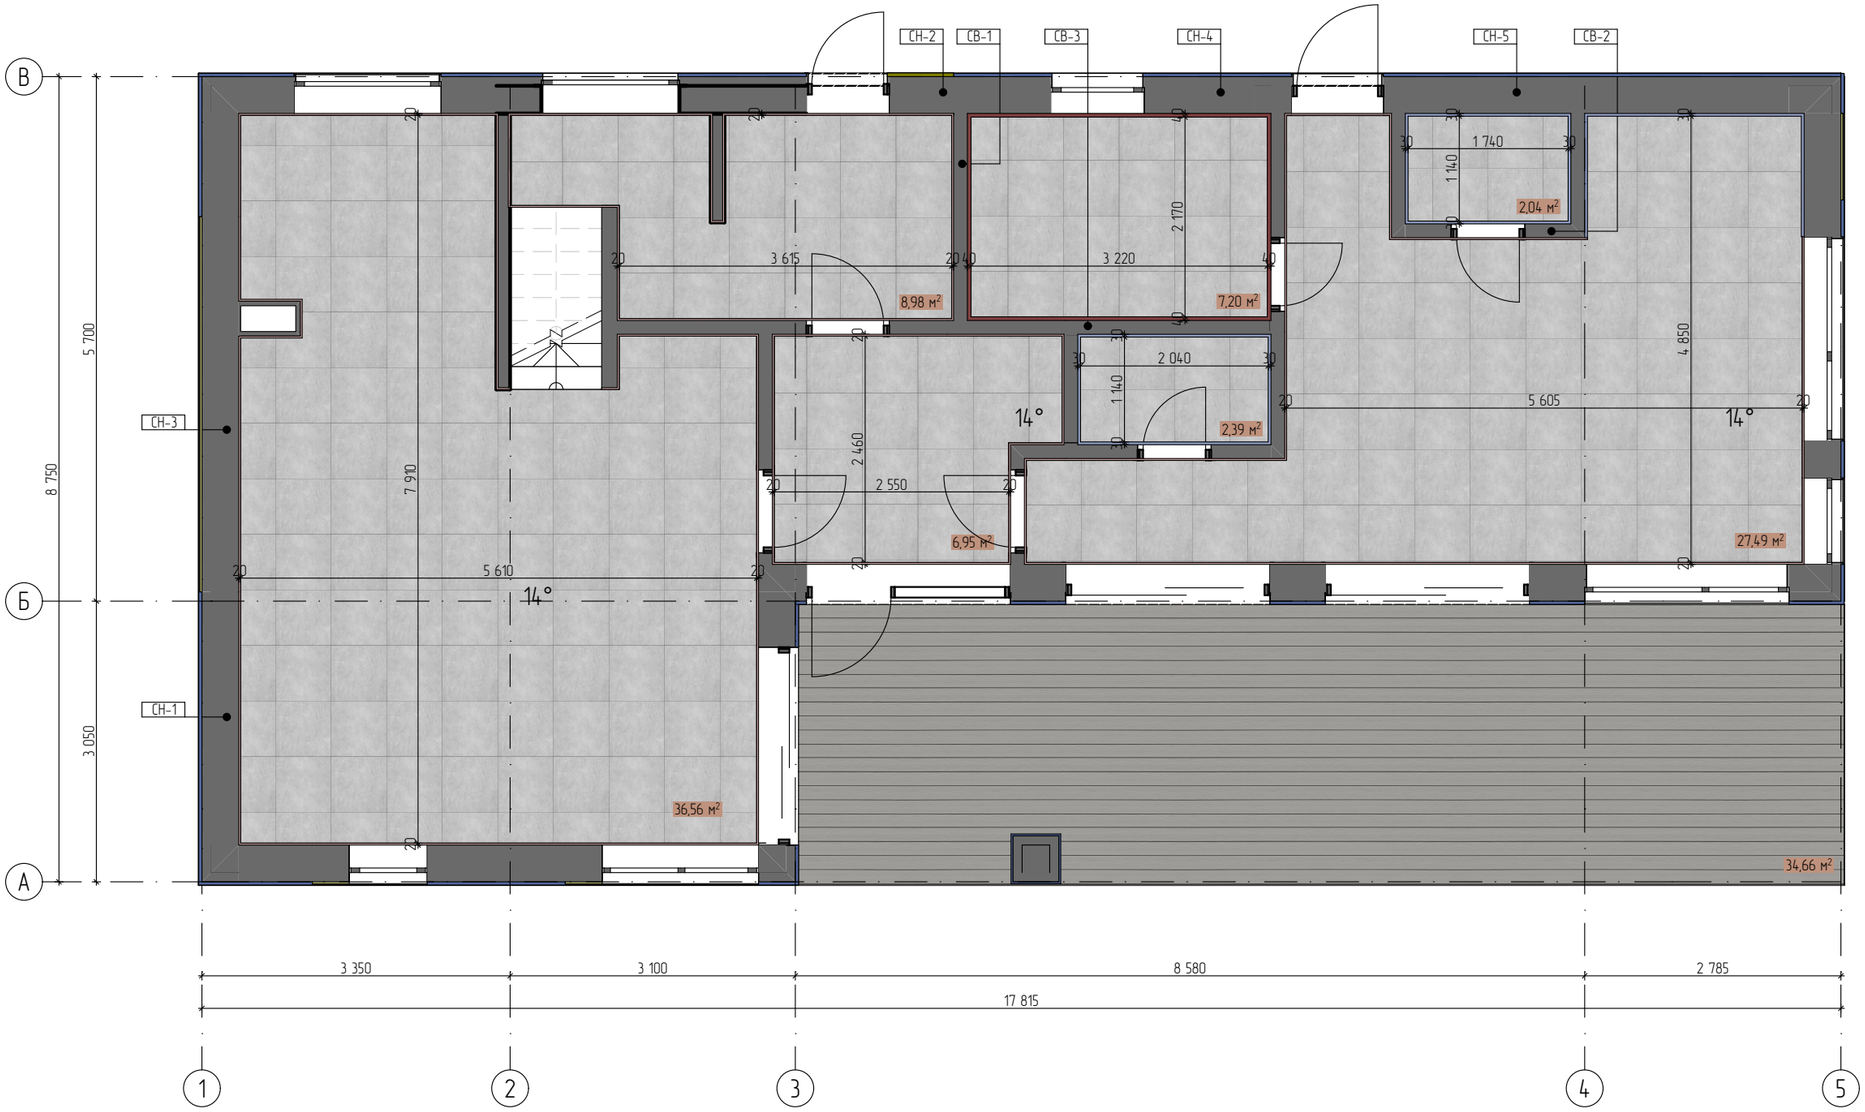

Условные обозначения:

Пирог покрытия пола:

- По керамограниту
- По террасной доске

Пирог отделки стен:

- Искусственный камень
- Декоративная штукатурка
- Планкен вертикальный
- Декоративная штукатурка
- Вагонка
- Керамогранит

*Маркировку стен и полов см. лист 15-16

Изм.	Колуч.	Лист	№Док.	Подп.	Дата	Двухэтажное здание (баня)	Стадия	Лист	Листов
Разраб.							П		
Пров.									
Т. контр.									
Н. контр.						Маркировочные план стен и пола 1 этажа			
Утв.									

Маркировочные план стен и пола 2 этажа

Условные обозначения:

Пирог покрытия пола:

- –По керамограниту
- –По ламинату/кварцвинилу

Пирог отделки стен:

- – Искусственный камень
- – Декоративная штукатурка
- – Планкен вертикальный
- – Декоративная штукатурка
- – Вагонка
- – Керамогранит

*Маркировку стен и полов см. лист 15–16

Изм.	Колуч.	Лист	№Док.	Подп.	Дата	Двухэтажное здание (баня)	Стадия	Лист	Листов
Разраб.							П		
Пров.									
Т. контр.						Маркировочные план стен и пола 2 этажа			
Н. контр.									
Утв.									

Перечень ограждающих конструкций (лист 1)

Ведомость материалов на стены

Поз.	Сечение стен	Список материалов
СВ-1	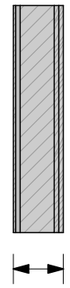 210	СВ-1 20 мм Вагонка - внутренняя отделка 20 мм Обрешетка - брусок 20х40мм 0 мм Специализированная фольгированная пароизоляционная мембрана для бань и саун 150 мм Газобетонный блок 10 мм Выравнивающий штукатурный слой по маякам 10 мм Декоративная штукатурка финишная - внутренняя отделка
СВ-2	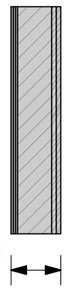 200	СВ-2 10 мм Керамогранит 10 мм Плиточный клей 10 мм Выравнивающий штукатурный слой по маякам 150 мм Газобетонный блок 10 мм Выравнивающий штукатурный слой по маякам 10 мм Декоративная штукатурка финишная - внутренняя отделка
СВ-3	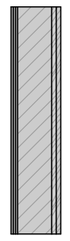 220	СВ-3 20 мм Вагонка - внутренняя отделка 20 мм Обрешетка - брусок 20х40мм 0 мм Специализированная фольгированная пароизоляционная мембрана для бань и саун 150 мм Газобетонный блок 10 мм Выравнивающий штукатурный слой по маякам 10 мм Плиточный клей 10 мм Керамогранит
СН-1	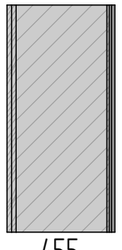 455	СН-1 10 мм Декоративная штукатурка финишная - внутренняя отделка 10 мм Выравнивающий штукатурный слой по маякам 400 мм Газобетонный блок 10 мм Штукатурка по армирующей сетке 10 мм Клей для фасадной плитки 15 мм Отделка искусственным камнем - Хайлэнд 298-80

Ведомость материалов на стены

Поз.	Сечение стен	Список материалов
СН-2	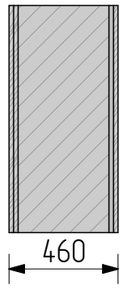 460	СН-2 10 мм Декоративная штукатурка финишная - внутренняя отделка 10 мм Выравнивающий штукатурный слой по маякам 400 мм Газобетонный блок 20 мм Обрешетка - брусок 20х40мм 20 мм Планкен вертикальный
СН-3	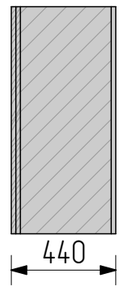 440	СН-3 10 мм Декоративная штукатурка финишная - внутренняя отделка 10 мм Выравнивающий штукатурный слой по маякам 400 мм Газобетонный блок 20 мм Штукатурка черная - Фасадная система (армирующий слой, грунтовка, декоративное покрытие)
СН-4	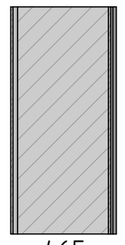 465	СН-4 20 мм Вагонка - внутренняя отделка 20 мм Обрешетка - брусок 20х40мм 0 мм Специализированная фольгированная пароизоляционная мембрана для бань и саун 400 мм Газобетонный блок 10 мм Штукатурка по армирующей сетке 10 мм Клей для фасадной плитки 15 мм Отделка искусственным камнем - Хайлэнд 298-80
СН-5	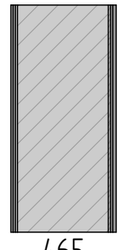 465	СН-5 10 мм Керамогранит 10 мм Плиточный клей 10 мм Выравнивающий штукатурный слой по маякам 400 мм Газобетонный блок 10 мм Штукатурка по армирующей сетке 10 мм Клей для фасадной плитки 15 мм Отделка искусственным камнем - Хайлэнд 298-80

Изм.	Колуч.	Лист	№Док.	Подп.	Дата	Двухэтажное здание (баня)	Стадия	Лист	Листов
Разраб.							П		
Пров.									
Т. контр.									
Н. контр.						Перечень ограждающих конструкций (лист 1)			
Утв.									

Перечень ограждающих конструкций (лист 2)

Ведомость материалов на полы 1 этаж			
Поз.	Наименование материала	Толщина, мм	Сечение пола
1			
	Керамогранит	10	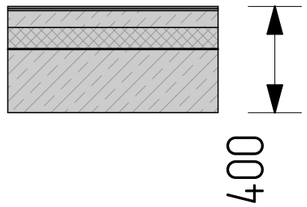
	Плиточный клей	10	
	Цементно-песчаная стяжка с системой водяных теплых полов	80	
	Утеплитель ЭППС	100	
	Ж/б плита перекрытия	200	
*Учесть разуклонку в мокрых зонах			

Ведомость материалов на полы 2 этажа			
Поз.	Наименование материала	Толщина, мм	Сечение пола
2			
	Керамогранит	10	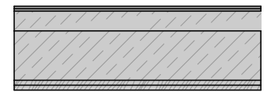
	Плиточный клей	10	
	Цементно-песчаная стяжка с системой водяных теплых полов	80	
	Ж/б плита перекрытия	200	
	Выравнивающий штукатурный слой по маякам	20	
	Декоративная штукатурка финишная - внутренняя отделка	20	
3			
	Ламинат	10	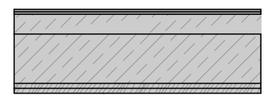
	Подложка из вспененного полиэтилена	10	
	Цементно-песчаная стяжка с системой водяных теплых полов	80	
	Ж/б плита перекрытия	200	
	Выравнивающий штукатурный слой по маякам	20	
	Декоративная штукатурка финишная - внутренняя отделка	20	

Изм.	Колуч.	Лист	№Док.	Подп.	Дата.	Двухэтажное здание (баня)	Стадия	Лист	Листов
Разраб.							П		
Пров.									
Т. контр.									
Н. контр.						Перечень ограждающих конструкций (лист 2)			
Утв.									

План крыши

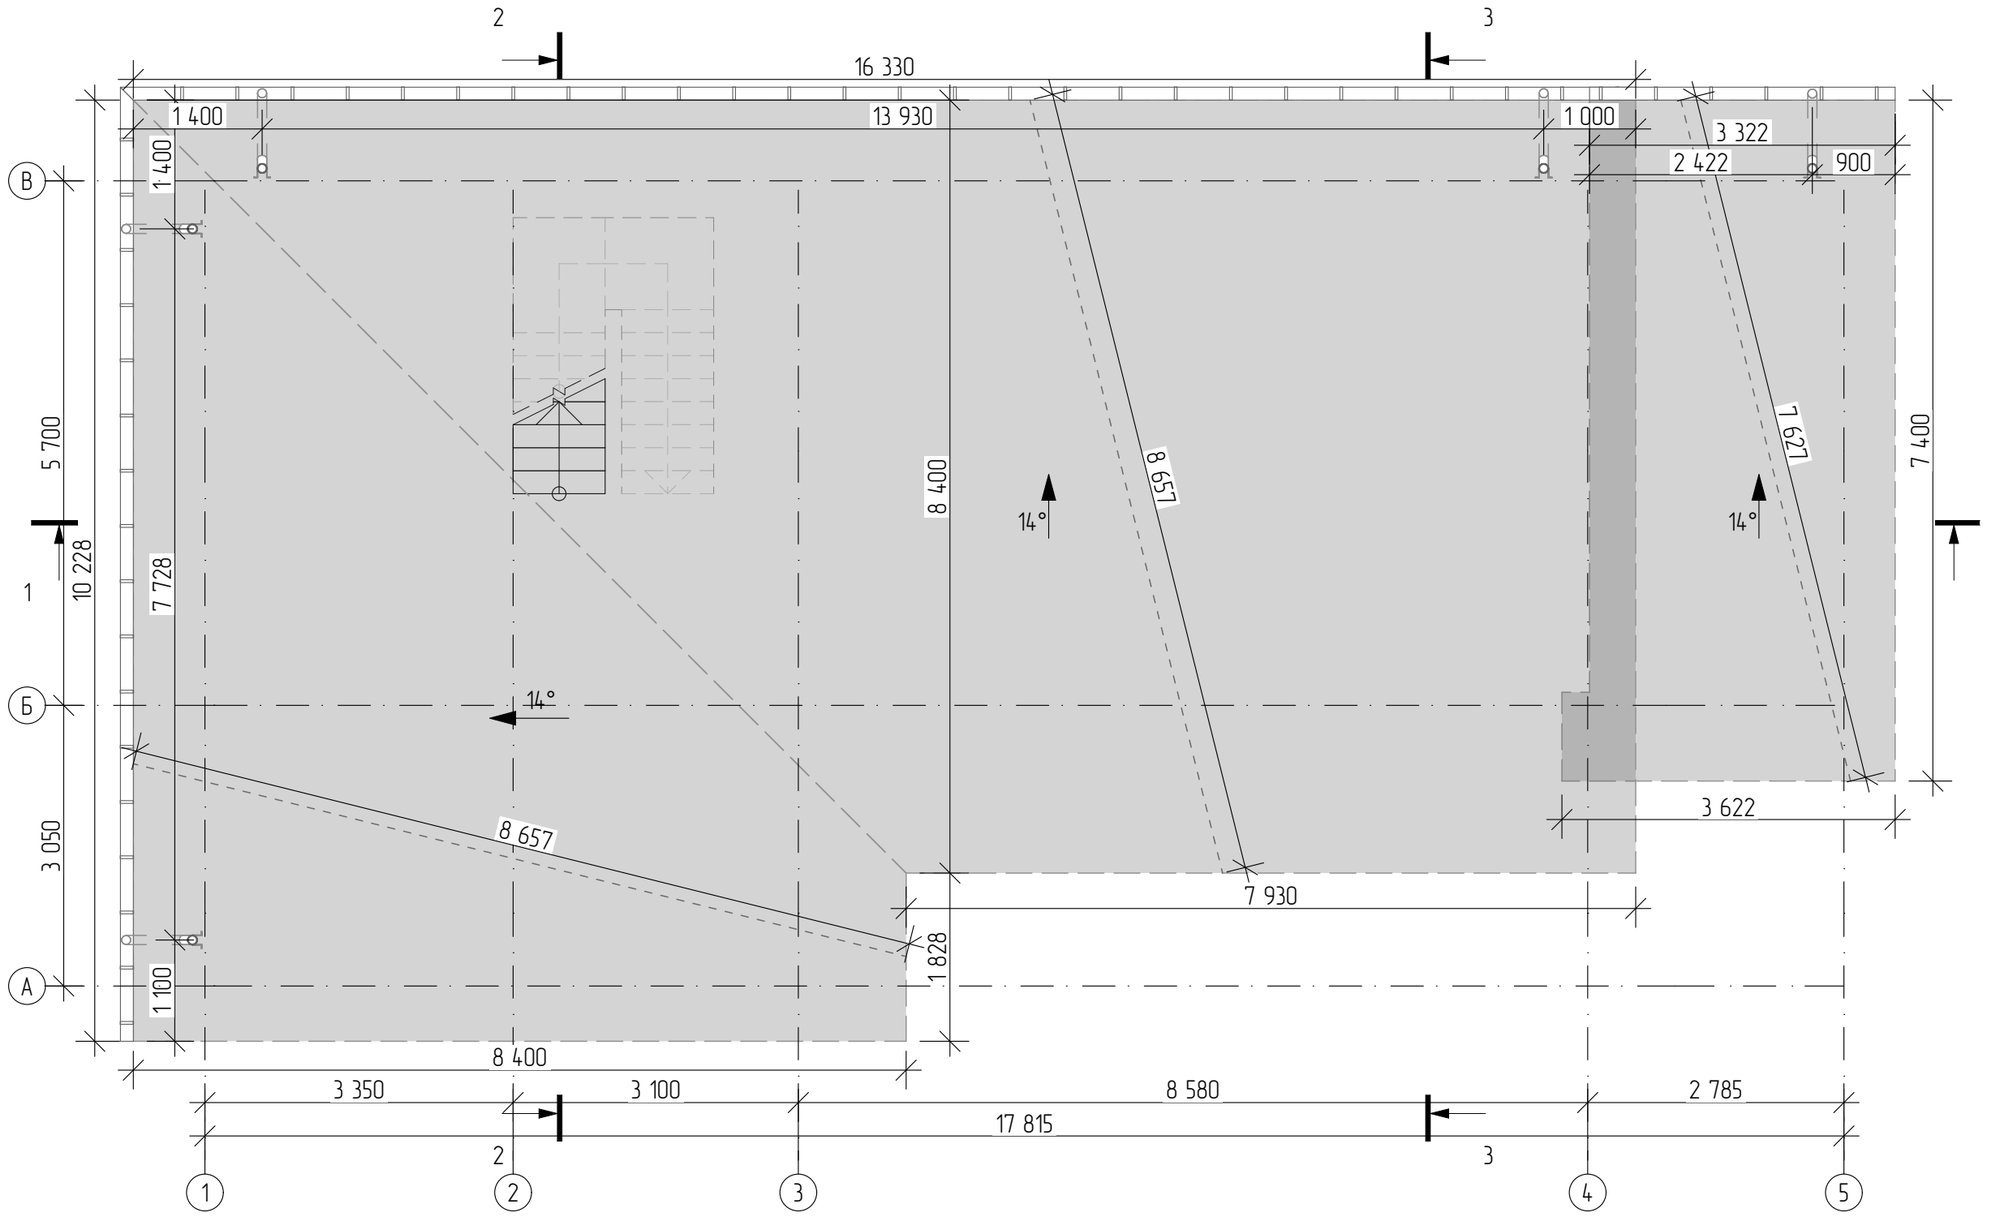

Изм.	Колуч.	Лист	№Док.	Подп.	Дата	Двухэтажное здание (баня)	Стадия	Лист	Листов
Разраб.							П		
Пров.									
Т. контр.									
Н. контр.						План крыши			
Утв.									

Разрез 1-1

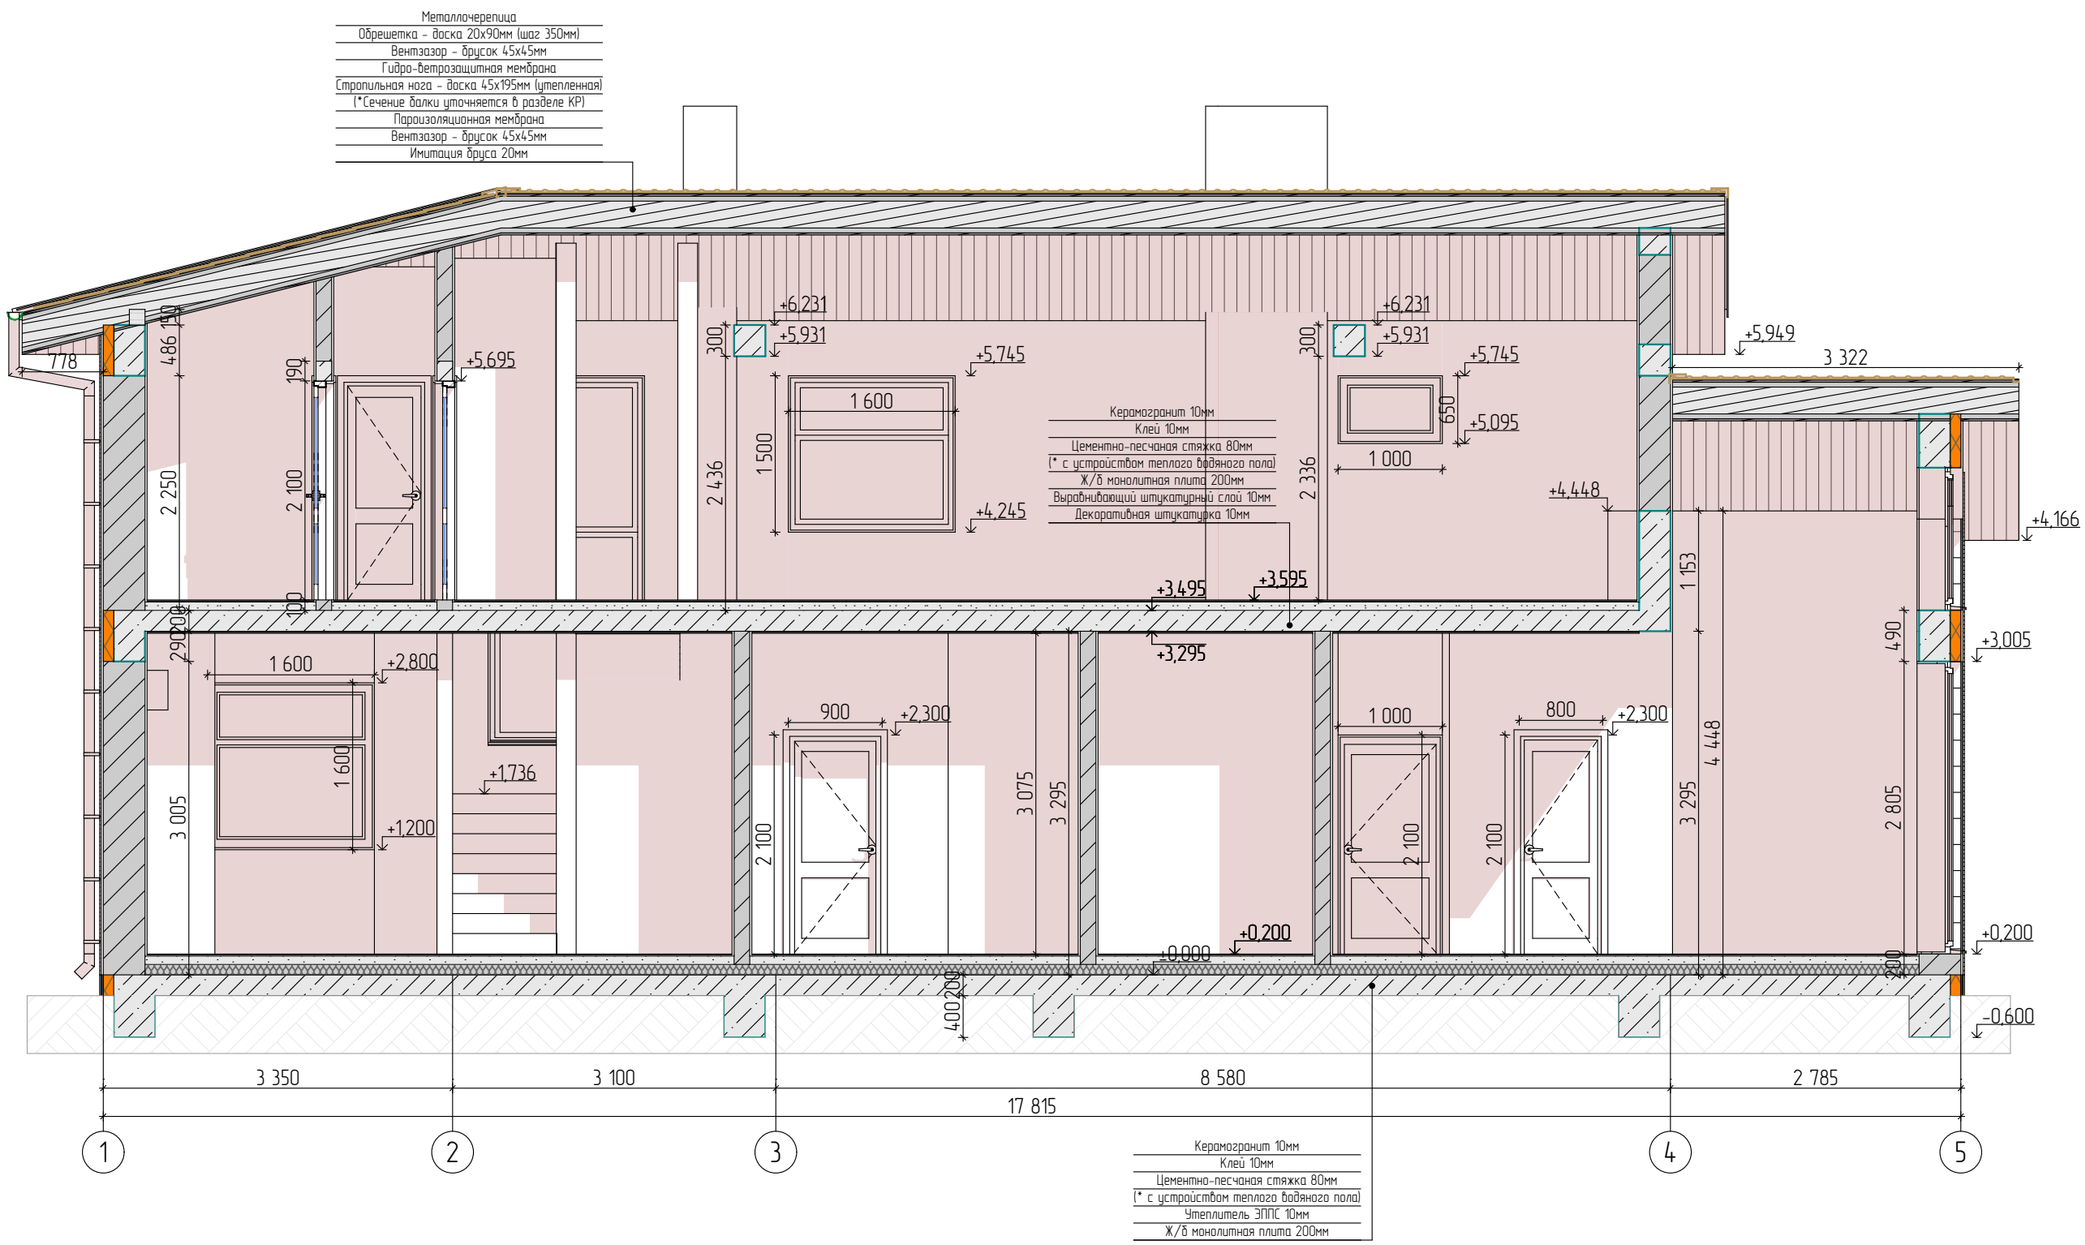

Изм.	Колуч.	Лист	№Док.	Подп.	Дата	Двухэтажное здание (баня)	Стадия	Лист	Листов
Разраб.							П		
Пров.									
Т. контр.									
Н. контр.						Разрез 1-1			
Утв.									

Разрез 2-2; Разрез 3-3

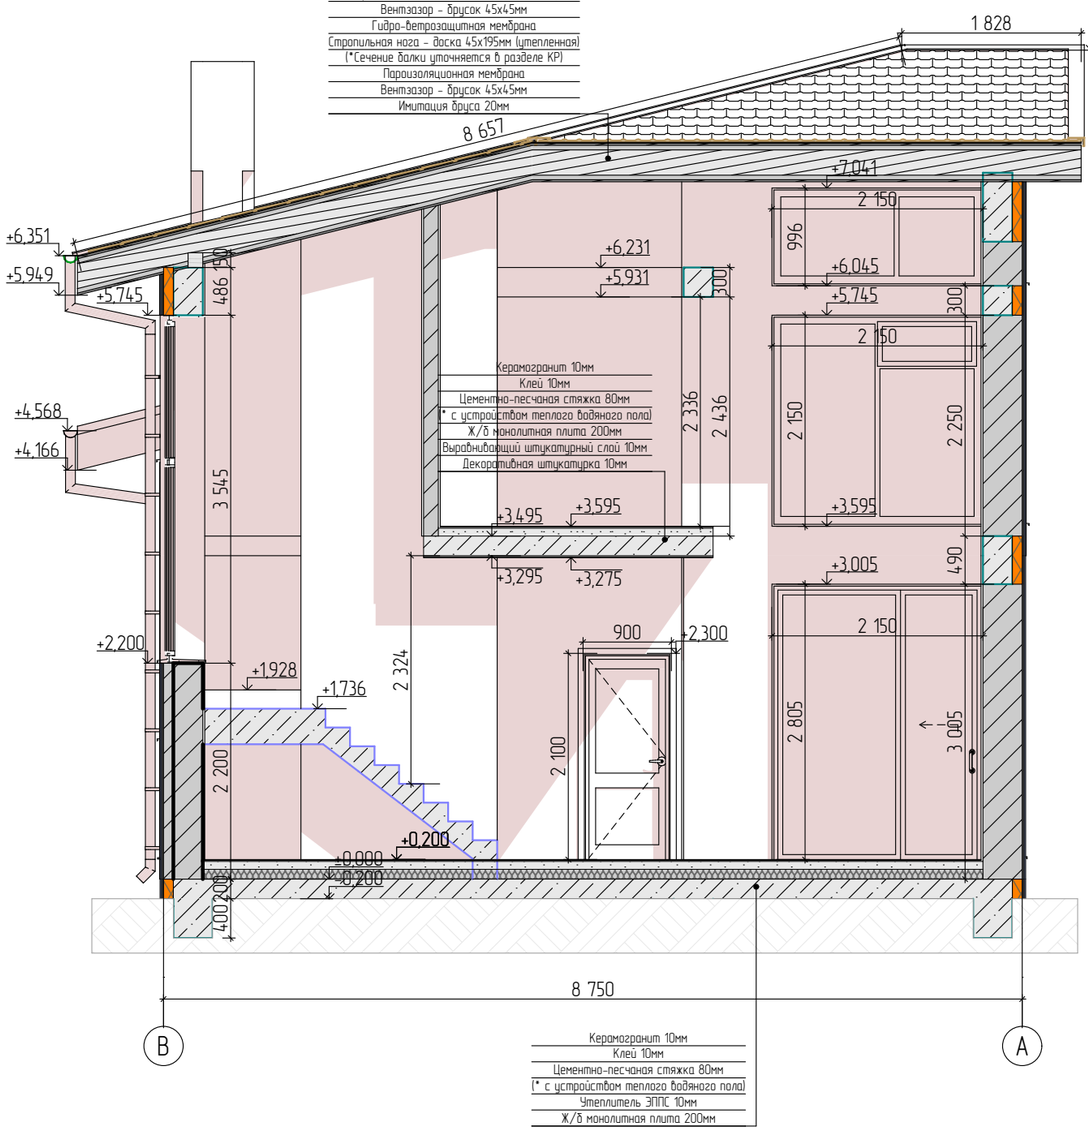

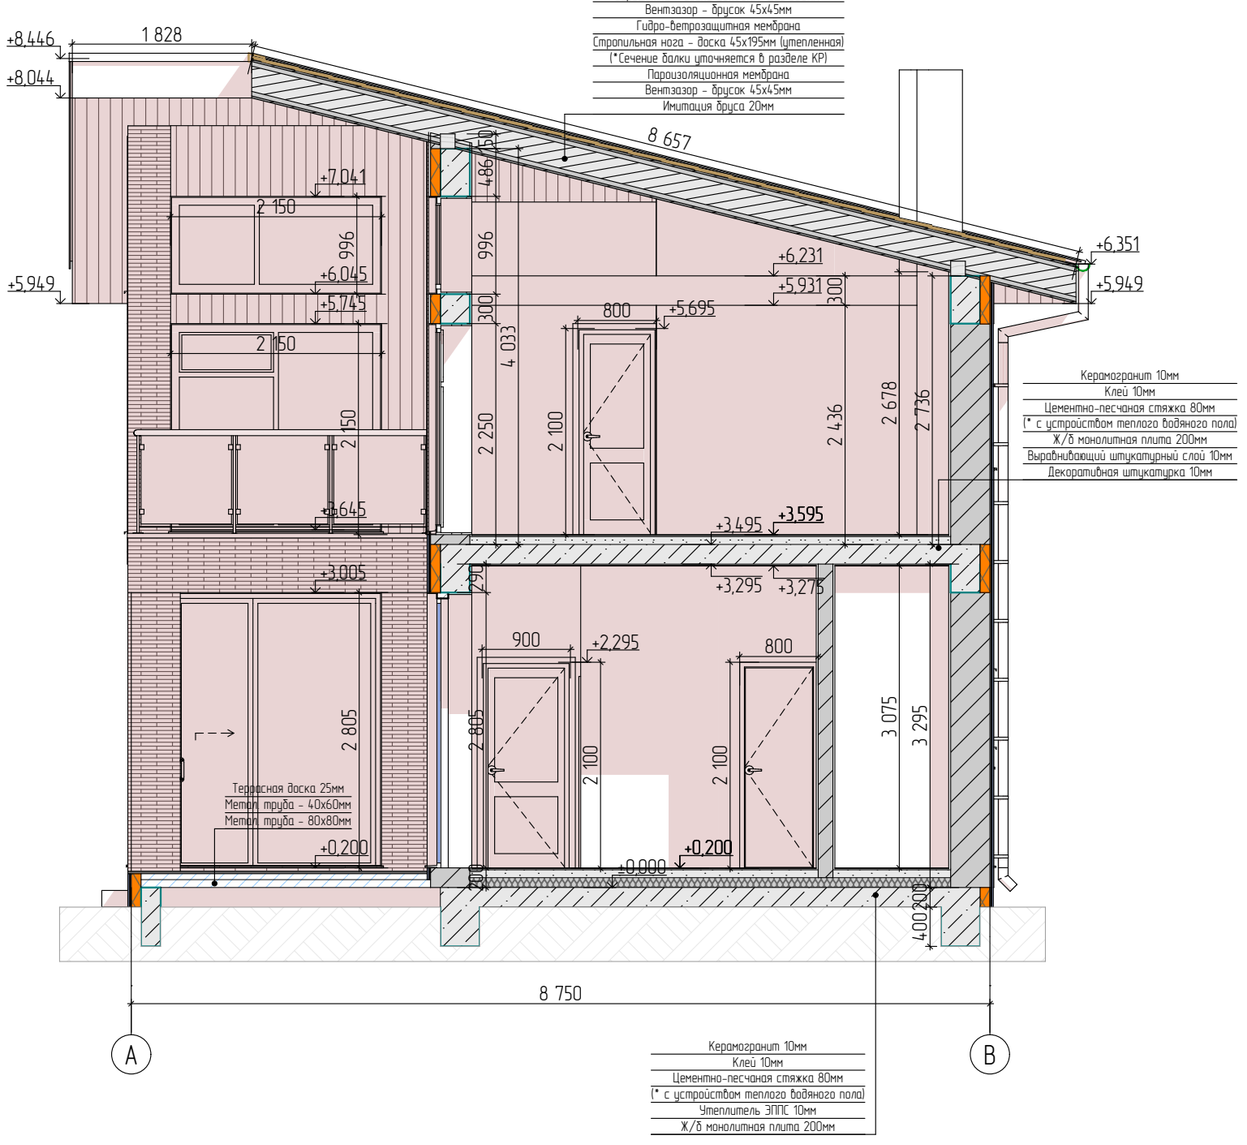

Изм.	Колуч.	Лист	№Док.	Подп.	Дата	Двухэтажное здание (баня)	Стадия	Лист	Листов
Разраб.							П		
Пров.									
Т. контр.						Разрез 2-2; Разрез 3-3			
Н. контр.									
Утв.									

Фасад 1-5

Изм.	Колуч.	Лист	№Док.	Подп.	Дата	Двухэтажное здание (баня)	Стадия	Лист	Листов
Разраб.							П		
Пров.									
Т. контр.									
Н. контр.						Фасад 1-5			
Утв.									

Фасад В-А

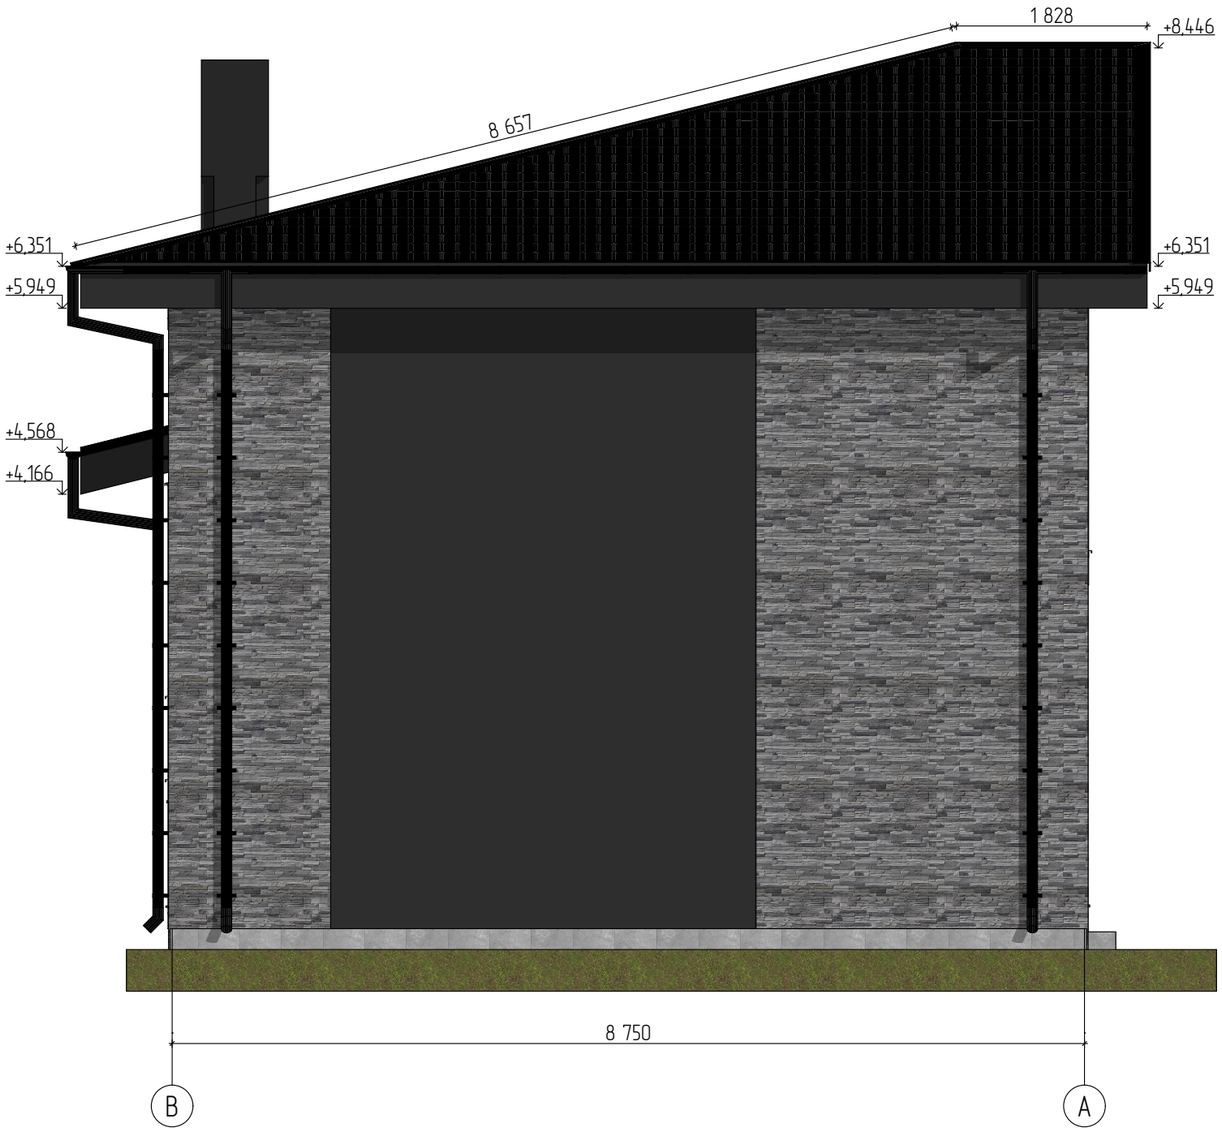

Условные обозначения:

1 – Искусственный камень

2 – Декоративная штукатурка

3 – Планкен вертикальный

4 – Водосточная система, металлочерепица, наличники, лобовая доска

Изм.	Колуч.	Лист	№Док.	Подп.	Дата	Двухэтажное здание (баня)	Стадия	Лист	Листов
Разраб.							П		
Пров.									
Т. контр.						Фасад В-А			
Н. контр.									
Утв.									

Фасад 5-1

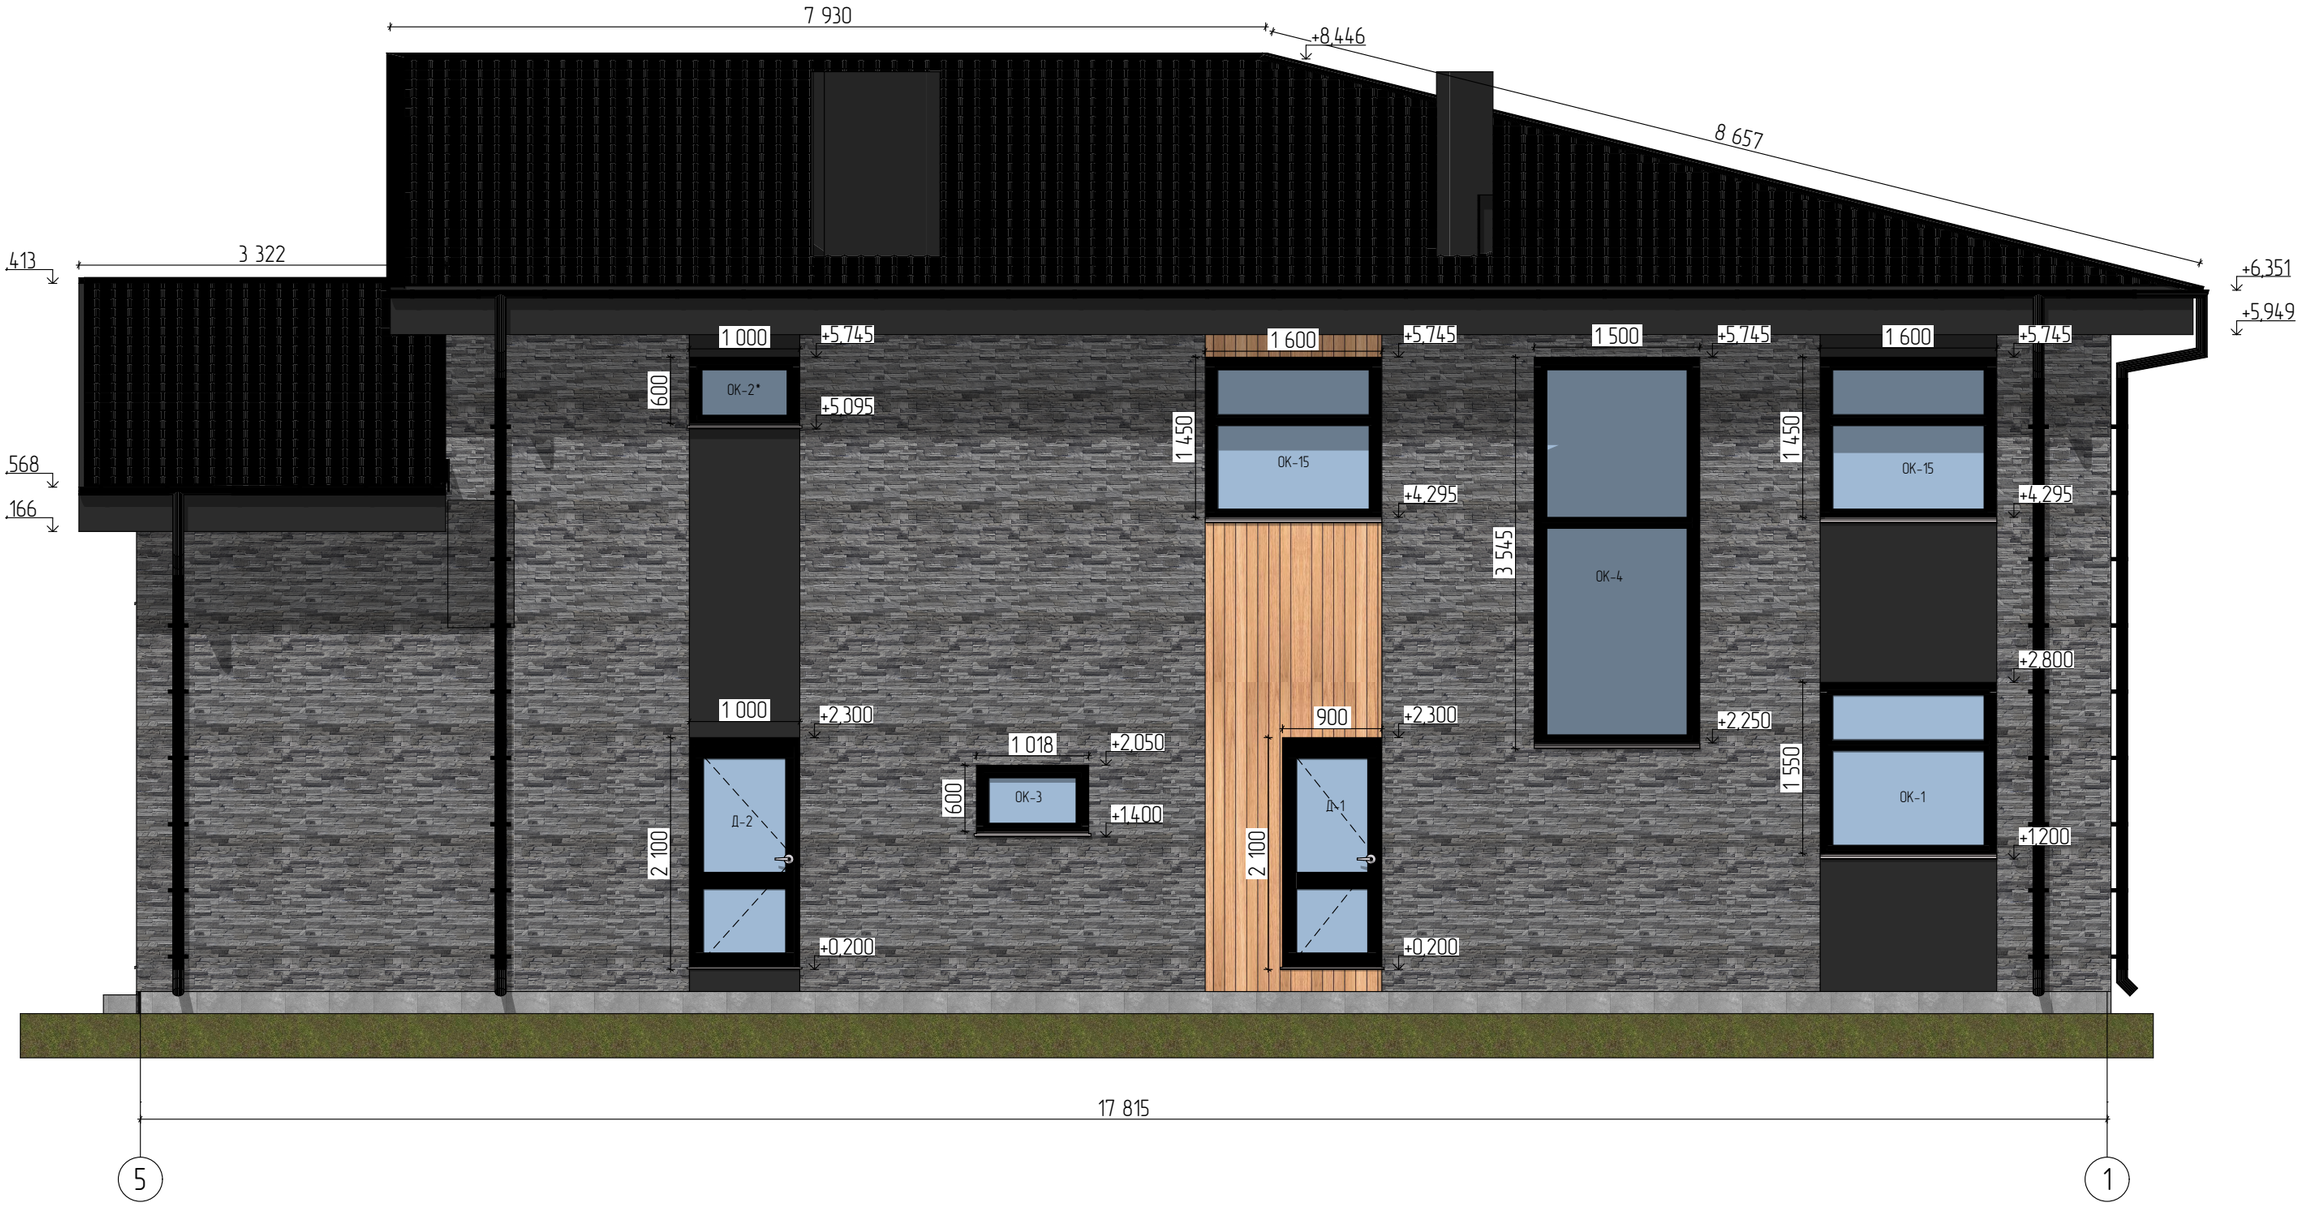

Изм.	Колич.	Лист	№Док.	Подп.	Дата.	Двухэтажное здание (баня)	Стадия	Лист	Листов
Разраб.							П		
Пров.									
Т. контр.									
Н. контр.						Фасад 5-1			
Утв.									

Фасад А-В

Условные обозначения:

1 – Искусственный камень

2 – Декоративная штукатурка

3 – Планкен вертикальный

4 – Водосточная система, металлочерепица, наличники, лобовая доска

Изм.	Колуч.	Лист	№Док.	Подп.	Дата.	Двухэтажное здание (баня)	Стадия	Лист	Листов
Разраб.							П		
Пров.									
Т. контр.						Фасад А-В			
Н. контр.									
Утв.									