Рабочая документация



Архитектурные решения
(раздел АР)
Одноэтажное здание
(баня)
Основной комплект чертежей
(планы, разрезы, фасады)

Архитектор _____ _____

Заказчик _____ _____

Москва
2026

Архитектурно-планировочные решения:
Эскизный проект одноэтажной бани общей площадью - 66,26м2, разработан на основании требований и пожеланий заказчика.
Баня закрытая.
Размеры строения в осях 1-4 - 13,5м; в осях А-В - 5,3м.
За относительную отметку ±0.000 принят уровень верха балок перекрытия.

Конструктивные решения:
1. Рабочие чертежи разработаны на основании задания на проетирования (АР).

2. Объект строительства расположен в следующих климатических условиях:
- Нормативный вес снегового покрова для III района (СНиП 2.01.07-85) - 180 кгс/м2;
- Нормативное ветровое давление для I района (СНиП 2.01.07-85) - 23 кгс/м2;
- Расчетная зимняя температура наружнего воздуха (СНиП 23-01-99) - минус 26 ОС;
- Нормативная глубина промерзания (СНиП 23-01-99) - 1,4 м;
- Полезная нагрузка на покрытие - 150 кгс/м2

.
3. Конструктивно строение представляет собой сооружение со свайным фундаментом, несущим каркасом, вальмовой/двускатной кровлей по деревянным стропилам.

4. При проведении строительных работ необходимо осуществлять технический надзор с ведением журнала работ. Осуществлять входной контроль материалов, вести приемку по каждому этапу работ.

5. - Фундамент - Сваи d108;
- Несущие конструкции - Каркас из строганной доски сечением 45х195(h)мм;
- Стропильная система - из строгонной доски сечением 45х145h)мм
- Крыша - Вальмовая;
- Кровля - Металлочерепица.

6. Все деревянные конструкции обработать огне-биозащитными септиками в соответствии со СНиП 3.04.03-80.

7. Кровельные работы выполнять в соответствии с требованиями фирмы производителя.

8. Все работы вести в строгом соответствии с требованиями СНиП 12.03.99 (Безопасность труда в строительстве).

9. При выполнении всех работ строго соблюдать меры противопожарной безопасности.

10. Возможна замена материалов аналогами.

*Решения, принятые в проекте и отображенные в чертежах, соответствуют требованиям экологических, санитарно -гигиенических, противопожарных и других норм, действующих на территории Российской Федерации, и обеспечивают безопасную для жизни и здоровья людей эксплуатацию объекта при соблюдении предусмотренных рабочих чертежей и мероприятий.

Изм.	Колич.	Лист	№Док.	Подп.	Дата.	Одноэтажное здание (баня)	Стадия	Лист	Листов
Разраб.							АР		
Пров.									
Т. контр.						Пояснительная записка			
Н. контр.									
Утв.									

Лист	Наименование
1	Титульный
2	Пояснительная записка
3	Состав чертежей
4	Визуализация
5	Визуализация
6	Визуализация
7	Визуализация
8	Визуализация
9	Визуализация
10	Маркировочный план
11	Размерный план
12	Ведомость заполнения оконных и дверных проемов
13	3д-вид
14	3д-вид
15	3д-вид
16	Маркировочные план стен и пола
17	Перечень ограждающих конструкций (лист 1)
18	Перечень ограждающих конструкций (лист 2)
19	Перечень ограждающих конструкций (лист 3)
20	План электрооборудования
21	План крыши
22	Разрез 1-1
23	Разрез 2-2
24	Разрез 3-3
25	Фасад 1-4
26	Фасад А-В
27	Фасад Б-А
28	Фасад 4-1

Изм.	Колуч.	Лист	№Док.	Подп.	Дата	Одноэтажное здание (баня)	Стадия	Лист	Листов
Разраб.							АР		
Пров.									
Т. контр.									
Н. контр.						Состав чертежей			
Утв.									



Изм.	Колуч.	Лист	№Док.	Подп.	Дата	Однoэтажное здание (баня)	Стадия	Лист	Листов
Разраб.							АР		
Пров.									
Т. контр.									
Н. контр.						Визуализация			
Утв.									

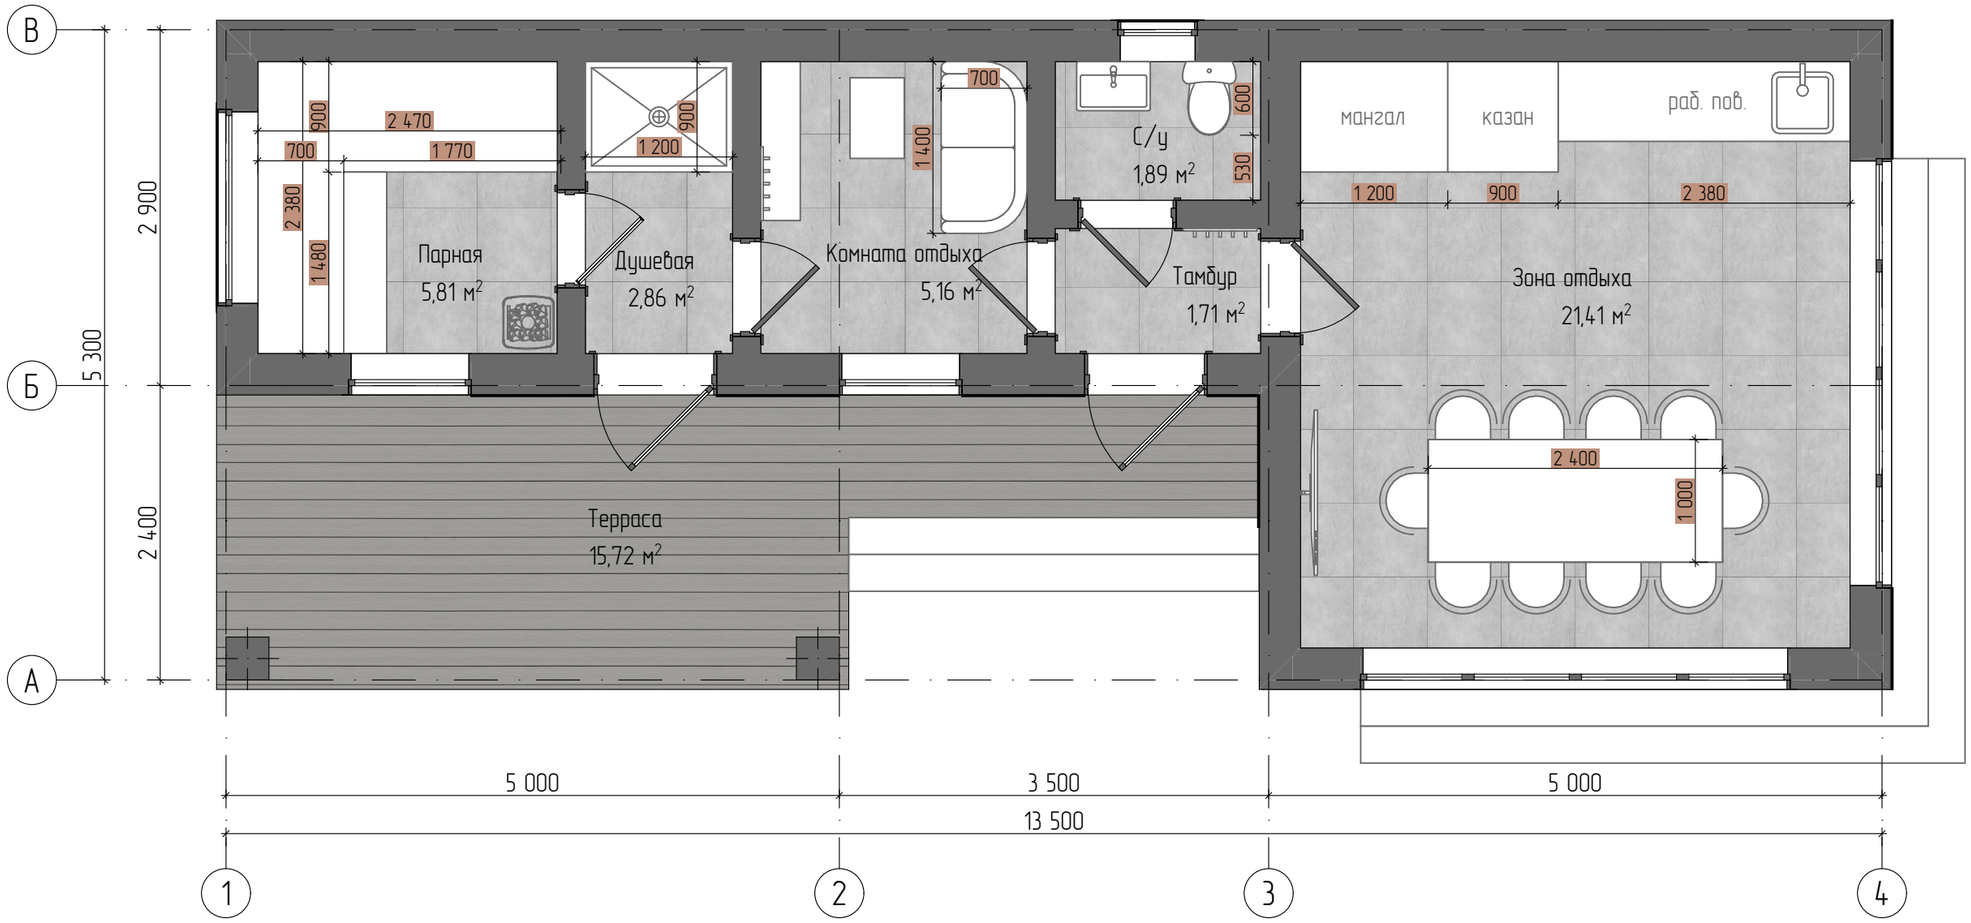


Изм.	Колуч.	Лист	№Док.	Подп.	Дата	Одноэтажное здание (баня)	Стадия	Лист	Листов
Разраб.							АР		
Пров.									
Т. контр.									
Н. контр.						Визуализация			
Утв.									



Изм.	Колуч.	Лист	№Док.	Подп.	Дата.	Однозтажное здание (баня)	Стадия	Лист	Листов
Разраб.		.					АР		
Пров.									
Т. контр.						Визуализация			
Н. контр.									
Утв.									

Маркировочный план




Экспликация 1-й этаж		
№	Название	Площадь, м2
Внутренняя площадь		
1	Зона отдыха	21,41
1	Терраса	15,72
2	Тамбур	1,71
3	С/у	1,89
4	Комната отдыха	5,16
5	Душевая	2,86
6	Парная	5,81
Общая площадь пристройки к дому		
		66,26

1. Вся индивидуальная мебель выполняется по отдельному проекту с детальной проработкой и калькуляцией. Чертежи предоставляет фирма-изготовитель столярных изделий.
2. Цветовое решение материалов отделки показаны в проекте приблизительно.

Изм.	Колуч.	Лист	№Док.	Подп.	Дата	Одноэтажное здание (баня)	Стадия	Лист	Листов
Разраб.							АР		
Пров.									
Т. контр.									
Н. контр.						Маркировочный план			
Утв.									


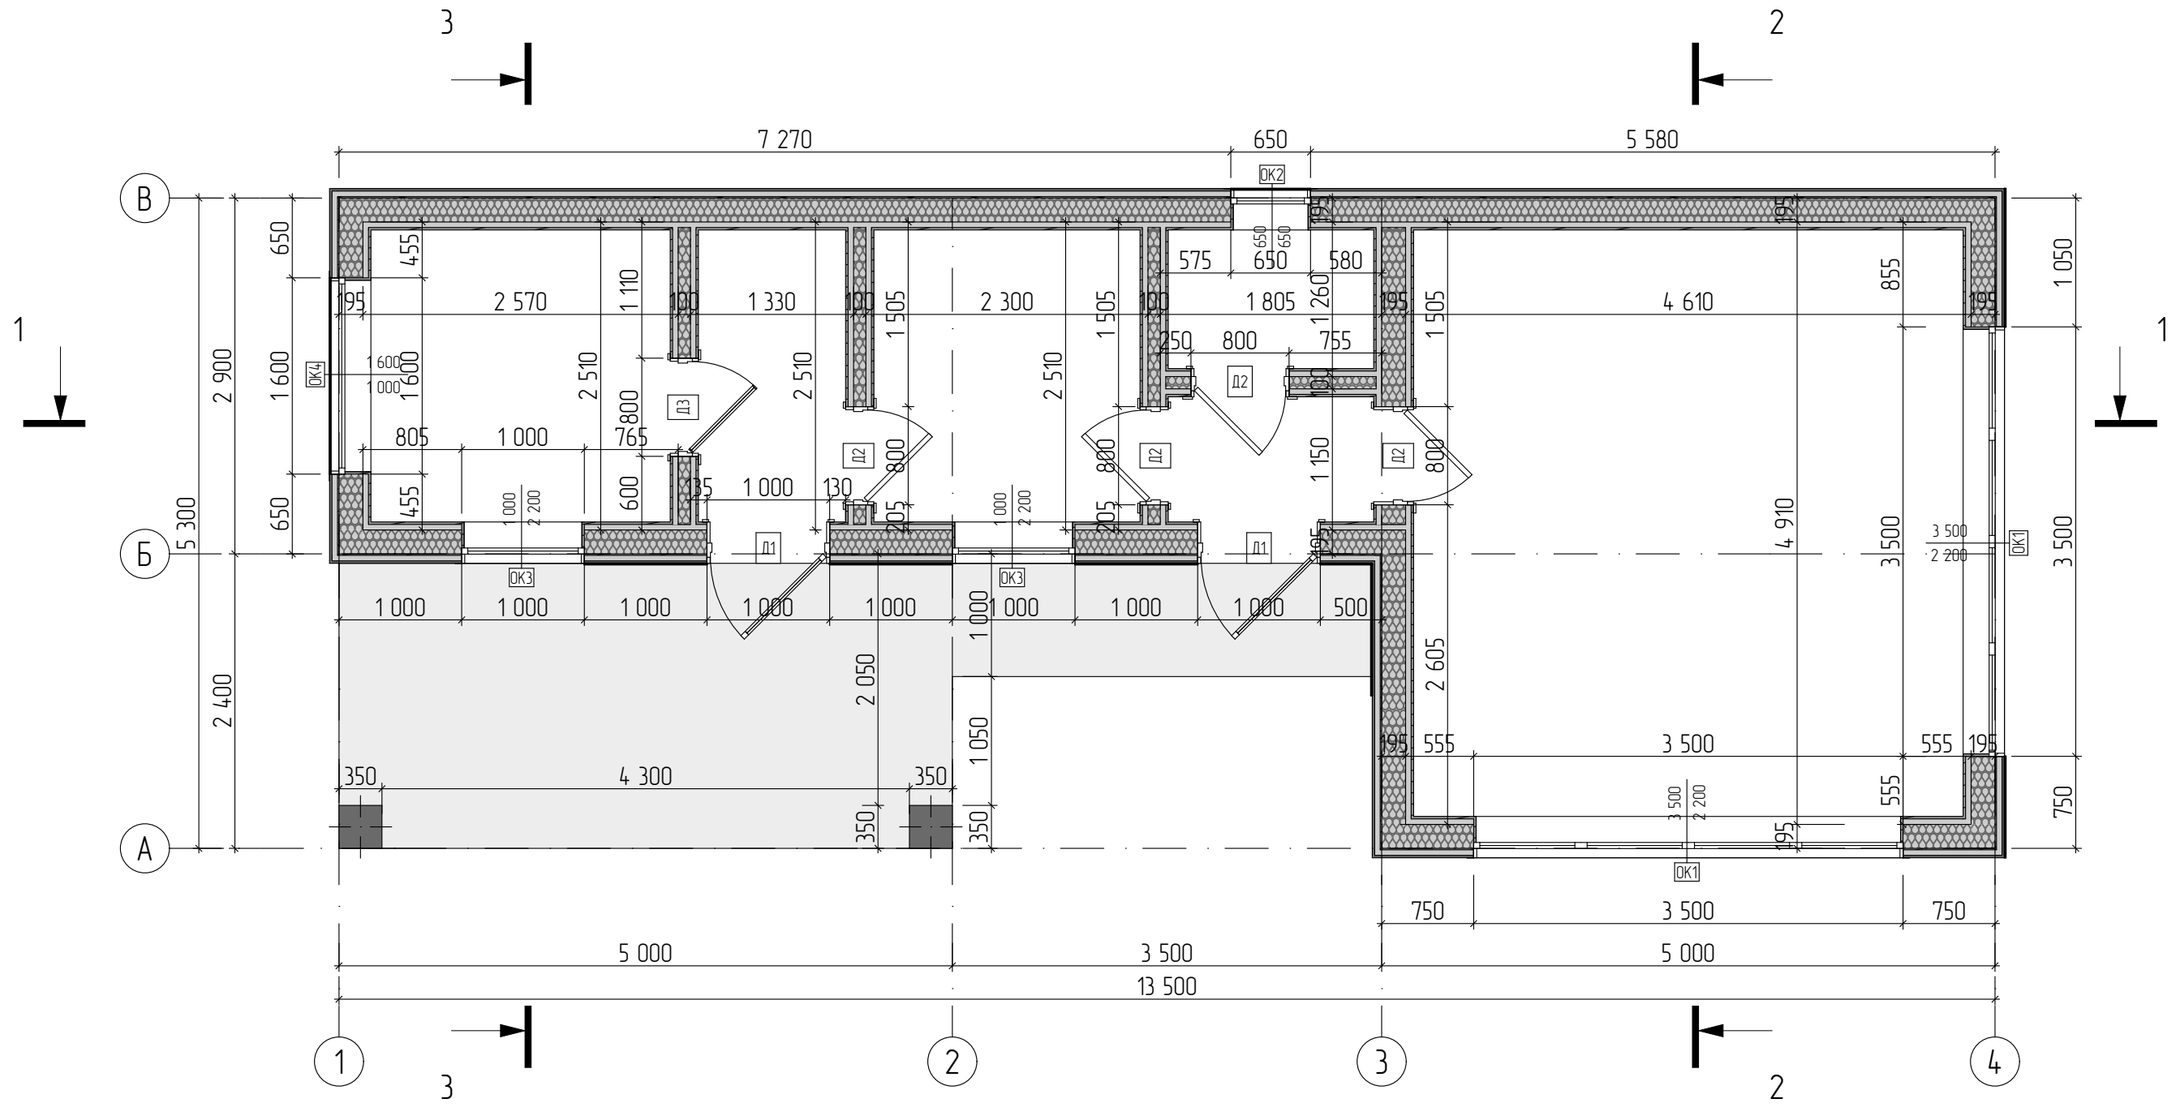
Размерный план






1. Размеры указаны без учета отделки.
2. Спецификацию оконных и дверных проёмов см. след. лист.

Изм.	Колуч.	Лист	№Док.	Подп.	Дата	Однoэтажное здание (баня)	Стадия	Лист	Листов
Разраб.							АР		
Пров.									
Т. контр.						Размерный план			
Н. контр.									
Утв.									

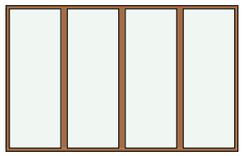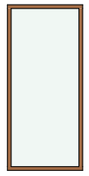Ведомость заполнения оконных и дверных проемов

Ведомость заполнения оконных проемов				
Название	Размер проема Ш х В, мм	Кол-во, шт	Вид	Площадь
ОК1	3 500×2 200	2		7,70
ОК2	650×650	1		0,42
ОК3	1 000×2 200	2		2,20
ОК4	1 600×1 000	1		1,60
				21,82 м²

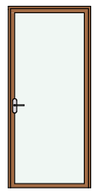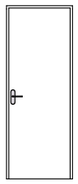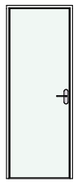Ведомость заполенения дверных проемов				
Название	Размер проема Ш х В, мм	Кол-во, шт	Вид	Площадь
Д1	1 000×2 200	2		2,20
Д2	800×2 100	4		1,68
Д3	800×2 100	1		1,68
				12,80 м²

1. Изготовление окон и дверей определяется заказчиком, допускается изменение открывания окон и дверей;
2. При заказе оконных и дверных блоков необходим обмер по месту от изготовителя;
3. Оконные и дверные изделия изображены со стороны открывания.

Изм.	Колуч.	Лист	№Док.	Подп.	Дата.		
Разраб.						Одноэтажное здание (баня)	Стадия: АР; Лист; Листов
Пров.							
Т. контр.							
Н. контр.						Ведомость заполнения оконных и дверных проемов	
Утв.							


Изм.	Кол.уч.	/lucm	№док.	Подп.	Дата

Разраб.	
Пров.	
Т. контр.	
Н. контр.	
Утв.	

Однокомнатное задние (бокл)

Стадия	/lucm	/lucmob
АР		

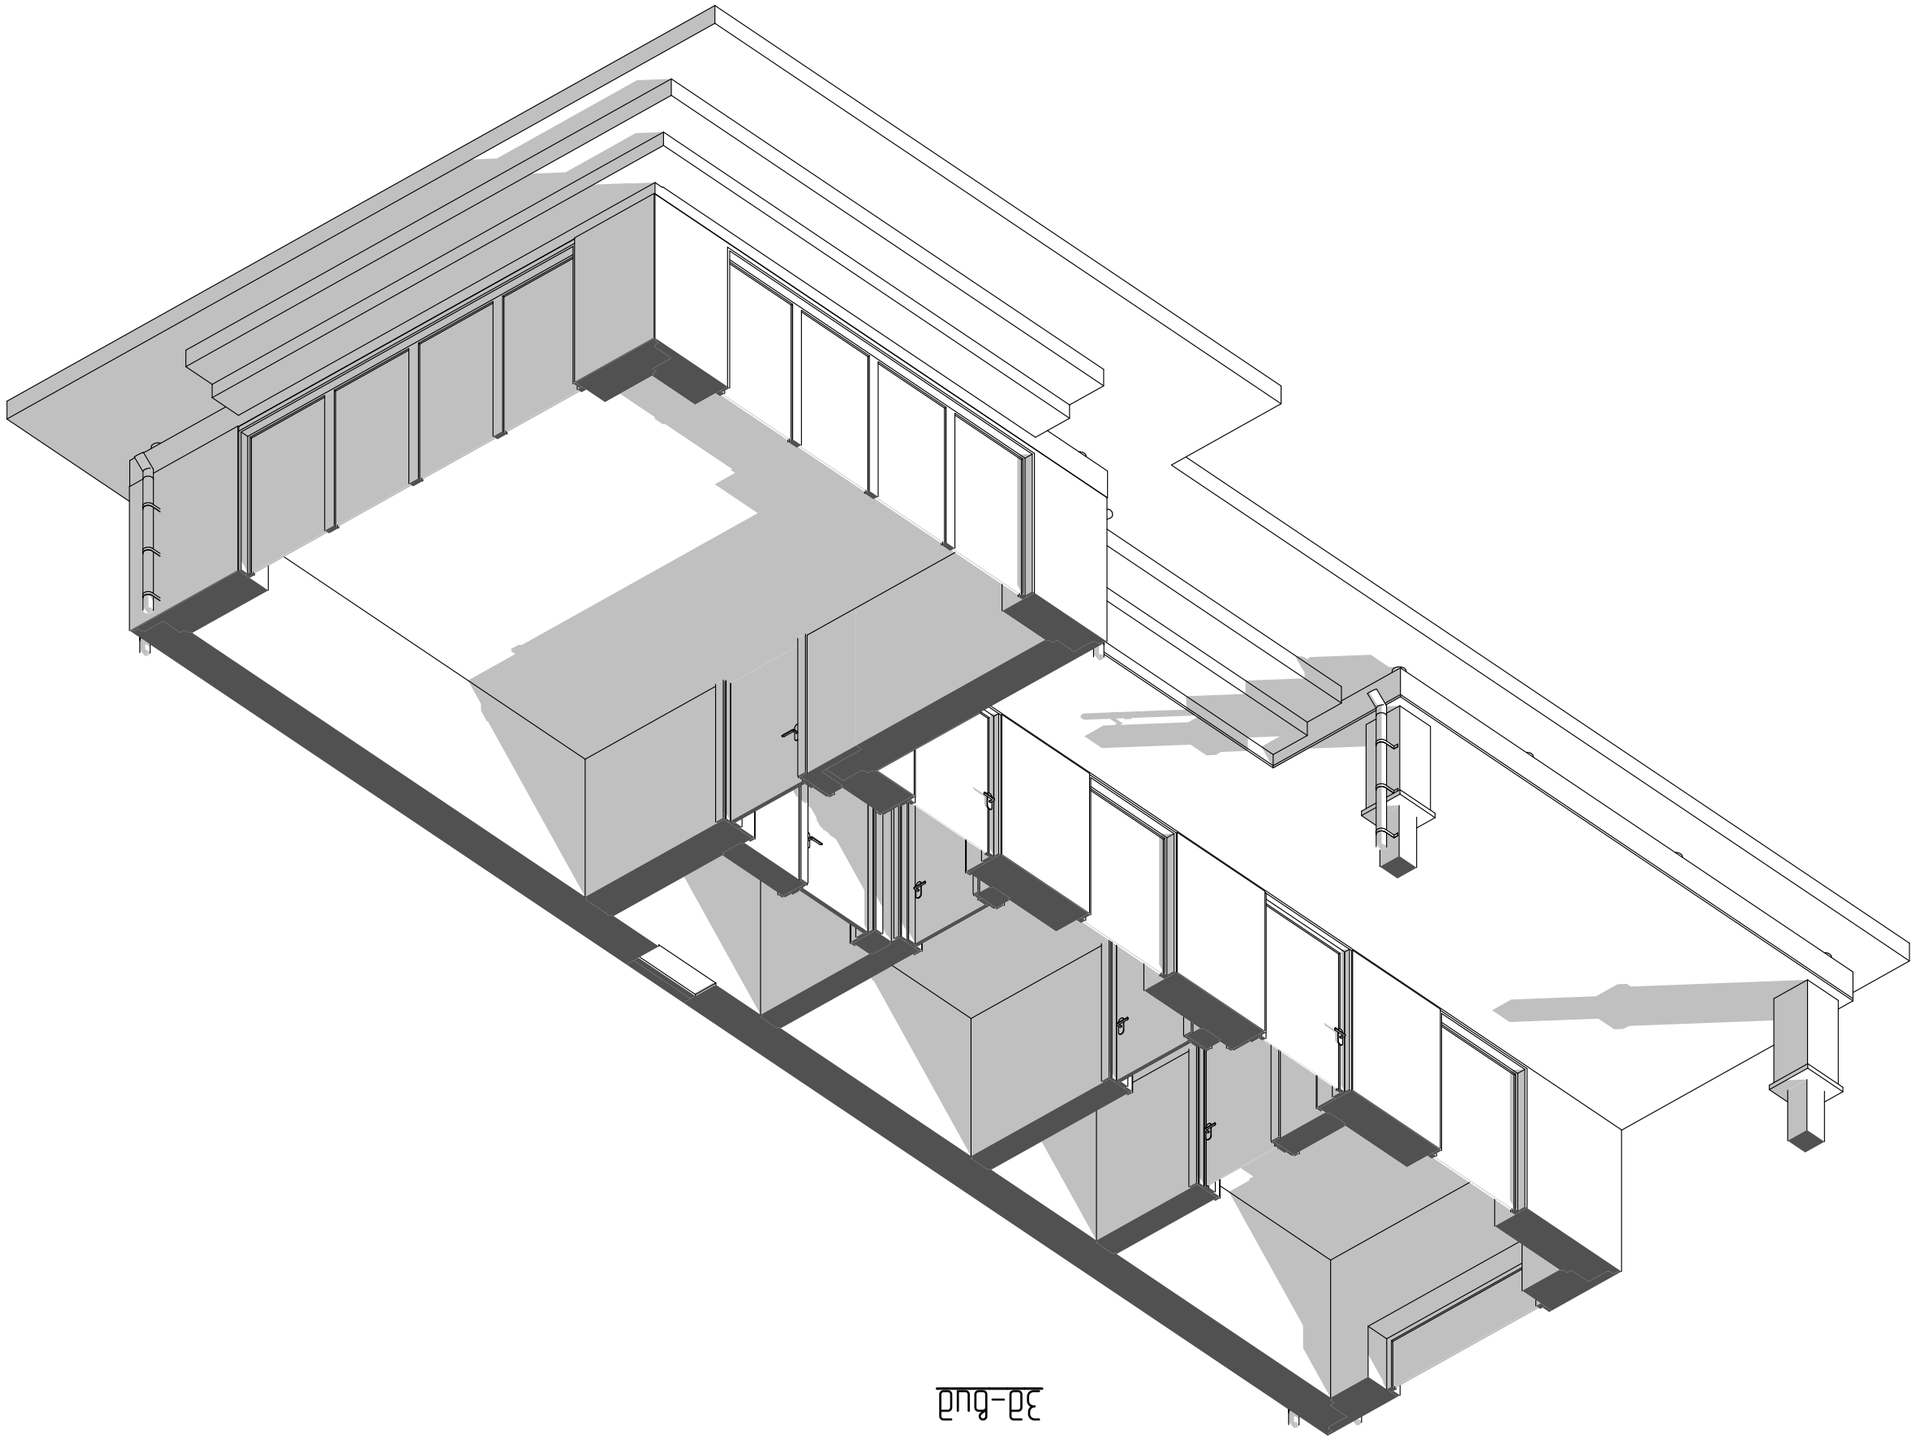3d-bud



3d-bud


Изм.	Кол.уч.	/lucm	№док	Подп.	Дата

Разраб.		
Пров.		
Т. контр.		
Н. контр.		
Утв.		

Одноэтажное здание (баня)

Стадия	/lucm	/lucmob
АР		

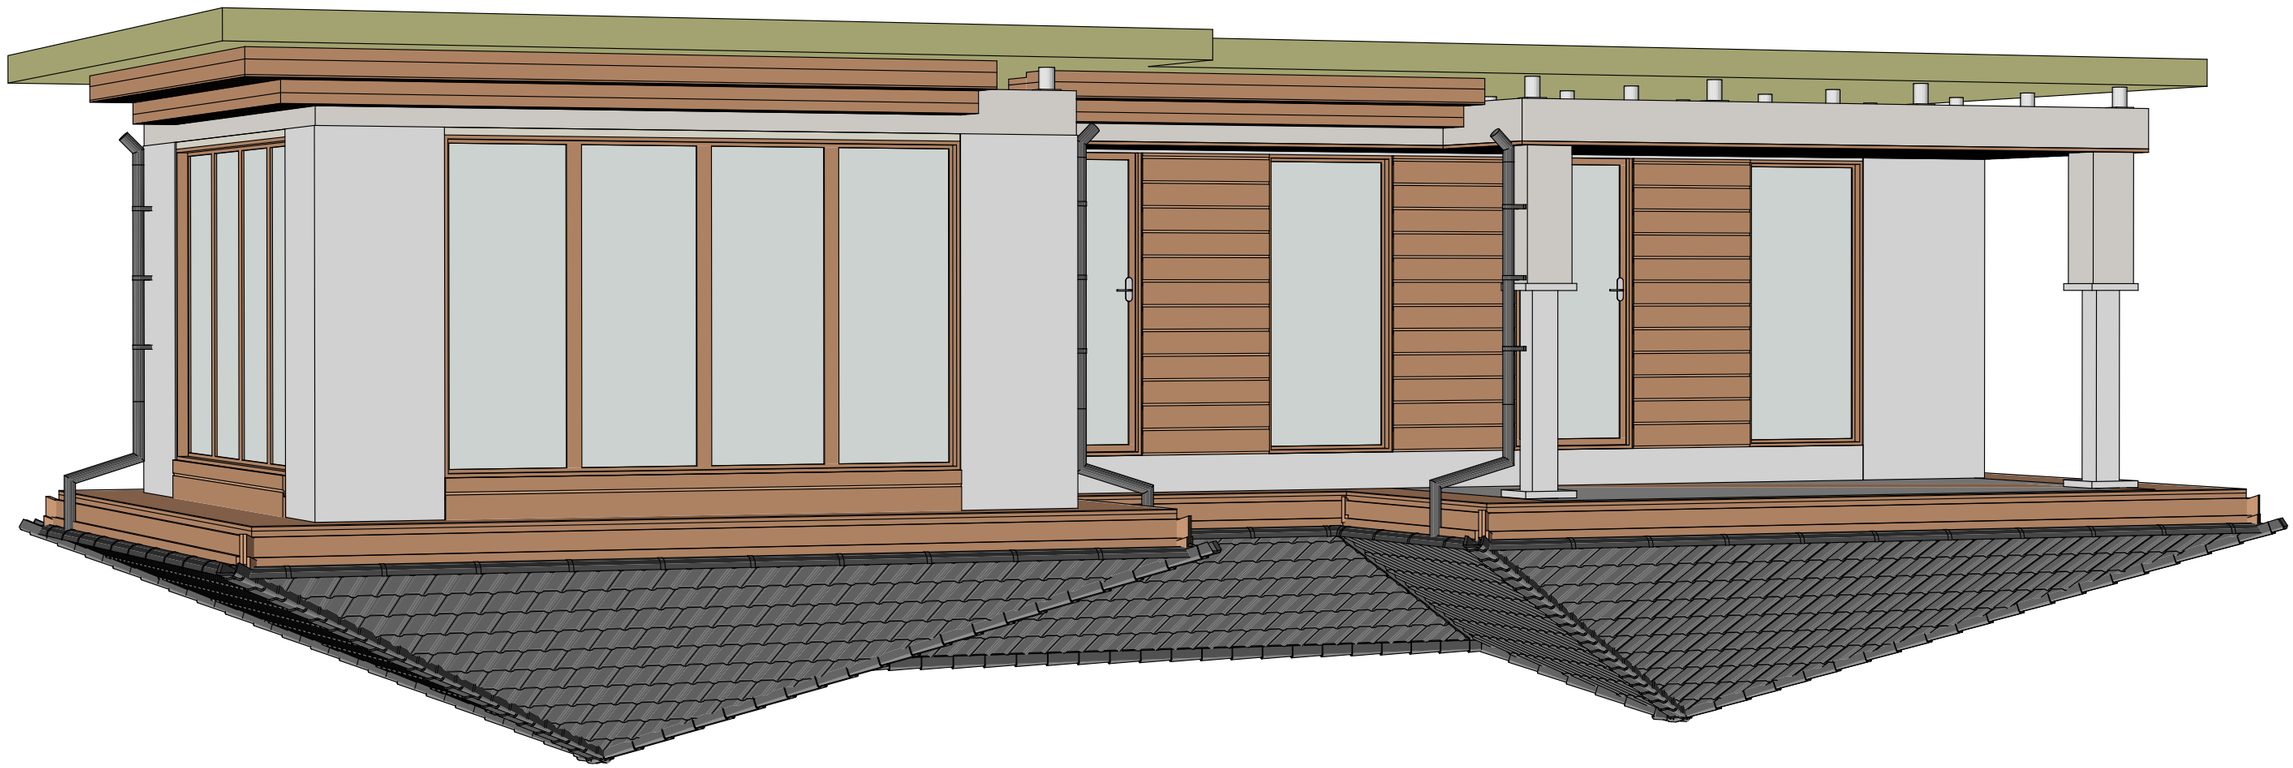3d-вид



3d-вид


Изм.	Кол.уч.	/lucm	№док.	Подп.	Дата

Разраб.	
Пров.	
Т. контр.	
Н. контр.	
Утв.	

Стадия	/lucm	/lucmob
АР		


Одноэтажное задние (баня)

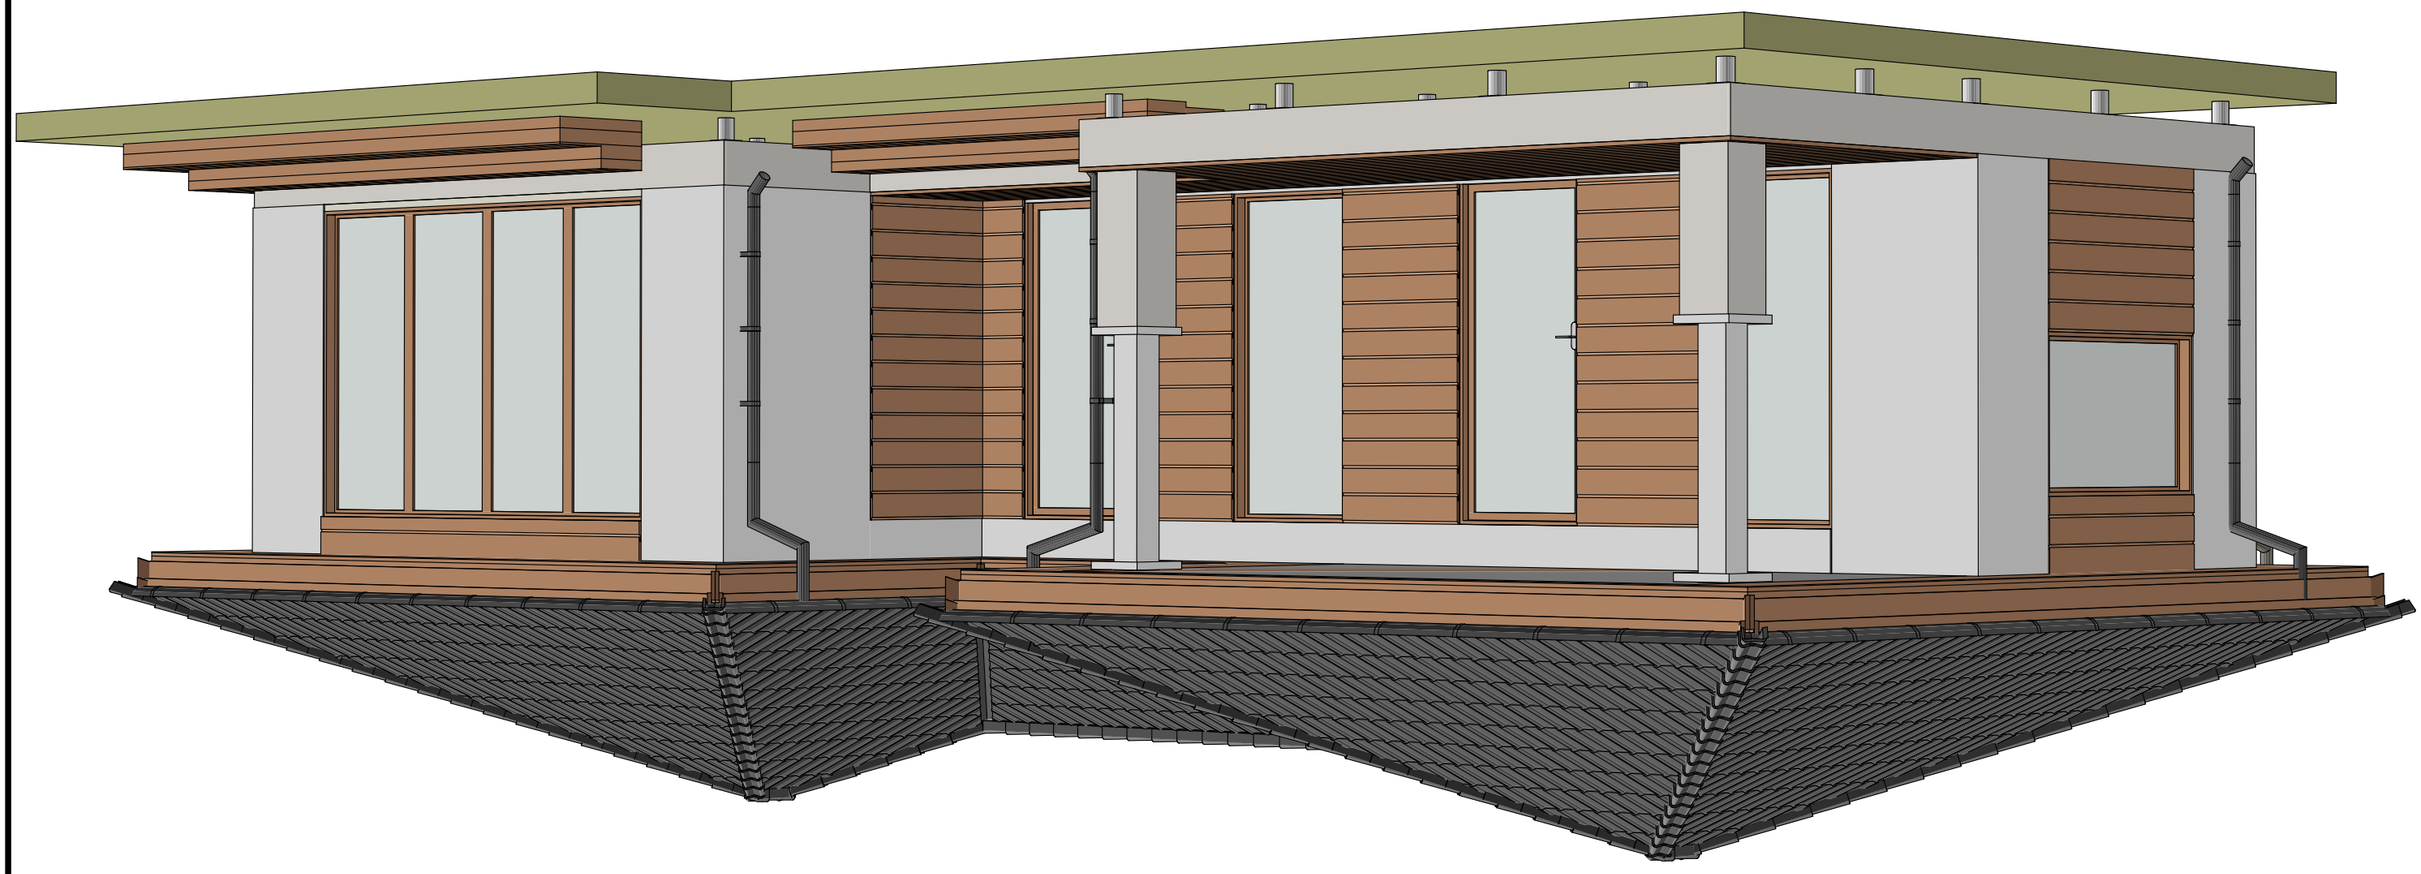3д-бид



3д-бид

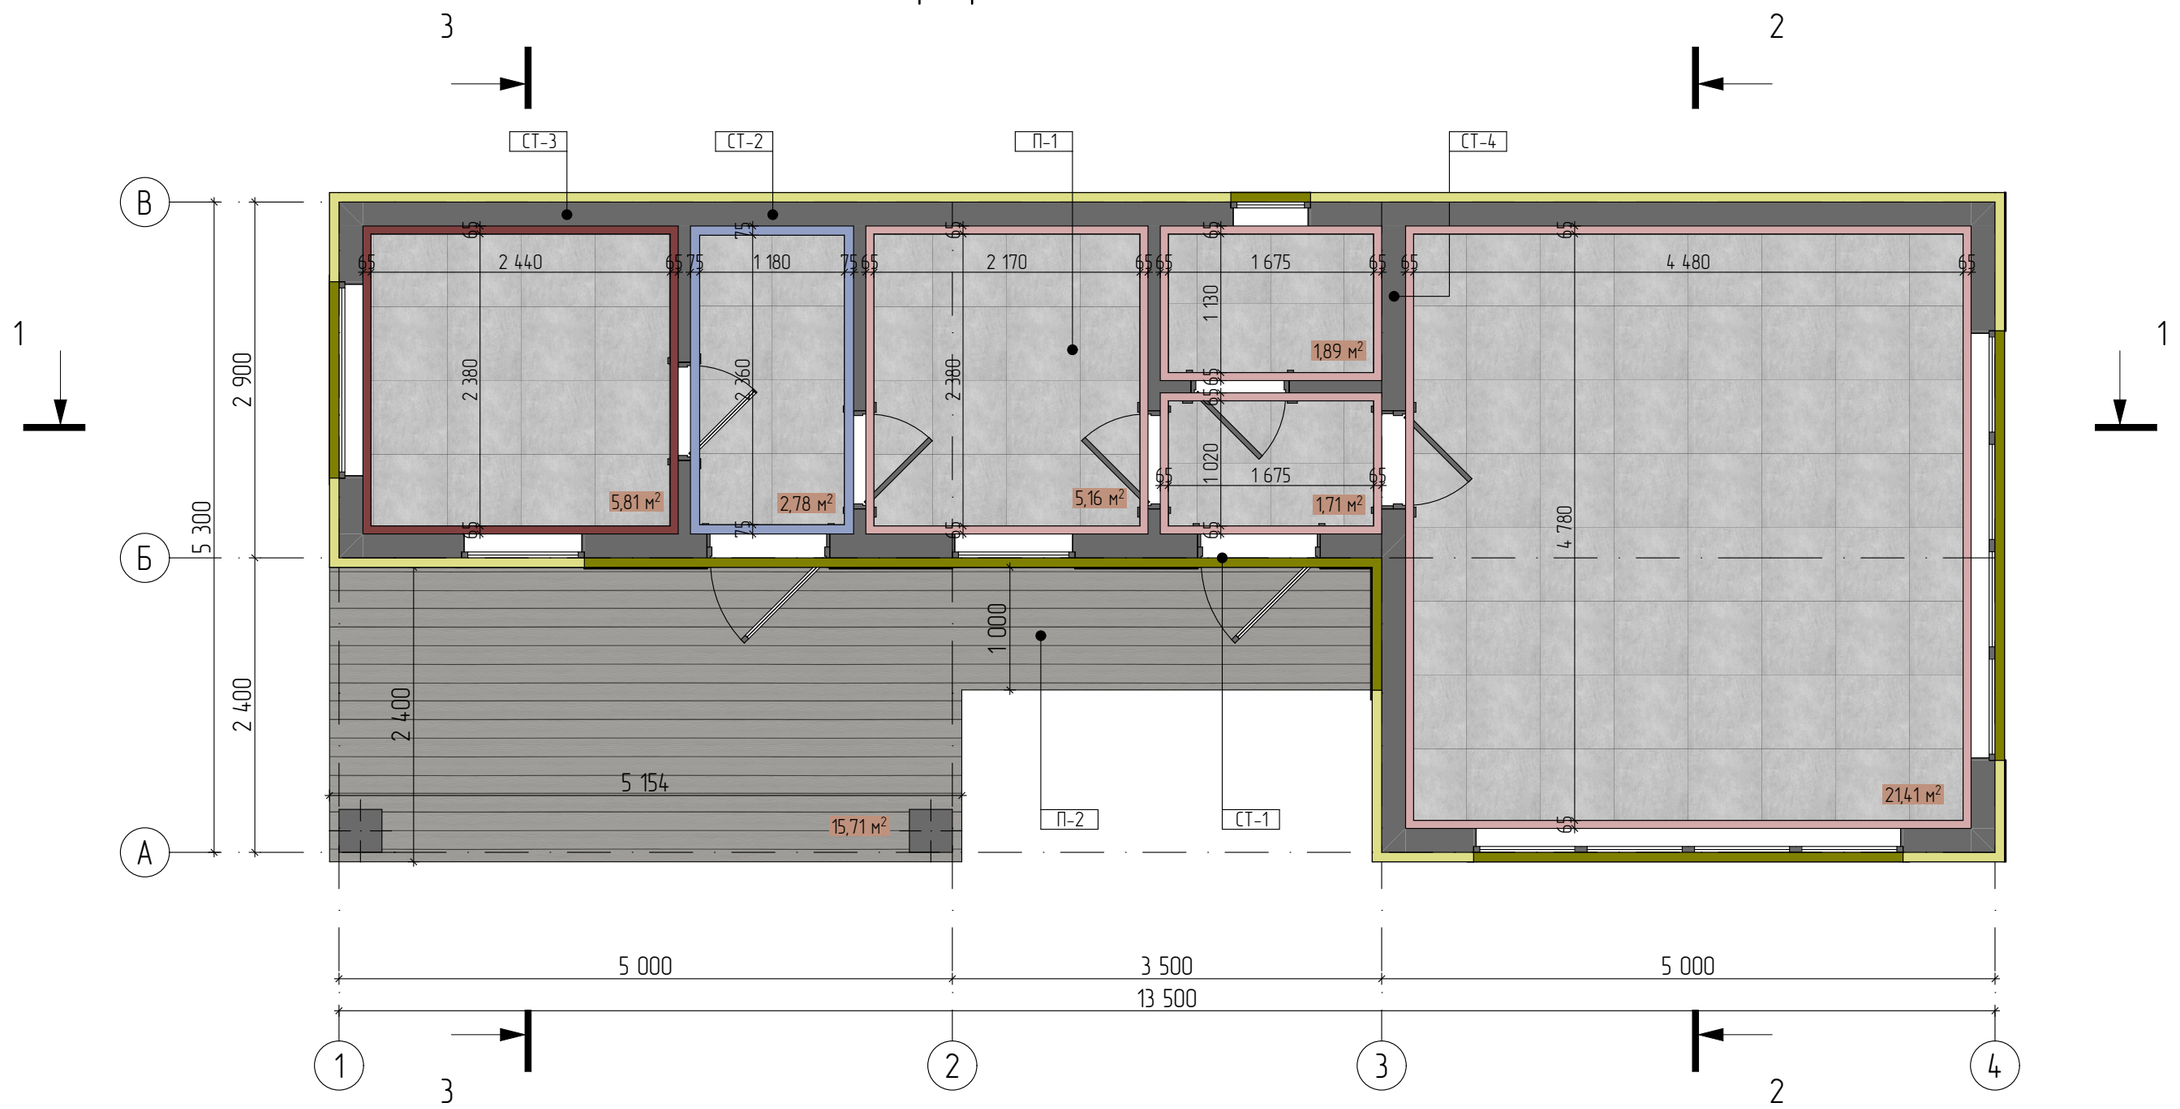Маркировочные план стен и пола



Условные обозначения:

Пирог покрытия пола:

-По керамограниту




-По ДПК


Пирог отделки стен:

- Фиброцементные панели 20мм
- Планкен 20мм
- Имитация бруса 20мм
- Керамогранит 10мм
- Вагонка 20мм

Изм.	Колуч.	Лист	№Док.	Подп.	Дата	Однозтажное здание (баня)	Стадия	Лист	Листов
Разраб.							АР		
Пров.									
Т. контр.						Маркировочные план стен и пола			
Н. контр.									
Утв.									

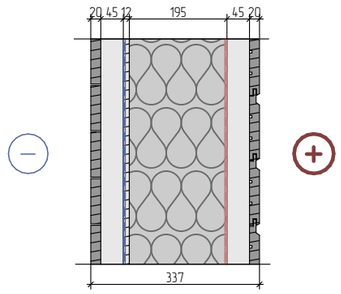
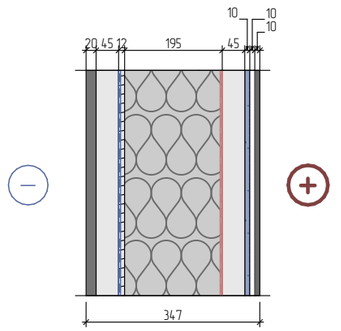
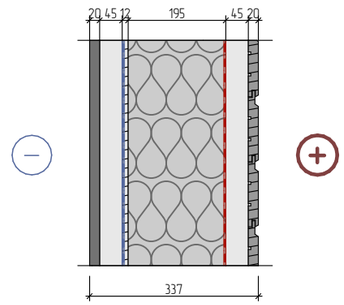
Перечень ограждающих конструкций (лист 1)

Наименование	Графическое изображение	Перечень материалов
СТ-1		Планкен 20мм Вентзазор - брусок 45х45мм Гидро-ветрозащитная мембрана Фанера 12мм Стойка - 45х195мм (Утепленная 200мм) Пароизоляционная мембрана Вентзазор - брусок 45х45мм Имитация бруса 20мм
СТ-2		Фиброцементные панели 20мм Вентзазор - брусок 45х45мм Гидро-ветрозащитная мембрана Фанера 12мм Стойка - 45х195мм (Утепленная 200мм) Пароизоляционная мембрана Вентзазор - брусок 45х45мм ЦСП 10мм Клей 10мм Керамогранит 10мм
СТ-3		Фиброцементные панели 20мм Вентзазор - брусок 45х45мм Гидро-ветрозащитная мембрана Фанера 12мм Стойка - 45х195мм (Утепленная 200мм) Пароизоляционная мембрана (алюм. фольга) Вентзазор - брусок 45х45мм Вагонка 20мм

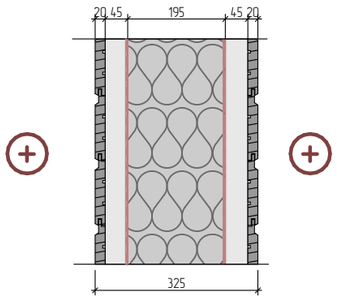Наименование	Графическое изображение	Перечень материалов
СТ-4		Имитация бруса 20мм Вентзазор - брусок 45х45мм Пароизоляционная мембрана Стойка - 45х195мм (Утепленная 200мм) Пароизоляционная мембрана Вентзазор - брусок 45х45мм Имитация бруса 20мм




Изм.	Колич.	Лист	№Док.	Подп.	Дата	Одноэтажное здание (баня)	Стадия	Лист	Листов
Разраб.							АР		
Пров.									
Т. контр.						Перечень ограждающих конструкций (лист 1)			
Н. контр.									
Утв.									

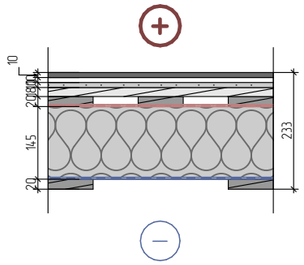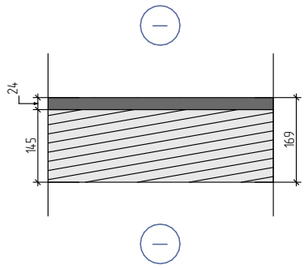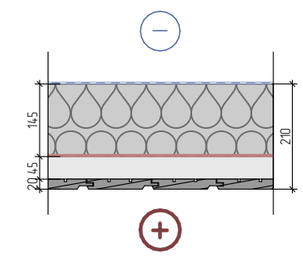Перечень ограждающих конструкций (лист 2)

Наименование	Графическое изображение	Перечень материалов
П-1		Керамогранит 10мм Клей 10мм *с устройством эл. теплого пола ЦСП 10мм Фанера 18мм Вентбрусок - доска 20х90мм Пароизоляционная мембрана Лага перекрытия - 45х145мм (Утепленная 150мм) Гидроветрозащитная мембрана Просечка (сетка, ячейка 5х5мм) Обрешетка - доска 20х90мм (шаг 400мм) Нижняя обвязка - 3 сращеная доска 50х150мм
П-2		ДПК 24мм Лага перекрытия - 45х145мм Нижняя обвязка - 3 сращеная доска 50х150мм
П-3 (*чердачное перекрытие)		Гидро-ветрозащитная мембрана Лага перекрытия - 45х145мм (с утеплителем в теле 150мм) Пароизоляционная мембрана Вентзазор - брусок 45х45мм Имитация бруса 20мм


Изм.	Колуч.	Лист	№Док.	Подп.	Дата	Одноэтажное здание (баня)	Стадия	Лист	Листов
Разраб.							АР		
Пров.									
Т. контр.						Перечень ограждающих конструкций (лист 2)			
Н. контр.									
Утв.									

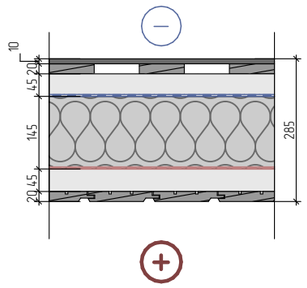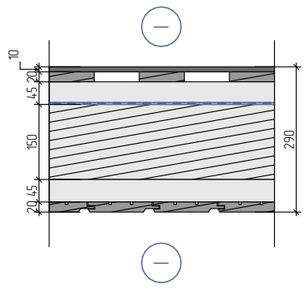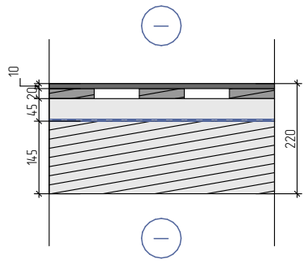Перечень ограждающих конструкций (лист 3)

Наименование	Графическое изображение	Перечень материалов
К-1		Металлочерепица Обрешетка - доска 20х90мм (шаг 350мм) Вентзазор - брусок 45х45мм Гидро-ветрозащитная мембрана Стропило - 45х145мм (Утепленная 150мм) Пароизоляционная мембрана Вентбрусок - 45х45мм Имитация бруса 20мм
К-2		Металлочерепица Обрешетка - доска 20х90мм (шаг 350мм) Вентзазор - брусок 45х45мм Гидро-ветрозащитная мембрана Стропило - 45х145мм Вентбрусок - 45х45мм Планкен 20мм
К-3		Металлочерепица Обрешетка - доска 20х90мм (шаг 350мм) Вентзазор - брусок 45х45мм Гидро-ветрозащитная мембрана Стропило - 45х145мм

Изм.	Колуч.	Лист	№Док.	Подп.	Дата	Одноэтажное здание (баня)	Стадия	Лист	Листов
Разраб.							АР		
Пров.									
Т. контр.						Перечень ограждающих конструкций (лист 3)			
Н. контр.									
Утв.									

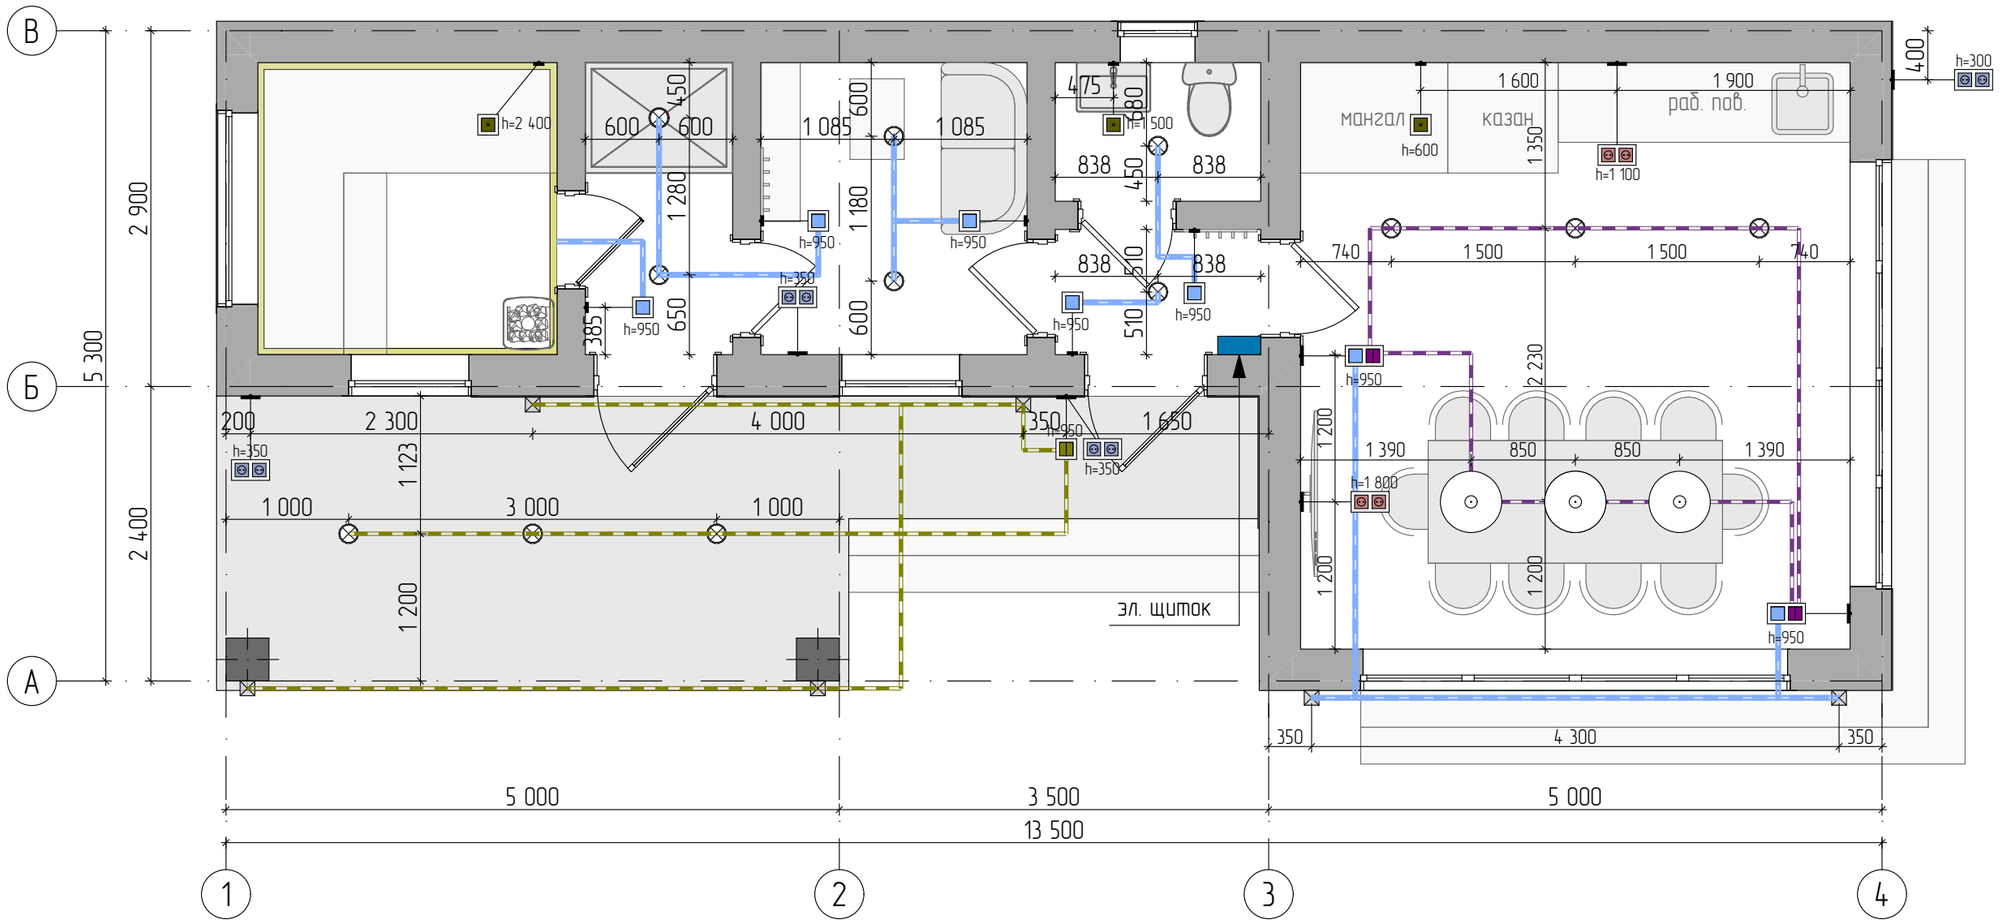План электрооборудования




Спецификация электрооборудования		
2D-вид	Тип оборудования	Кол-тво, шт.
	Выключатель двухклавишный (рамка 1 секции)	1
	Выключатель одно- и двухклавишный (рамка 2 секции)	2
	Выключатель одноклавишный (рамка 1 секции)	5
	Розетка 220v (рамка 2 секции)	2
	Розетка 220v влагозащитная (рамка 2 секции)	4

	Светильник подвесной	3
	Светильник точечный	13
	Уличный светильник	6
	Эл. вывод	3
		39

1. Схема размещения розеток является рекомендательной и требует согласования с заказчиком по месту.
2. Все высоты даны от чистового пола.
3. Все указанные размеры даются до центра позиций.
4. Отметки розеток, выключателей, выводов и др. оборудования, являются предварительными и уточняются после выбора финишных материалов и мебели.
5. Размеры уточняются дополнительно

Изм.	Колуч.	Лист	№Док.	Подп.	Дата	Однoэтажное здание (баня)	Стадия	Лист	Листов
Разраб.							АР		
Пров.									
Т. контр.						План электрооборудования			
Н. контр.									
Утв.									

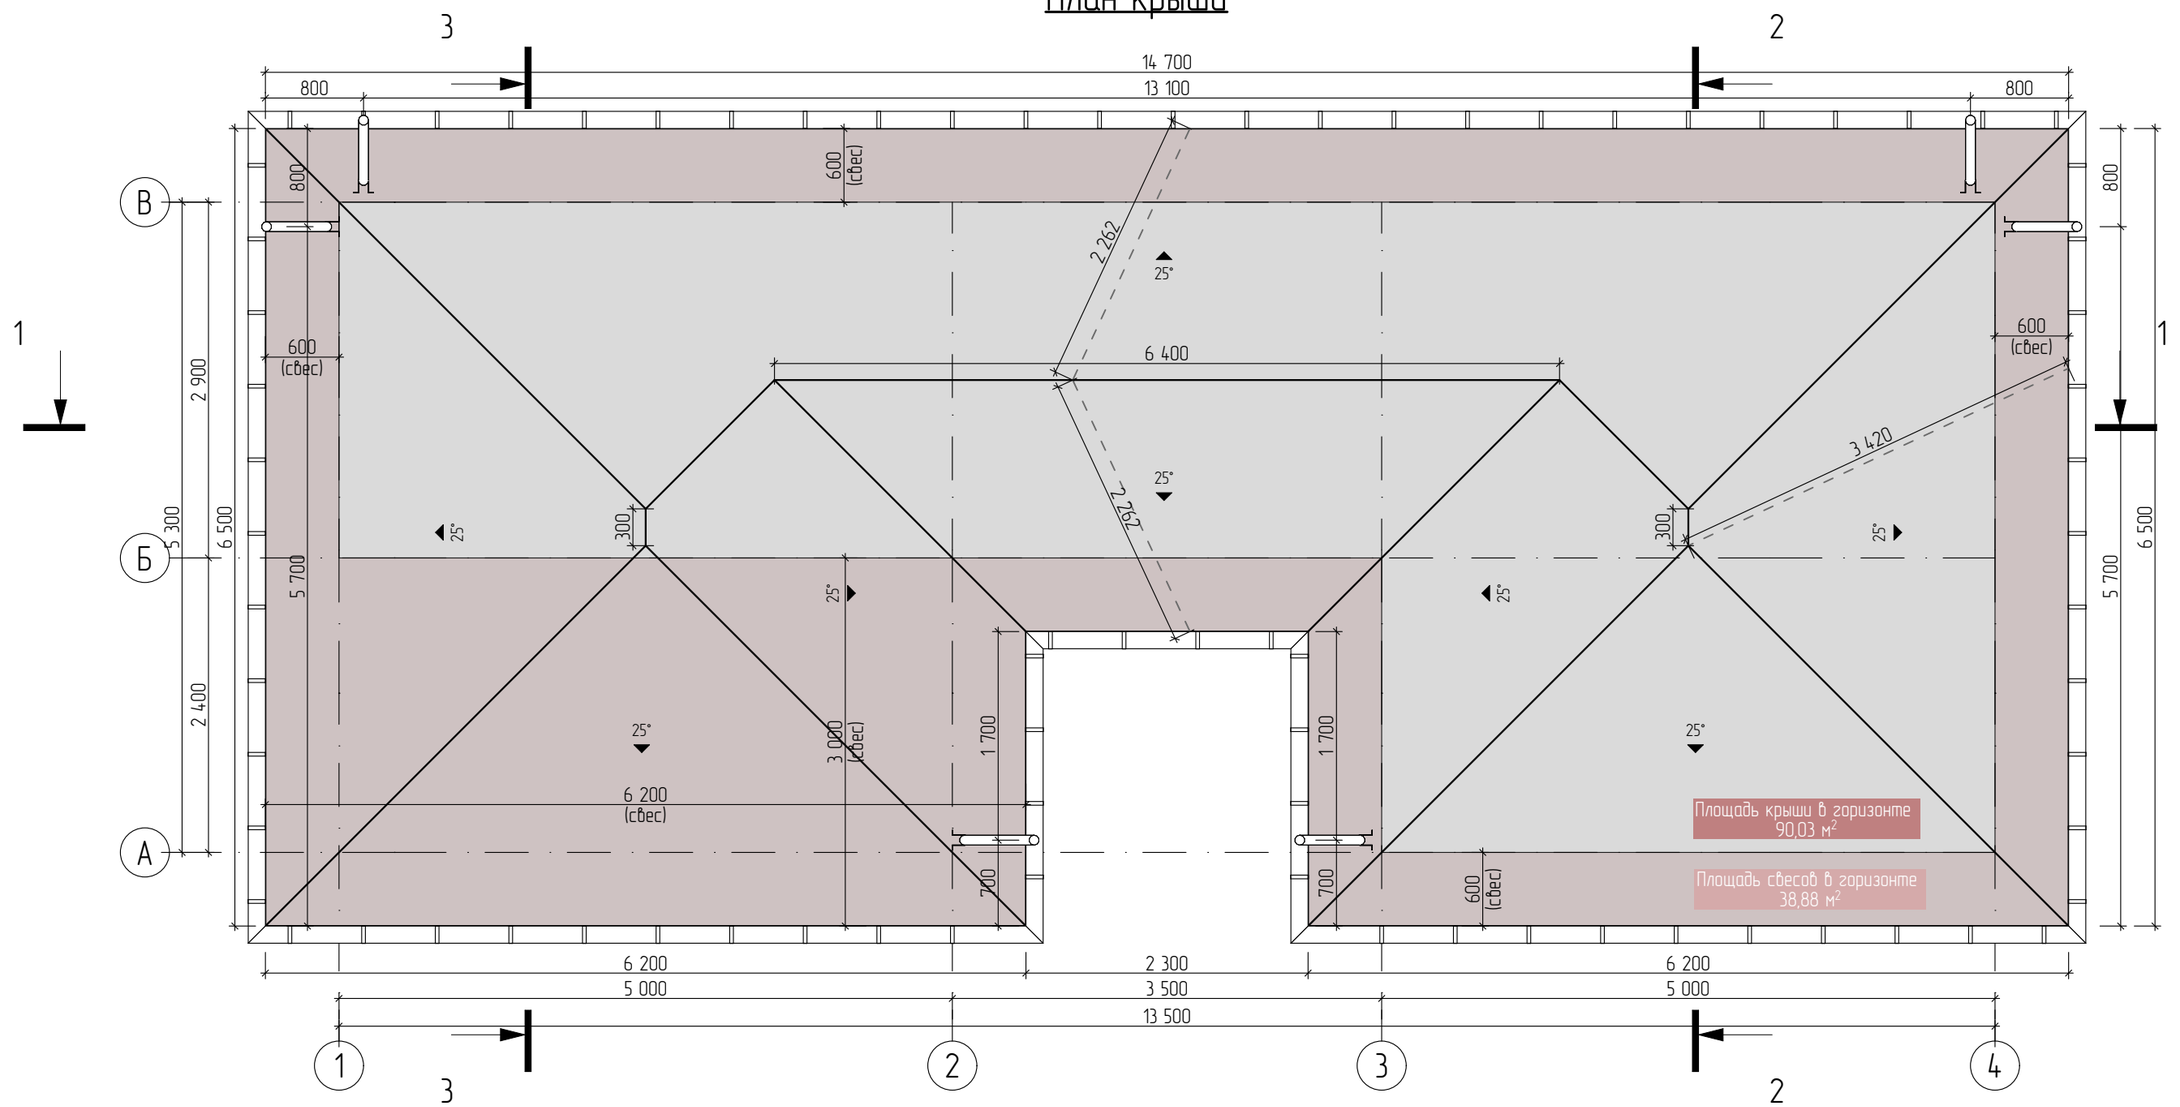План крыши



Условные обозначения:


- Крыша бани

- Свесы крыши бани

Площадь крыши бани
(S, м²) = 99,33м²

Изм.	Колич.	Лист	№Док.	Подп.	Дата			
Разраб.						Одноэтажное здание (баня)	Стадия	Лист	Листов
Пров.							АР		
Т. контр.									
Н. контр.						План крыши			
Утв.									

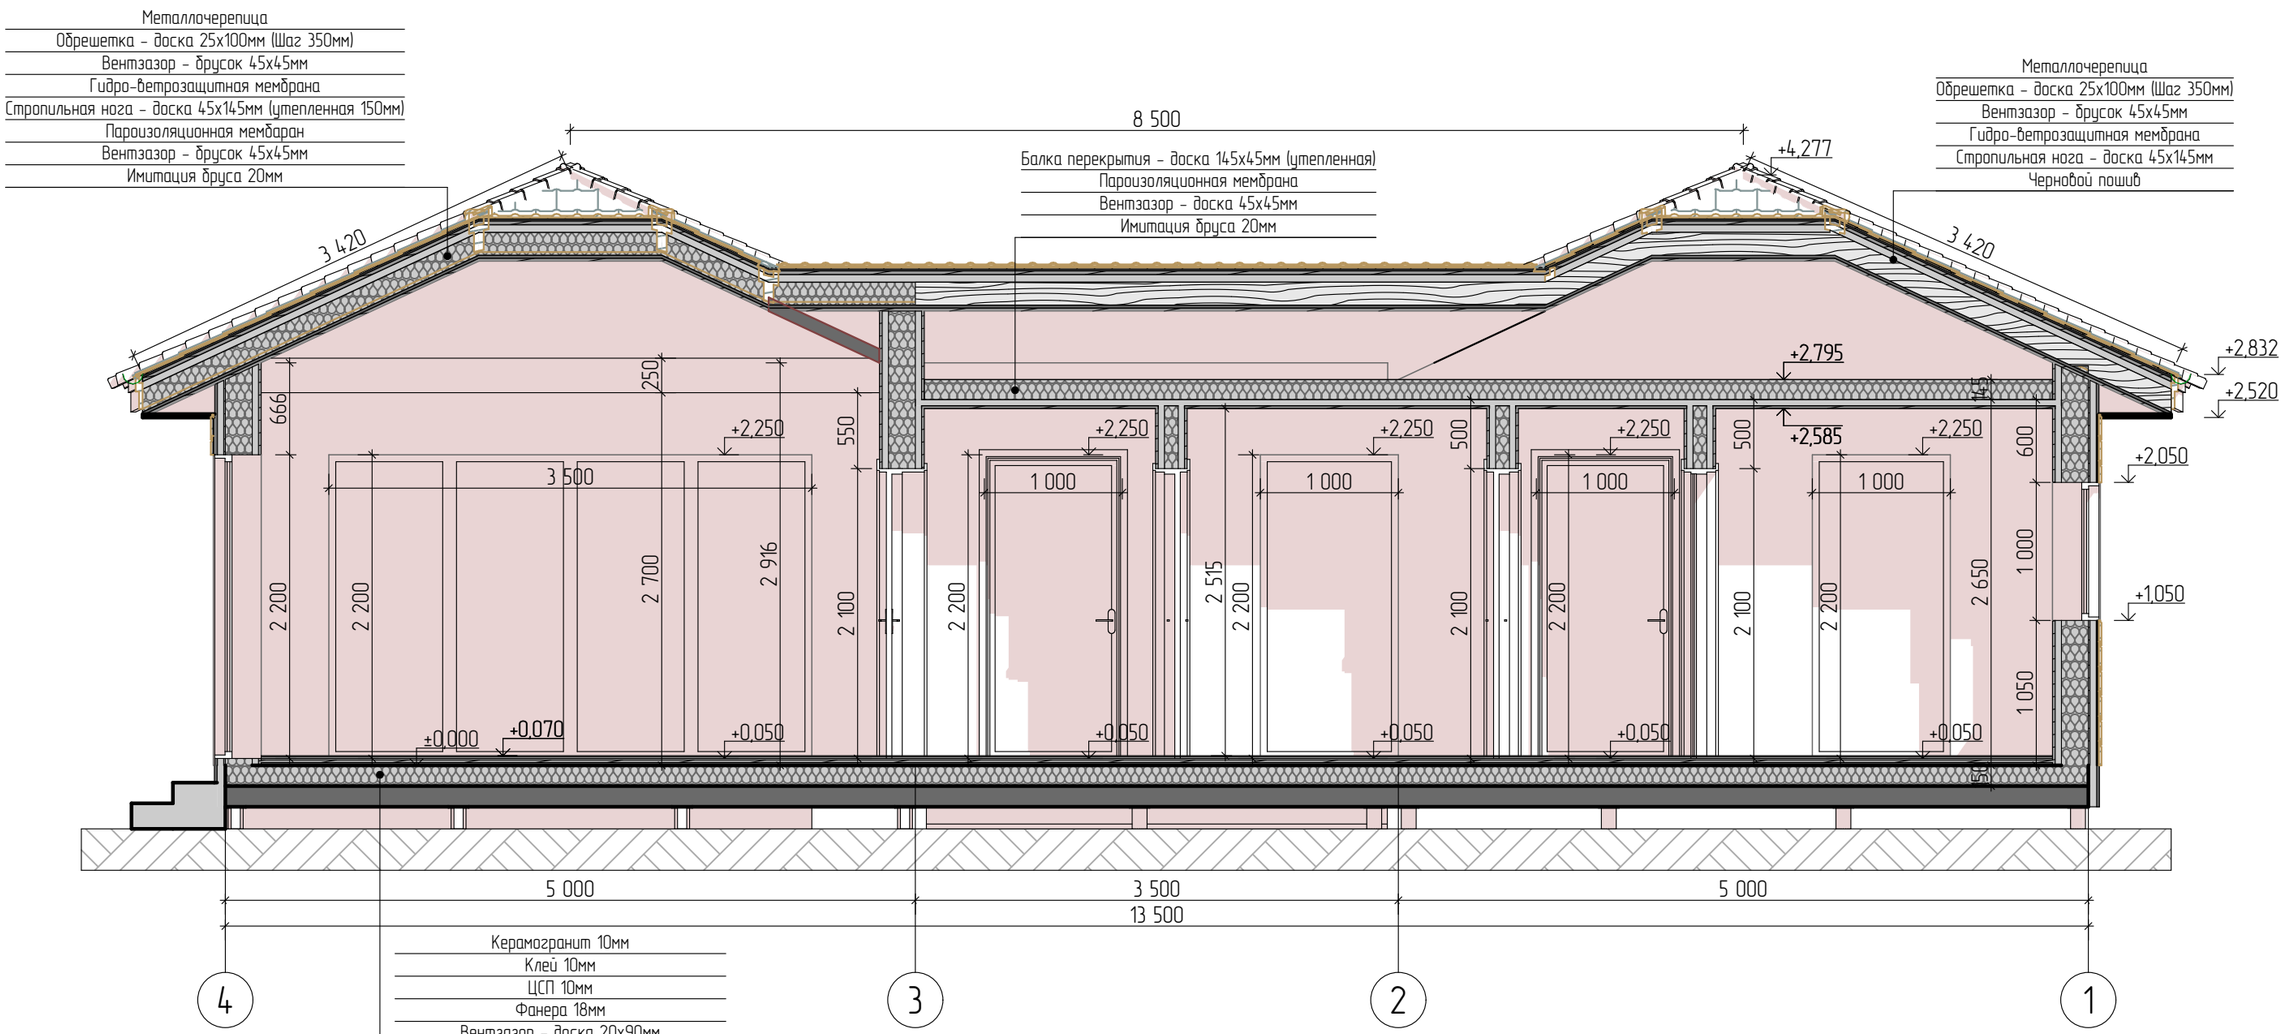Разрез 1-1




Керамогранит 10мм
Клей 10мм
ЦСП 10мм
Фанера 18мм
Вентзазор - доска 20х90мм
Пароизоляционная мембрана
Балка перекрытия 45х145 (Утепленная 150мм)
Гидро-ветрозащитная мембрана
Просечка (сетка, ячейка 5х5)
Обрешетка - доска 25х100 (шаг 400)
Нижняя обвязка - 3 сращеных доски 50х150мм

Изм.	Колуч.	Лист	№Док.	Подп.	Дата	Одноэтажное здание (баня)	Стадия	Лист	Листов
Разраб.							АР		
Пров.									
Т. контр.						Разрез 1-1			
Н. контр.									
Утв.									

Разрез 2-2

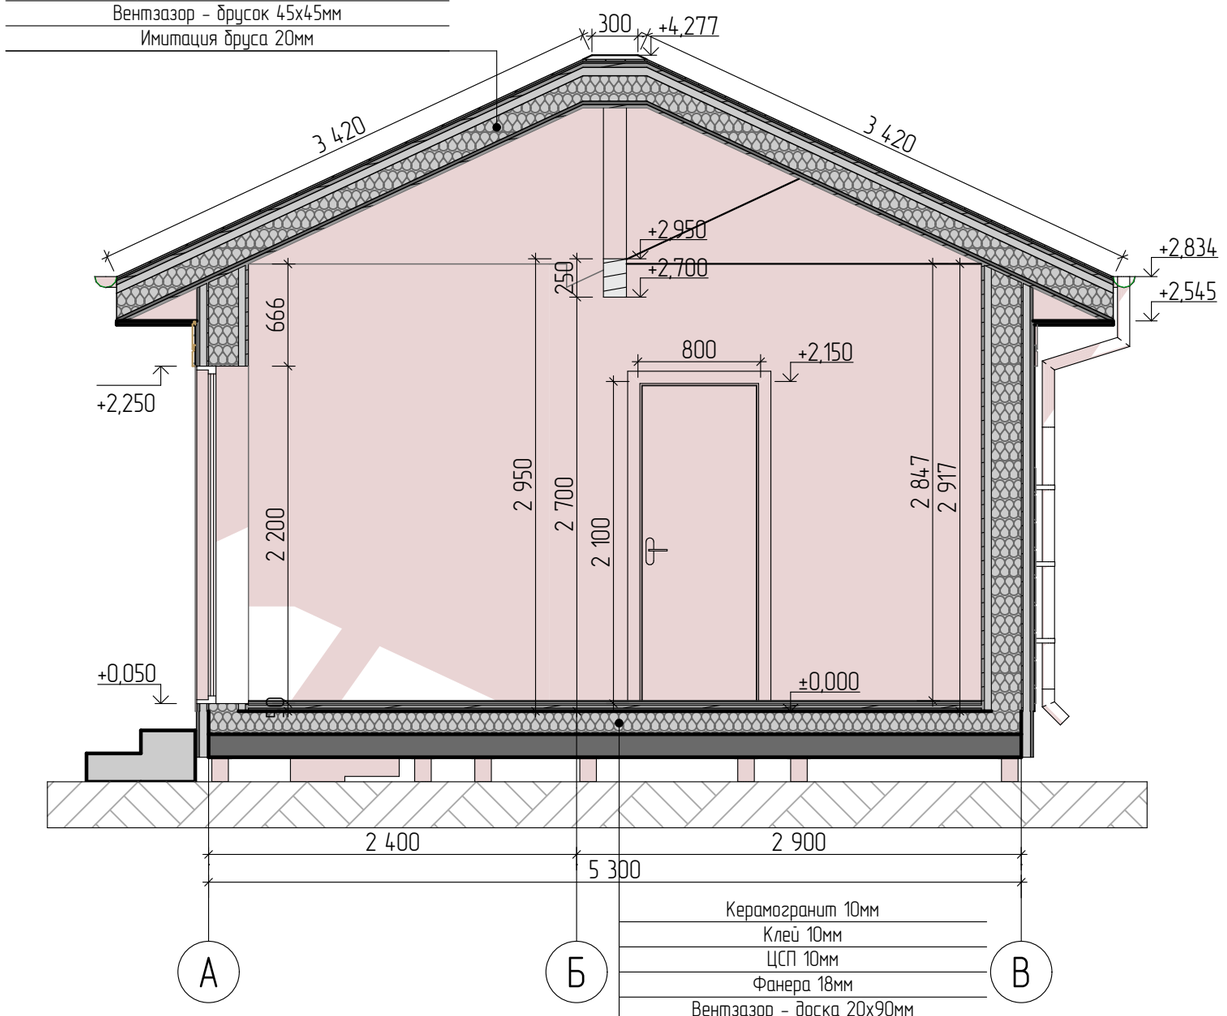
Металлочерепица
Обрешетка - доска 25х100мм (Шаг 350мм)
Вентзазор - брусок 45х45мм
Гидро-ветрозащитная мембрана
Стропильная нога - доска 45х145мм (утепленная 150мм)
Пароизоляционная мембран
Вентзазор - брусок 45х45мм
Имитация бруса 20мм



Керамогранит 10мм
Клей 10мм
ЦСП 10мм
Фанера 18мм
Вентзазор - доска 20х90мм
Пароизоляционная мембрана
Балка перекрытия 45х145 (Утепленная 150мм)
Гидро-ветрозащитная мембрана
Просечка (сетка, ячейка 5х5)
Обрешетка - доска 25х100 (шаг 400)
Нижняя обвязка - 3 сращеных доски 50х150мм


Изм.	Колуч.	Лист	№Док.	Подп.	Дата	Однозтажное здание (баня)	Стадия	Лист	Листов
Разраб.							АР		
Пров.									
Т. контр.									
Н. контр.						Разрез 2-2			
Утв.									

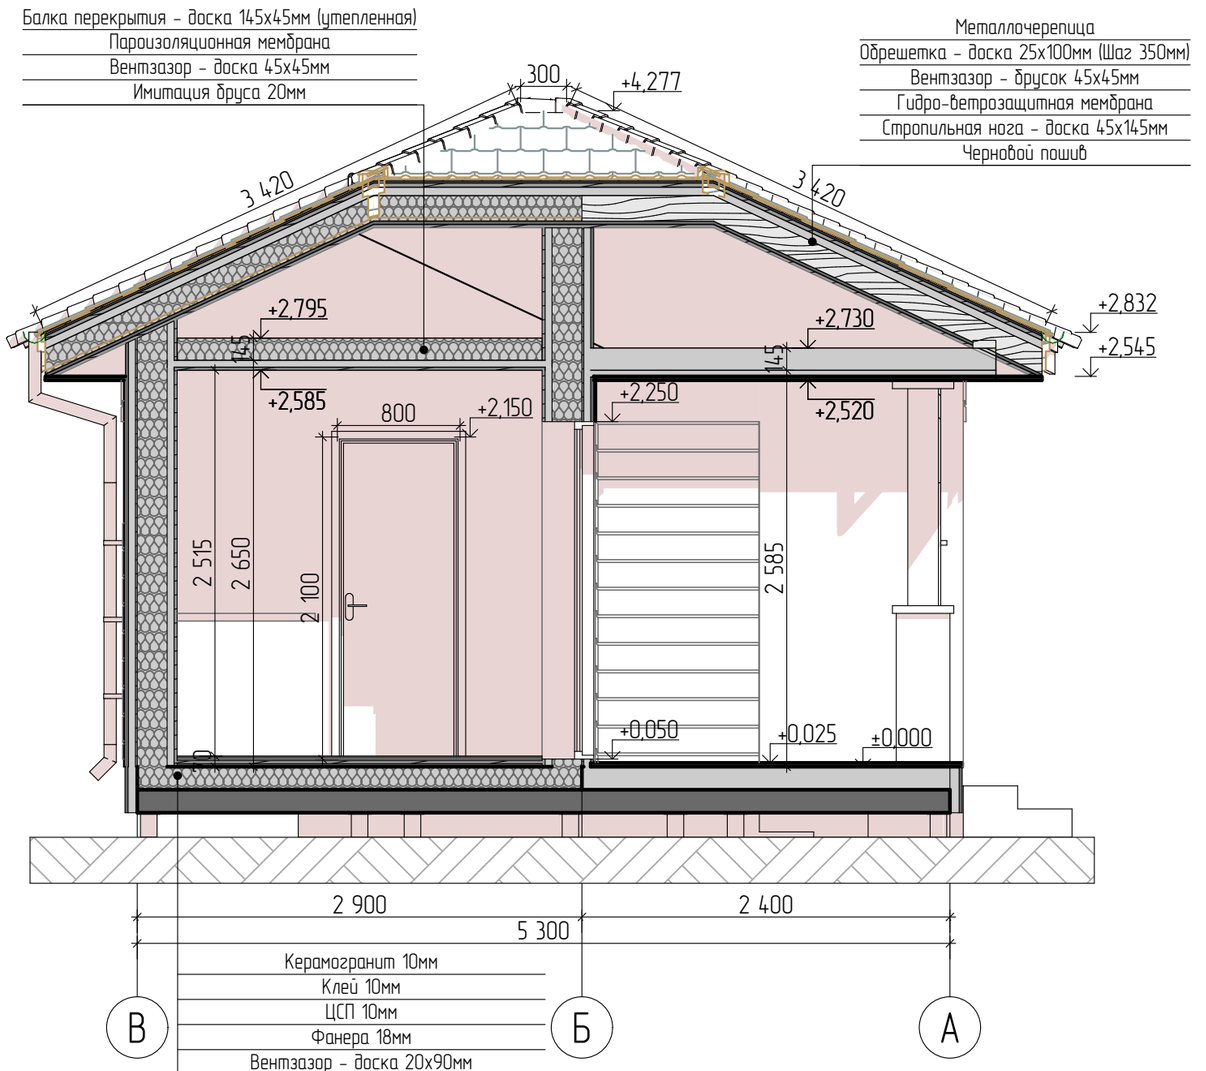Разрез 3-3




Изм.	Колуч.	Лист	№Док.	Подп.	Дата	Одноэтажное здание (баня)	Стадия	Лист	Листов
Разраб.							АР		
Пров.									
Т. контр.									
Н. контр.						Разрез 3-3			
Утв.									

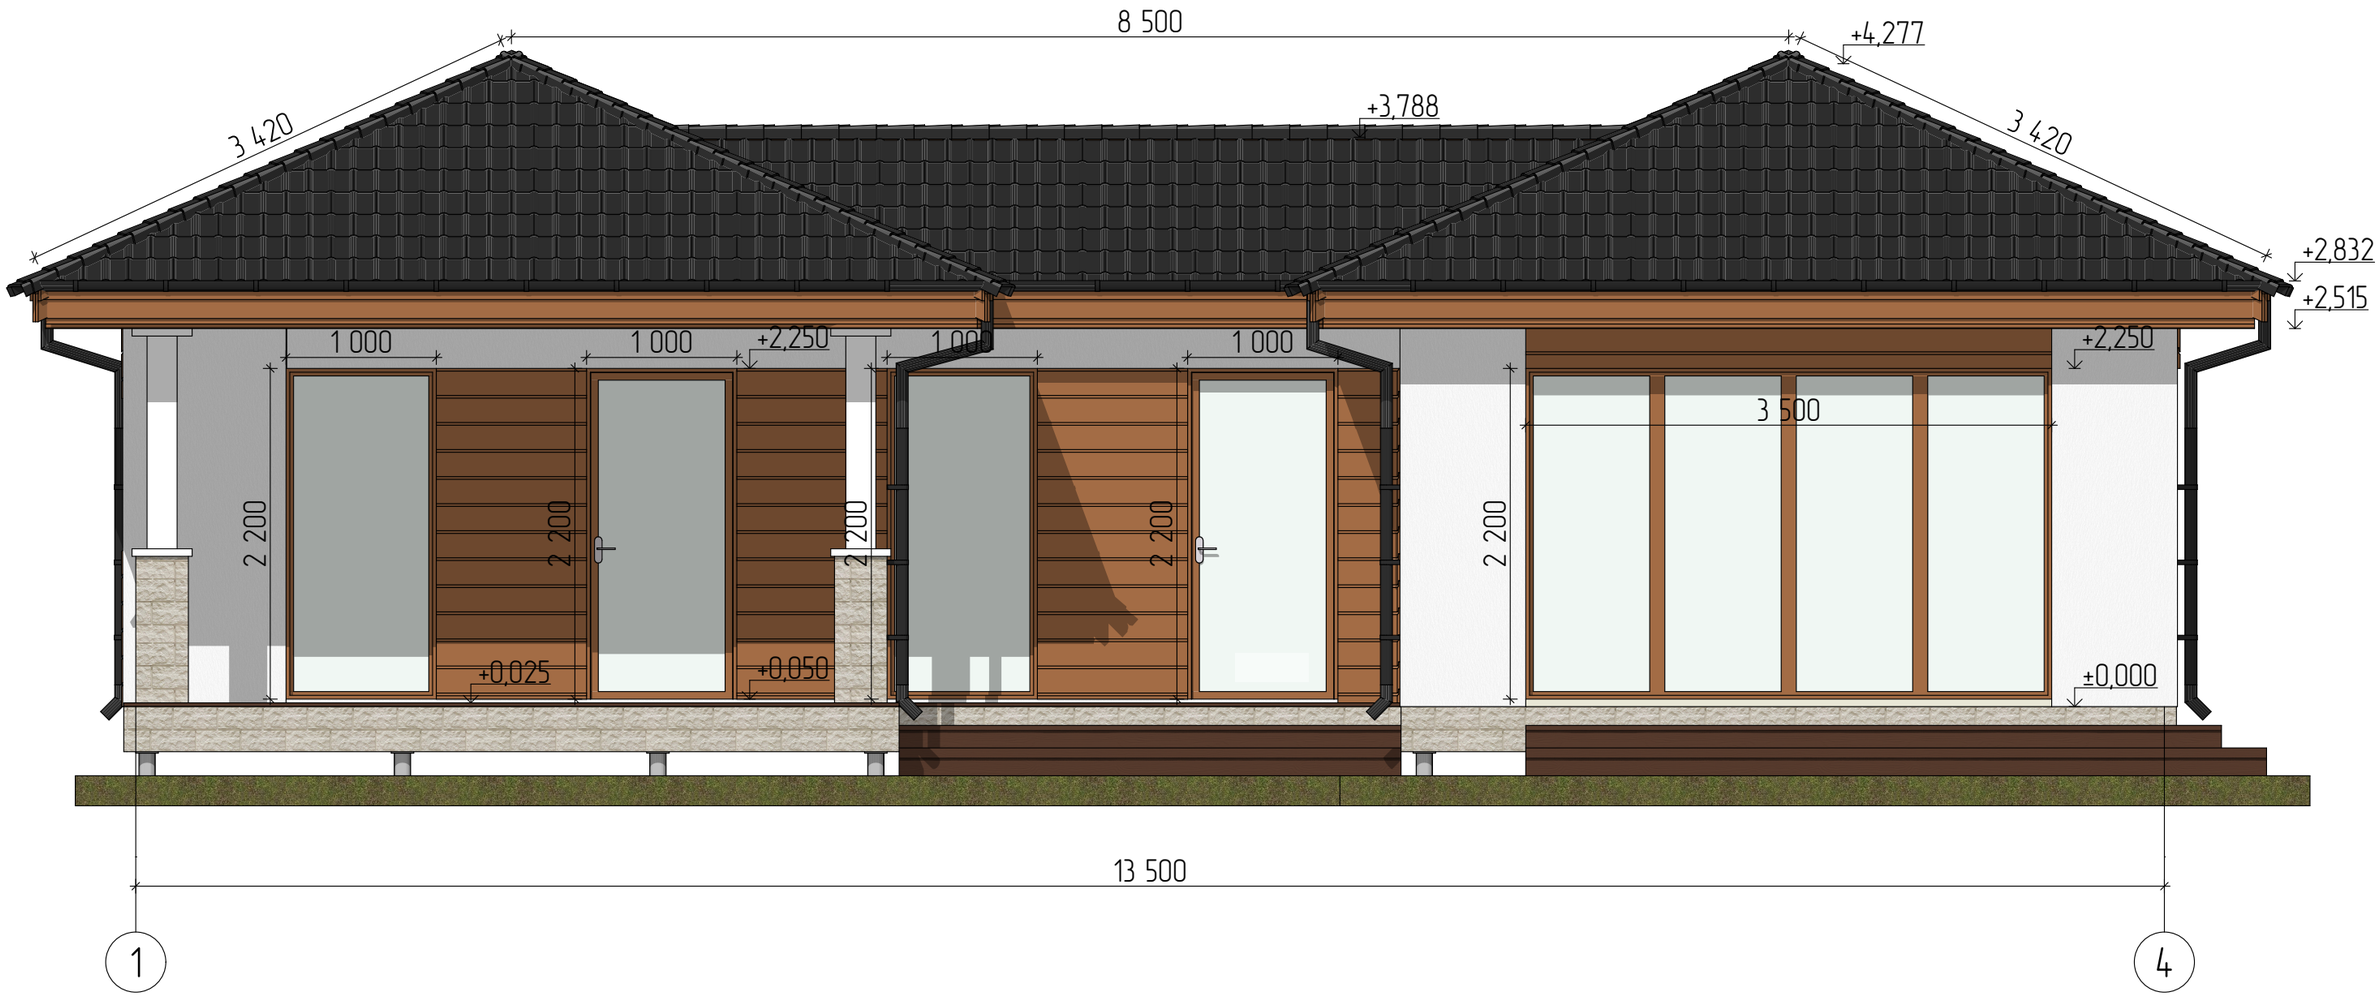Фасад 1-4



Изм.	Колуч.	Лист	№Док.	Подп.	Дата	Одноэтажное здание (баня)	Стадия	Лист	Листов
Разраб.							АР		
Пров.									
Т. контр.									
Н. контр.						Фасад 1-4			
Утв.									

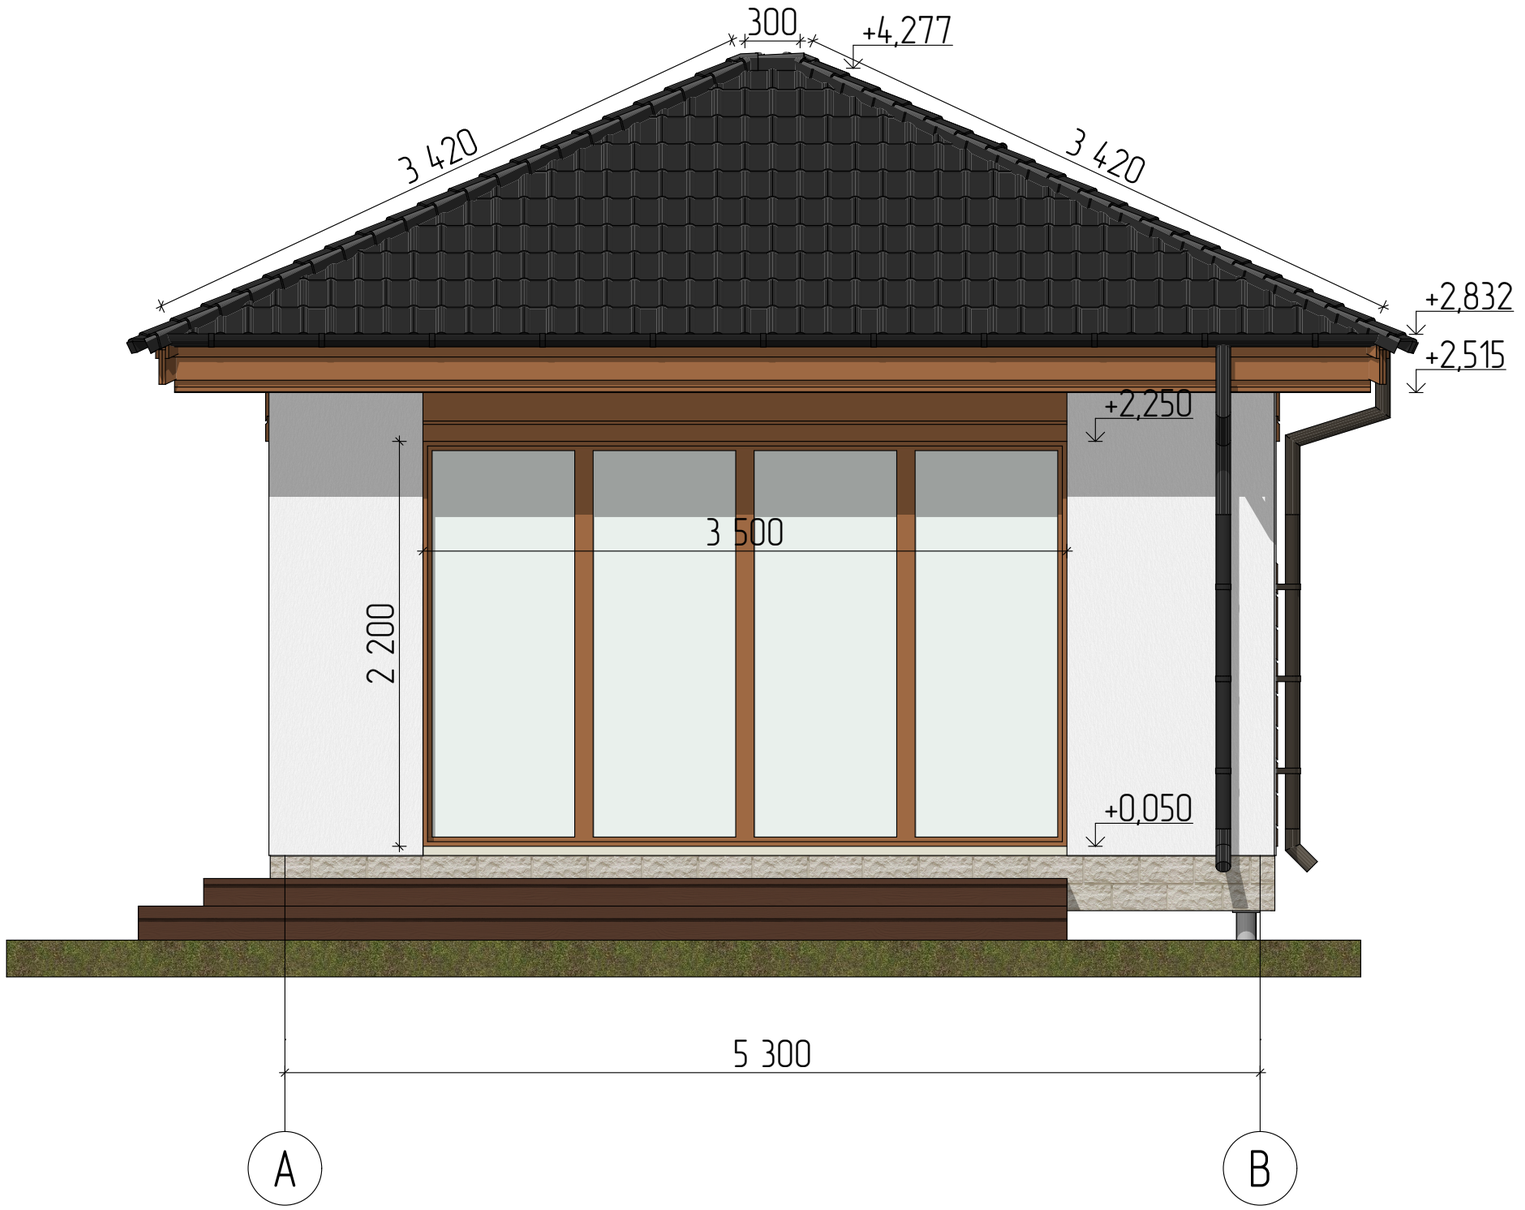Фасад А-В



Условные обозначения:

1 – Фиброцементные панели

2 – Террасная доска

3 – Водосточная система, металлочерепица

4 – Планкен

Изм.	Колуч.	Лист	№Док.	Подп.	Дата				
Разраб.						Одноэтажное здание (баня)	Стадия	Лист	Листов
Пров.							АР	26	
Т. контр.									
Н. контр.						Фасад А-В			
Утв.									

Фасад Б-А



Условные обозначения:

1 – Фиброцементные панели


2 – Террасная доска

3 – Водосточная система, металлочерепица

4 – Планкен

Изм.	Колуч.	Лист	№Док.	Подп.	Дата	Одноэтажное здание (баня)	Стадия	Лист	Листов
Разраб.							АР		
Пров.									
Т. контр.									
Н. контр.						Фасад Б-А			
Утв.									

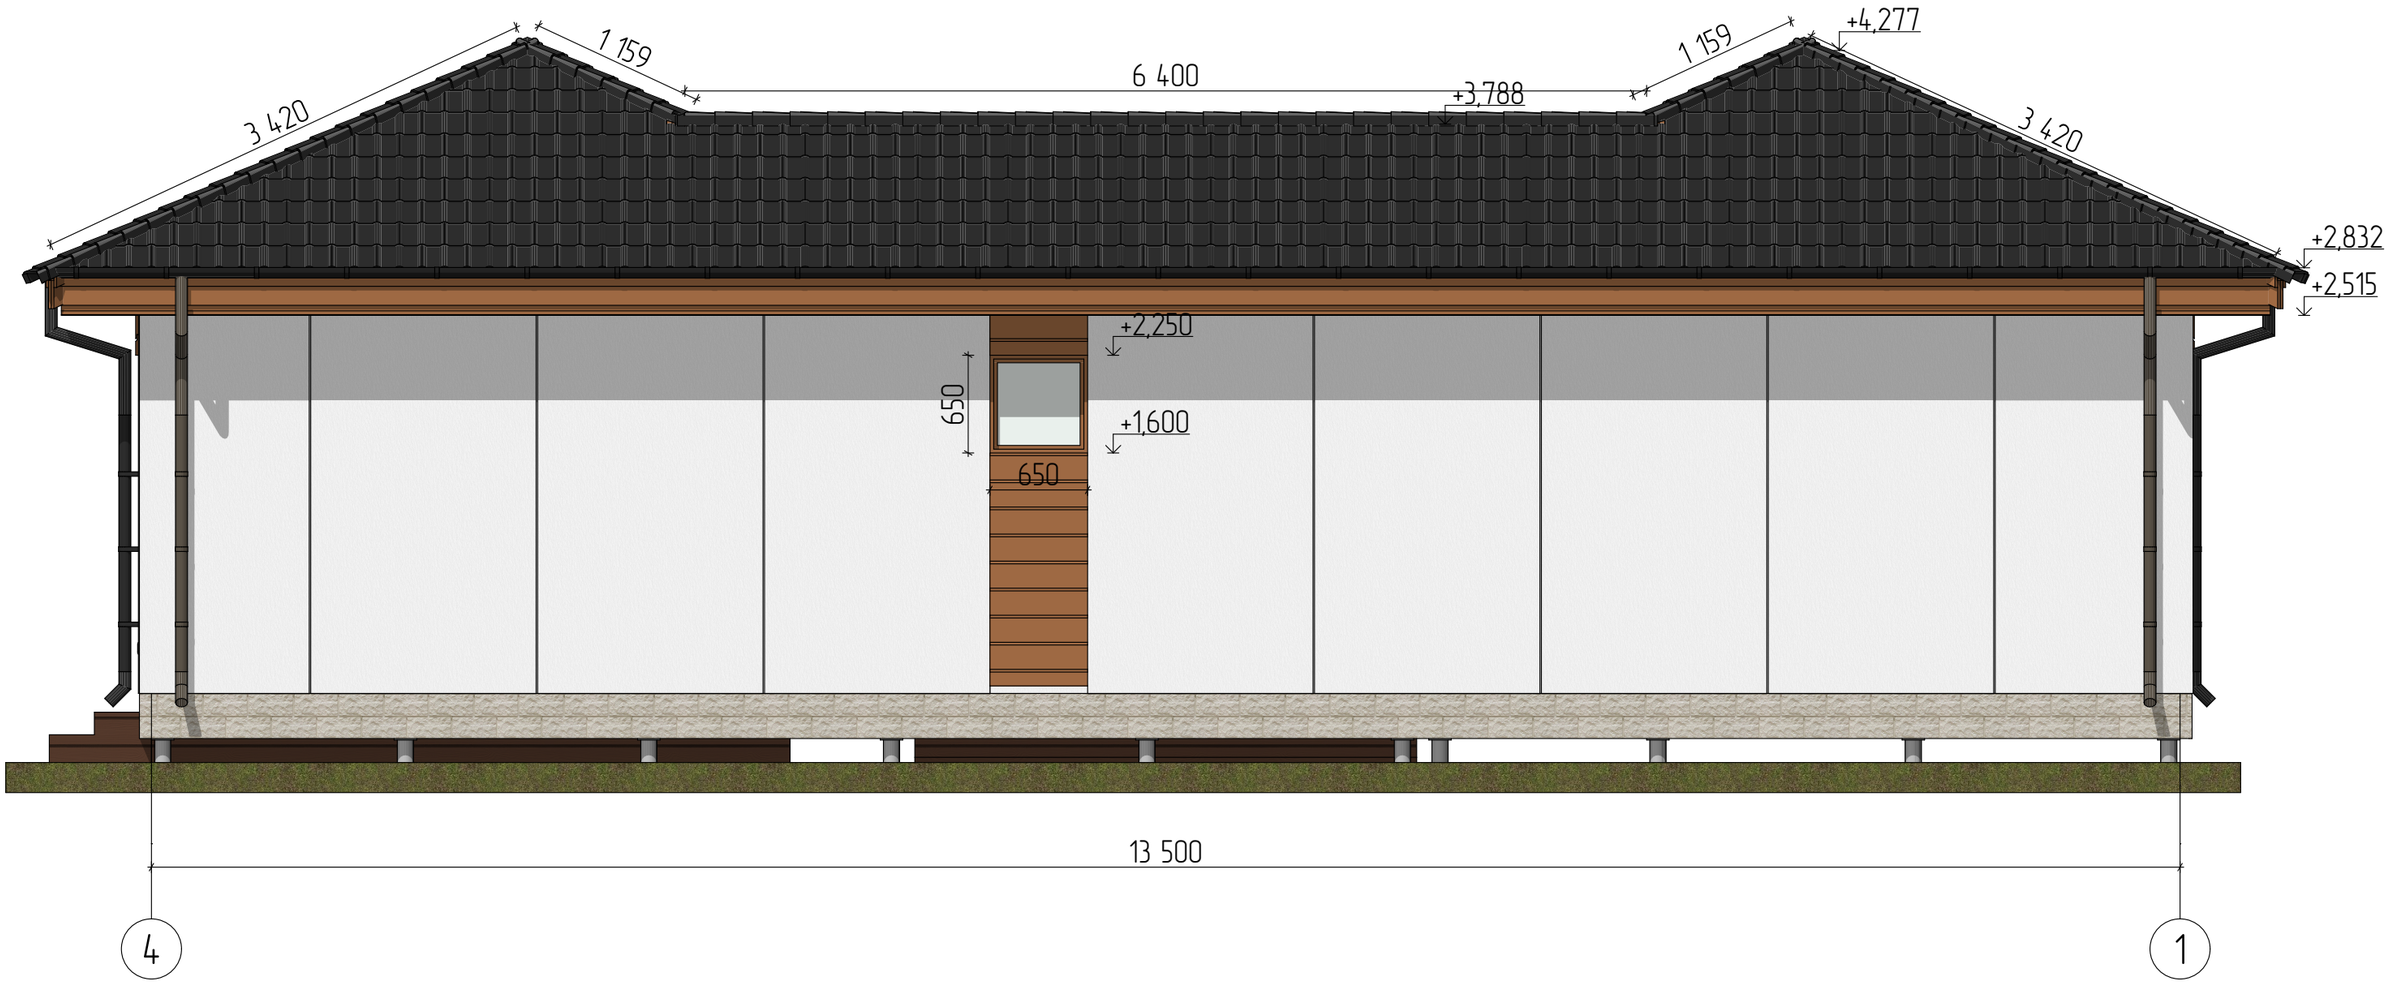Фасад 4-1



Изм.	Колуч.	Лист	№Док.	Подп.	Дата.	Одноэтажное здание (баня)	Стадия	Лист	Листов
Разраб.							АР		
Пров.									
Т. контр.						Фасад 4-1			
Н. контр.									
Утв.									