ПРОЕКТНАЯ ДОКУМЕНТАЦИЯ

Архитектурные решения (раздел АР)

ИС (Индивидуальные строение "беседки")

ГАП:

Архитектор: Жмакни

Москва , 2026 год

Наименование	Страница	Примечание
Титульный лист	1	
Содержание раздела	2	
Пояснительная записка	3	
Размерный план 0,000 с экспликацией М1:50	4	
План-схема мебелировки на отметке 0,000 с экспликацией помещений М1:50	5	
Фасад А-Б М1:50	6	
Фасад 2-1 М1:50	7	
Фасад Б-А М1:50	8	
Фасад 1-2 М1:50	9	
Разрез 1-1 М1:50	10	
Разрез 2-2 М1:50	11	
Аксонометрия 1	12	
Аксонометрия 2	13	
Аксонометрия 3	14	
Аксонометрия 4	15	
План-схема электрики М1:50	16	
Спецификация заполнения дверных и оконных проемов	17	
План - схема кровли М1:50	18	
Схема пирогов ограждающих конструкций	19	
Визуализация 1	20	
Визуализация 2	21	
Визуализация 3	22	

Подп. и дата | Инв. № дубля | Взам.инв № | Подп. и дата | Инв. № подл.

Изм.	Кол.уч.	Лист	№Док.	Подп.	Дата

Архитектурные решения

Лист | Листов

Содержание раздела

Пояснительная записка

Общие данные:

1. Проект одноэтажной "беседки", выполнен индивидуально на основании исходных данных представленных заказчиком.

2. Состав пирогов конструкций предусматривает его круглогодичную эксплуатацию.

Размеры строения 5х8 м. в осях

За относительную отметку ±0.000 принять уровень чистого пола.

3. Адрес строительства:

Конструктивные решения:

1. Чертежи разработаны на основании задания на проетирования.

2. Объект строительства расположен в следующих климатических условиях:
- Нормативный вес снегового покрова для III района – Sg=1,5 кН/м2;
- Нормативное ветровое давление для I района – 23 кгс/м^2;
- Расчетная зимняя температура наружнего воздуха – минус 26°С;
- Нормативная глубина промерзания – 1,4 м;
- Полезная нагрузка на покрытие – 150 кгс/м^2.

3. Общая характеристика:
- Уровень ответственности – нормальный.
- Степень огнестойкости – III.
- Зона влажности – нормальный.
- Расчетная температура наружного воздуха наиболее холодной пятидневки: –29°С.

4. Конструктивно строение представляет собой сооружение со свайным фундаментом, несущими стенами из деревянного каркаса , кровлей по деревянным стропилам.

5. При проведении строительных работ необходимо осуществлять технический надзор с ведением журнала работ. Осуществлять входной контроль материалов, вести приемку по каждому этапу работ.

6. Описание конструкций строения:
- Фундамент – монолитная железобитонная плита, проектом не разрабатывается;
- Несущие конструкции – газоблок, 300 мм;
- Стропильная система – из строганной доски сечением 190х45(h)мм, уточняется в разделе КР;
- Кровля – двускатная, отделка – мягкая черепица;
- Отделка цоколя – клинкерный кирпич

7. Все деревянные конструкции обработать огне-биозащитными септиками в соответствии с СП 64.13330.2017

8. Кровельные работы выполнять в соответствии с требованиями фирмы производителя.

9. Все работы вести в строгом соответствии с требованиями СП 49.13330.2012 (Безопасность труда в строительстве).

10 При выполнении всех работ строго соблюдать меры противопожарной безопасности.

11. Возможна замена материалов аналогами.

*Решения, принятые в проекте и отображенные в чертежах, соответствуют требованиям экологических, санитарно –гигиенических, противопожарных и других норм, действующих на территории Российской Федерации, и обеспечивают безопасную для жизни и здоровья людей эксплуатацию объекта при соблюдении предусмотренных рабочих чертежей и мероприятий.

Изм.	Кол.уч.	Лист	№Док.	Подп.	Дата				
						Архитектурные решения	Стадия	Лист	Листов
						Пояснительная записка			

Подп. и дата | Инв. № дубля | Взам.инв № | Подп. и дата | Инв. № подл.

Размерный план 0,000 с экспликацией М1:50

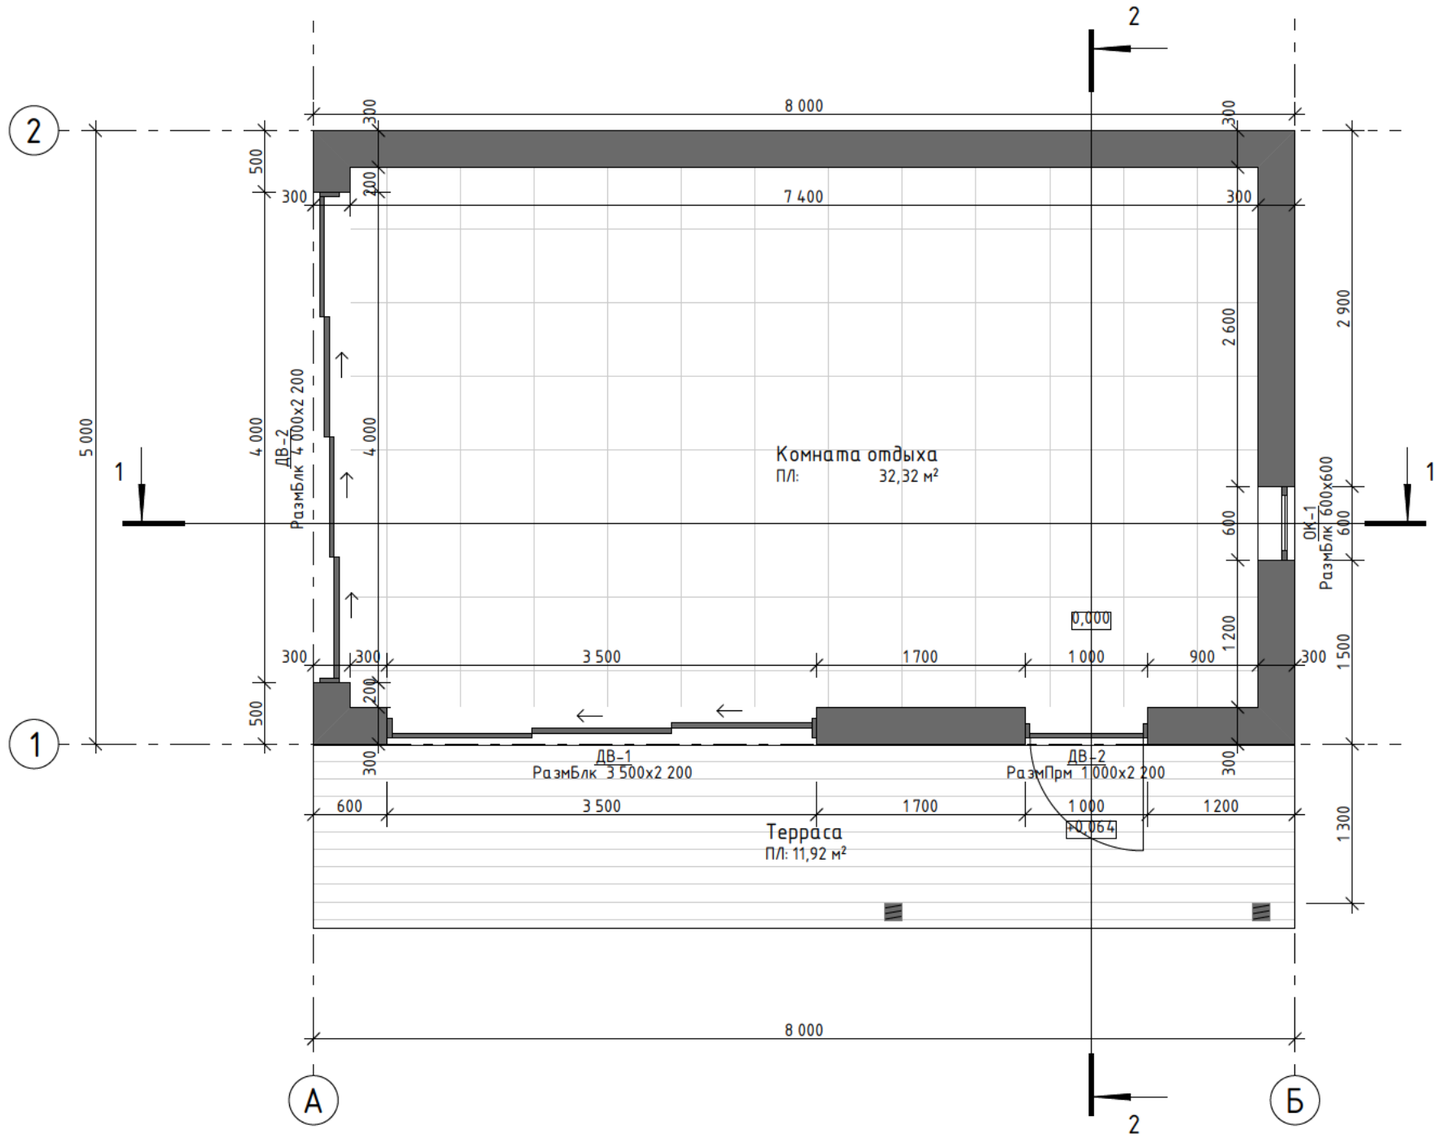

Экспликация:

№ п/п	Наименование	Площадь, м2
1	Комната отдыха	32,32
2	Терраса	11,92
		44,24 м²

Наименование	Площадь,м2
Площадь застройки	52,18

Примечания:

1. Размеры указаны по черновой отделке
2. Количество ступеней показано условно и может изменится при разработке раздела КР

Изм.	Кол.уч.	Лист	№Док.	Подп.	Дата				
						Архитектурные решения	Стадия	Лист	Листов
						Размерный план 0,000 с экспликацией М1:50			

Подп. и дата | Инв. № дубля | Взам.инв № | Подп. и дата | Инв. № подл.

План-схема мебелировки на отметке 0,000 с экспликацией помещений М1:50

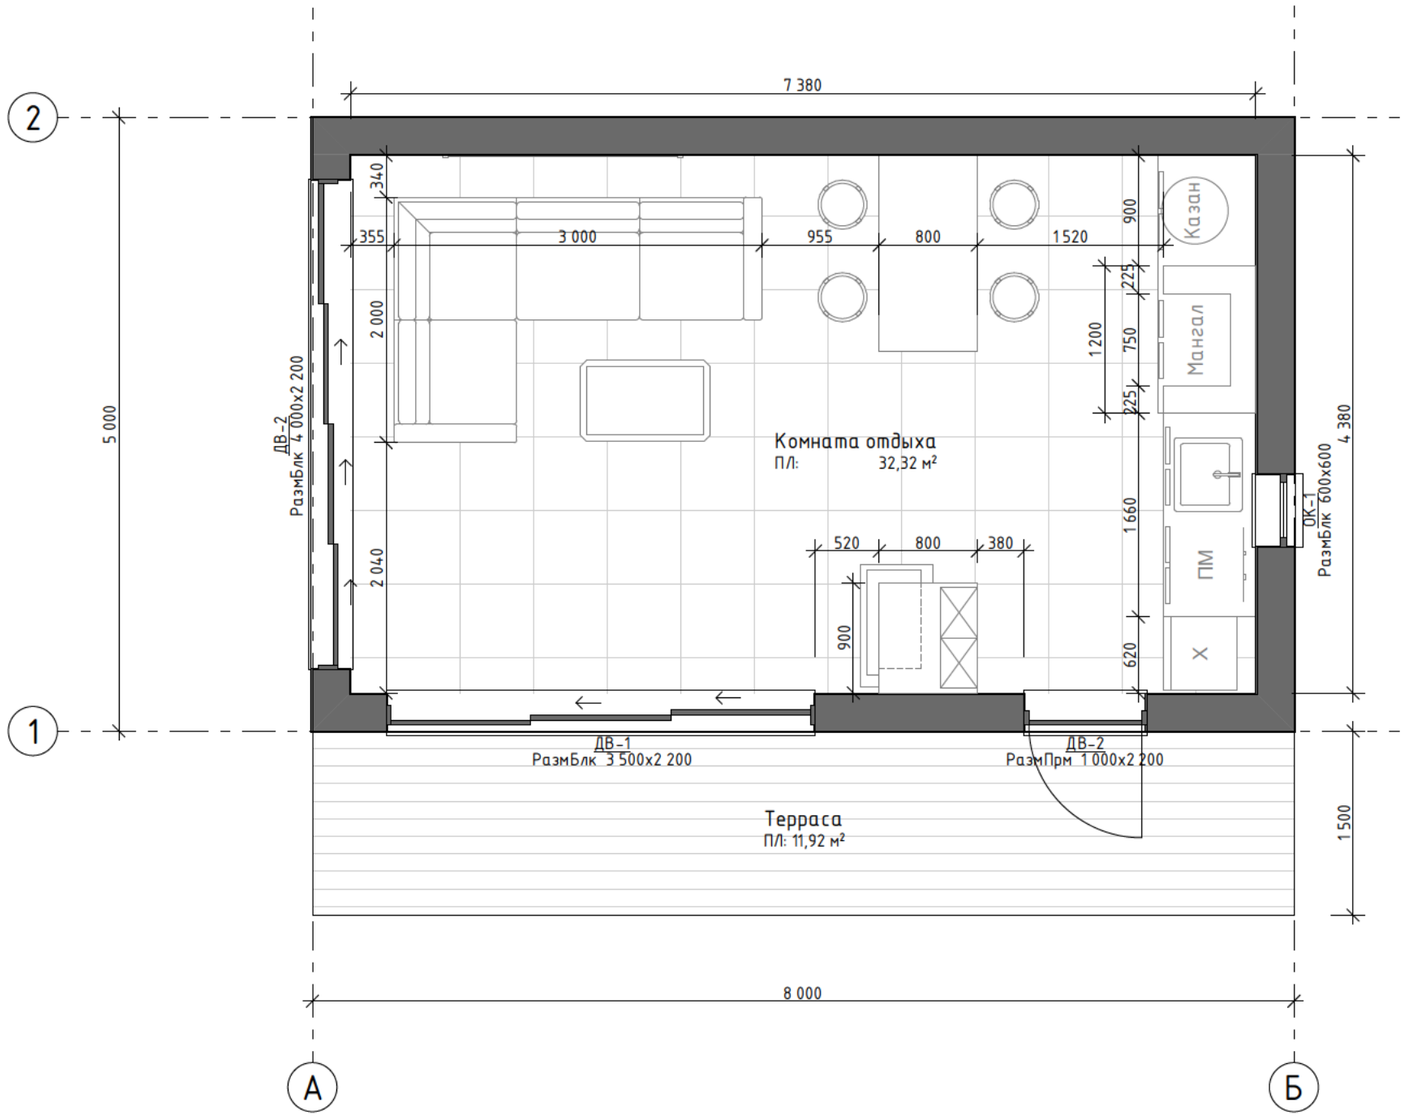

Экспликация:

№ п/п	Наименование	Площадь, м2
1	Комната отдыха	32,32
2	Терраса	11,92
		44,24 м²

Наименование	Площадь,м2
Площадь застройки	52,18

Примечания:

1. Полный перечень стеновых конструкций смотреть на ст. ___
2. Количество ступеней показано условно и может изменится при разработке раздела КР
3. Мебелеровка прорабатывается на дальнейшей стадии проектирования в разделе ИР

Изм.	Кол.уч.	Лист	№Док.	Подп.	Дата

Архитектурные решения	Стадия	Лист	Листов
План-схема мебелировки на отметке 0,000 с экспликацией помещений М1:50			

Подп. и дата | Инв. № дубля | Взам.инв № | Подп. и дата | Инв. № подл.

Фасад А-Б М1:50

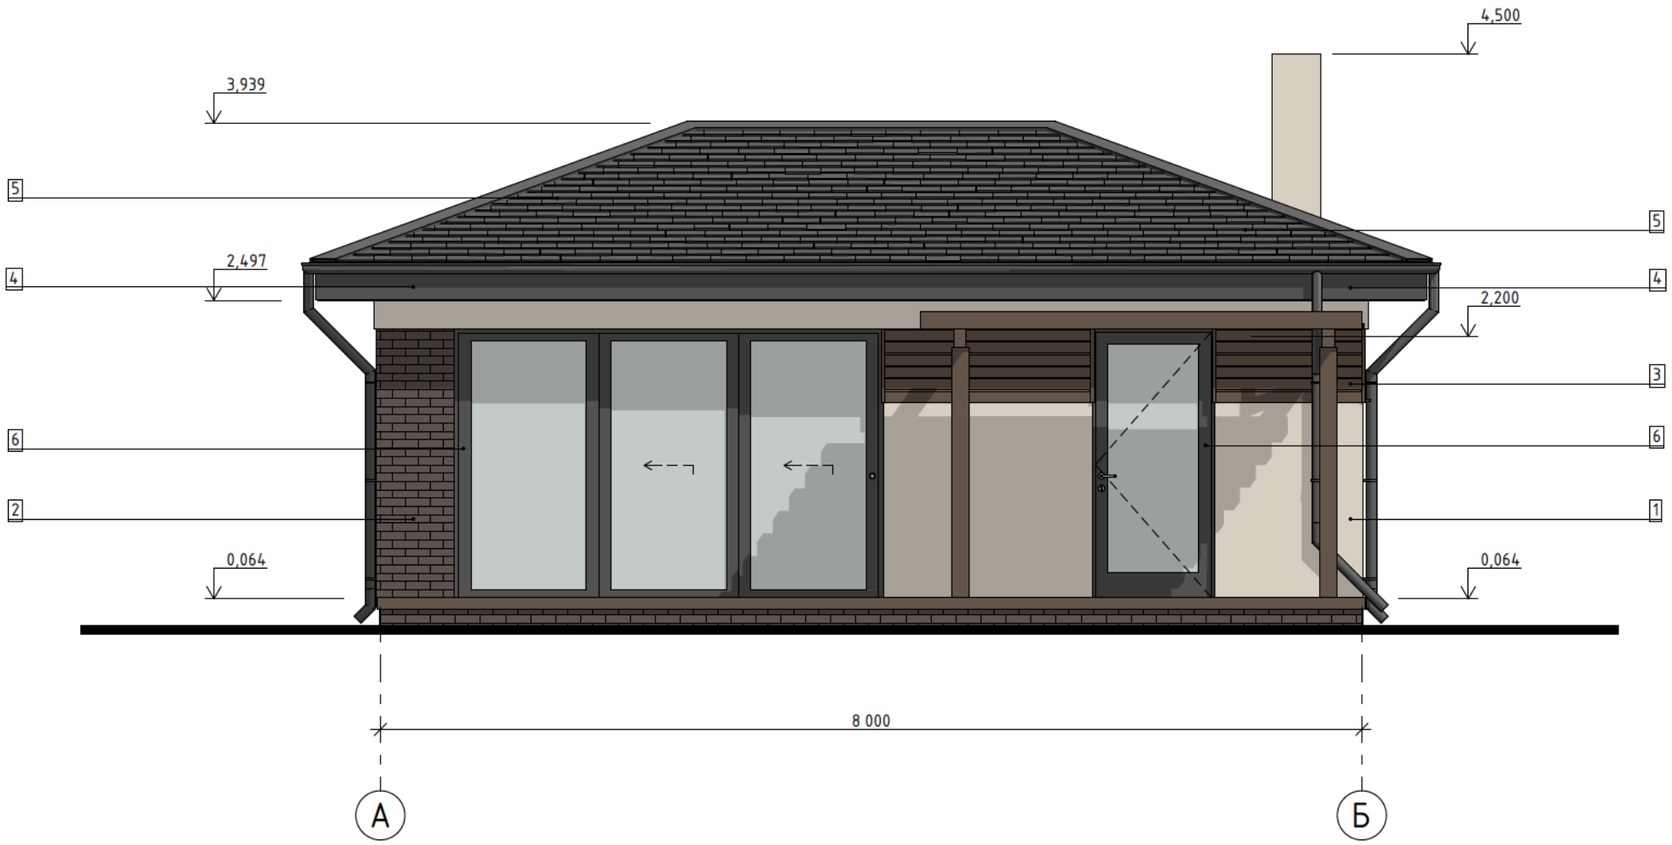

Ведомость отделки фасада

№ п/п	Наименование	Примечание
1	Отделка стен, штукатурка	
2	Отделка стен, клинкерный кирпич	
3	Отделка стен, фасадная доска,	
4	Обшивка кровли, софиты	
5	Отделка кровли, мягкая черепица,	
6	Оконные и дверные профили	

Примечания:

1. Цветовое решение, а так же материалы фасада уточняются на дальнейшей стадии производства работ, выполняются выкрасы на стадии фасадных работ.
2. В цветовой гамме придерживатся дизайн кода поселка.

Изм.	Кол.уч.	Лист	№Док.	Подп.	Дата				
						Архитектурные решения	Стадия	Лист	Листов
						Фасад А-Б М1:50			

Подп. и дата | Инв. № дубля | Взам.инв № | Подп. и дата | Инв. № подл.

Фасад 2-1 М1:50

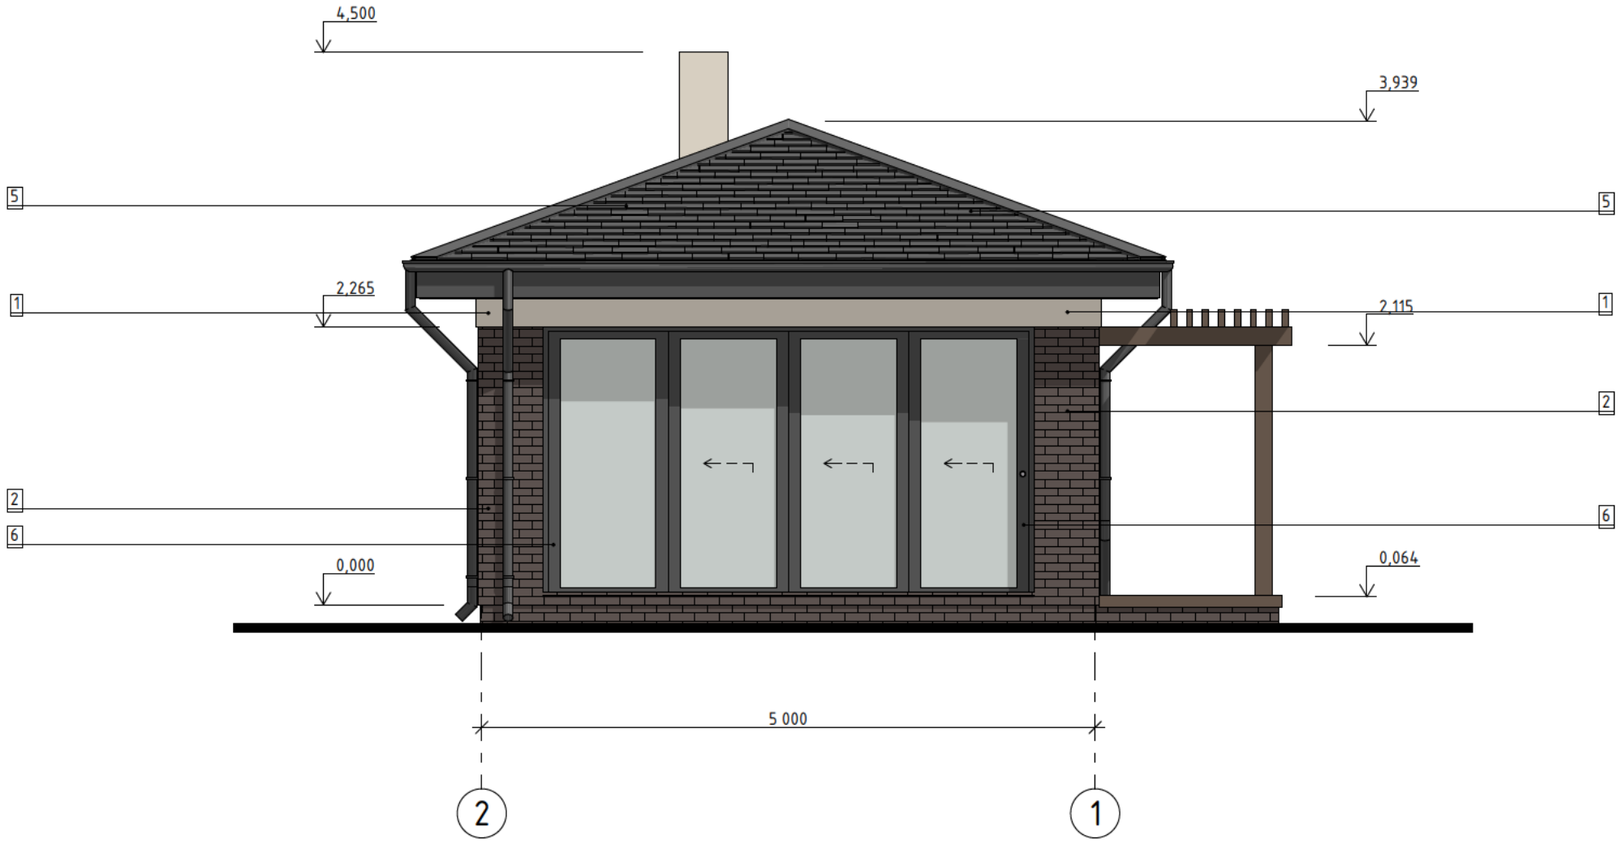

Ведомость отделки фасада

№ п/п	Наименование	Примечание
1	Отделка стен, штукатурка	
2	Отделка стен, клинкерный кирпич	
3	Отделка стен, фасадная доска	
4	Обшивка кровли, софиты	
5	Отделка кровли, мягкая черепица,	
6	Оконные и дверные профили	

Примечания:

1. Цветовое решение, а так же материалы фасада уточняются на дальнейшей стадии производства работ, выполняются выкрасы на стадии фасадных работ.
2. В цветовой гамме придерживатся дизайн кода поселка.

Изм.	Кол.уч.	Лист	№Док.	Подп.	Дата				
						Архитектурные решения	Стадия	Лист	Листов
						Фасад 2-1 М1:50			

Подп. и дата | Инв. № дубля | Взам.инв № | Подп. и дата | Инв. № подл.

Фасад 1-2 М1:50

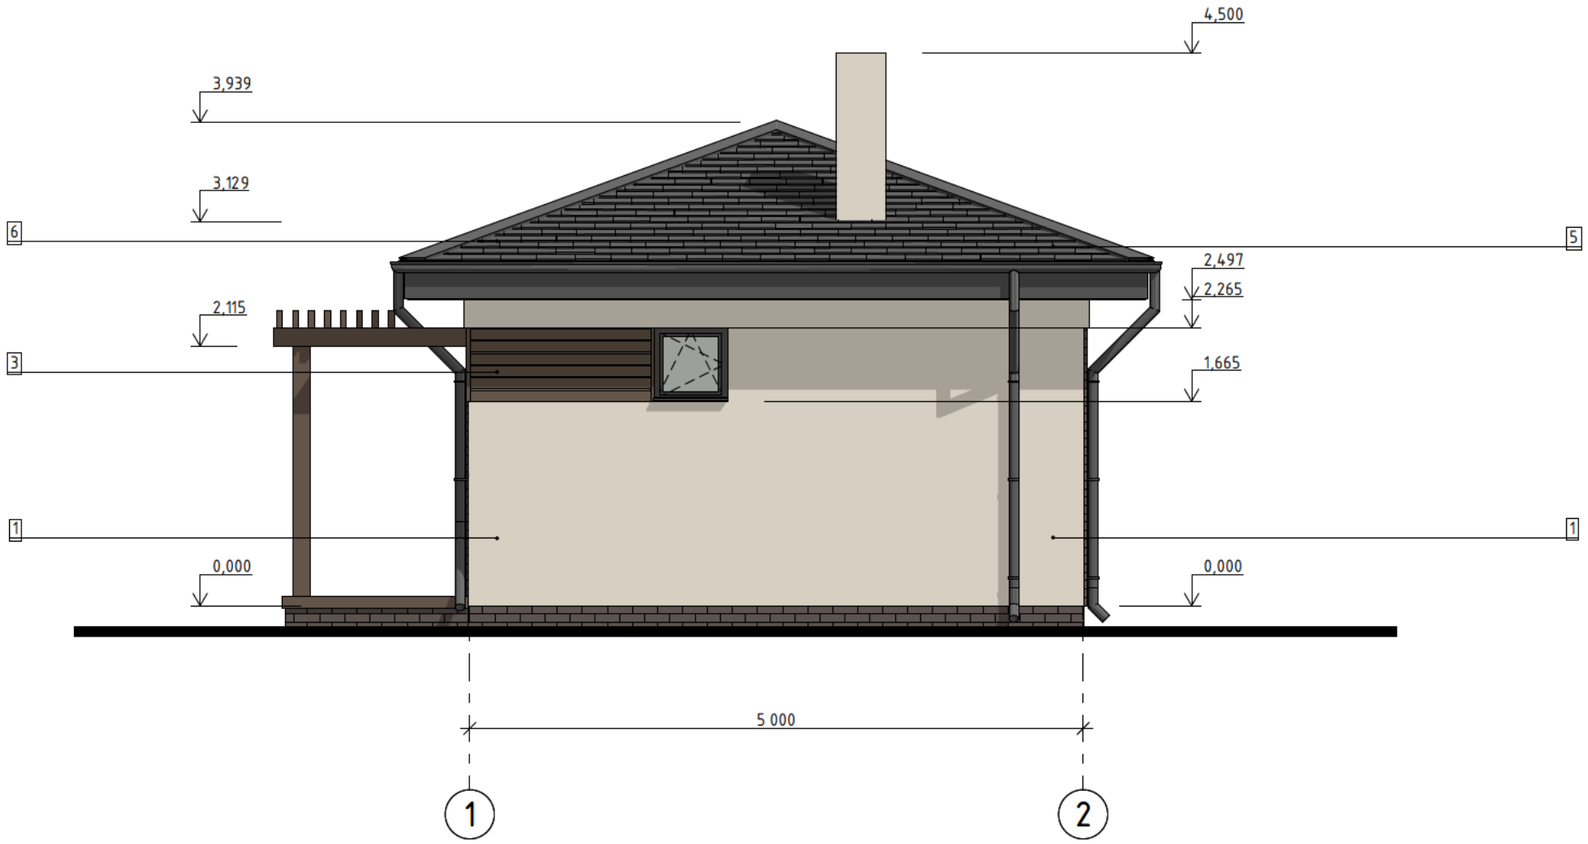

Ведомость отделки фасада

№ п/п	Наименование	Примечание
1	Отделка стен, штукатурка	
2	Отделка стен, клинкерный кирпич	
3	Отделка стен, фасадная доска	
4	Обшивка кровли, софиты	
5	Отделка кровли, мягкая черепица,	
6	Оконные и дверные профили	

Примечания:

1. Цветовое решение, а так же материалы фасада уточняются на дальнейшей стадии производства работ, выполняются выкрасы на стадии фасадных работ.
2. В цветовой гамме придерживатся дизайн кода поселка.

Изм.	Кол.уч.	Лист	№Док.	Подп.	Дата

Архитектурные решения	Стадия	Лист	Листов
Фасад 1-2 М1:50			

Подп. и дата | Инд. № дубля | Взам.инв № | Подп. и дата | Инв. № подл.

Разрез 1-1 М1:50

Мягкая черепица
Подкладочный ковер
OSB, 16мм
Обрешетка, 20х100мм
Гидро-ветрозащитная мембрана
Контробрешетка, 45х45мм
Стропило, 190х45мм
(утеплитель 200мм)
Пароборьер
Обрешетка, 45х45мм
Подшивка кровли, имитация бруса, 20мм

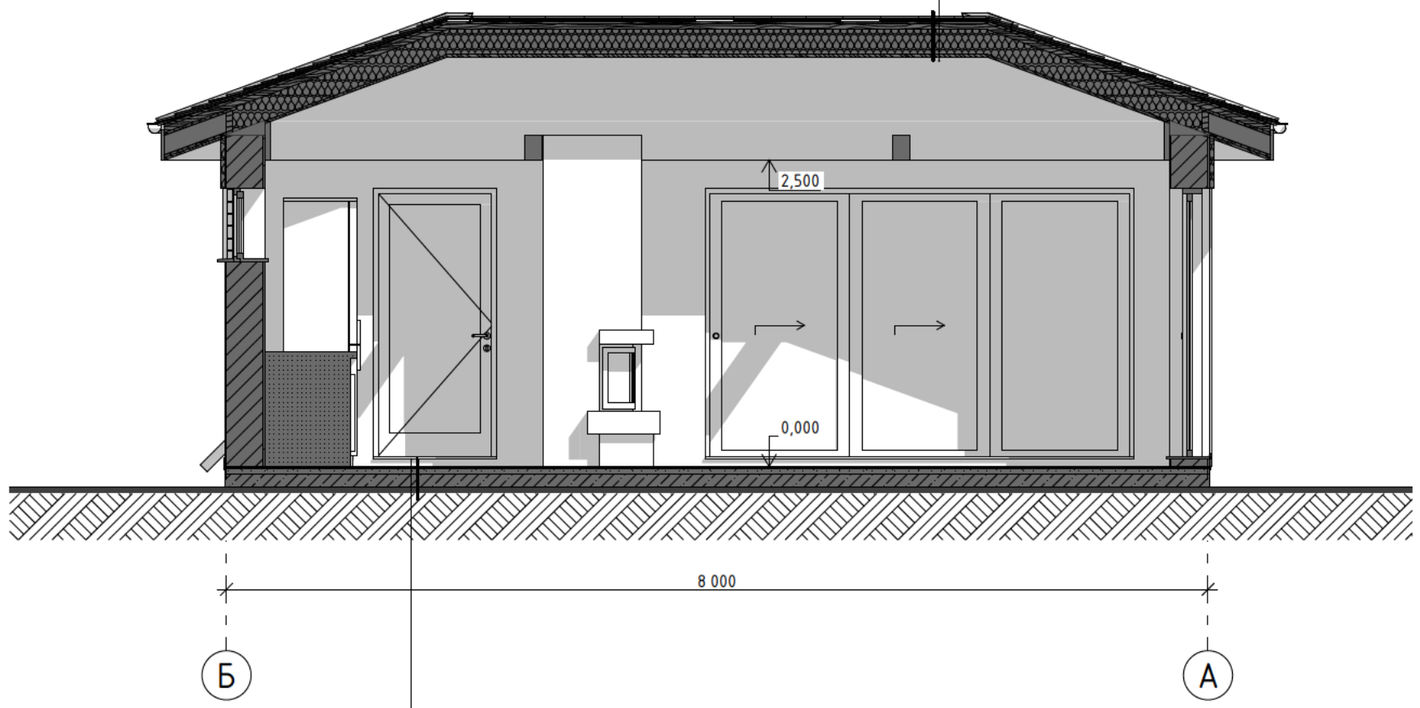

Керамогранит, 10мм
Плиточный клей, 10мм
Стяжка чистовая, 40мм
Бетонная плита основания

Примечания:
1. Шаг затяжек уточняется на дальнейшей стадии проектирования, в разделе КР

Изм.	Кол.уч.	Лист	№Док.	Подп.	Дата			
						Архитектурные решения	Стадия	Лист	Листов
						Разрез 1-1 М1:50		

Подп. и дата | Инв. № дубля | Взам.инв № | Подп. и дата | Инв. № подл.

Разрез 2-2 М1:50

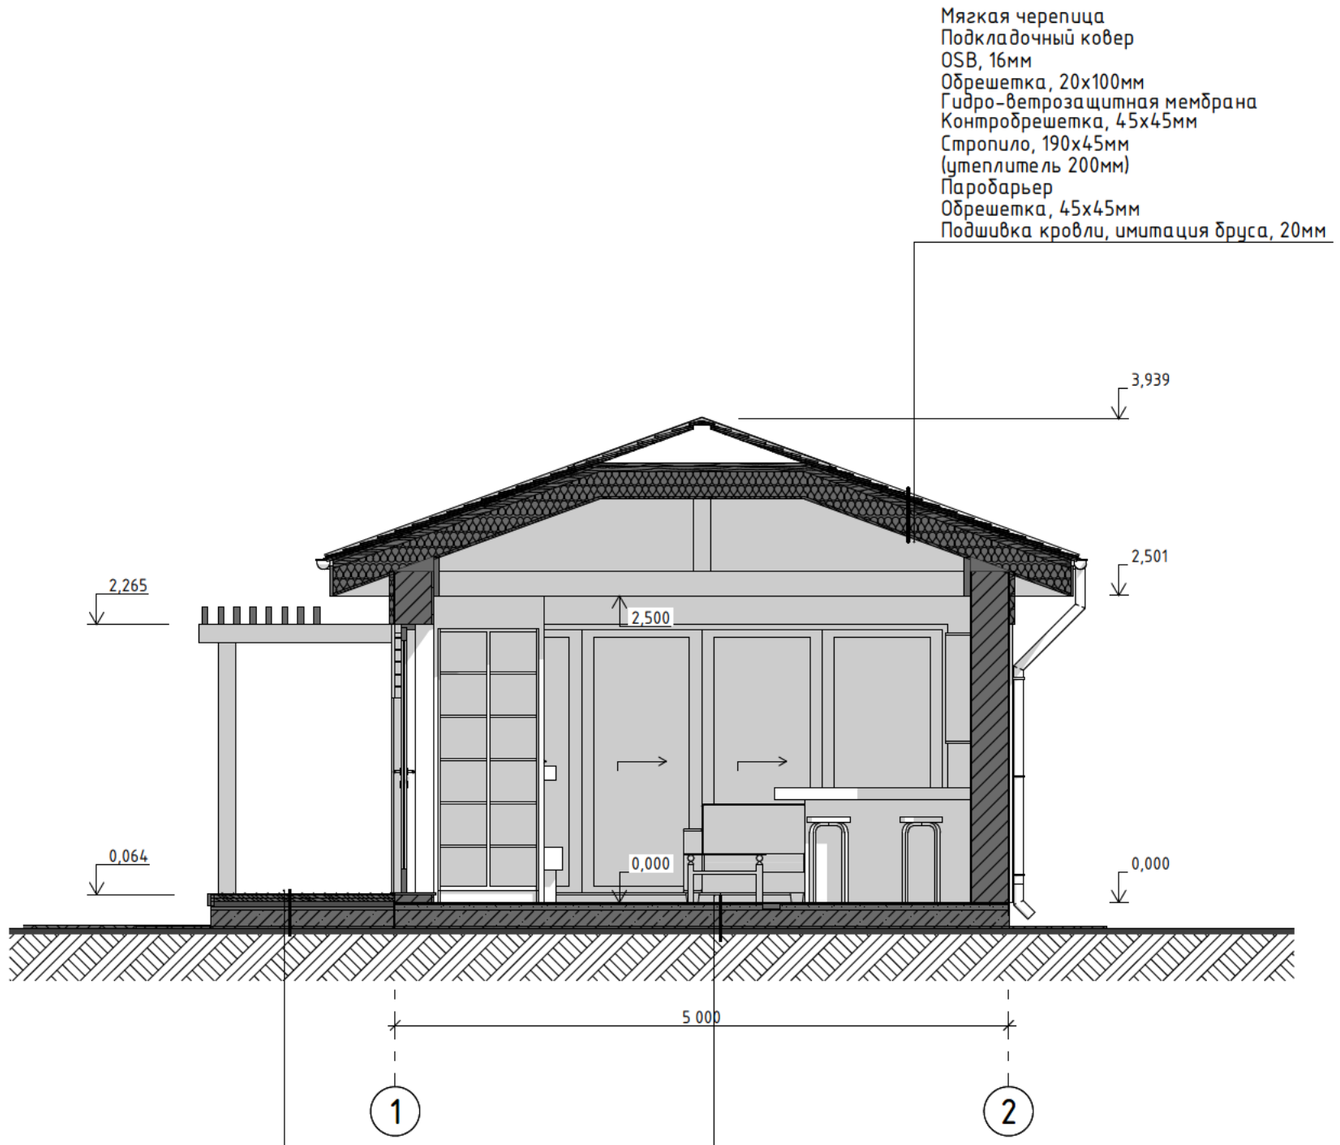

Изм.	Кол.уч.	Лист	№Док.	Подп.	Дата			
						Архитектурные решения	Стадия	Лист	Листов
						Разрез 2-2 М1:50			

Подп. и дата | Инв. № дубля | Взам.инв № | Подп. и дата | Инв. № подл.

Аксонометрия 1

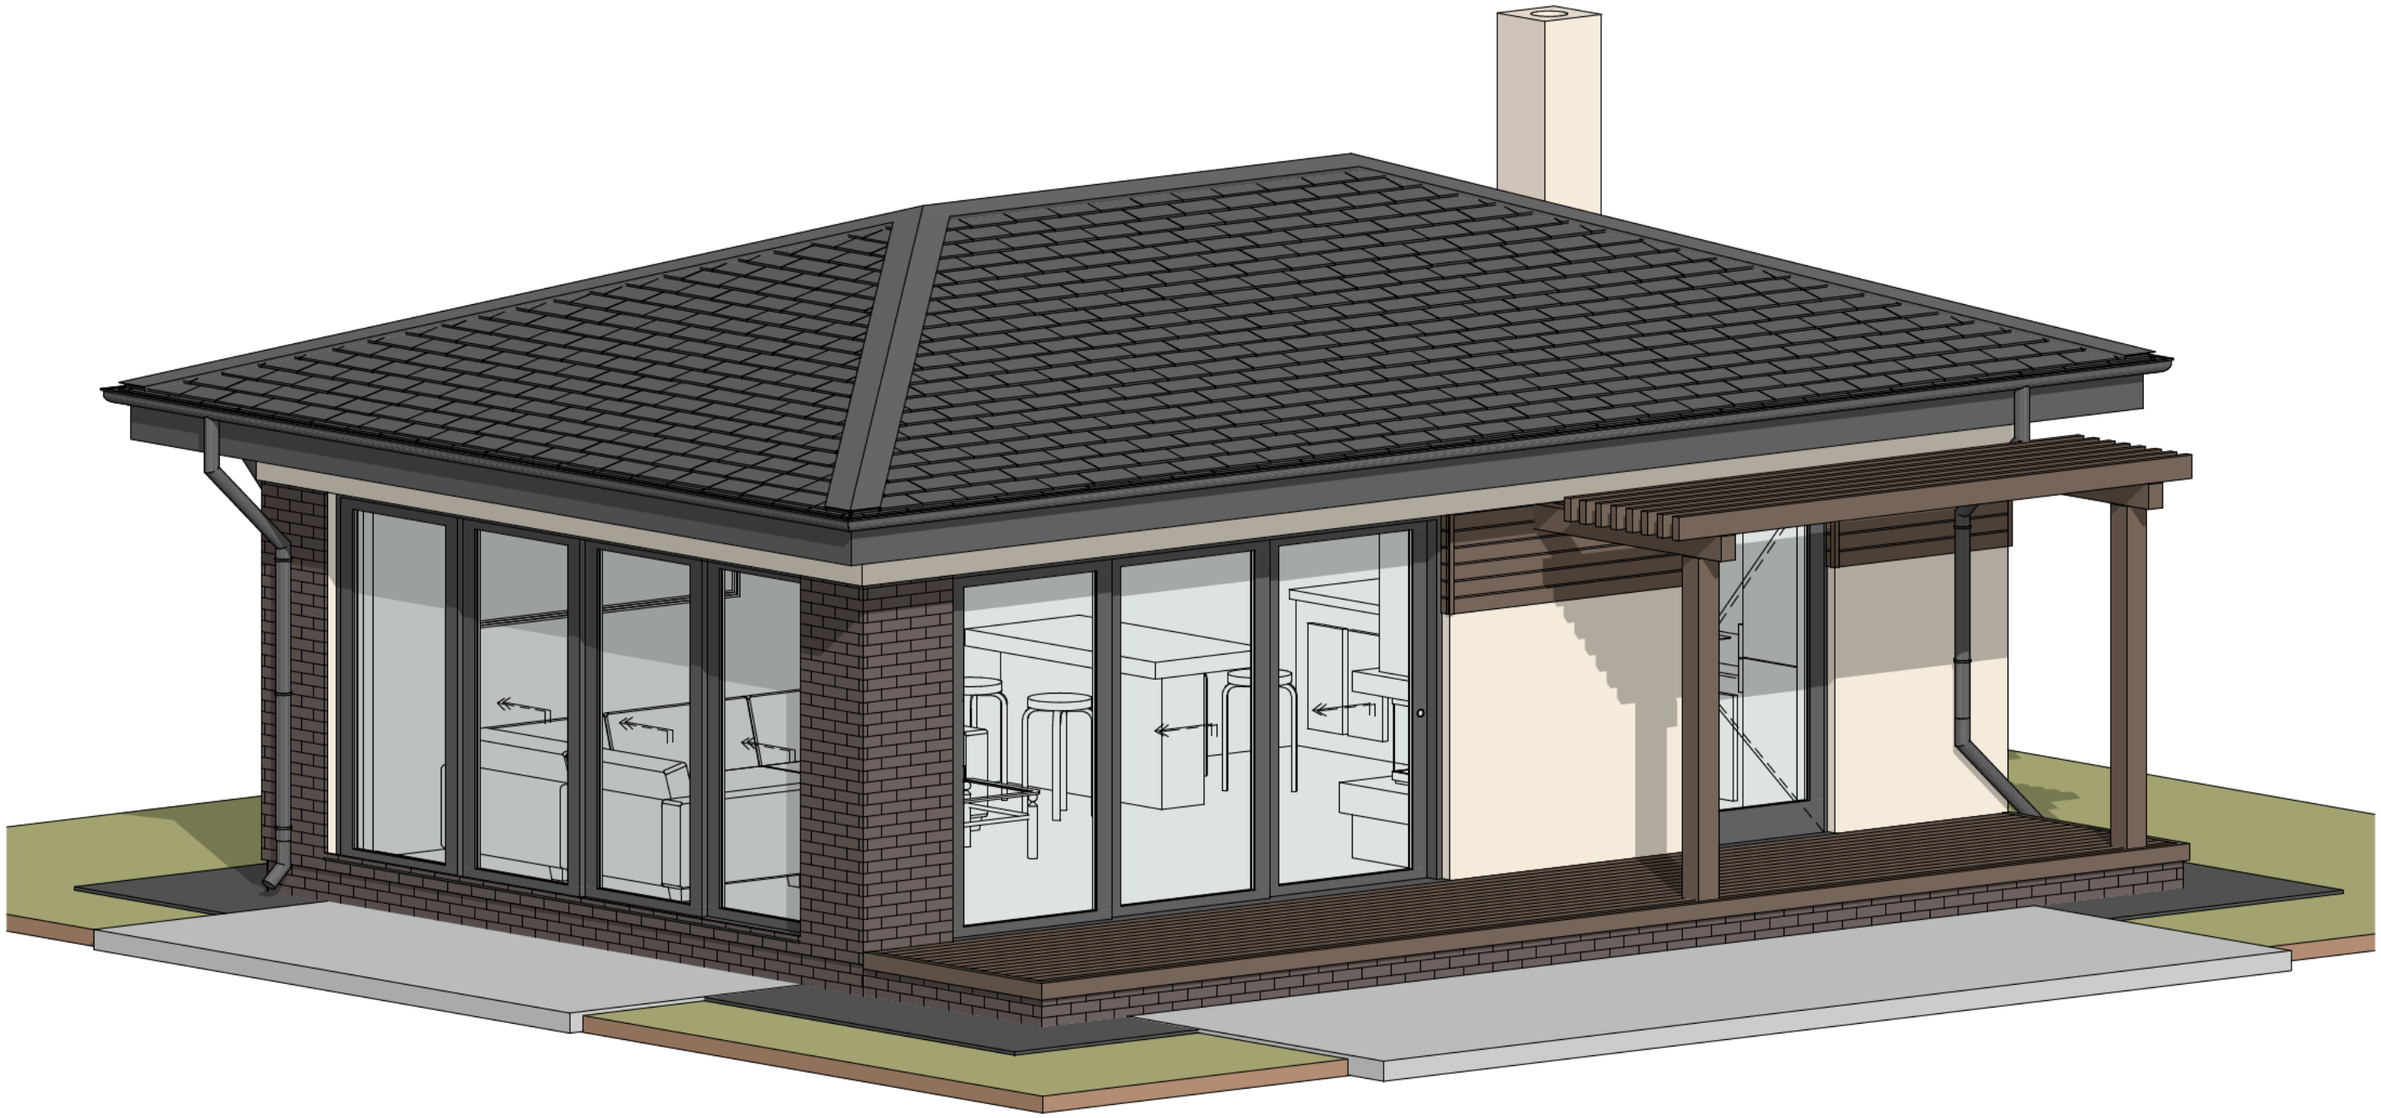

Примечания:

1. Цветовое решение, а так же материалы фасада уточняются на дальнейшей стадии проектирования

Изм.	Кол.уч.	Лист	№Док.	Подп.	Дата			
						Архитектурные решения	Стадия	Лист	Листов
						Аксонометрия 1			

Подп. и дата | Инв. № дубля | Взам.инв № | Подп. и дата | Инв. № подл.

Аксонометрия 2

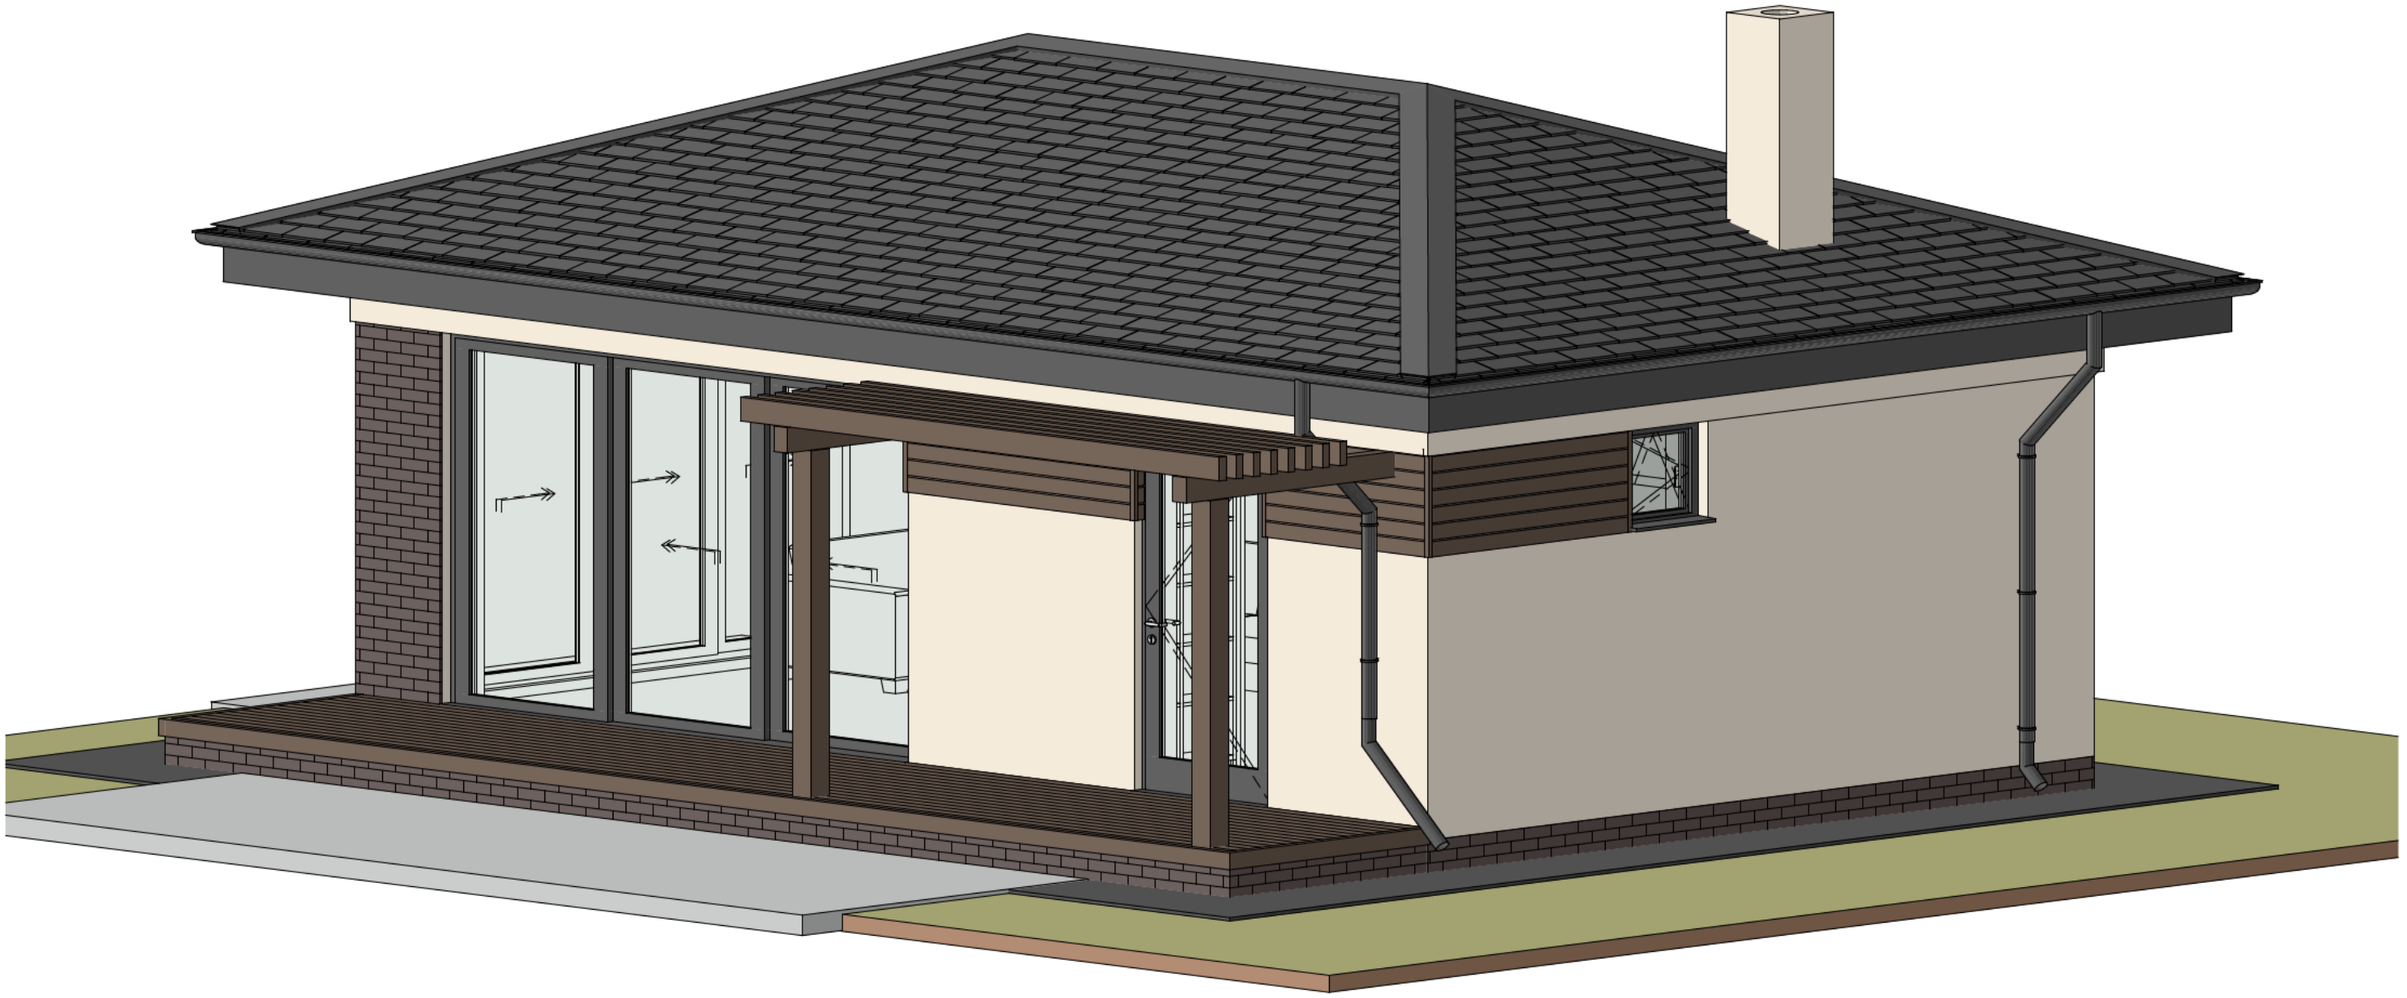

Примечания:

1. Цветовое решение, а так же материалы фасада уточняются на дальнейшей стадии проектирования

Изм.	Кол.уч.	Лист	№Док.	Подп.	Дата			
						Архитектурные решения	Стадия	Лист	Листов
						Аксонометрия 2			

Подп. и дата | Инв. № дубл | Взам.инв № | Подп. и дата | Инв. № подл.

Аксонометрия 3

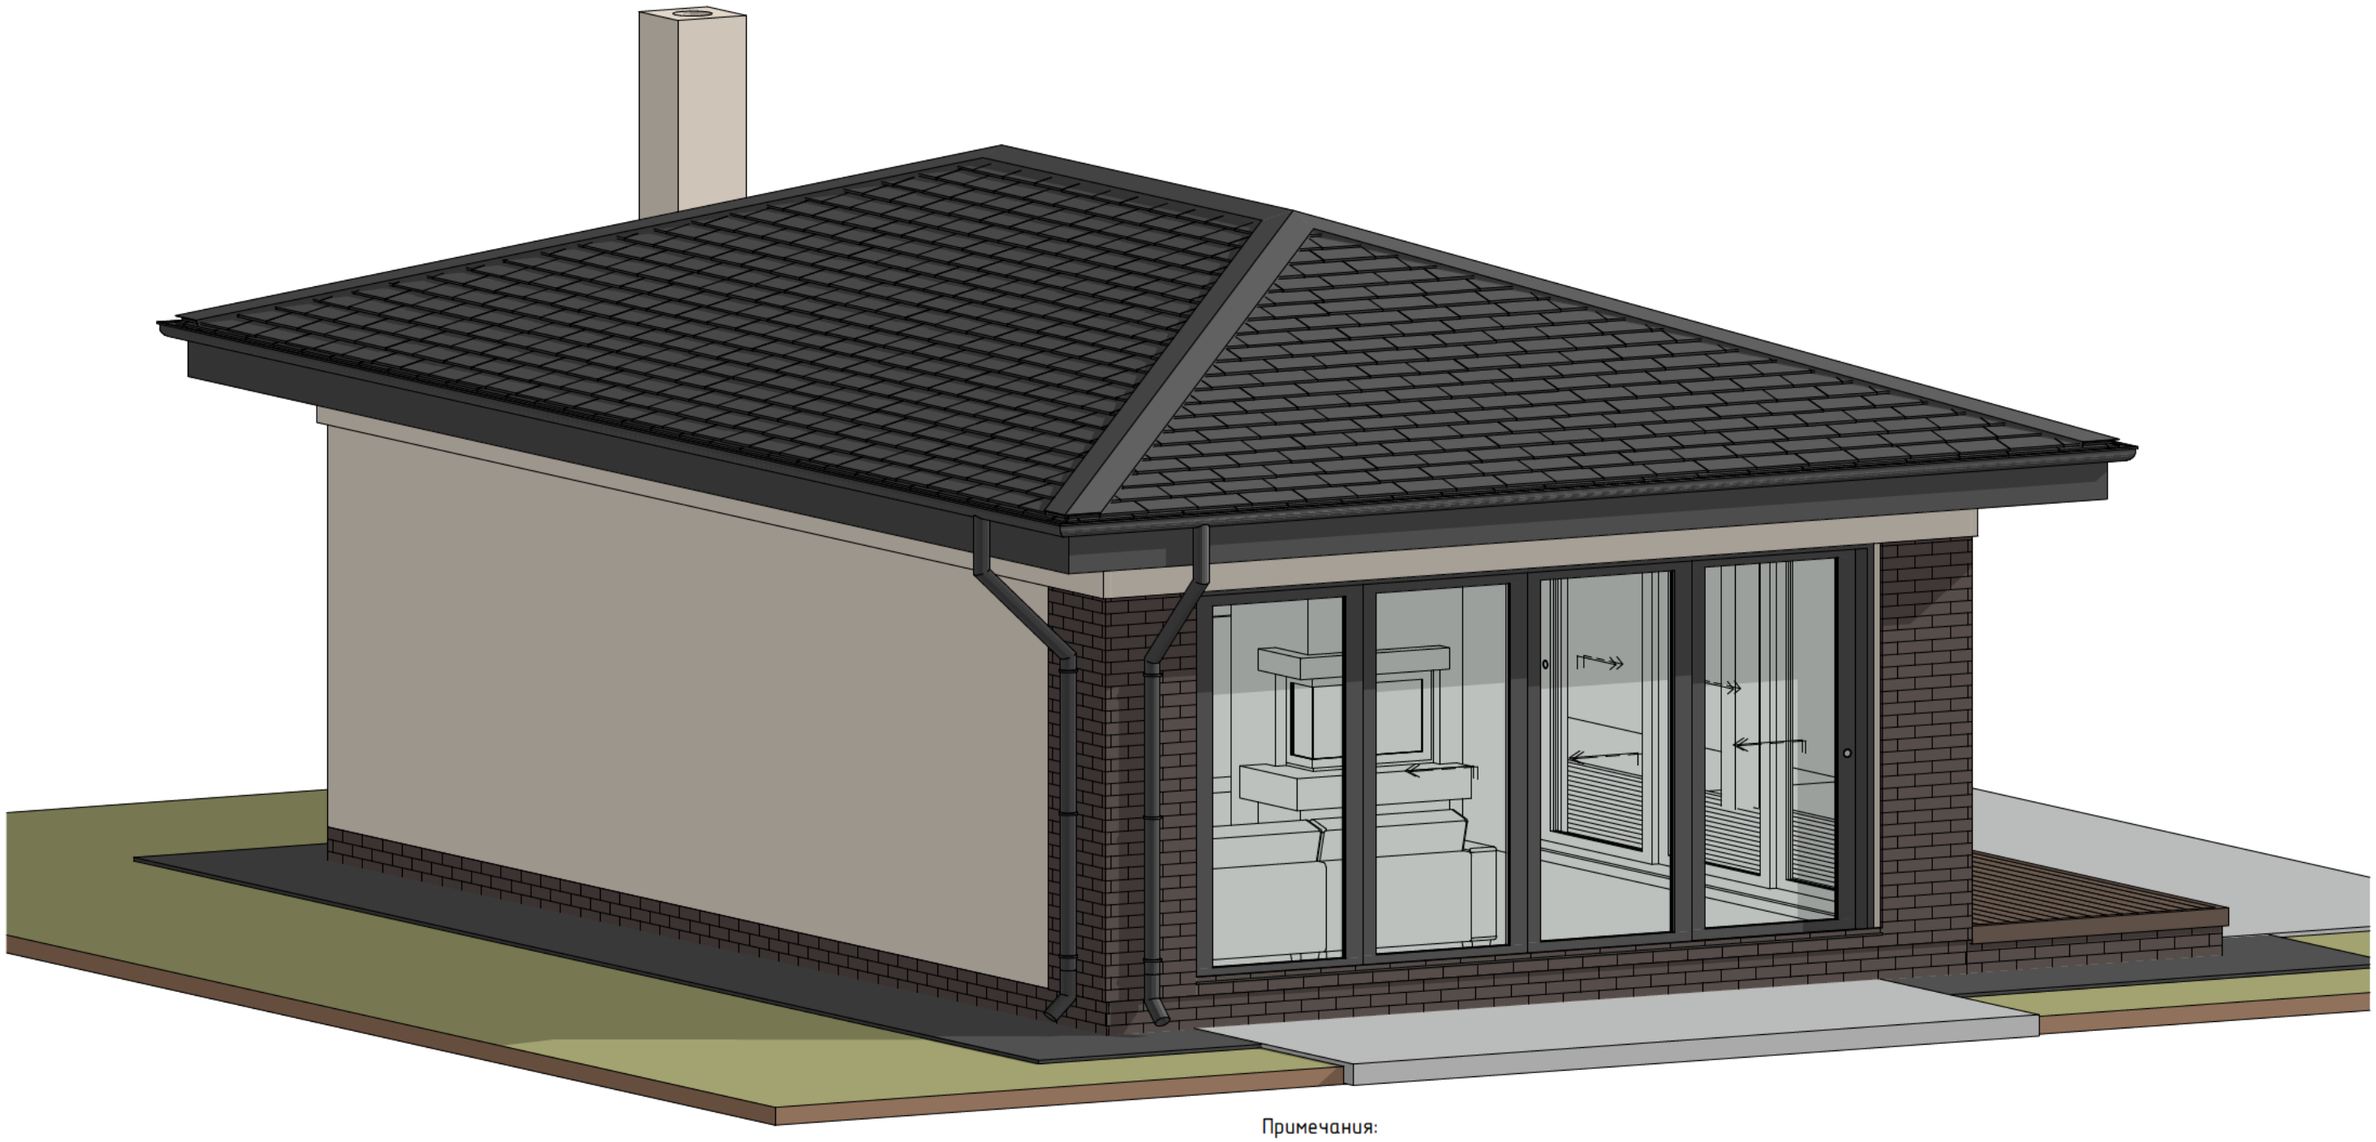

Примечания:

1. Цветовое решение, а так же материалы фасада уточняются на дальнейшей стадии проектирования

Изм.	Кол.уч.	Лист	№Док.	Подп.	Дата	Архитектурные решения	Стадия	Лист	Листов
						Аксонометрия 3			

Подп. и дата | Инд. № дубля | Взам.инд № | Подп. и дата | Инв. № подл.

Аксонометрия 4

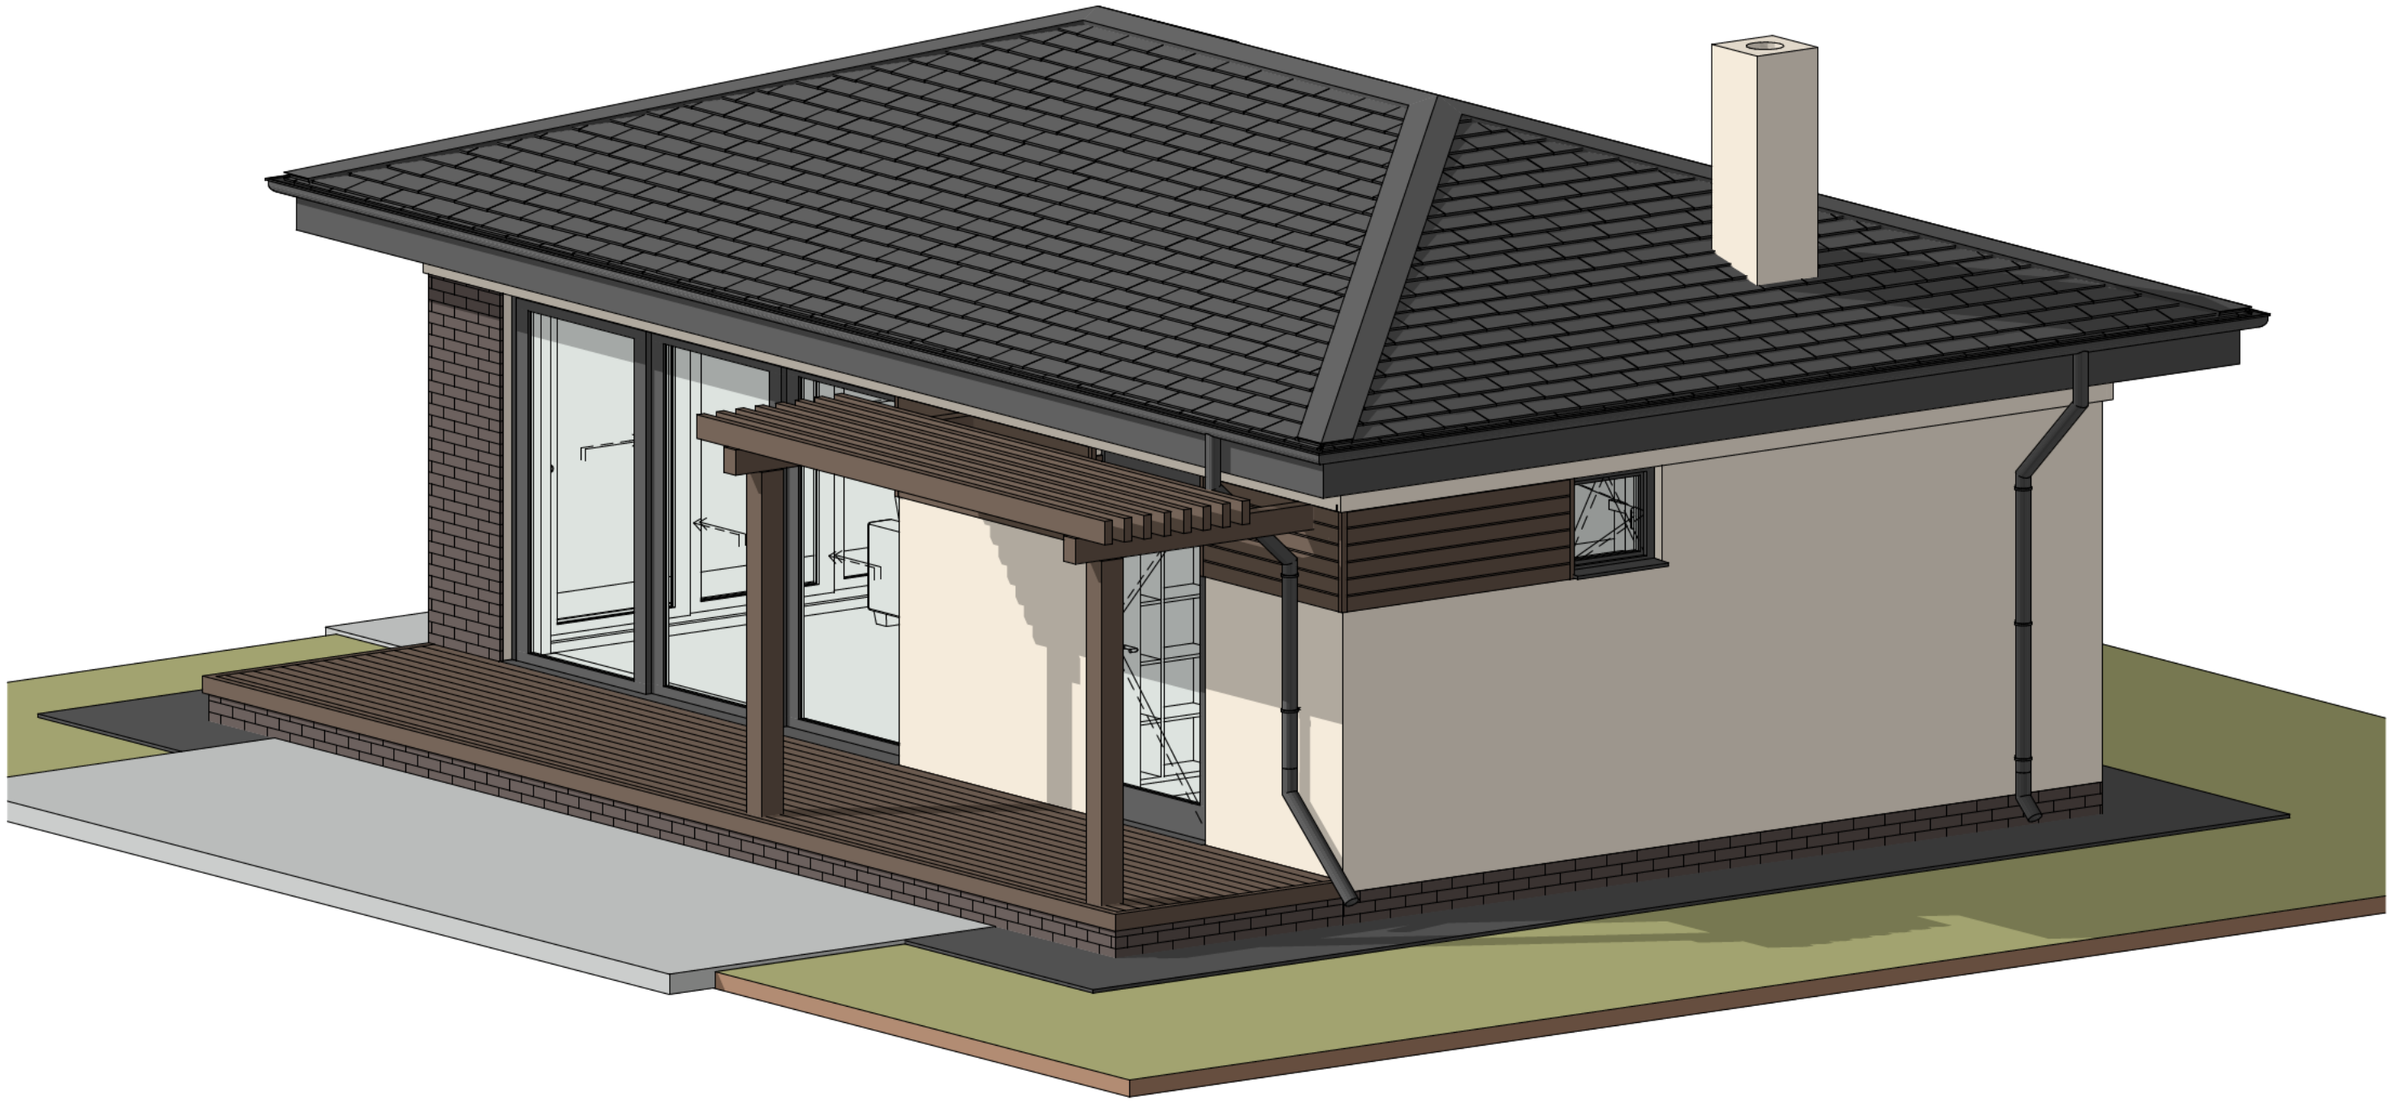

Примечания:

1. Цветовое решение, а так же материалы фасада уточняются на дальнейшей стадии проектирования

Изм.	Кол.уч.	Лист	№Док.	Подп.	Дата				
						Архитектурные решения	Стадия	Лист	Листов
						Аксонометрия 4			

Подп. и дата | Инв. № дубля | Взам.инв № | Подп. и дата | Инв. № подл.

План-схема электрики М1:50

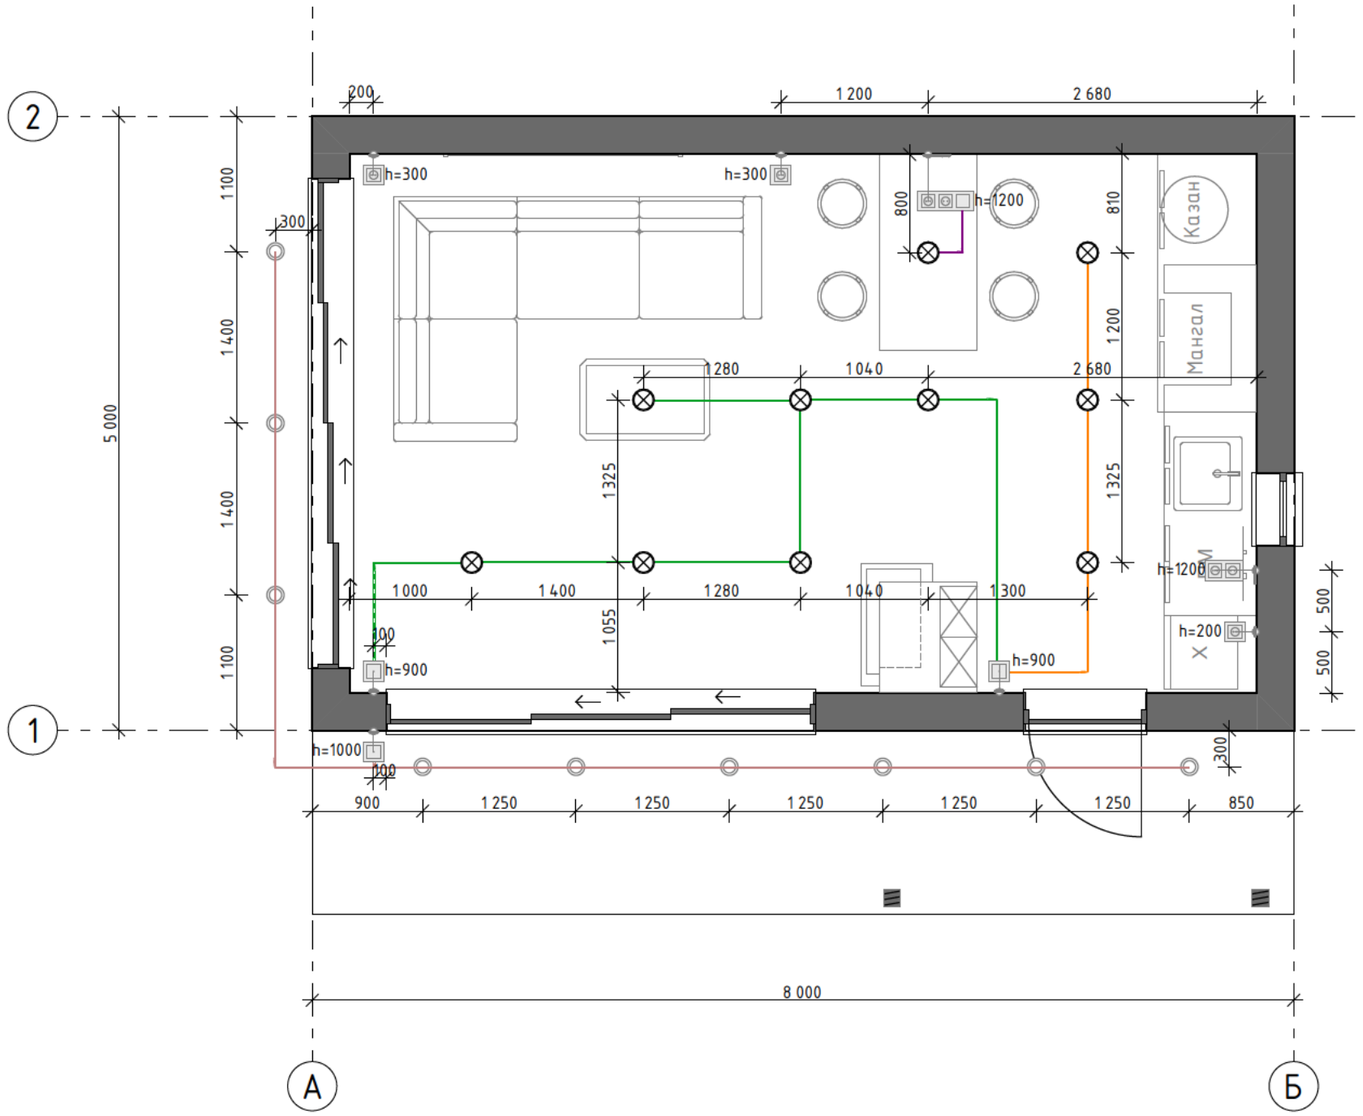

Спецификация электрооборудования:

Графическое изображение прибора	Наименование прибора	Количество	Примечания
	Выключатель 2х клавишкый (рамка 2 секции)	1	
	Выключатель (рамка 1 секция)	1	
	Выключатель одноклавишный(рамка 1 секция, уличный, IP 45)	1	уличный
⊗	Место расположения осветительного прибора	10	
○	Место расположения осветительного прибора (улица,IP 45)	9	уличный
	Розетка 220v (рамка 1 секция)	3	
	Розетка 220v (рамка 2 секции)	1	
	Розетка 220v, выключатель одноклавишный (рамка 3 секции)	1	
		27	

Примечания:
1. Схема размещения розеток является рекомендательной и требует согласования с заказчиком по месту.
2. Все высоты даны от чистового пола, все указанные размеры даются до центра позиций.
3. Отметки розеток, выключателей, выводов и др. оборудования, являются предварительными и уточняются после выбора финишных материалов и мебели.
4. Размеры даны без учета отделки.

Изм.	Кол.уч.	Лист	№Док.	Подп.	Дата

	Стадия	Лист	Листов
Архитектурные решения			
План-схема электрики М1:50			

Подп. и дата | Инв. № дубля | Взам.инв № | Подп. и дата | Инв. № подл.

Спецификация заполнения оконных проемов

Наименование	ОК-1
Количество	1
Размер Ш х В	600×600
Вид в плане	
Вид с фасада	
Площадь, м2	0,36
Примечания	

Спецификация заполнения дверных проемов

Наименование	ДВ-1	ДВ-2	ДВ-2
Количество	1	1	1
Размер Ш х В	3 500×2 200	1 000×2 200	4 000×2 200
Вид в плане	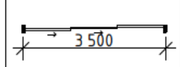	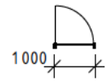	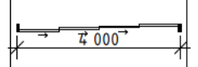
Вид с фасада	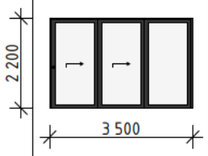	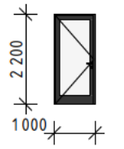	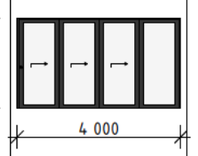
Площадь, м2	7,70	2,20	8,80
Примечания			

Подп. и дата | Инв. № дубл | Взам.инв № | Подп. и дата | Инв. № подл.

Изм.	Кол.уч.	Лист	№Док.	Подп.	Дата				
						Архитектурные решения	Стадия	Лист	Листов
						Спецификация заполнения дверных и оконных проемов			

План – схема кровли М1:50

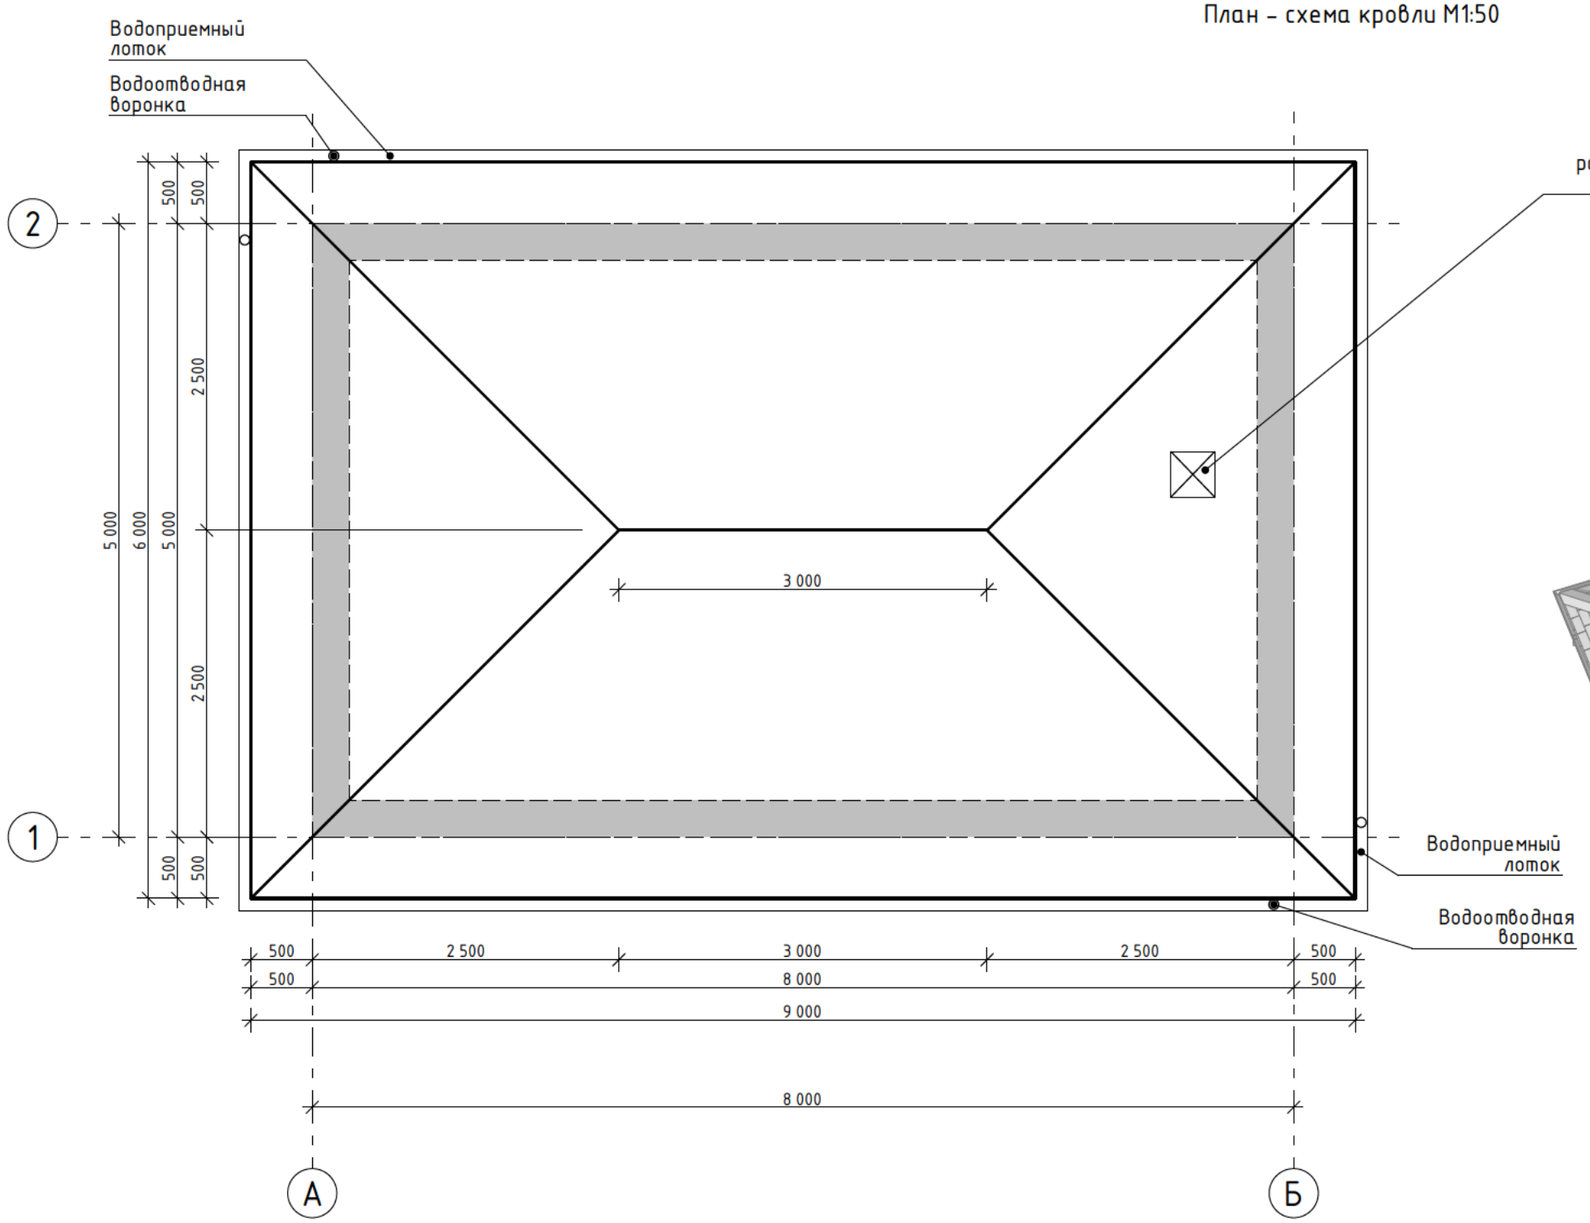

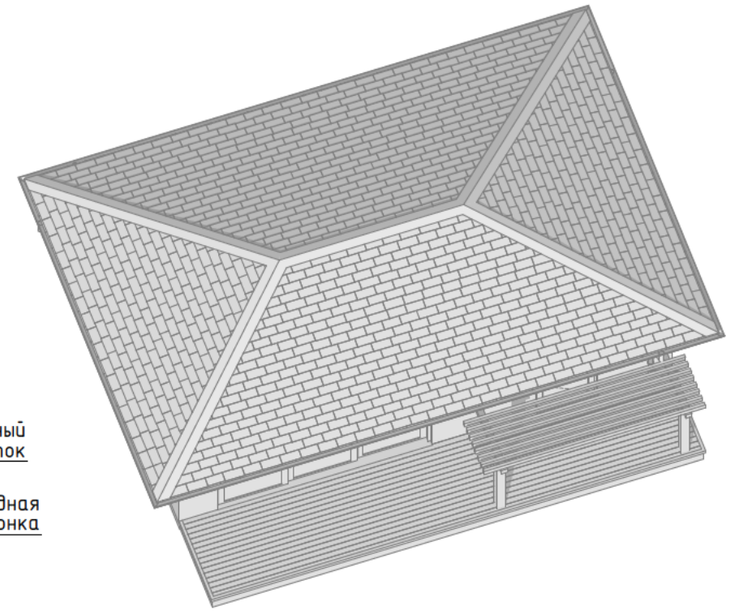

Примечания:

1. Место расположения дымохода и вентиляционных клапанов уточняется на плане стропильной системы в разделе КР

Изм.	Кол.уч.	Лист	№Док.	Подп.	Дата			
						Архитектурные решения	Стадия	Лист	Листов
						План – схема кровли М1:50			

Подп. и дата | Инв. № дубля | Взам.инв № | Подп. и дата | Инв. № подл.

Схема пирогов ограждающих конструкций, кровля

Номер п/п	Схема пирога ограждающей конструкции	Перечень материалов ограждающей конструкции
Кровельный пирог		
К-1	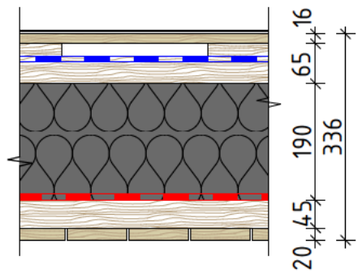	Мягкая черепица Подкладочный ковер OSB, 16мм Обрешетка, 20х100мм Гидро-ветрозащитная мембрана Контробрешетка, 45х45мм Стропило, 190х45мм (утеплитель 200мм) Паробарьер Обрешетка, 45х45мм Подшивка кровли, имитация бруса, 20мм

Схема пирогов ограждающих конструкций, стены

Номер п/п	Схема пирога ограждающей конструкции	Перечень материалов ограждающей конструкции
Стеновой пирог		
С-1	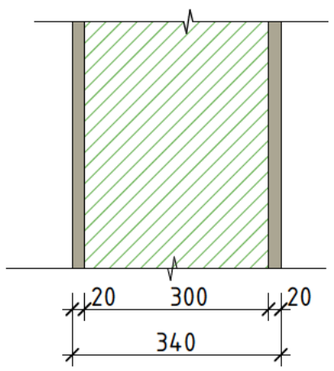	Штукатурка под покраску, 20мм Газоблок, 300мм Штукатурка под покраску, 20мм

Схема пирогов ограждающих конструкций, перекрытие

Номер п/п	Схема пирога ограждающей конструкции	Перечень материалов ограждающей конструкции
Пирог пола		
П-1	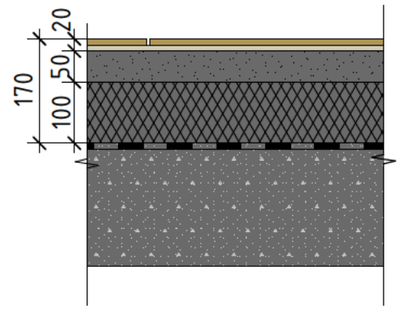	Керамогранит, 10мм Плиточный клей, 10мм (с устройством теплого пола) Чистовая стяжка, 50мм ЭППС, 100мм Гидроизоляция наплавляемая, 2 слоя Битумный праймер Ж.б. плита основания
П-2	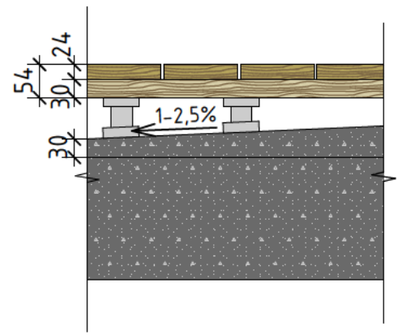	ДПК, 20мм Профиль основания, 30мм Регулируемая опора Гидроизоляция наплавляемая Уклонообразующая стяжка, от 30мм Ж.б. плита основания

Подп. и дата | Инв. № дубля | Взам.инв № | Подп. и дата | Инв. № подл.

Изм.	Кол.уч.	Лист	№Док.	Подп.	Дата

Архитектурные решения	Стадия	Лист	Листов
Схема пирогов ограждающих конструкций			

Примечания:
1. Цвета на визуализации могут незначительно отличатся от выбранных в итоге материалов из за индивидуальной цветопередачи каждого электронного устройства.

Изм.	Кол.уч.	Лист	№Док.	Подп.	Дата			
						Архитектурные решения	Стадия	Лист	Листов
						Визуализация 1			

Подп. и дата | Инв. № дубля | Взам.инв № | Подп. и дата | Инв. № подл.

Примечания:

1. Цвета на визуализации могут незначительно отличатся от выбранных в итоге материалов из за индивидуальной цветопередачи каждого электронного устройства.

Изм.	Кол.уч.	Лист	№Док.	Подп.	Дата

Архитектурные решения	Стадия	Лист	Листов
Визуализация 2			

Подп. и дата | Инв. № дубля | Взам.инв № | Подп. и дата | Инв. № подл.

Примечания:
1. Цвета на визуализации могут незначительно отличатся от выбранных в итоге материалов из за индивидуальной цветопередачи каждого электронного устройства.

Изм.	Кол.уч.	Лист	№Док.	Подп.	Дата			
						Архитектурные решения	Стадия	Лист	Листов
						Визуализация 3			

Инв. № подл. | Подп. и дата | Взам.инв № | Инв. № дубля | Подп. и дата