

ARCHITECTURE/
CONSTRUCTION



Название:
Разработал:
Принял:
г. Москва



Согласовано				
И-в. № подл.	Подп. и дата	Взам. инв. №		

Лист	Наименование	Примечание
1	Ведомость чертежей	
2	Пояснительная записка	
3	Схема планировочной организации земельного участка	
4	Маркировочный план	
5	Размерный план	
6	План расстановки мебели и оборудования	
7	3д-разрез	
8	План водяного теплого пола	
9	План покрытий пола	
10	Экспликация покрытий пола	
11	План покрытия отделки стен	
12	Экспликация отделки стен	
13	План размещения розеток стен	
14	План расстановки светильников и выключателей	
15	План кровли	
16	Разрез 1-1	
17	Разрез 2-2	
18	Ведомость оконных проёмов	
19	Ведомость дверных проёмов	
20	Цветовое решение; Фасад в осях В-А	
21	Цветовое решение; Фасад в осях 3-1	
22	Аксонометрия №1	
23	Цветовое решение; Фасад в осях А-В	
24	Цветовое решение; Фасад в осях 1-3	
25	Аксонометрия №2	
26	Визуализация №1	
27	Визуализация №2	
28	Визуализация №3	
29	Визуализация №4	
30	Визуализация №5	
31	Визуализация №6	

Лист	Изм.	№ Докум.	Подп.	Дата	Адрес:	Ведомость чертежей	#Название Организации	Лист
								1

В основу архитектурно-планировочных решений положены требования технологических заданий и требования норм и правил строительного проектирования, действующих на территории РФ.

Основные параметры и требования разработаны на основании пожеланий и требований заказчика.

- Архитектурные решения приняты в соответствии со следующими нормативными документами:
- Градостроительный кодекс российской федерации.
 - Земельного Кодекса Российской Федерации.
 - Федеральный закон от 22.07.2008 N 123 - ФЗ (ред. от 29.07.2017)"Технический регламент о требованиях пожарной безопасности.
 - Федеральный закон № 384 - ФЗ «Технический регламент о безопасности зданий и сооружений».
 - ГОСТ Р 21.1101-2013.«Основные требования к проектной и рабочей документации».
 - Постановление правительства РФ от 16.02.2008 № 87 «Положение о составе разделов проектной документации и требованиях к их содержанию».
 - СП 42.13330.2011 «Градостроительство. Планировка и застройка городских и сельских поселений».
 - СП 131.13330.2018 «СНиП 23-01-99* Строительная климатология».
 - СП 20.13330.2016 «СНиП 2.01.07-85* Нагрузки и воздействия».
 - СП 22.13330.2016 «СНиП 2.02.01-83* Основания зданий и сооружений».
 - СП 70.13330.2012 (с изменениями №1) «СНиП 3.03.01-87 Несущие и ограждающие конструкции».
 - СП 64.13330.2017 «СНиП II-25-80 Деревянные конструкции».
 - СП 17.13330.2017 «СНиП II-26-76 Кровли».
 - СП 29.13330.2011 «СНиП 2.03.13-88 Полы».
 - СП 28.13330.2017 «СНиП 2.03.11-85 Защита строительных конструкций от коррозии».
 - СП 50.13330.2012 «СНиП 23-02-2003 Тепловая защита зданий».

Согласовано				
И-нв. № подл.	Подп. и дата	Взам. инв. №		

1. Общие данные:

1.1. Архитектурный проект разработан на основании требований и пожеланий заказчика.

Тип строения	Баня
Относительная отм. ±0.000	ур. верха лаг перекрытия
Общая площадь застройки, м2	65,45
Габаритные размеры каркаса здания	7,7х6 м
Этажность	1 этаж
Конструктивная схема	Деревянный каркас

2. Конструктивные решения:

2.1. Рабочие чертежи разработаны на основании задания на проектирование

Полезная нагрузка на перекрытие	150 кгс/м2	-
Нормативная глубина промерзания	1,2м	СП 22.13330.2016 СП 131.13330.2020
Нормативное ветровое давление	I район (23кгс/м2)	СП 22.13330.2016
Нормативный вес снегового покрова	III район (150кгс/м2)	СП 22.13330.2016
Температура наиболее холодной пятидневки	-29°С	СП 131.13330.2020

2.2. Конструктивное строение представляет собой сооружение:

- на свайном фундаменте
- несущими стенами из деревянного каркаса
- вальмовой кровлей по деревянным стропилам

2.3. Необходимо осуществлять технический надзор за производством строительных работ. Данные по проведённым работам необходимо систематически вносить в журнал работ.

По каждому из этапов работ необходимо осуществлять входной контроль материалов и вести приёмку.

Несущие конструкции	деревянный каркас (140х45мм)
Покрытие кровли	металлическая черепица
Стропильная система	строганая доска (140х45мм)
Тип крыши	вальма
Фундамент	винтовые сваи (d108мм)

2.4. Все деревянные конструкции обработать огне-биозащитными септиками в соответствии со СП 28.13330.2017 "Защита строительных конструкций от коррозии".

2.5. Кровельные работы выполнять в соответствии с требованиями фирмы производителя.

2.6. Все работы вести в строгом соответствии с требованиями СНиП 12.03.2001 "Безопасность труда в строительстве".

2.7. При выполнении всех работ строго соблюдать меры противопожарной безопасности.

2.8. Возможна замена материалов аналогами.

*Решения, принятые в проекте и отображенные в чертежах, соответствуют требованиям экологических, санитарно - гигиенических, противопожарных и других норм, действующих на территории Российской Федерации, и обеспечивают безопасную для жизни и здоровья людей эксплуатацию объекта при соблюдении предусмотренных рабочих чертежей и мероприятий.

Лист	Изм.	№ Докум.	Подп.	Дата

Адрес:



Пояснительная записка

#Название Организации

- Граница участка
- Граница застройки участка
- 1 - Существующий индивидуальный жилой дом
- 2 - Банный комплекс (проектируемая постройка)

Технико-экономические показатели

Наименование	Площадь, м²
Общая площадь застройки (баня+ИЖД)	168,34
Площадь участка (по топографической съемке)	782,80
Площадь застройки (баня)	65,45
Площадь застройки (ИЖД)	102,89

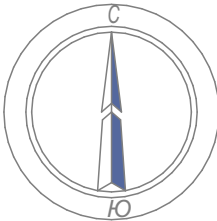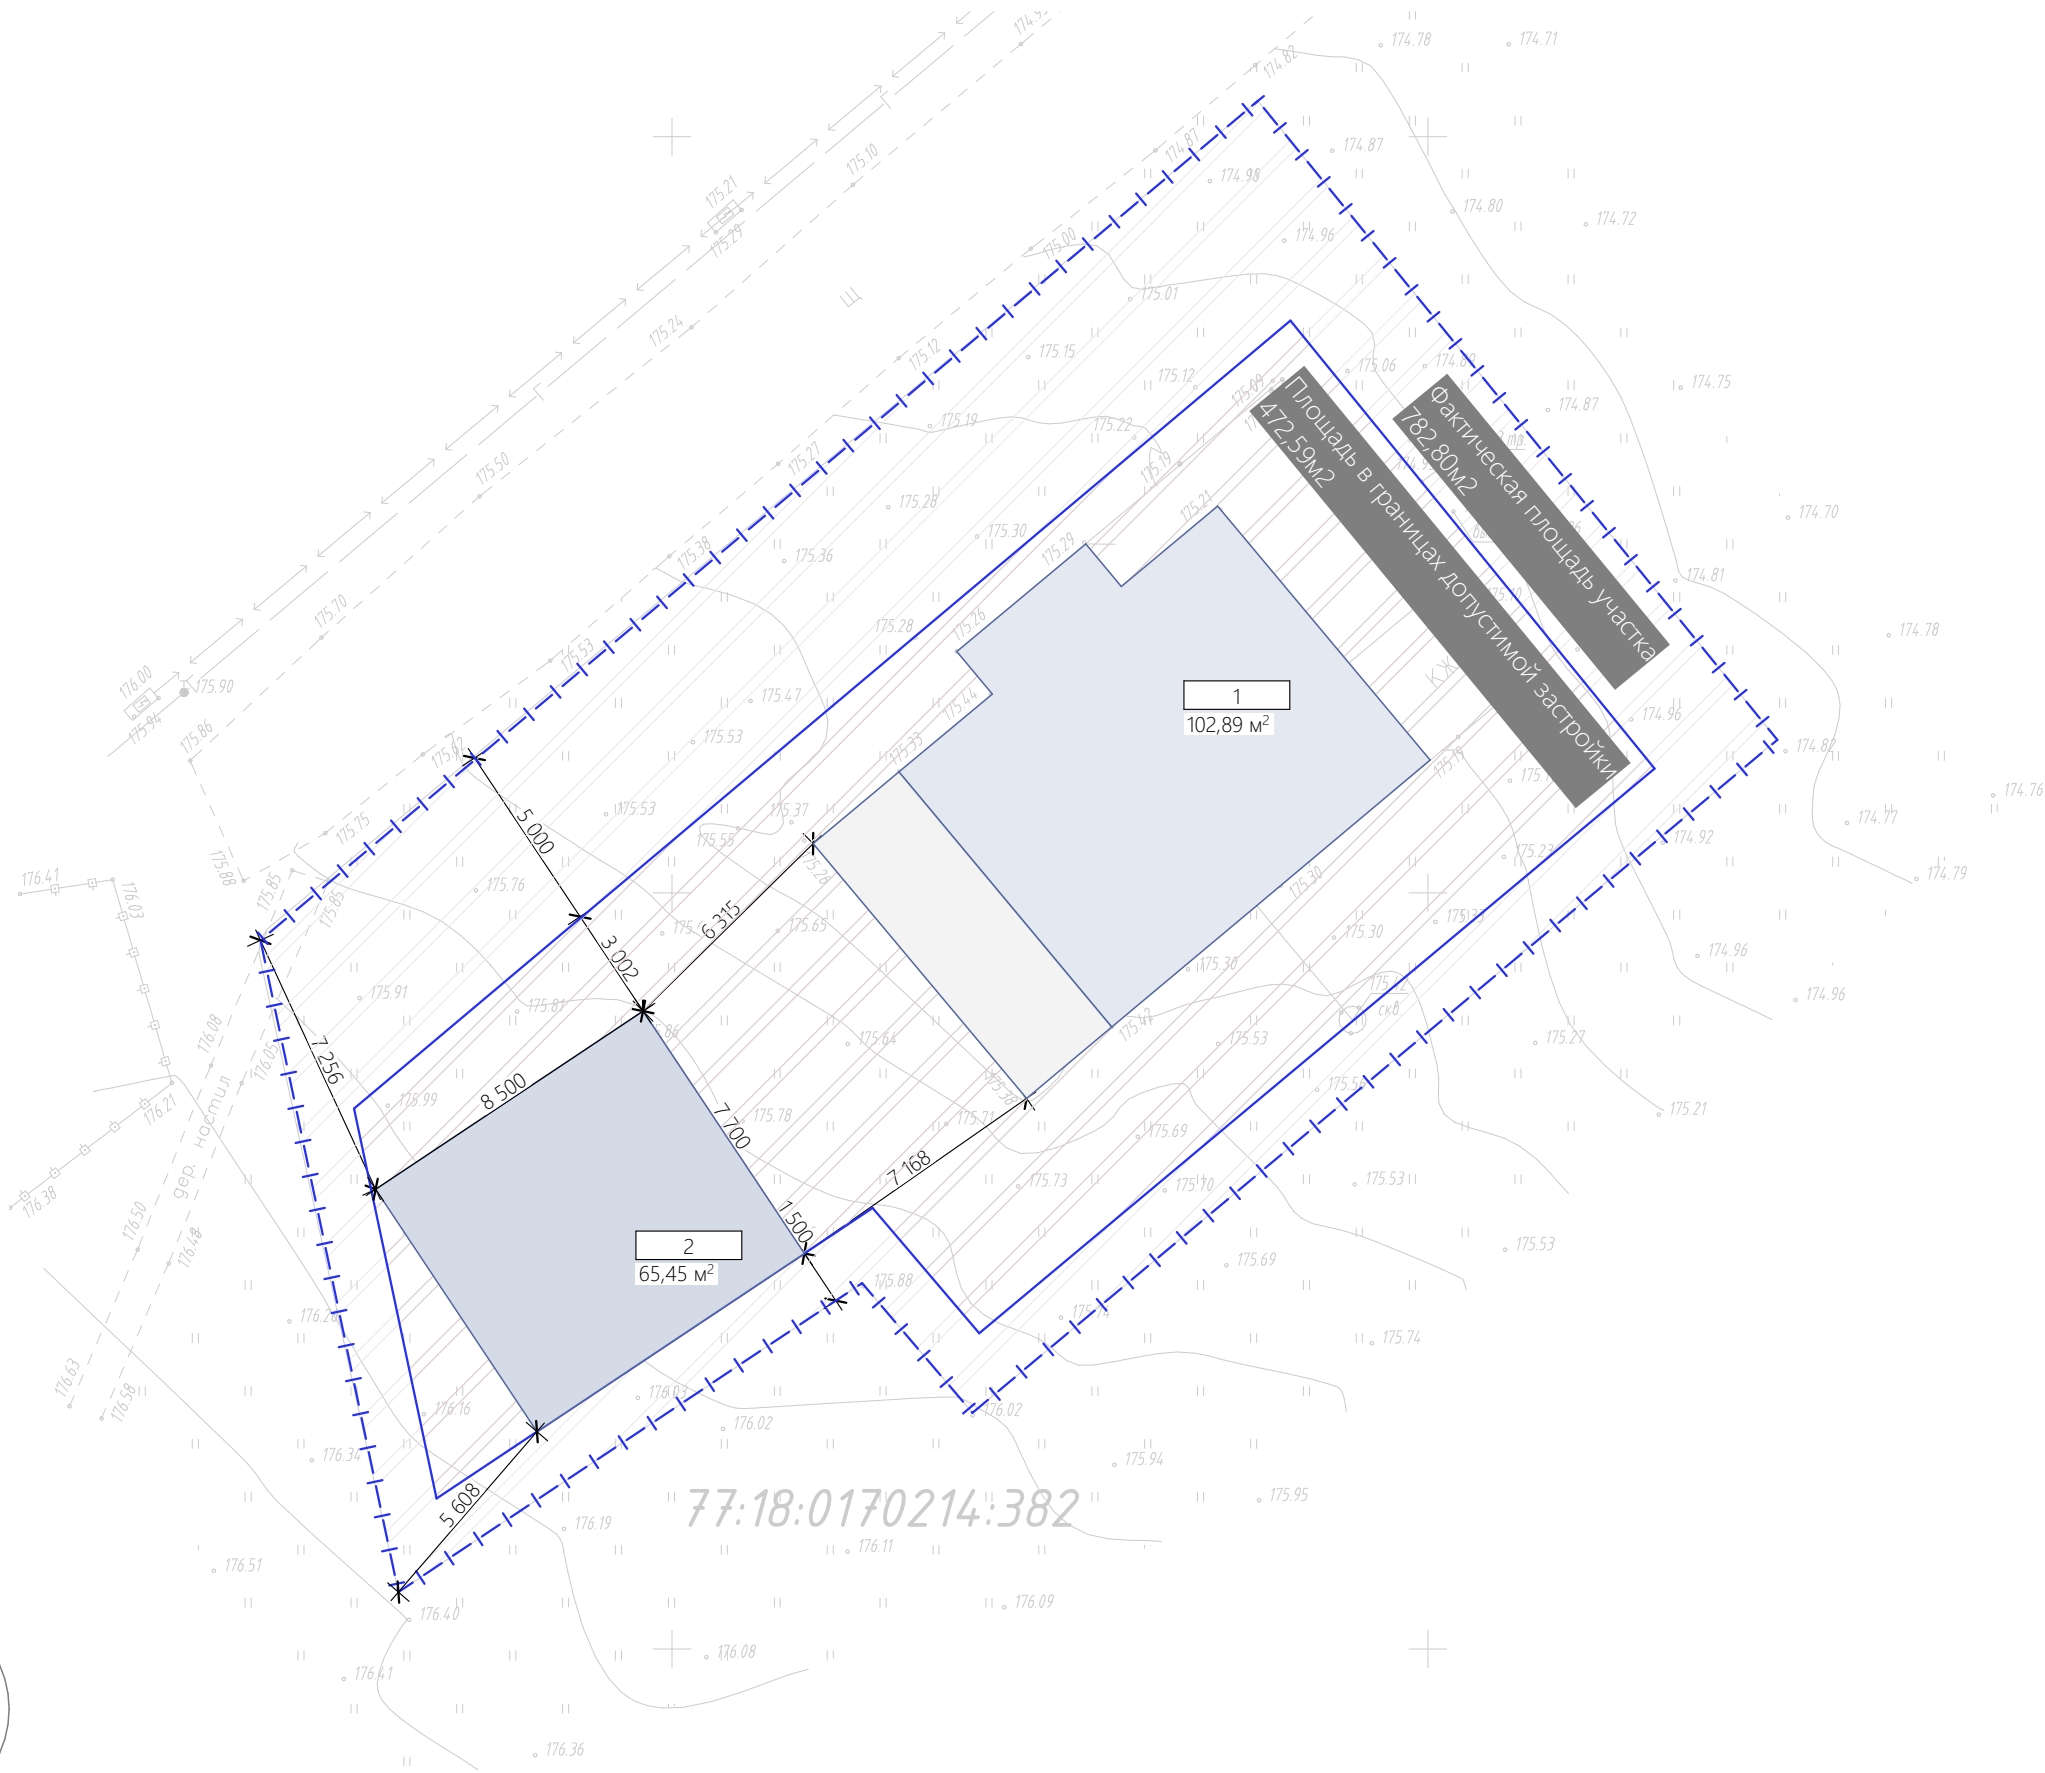


Согласовано				
И-нв. № подл.	Подп. и дата	Взам. инв. №		

Лист	Изм.	№ Докум.	Подп.	Дата

Адрес:

Схема планировочной организации земельного участка

#Название Организации	Лист
	3

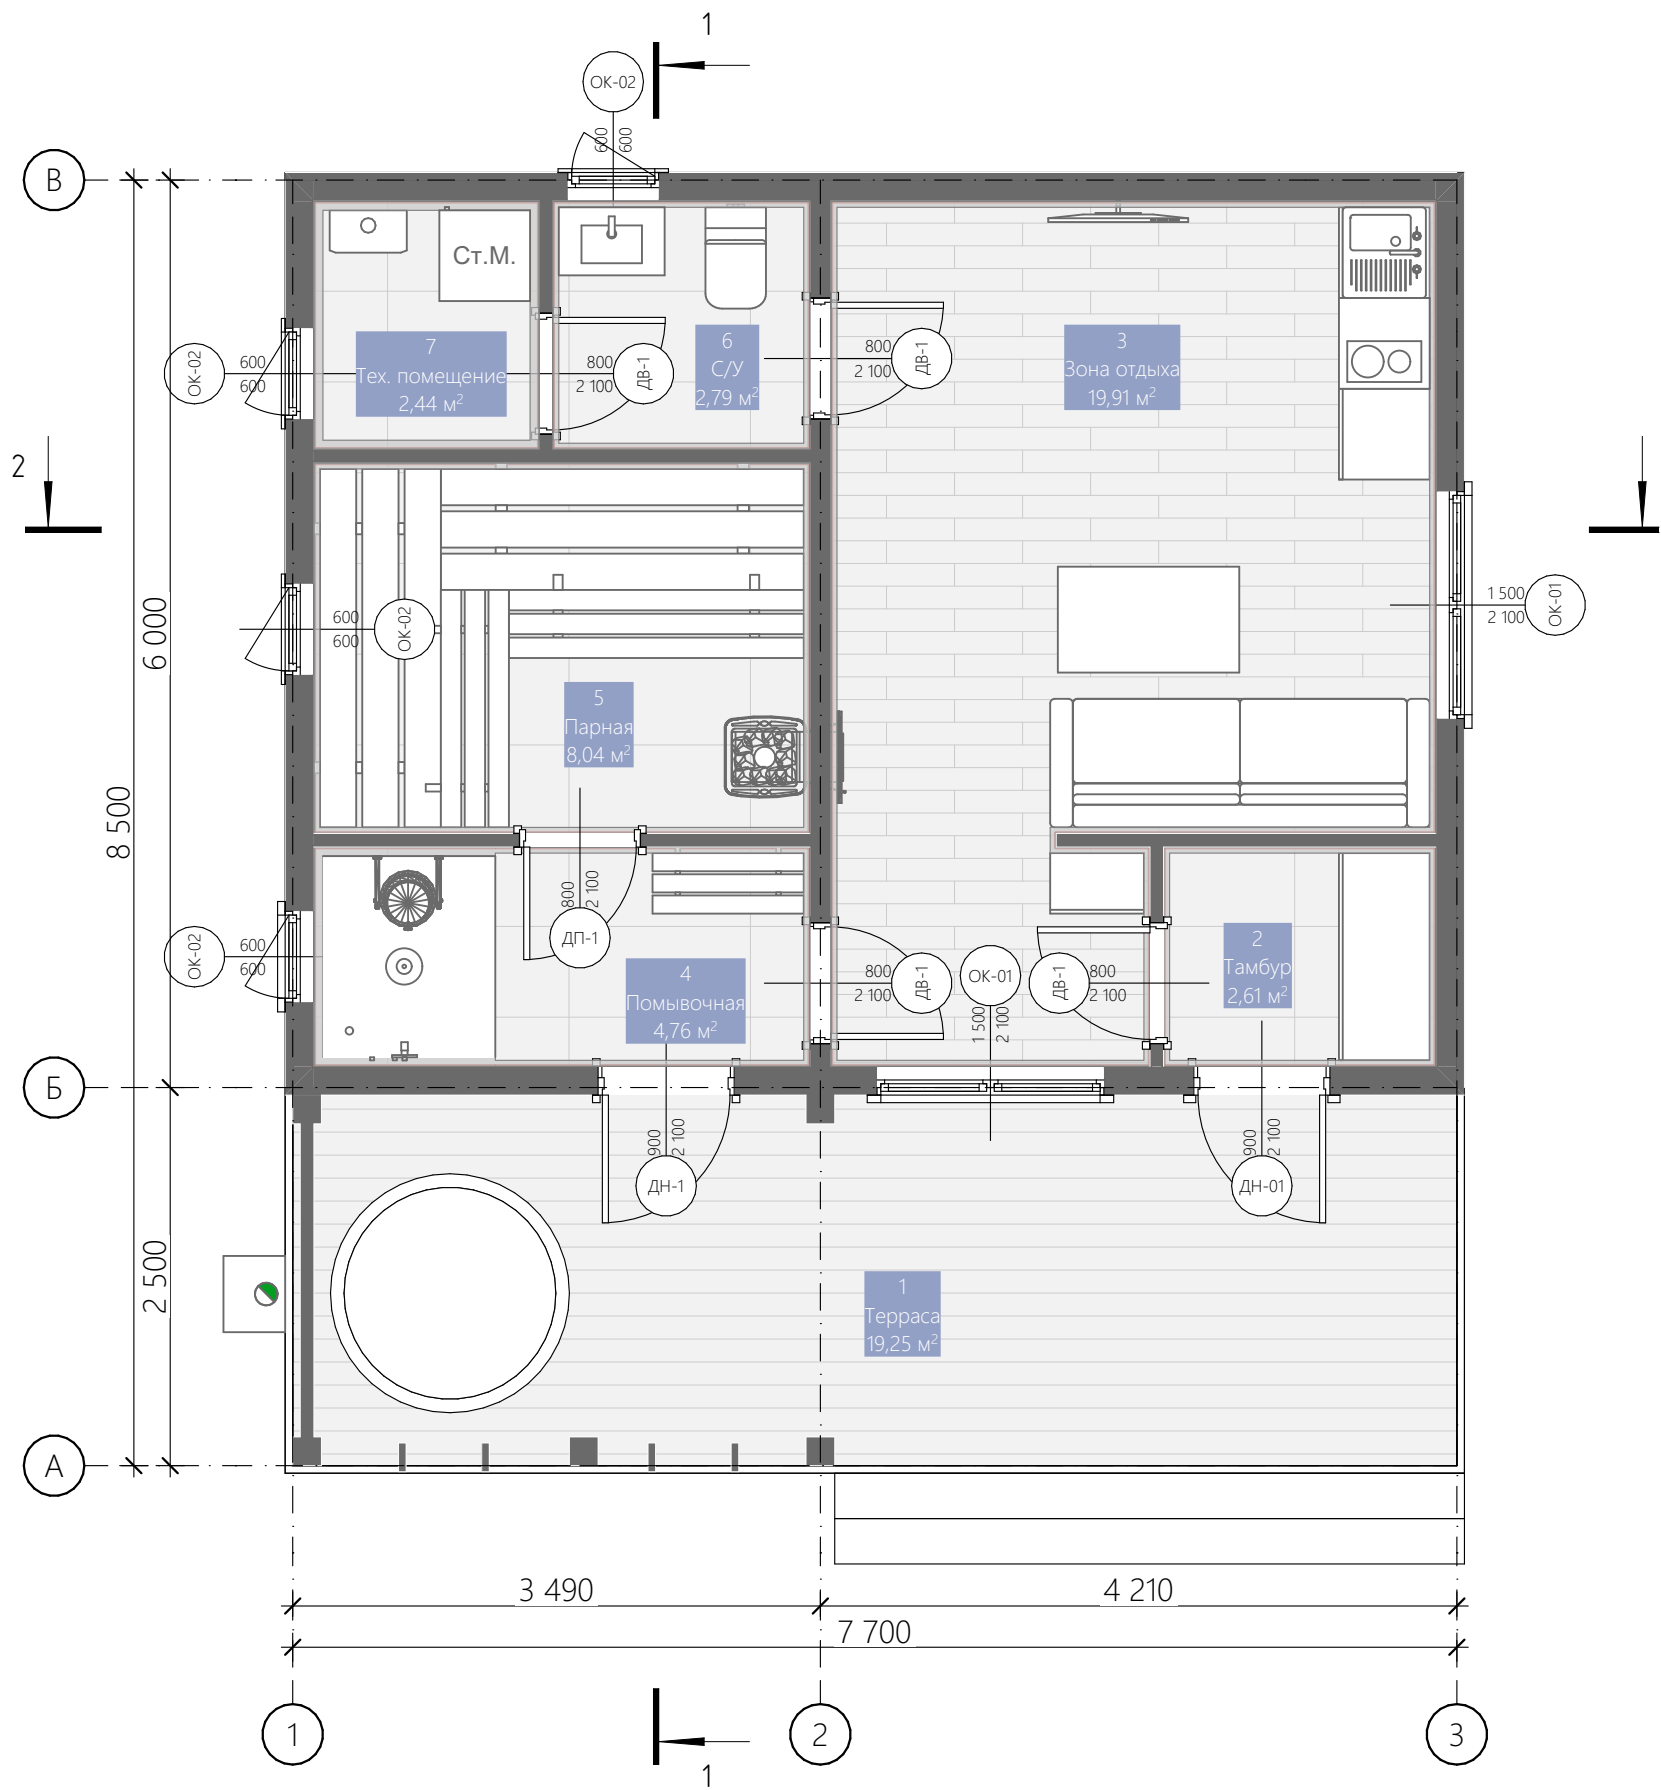

Экспликация помещений		
№	Наименование	Площадь, кв. м.
1	Терраса	19,25
2	Тамбур	2,61
3	Зона отдыха	19,91
4	Помывочная	4,76
5	Парная	8,04
6	С/У	2,79
7	Тех. помещение	2,44
		59,80 м²
Наименование		Площадь, кв. м.
Площадь застройки		65,45
Примечание:		
1. Вся индивидуальная мебель выполняется по отдельному проекту с детальной проработкой и калькуляцией. Чертежи предоставляет фирма-изготовитель столярных изделий.		
2. Данный проект отдельно согласовывается с автором проекта и непосредственно с заказчиком.		
3. Цветовое решение фасада и материалов отделки показаны в проекте приблизительно.		
4. Количество ступеней показано условно.		
#Название Организации		Лист
		4


Согласовано				
И-нв. № подл.	Подп. и дата	Взам. инв. №		

Лист	Изм.	№ Докум.	Подп.	Дата

Адрес:

Размерный план

1:50

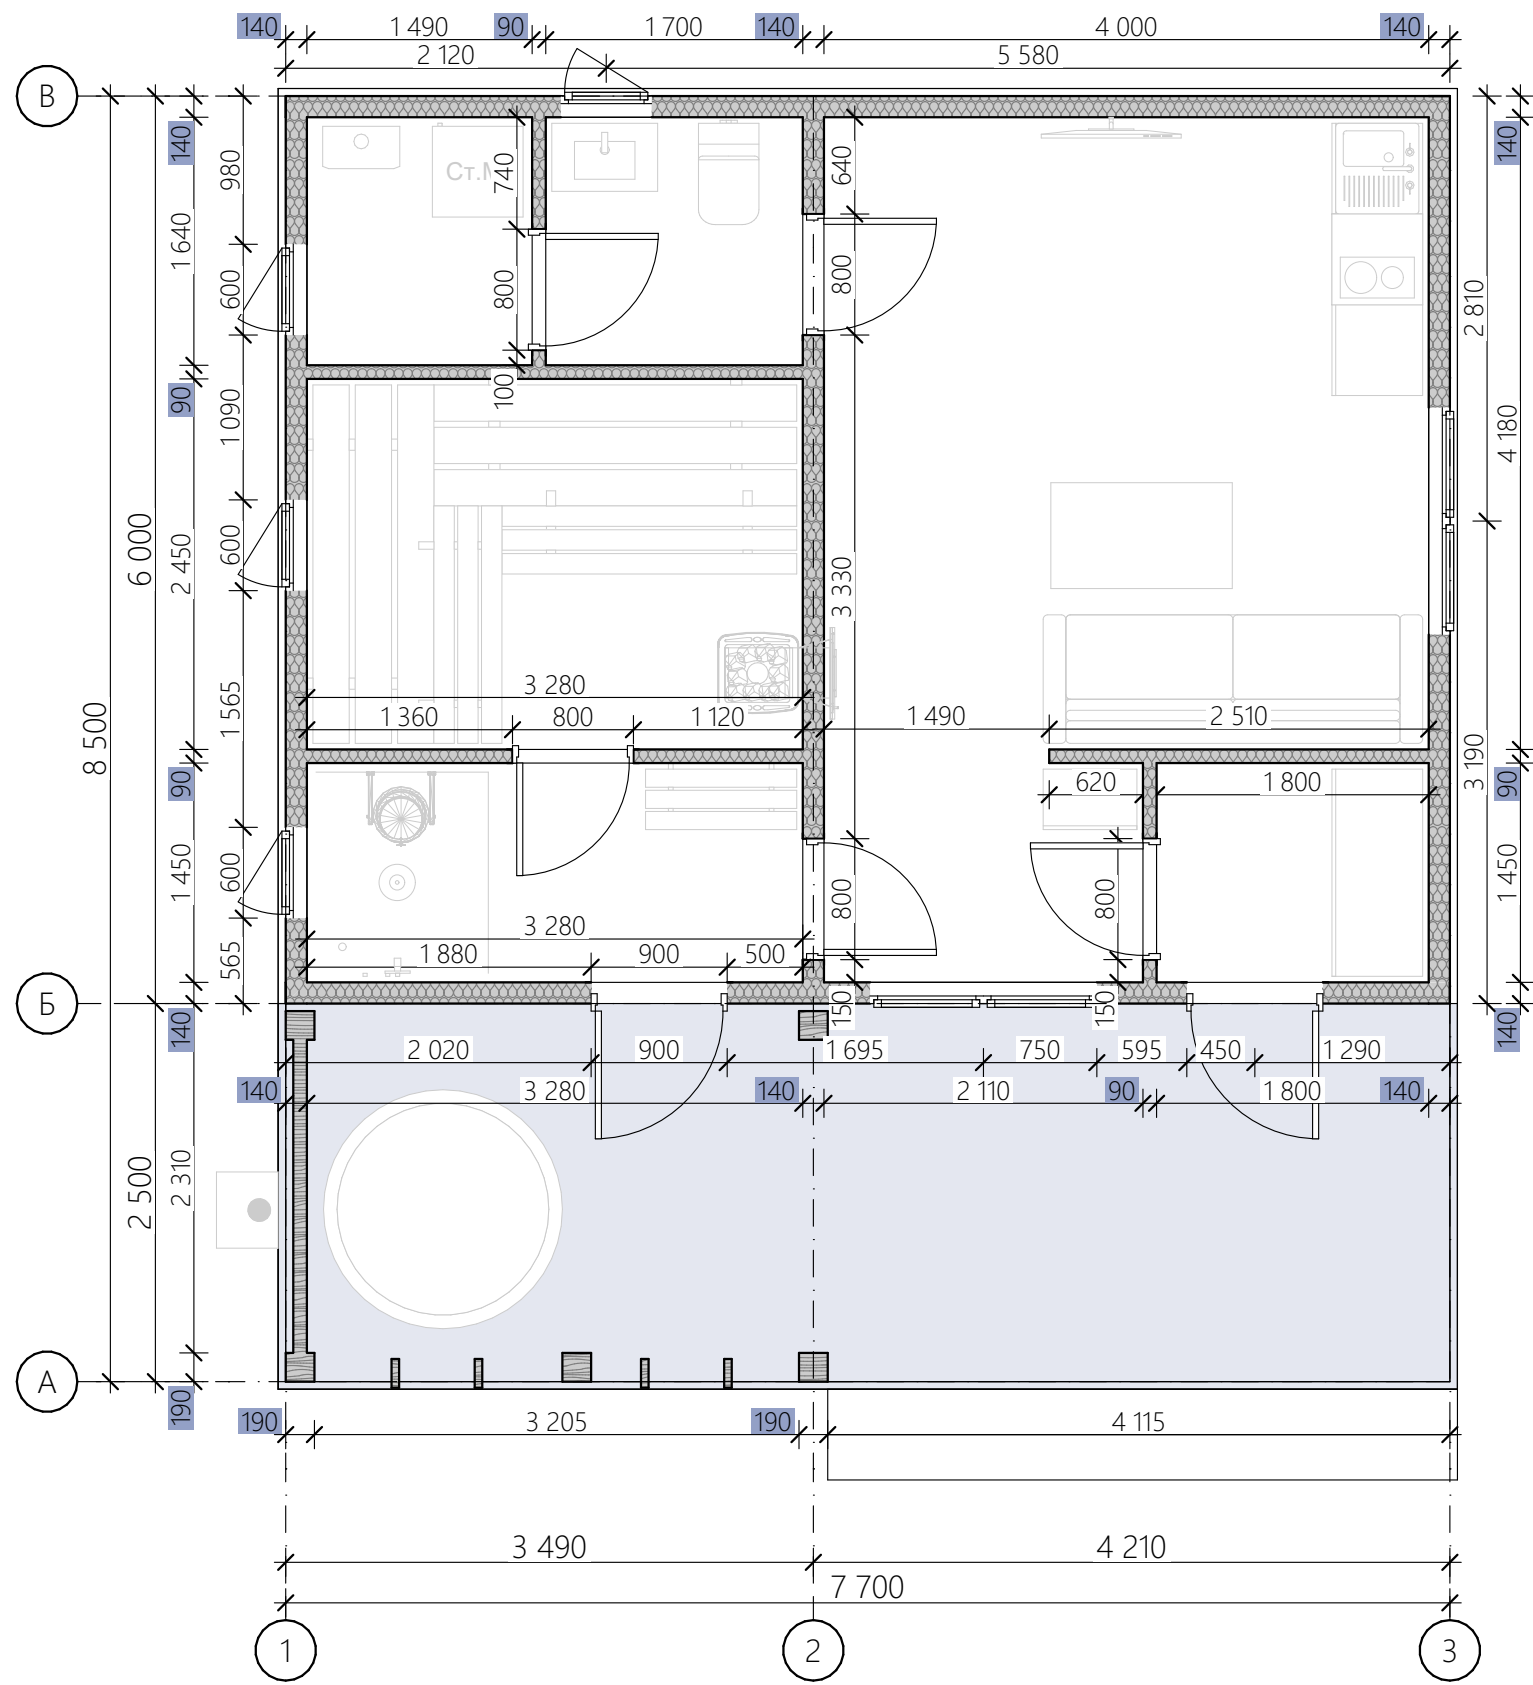

Согласовано				
И-нв. № подл.	Подп. и дата	Взам. инв. №		


Лист	Изм.	№ Докум.	Подп.	Дата

Адрес: _____

Размерный план

Примечание:
1. Представленные размеры
указаны без учета внешней и
внутренней отделки

1:50

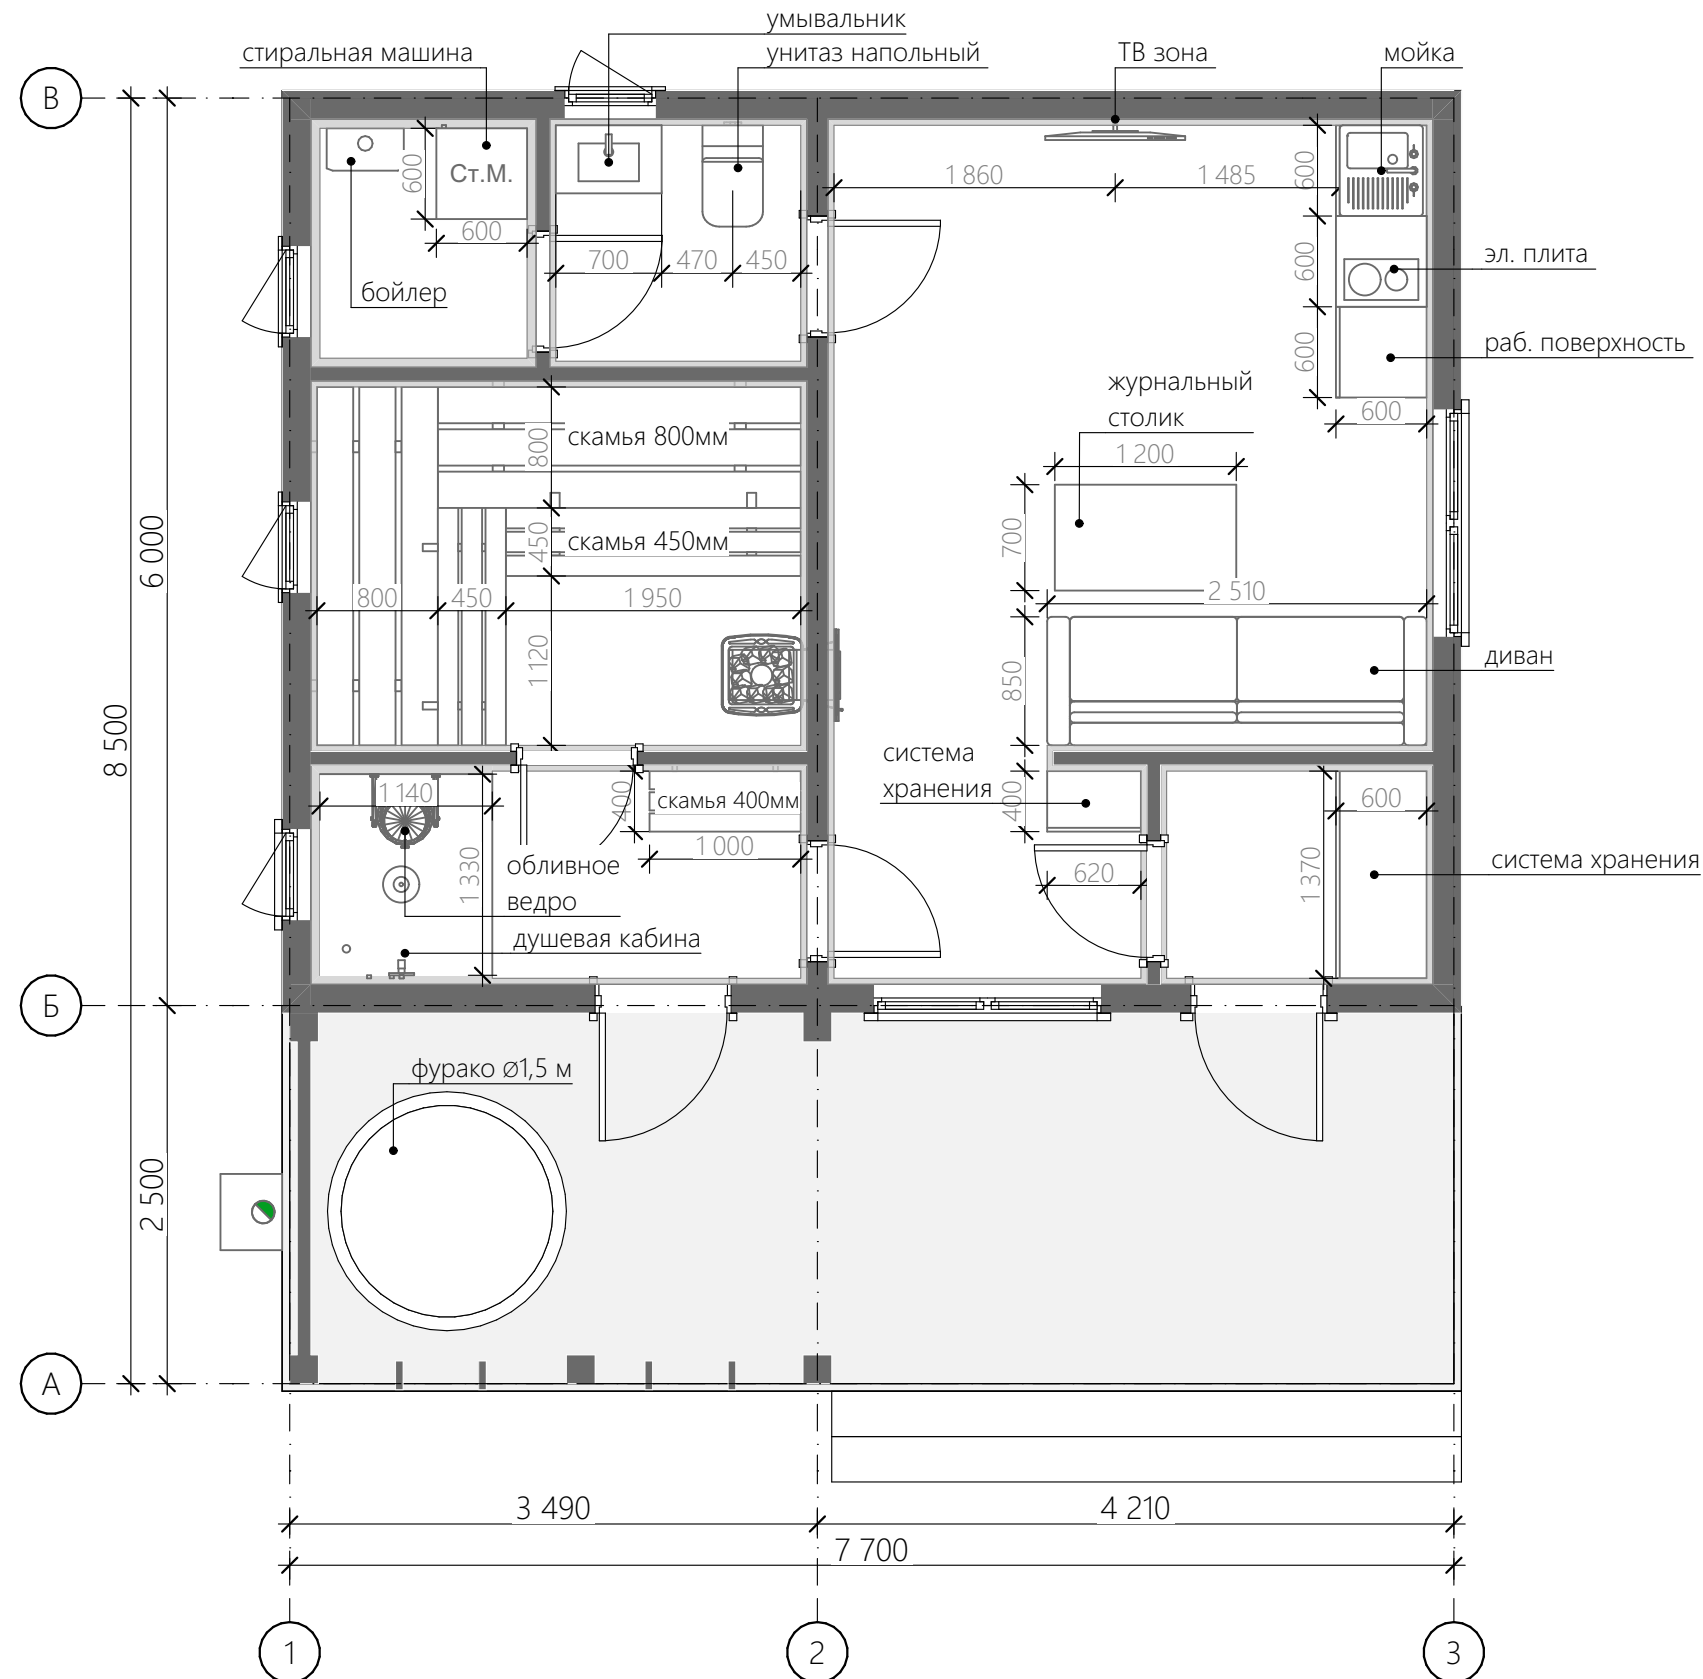

2. Финальные размеры мебели и оборудования указаны ориентировочно — для точной компоновки требуется разработка дизайн-проекта.

Инов. № подл.	Подп. и дата	Взам. инв. №	Согласовано		

Лист	Изм.	№ Докум.	Подп.	Дата

Адрес:

План расстановки мебели и оборудования

#Название Организации

6

Согласовано

Взам. инв. №

Подп. и дата


Инв. № подл.

Лист	Изм.	№ Докум.	Подп.	Дата

Адрес:


Зд-разрез

#Название Организации

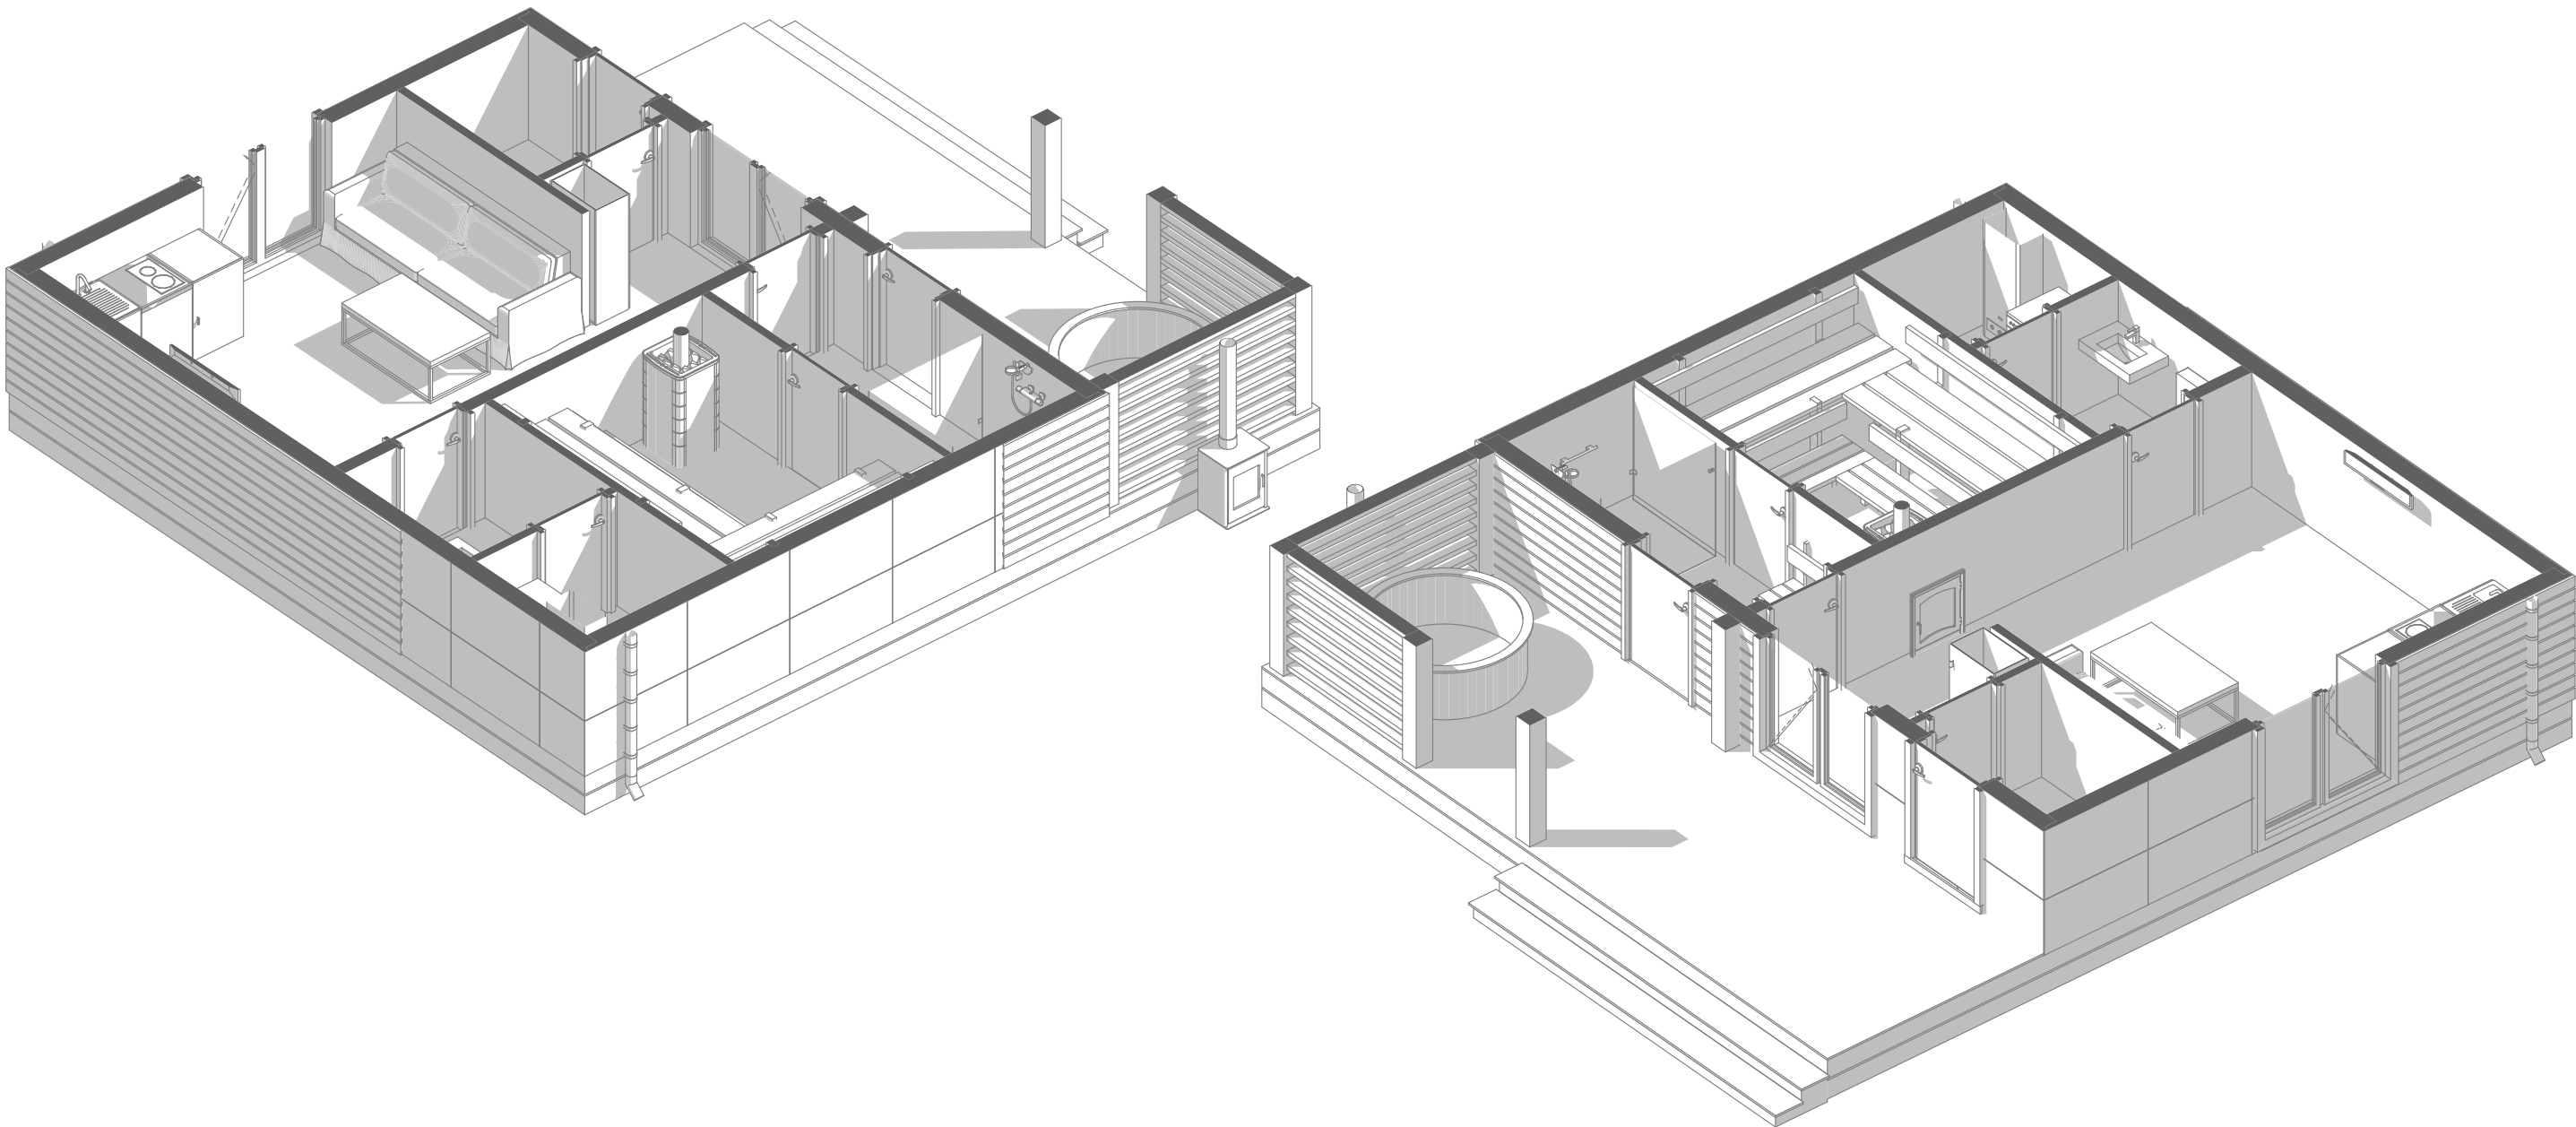


План тёплого водяного пола

1:50

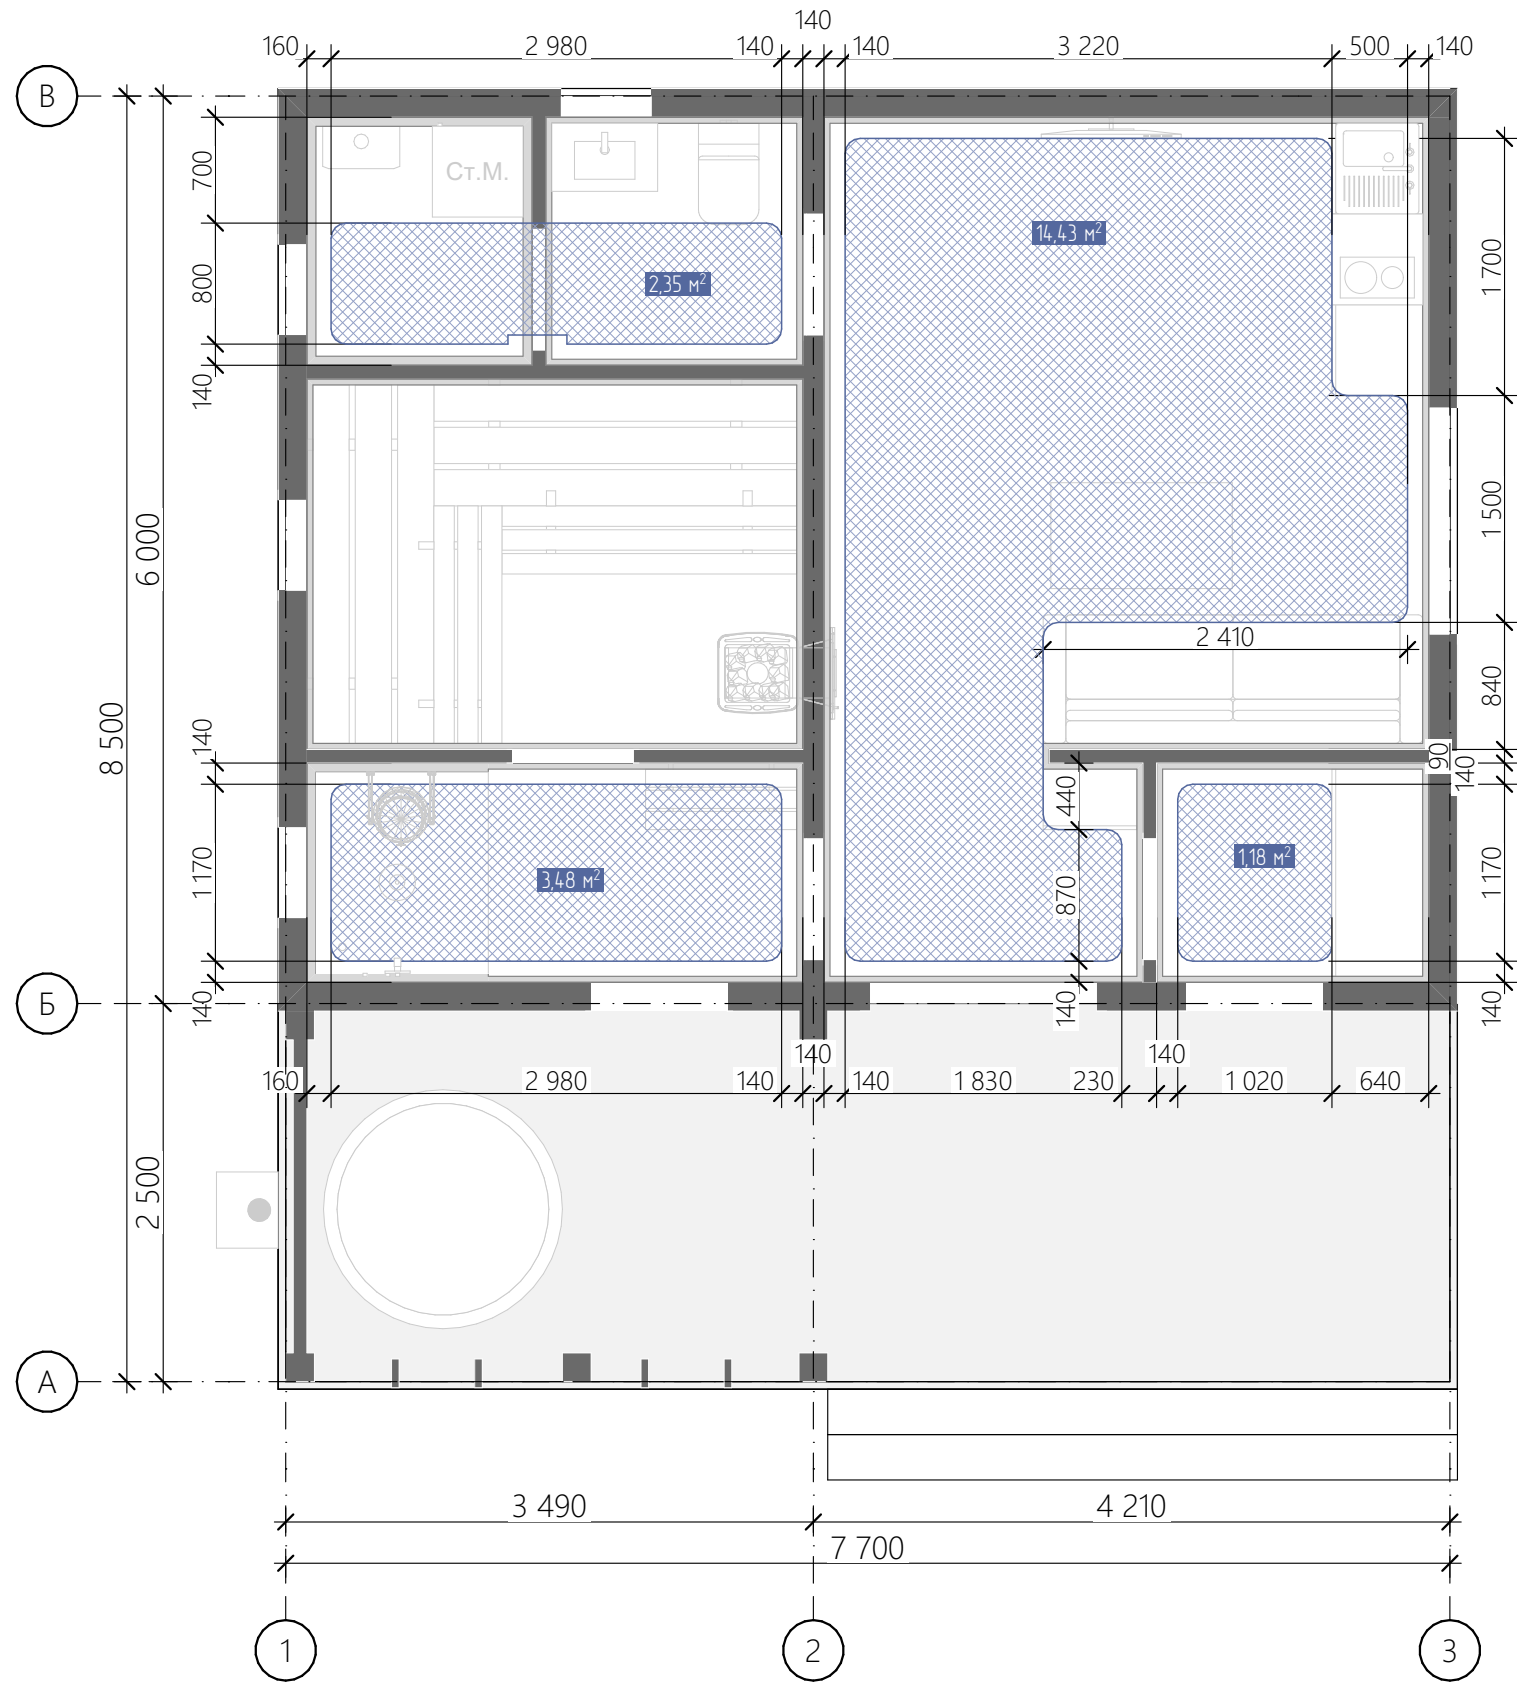

Условные обозначения

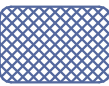 - Контур устройства
теплого пола

Экспликация теплого пола

Наименование зоны	Площадь, м2
Помывочная	3,48
Комната отдыха	14,43
С/У	2,35
Тамбур	1,18
21,44 м²	

Примечание:

1. Отображение носит схематичный характер. Фактическая реализация выполняется в соответствии с детальными проектными решениями инженерных сетей.

Согласовано				
И-нв. № подл.	Подп. и дата	Взам. инв. №		


Лист	Изм.	№ Докум.	Подп.	Дата

Адрес:

План водяного теплого пола

#Название Организации

Условные обозначения

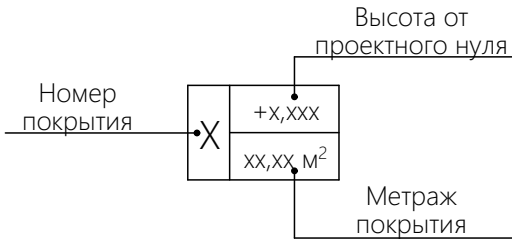


Ведомость покрытий пола

№	Наименование	м2
1	ДПК- террасная доска	19,07
2	ламинат	19,91
3	керамогранит	20,64

Примечание:

1. Приведённые цветовые решения носят рекомендательный характер. Фактический подбор оттенков и материалов выполняется на этапе реализации с учётом наличия продукции у поставщиков и утверждения заказчиком.

2. Пирог покрытия смотреть на след. листе.

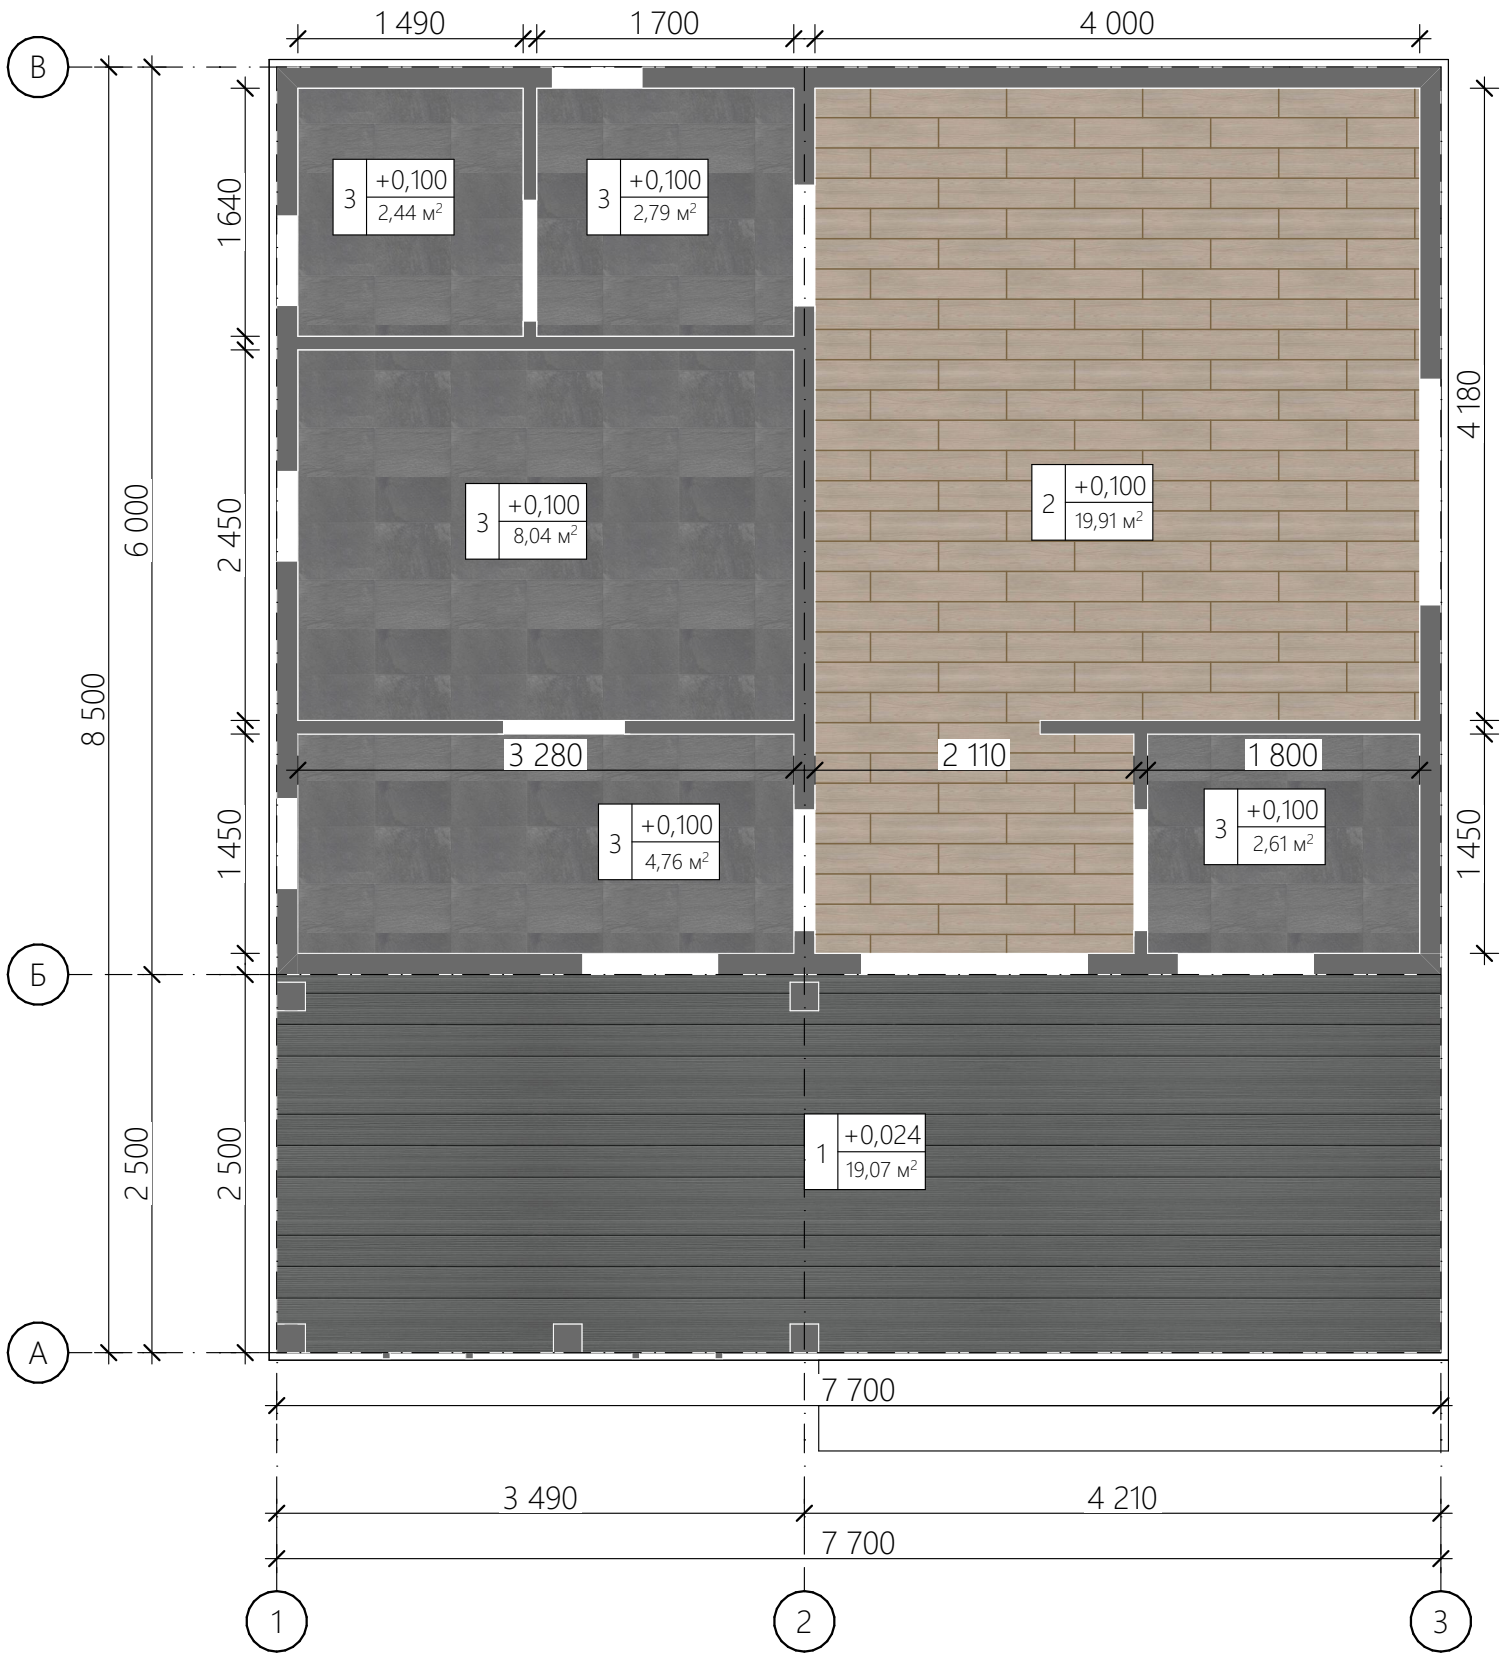

Согласовано				
Инва. № подл.	Подп. и дата	Взам. инв. №		




Лист	Изм.	№ Докум.	Подп.	Дата

Адрес:

План покрытий пола

#Название Организации

Экспликация покрытий пола

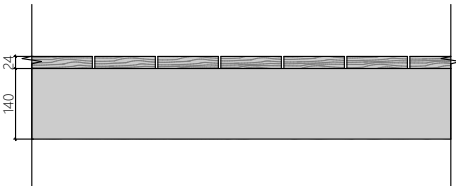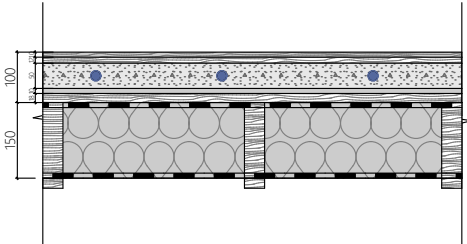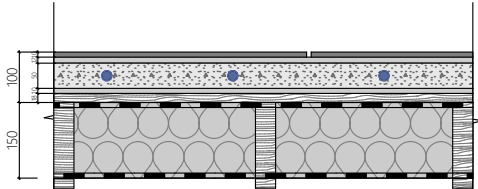№	Наименование	Разрез	Состав
1	Террасная доска		-Террасная доска 24мм -Лага, доска 140х45мм 140 мм
2	Ламинат		-Ламинат 10мм -Подложка под ламинат 10мм -Полусухая цементно-песчаная стяжка (с устройством теплого водяного пола) 50мм -ЦСП 10мм -ОСБ 18мм
3	Керамогранит		-Керамогранит 10мм -Клей 10мм -Полусухая цементно-песчаная стяжка (с устройством теплого водяного пола) 50мм -ЦСП 10мм -ОСБ 18мм


Согласовано				

Индв. № подл.	Подп. и дата	Взам. инв. №

Лист	Изм.	№ Докум.	Подп.	Дата	Экспликация покрытий пола	#Название Организации	Лист
							10

План отделки стен

1:50

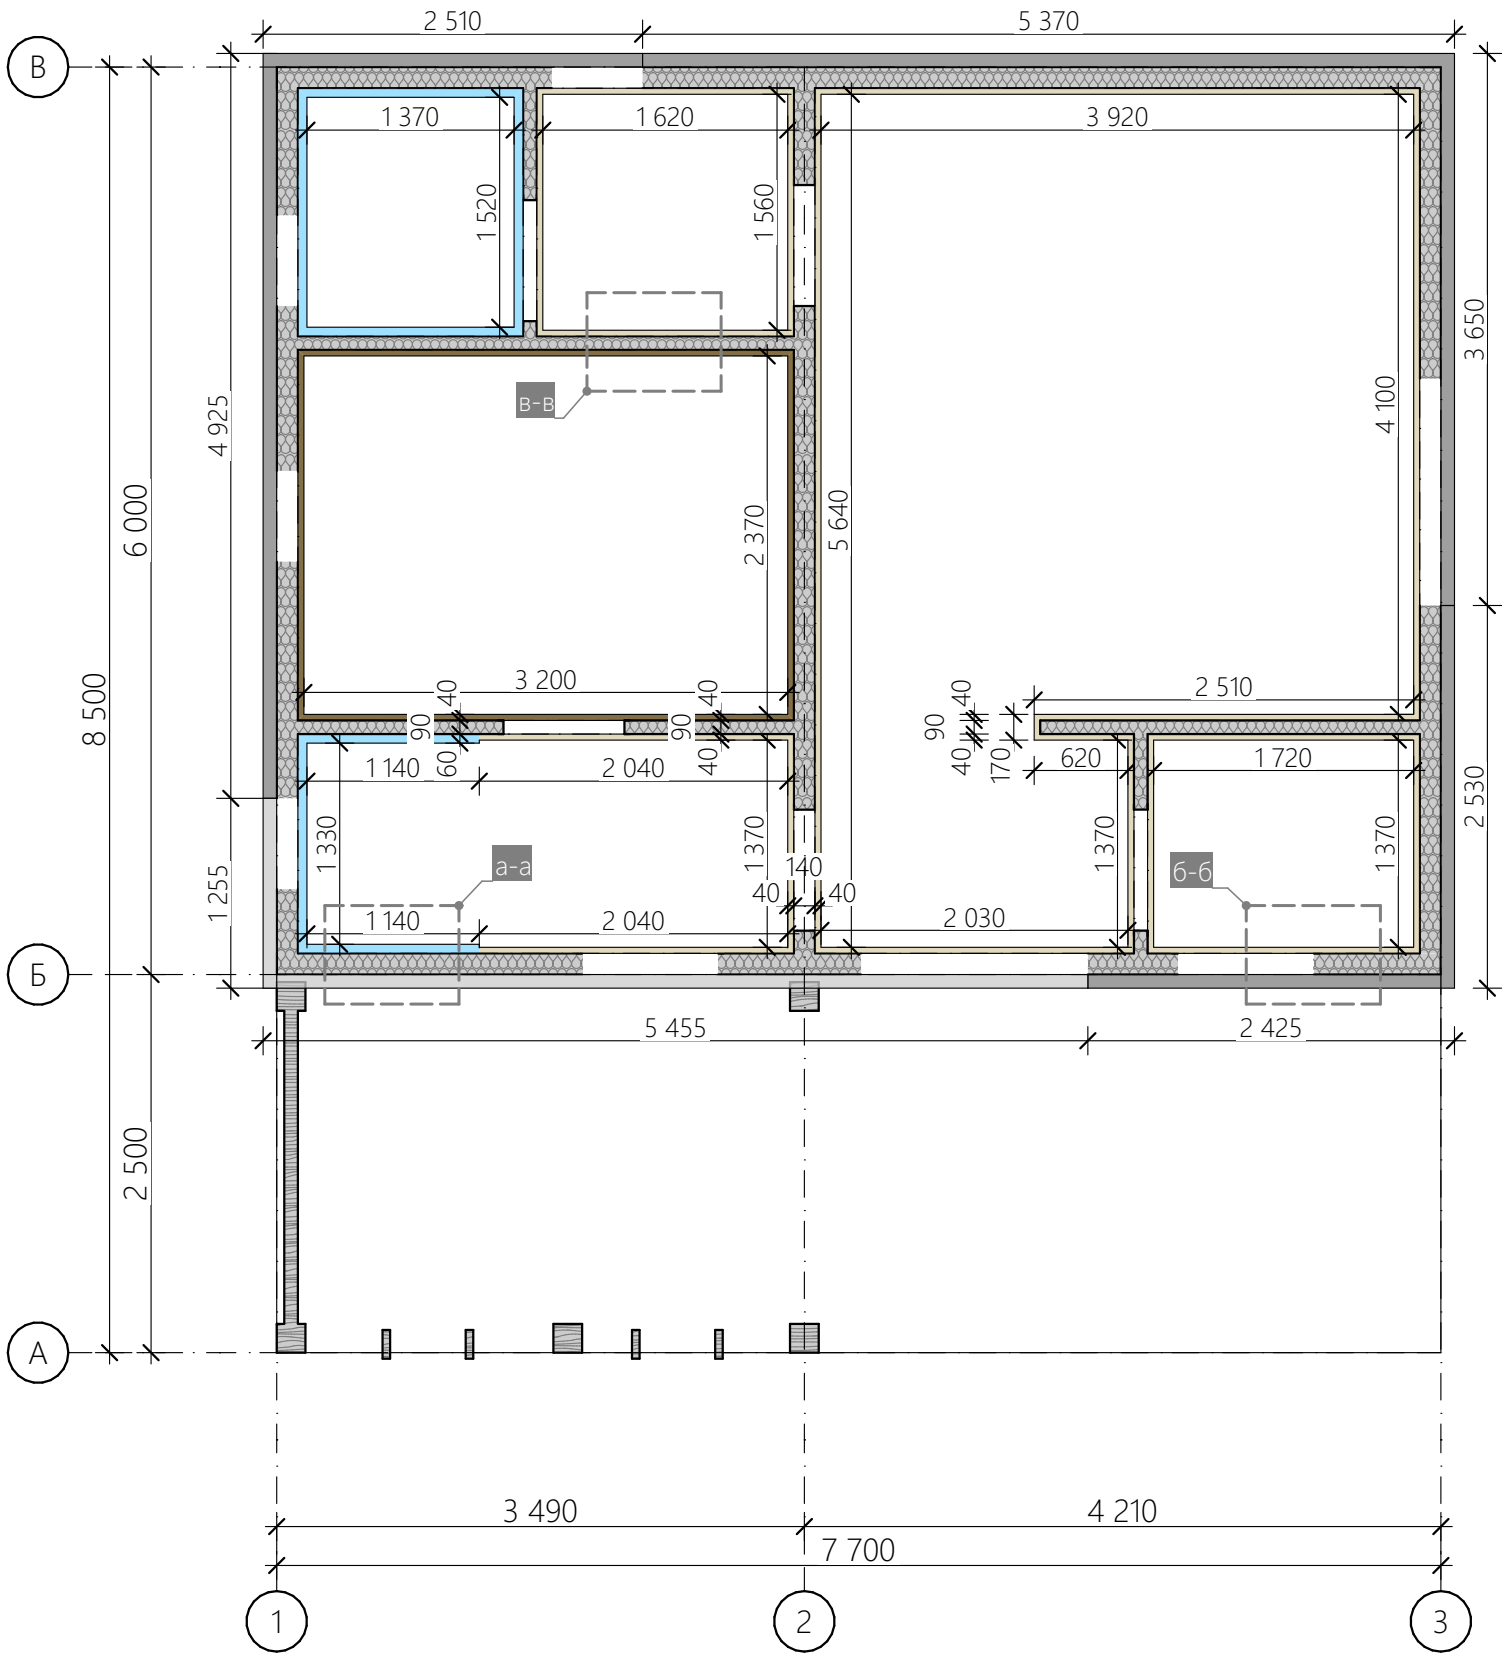

Ведомость покрытий стен

№	Наименование	Условное обозначение
1	Планкен (20мм)	
2	Гибкая керамика (Фоми)	
3	Имитация бруса (20мм)	
4	Вагонка (16мм)	
5	Керамогранит (10мм)	

Примечание:
1. Сечение по стенам смотреть на след. листе

Согласовано				
И-нв. № подл.	Подп. и дата	Взам. инв. №		

Лист	Изм.	№ Докум.	Подп.	Дата

Адрес:

План покрытия отделки стен

#Название Организации


Экспликация отделки стен

№ разреза

Сечение


Состав

а-а

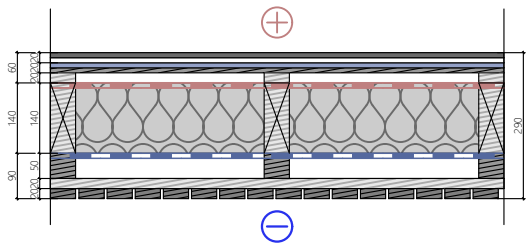


-Керамогранит	10мм
-Клей	10мм
-Рупанель	10мм
-ОСБ	9мм
-Обрешётка	20мм
-Пароизоляционная мембрана	-
-Стойка каркаса (утеплённая)	140мм
-Гидро-ветрозащитная мембрана	-
-Вентбрусok (вертикально)	50мм
-Обрешётка по стойкам	20мм
-Планкен	20мм

б-б

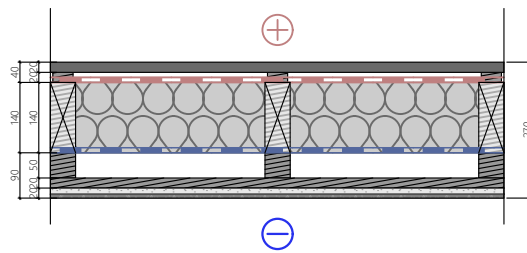

-Имитация бруса	20мм
-Вентбрусok (вертикально)	20мм
-Пароизоляционная мембрана	-
-Стойка каркаса (утепленная)	140мм
-Гидро-ветрозащитная мембрана	-
-Вентбрусok (вертикально)	50мм
-Обрешётка	20мм
-ЦСП	12мм
-Гибкая керамика	8мм

в-в

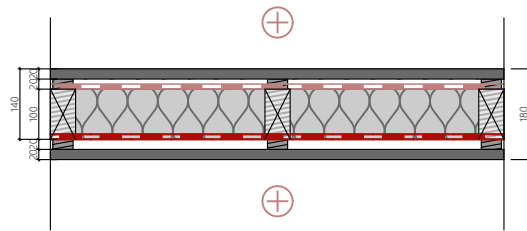

-Имитация бруса	20мм
-Вентбрусok (вертикально)	50мм
-Пароизоляционная мембрана	-
-Стойка каркаса (утепленная)	90мм
-Пароизоляционная мембрана (алюминиевая фольга)	-
-Вентбрусok (вертикально)	50мм
-Имитация бруса	20мм

Согласовано

Взам. инв. №

Подп. и дата

Инв. № подл.

Лист	Изм.	№ Докум.	Подп.	Дата

Экспликация отделки стен

#Название Организации

Лист


12

План расстановки розеток

1:50

Условные обозначения:

-  - розетка 220V с заземлением
-  - розетка 220V с заземлением и влагозащитой
-  - розетка для ТВ
-  - интернет - розетка
-  - электровывод

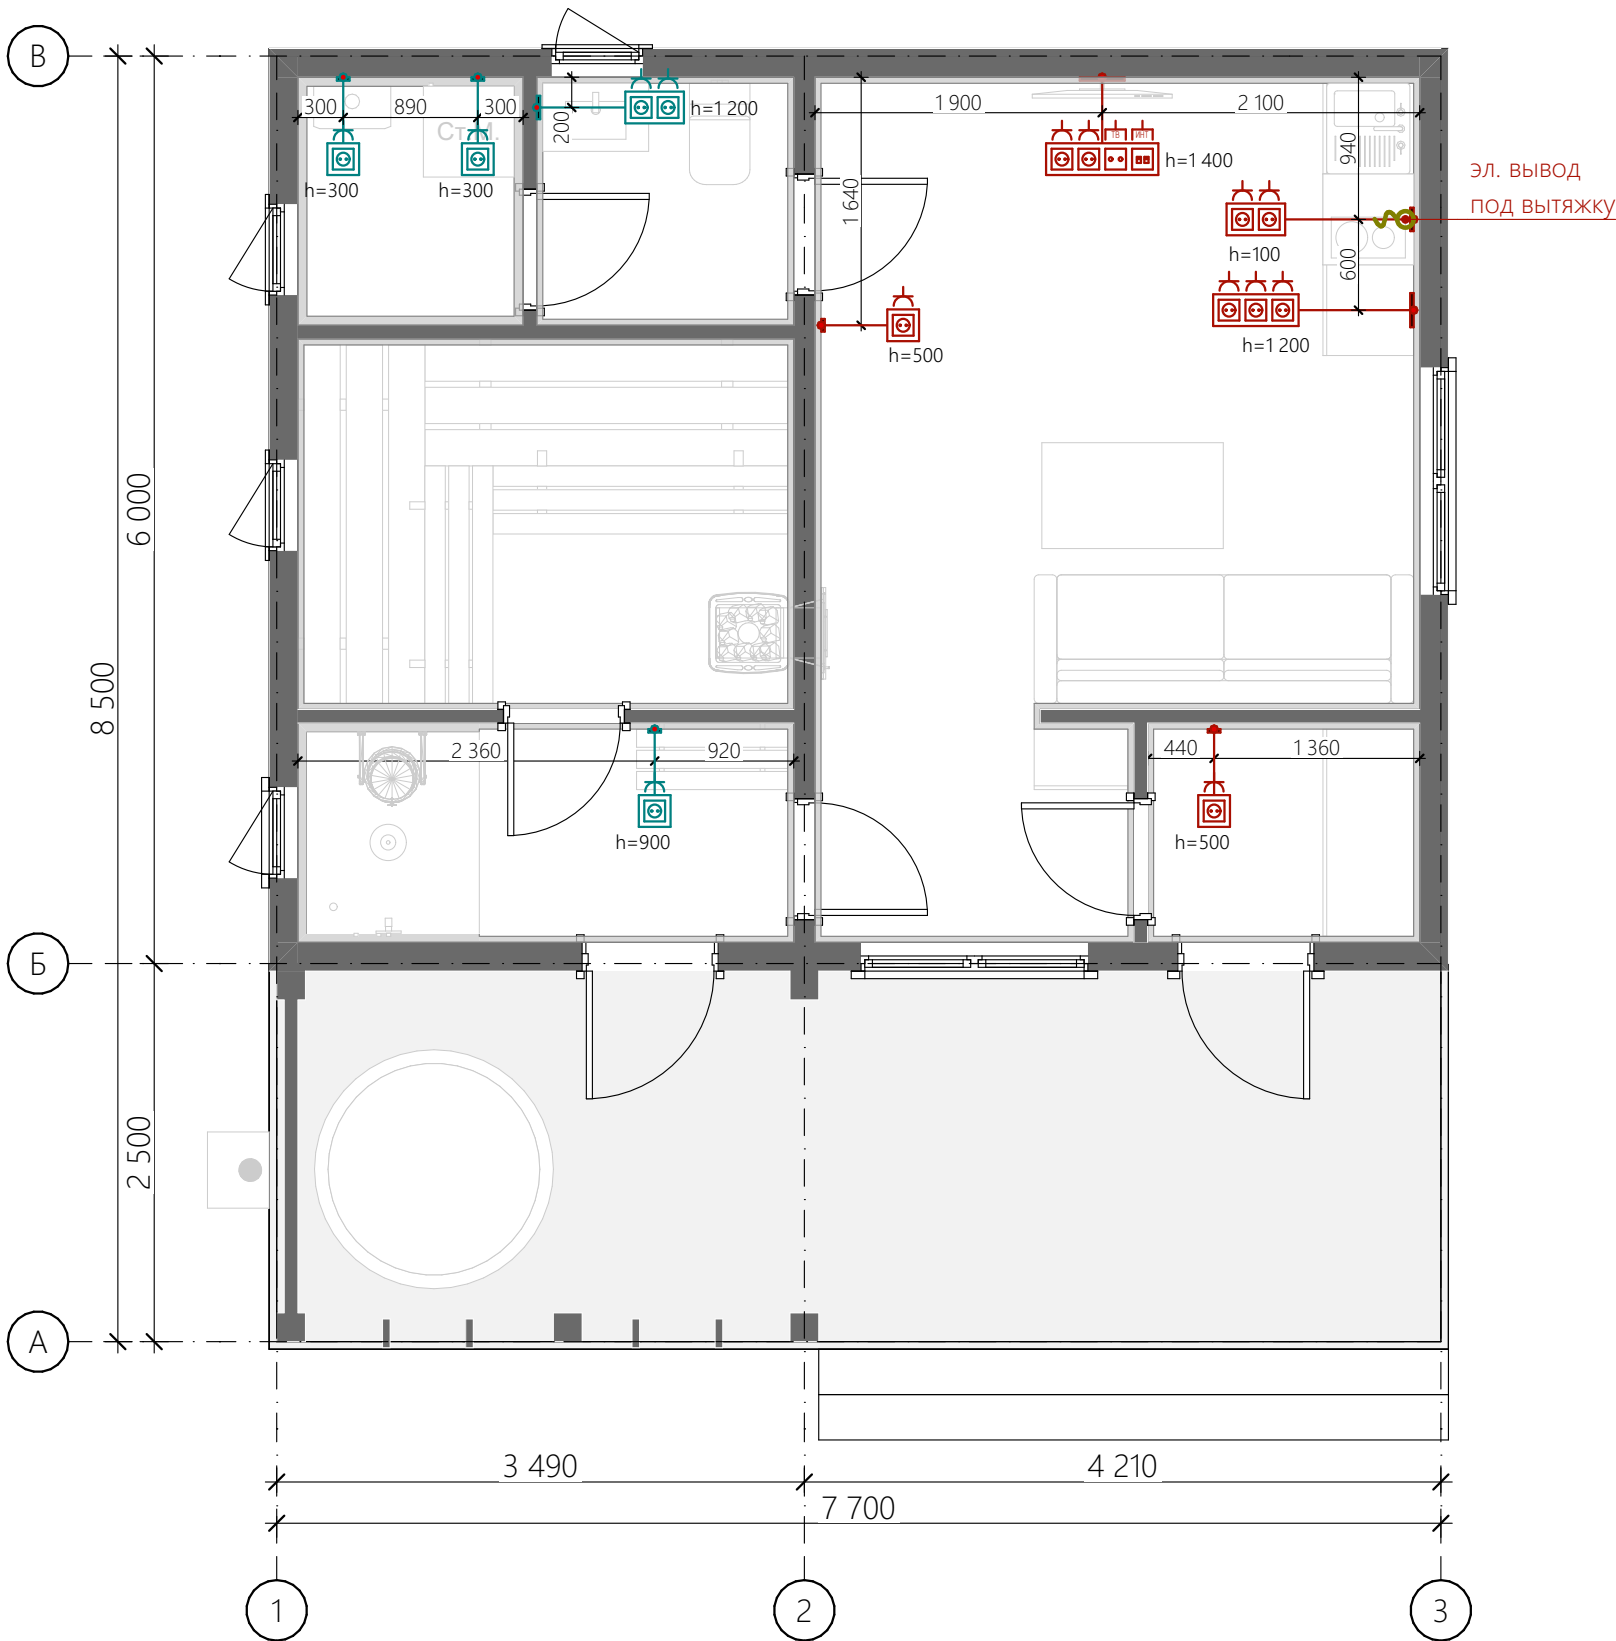

Примечание:

1. Схема размещения розеток является рекомендательной и требует согласования с заказчиком по месту.
2. Все высоты даны от чистового пола.
3. Все указанные размеры даются до центра позиций.
4. Отметки розеток, выключателей, выводов и др. оборудования, являются предварительными и уточняются после выбора финишных материалов и мебели.
5. Размеры уточняются дополнительно

Согласовано				
Взам. инв. №				
Подп. и дата				
Инв. № подл.				


Лист	Изм.	№ Докум.	Подп.	Дата

Адрес:

План размещения розеток
стен

#Название Организации

-  - выключатель одноклавишный
-  - выключатель двухклавишный
-  - люстра
-  - точечный светильник
-  - настенные бра
-  - контурная подсветка
-  - трековый светильник

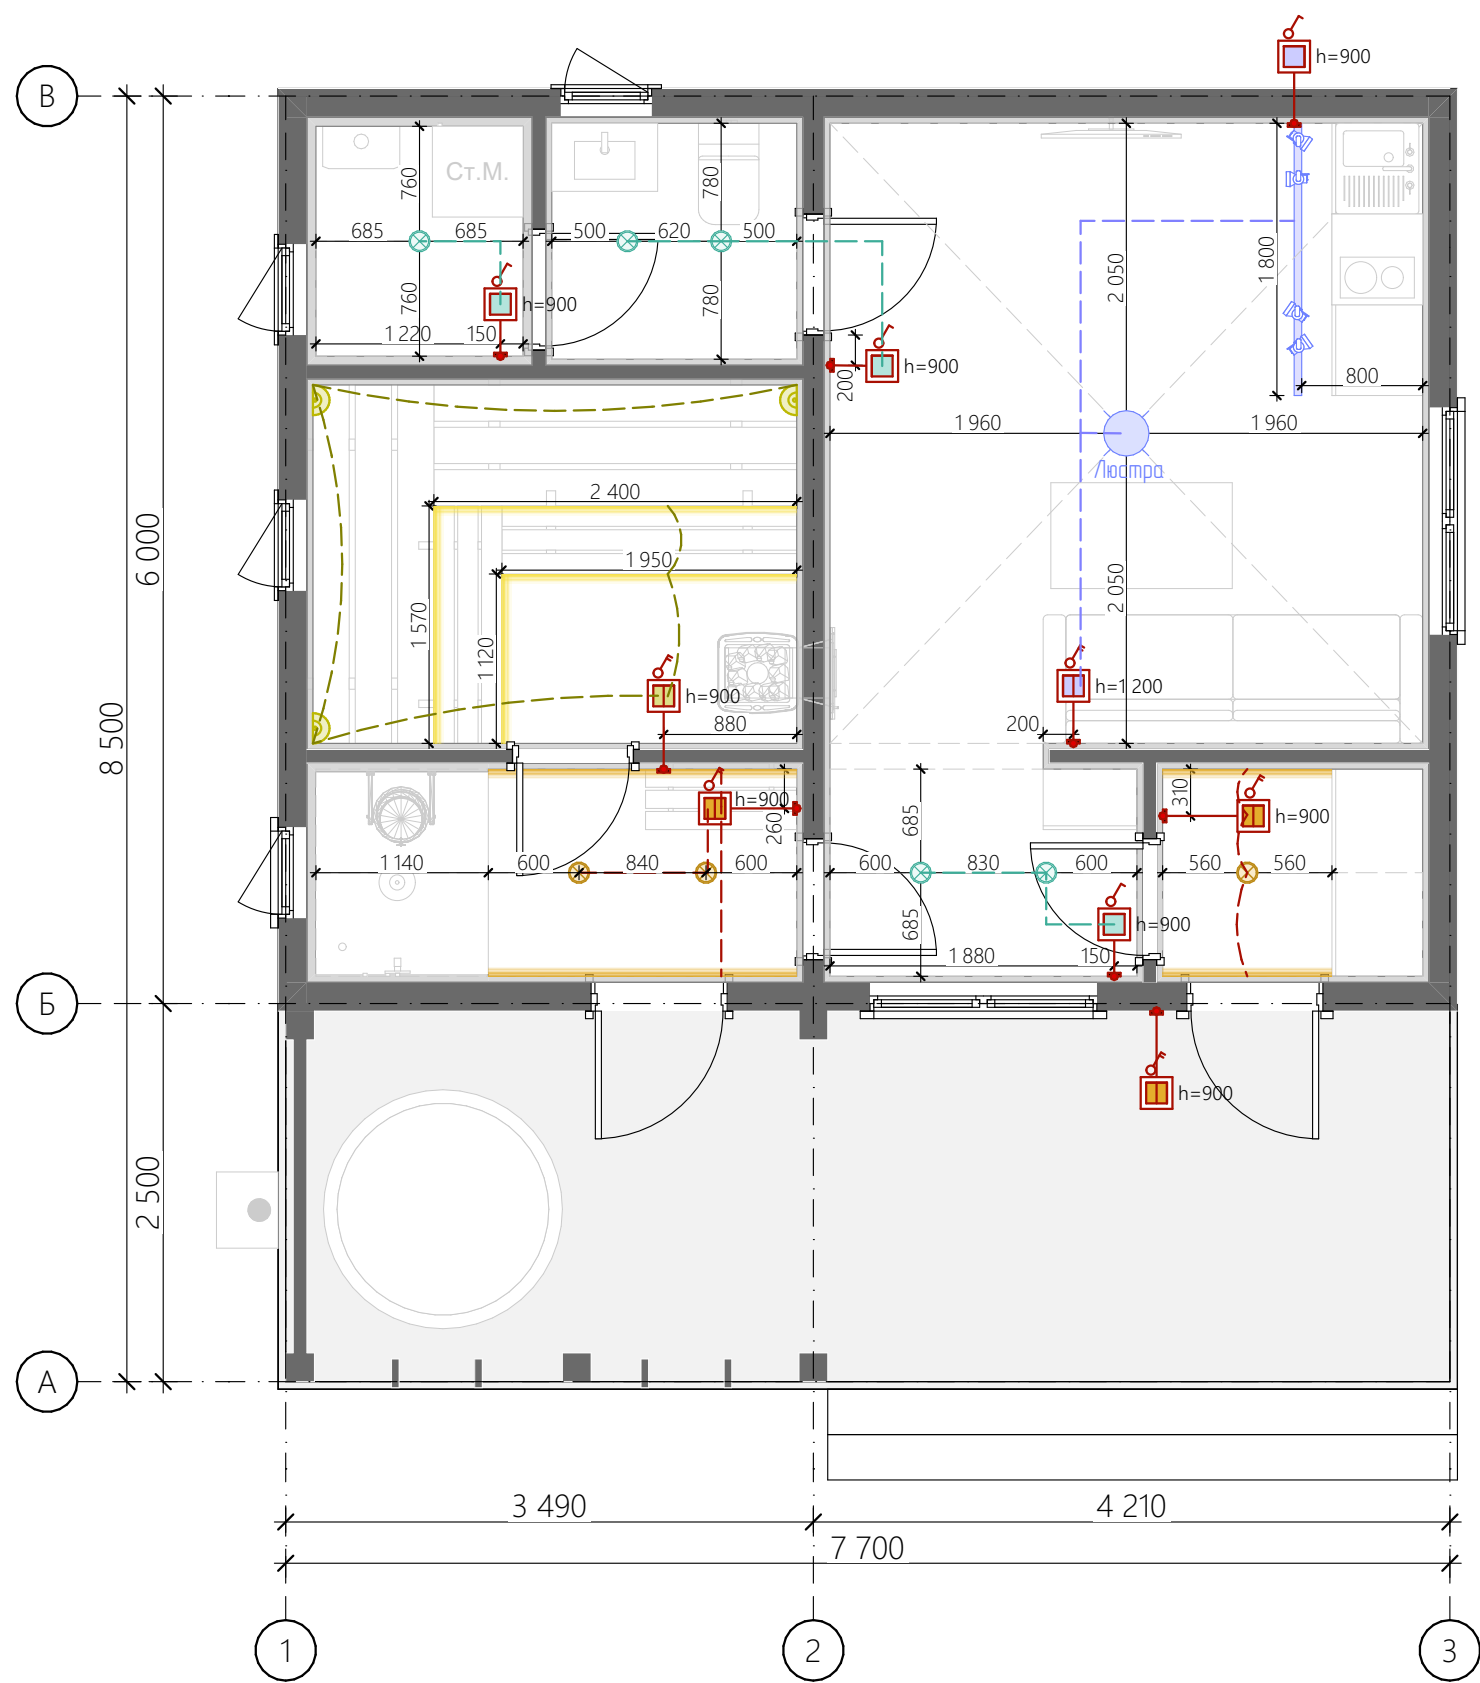

Примечание:

1. Схема размещения розеток является рекомендательной и требует согласования с заказчиком по месту.
2. Все высоты даны от чистового пола.
3. Все указанные размеры даются до центра позиций.
4. Отметки розеток, выключателей, выводов и др. оборудования, являются предварительными и уточняются после выбора финишных материалов и мебели.
5. Размеры уточняются дополнительно

Согласовано				
И.нв. № подл.	Взам. инв. №	Подп. и дата		


Лист	Изм.	№ Докум.	Подп.	Дата

Адрес:

План расстановки
светильников и
выключателей

План кровли


1:50

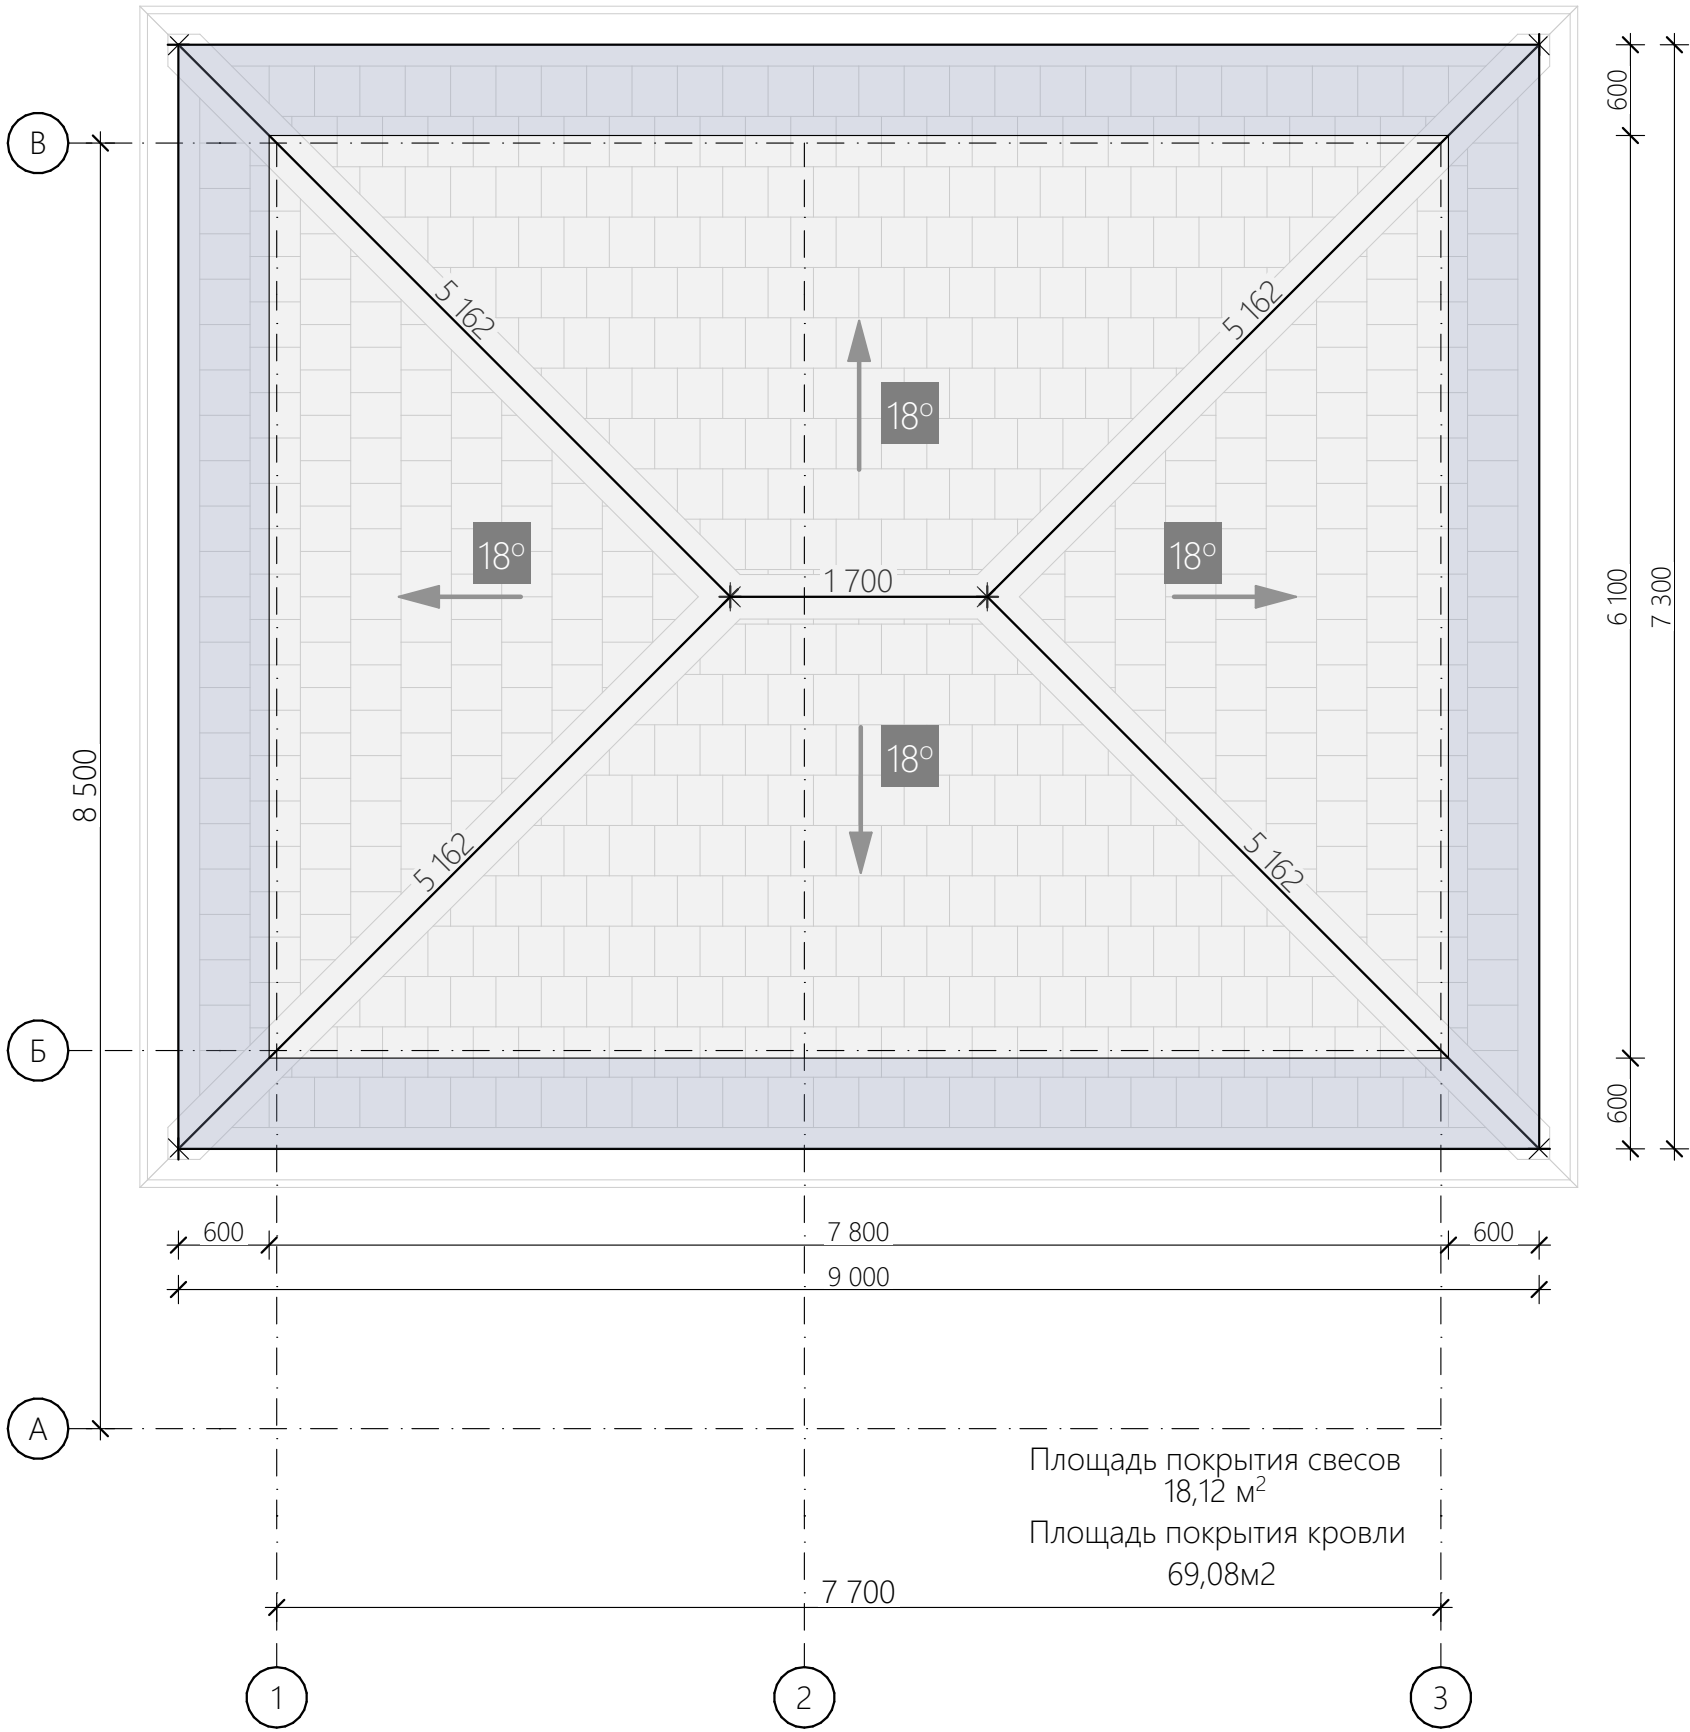

Условные обозначения:

- Кровля бани
- Подшив свесов бани

аксонометрия кровли:

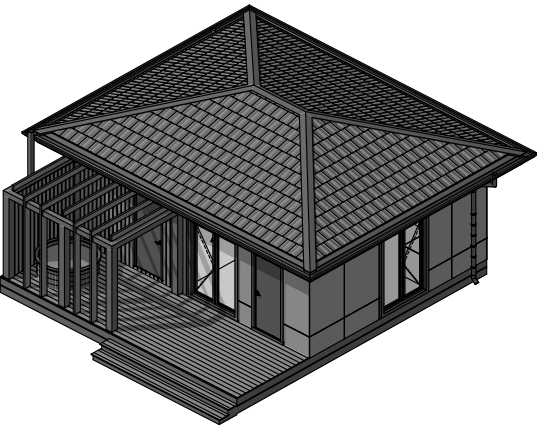

Согласовано				
И-нв. № подл.	Подп. и дата	Взам. инв. №		

Лист	Изм.	№ Докум.	Подп.	Дата


Адрес:

План кровли

#Название Организации

Разрез 1-1

1:40

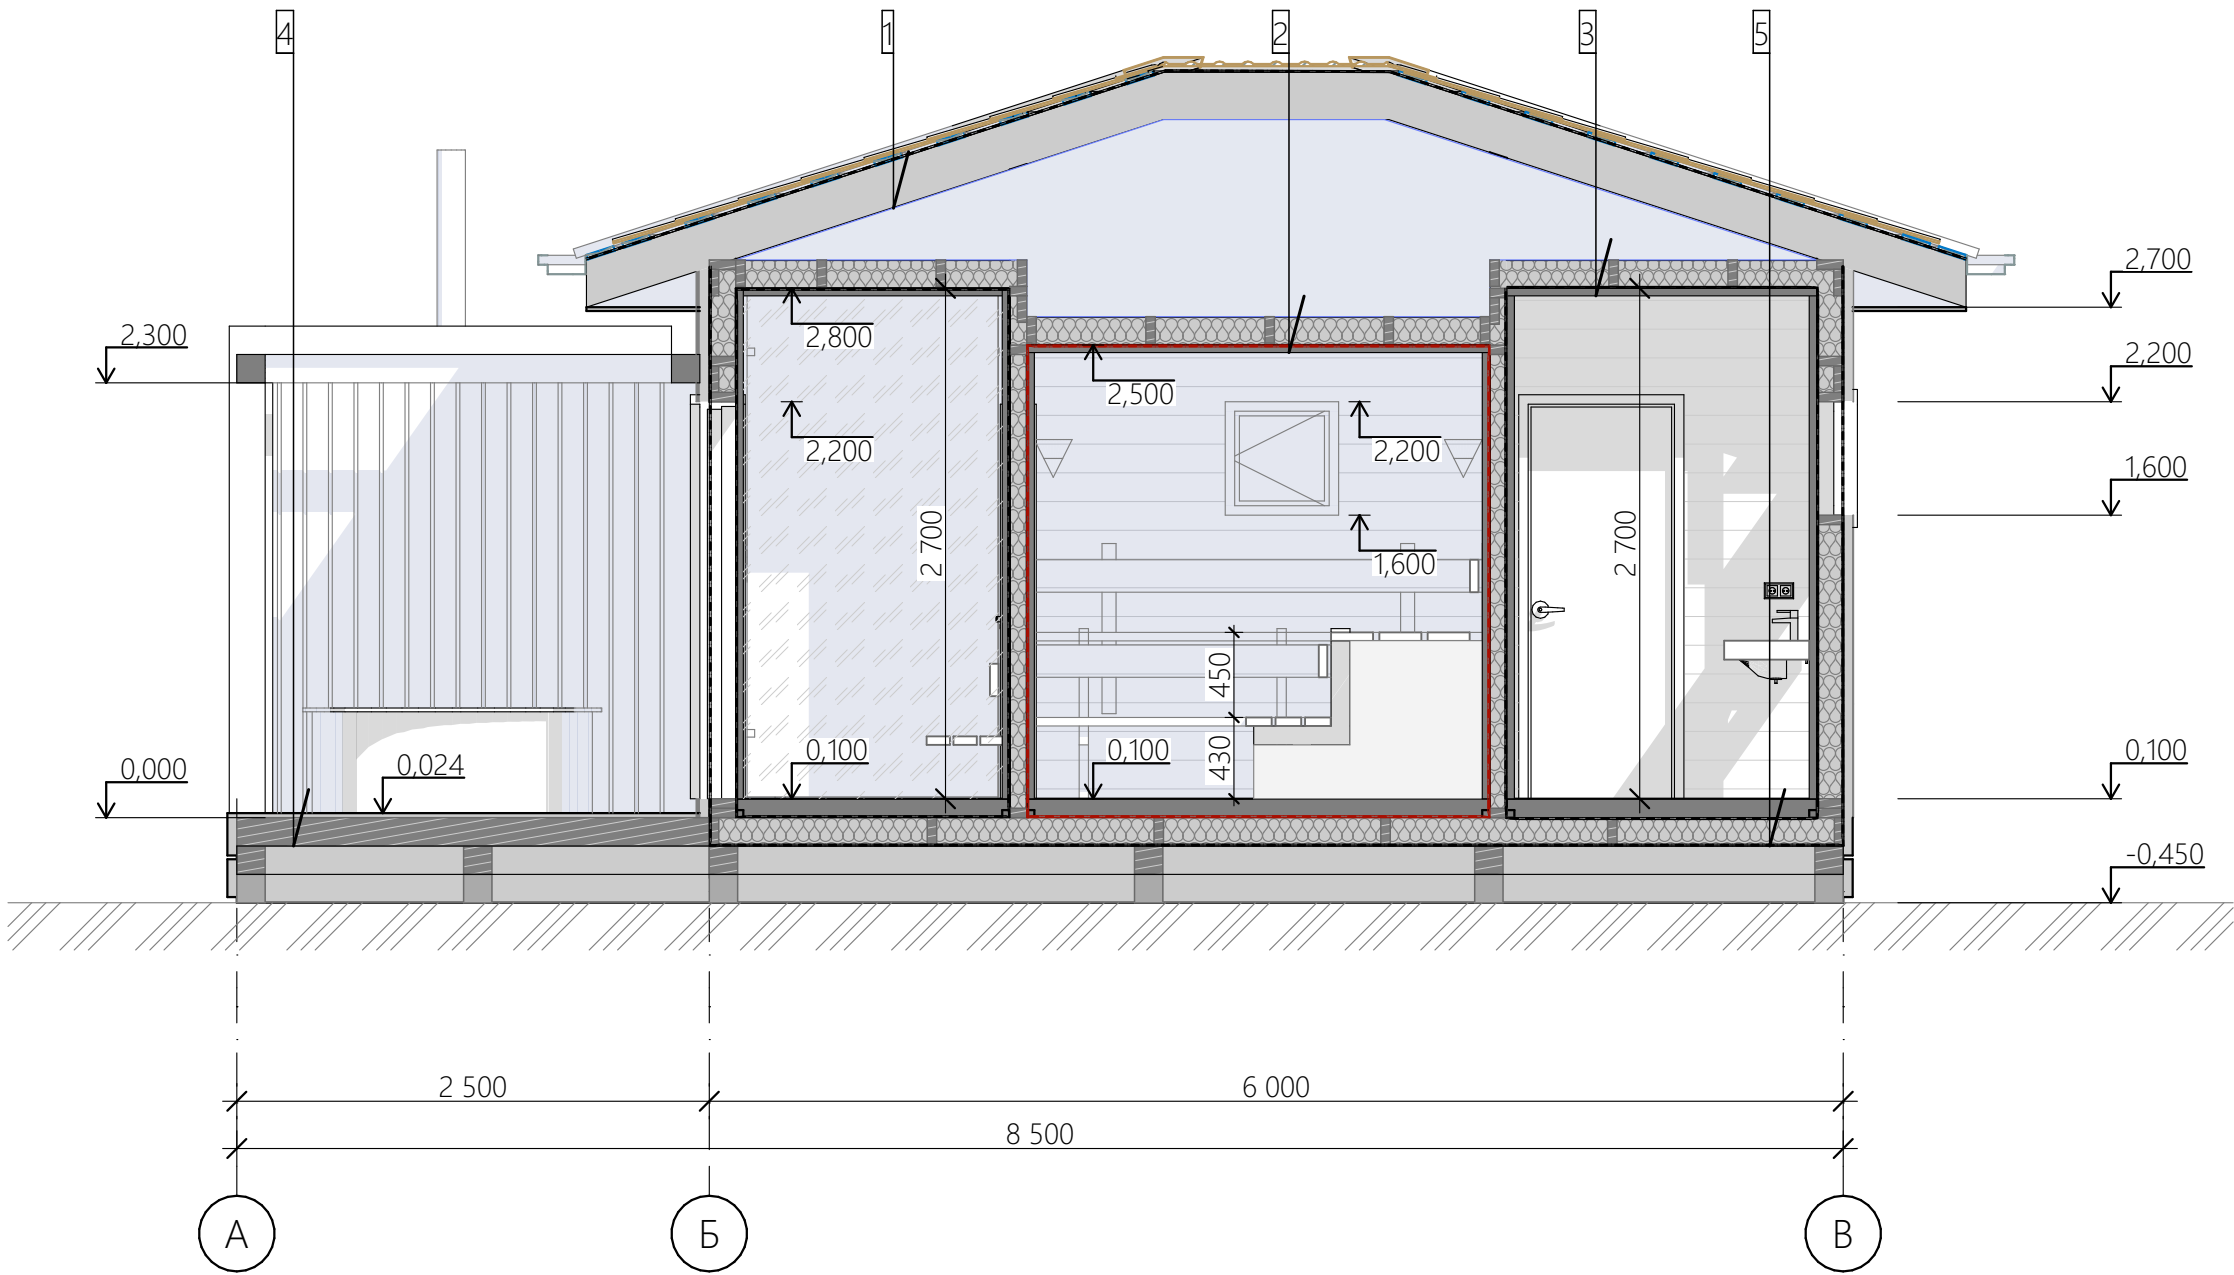

- 1 -Металлическая черепица 25x100мм
-Обрешётка 50x50мм
-Контробрешётка 50x50мм
-Гидроветрозащитная мембрана 190x45мм
-Стропильная система 190x45мм
- 2 -Лаги перекрытия (утеплённые 150мм) 140x45мм
-Пароизоляционная мембрана (алюминиевая фольга) 20x40мм
-Обрешётка 20x40мм
-Вагонка 20мм
- 3 -Лаги перекрытия (утеплённые 150мм) 140x45мм
-Пароизоляционная мембрана 20x40мм
-Обрешётка 20x40мм
-Имитация бруса 20мм
- 4 -Террасная доска 24мм
-Лага, доска 140x45мм 140 мм
- 5 -Керамогранит 10мм
-Клей 10мм
-Полусухая цементно-песчаная стяжка (с устройством теплого водяного пола) 50мм
-ЦСП 10мм
-ОСБ 18мм
-Пароизоляционная мембрана 140мм
-Лаги перекрытия (утепл.) 140мм
-Гидроветрозащитная мембрана 10мм
-Просечка (сетка яч. 5x5) 18мм
-Обрешётка 20мм

Согласовано				
Изм. № подл.	Взам. инв. №	Подп. и дата		

Лист	Изм.	№ Докум.	Подп.	Дата


Адрес:

Разрез 1-1

#Название Организации

Разрез 2-2

1:40

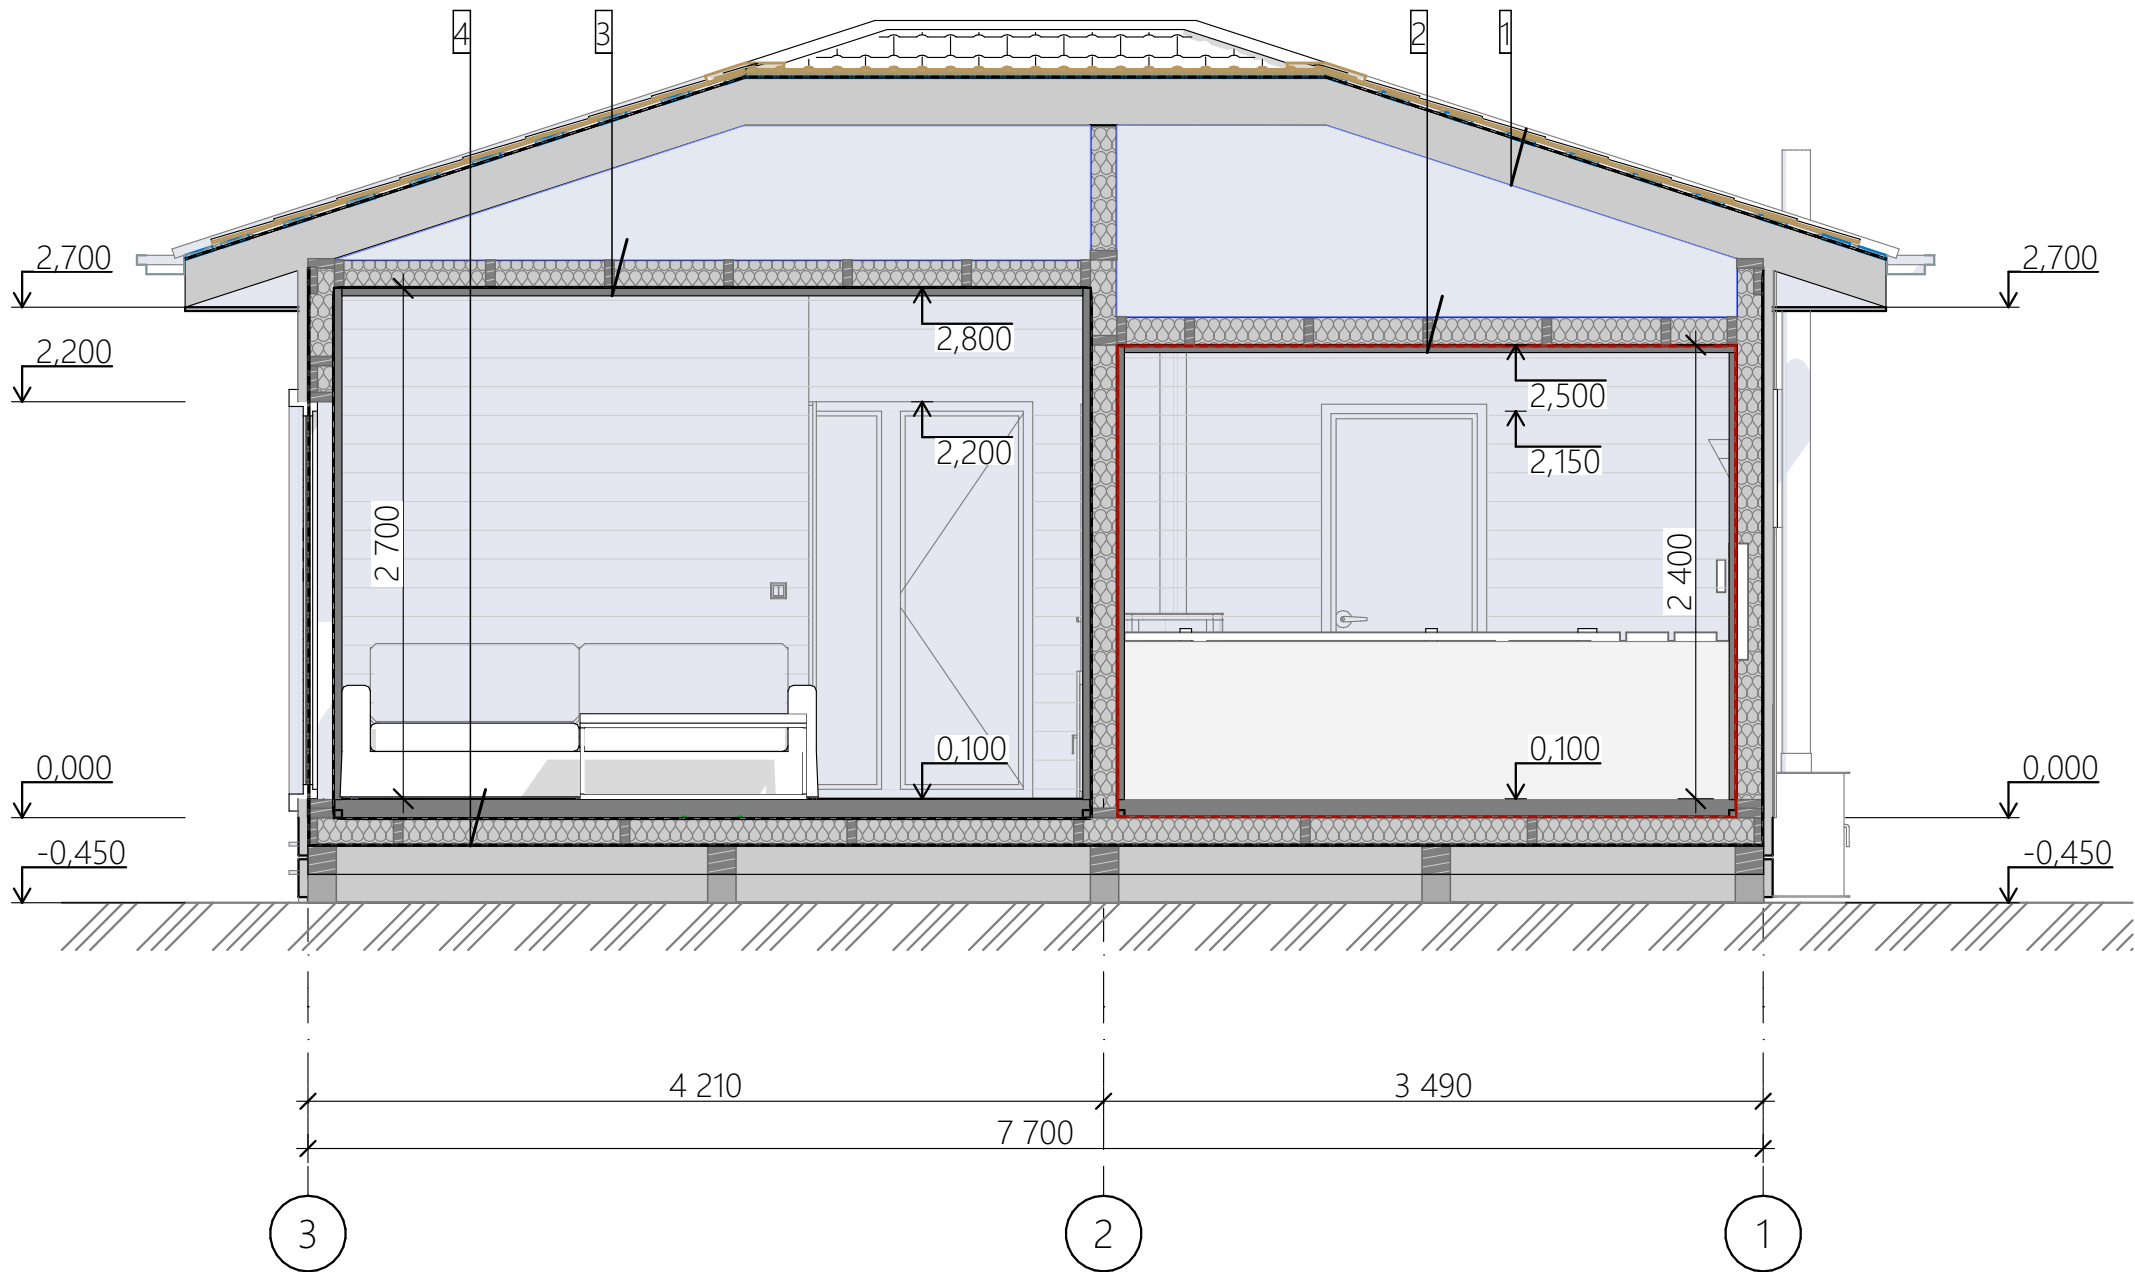

- | | | |
|---|---|----------|
| 1 | -Металлическая черепица | |
| | -Обрешётка | 25x100мм |
| | -Контробрешётка | 50x50мм |
| | -Гидроветрозащитная мембрана | |
| | -Стропильная система | 190x45мм |
| 2 | -Лаги перекрытия (утеплённые 150мм) | 140x45мм |
| | -Пароизоляционная мембрана (алюминиевая фольга) | |
| | -Обрешётка | 20x40мм |
| | -Вагонка | 20мм |
| 3 | -Лаги перекрытия (утеплённые 150мм) | 140x45мм |
| | -Пароизоляционная мембрана | |
| | -Обрешётка | 20x40мм |
| | -Имитация бруса | 20мм |
| 4 | -Ламинат | 10мм |
| | -Подложка под ламинат | 10мм |
| | -Полусухая цементно-песчаная стяжка | 50мм |
| | -ЦСП | 10мм |
| | -ОСБ | 18мм |
| | -Пароизоляция мембрана | |
| | -Лаги перекрытия (утепл.) | 140мм |
| | -Гидроветрозащитная мембрана | |
| | -Просечка (сетка яч. 5x5) | |
| | -Обрешётка | 20мм |

Согласовано

Взам. инв. №

Подп. и дата

Инв. № подл.

Лист	Изм.	№ Докум.	Подп.	Дата

Адрес:

Разрез 2-2

#Название Организации

Лист


17

Ведомость оконных проемов

1:1

Наименование Размеры проема Ш х В, мм Вид Площадь, м2

ОК-01 1 500×2 100

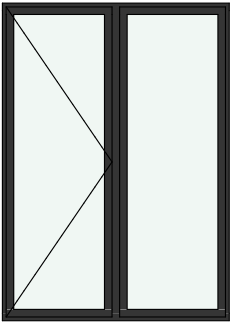

3,15

ОК-02 600×600



0,36

7,74 м²



Примечание:

- 1. Изготовление окон и дверей определяется заказчиком, допускается изменение открывания окон и дверей;
- 2. При заказе оконных и дверных блоков необходим обмер по месту от изготовителя;
- 3. Оконные и дверные изделия изображены со стороны открывания.

Согласовано

Ив. № подл. Подп. и дата Взам. инв. №

Лист	Изм.	№ Докум.	Подп.	Дата	Ведомость оконных проёмов	#Название Организации	Лист
							18

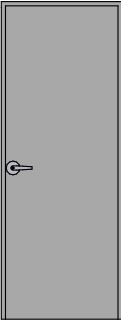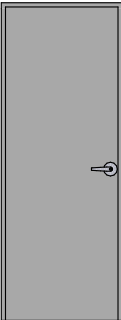Ведомость дверных проемов										1:1	
Наименование		Размеры проема Ш x В, мм			Вид			Площадь, м2			
ДВ-1		800×2 100						1,68			
ДН-1		900×2 100						1,89			
ДН-01		900×2 100						1,89			
ДП-1		800×2 100						1,68			
								12,18 м²			
Примечание: 1. Изготовление окон и дверей определяется заказчиком, допускается изменение открывания окон и дверей; 2. При заказе оконных и дверных блоков необходим обмер по месту от изготовителя; 3. Оконные и дверные изделия изображены со стороны открывания.											
Инв. № подл.	Изм.	№ Докум.	Подп.	Дата	Ведомость дверных проёмов		#Название Организации		Лист		
									19		

Согласовано

Взам. инв. №

Подп. и дата

Инв. № подл.


Согласовано				
И-нв. № подл.	Подп. и дата	Взам. инв. №		

Ф-1

1:40

Условные обозначения:

- Планкен (Цвет орех)
- Террасная доска ДПК
- Водосточная система, наличники, оконные рамы, кровля(RAL 9005)
- Гибкая керамика
Фоми, Polish Concrete
Wall

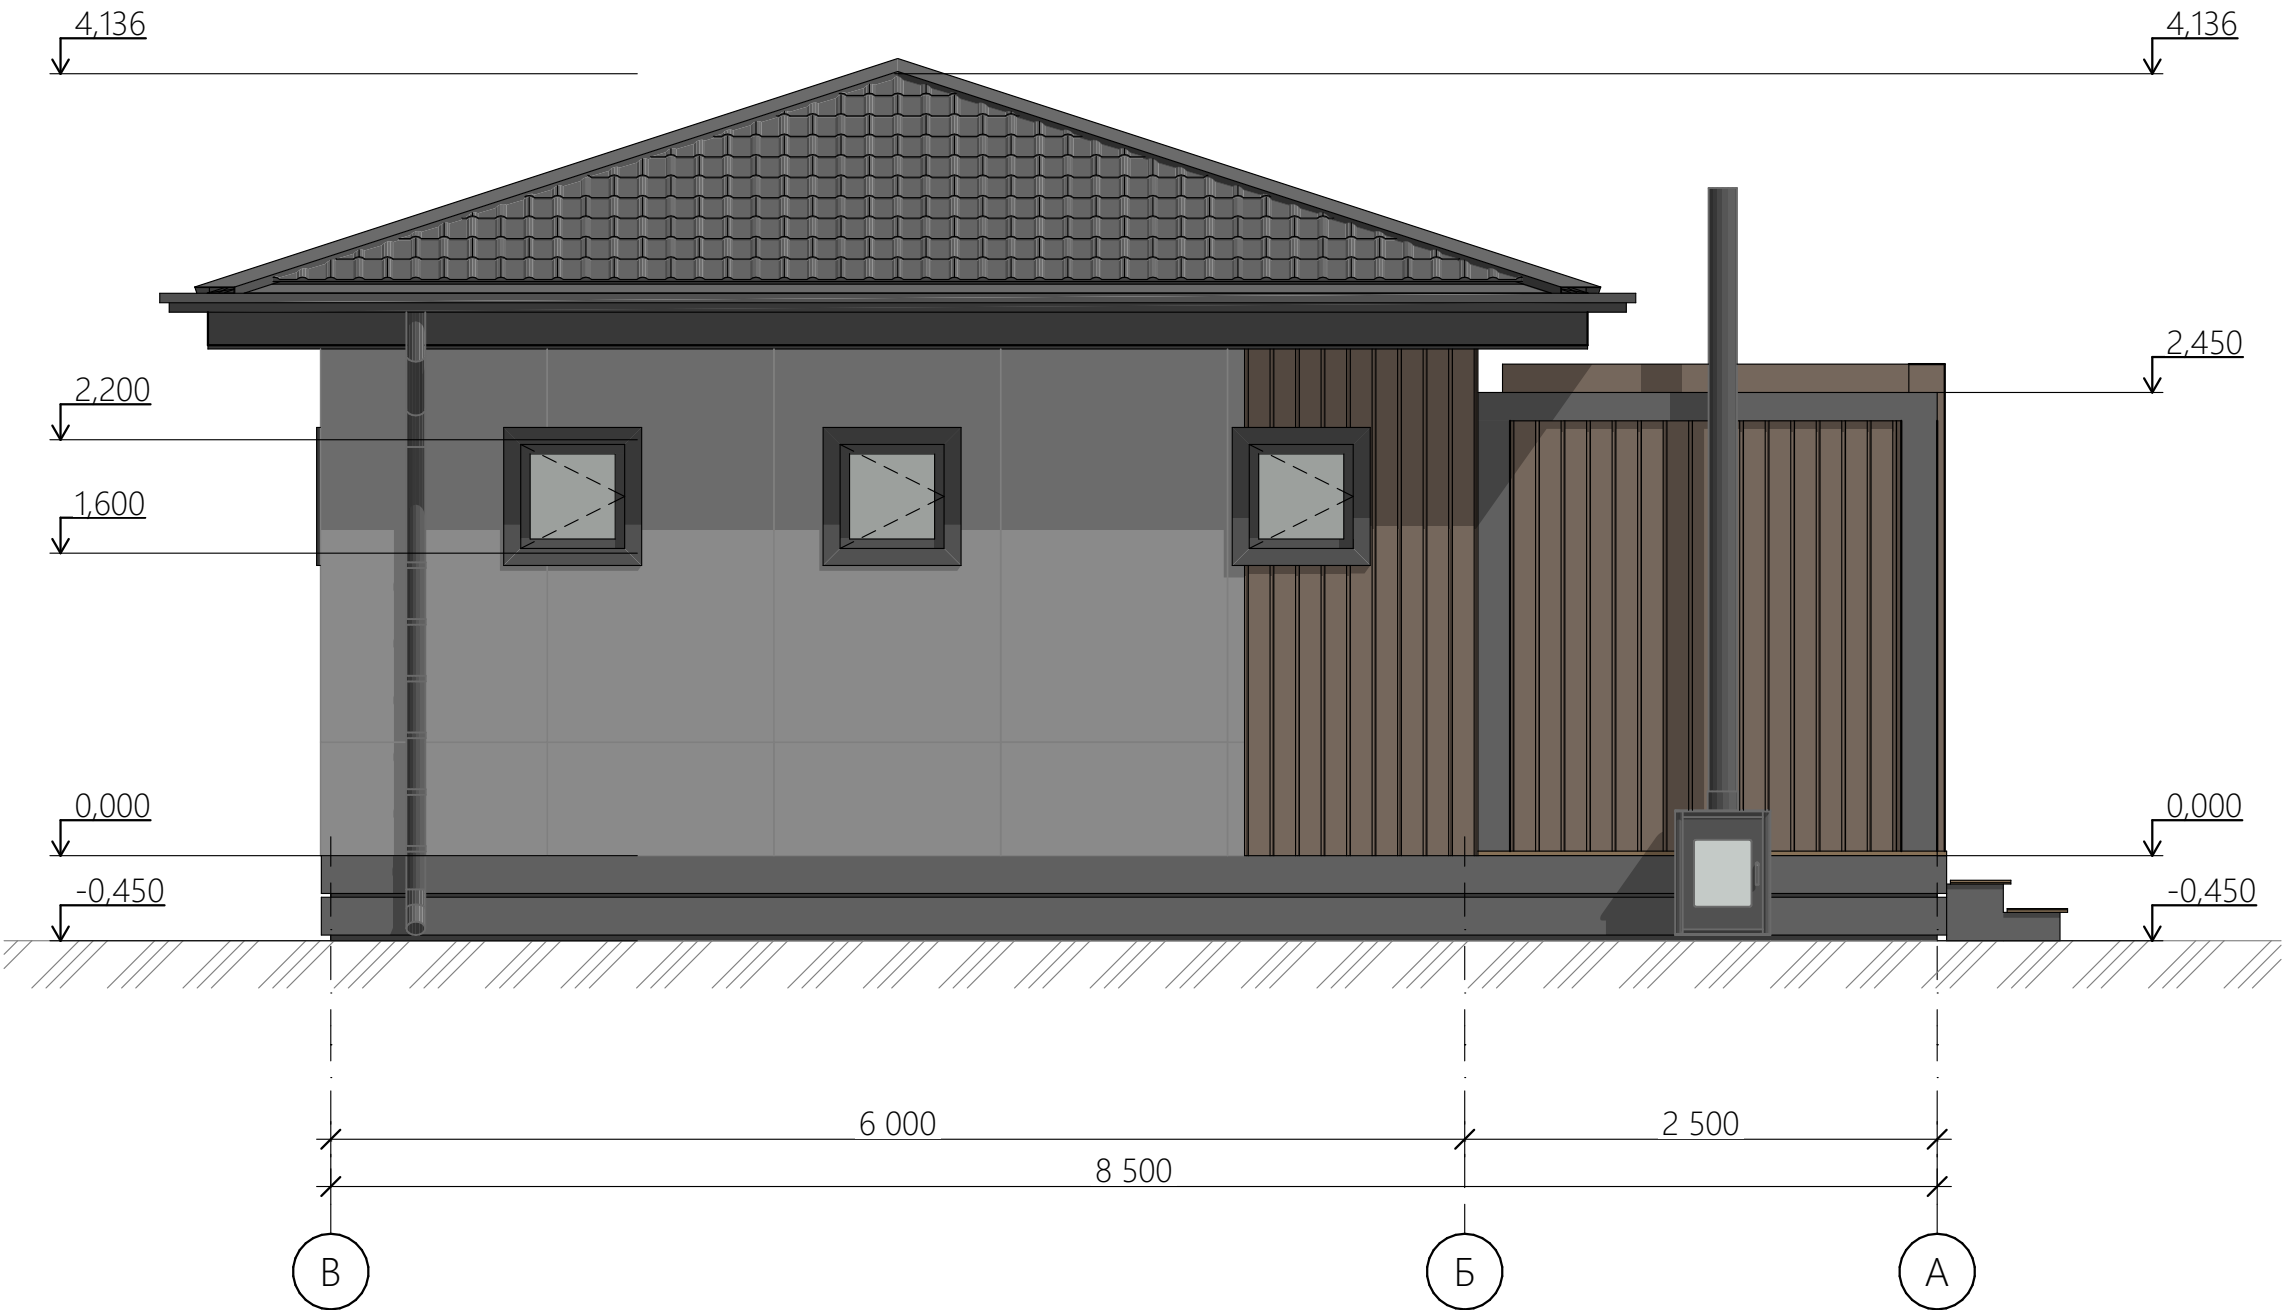

Лист	Изм.	№ Докум.	Подп.	Дата

Адрес:

Цветовое решение; Фасад в
осях В-А


#Название Организации

Ф-2

1:40

Условные обозначения:

-  -Планкен (Цвет орех)
-  -Террасная доска ДПК
-  -Водосточная система, наличники, оконные рамы, кровля(RAL 9005)
-  -Гибкая керамика Фоми, Polish Concrete Wall

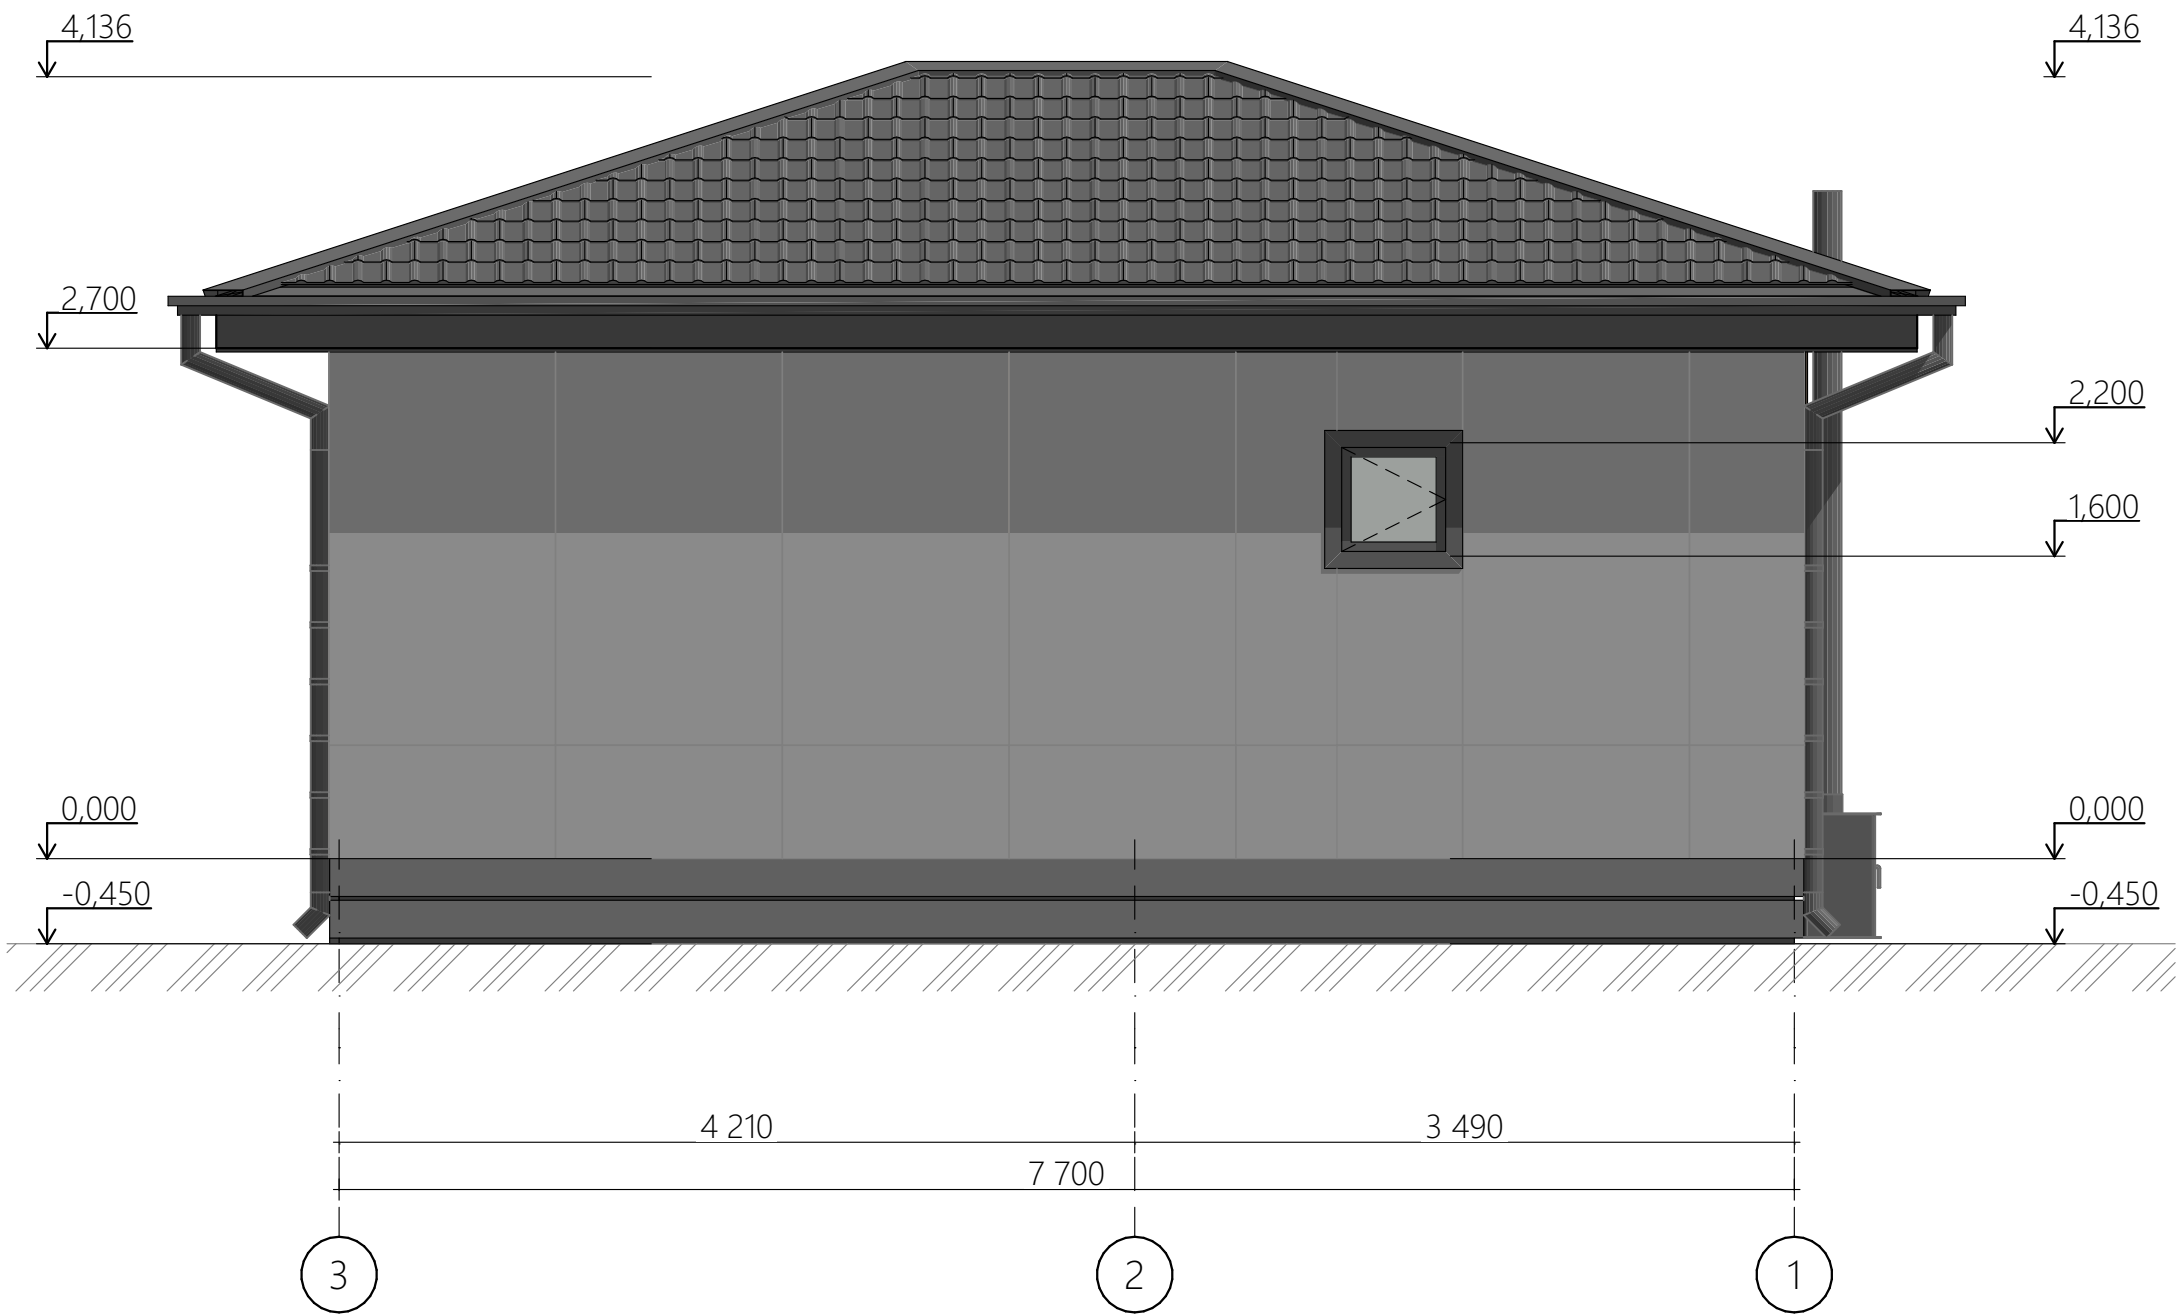

Согласовано

Взам. инв. №

Подп. и дата

Инв. № подл.

Лист	Изм.	№ Докум.	Подп.	Дата

Адрес:

Цветовое решение; Фасад в осях 3-1

#Название Организации

Лист

21

Согласовано			


Инва. № подл.	Подп. и дата	Взам. инв. №	

Лист	Изм.	№ Докум.	Подп.	Дата

Адрес:

Аксонометрия №1

#Название Организации

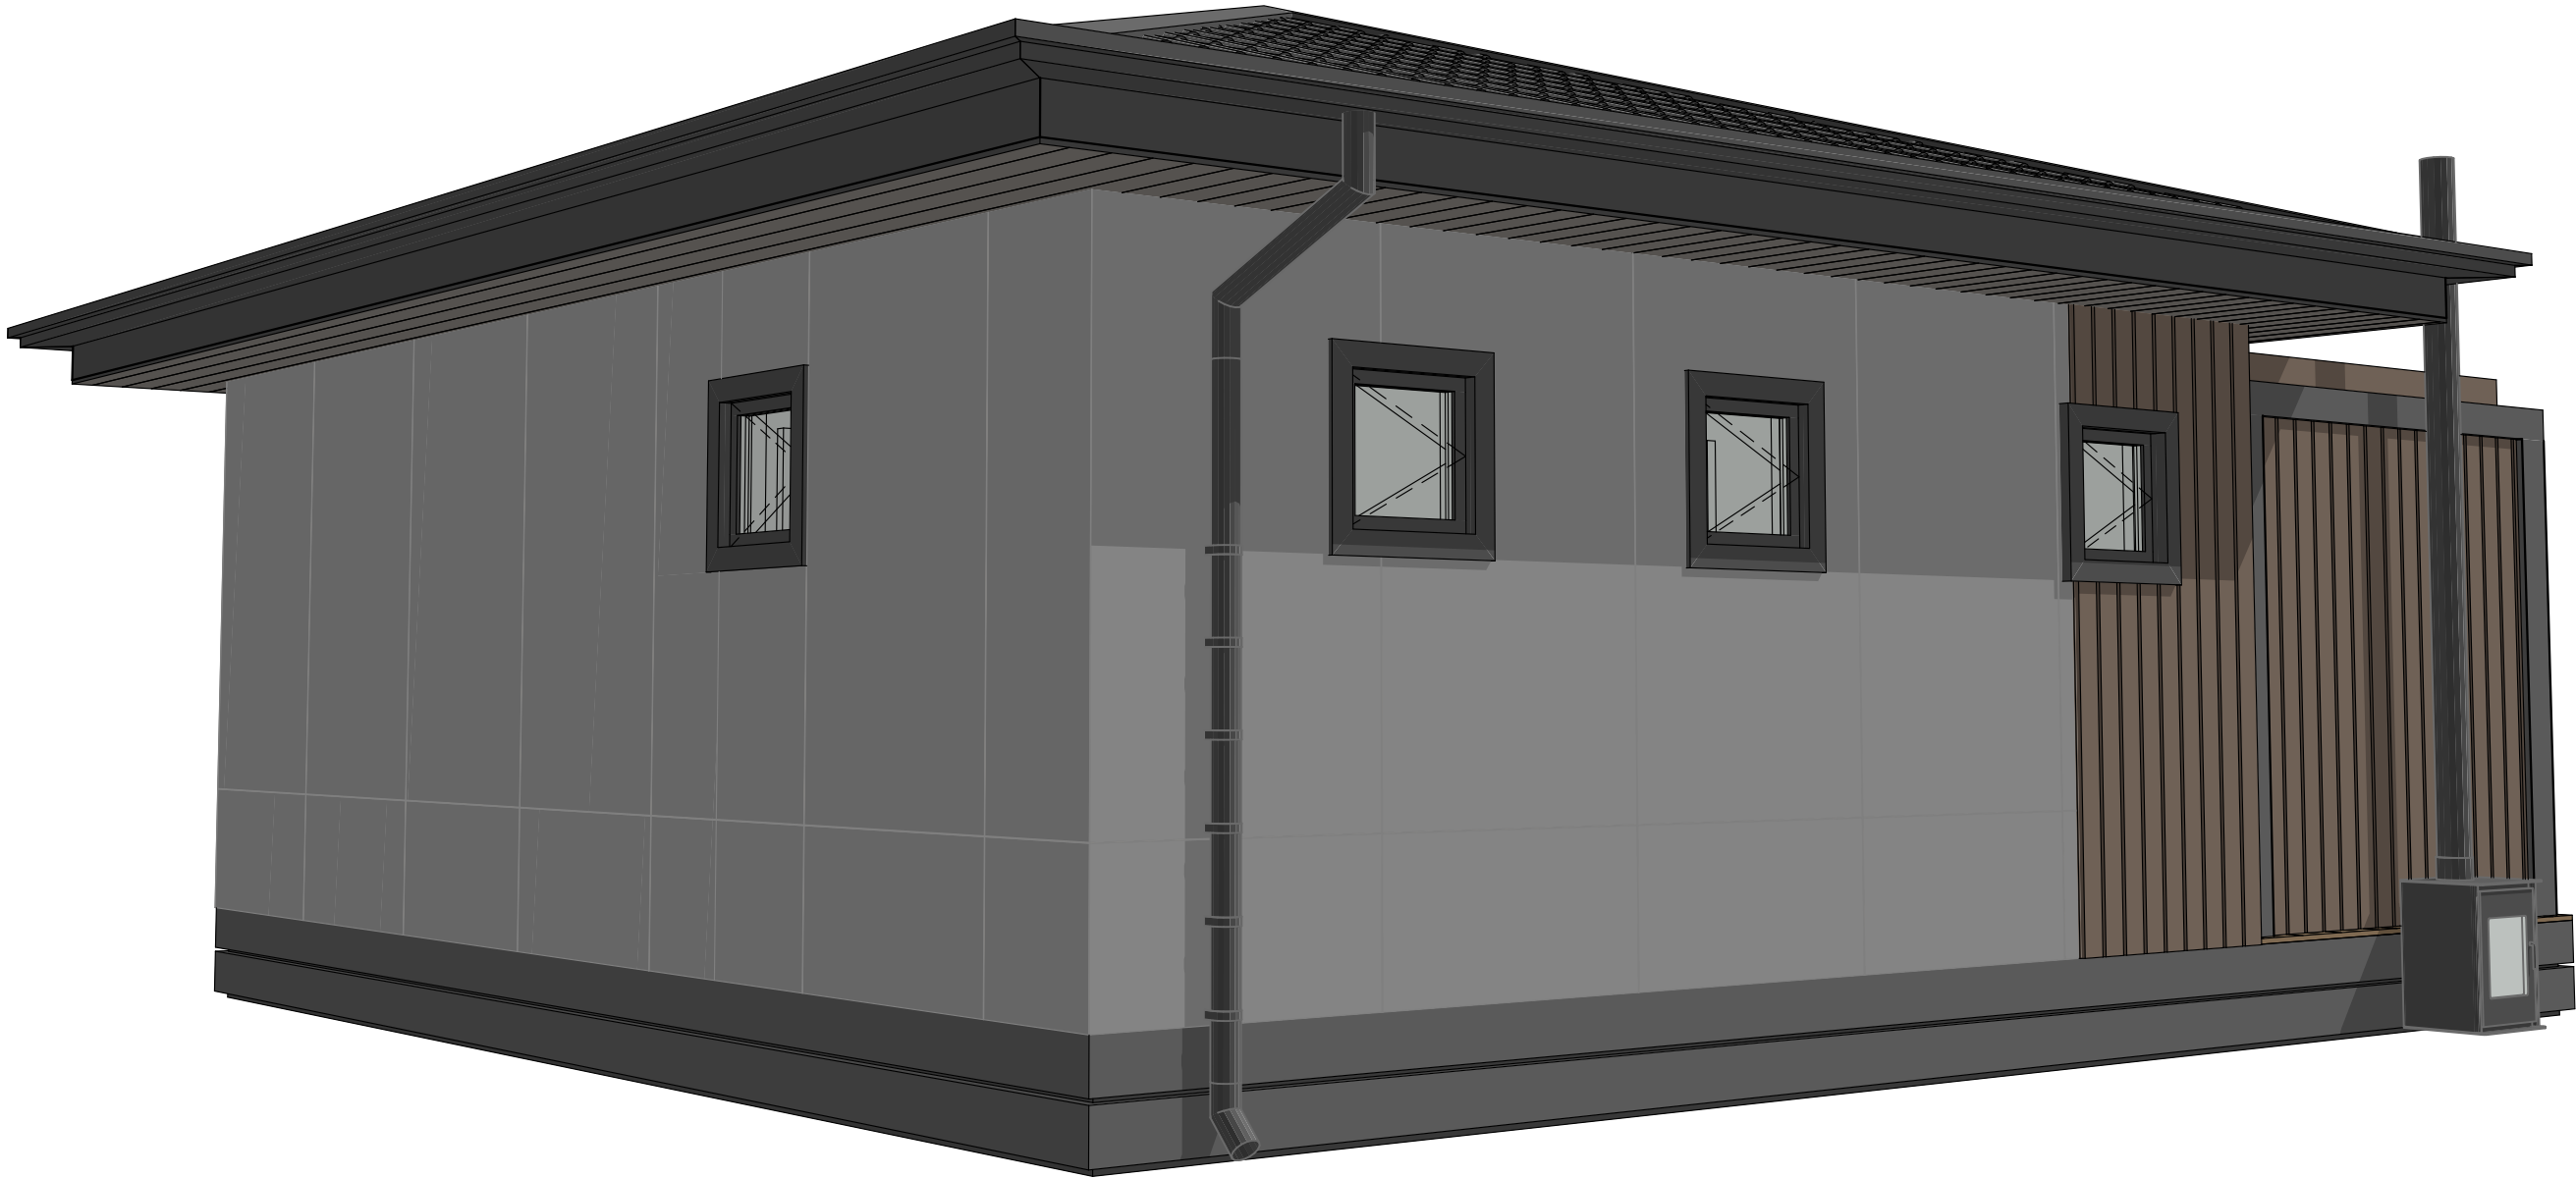

Ф-3

1:40

Условные обозначения:



-Планкен (Цвет орех)




-Террасная доска ДПК



-Водосточная система,
наличники, оконные
рамы, кровля(RAL 9005)



-Гибкая керамика
Фоми, Polish Concrete
Wall

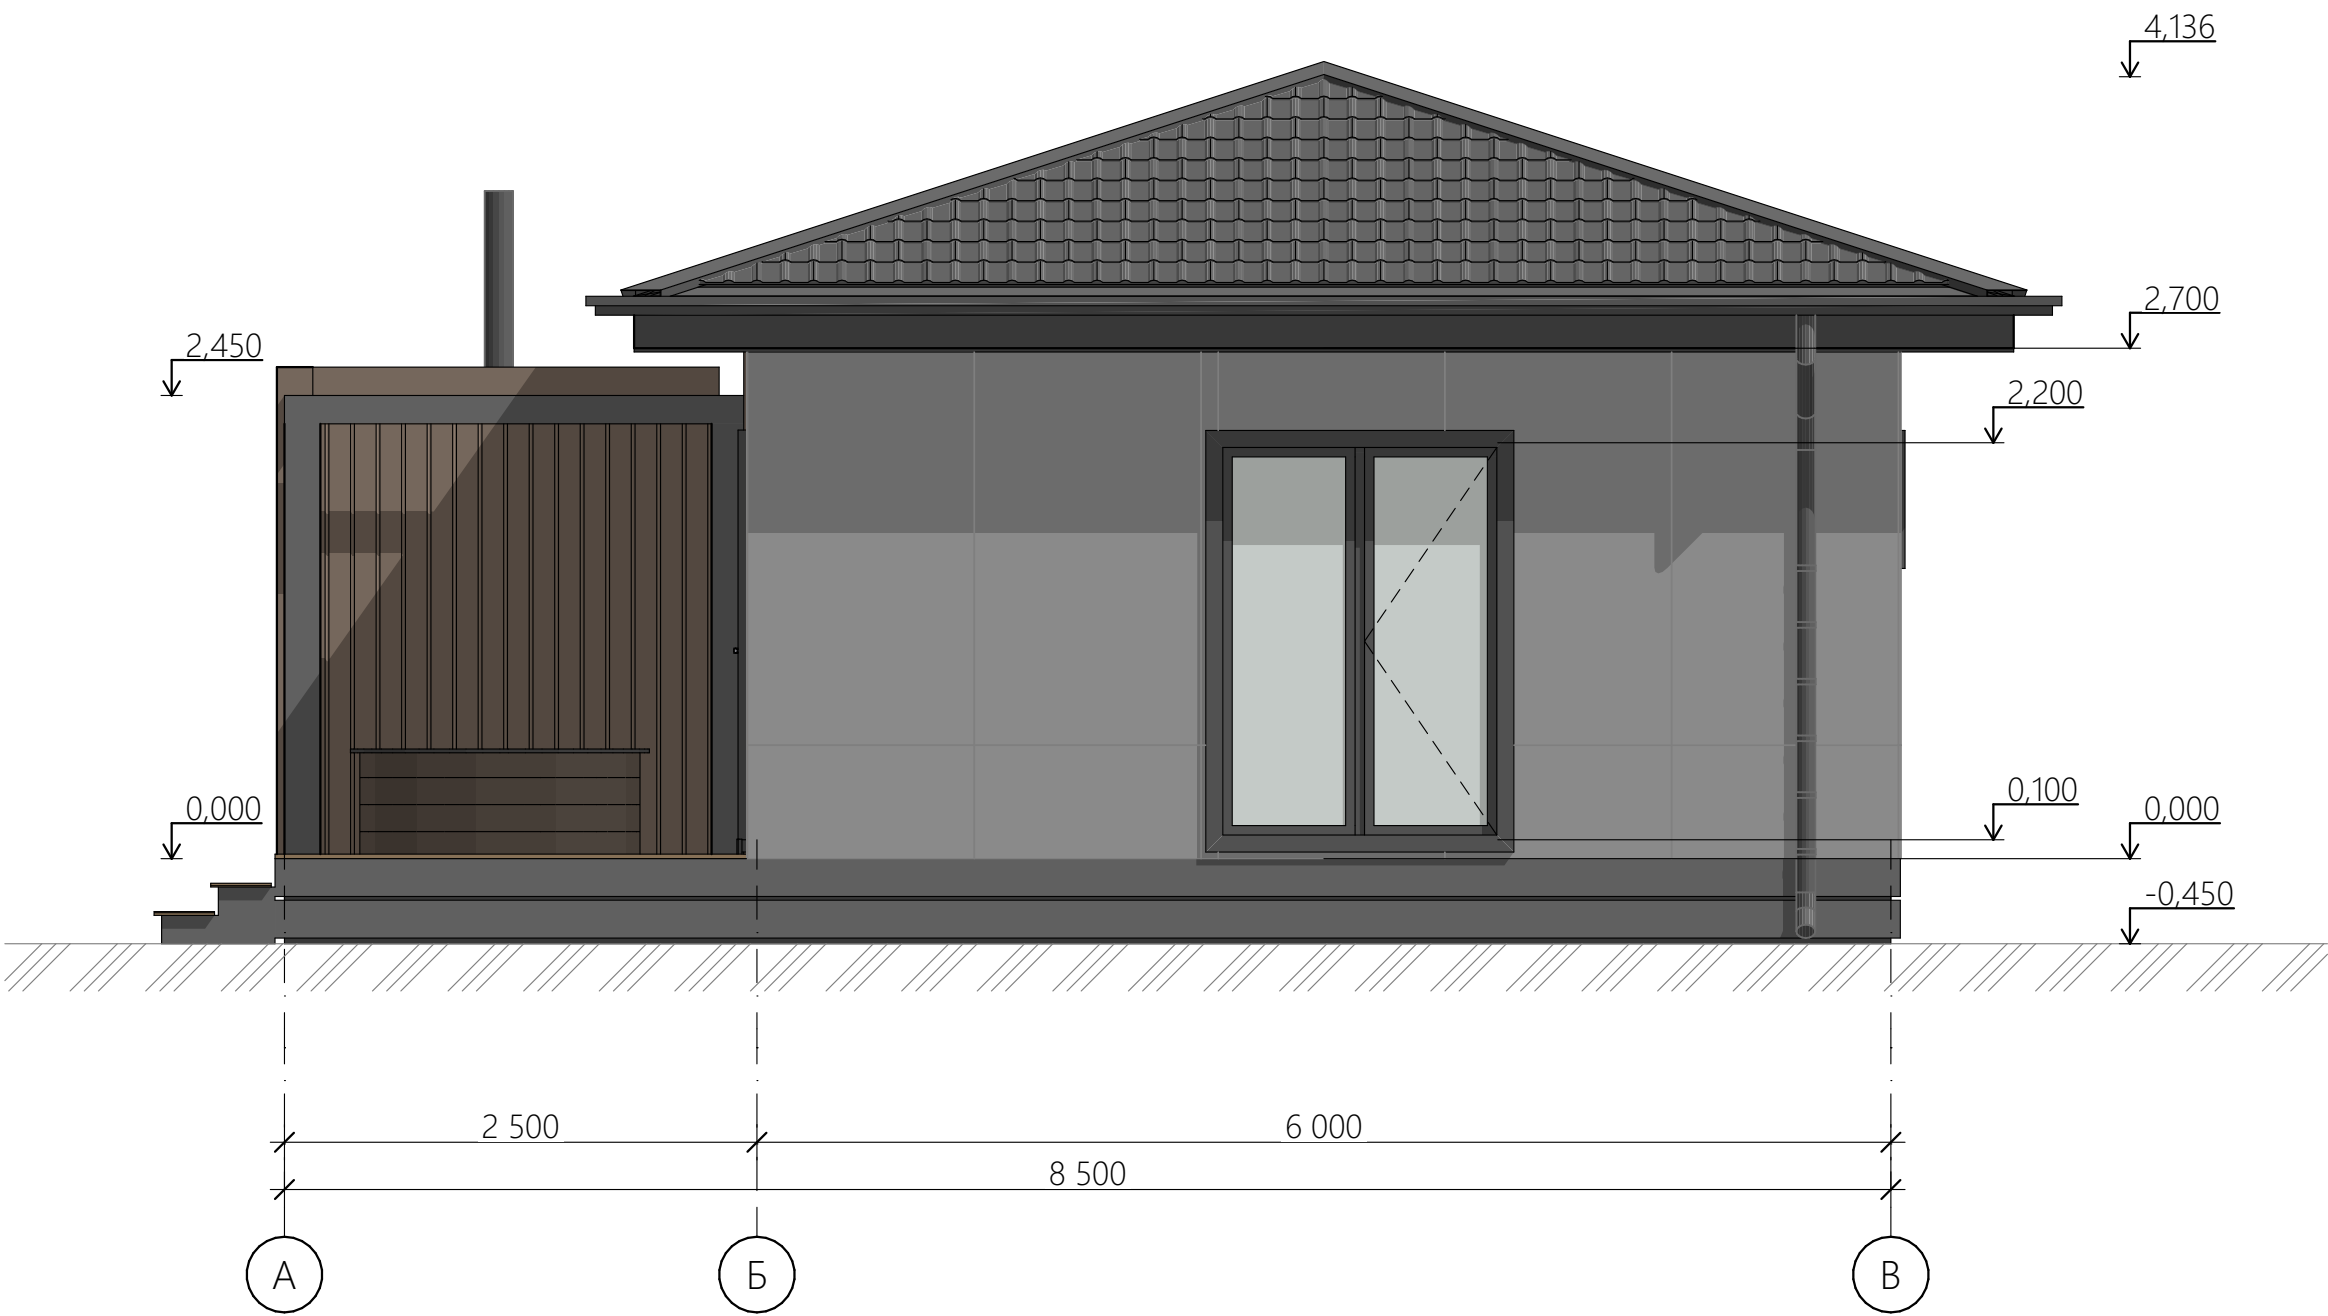

Согласовано

Взам. инв. №

Подп. и дата

Инв. № подл.

Лист	Изм.	№ Докум.	Подп.	Дата

Адрес:

Цветовое решение; Фасад в
осях А-В

#Название Организации

Лист


23

Ф-4

1:40

Условные обозначения:

- Планкен (Цвет орех)
- Террасная доска ДПК
- Водосточная система, наличники, оконные рамы, кровля(RAL 9005)
- Гибкая керамика Фоми, Polish Concrete Wall

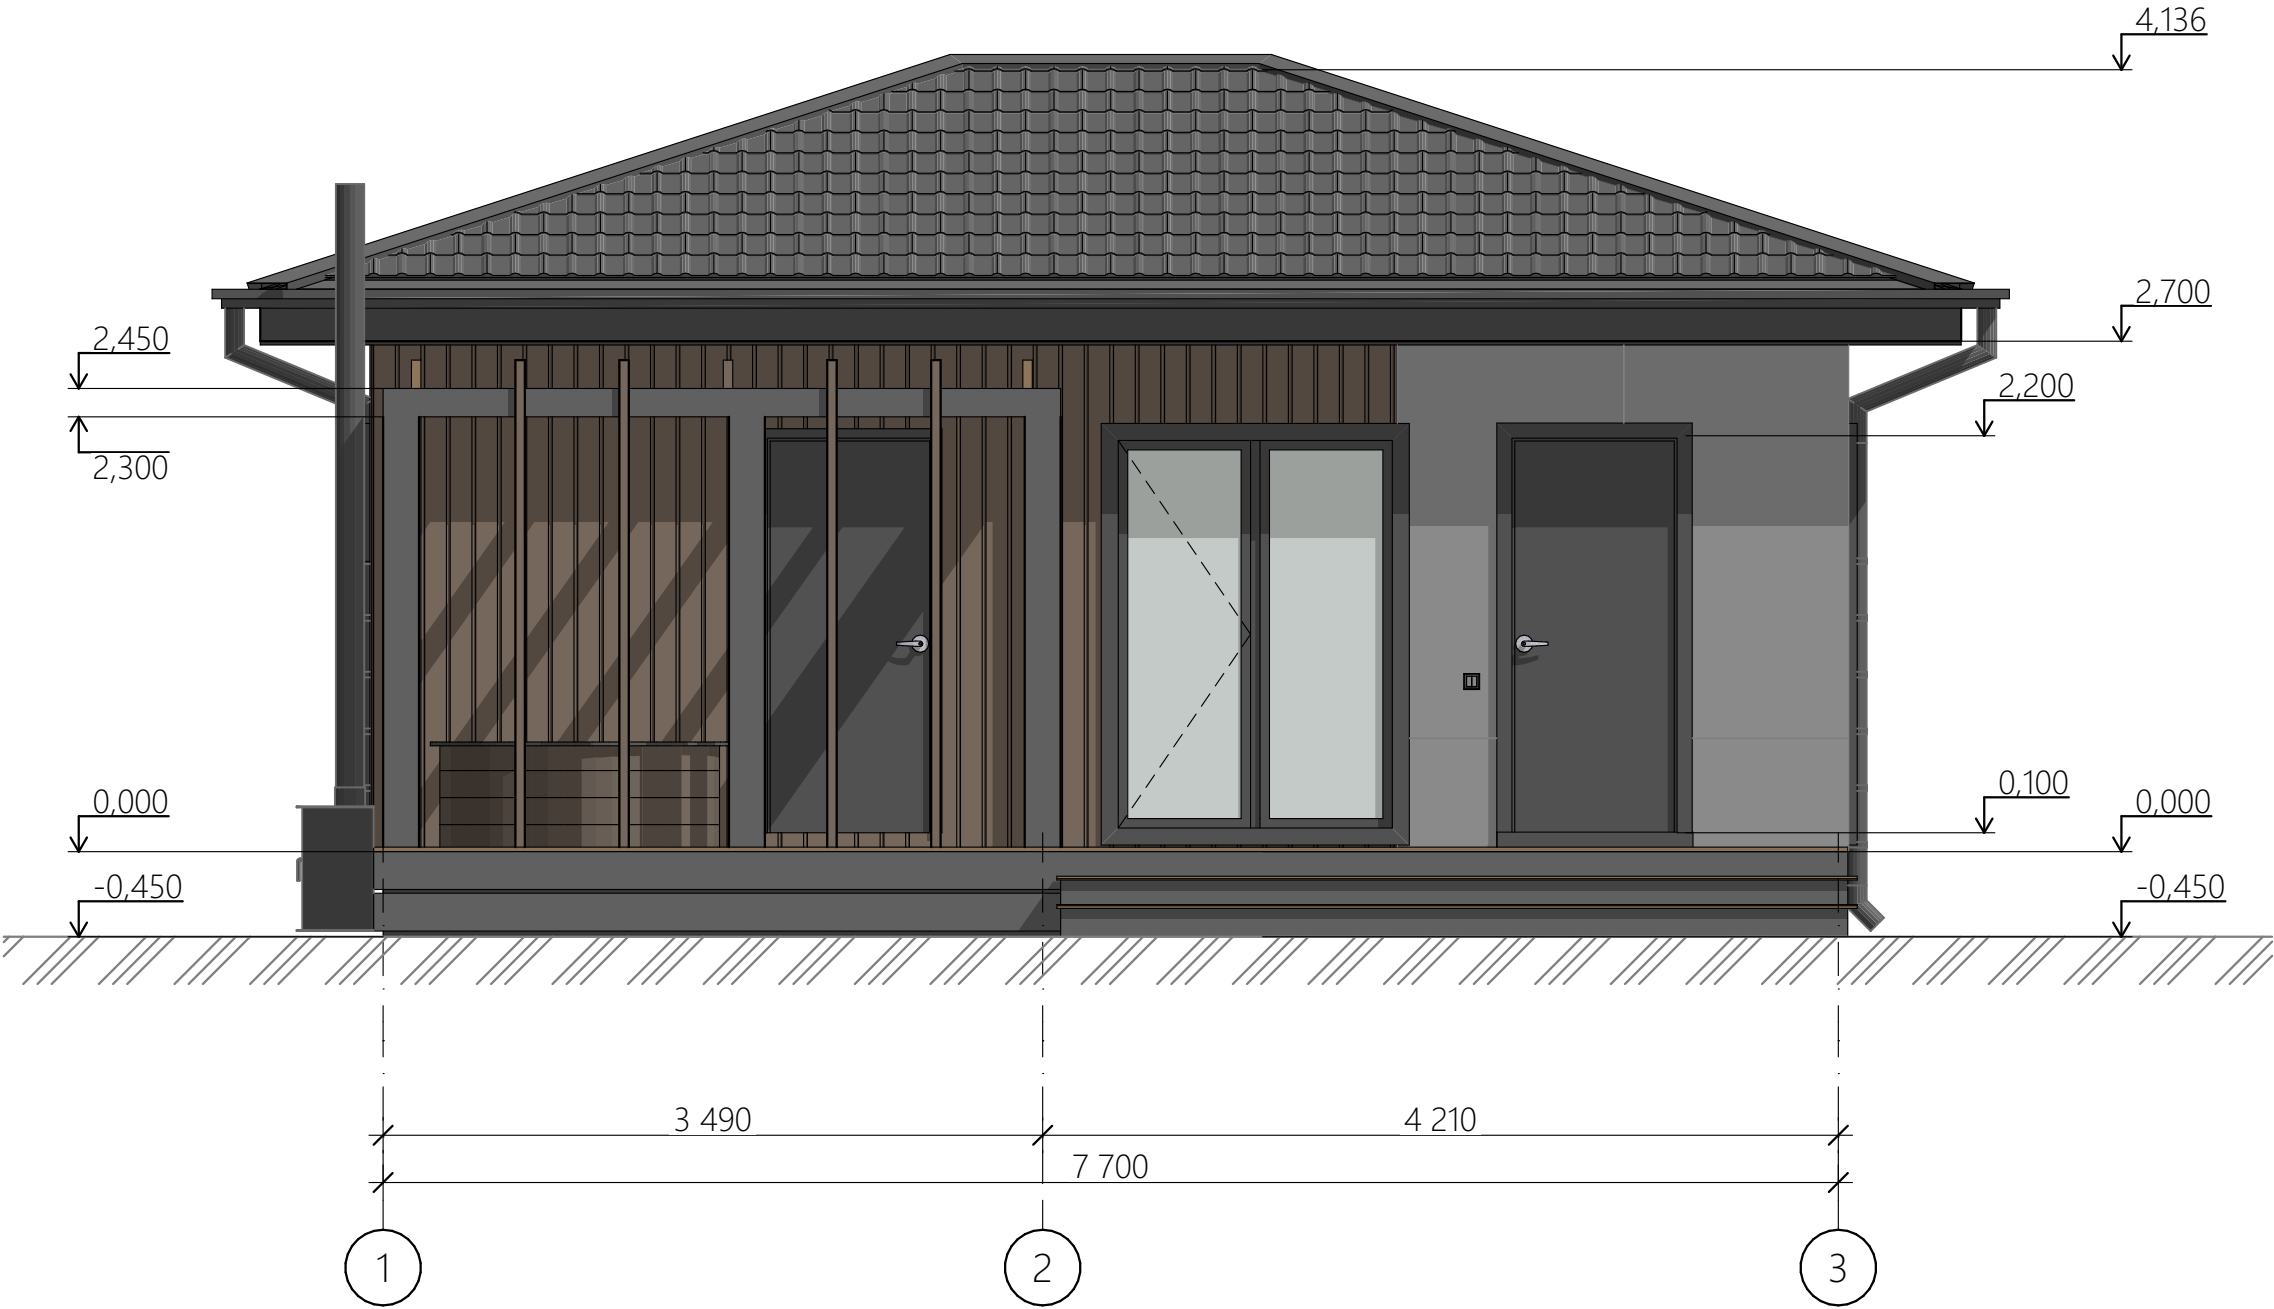

Согласовано

Взам. инв. №

Подп. и дата

Инв. № подл.

Лист	Изм.	№ Докум.	Подп.	Дата

Адрес:

Цветовое решение; Фасад в осях 1-3

#Название Организации

Лист


24

Согласовано

И-нв. № подл. Подп. и дата Взам. инв. №

Лист	Изм.	№ Докум.	Подп.	Дата

Адрес:

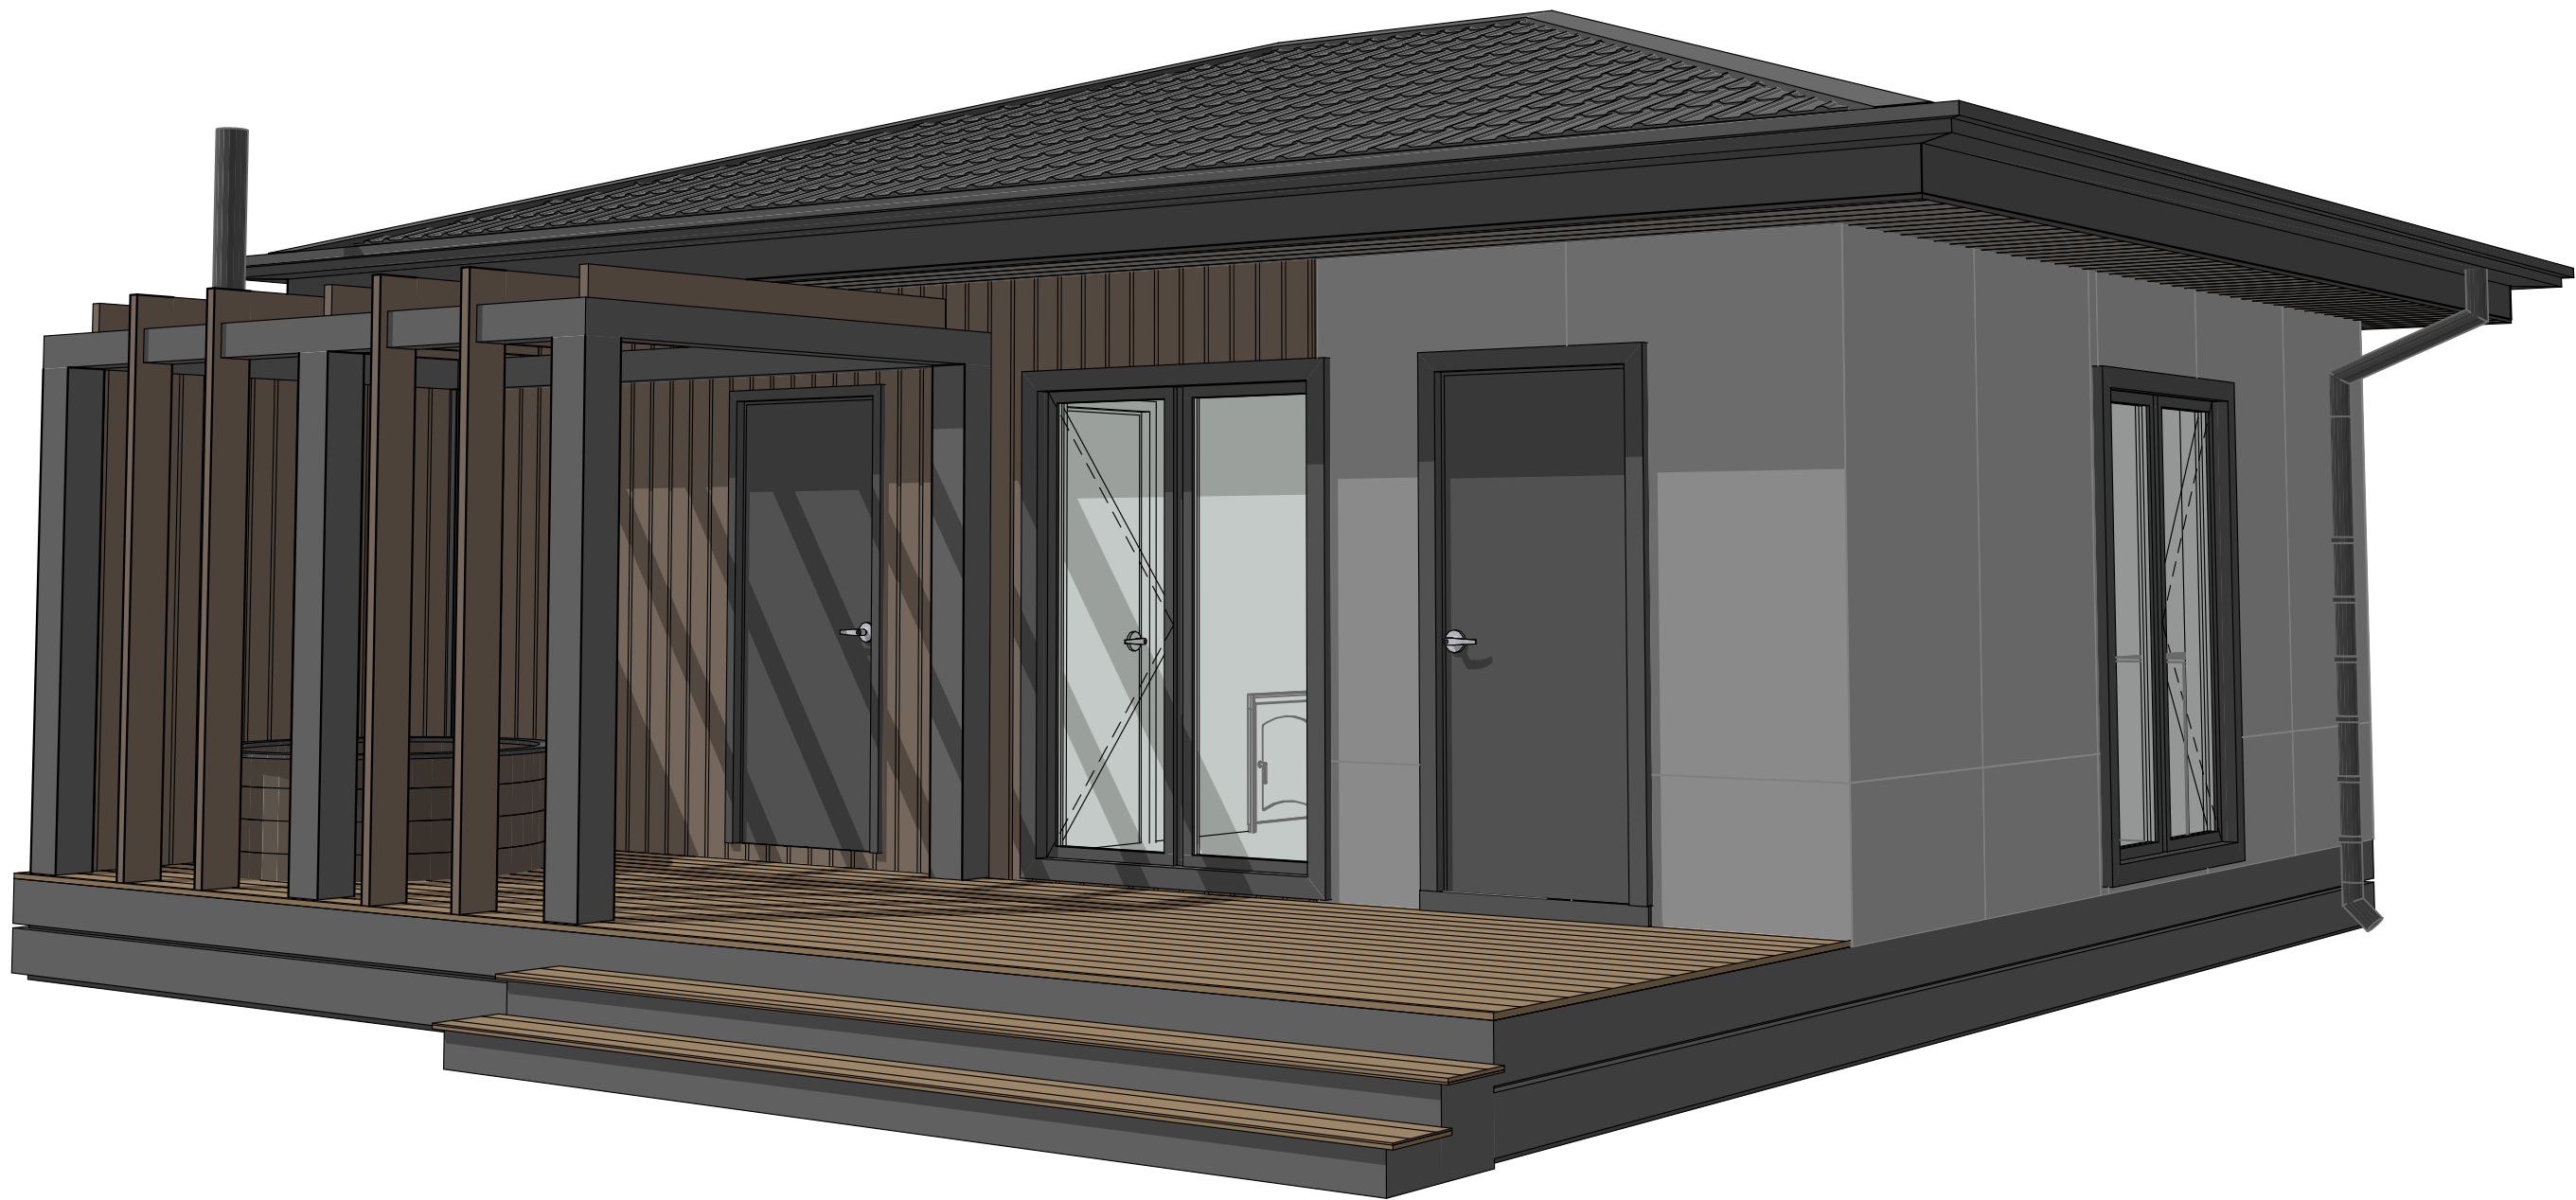

Аксонометрия №2

#Название Организации

Согласовано

Взам. инв. №

Подп. и дата

Инв. № подл.



Лист	Изм.	№ Докум.	Подп.	Дата

Адрес:

Визуализация №1

#Название Организации

Согласовано			

Инва. № подл.	Подп. и дата	Взам. инв. №	

Лист	Изм.	№ Докум.	Подп.	Дата

Адрес:

Визуализация №2

#Название Организации



Согласовано					
Инва. № подл.	Подп. и дата		Взам. инв. №		



Лист	Изм.	№ Докум.	Подп.	Дата

Адрес:

Визуализация №3

#Название Организации

Согласовано

Взам. инв. №

Подп. и дата

Инв. № подл.



Лист	Изм.	№ Докум.	Подп.	Дата

Адрес:

Визуализация №4

#Название Организации

Согласовано

Взам. инв. №

Подп. и дата

Инв. № подл.



Лист	Изм.	№ Докум.	Подп.	Дата

Адрес:

Визуализация №5

#Название Организации

Согласовано					
Инва. № подл.	Подп. и дата		Взам. инв. №		



Лист	Изм.	№ Докум.	Подп.	Дата

Адрес:

Визуализация №6

#Название Организации