

ARCHITECTURE/
CONSTRUCTION



Название:
Разработал:
Принял:
г. Москва



Согласовано				
И-нв. № подл.	Подп. и дата	Взам. инв. №		

Лист	Наименование	Примечание
1	Ведомость чертежей	
2	Пояснительная записка	
3	Схема планировочной организации земельного участка	
4	Маркировочный план	
5	Размерный план	
6	План расстановки мебели и оборудования	
7	Зд-разрез	
8	План водяного теплого пола	
9	План покрытий пола	
10	Экспликация покрытий пола	
11	План покрытия отделки стен	
12	Экспликация отделки стен	
13	План размещения розеток стен	
14	План расстановки светильников и выключателей	
15	План кровли	
16	Разрез 1-1	
17	Разрез 2-2	
18	Ведомость оконных проёмов (начало)	
19	Ведомость оконных проёмов (окончание)	
20	Ведомость дверных проёмов	
21	Цветовое решение; Фасад в осях В-А	
22	Цветовое решение; Фасад в осях З-1	
23	Аксонометрия №1	
24	Цветовое решение; Фасад в осях А-В	
25	Цветовое решение; Фасад в осях 1-3	
26	Аксонометрия №2	
27	Визуализация №1	
28	Визуализация №2	
29	Визуализация №3	
30	Визуализация №4	

Лист	Наименование	Примечание
31	Визуализация №5	
32	Визуализация №6	

В основу архитектурно-планировочных решений положены требования технологических заданий и требования норм и правил строительного проектирования, действующих на территории РФ.

Основные параметры и требования разработаны на основании пожеланий и требований заказчика.

Архитектурные решения приняты в соответствии со следующими нормативными документами:

- Градостроительный кодекс российской федерации.
- Земельного Кодекса Российской Федерации.
- Федеральный закон от 22.07.2008 N 123 - ФЗ (ред. от 29.07.2017)"Технический регламент о требованиях пожарной безопасности.
- Федеральный закон № 384 - ФЗ «Технический регламент о безопасности зданий и сооружений».
- ГОСТ Р 21.1101-2013.«Основные требования к проектной и рабочей документации».
- Постановление правительства РФ от 16.02.2008 № 87 «Положение о составе разделов проектной документации и требованиях к их содержанию».
- СП 42.13330.2011 «Градостроительство. Планировка и застройка городских и сельских поселений».
- СП 131.13330.2018 «СНиП 23-01-99* Строительная климатология».
- СП 20.13330.2016 «СНиП 2.01.07-85* Нагрузки и воздействия».
- СП 22.13330.2016 «СНиП 2.02.01-83* Основания зданий и сооружений».
- СП 70.13330.2012 (с изменениями №1) «СНиП 3.03.01-87 Несущие и ограждающие конструкции».
- СП 64.13330.2017 «СНиП II-25-80 Деревянные конструкции».
- СП 17.13330.2017 «СНиП II-26-76 Кровли».
- СП 29.13330.2011 «СНиП 2.03.13-88 Полы».
- СП 28.13330.2017 «СНиП 2.03.11-85 Защита строительных конструкций от коррозии».
- СП 50.13330.2012 «СНиП 23-02-2003 Тепловая защита зданий».

Согласовано				
И-нв. № подл.	Подп. и дата	Взам. инв. №		

1. Общие данные:

1.1. Архитектурный проект разработан на основании требований и пожеланий заказчика.

Тип строения	ИЖД
Относительная отм. ±0.000	ур. верха фундаментной плиты
Общая площадь застройки, м2	93,80
Габаритные размеры каркаса здания	10х7 м
Этажность	1 этаж
Конструктивная схема	Деревянный каркас

2. Конструктивные решения:

2.1. Рабочие чертежи разработаны на основании задания на проектирование

Полезная нагрузка на перекрытие	150 кгс/м2	-
Нормативная глубина промерзания	1,2м	СП 22.13330.2016 СП 131.13330.2020
Нормативное ветровое давление	I район (23кгс/м2)	СП 22.13330.2016
Нормативный вес снегового покрова	III район (150кгс/м2)	СП 22.13330.2016
Температура наиболее холодной пятидневки	-29°С	СП 131.13330.2020

2.2. Конструктивное строение представляет собой сооружение:

- на свайном фундаменте
- несущими стенами из деревянного каркаса
- вальмовой кровлей по деревянным стропилам

2.3. Необходимо осуществлять технический надзор за производством строительных работ. Данные по проведённым работам необходимо систематически вносить в журнал работ.

По каждому из этапов работ необходимо осуществлять входной контроль материалов и вести приёмку.

Фундамент	винтовые сваи (д 108мм)
Несущие конструкции	деревянный каркас (140х45мм)
Стропильная система	строганая доска (190х45мм)
Тип крыши	двускатная
Покрытие кровли	профлист

2.4. Все деревянные конструкции обработать огне-биозащитными септиками в соответствии со СП 28.13330.2017 "Защита строительных конструкций от коррозии".

2.5. Кровельные работы выполнять в соответствии с требованиями фирмы производителя.

2.6. Все работы вести в строгом соответствии с требованиями СНиП 12.03.2001 "Безопасность труда в строительстве".

2.7. При выполнении всех работ строго соблюдать меры противопожарной безопасности.

2.8. Возможна замена материалов аналогами.

*Решения, принятые в проекте и отображенные в чертежах, соответствуют требованиям экологических, санитарно - гигиенических, противопожарных и других норм, действующих на территории Российской Федерации, и обеспечивают безопасную для жизни и здоровья людей эксплуатацию объекта при соблюдении предусмотренных рабочих чертежей и мероприятий.

Лист	Изм.	№ Докум.	Подп.	Дата

Адрес:

Пояснительная записка

#Название Организации

Согласовано


Взам. инв. №

Подп. и дата

Инв. № подл.

Маркировочный план

1:65

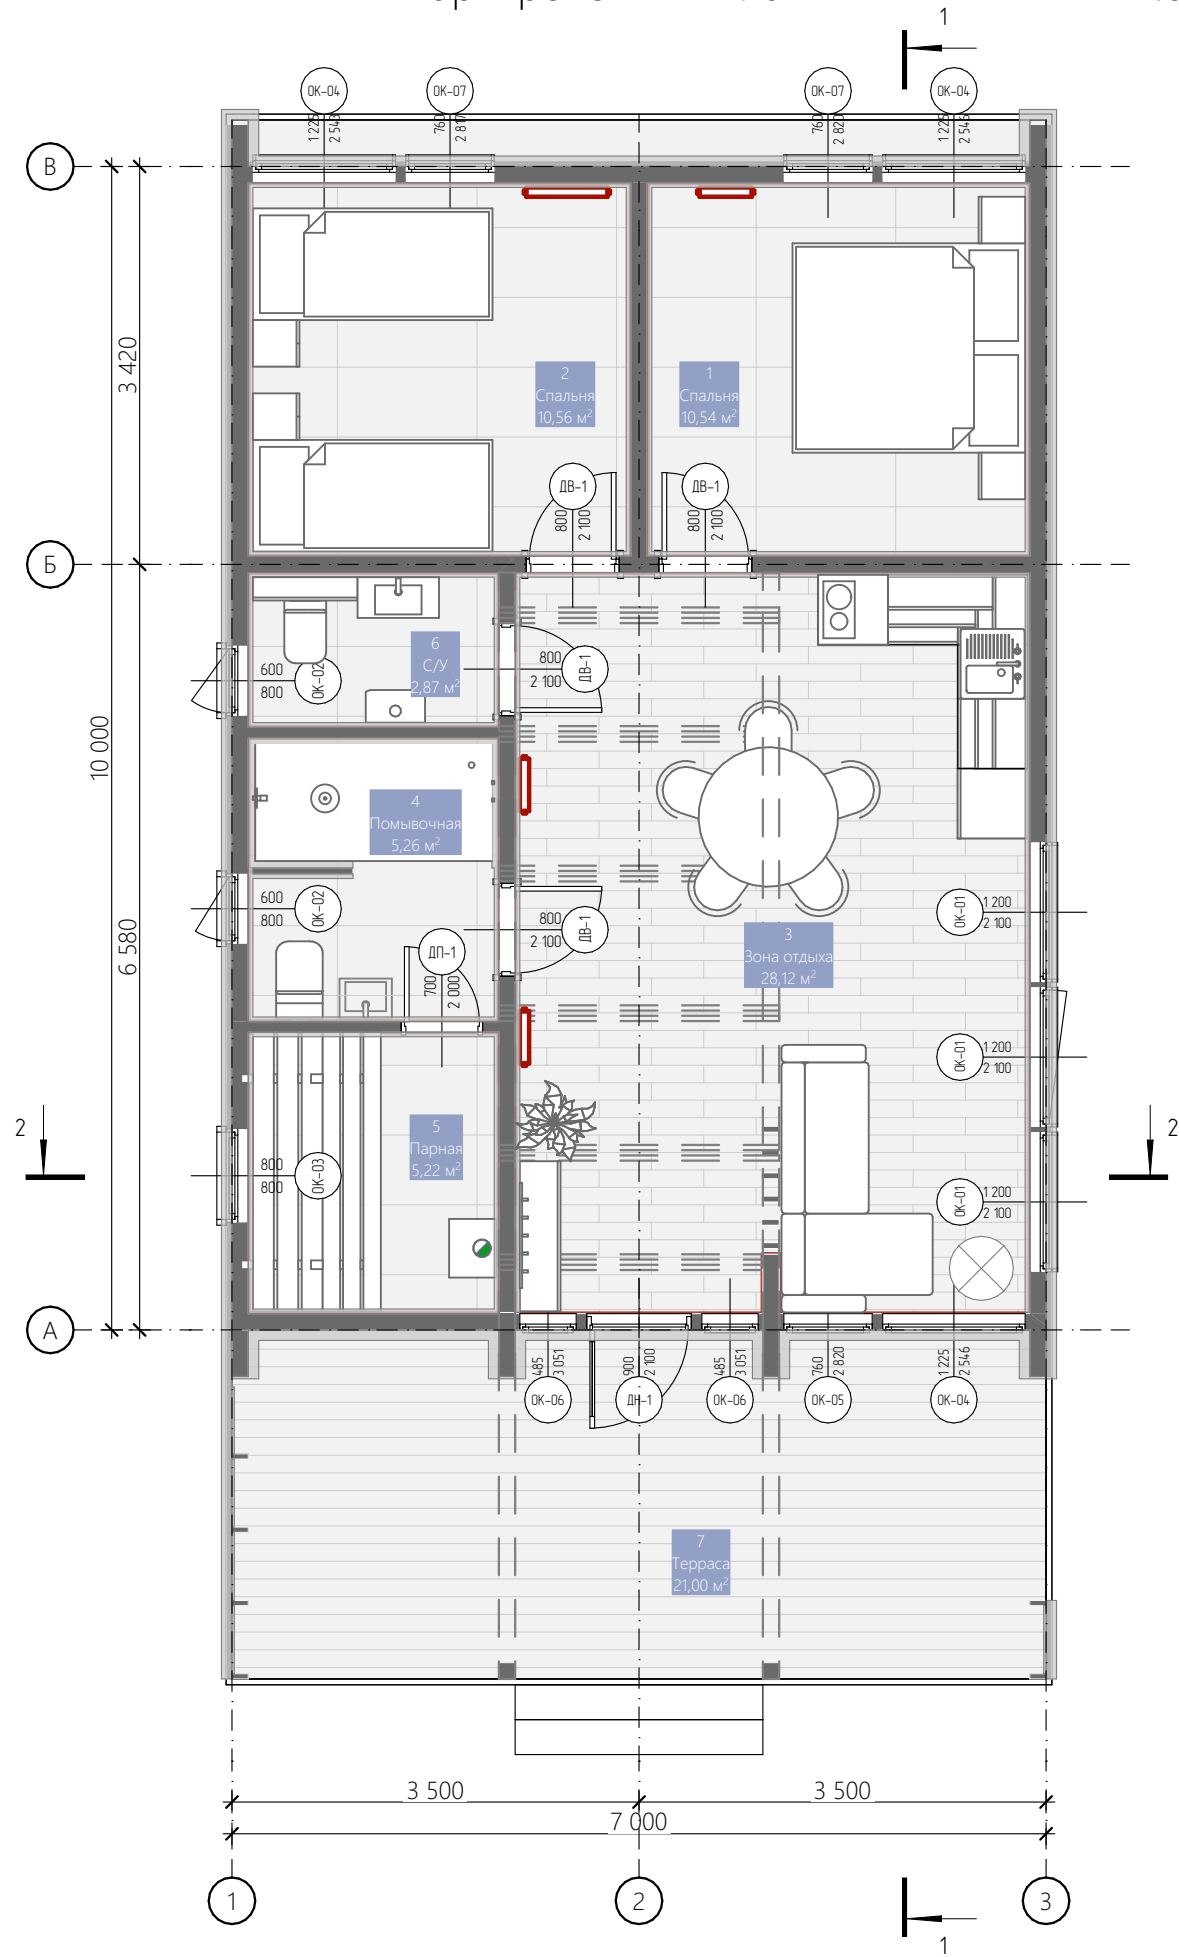

Экспликация помещений

№	Наименование	Площадь, кв. м.
1	Спальня	10,54
2	Спальня	10,56
3	Зона отдыха	28,12
4	Помывочная	5,26
5	Парная	5,22
6	С/У	2,87
7	Терраса	21,00
		83,57 м²

Наименование	Площадь, кв. м.
Площадь застройки	93,80

Примечание:

1. Вся индивидуальная мебель выполняется по отдельному проекту с детальной проработкой и калькуляцией. Чертежи предоставляет фирма-изготовитель столярных изделий.

2. Данный проект отдельно согласовывается с автором проекта и непосредственно с заказчиком.

3. Цветовое решение фасада и материалов отделки показаны в проекте приблизительно.

4. Количество ступеней показано условно.


Лист	Изм.	№ Докум.	Подп.	Дата

Адрес:

Маркировочный план

#Название Организации

1:65

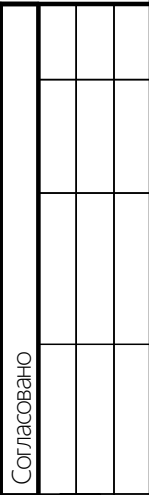

ИНВ. № подл.


Адрес:

#Название Организации

1. Представленные размеры
указаны без учета внешней и
внутренней отделки

ИСТ
5

1:65

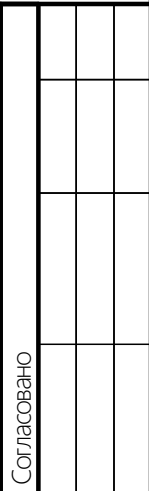

ИНВ. № подл.

6


2. Финальные размеры мебели и оборудования указаны ориентировочно — для точной компоновки требуется разработка дизайн-проекта.

Согласовано

Взам. инв. №

Подп. и дата

Инв. № подл.

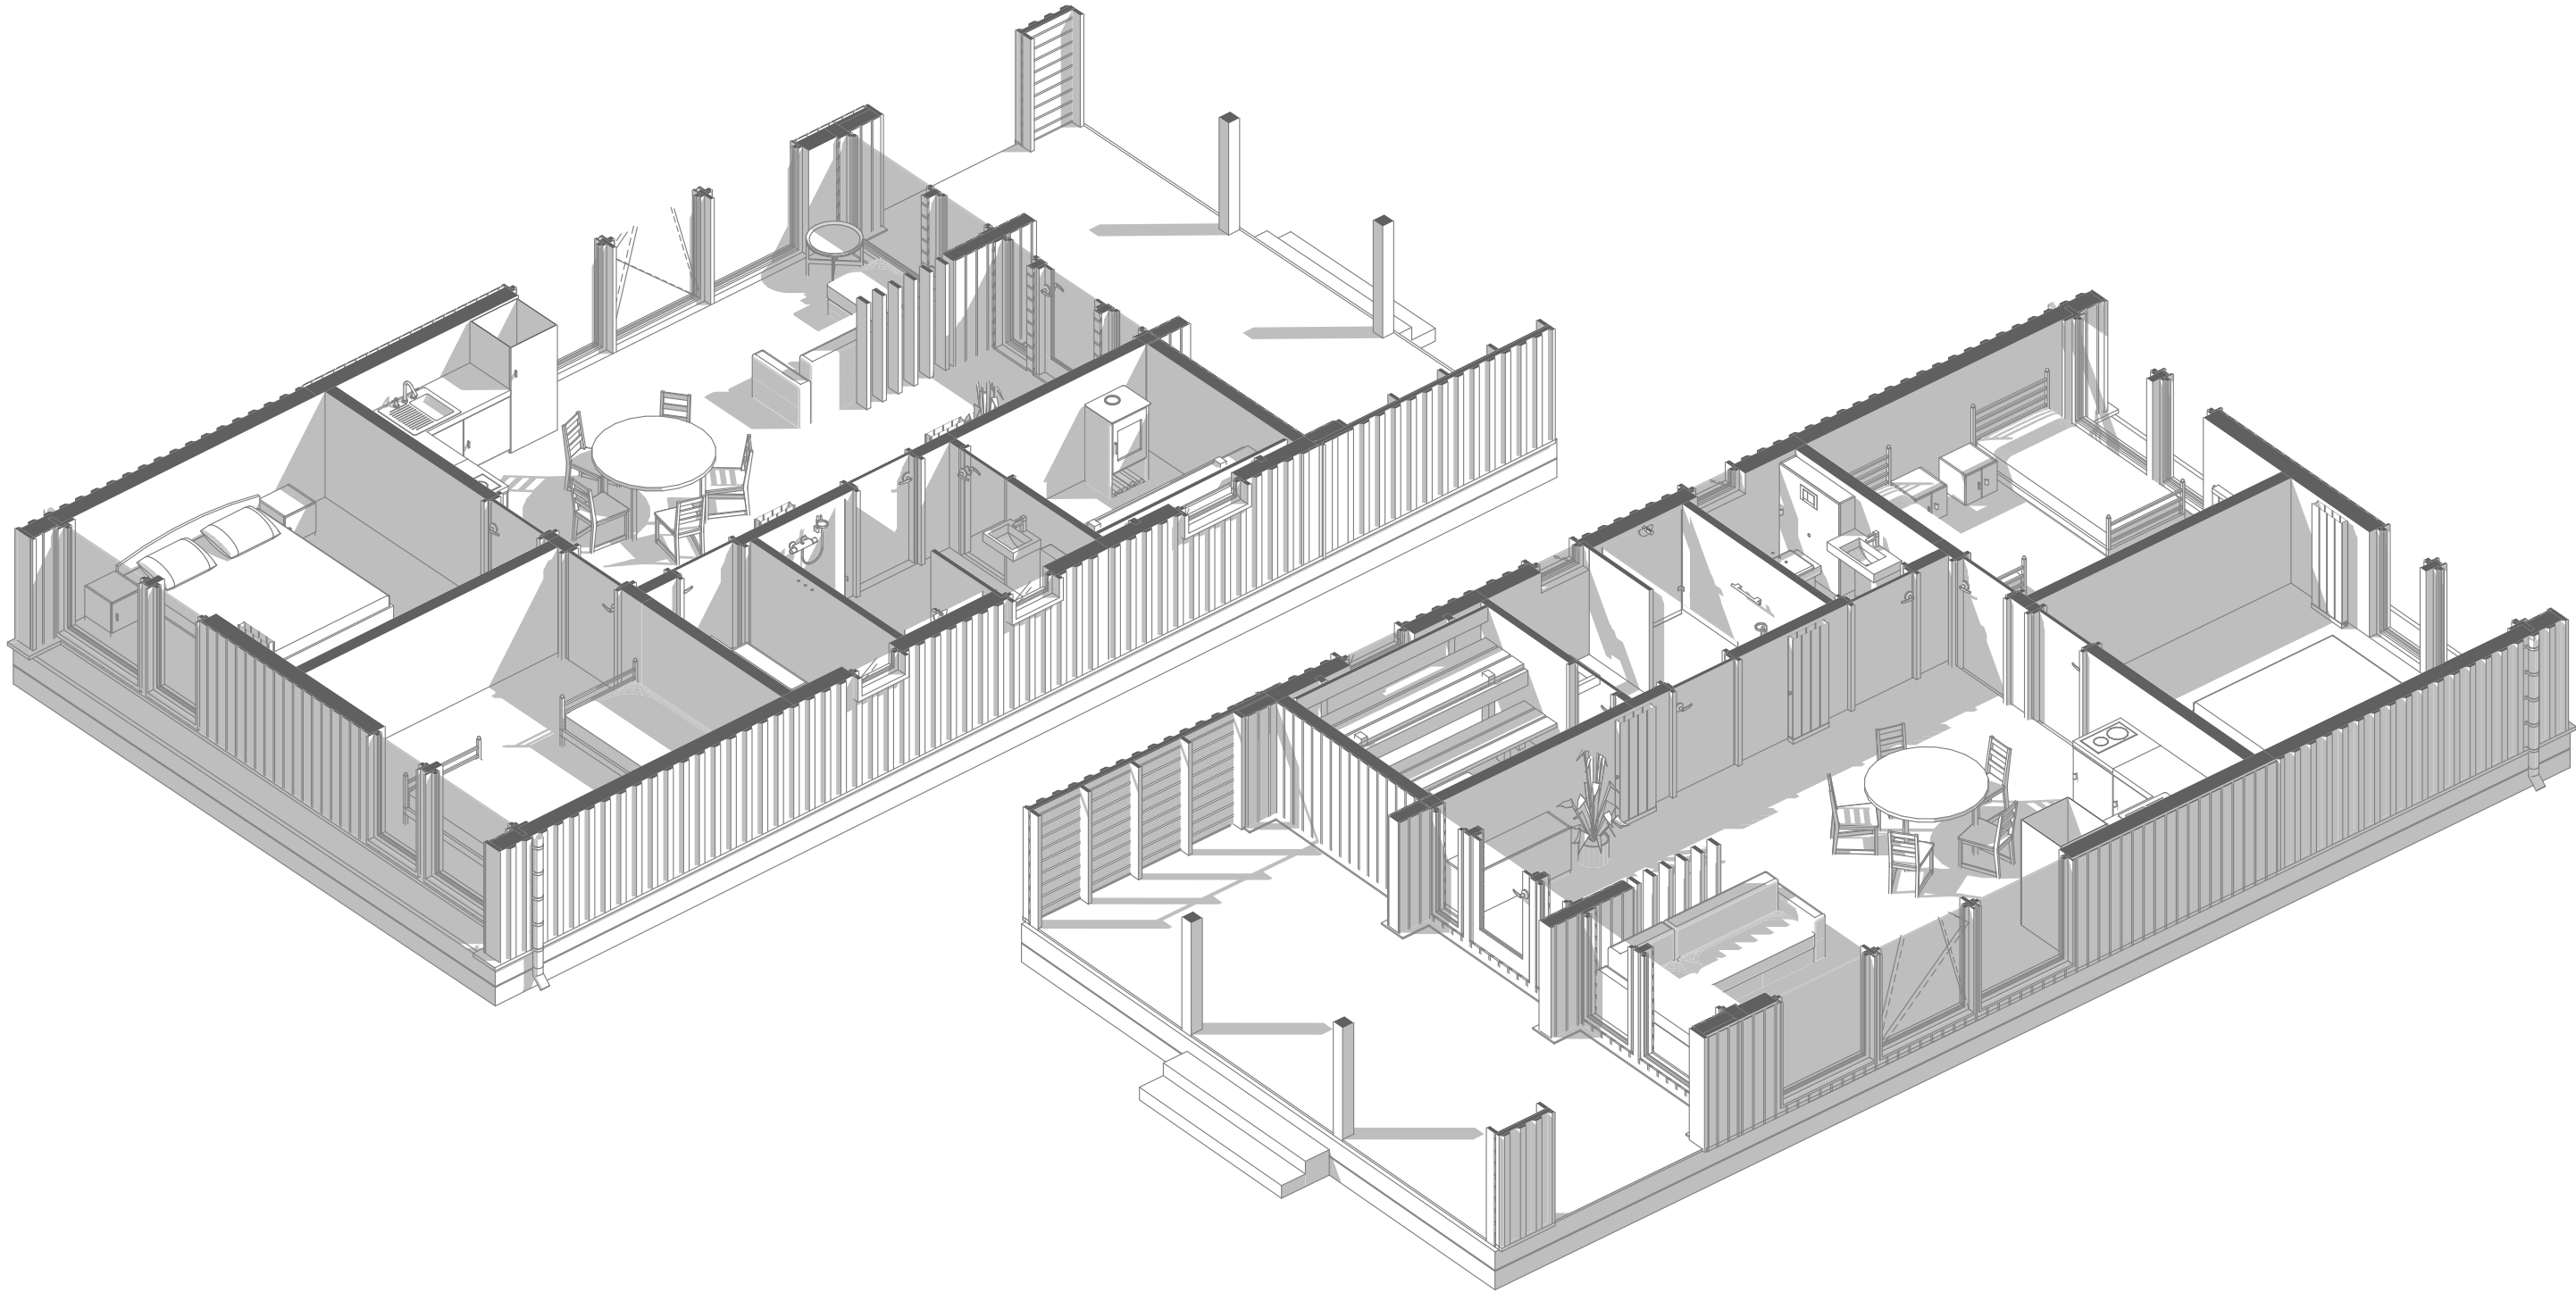


Лист	Изм.	№ Докум.	Подп.	Дата


Адрес:

Зд-разрез

#Название Организации

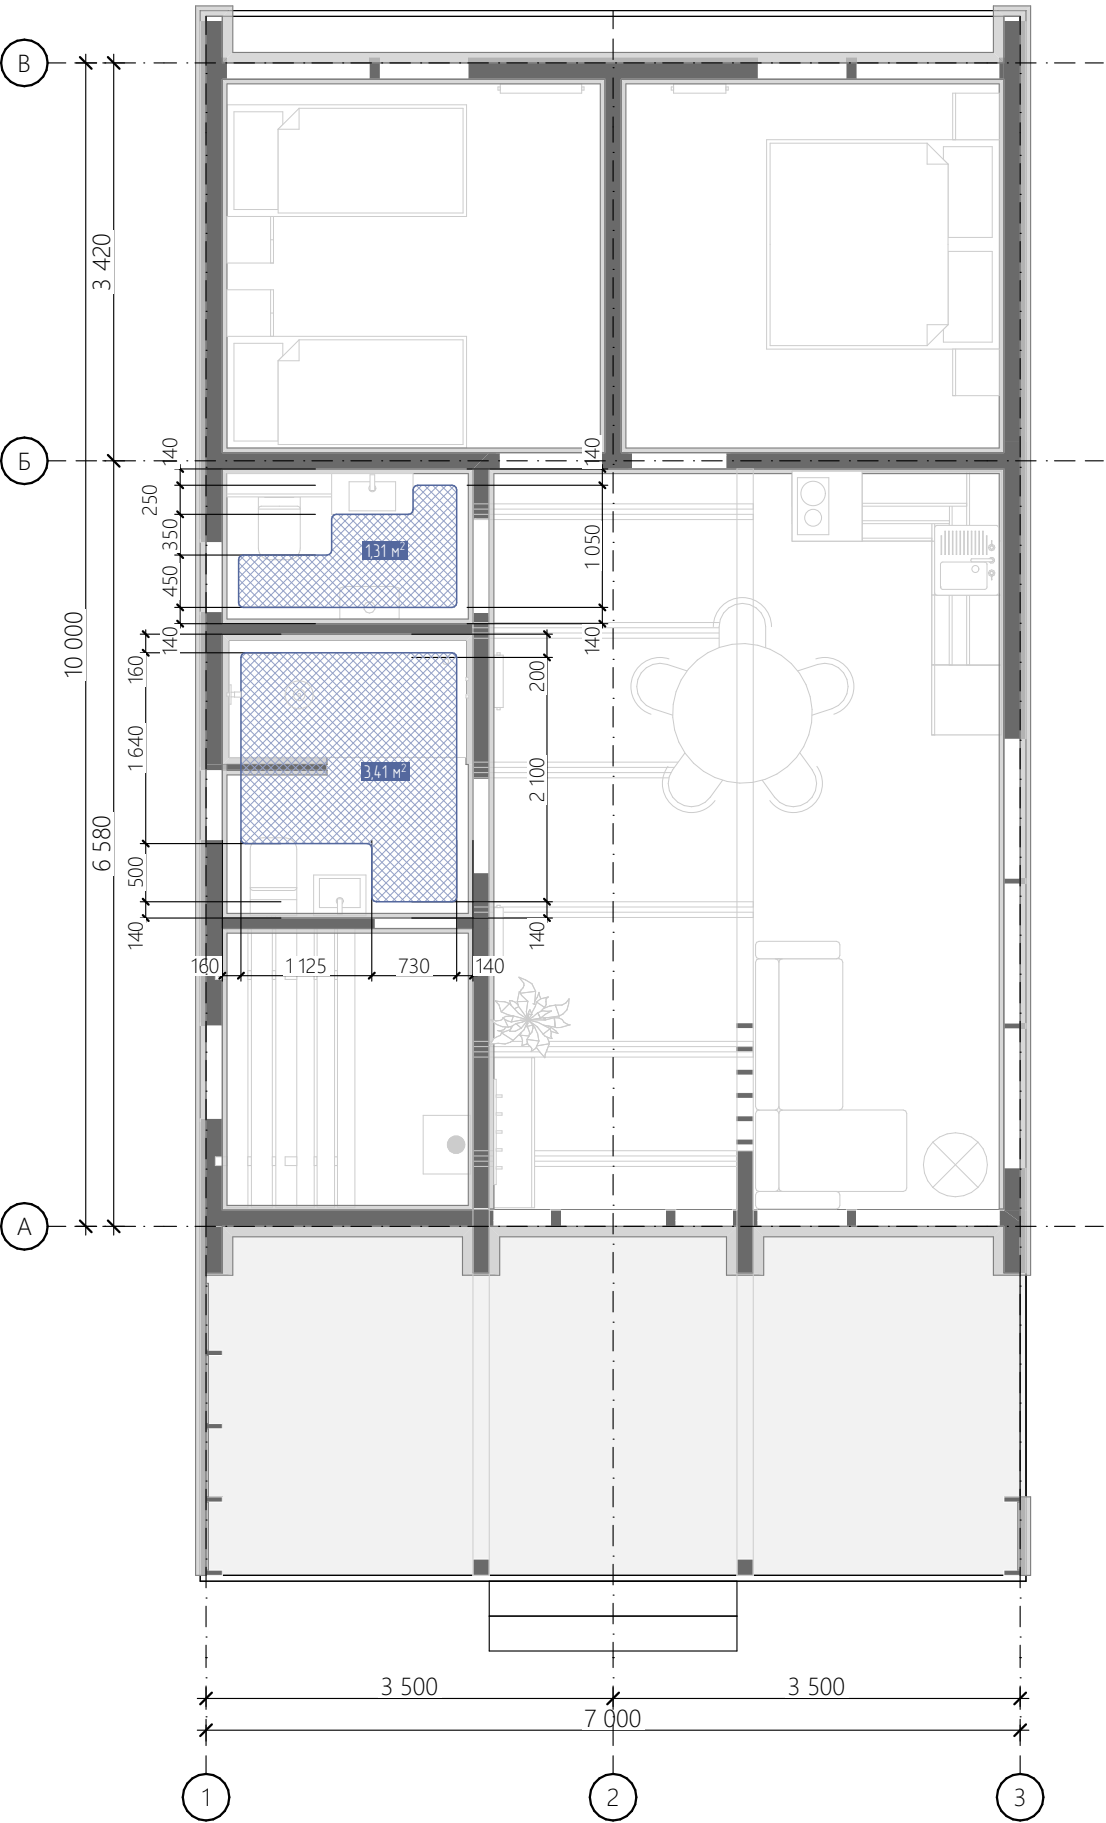

Условные обозначения

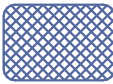 - Контур устройства
теплого пола

Экспликация теплого пола

Наименование зоны	Площадь, м2
Помывочная	3,41
С/У	1,31
4,72 м²	

Примечание:

1. Отображение носит схематичный характер. Фактическая реализация выполняется в соответствии с детальными проектными решениями инженерных сетей.

Согласовано				
И-нв. № подл.	Подп. и дата	Взам. инв. №		

Лист	Изм.	№ Докум.	Подп.	Дата

Адрес:

План водяного теплого пола

#Название Организации


Согласовано

И-нв. № подл.


Подп. и дата

Взам. инв. №

План покрытия пола1:65

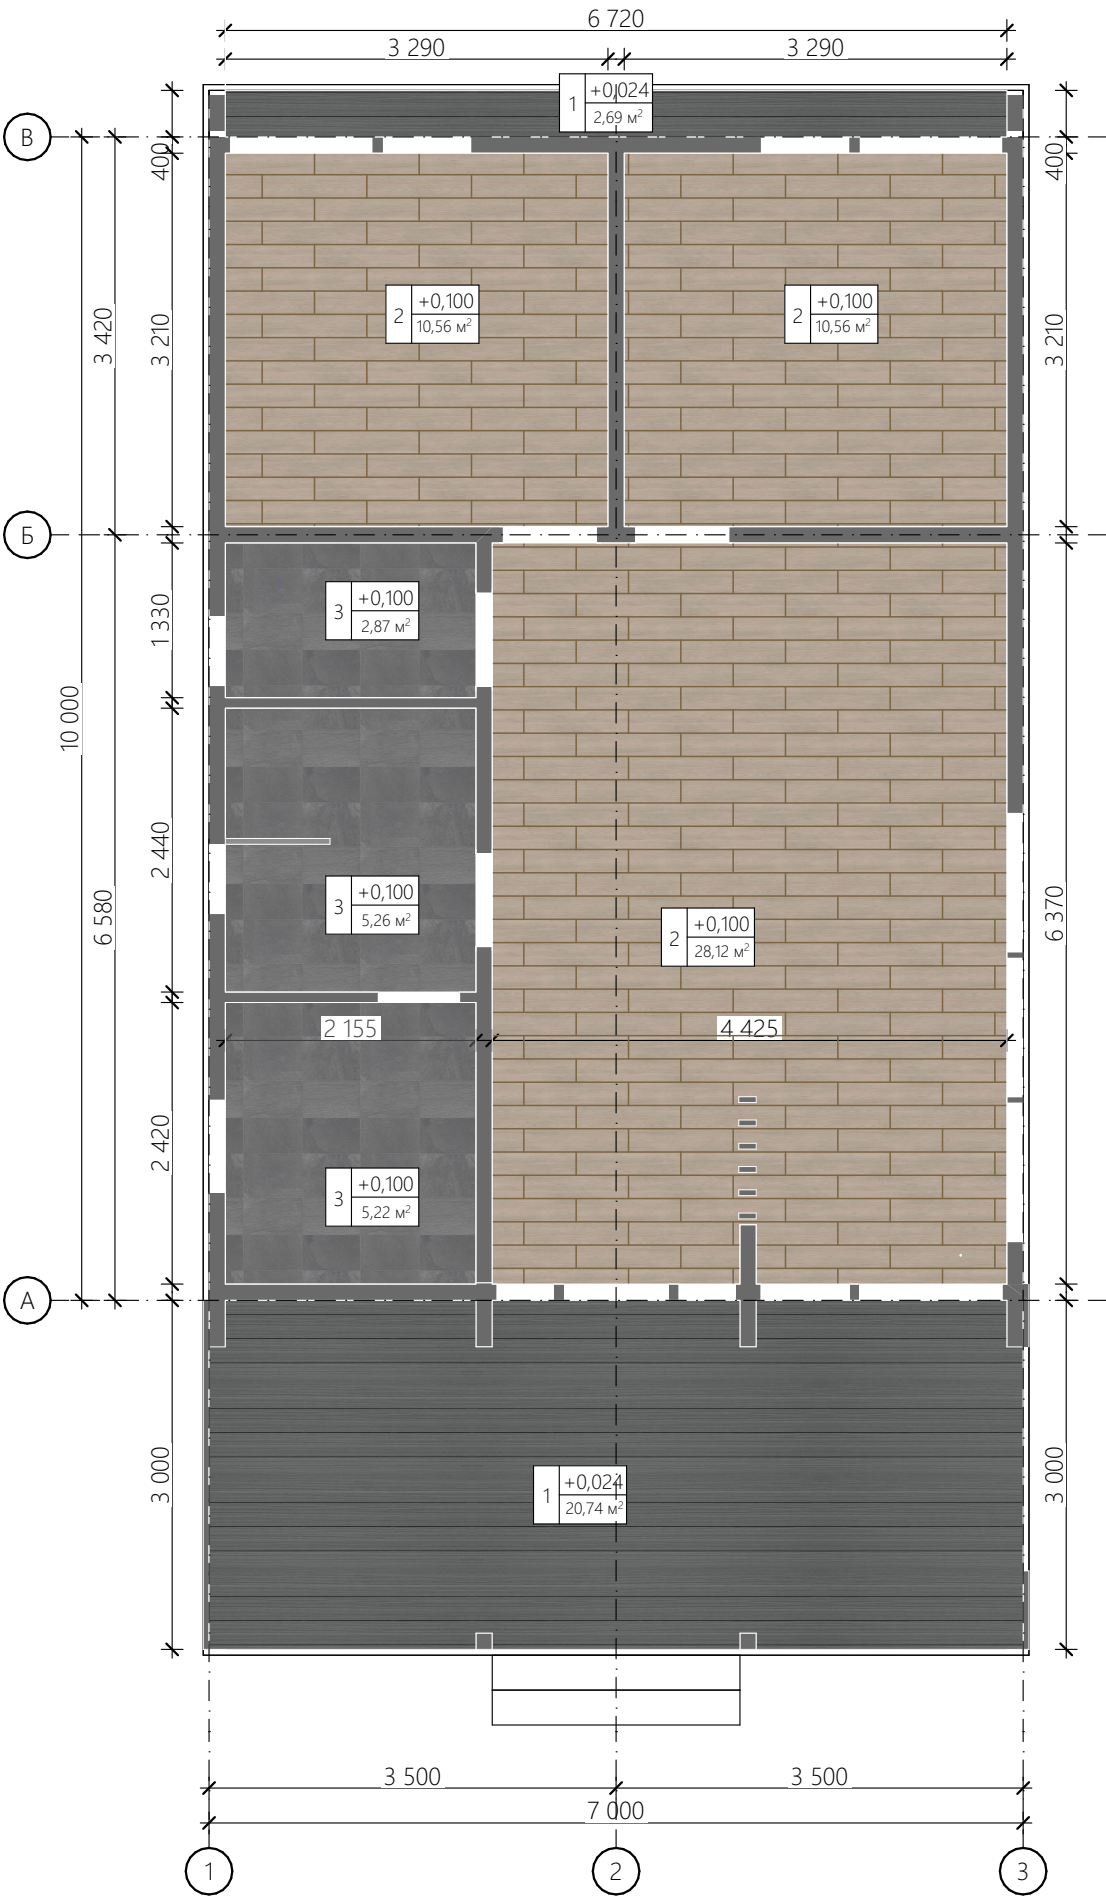

Условные обозначения

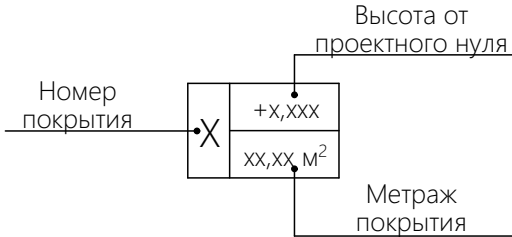

Ведомость покрытий пола

№	Наименование	м2
1	ДПК- террасная доска	39,21
2	ламинат	54,45
3	керамогранит	16,22

Примечание:

1. Приведённые цветовые решения носят рекомендательный характер. Фактический подбор оттенков и материалов выполняется на этапе реализации с учётом наличия продукции у поставщиков и утверждения заказчиком.

2. Пирог покрытия смотреть на след. листе.




Лист	Изм.	№ Докум.	Подп.	Дата

Адрес:

План покрытий пола

#Название Организации

Экспликация покрытий пола

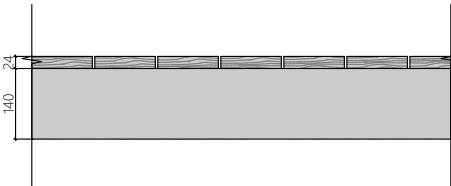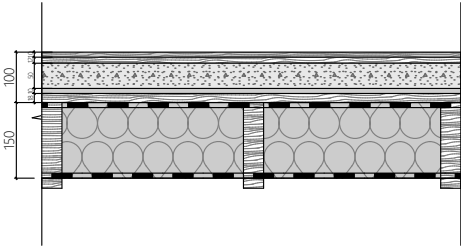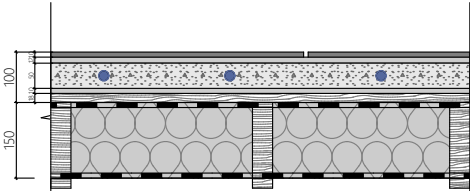№	Наименование	Разрез	Состав
1	Террасная доска		-Террасная доска 24мм -Лага, доска 140х45мм 140 мм
2	Ламинат		-Ламинат 10мм -Подложка под ламинат 10мм -Полусухая цементно-песчаная стяжка 50мм -ЦСП 10мм -ОСБ 18мм
3	Керамогранит		-Керамогранит 10мм -Клей 10мм -Полусухая цементно-песчаная стяжка (с устройством теплого водяного пола) 50мм -ЦСП 10мм -ОСБ 18мм

Согласовано				


Индв. № подл.	Подп. и дата	Взам. инв. №

Лист	Изм.	№ Докум.	Подп.	Дата	Экспликация покрытий пола	#Название Организации	Лист
							10

Согласовано				
Инв. № подл.	Подп. и дата	Взам. инв. №		

Лист	Изм.	№ Докум.	Подп.	Дата

Адрес:

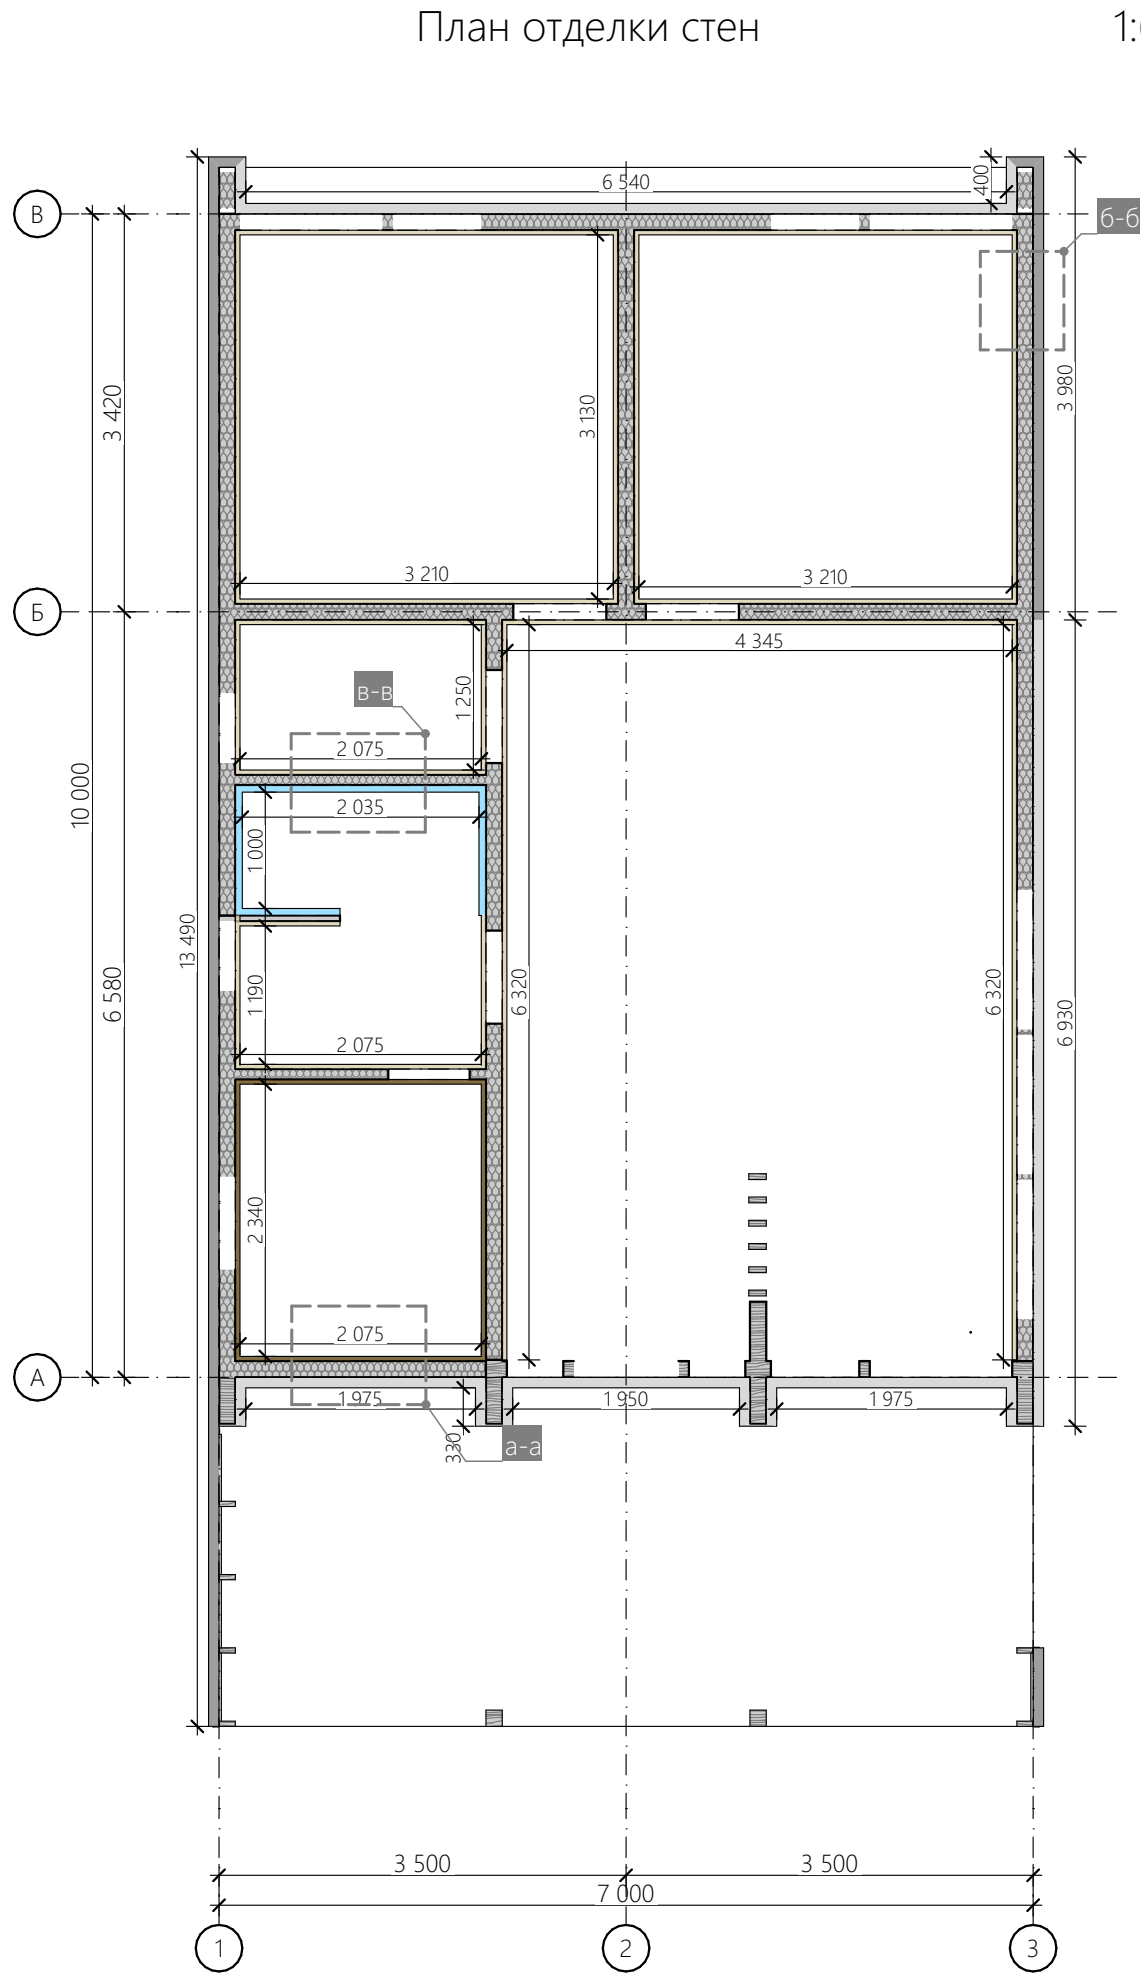

План покрытия отделки стен

Ведомость покрытий стен		
№	Наименование	Условное обозначение
1	Планкен (20мм)	
2	Профлист	
3	Имитация бруса (20мм)	
4	Вагонка (16мм)	
5	Керамогранит (10мм)	
Примечание: 1. Сечение по стенам смотреть на след. листе		
#Название Организации		Лист
		11


Экспликация отделки стен

№ разреза

Сечение


Состав

а-а

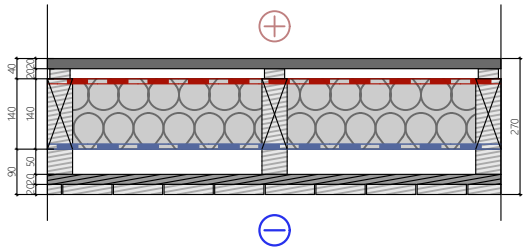


-Вагонка	20мм
-Обрешётка	20мм
-Пароизоляционная мембрана (алюминиевая фольга)	
-Стойка каркаса (утеплённая)	140мм
-Гидро-ветрозащитная мембрана	
-Вентбрусок (вертикально)	50мм
-Обрешётка	20мм
-Планкен	20мм

б-б

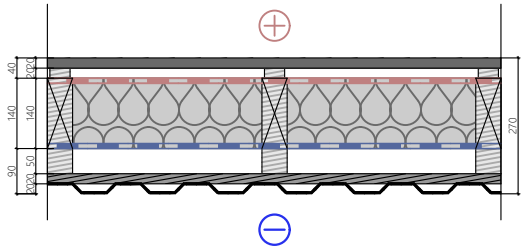

-Имитация бруса	20мм
-Вентбрусок (вертикально)	20мм
-Пароизоляционная мембрана	
-Стойка каркаса (утепленная)	140мм
-Гидро-ветрозащитная мембрана	
-Вентбрусок (вертикально)	50мм
-Обрешётка	20мм
-Профлист	

в-в

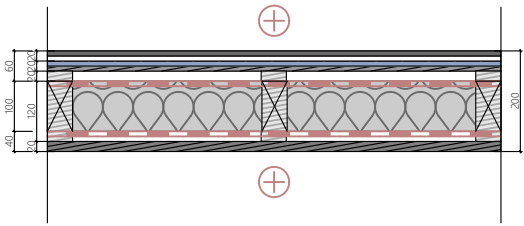

-Керамогранит	10мм
-Клей	10мм
-Руспанель	10мм
-ОСБ	9мм
-Обрешётка	20мм
-Пароизоляционная мембрана	
-Стойка каркаса (утепленная)	90мм
-Пароизоляционная мембрана	
-Вентбрусок (вертикально)	20мм
-Имитация бруса	20мм

Согласовано

Взам. инв. №

Подп. и дата

Инв. № подл.

Лист	Изм.	№ Докум.	Подп.	Дата

Экспликация отделки стен


#Название Организации

Лист

12

Условные обозначения:

-  - розетка 220V с заземлением
-  - розетка 220V с заземлением и влагозащитой
-  - розетка для ТВ
-  - интернет - розетка
-  - электровывод

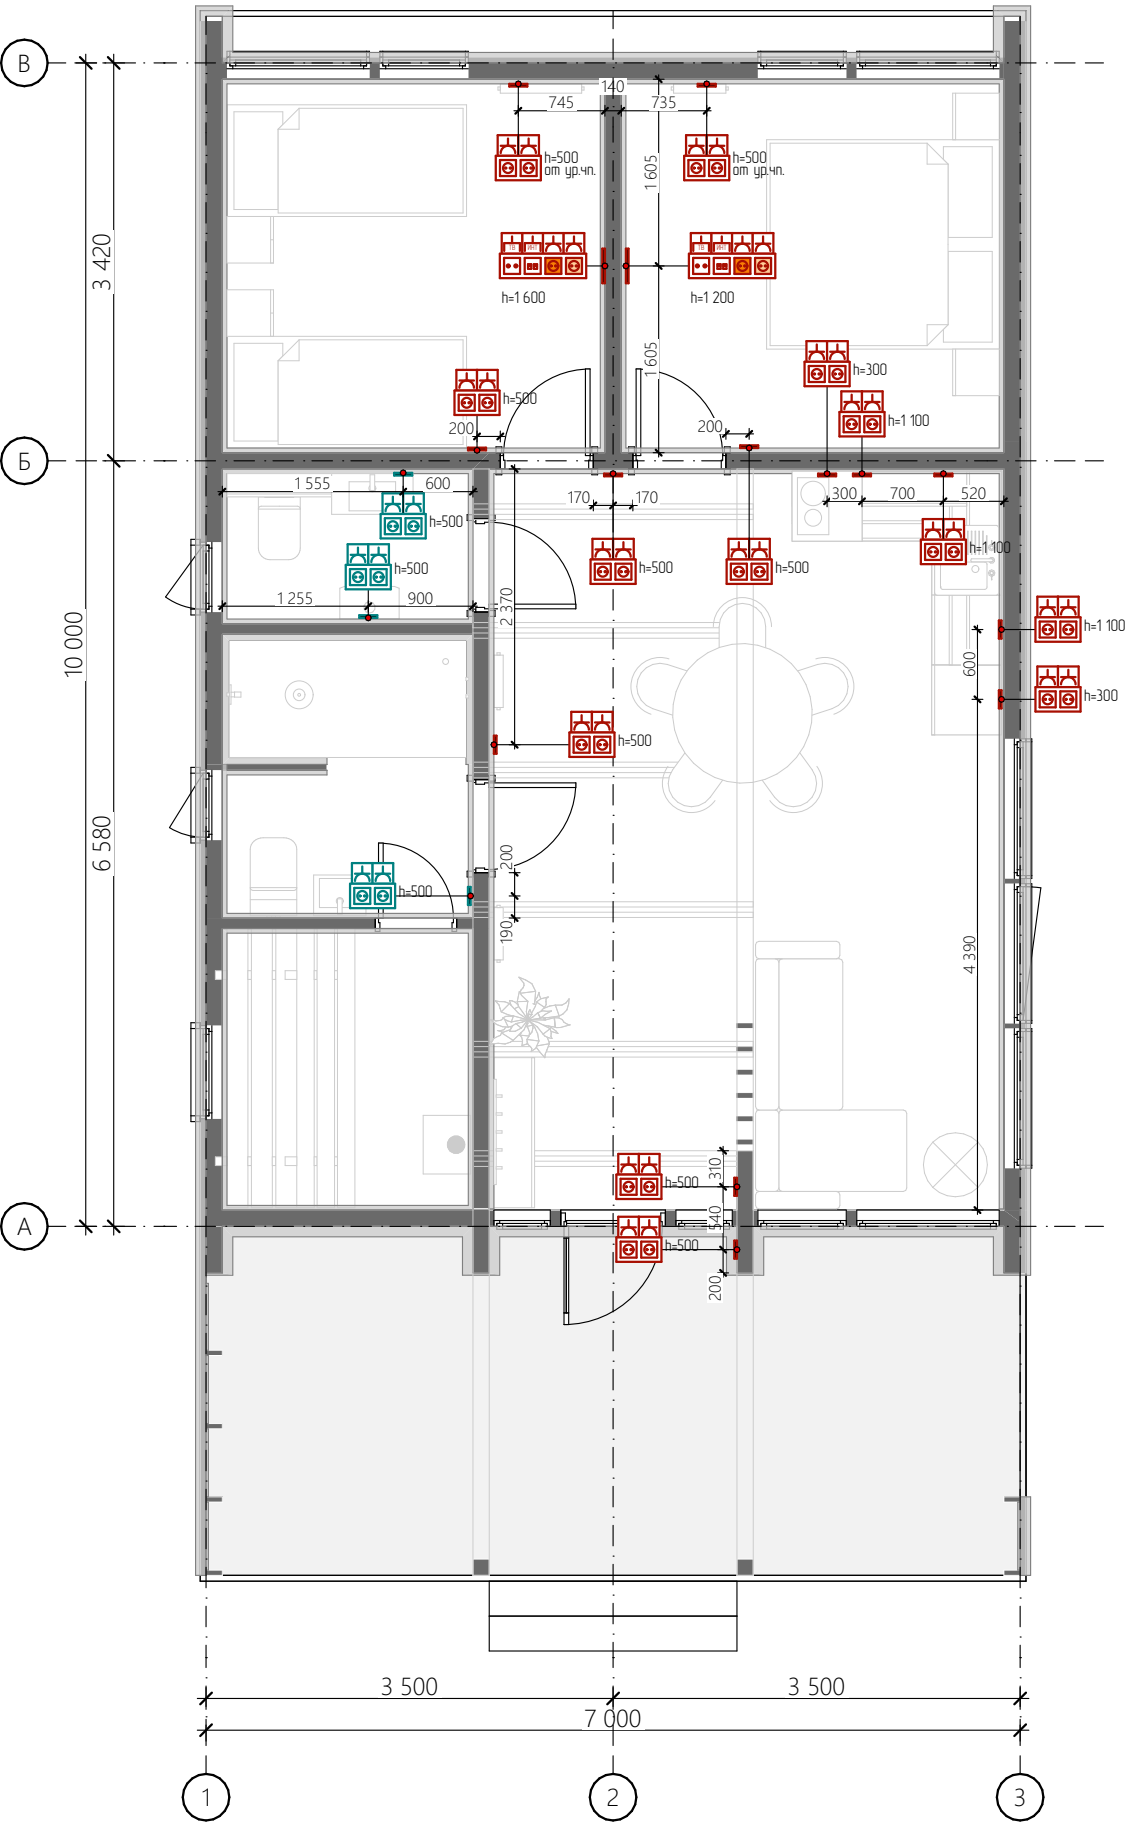

Примечание:

1. Схема размещения розеток является рекомендательной и требует согласования с заказчиком по месту.
2. Все высоты даны от чистового пола.
3. Все указанные размеры даются до центра позиций.
4. Отметки розеток, выключателей, выводов и др. оборудования, являются предварительными и уточняются после выбора финишных материалов и мебели.
5. Размеры уточняются дополнительно

Согласовано				
И-нв. № подл.	Подп. и дата	Взам. инв. №		


Лист	Изм.	№ Докум.	Подп.	Дата


Адрес:

План размещения розеток
стен

#Название Организации

Условные обозначения:

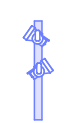-  - выключатель одноклавишный
-  - выключатель двухклавишный
-  - люстра
-  - точечный светильник
-  - настенные бра
-  - контурная подсветка
-  - трековый светильник

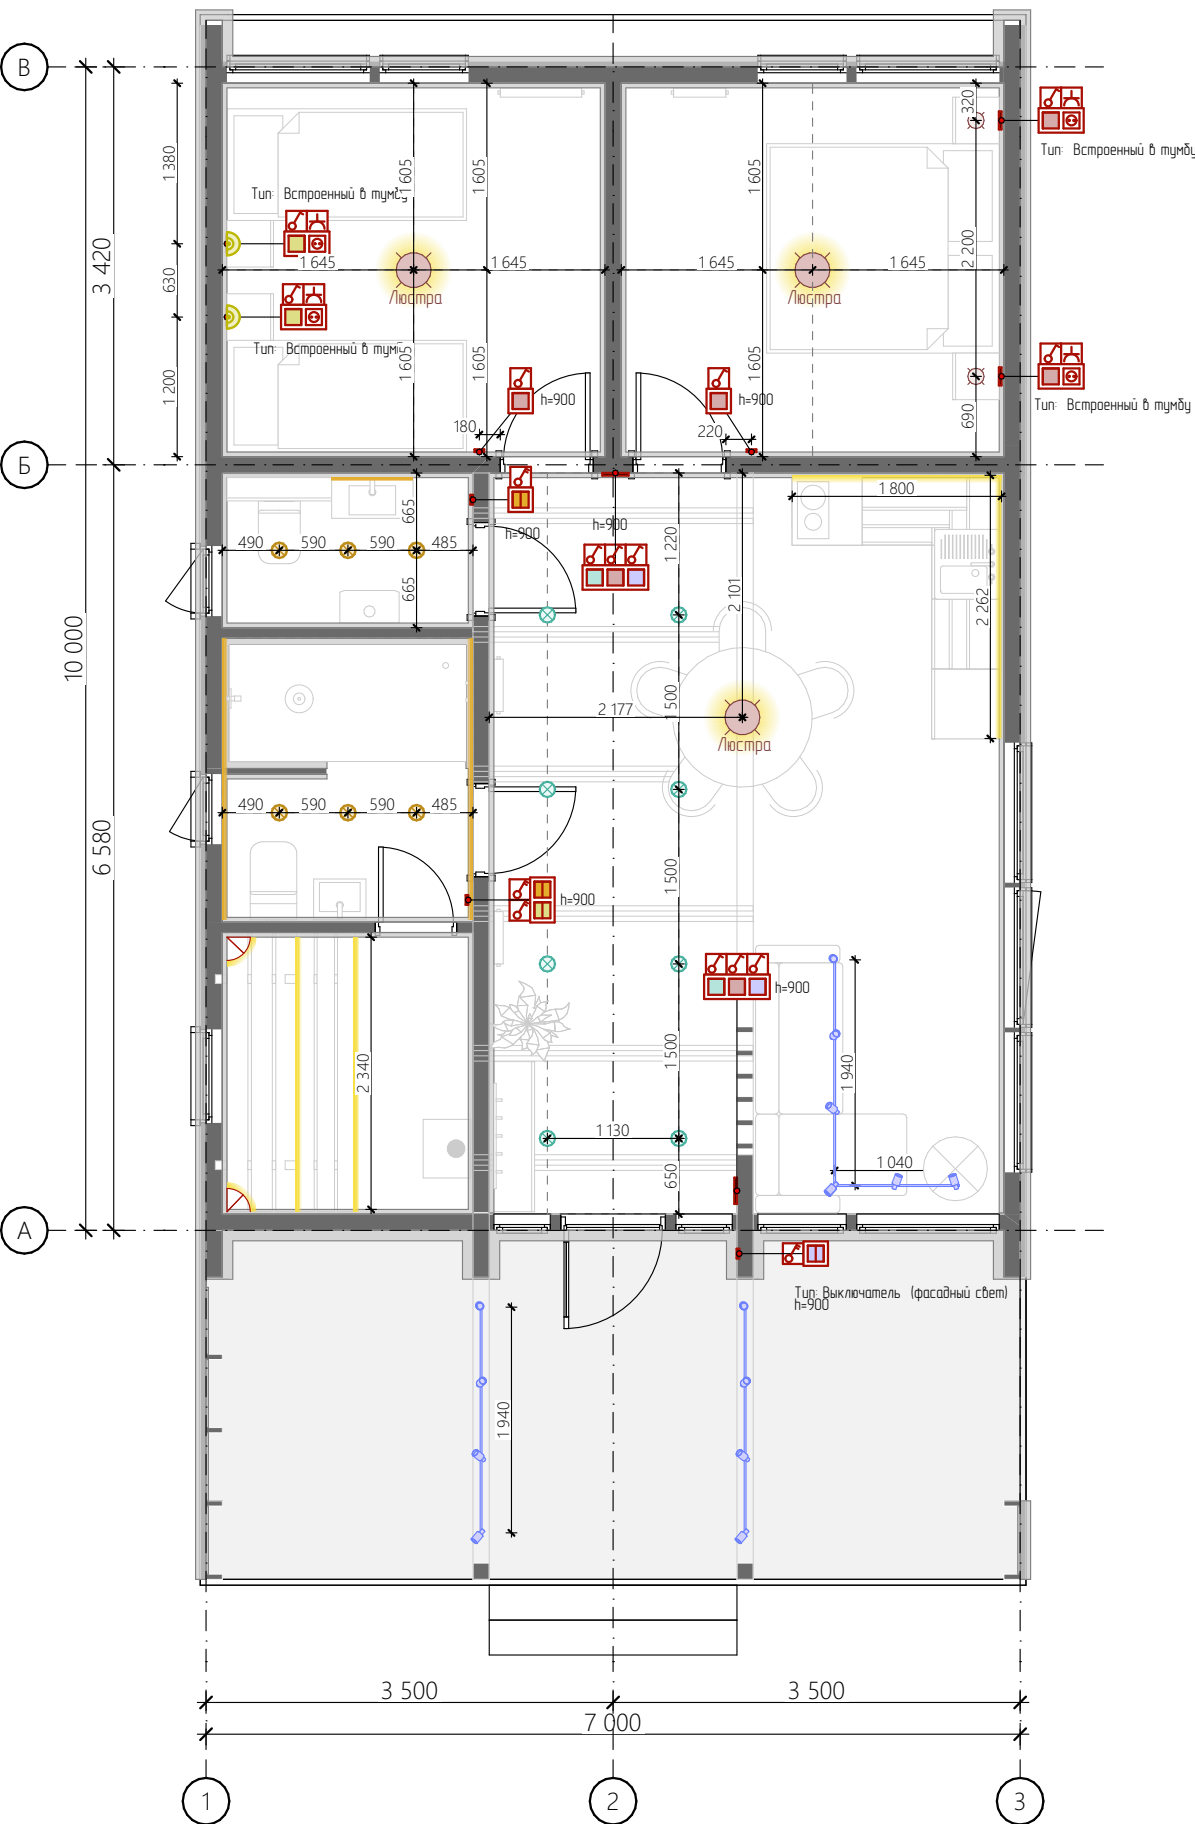

Примечание:

1. Схема размещения розеток является рекомендательной и требует согласования с заказчиком по месту.
2. Все высоты даны от чистового пола.
3. Все указанные размеры даются до центра позиций.
4. Отметки розеток, выключателей, выводов и др. оборудования, являются предварительными и уточняются после выбора финишных материалов и мебели.
5. Размеры уточняются дополнительно

Согласовано				
И-нв. № подл.	Подп. и дата	Взам. инв. №		

Лист	Изм.	№ Докум.	Подп.	Дата


Адрес:

План расстановки
светильников и
выключателей


#Название Организации

Условные обозначения:

- Кровля бани
- Подшив свесов бани

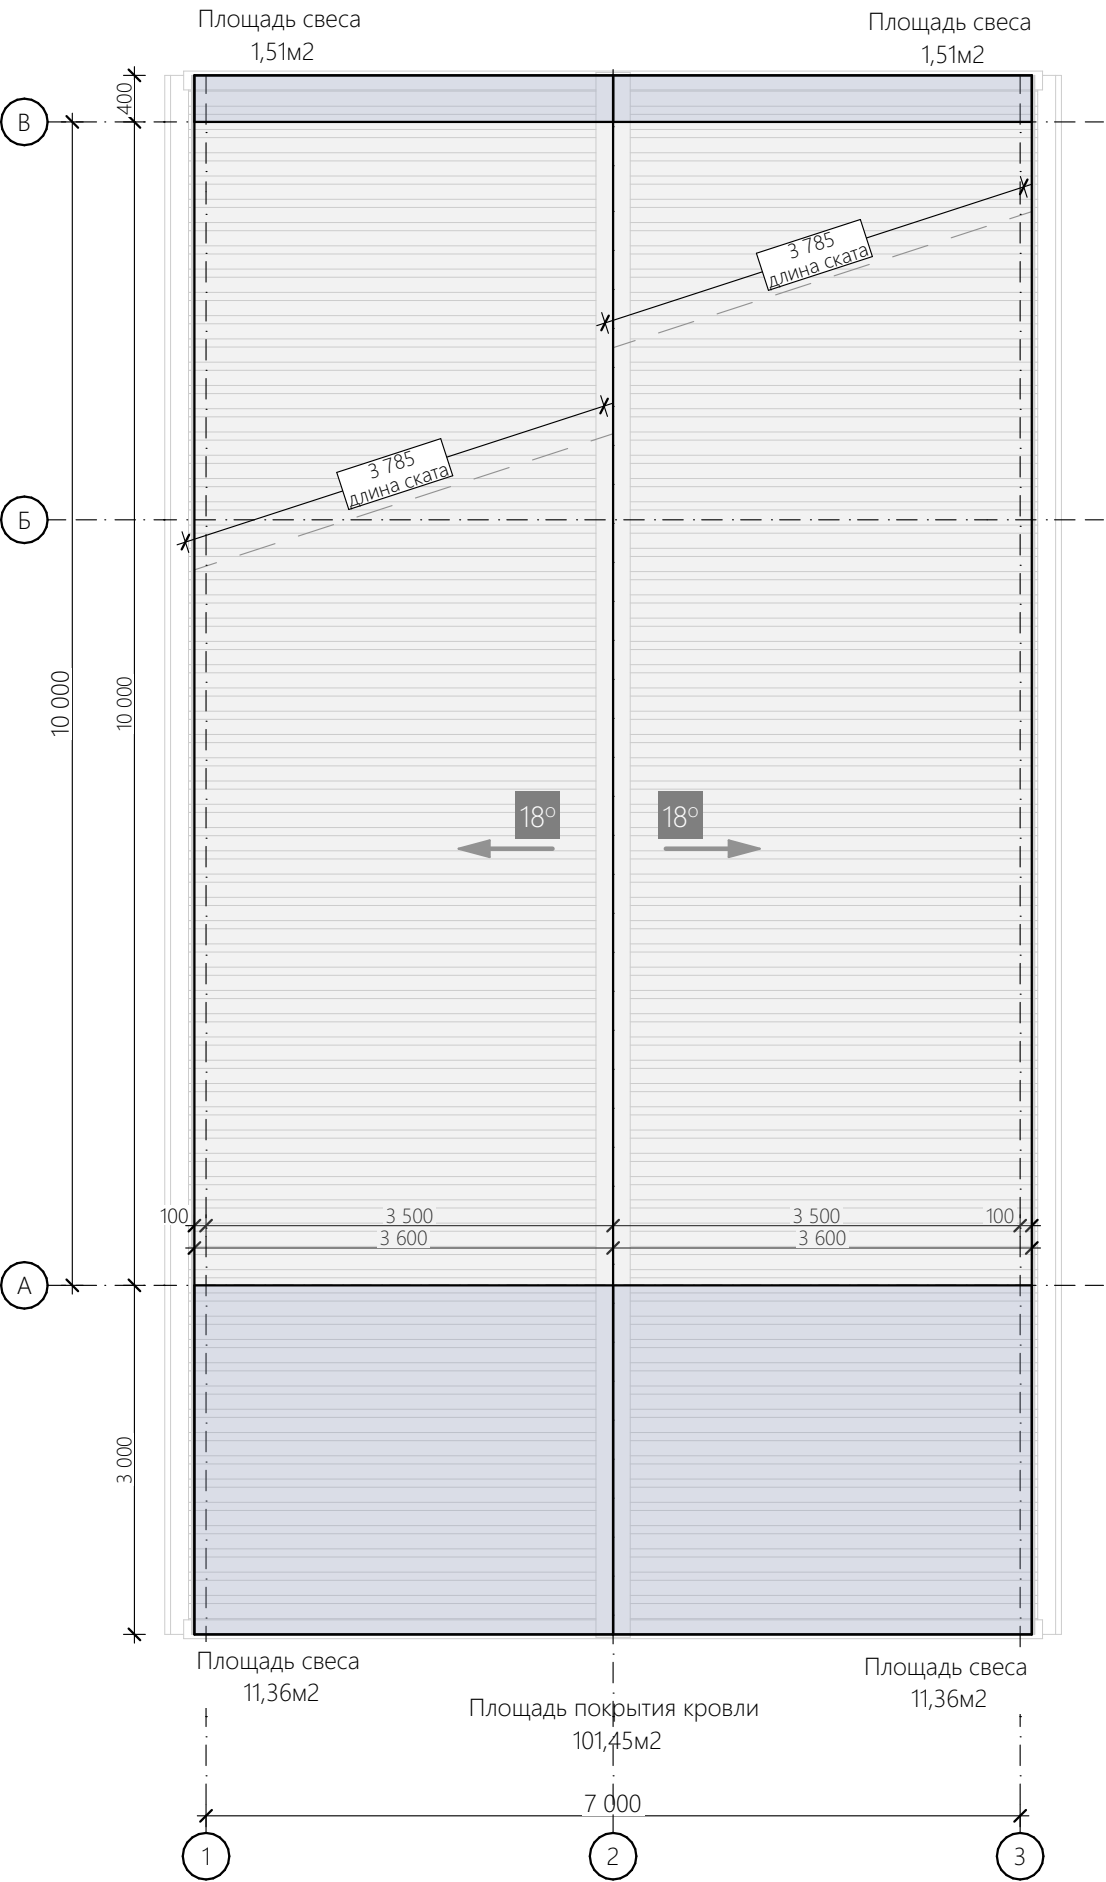

аксонометрия кровли:

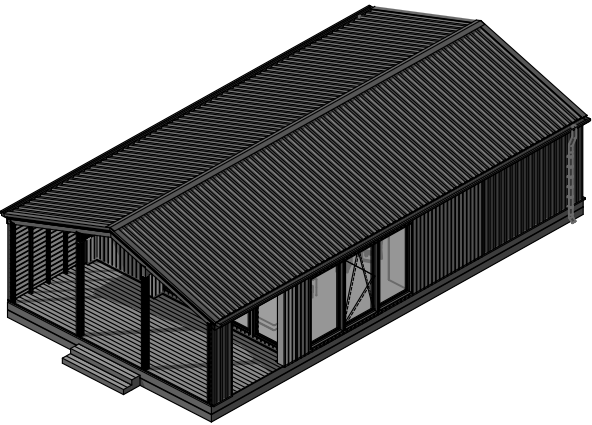

Согласовано				

И-нв. № подл.	Подп. и дата	Взам. инв. №	

Лист	Изм.	№ Докум.	Подп.	Дата


Адрес:

План кровли

#Название Организации

ЛИСТ


16

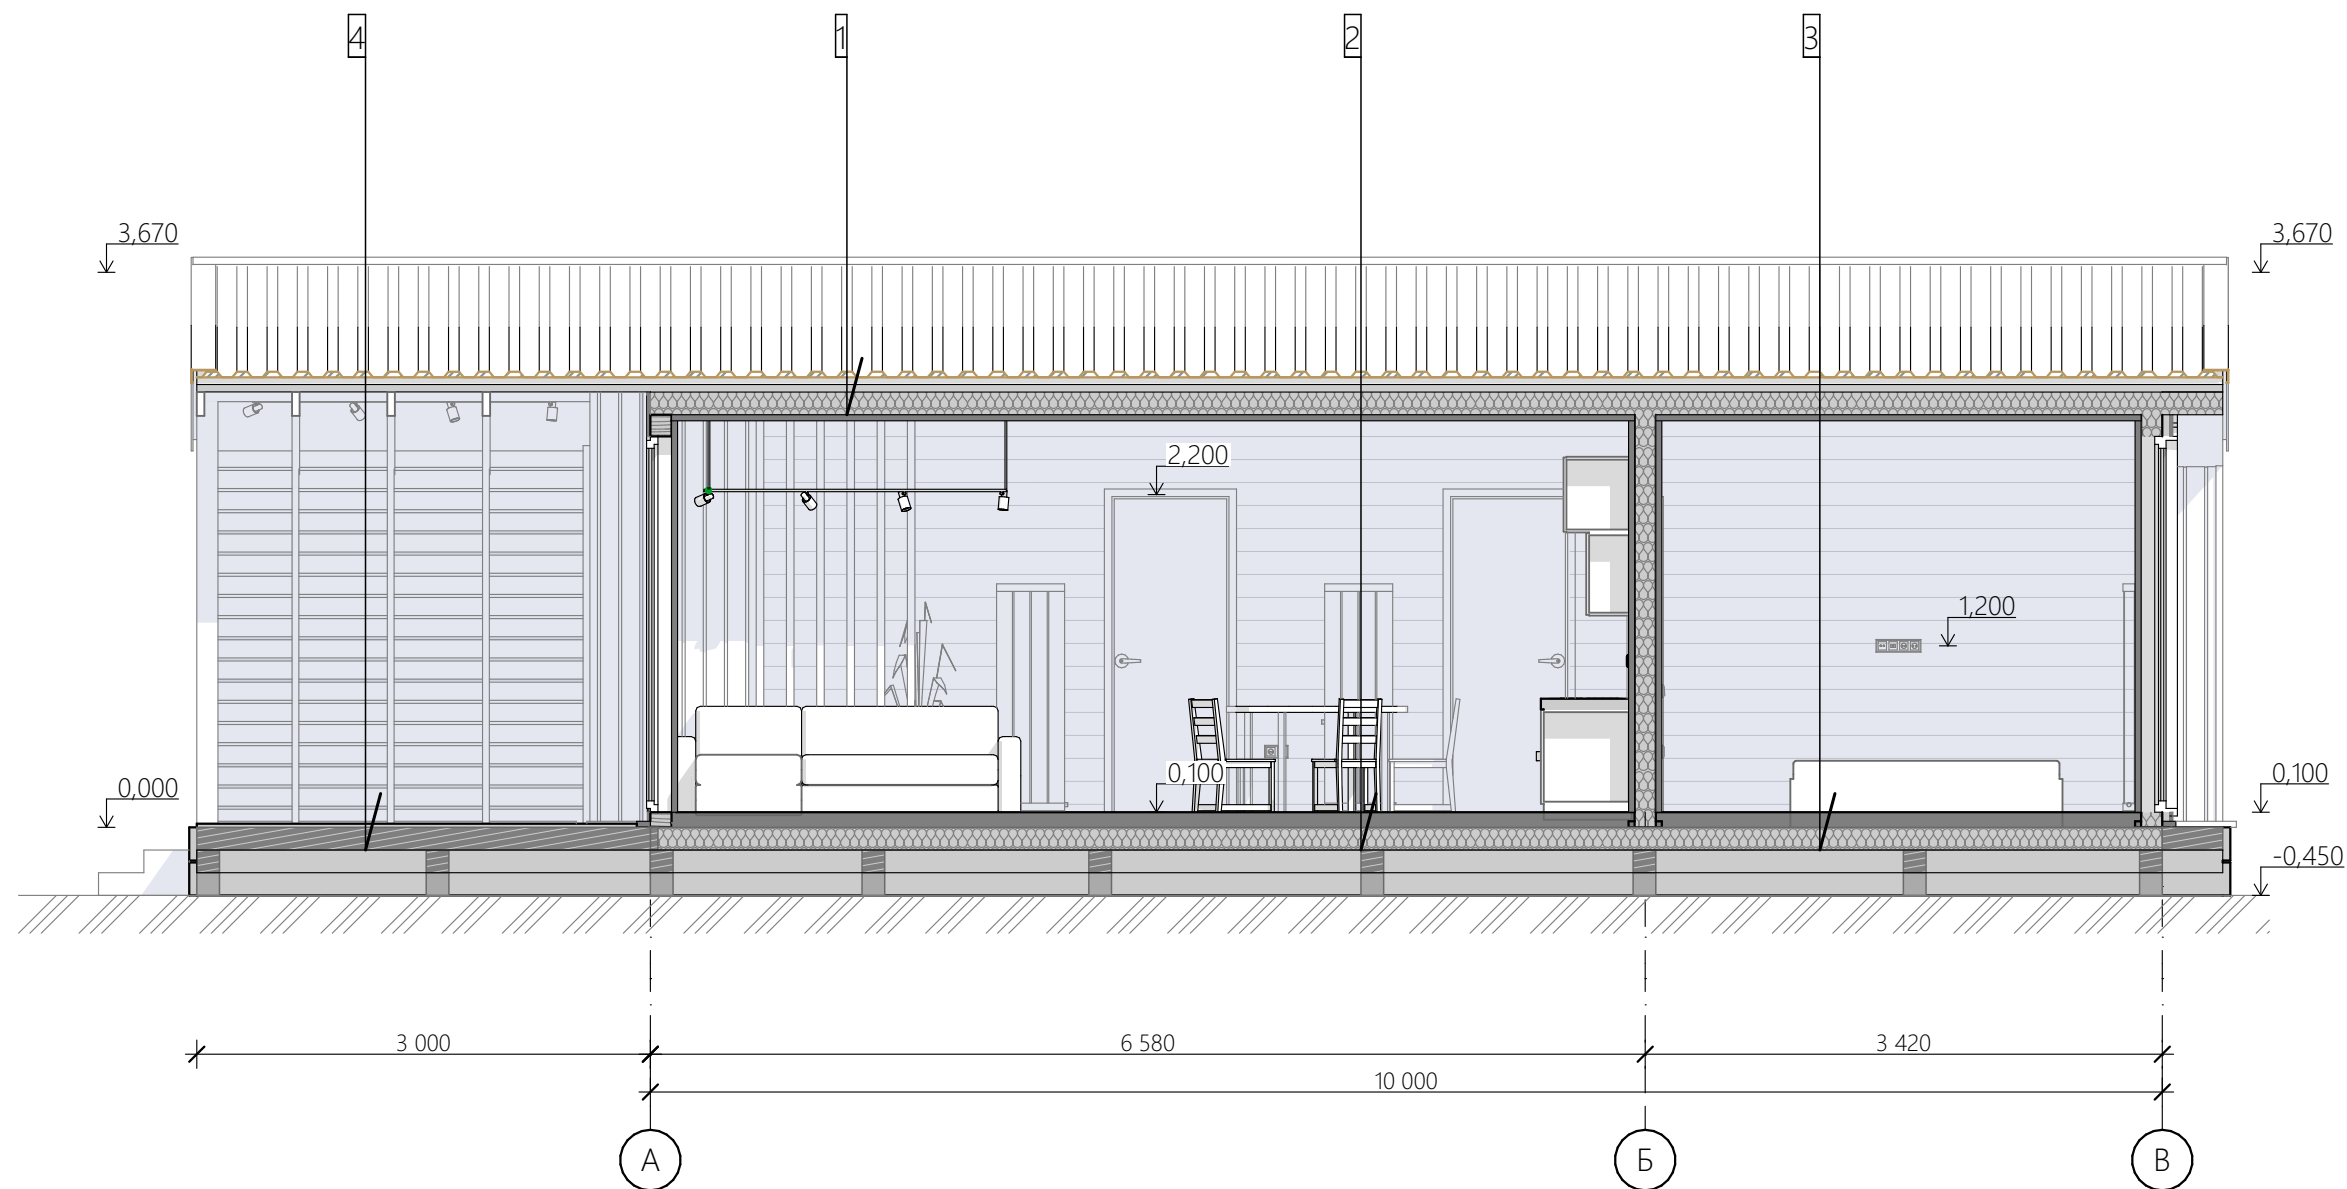

1	-Профлист	C-35
	-Обрешётка	25x100мм
	-Контробрешётка	50x50мм
	-Гидроветрозашитная мембрана	
	-Стропильная система	190x45мм
	утепленная	
	-Пароизоляционная мембрана	
	-Обрешётка	20мм
	-Имитация бруса	20мм
2	-Ламинат	10мм
	-Подложка под ламинат	10мм
	-Полусухая цементно-песчаная стяжка	50мм
	-ЦСП	10мм
	-ОСБ	18мм
	-Пароизоляционная мембрана	
	-Лаги перекрытия (утепл.)	140мм
	-Гидроветрозашитная мембрана	
	-Просечка (сетка яч. 5x5)	
	-Обрешётка	20мм
3	-Ламинат	10мм
	-Подложка под ламинат	10мм
	-Полусухая цементно-песчаная стяжка	50мм
	-ЦСП	10мм
	-ОСБ	18мм
	-Пароизоляционная мембрана	
	-Лаги перекрытия (утепл.)	140мм
	-Гидроветрозашитная мембрана	
	-Просечка (сетка яч. 5x5)	
	-Обрешётка	20мм
4	-Террасная доска	24мм
	-Лага, доска 140x45мм	140 мм

Разрез 2-2

1:40

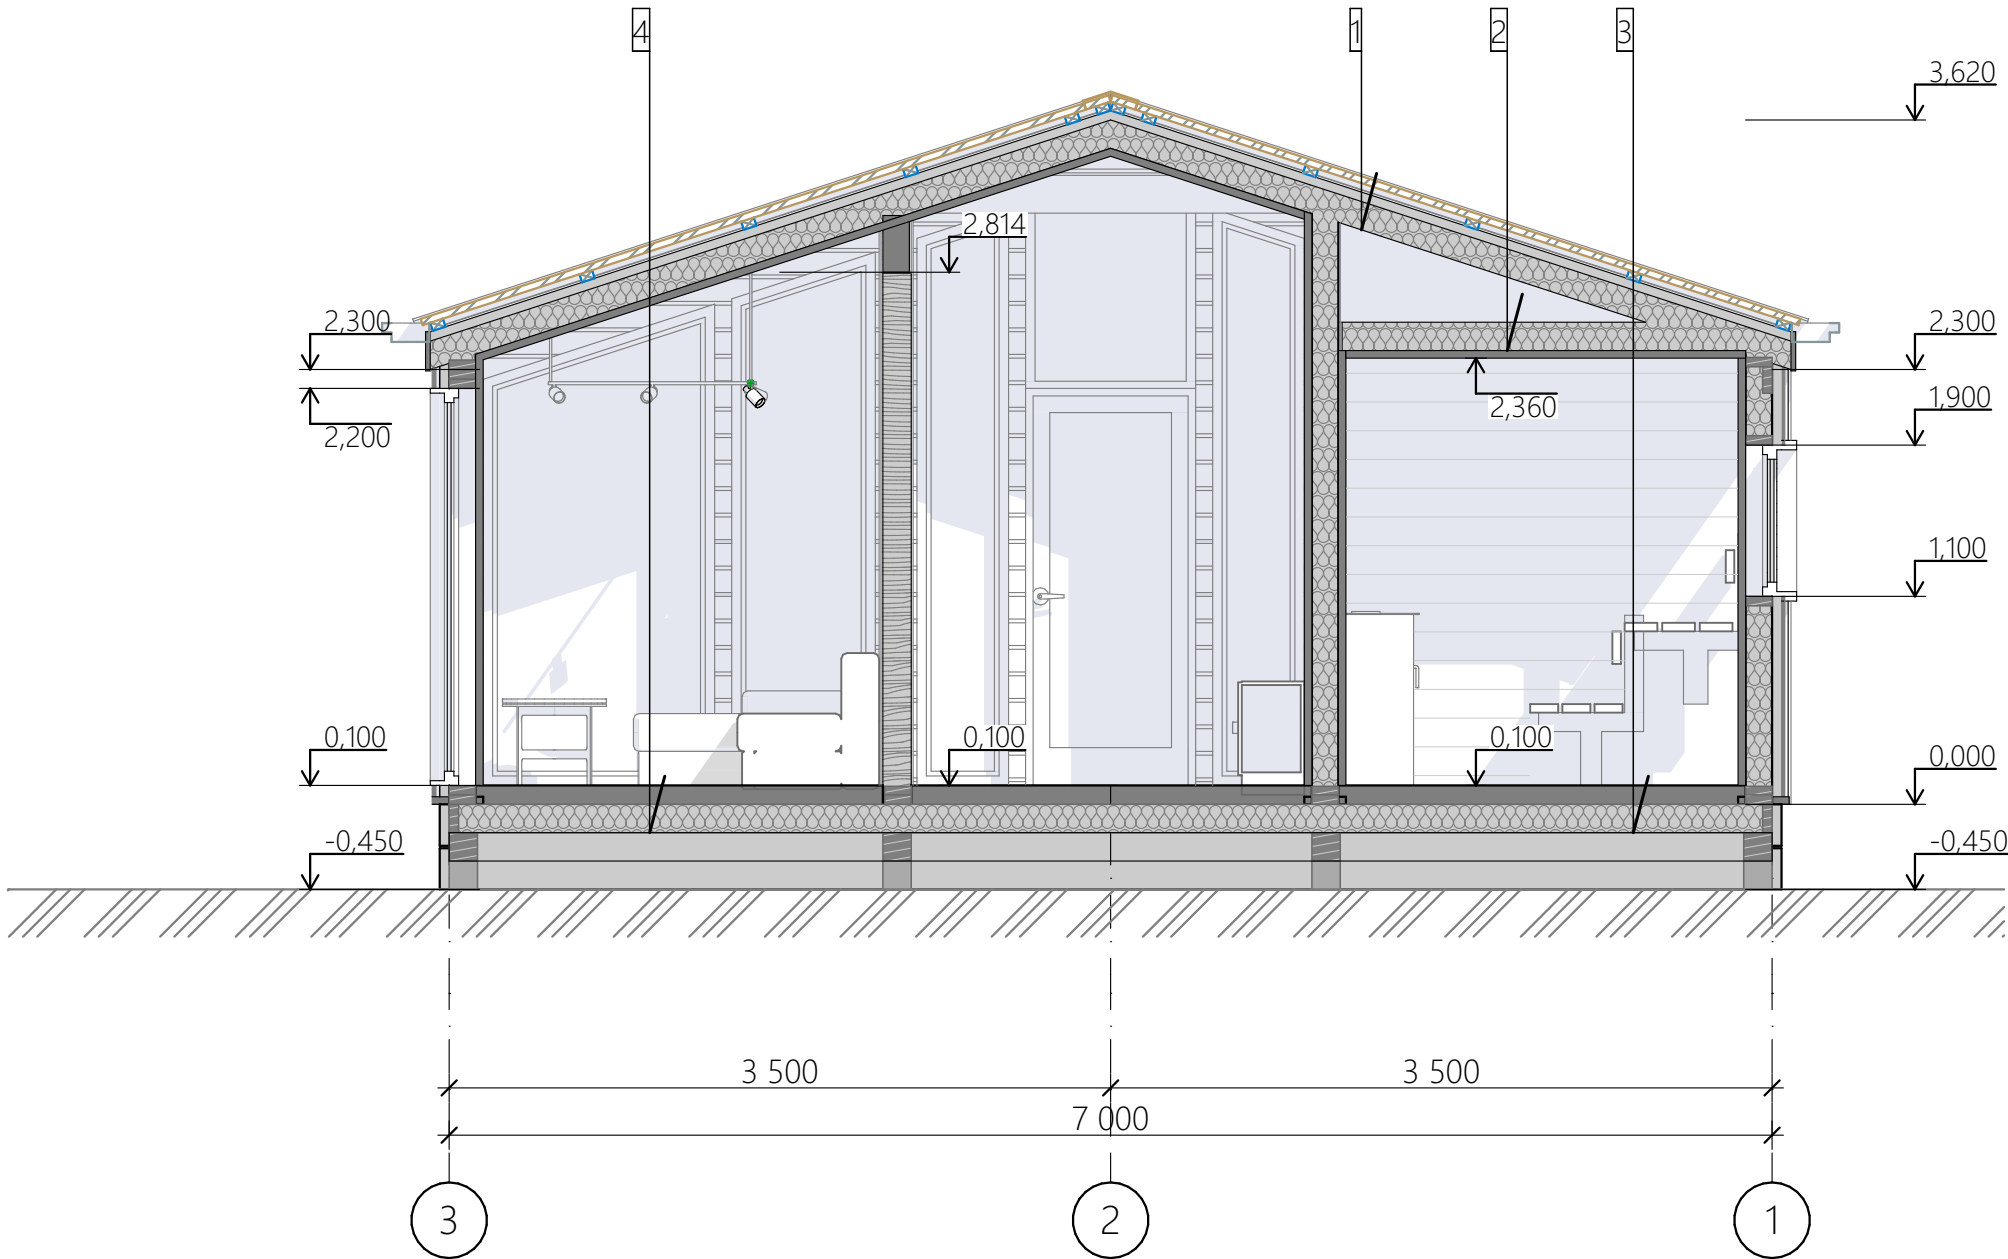

- | | | |
|---|---|----------|
| 1 | -Профлист С-35 | |
| | -Обрешётка 25x100мм | |
| | -Контробрешётка 50x50мм | |
| | -Гидроветрозащитная мембрана | |
| | -Стропильная система 190x45мм | |
| | утепленная | |
| | -Пароизоляционная мембрана | |
| | -Обрешётка 20мм | |
| | -Имитация бруса 20мм | |
| 2 | -Лаги перекрытия (утеплённые 150мм) | 140x45мм |
| | -Пароизоляционная мембрана (алюминиевая фольга) | |
| | -Обрешётка 20x40мм | |
| | -Вагонка 20мм | |
| 3 | -Керамогранит 10мм | |
| | -Клей 10мм | |
| | -Полусухая цементно-песчаная стяжка (с устройством теплого водяного пола) | 50мм |
| | -ЦСП 10мм | |
| | -ОСБ 18мм | |
| | -Пароизоляционная мембрана | |
| | алюминиевая фольга | |
| | -Лаги перекрытия (утепл.) 140мм | |
| | -Гидроветрозащитная мембрана | |
| | -Просечка (сетка яч. 5x5) | |
| | -Обрешётка 20мм | |
| 4 | -Ламинат 10мм | |
| | -Подложка под ламинат 10мм | |
| | -Полусухая цементно-песчаная стяжка 50мм | |
| | -ЦСП 10мм | |
| | -ОСБ 18мм | |
| | -Пароизоляционная мембрана | |
| | -Лаги перекрытия (утепл.) 140мм | |
| | -Гидроветрозащитная мембрана | |
| | -Просечка (сетка яч. 5x5) | |
| | -Обрешётка 20мм | |

Согласовано

Взам. инв. №

Подп. и дата

Инв. № подл.


Лист	Изм.	№ Докум.	Подп.	Дата

Адрес:

Разрез 2-2

#Название Организации

				Наименование		Размеры проема Ш x В, мм		Вид		Площадь, м2	
Согласовано Ив. № подл. Подп. и дата Взам. инв. №				OK-01		1 200×2 100				2,52	
				OK-02		600×800				0,48	
				OK-03		800×800				0,64	
				OK-04		1 225×2 543				2,87	
				OK-04		1 225×2 546				2,87	
				OK-05		760×2 820				2,05	

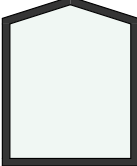Ведомость оконных проемов										1:1,00		
Наименование		Размеры проема Ш х В, мм			Вид			Площадь, м2				
OK-06		485×3 051						1,44				
OK-07		760×2 817						2,05				
OK-07		760×2 820						2,05				
OK-08		900×1 120						0,94				
								27,74 м²				
Примечание:												
1. Изготовление окон и дверей определяется заказчиком, допускается изменение открывания окон и дверей;												
2. При заказе оконных и дверных блоков необходим обмер по месту от изготовителя;												
3. Оконные и дверные изделия изображены со стороны открывания.												
Инв. № подл.	Подп. и дата	Взам. инв. №	Лист	Изм.	№ Докум.	Подп.	Дата	Ведомость оконных проёмов (окончание)		#Название Организации		Лист
												19


Ведомость дверных проемов

1:1

Наименование Размеры проема Ш x В, мм Вид Площадь, м2

ДВ-1


800×2 100

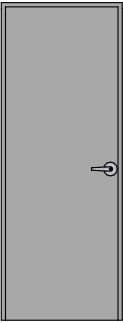

1,68

ДН-1


900×2 100

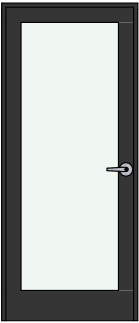

1,89

ДП-1

700×2 000

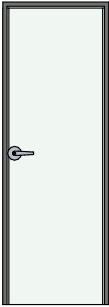

1,40


10,01 м²

Примечание:

- 1. Изготовление окон и дверей определяется заказчиком, допускается изменение открывания окон и дверей;
- 2. При заказе оконных и дверных блоков необходим обмер по месту от изготовителя;
- 3. Оконные и дверные изделия изображены со стороны открывания.

Лист	Изм.	№ Докум.	Подп.	Дата	Ведомость дверных проёмов	#Название Организации	Лист
							20

Согласовано				
И-нв. № подл.	Подп. и дата		Взам. инв. №	

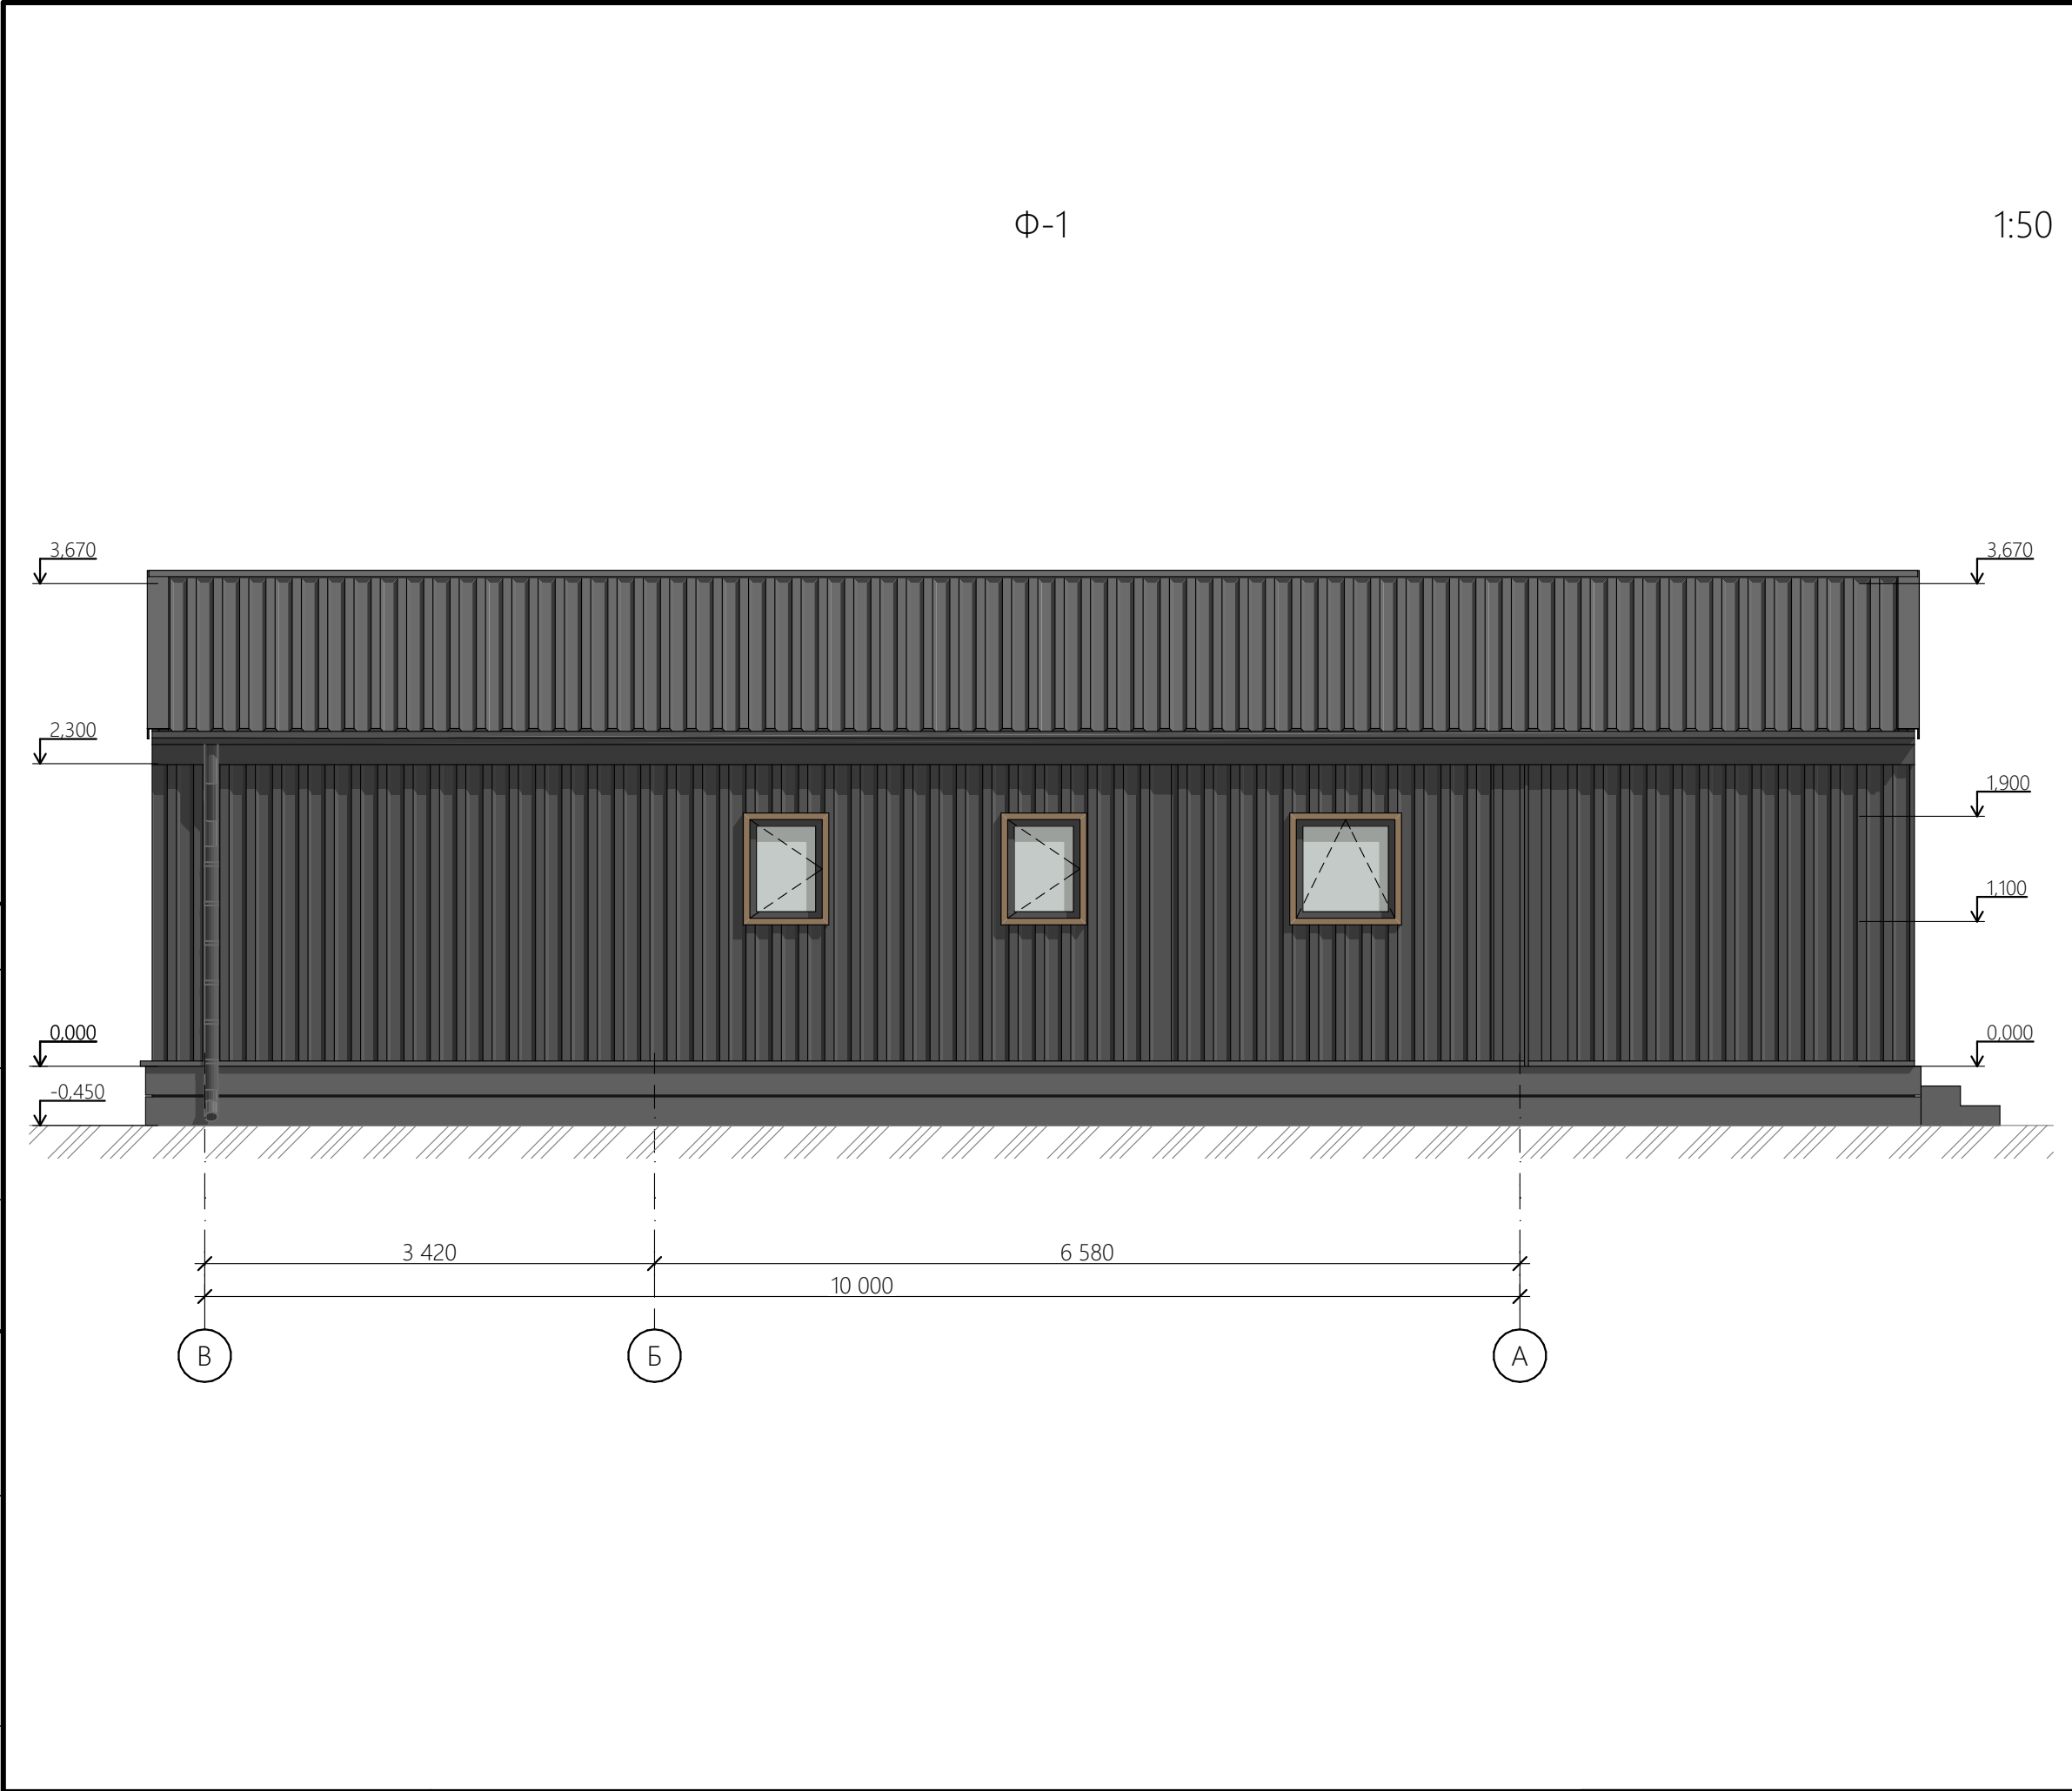

Лист	Изм.	№ Докум.	Подп.	Дата	Адрес:	Цветовое решение; Фасад в осях В-А	#Название Организации	Лист
								21


Согласовано					
И-нв. № подл.	Подп. и дата		Взам. инв. №		

Лист	Изм.	№ Докум.	Подп.	Дата


Адрес:

Цветовое решение; Фасад в осях 3-1

#Название Организации

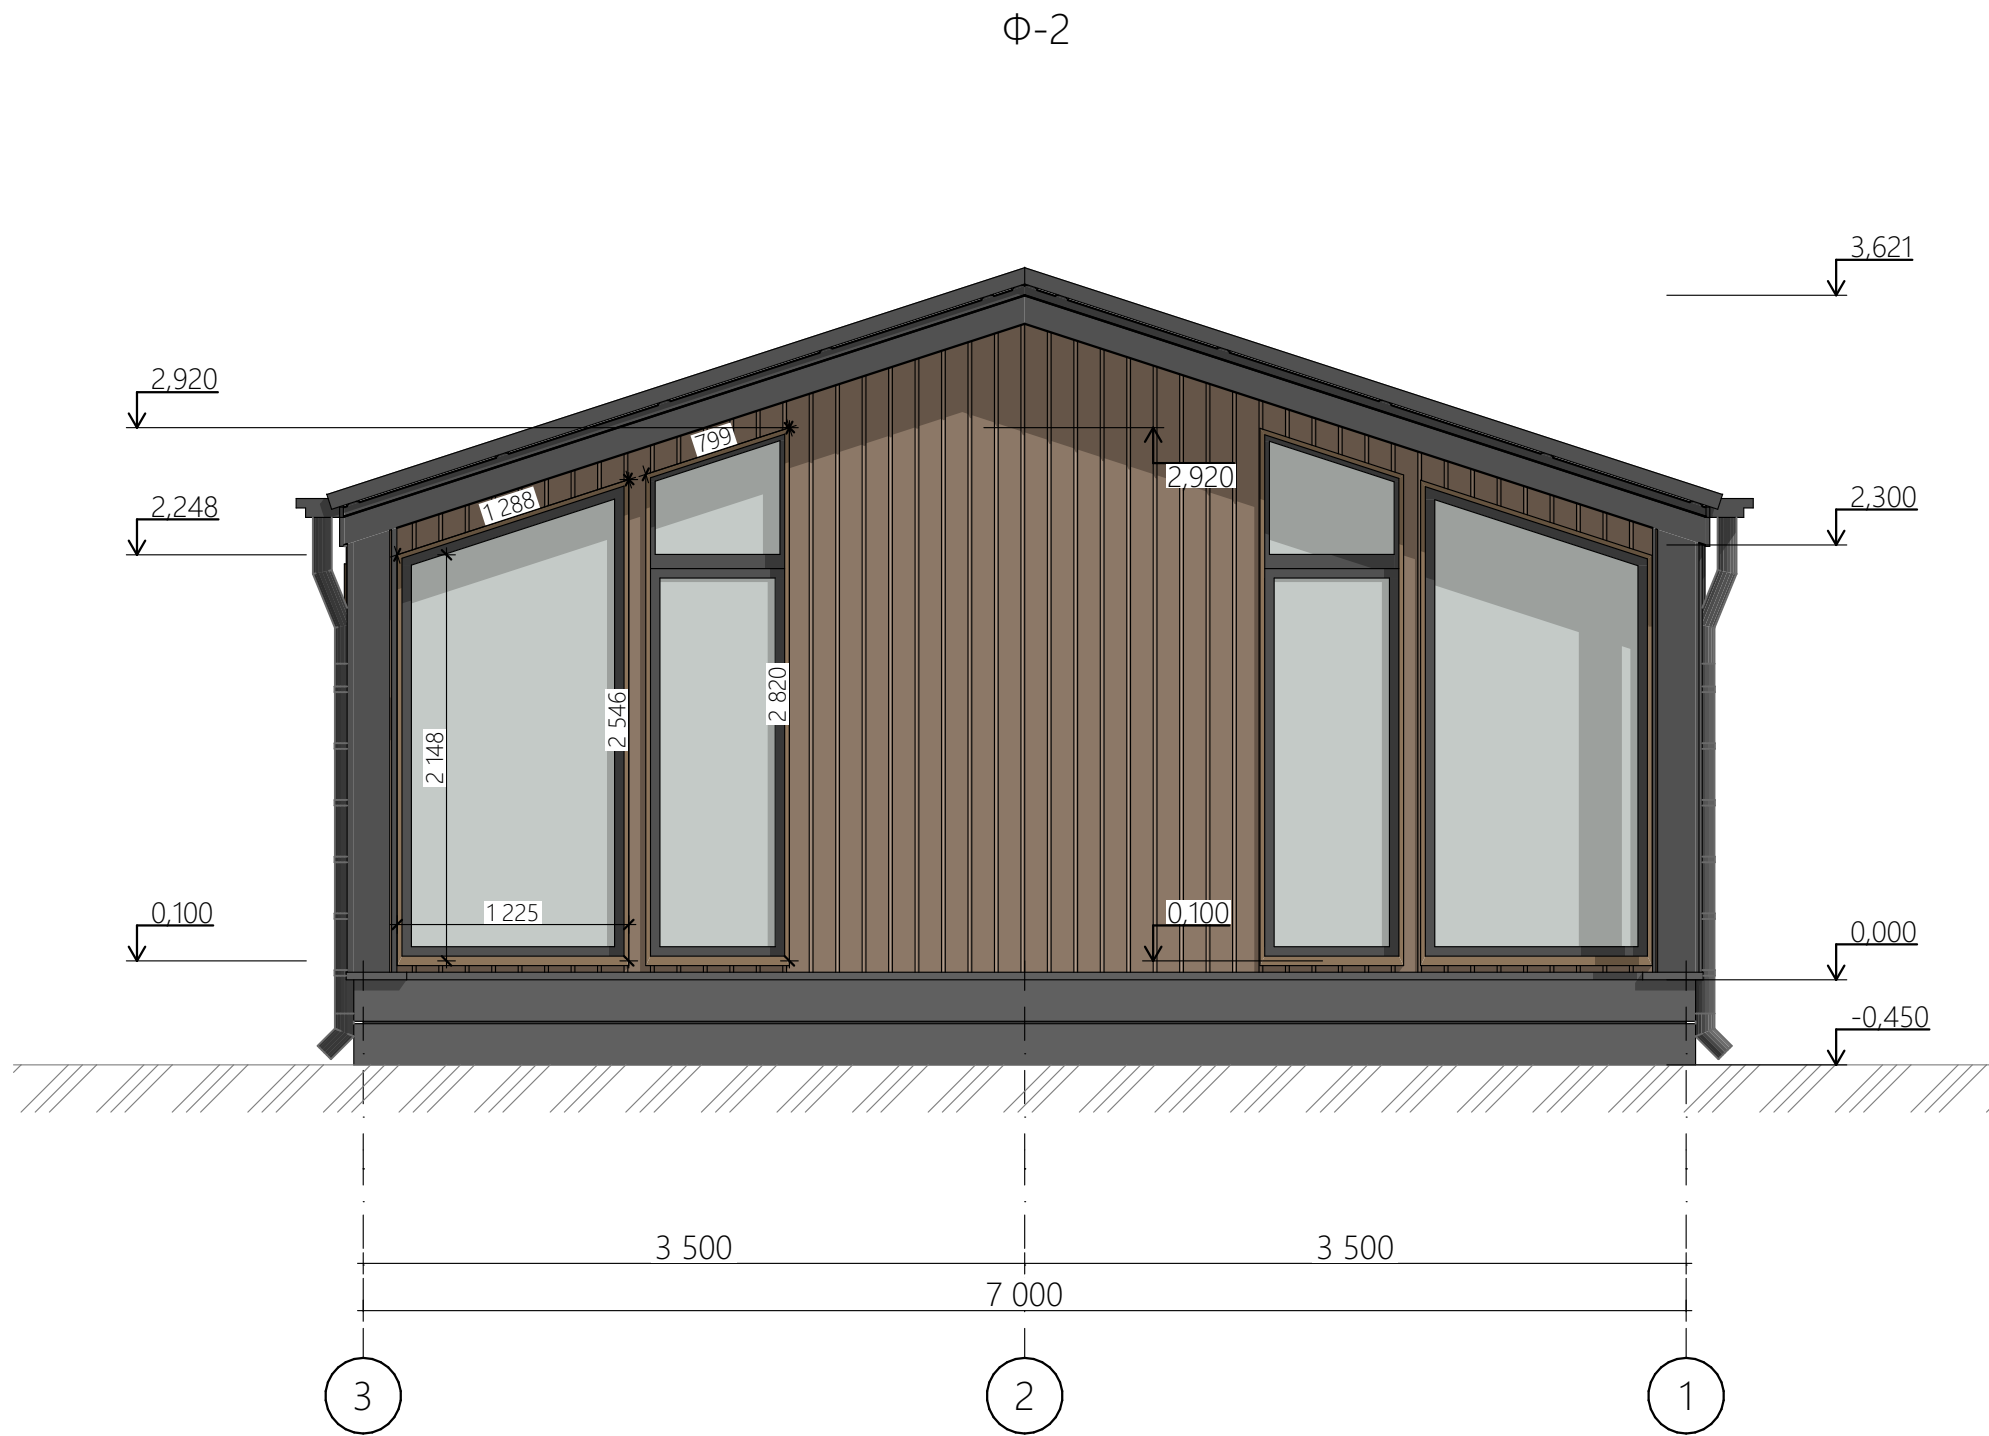

Условные обозначения:

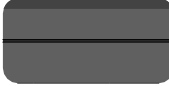-  -Планкен (Цвет орех)
-  -Террасная доска ДПК
-  -Водосточная система, наличники, оконные рамы, кровля(RAL 9005)
-  -Профлист С-35

Согласовано



И.нв. № подл. Подп. и дата Взам. инв. №

Лист	Изм.	№ Докум.	Подп.	Дата

Адрес:

Аксонометрия №1

#Название Организации

Согласовано

Взам. инв. №

Подп. и дата

Инв. № подл.

Ф-3

1:50

Условные обозначения:



-Планкен (Цвет орех)




-Террасная доска ДПК



-Водосточная система,
наличники, оконные
рамы, кровля(RAL 9005)



-Профлист С-35

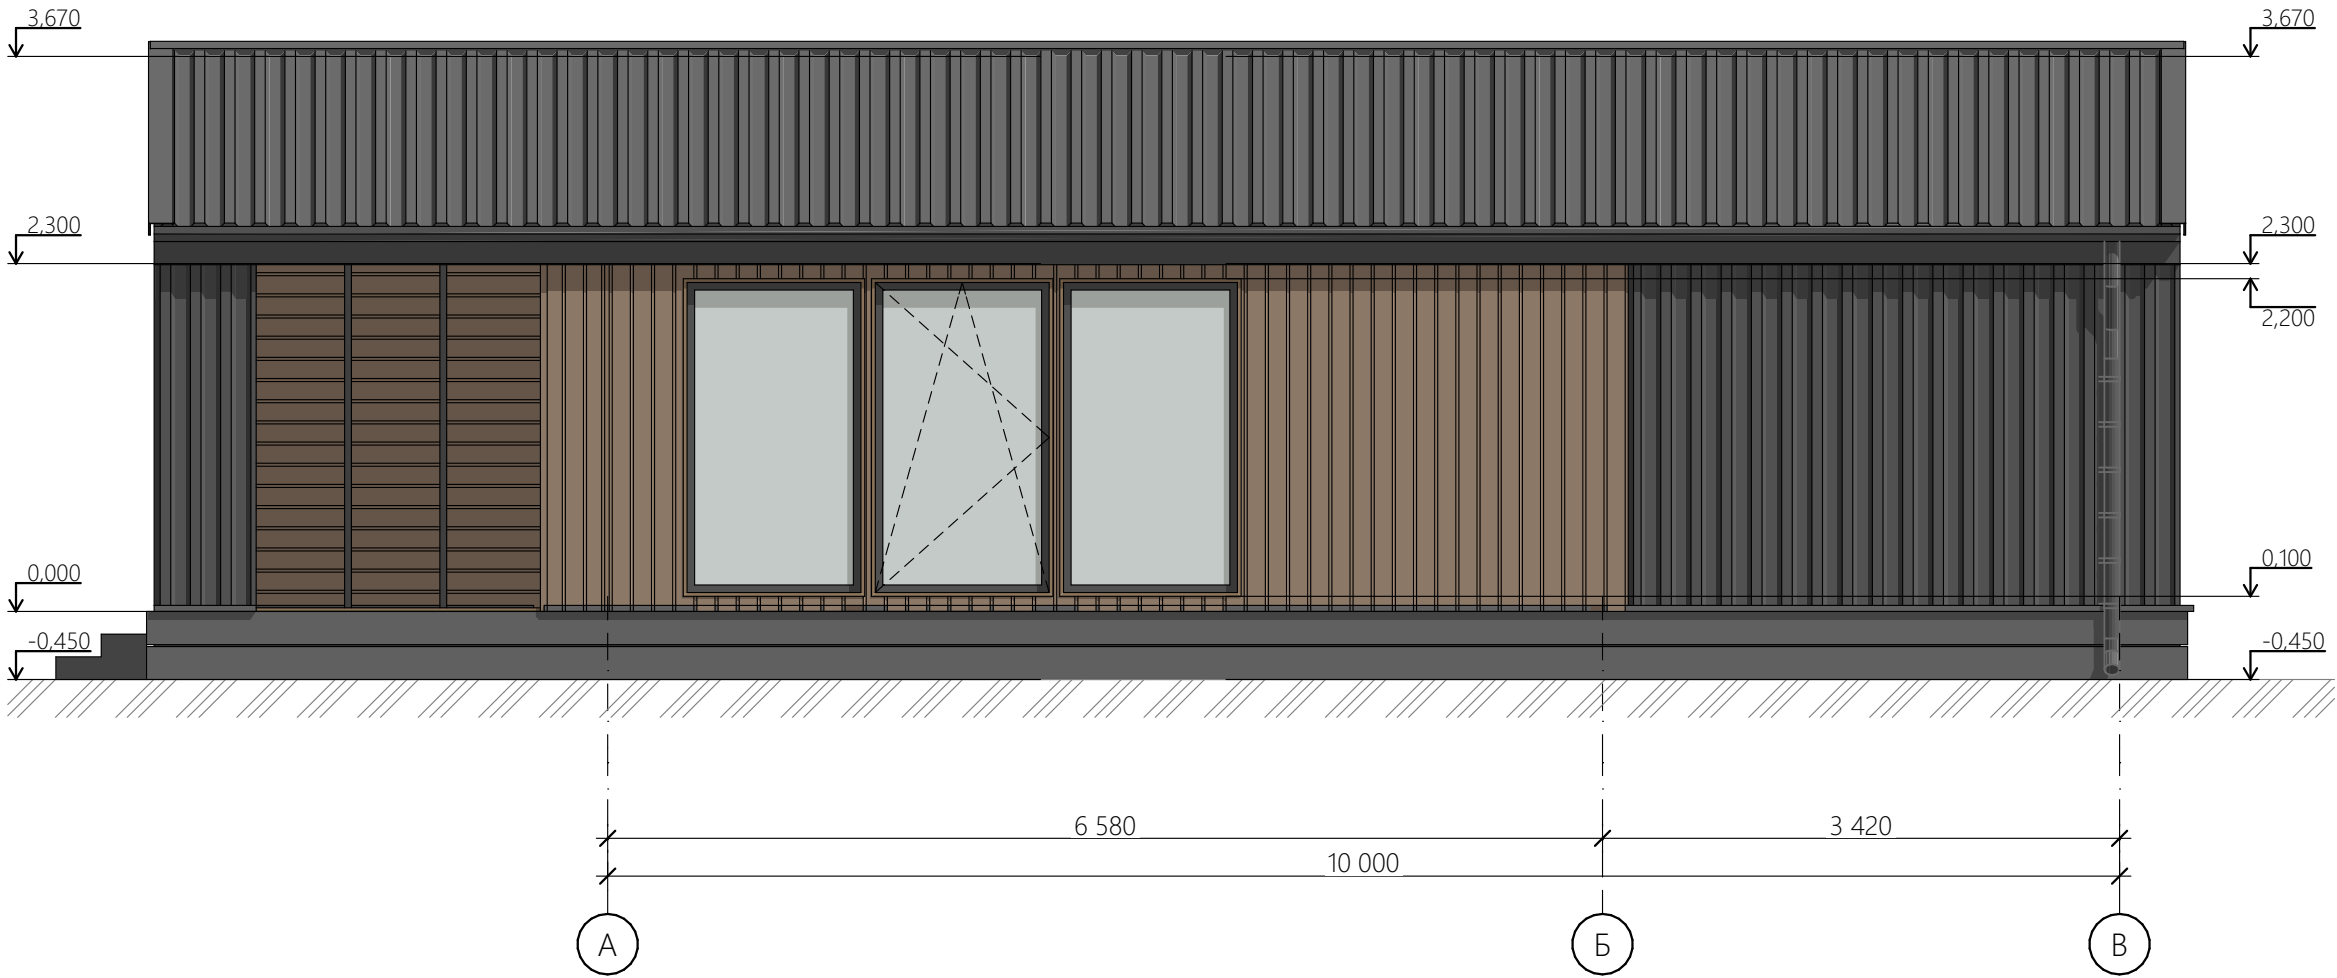

Лист	Изм.	№ Докум.	Подп.	Дата

Адрес:

Цветовое решение; Фасад в
осях А-В

#Название Организации

Лист

24


Согласовано					
Инов. № подл.	Подп. и дата		Взам. инв. №		

Лист	Изм.	№ Докум.	Подп.	Дата


Адрес:

Цветовое решение; Фасад в осях 1-3

#Название Организации

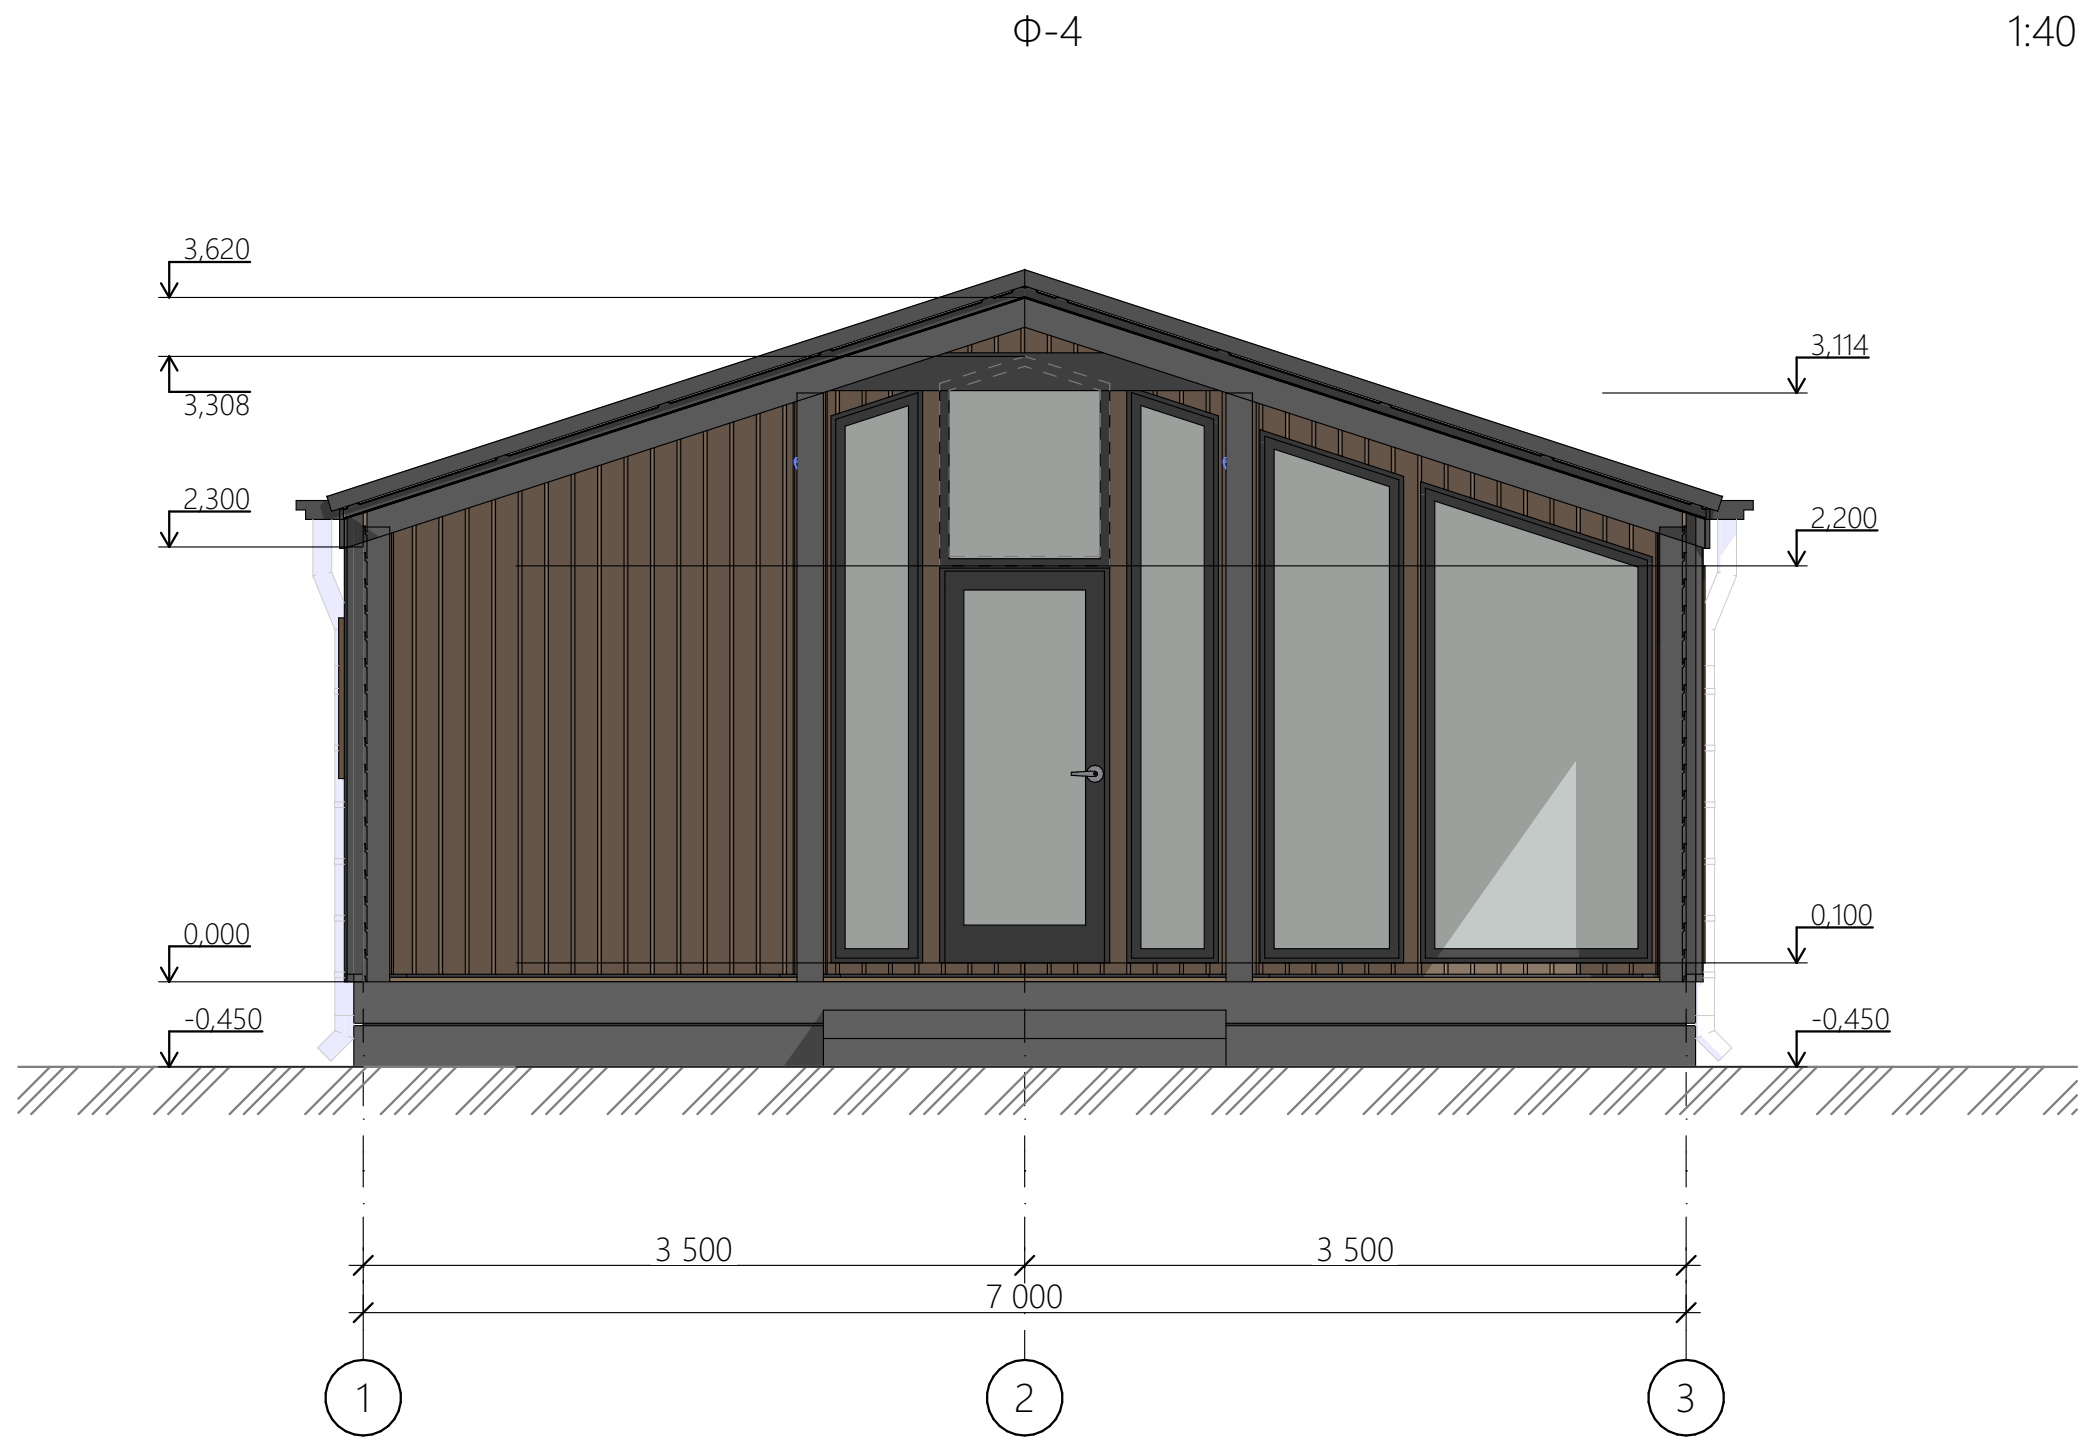

Условные обозначения:

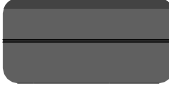-  -Планкен (Цвет орех)
-  -Террасная доска ДПК
-  -Водосточная система, наличники, оконные рамы, кровля(RAL 9005)
-  -Профлист С-35

Согласовано



И/в. № подл. Подп. и дата Взам. инв. №

Лист	Изм.	№ Докум.	Подп.	Дата

Адрес:

Аксометрия №2

#Название Организации

Лист
26

Согласовано

Взам. инв. №

Подп. и дата

Инв. № подл.



Лист	Изм.	№ Докум.	Подп.	Дата

Адрес:

Визуализация №1

#Название Организации

Согласовано

Взам. инв. №

Подп. и дата

Инв. № подл.



Лист	Изм.	№ Докум.	Подп.	Дата

Адрес:

Визуализация №2

#Название Организации

Согласовано			

Инва. № подл.	Подп. и дата	Взам. инв. №	



Лист	Изм.	№ Докум.	Подп.	Дата

Адрес:

Визуализация №3

#Название Организации



Согласовано			

Инва. № подл.	Подп. и дата	Взам. инв. №	

Лист	Изм.	№ Докум.	Подп.	Дата

Адрес:

Визуализация №4

#Название Организации

Согласовано				
Инва. № подл.	Подп. и дата	Взам. инв. №		



Лист	Изм.	№ Докум.	Подп.	Дата

Адрес:

Визуализация №5

#Название Организации

Согласовано			

Исх. № подл.	Подп. и дата	Взам. инв. №	



Лист	Изм.	№ Докум.	Подп.	Дата

Адрес:

Визуализация №6

#Название Организации