

ARCHITECTURE/
CONSTRUCTION



Название:
Разработал:
Принял:
г. Москва



Согласовано				
И-нв. № подл.	Подп. и дата	Взам. инв. №		

Лист	Наименование	Примечание
1	Ведомость чертежей	
2	Пояснительная записка	
3	Схема планировочной организации земельного участка	
4	Маркировочный план	
5	Размерный план	
6	План расстановки мебели и оборудования	
7	Зд-разрез	
8	План электрического теплого пола	
9	План покрытий пола	
10	Экспликация покрытий пола	
11	План покрытия отделки стен	
12	Экспликация отделки стен	
13	План размещения розеток стен	
14	План расстановки светильников и выключателей	
15	План кровли	
16	Разрез 1-1	
17	Разрез 2-2	
18	Ведомость оконных проёмов	
19	Ведомость дверных проёмов	
20	Цветовое решение; Фасад в осях В-А	
21	Цветовое решение; Фасад в осях 3-1	
22	Аксонометрия №1	
23	Цветовое решение; Фасад в осях А-В	
24	Цветовое решение; Фасад в осях 1-3	
25	Аксонометрия №2	
26	Визуализация №1	
27	Визуализация №2	
28	Визуализация №3	
29	Визуализация №4	
30	Визуализация №5	
31	Визуализация №6	

Лист	Изм.	№ Докум.	Подп.	Дата	Адрес:	Ведомость чертежей	#Название Организации	Лист
								1

В основу архитектурно-планировочных решений положены требования технологических заданий и требования норм и правил строительного проектирования, действующих на территории РФ.

Основные параметры и требования разработаны на основании пожеланий и требований заказчика.

Архитектурные решения приняты в соответствии со следующими нормативными документами:

- Градостроительный кодекс российской федерации.
- Земельного Кодекса Российской Федерации.
- Федеральный закон от 22.07.2008 N 123 - ФЗ (ред. от 29.07.2017)"Технический регламент о требованиях пожарной безопасности.
- Федеральный закон № 384 - ФЗ «Технический регламент о безопасности зданий и сооружений».
- ГОСТ Р 21.1101-2013.«Основные требования к проектной и рабочей документации».
- Постановление правительства РФ от 16.02.2008 № 87 «Положение о составе разделов проектной документации и требованиях к их содержанию».
- СП 42.13330.2011 «Градостроительство. Планировка и застройка городских и сельских поселений».
- СП 131.13330.2018 «СНиП 23-01-99* Строительная климатология».
- СП 20.13330.2016 «СНиП 2.01.07-85* Нагрузки и воздействия».
- СП 22.13330.2016 «СНиП 2.02.01-83* Основания зданий и сооружений».
- СП 70.13330.2012 (с изменениями №1) «СНиП 3.03.01-87 Несущие и ограждающие конструкции».
- СП 64.13330.2017 «СНиП II-25-80 Деревянные конструкции».
- СП 17.13330.2017 «СНиП II-26-76 Кровли».
- СП 29.13330.2011 «СНиП 2.03.13-88 Полы».
- СП 28.13330.2017 «СНиП 2.03.11-85 Защита строительных конструкций от коррозии».
- СП 50.13330.2012 «СНиП 23-02-2003 Тепловая защита зданий».

Согласовано				
И-нв. № подл.	Подп. и дата	Взам. инв. №		

1. Общие данные:

1.1. Архитектурный проект разработан на основании требований и пожеланий заказчика.

Тип строения	Баня
Относительная отм. ±0.000	ур. верха лаг деревянного перекрытия
Общая площадь застройки, м2	66,16
Габаритные размеры каркаса здания	10,4х6 м
Этажность	1 этаж
Конструктивная схема	Деревянный каркас

2. Конструктивные решения:

2.1. Рабочие чертежи разработаны на основании задания на проектирование

Полезная нагрузка на перекрытие	150 кгс/м2	-
Нормативная глубина промерзания	1,2м	СП 22.13330.2016 СП 131.13330.2020
Нормативное ветровое давление	I район (23кгс/м2)	СП 22.13330.2016
Нормативный вес снегового покрова	III район (150кгс/м2)	СП 22.13330.2016
Температура наиболее холодной пятидневки	-29°С	СП 131.13330.2020

2.2. Конструктивное строение представляет собой сооружение:

- на свайном фундаменте
- несущими стенами из деревянного каркаса
- вальмовой кровлей по деревянным стропилам

2.3. Необходимо осуществлять технический надзор за производством строительных работ. Данные по проведённым работам необходимо систематически вносить в журнал работ.

По каждому из этапов работ необходимо осуществлять входной контроль материалов и вести приёмку.

Фундамент	винтовые сваи (д 108мм)
Несущие конструкции	деревянный каркас (140х45мм)
Стропильная система	строганая доска (190х45мм)
Тип крыши	двускатная
Покрытие кровли	Фальц

2.4. Все деревянные конструкции обработать огне-биозащитными септиками в соответствии со СП 28.13330.2017 "Защита строительных конструкций от коррозии".

2.5. Кровельные работы выполнять в соответствии с требованиями фирмы производителя.

2.6. Все работы вести в строгом соответствии с требованиями СНиП 12.03.2001 "Безопасность труда в строительстве".

2.7. При выполнении всех работ строго соблюдать меры противопожарной безопасности.

2.8. Возможна замена материалов аналогами.


*Решения, принятые в проекте и отображенные в чертежах, соответствуют требованиям экологических, санитарно - гигиенических, противопожарных и других норм, действующих на территории Российской Федерации, и обеспечивают безопасную для жизни и здоровья людей эксплуатацию объекта при соблюдении предусмотренных рабочих чертежей и мероприятий.

Лист	Изм.	№ Докум.	Подп.	Дата

Адрес:

Пояснительная записка

#Название Организации

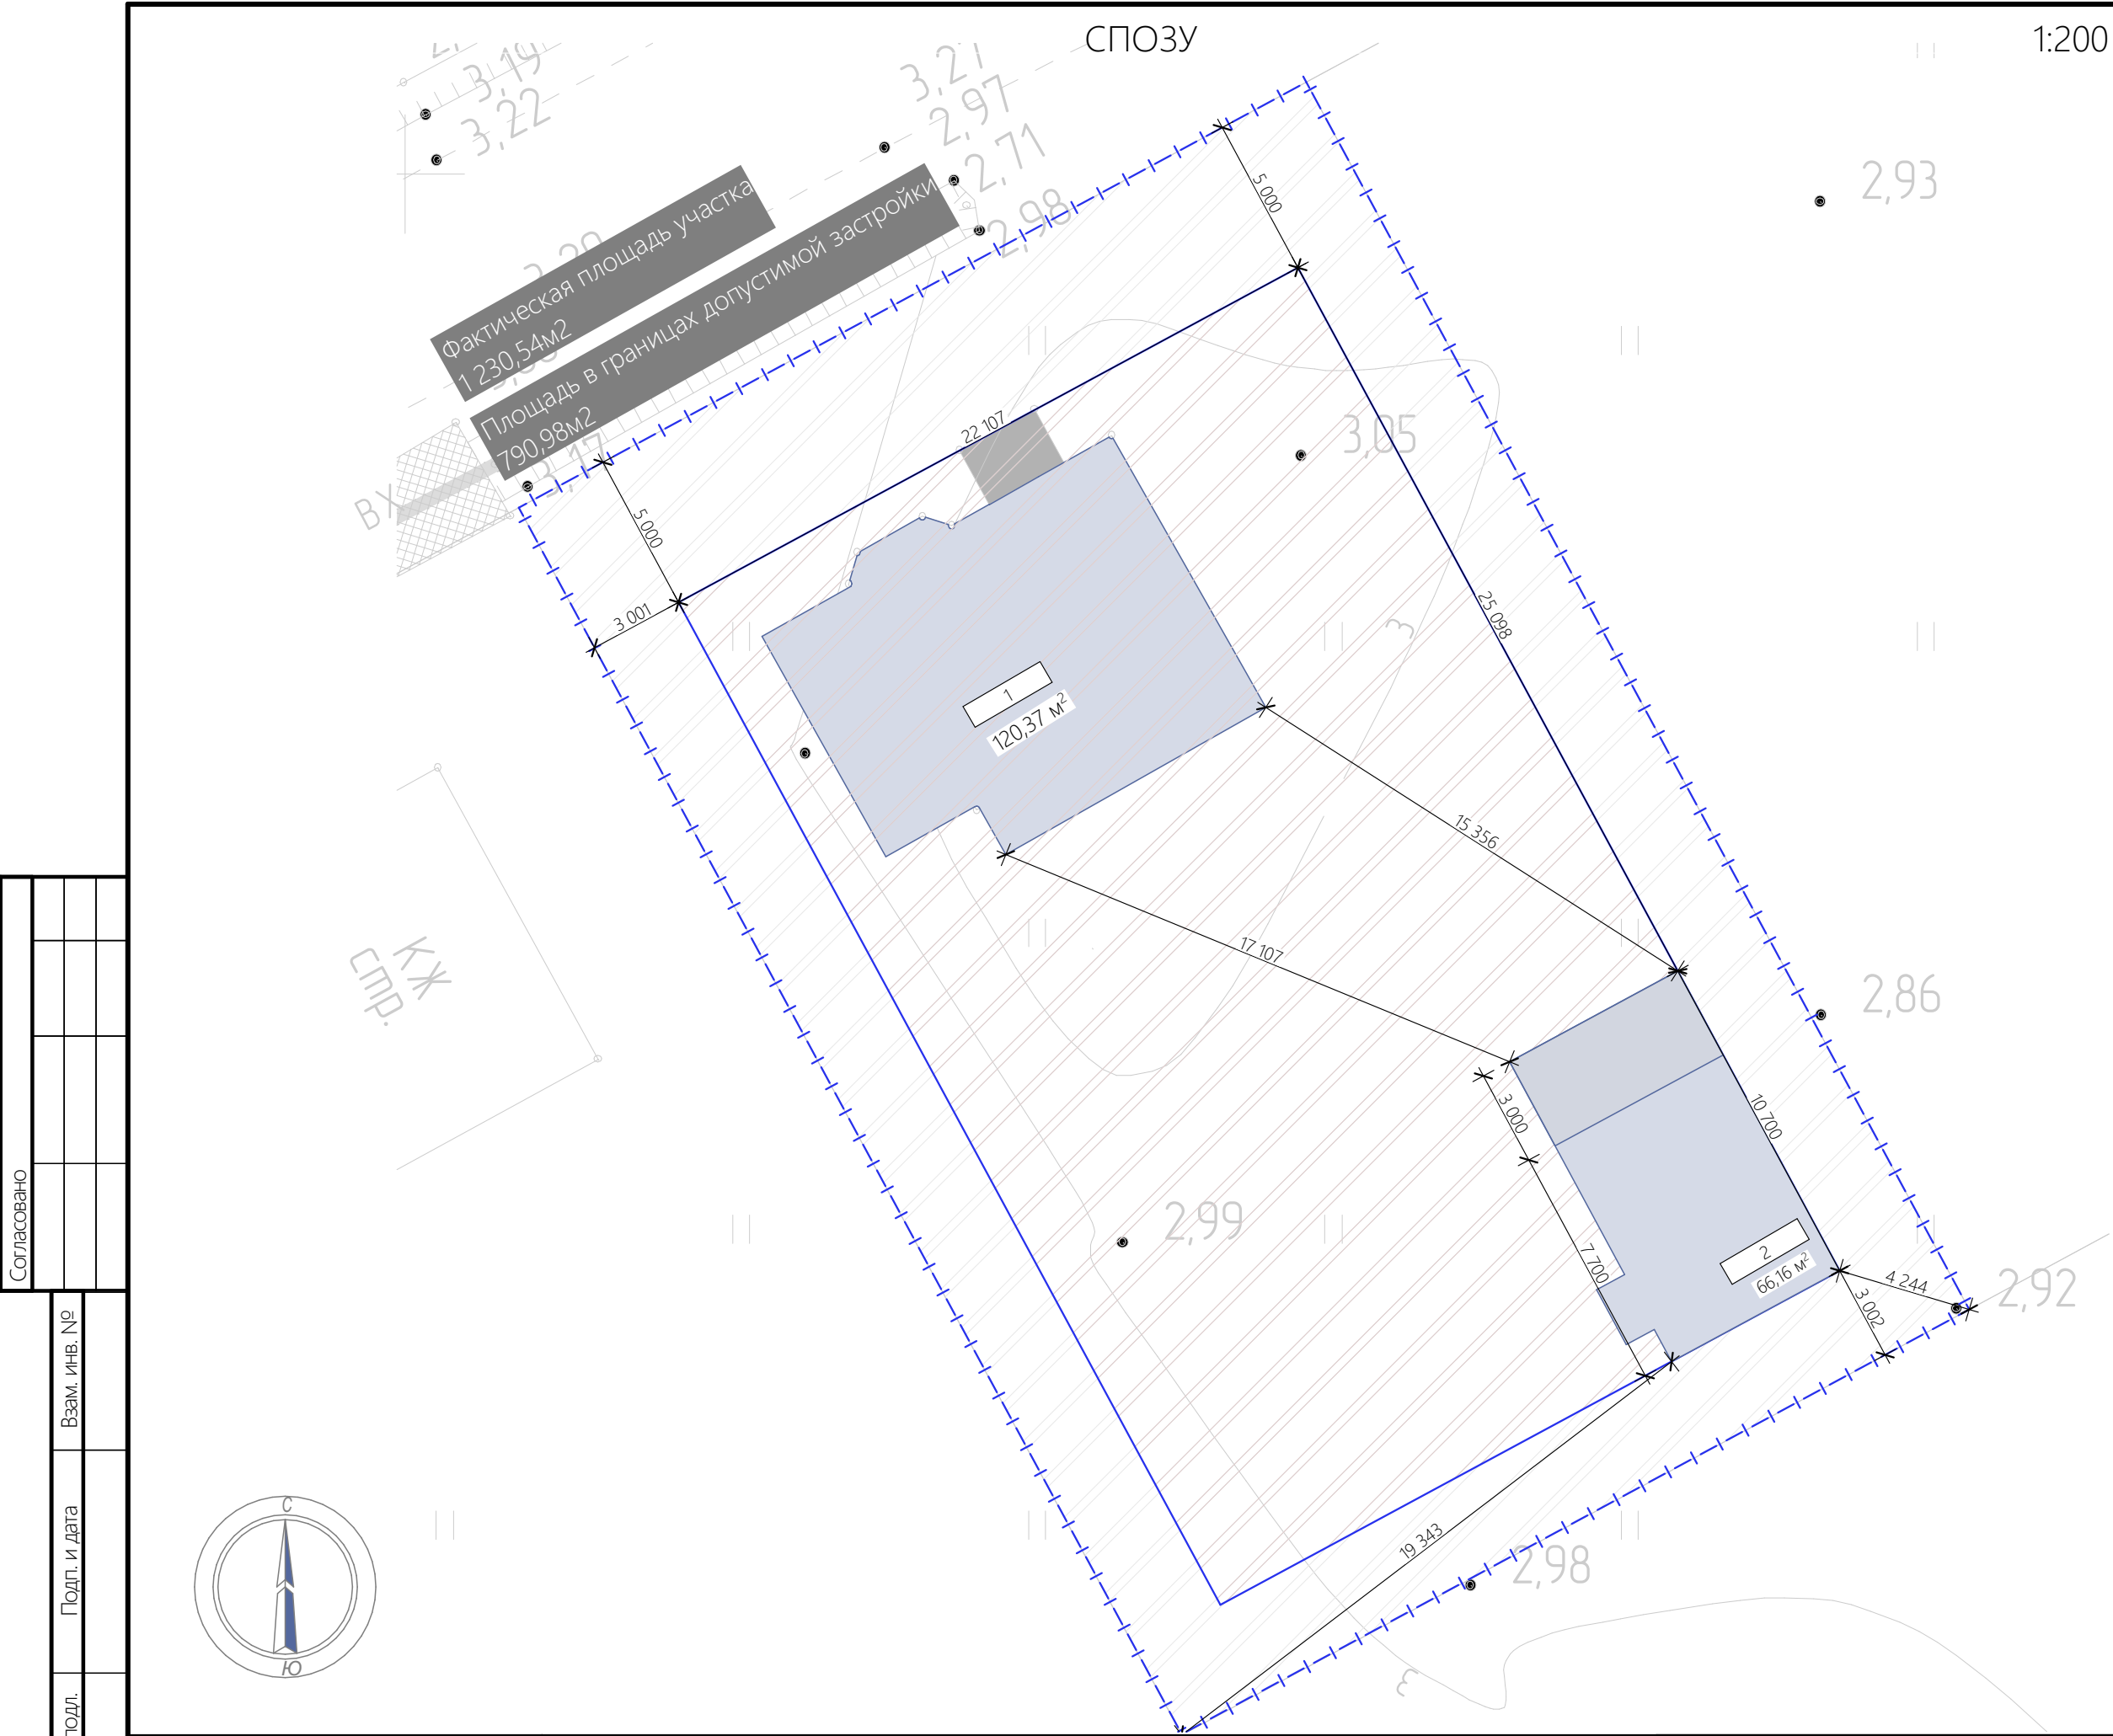

1:200

Условные обозначения:

- Граница участка
- Граница застройки участка
- 1 - Индивидуальный жилой дом
- 2 - Банный комплекс

Технико-экономические
показатели

Наименование	Площадь, м²
Общая площадь застройки (ИЖС+баня)	186,53
Площадь участка (по топографической съемке)	1230,54
Площадь застройки (баня)	66,16

Согласовано					

И-нв. № подл.	Подп. и дата	Взам. инв. №

Лист	Изм.	№ Докум.	Подп.	Дата


Адрес:

Схема планировочной
организации земельного
участка

#Название Организации

Маркировочный план

1:50

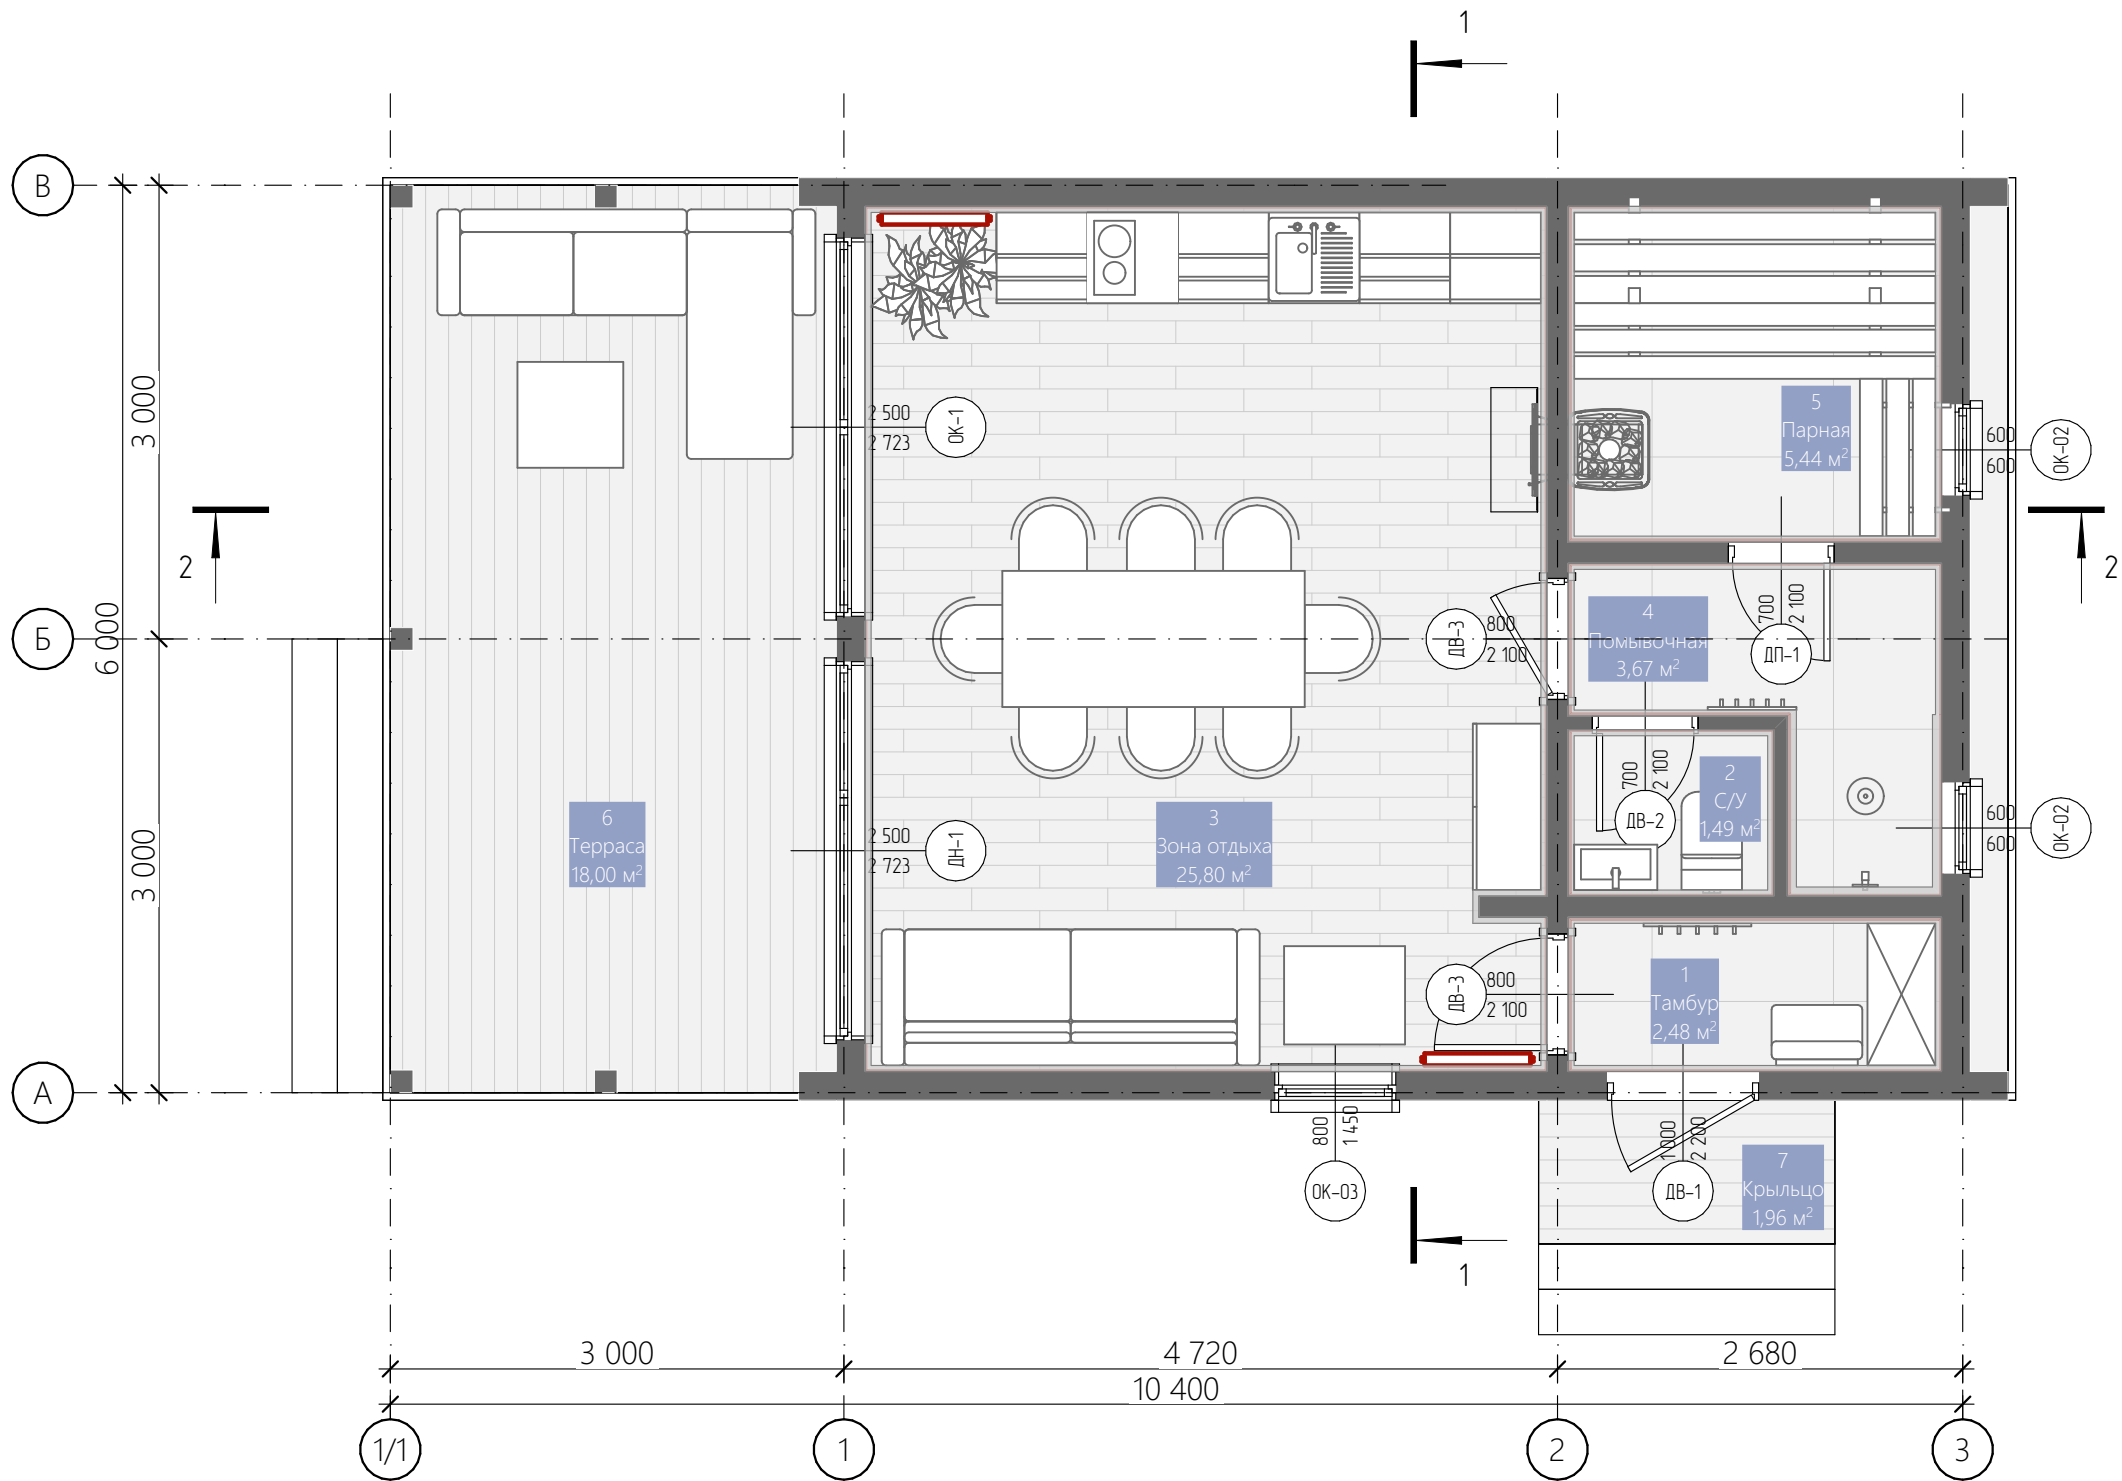

Экспликация помещений

№	Наименование	Площадь, кв. м.
1	Тамбур	2,48
2	С/У	1,49
3	Зона отдыха	25,80
4	Помывочная	3,67
5	Парная	5,44
6	Терраса	18,00
7	Крыльцо	1,96

58,84 м²

Наименование

Площадь, кв. м.

Площадь застройки

66,16

Примечание:

1. Вся индивидуальная мебель выполняется по отдельному проекту с детальной проработкой и калькуляцией. Чертежи предоставляет фирма-изготовитель столярных изделий.
2. Данный проект отдельно согласовывается с автором проекта и непосредственно с заказчиком.
3. Цветовое решение фасада и материалов отделки показаны в проекте приблизительно.
4. Количество ступеней показано условно.

Лист	Изм.	№ Докум.	Подп.	Дата

Адрес:

Маркировочный план


#Название Организации

Лист

4

Размерный план

1:50

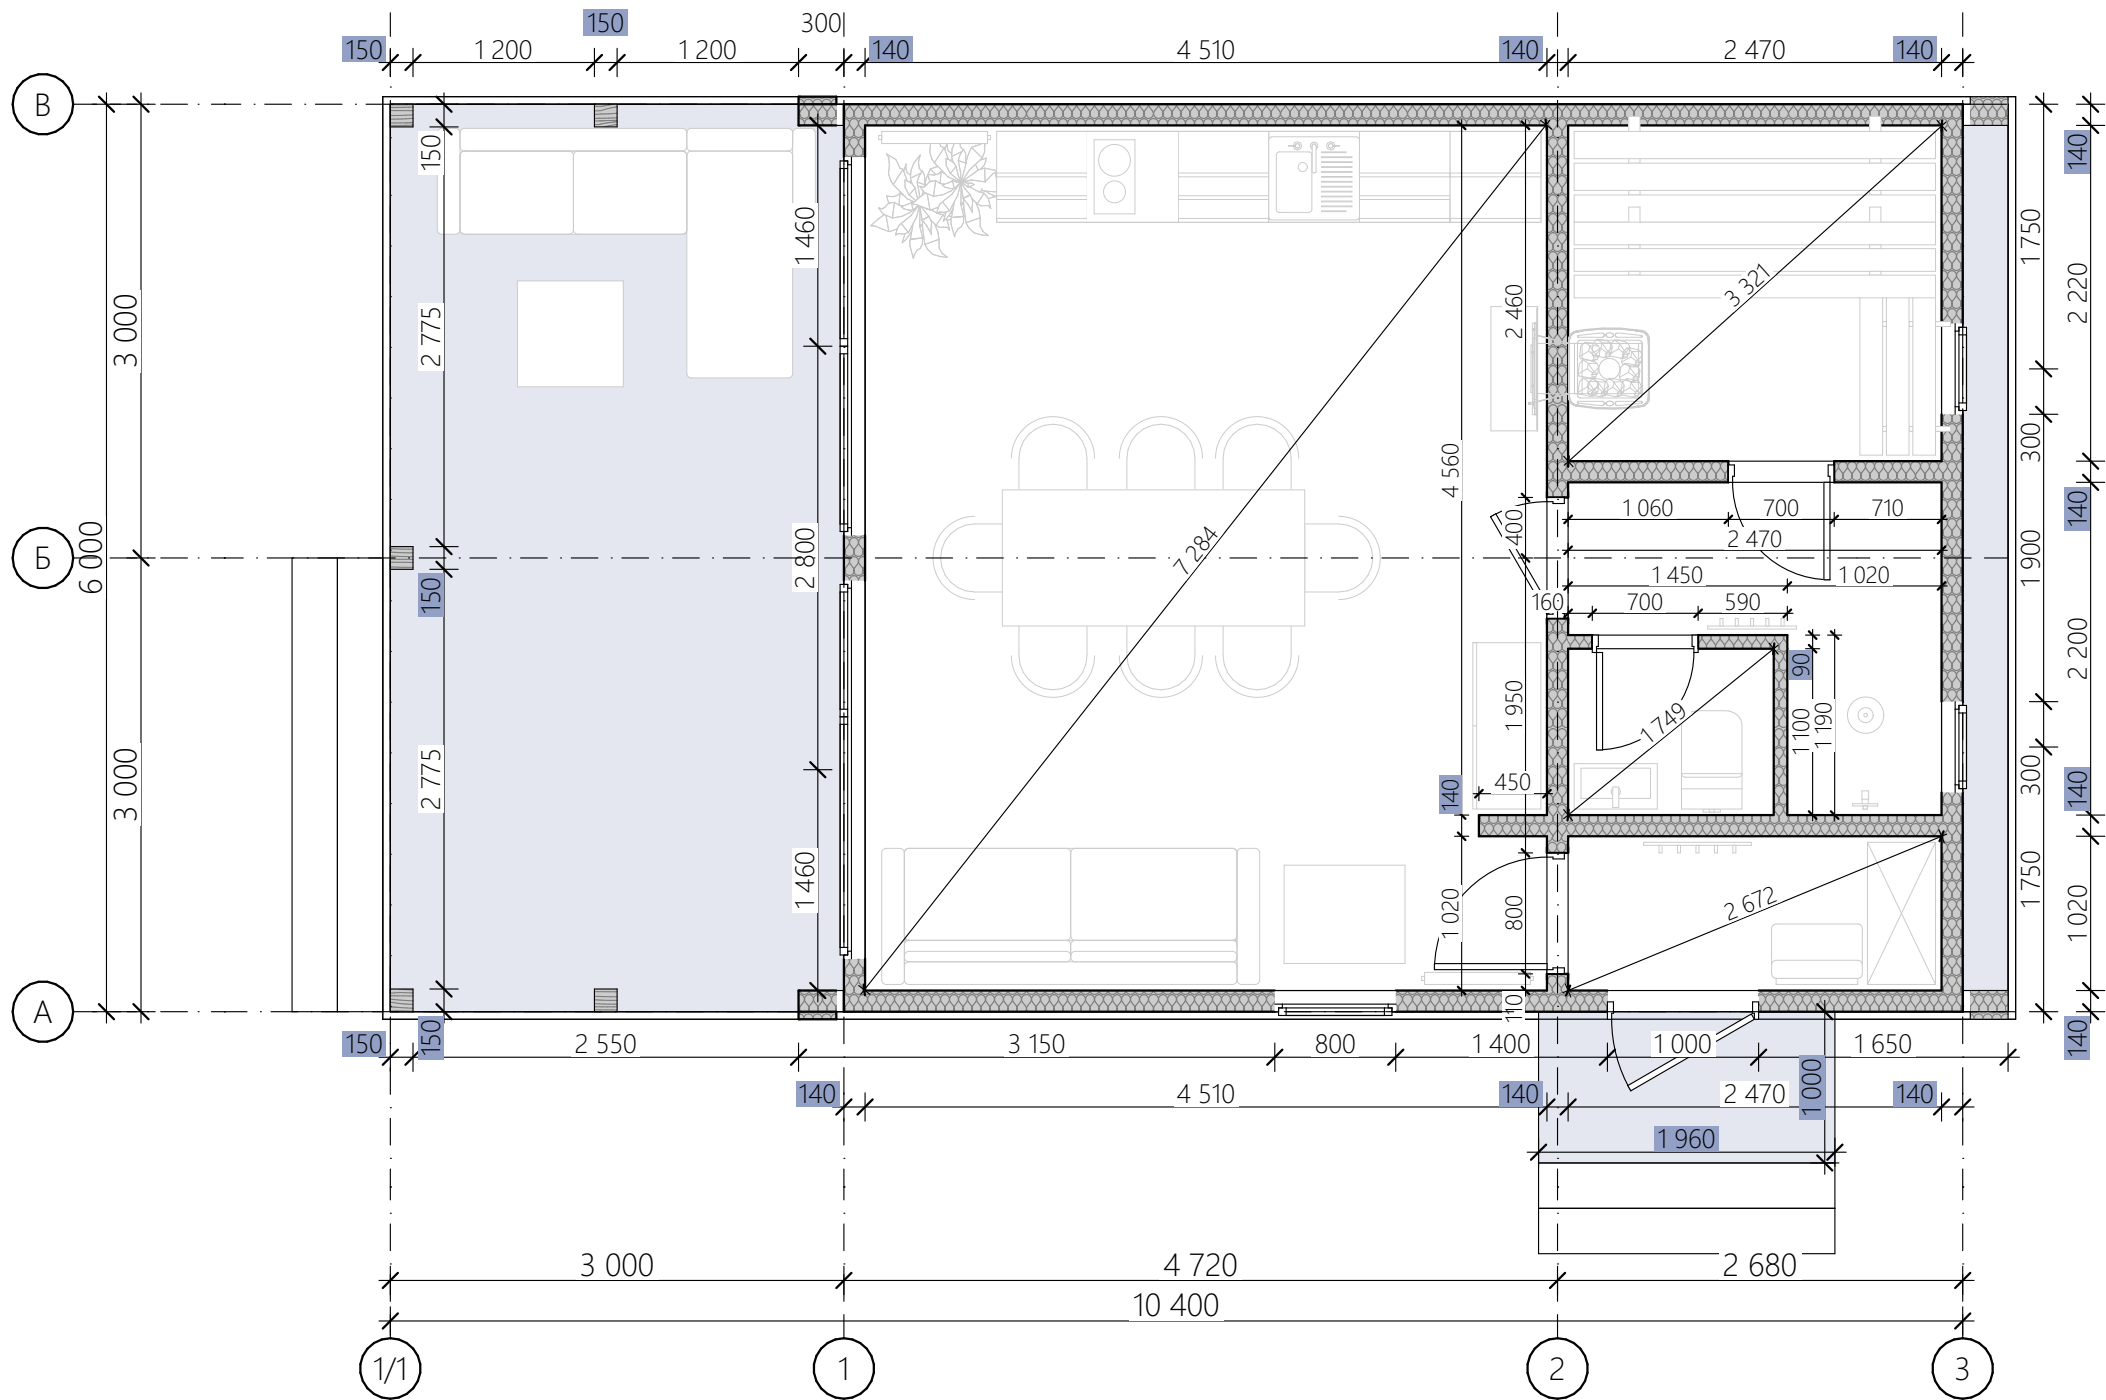

Примечание:
1. Представленные размеры
указаны без учета внешней и
внутренней отделки


Согласовано				
И-нв. № подл.	Подп. и дата	Взам. инв. №		

Лист	Изм.	№ Докум.	Подп.	Дата

Адрес:

Размерный план

#Название Организации

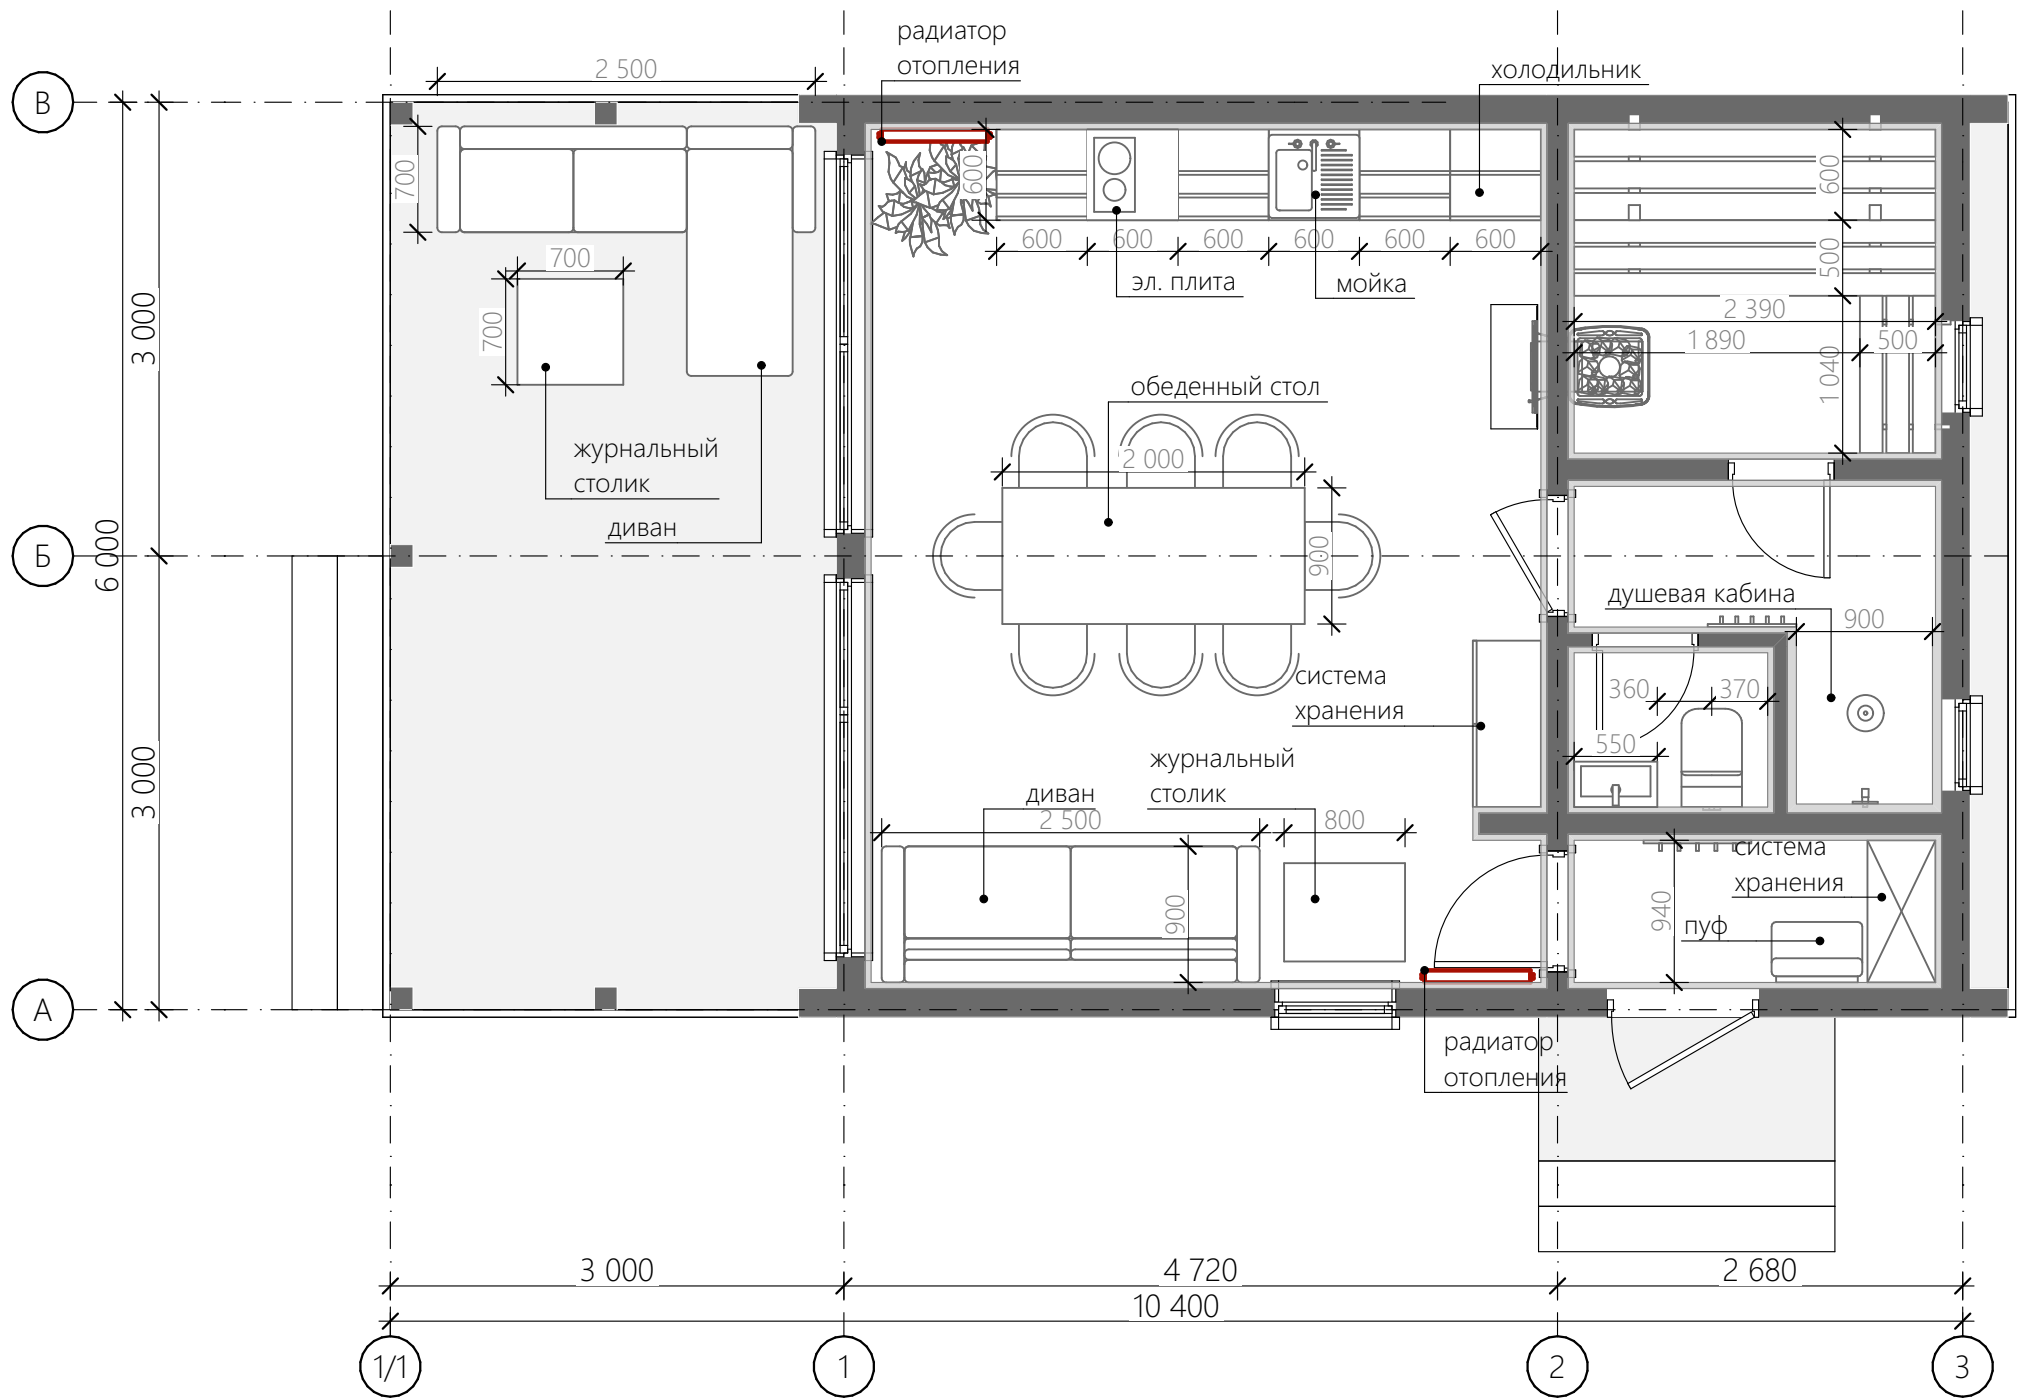

Примечание:

1. Вся индивидуальная мебель выполняется по отдельному проекту с детальной проработкой и калькуляцией. Чертежи предоставляет фирма-изготовитель столярных изделий.

2. Финальные размеры мебели и оборудования указаны ориентировочно — для точной компоновки требуется разработка дизайн-проекта.

Согласовано				
И-нв. № подл.	Подп. и дата	Взам. инв. №		



Лист	Изм.	№ Докум.	Подп.	Дата

Адрес:

План расстановки мебели и оборудования

#Название Организации

Согласовано

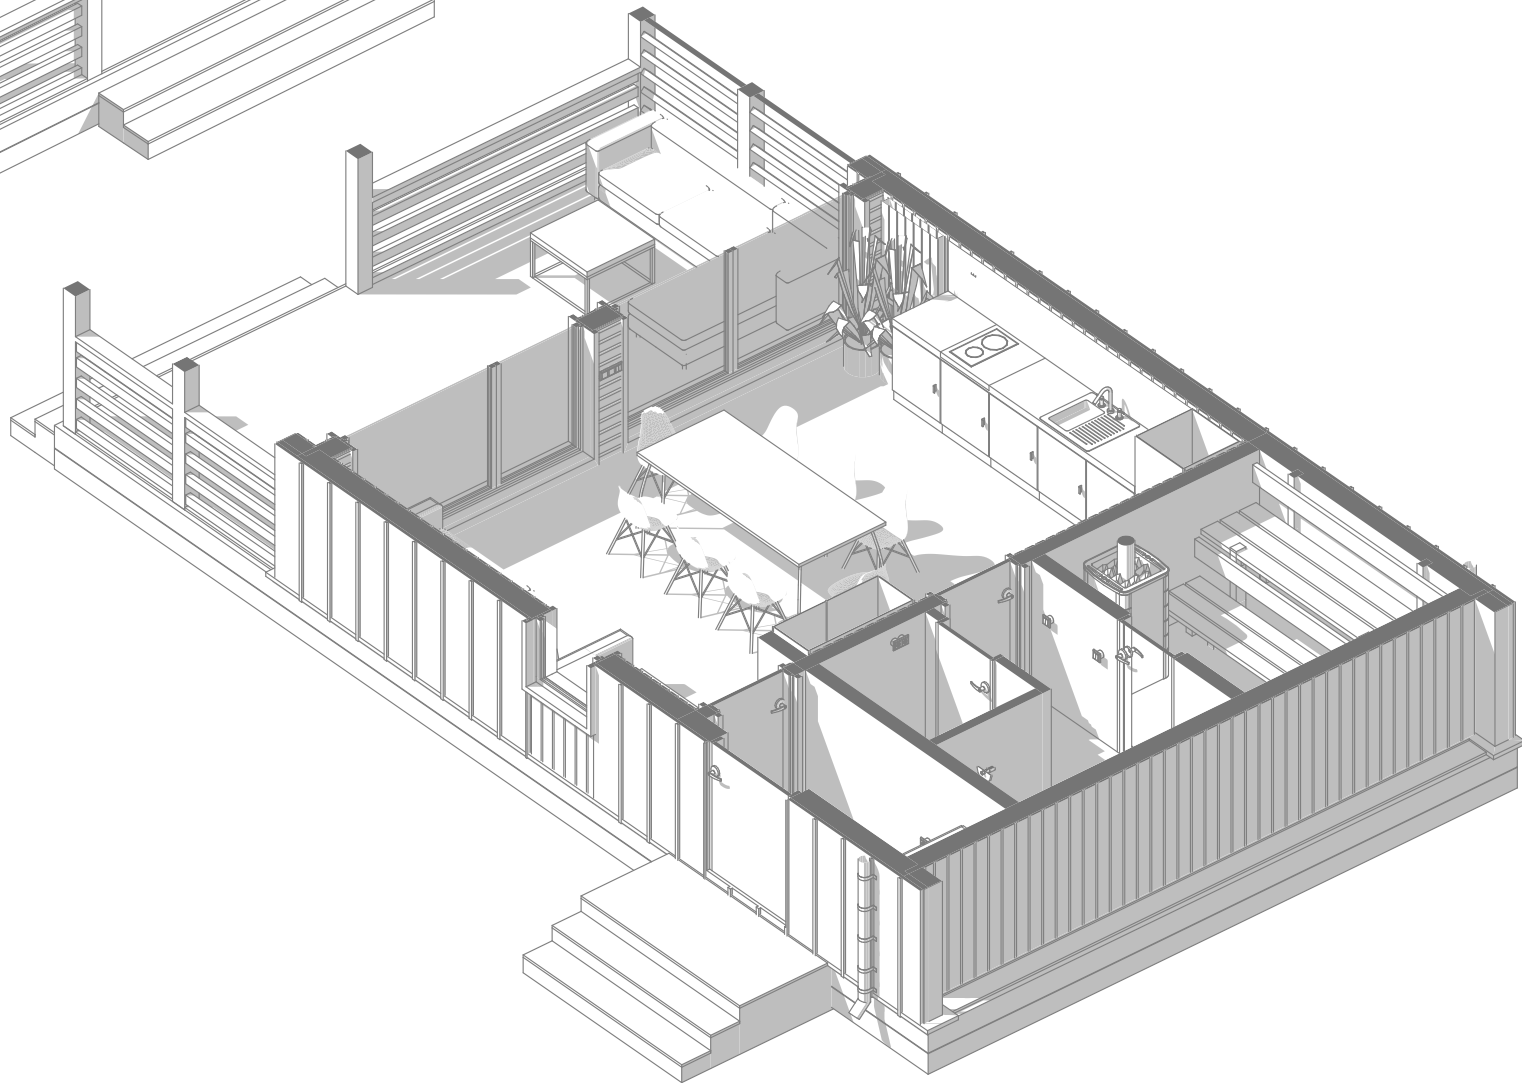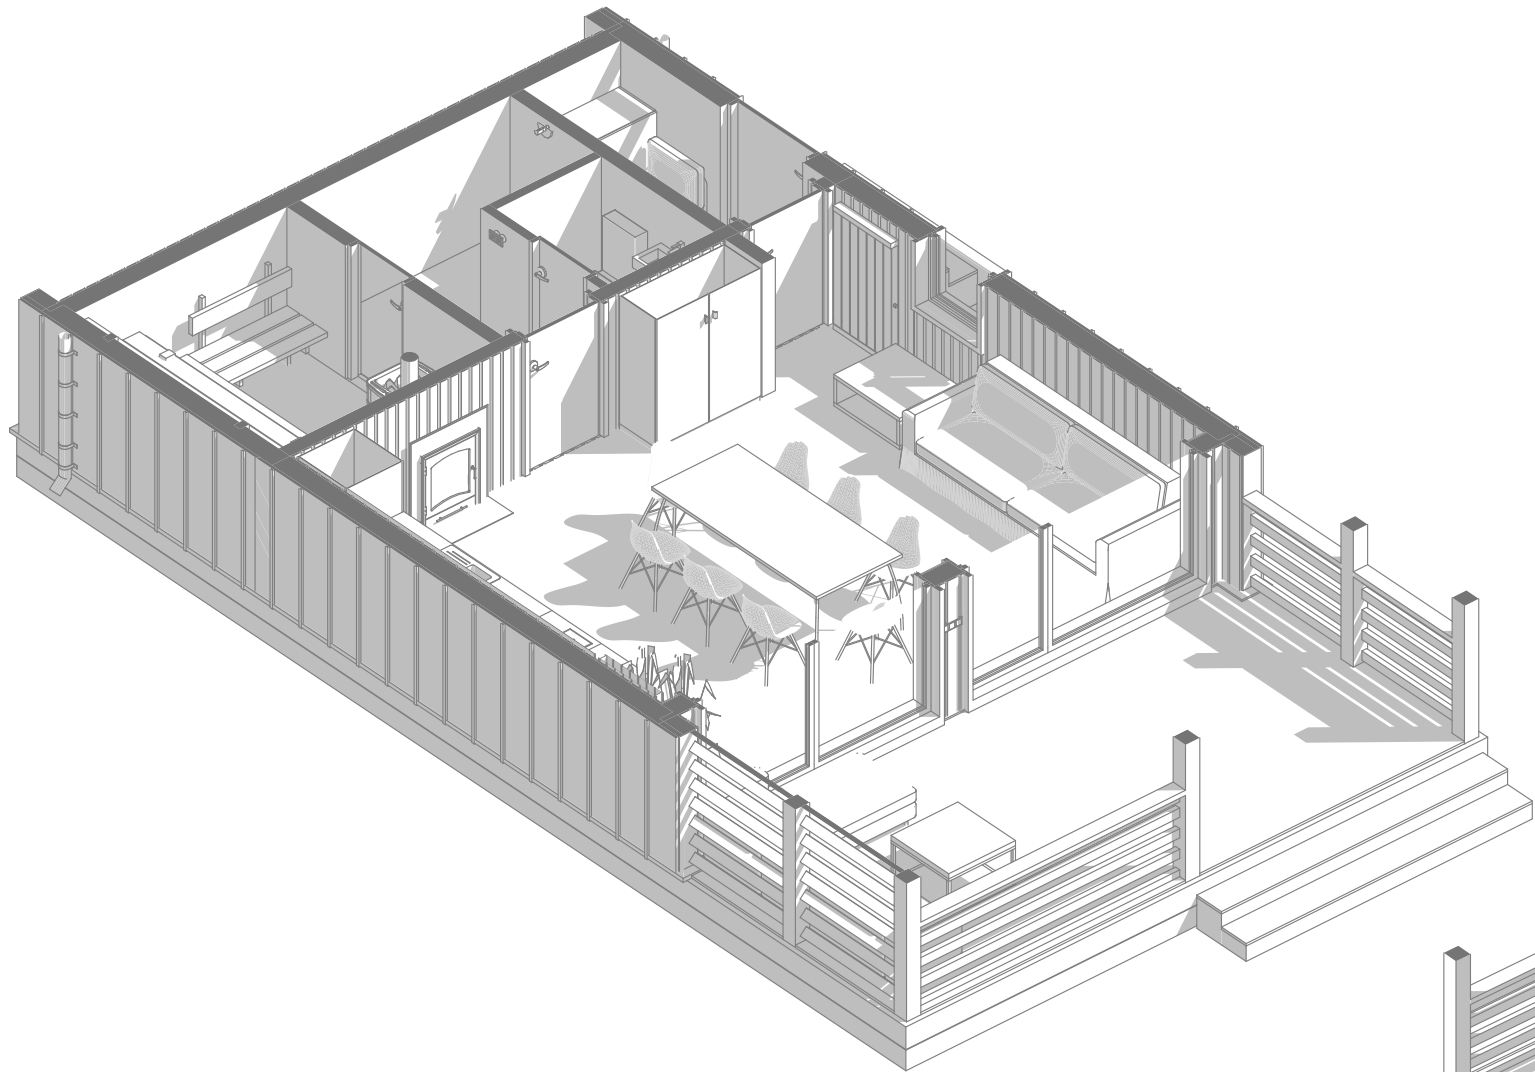

Инва. № подл.

Подп. и дата

Взам. инв. №

Лист	Изм.	№ Докум.	Подп.	Дата

Адрес:


Зд-разрез

#Название Организации

План тёплого электрического пола

1:50

Условные обозначения

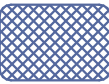
 - Контур устройства
теплого пола

Экспликация теплого пола

Наименование зоны	Площадь, м2
Помывочная	2,81
С/У	0,49
Тамбур	1,45
4,75 м²	

Примечание:

1. Отображение носит схематичный характер. Фактическая реализация выполняется в соответствии с детальными проектными решениями инженерных сетей.

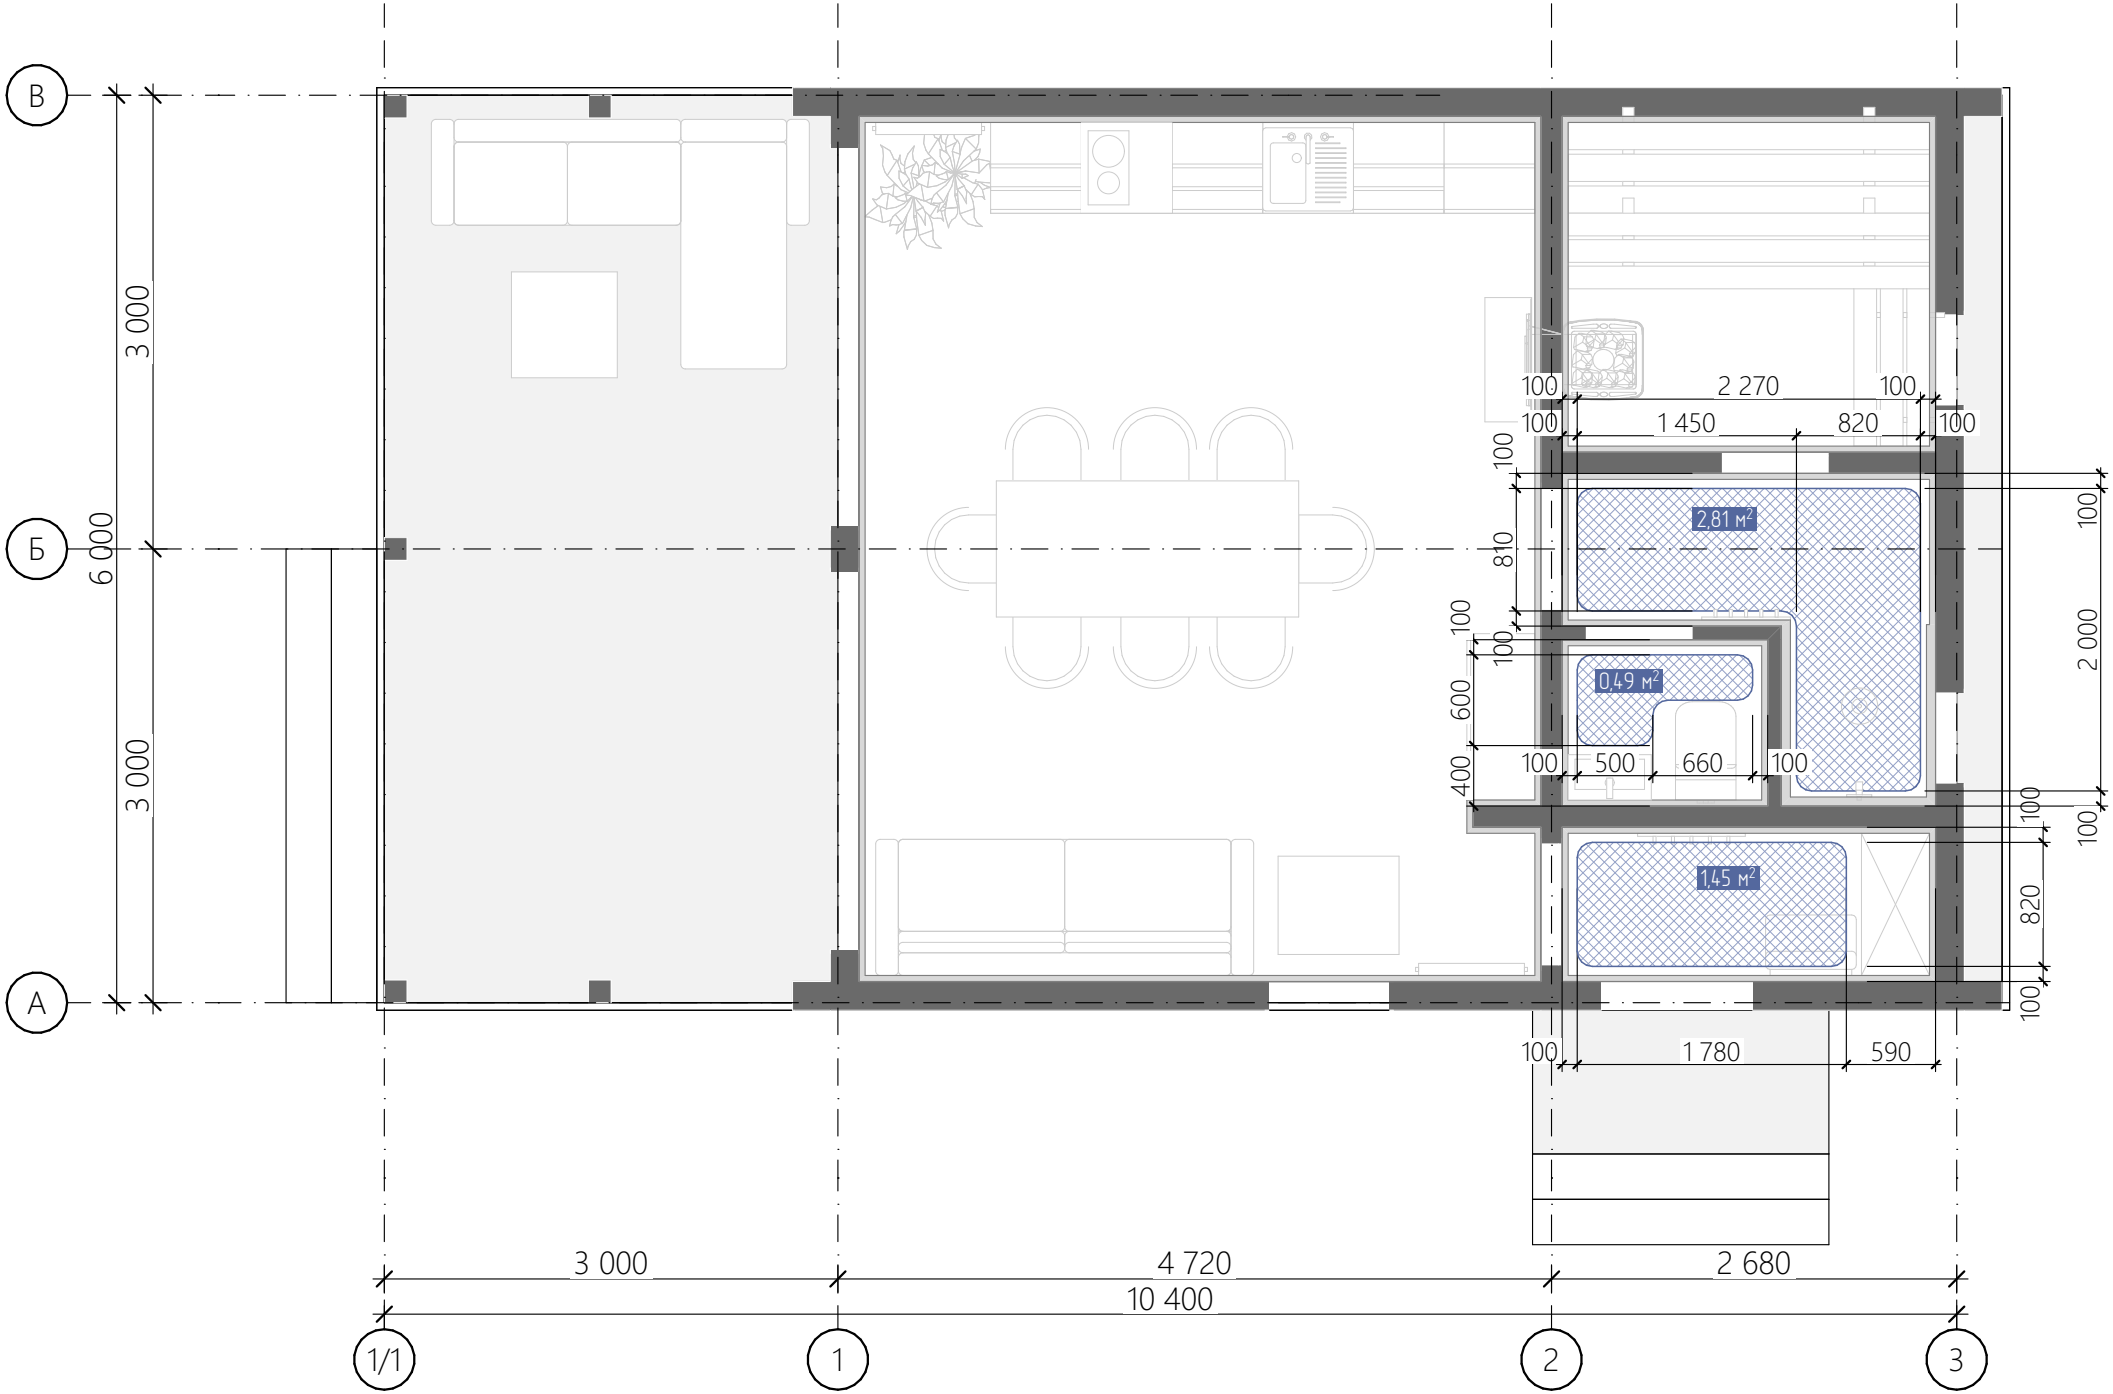

Согласовано				
И-нв. № подл.	Подп. и дата	Взам. инв. №		

Лист	Изм.	№ Докум.	Подп.	Дата

Адрес:


План электрического теплого
пола

#Название Организации

План покрытия пола

1:50

Условные обозначения

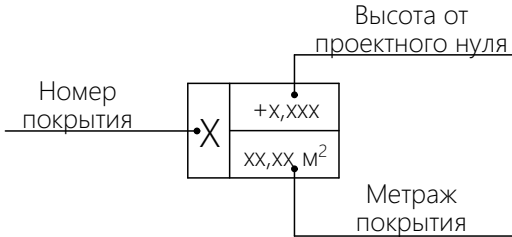


Ведомость покрытий пола

№	Наименование	м2
1	ДПК- террасная доска	21,54
2	ламинат	25,73
3	керамогранит	13,21

Примечание:

1. Приведённые цветовые решения носят рекомендательный характер. Фактический подбор оттенков и материалов выполняется на этапе реализации с учётом наличия продукции у поставщиков и утверждения заказчиком.

2. Пирог покрытия смотреть на след. листе.

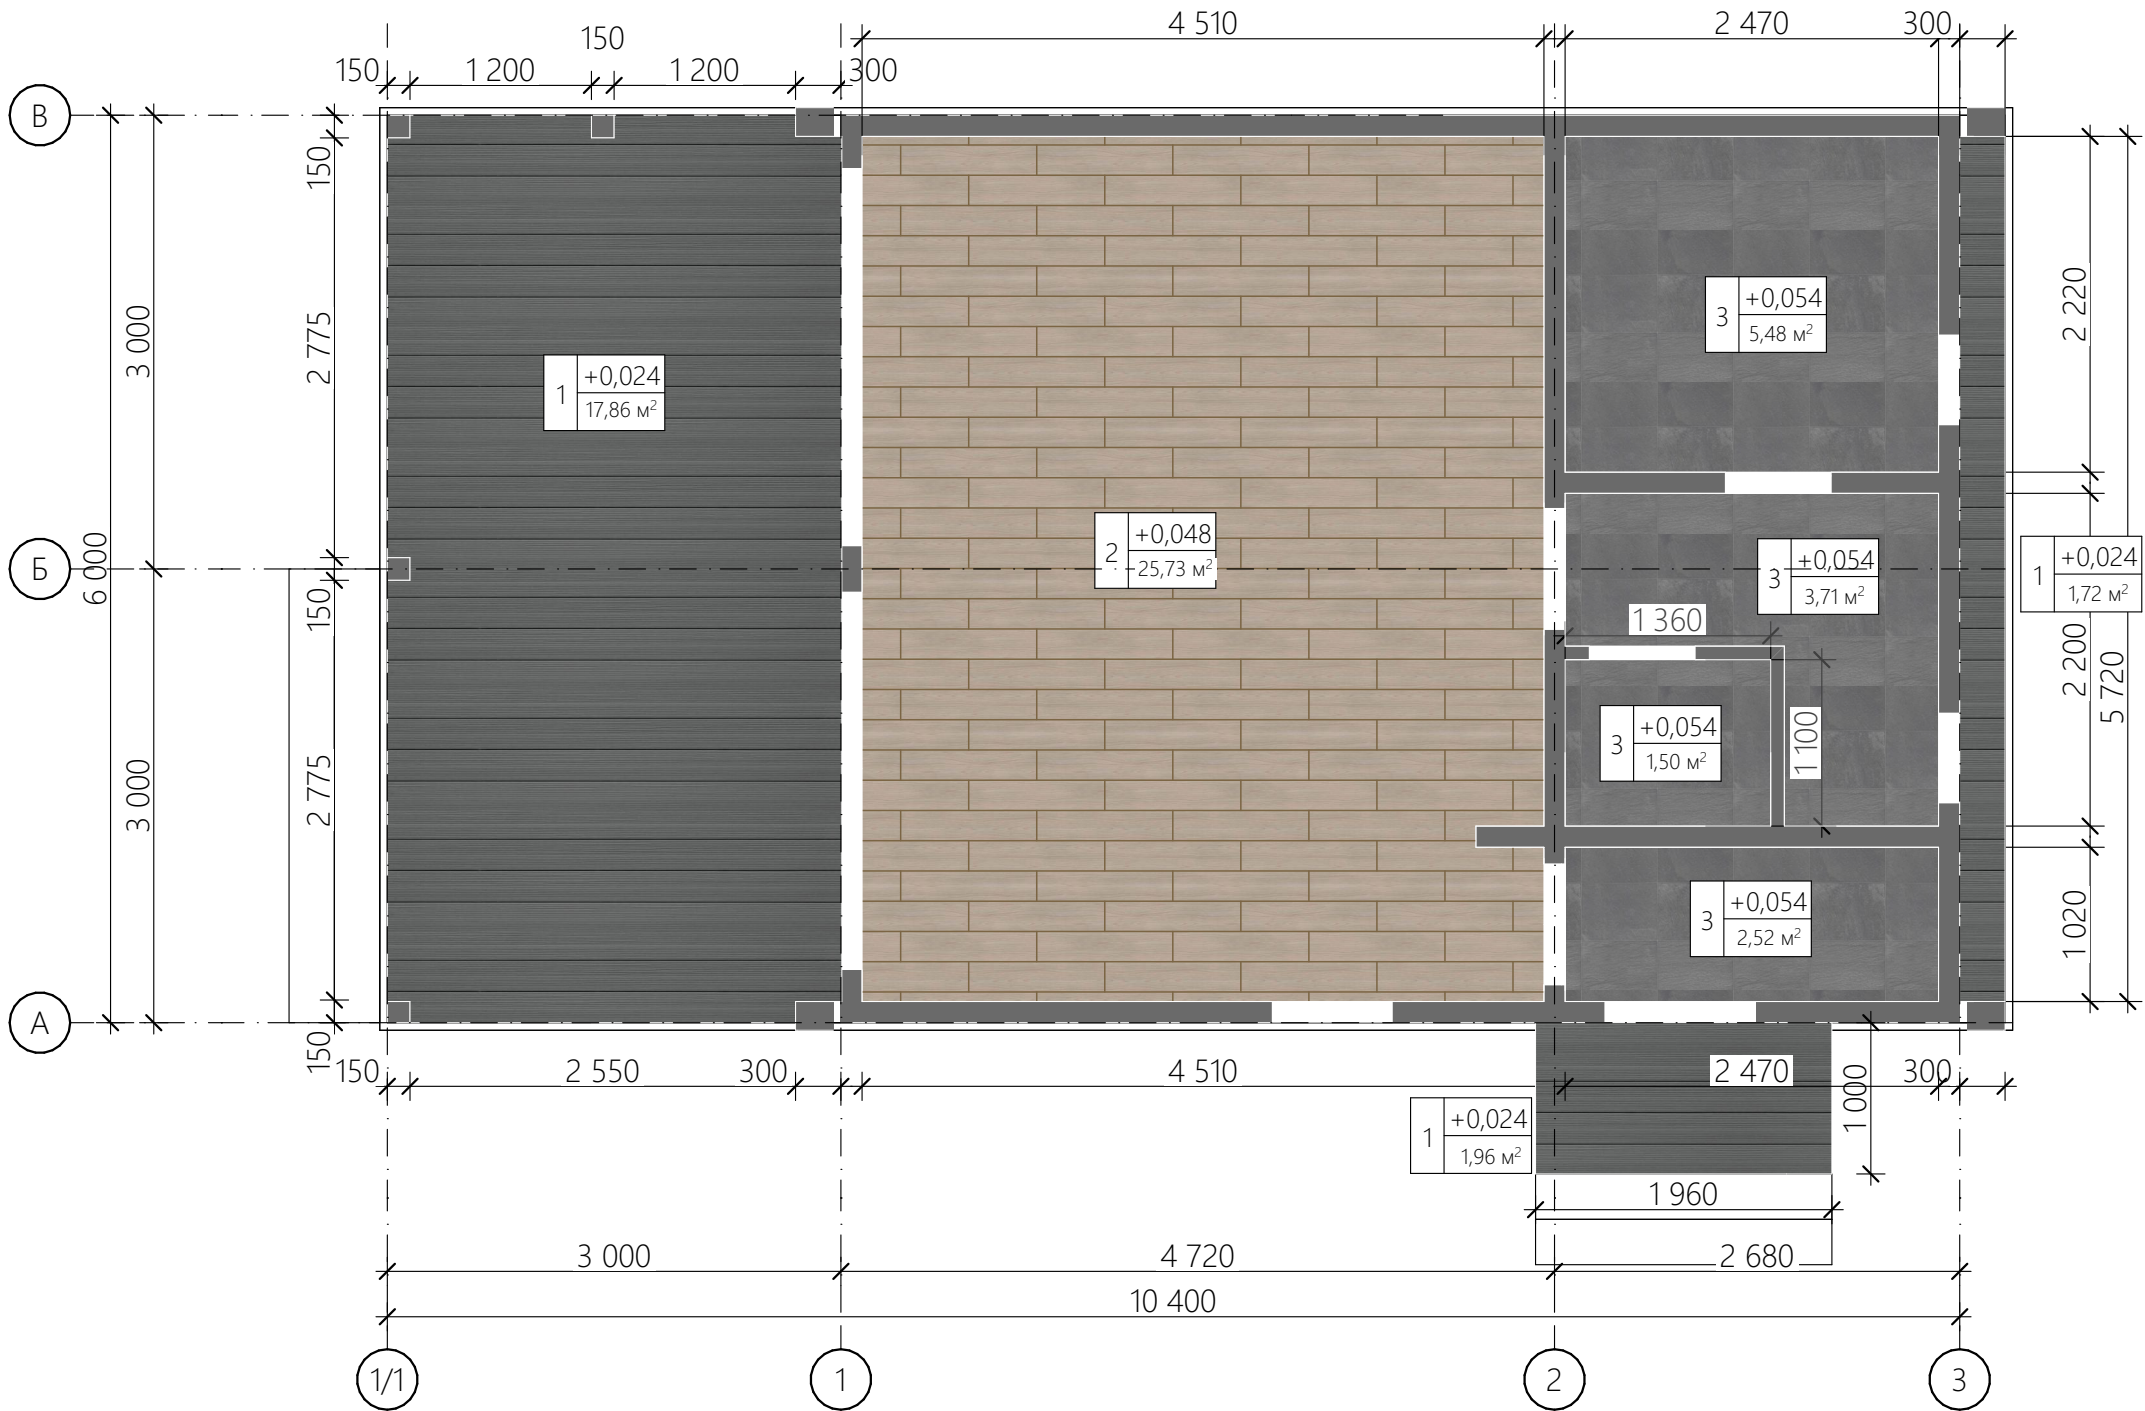

Согласовано				
И-нв. № подл.	Подп. и дата	Взам. инв. №		




Лист	Изм.	№ Докум.	Подп.	Дата

Адрес:

План покрытий пола

#Название Организации

Экспликация покрытий пола

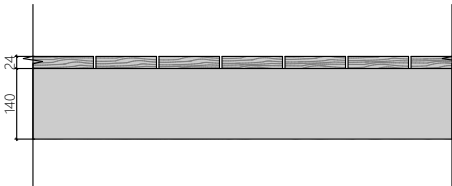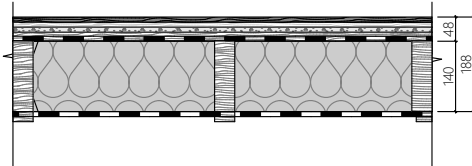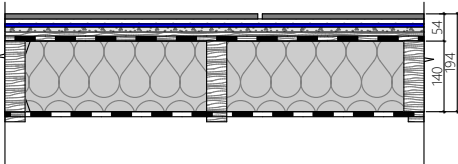№	Наименование	Разрез	Состав
1	Террасная доска		-Террасная доска 24мм -Лага, доска 140х45мм 140 мм
2	Ламинат		-Ламинат 10мм -Подложка под ламинат 10мм -ЦСП 10мм -ОСБ 18мм
3	Керамогранит		-Керамогранит 10мм -Клей 10мм (с устройством теплого эл. пола) -Руспанель 6мм -ЦСП 10мм -ОСБ 18мм

Согласовано				


Инд. № подл.	Подп. и дата	Взам. инв. №

Лист	Изм.	№ Докум.	Подп.	Дата	Экспликация покрытий пола	#Название Организации	Лист
							10

Согласовано				
И-нв. № подл.	Подп. и дата		Взам. инв. №	

План отделки стен

1:50

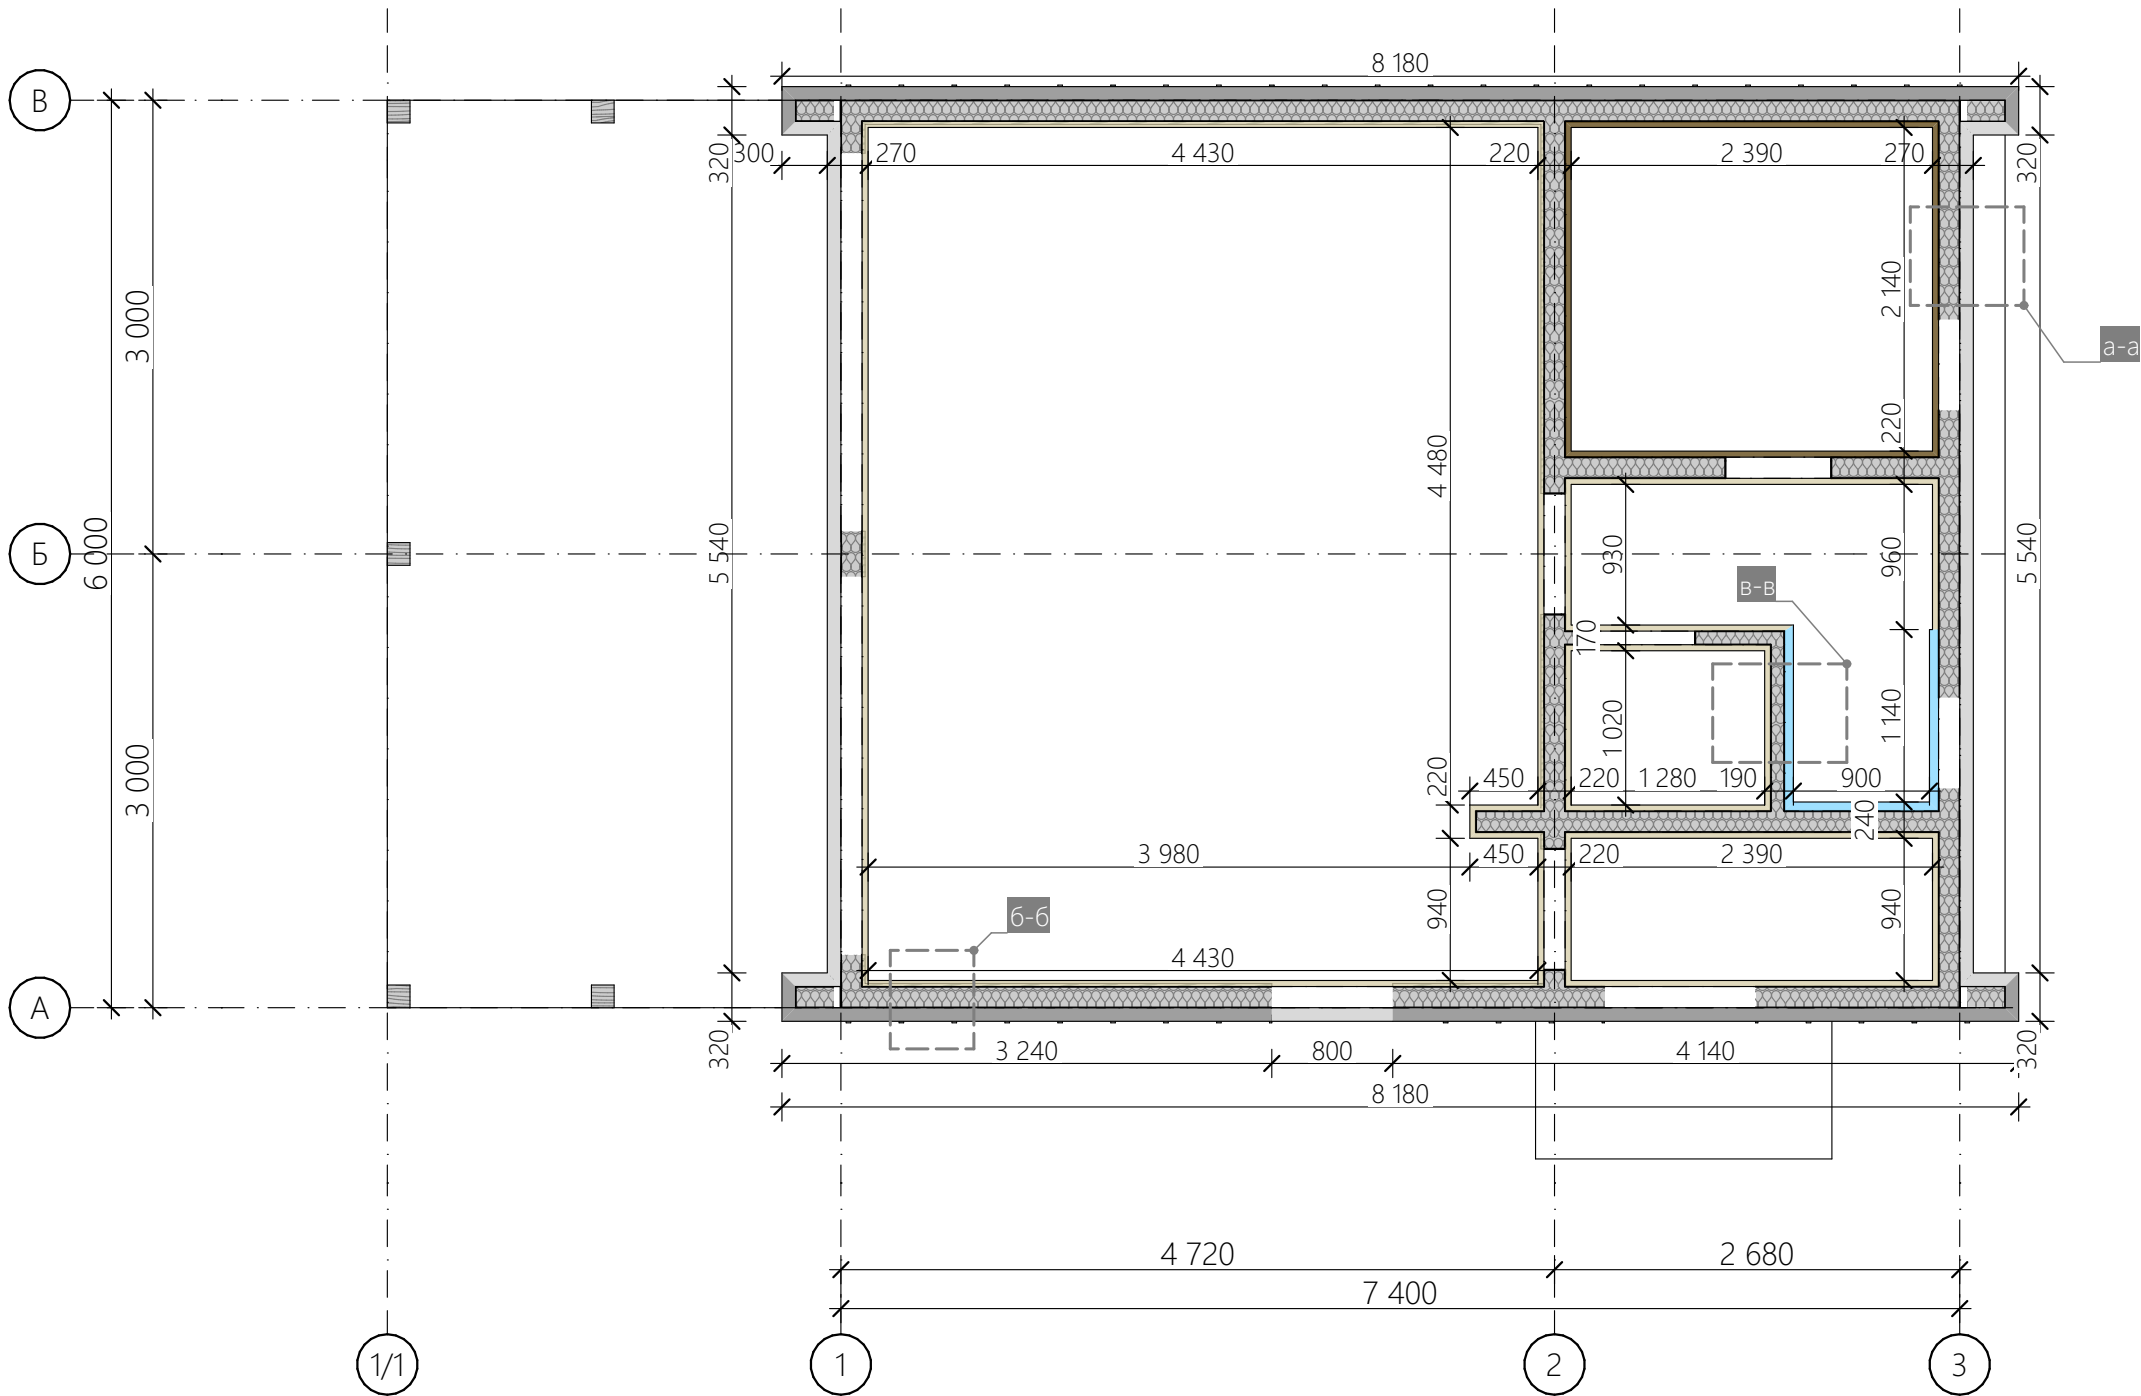

Ведомость покрытий стен

№	Наименование	Условное обозначение
1	Планкен (20мм)	
2	Фальц	
3	Имитация бруса (20мм)	
4	Вагонка (16мм)	
5	Керамогранит (10мм)	

Примечание:

1. Сечение по стенам смотреть на след. листе

Лист	Изм.	№ Докум.	Подп.	Дата

Адрес:

План покрытия отделки стен

#Название Организации


Экспликация отделки стен

№ разреза

Сечение


Состав

а-а

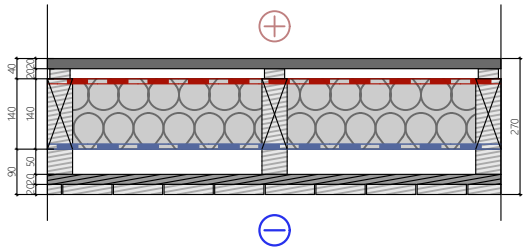


-Вагонка	20мм
-Обрешётка	20мм
-Пароизоляционная мембрана (алюминиевая фольга)	
-Стойка каркаса (утеплённая)	140мм
-Гидро-ветрозащитная мембрана	
-Вентбрусок (вертикально)	50мм
-Обрешётка	20мм
-Планкен	20мм

б-б

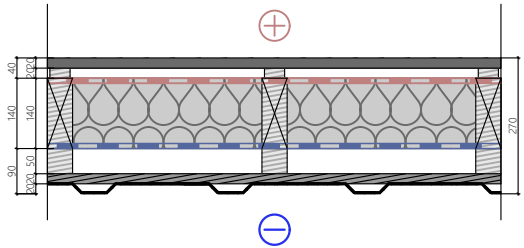

-Имитация бруса	20мм
-Вентбрусок (вертикально)	20мм
-Пароизоляционная мембрана	
-Стойка каркаса (утепленная)	140мм
-Гидро-ветрозащитная мембрана	
-Вентбрусок (вертикально)	50мм
-Обрешётка	20мм
-Фальц	

в-в

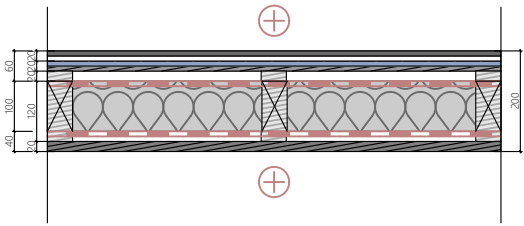

-Керамогранит	10мм
-Клей	10мм
-Руспанель	10мм
-ОСБ	9мм
-Обрешётка	20мм
-Пароизоляционная мембрана	
-Стойка каркаса (утепленная)	90мм
-Пароизоляционная мембрана	
-Вентбрусок (вертикально)	20мм
-Имитация бруса	20мм

Согласовано

Взам. инв. №

Подп. и дата

Инв. № подл.

Лист	Изм.	№ Докум.	Подп.	Дата

Экспликация отделки стен

#Название Организации

Лист


12

План расстановки розеток

1:50

Условные обозначения:

-  - розетка 220V с заземлением
-  - розетка 220V с заземлением и влагозащитой
-  - розетка для ТВ
-  - интернет - розетка
-  - электровывод

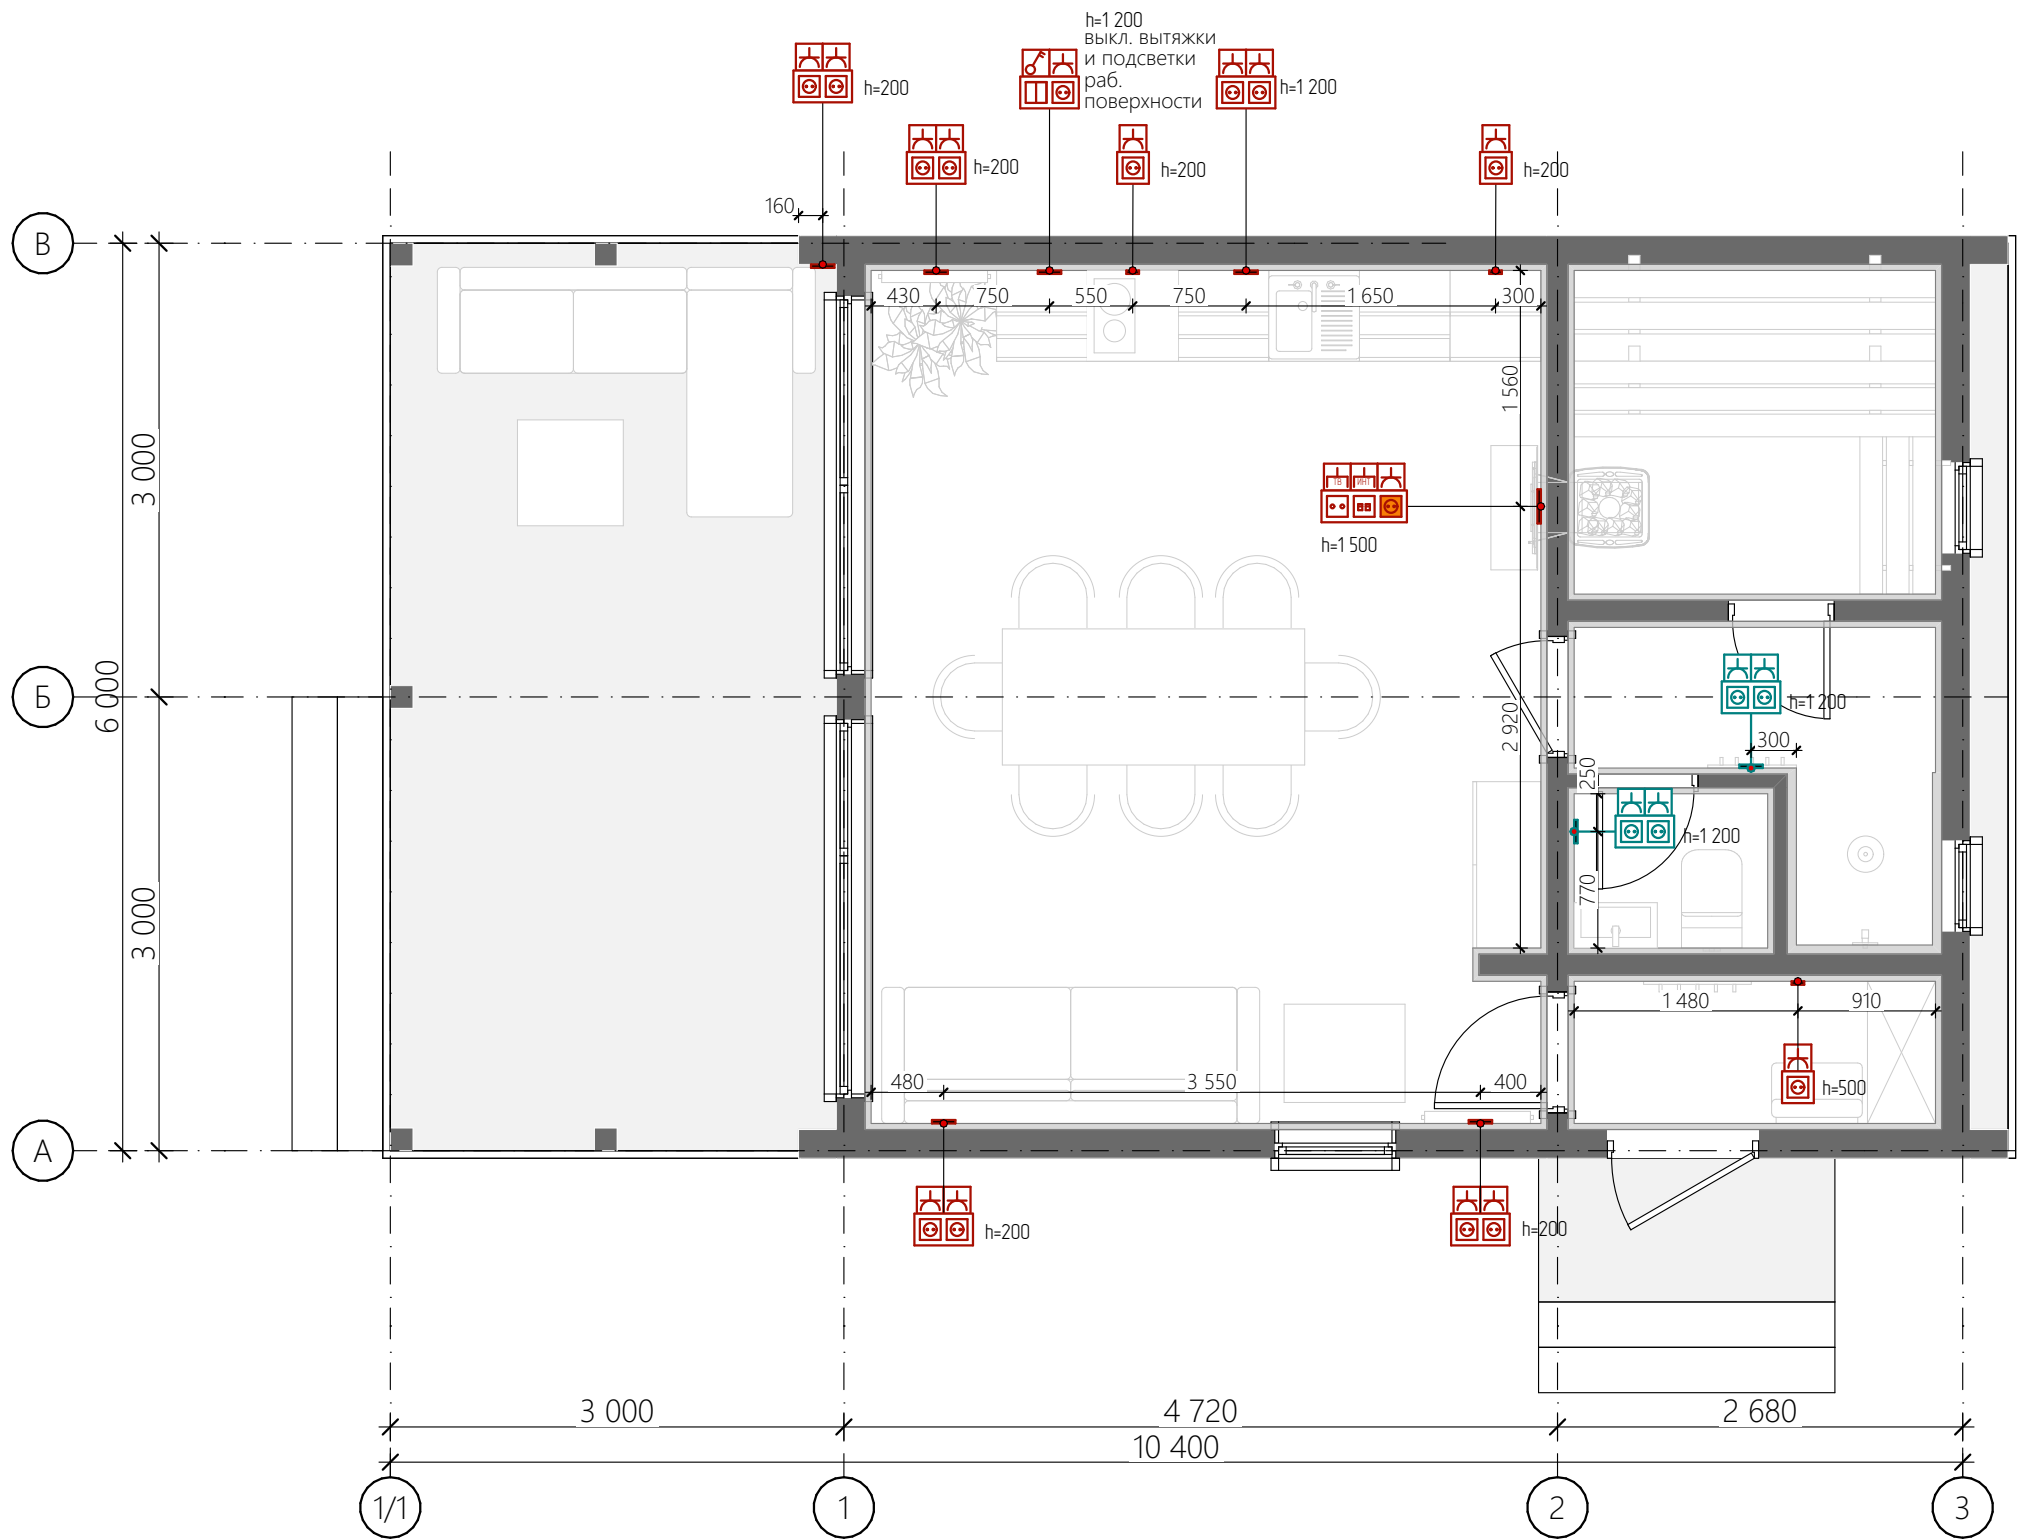

- Примечание:
1. Схема размещения розеток является рекомендательной и требует согласования с заказчиком по месту.
 2. Все высоты даны от чистового пола.
 3. Все указанные размеры даются до центра позиций.
 4. Отметки розеток, выключателей, выводов и др. оборудования, являются предварительными и уточняются после выбора финишных материалов и мебели.
 5. Размеры уточняются дополнительно

Согласовано				
Изм. № подл.				
Подп. и дата				
Взам. инв. №				

Лист	Изм.	№ Докум.	Подп.	Дата

Адрес:

План размещения розеток
стен


#Название Организации

План светильников и выключателей

1:50

Условные обозначения:

-  - выключатель одноклавишный
-  - выключатель двухклавишный
-   - люстра
-  - точечный светильник
-  - настенные бра
-  - контурная подсветка
-  - трековый светильник

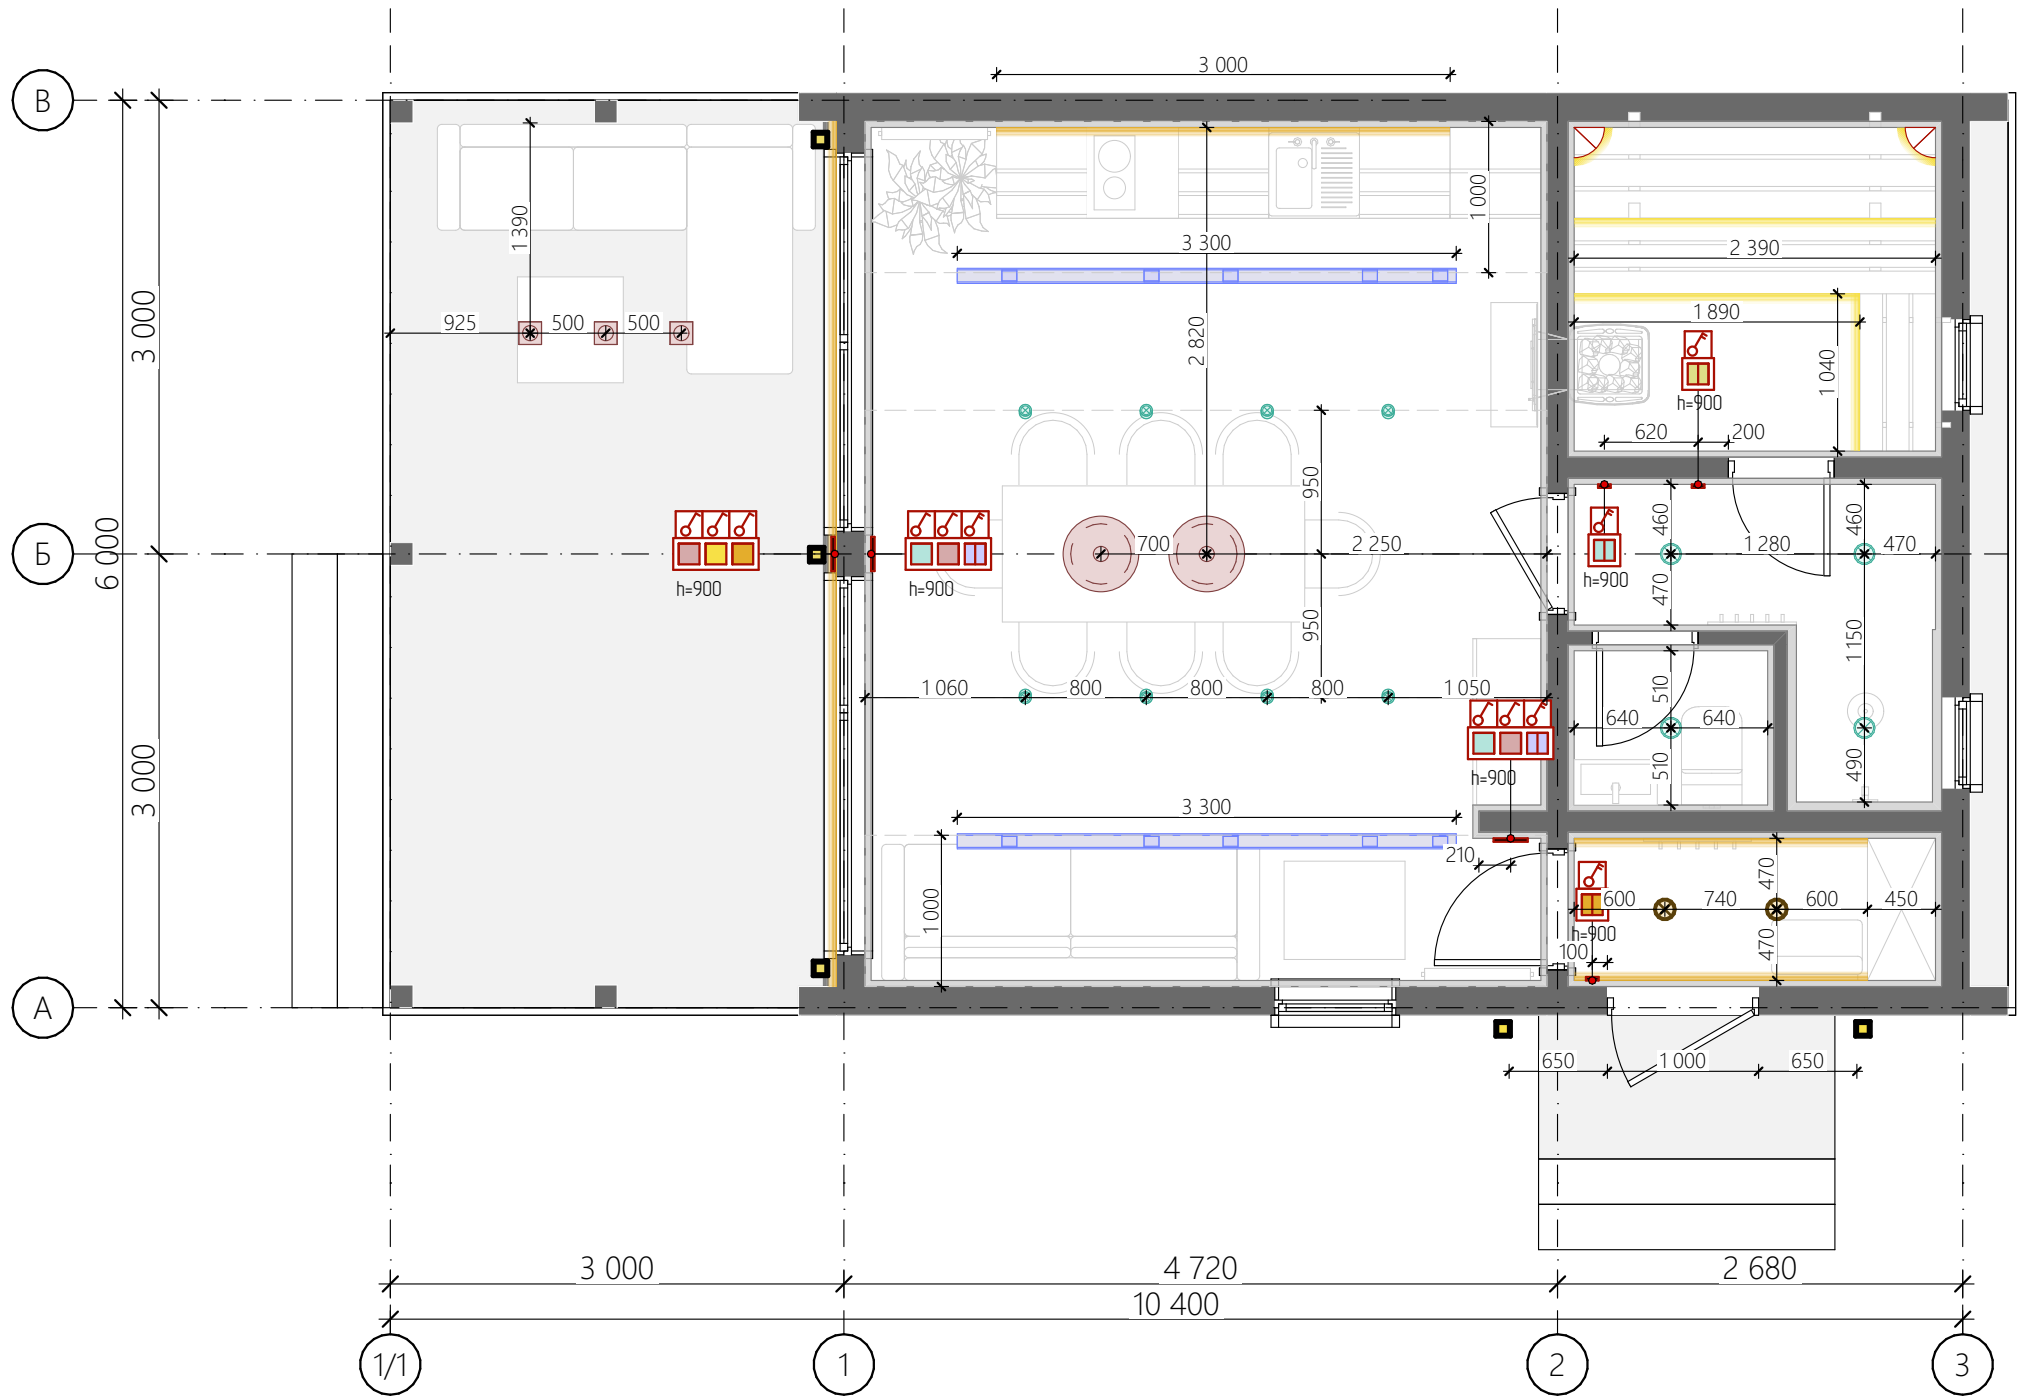

Примечание:

1. Схема размещения розеток является рекомендательной и требует согласования с заказчиком по месту.
2. Все высоты даны от чистового пола.
3. Все указанные размеры даются до центра позиций.
4. Отметки розеток, выключателей, выводов и др. оборудования, являются предварительными и уточняются после выбора финишных материалов и мебели.
5. Размеры уточняются дополнительно

Согласовано				
Взам. инв. №				
Подп. и дата				
Инв. № подл.				

Лист	Изм.	№ Докум.	Подп.	Дата

Адрес: _____

План расстановки
светильников и
выключателей


#Название Организации _____

План кровли


1:50

Условные обозначения:

- Кровля бани
- Подшив свесов бани

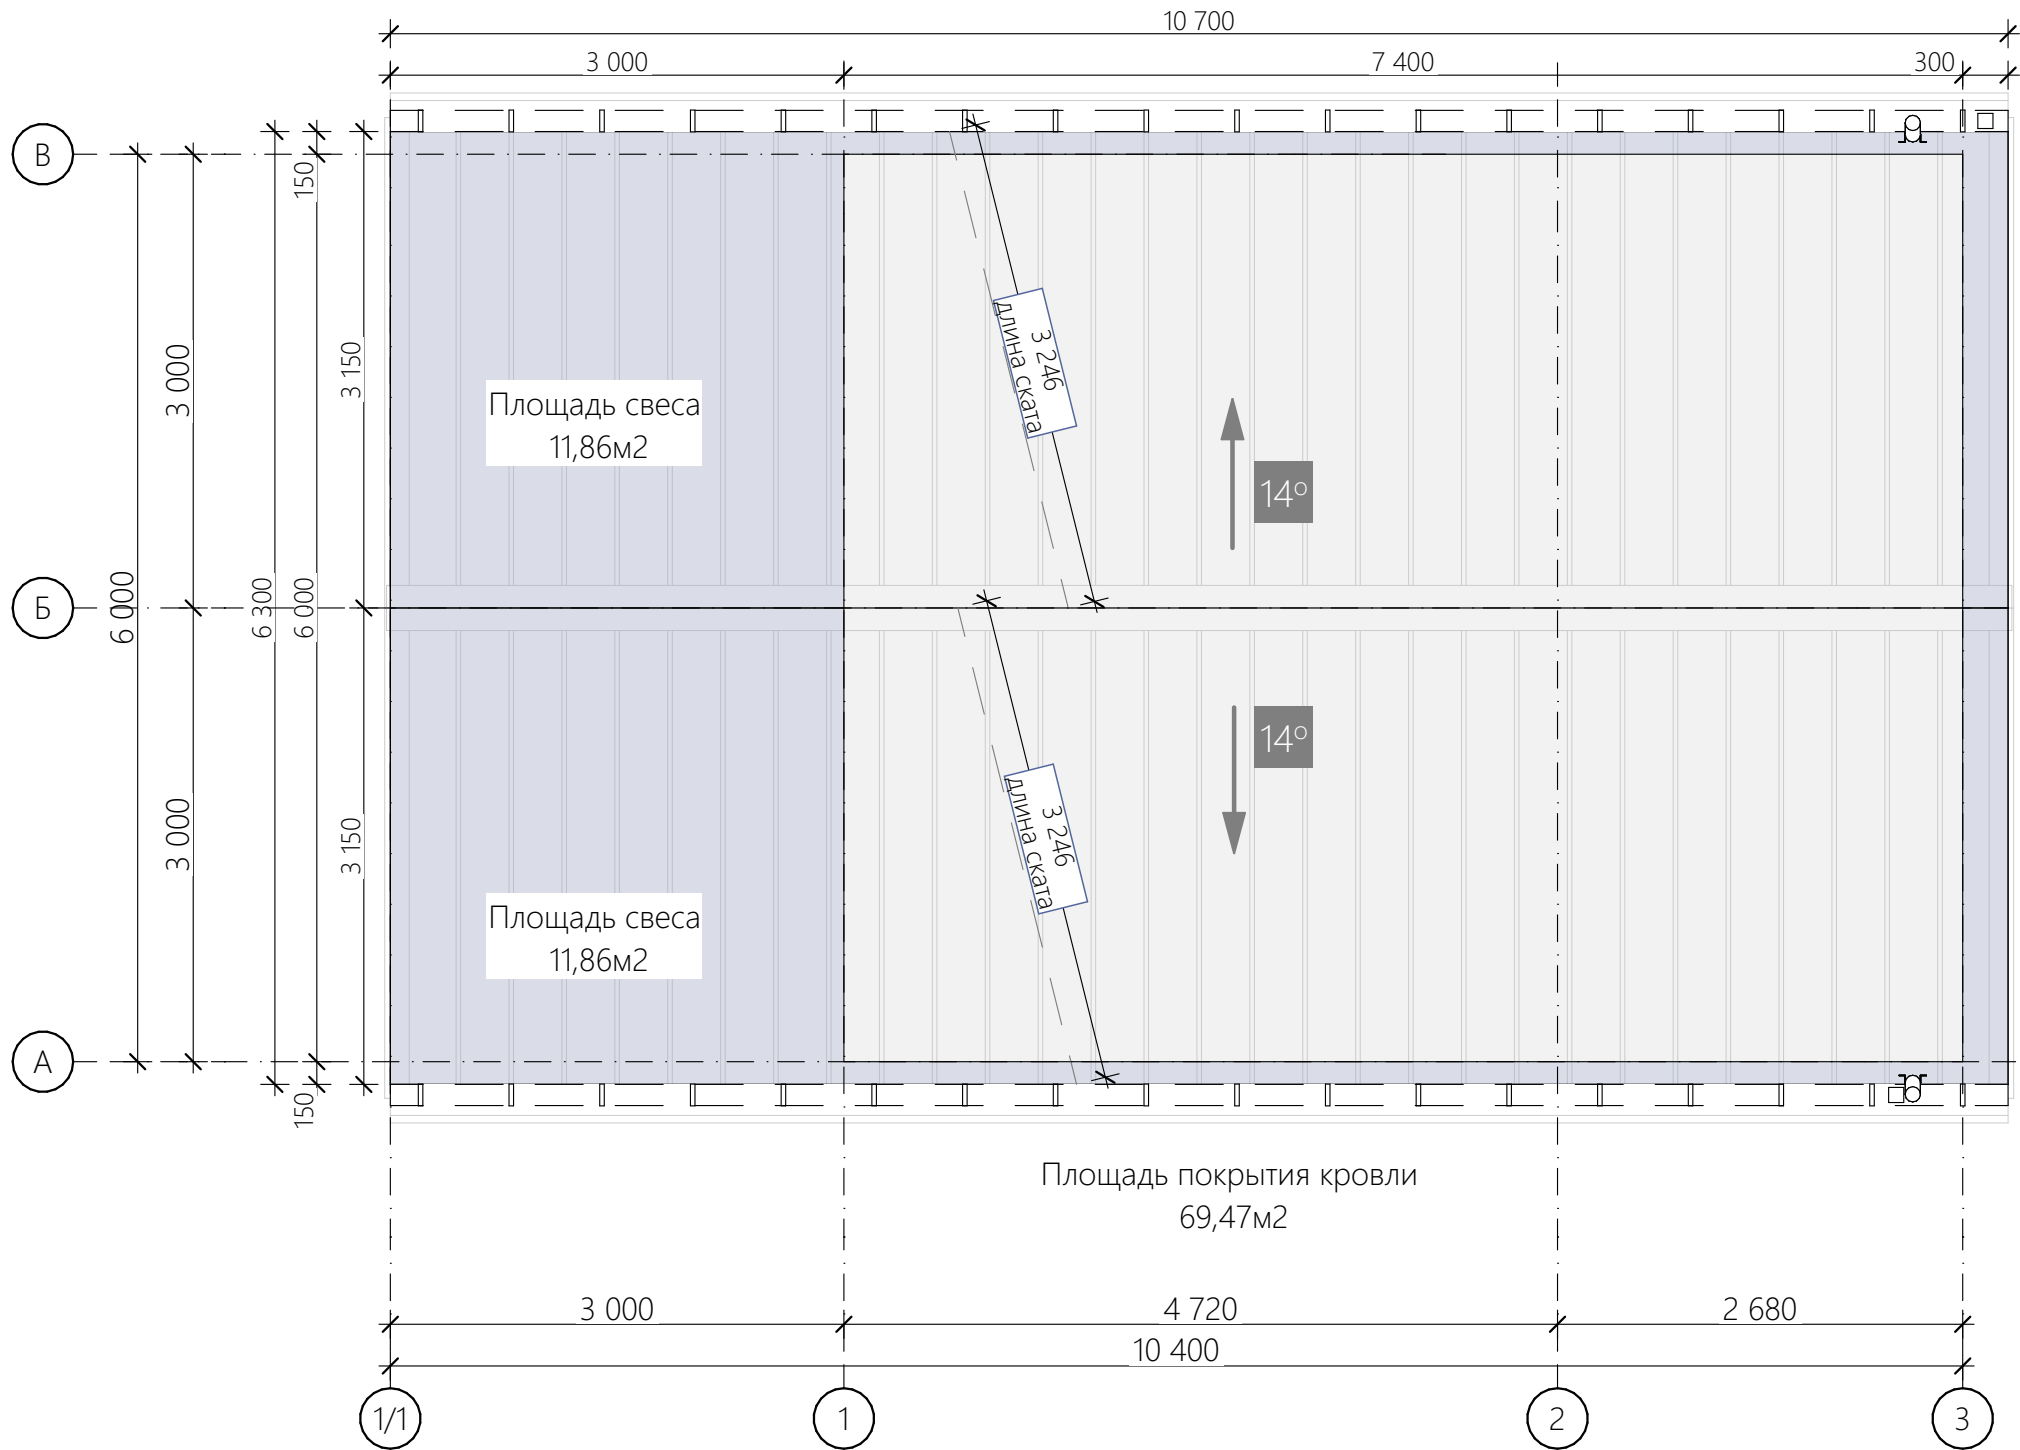

аксонометрия кровли:

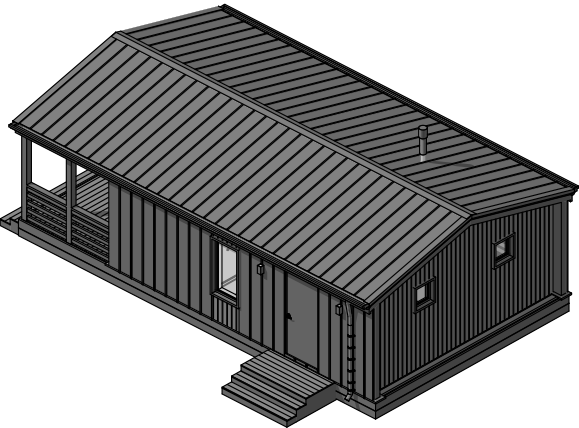

Согласовано			

И-нв. № подл.	Подп. и дата	Взам. инв. №	


Лист	Изм.	№ Докум.	Подп.	Дата

Адрес:


План кровли



#Название Организации

1:40

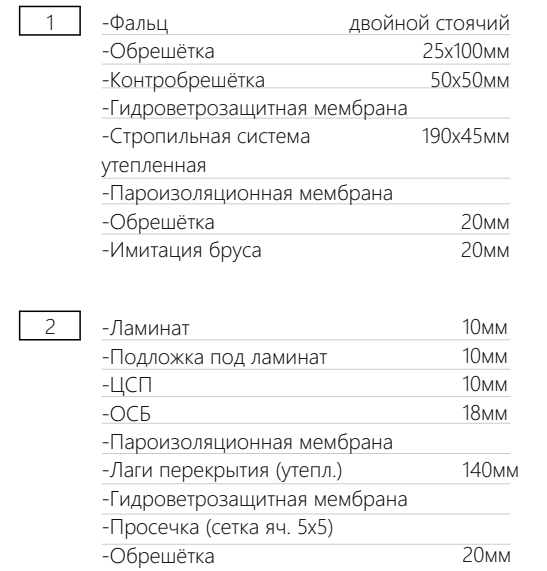

1:40

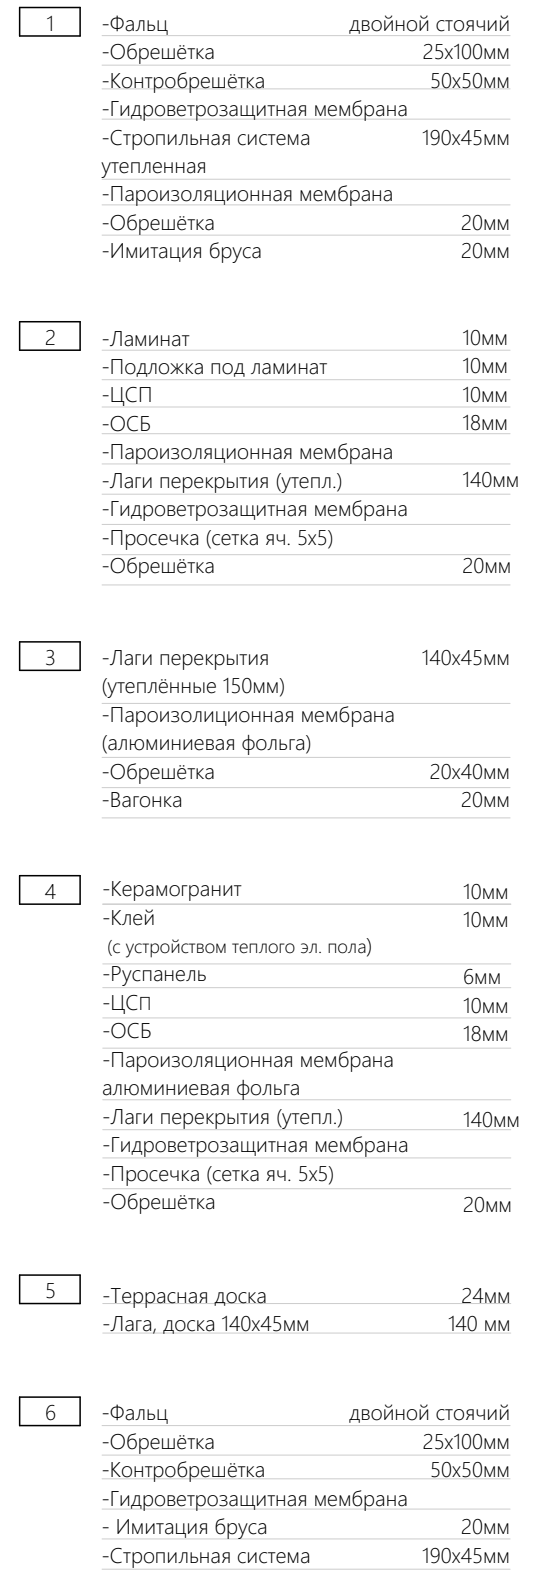


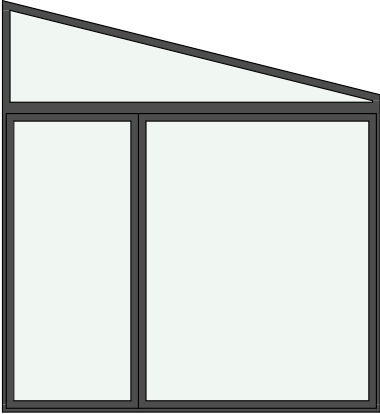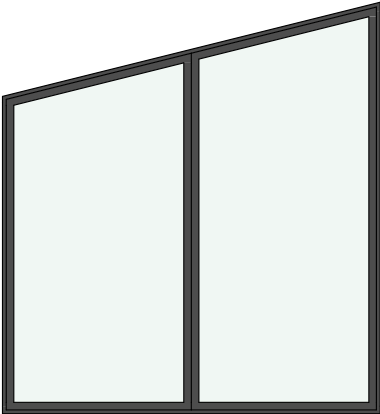
Ведомость оконных проемов									
Наименование		Размеры проема		Ш x В, мм		Вид		Площадь, м2	
ДН-1		2 500		2 723				6,03	
ОК-1		2 500		2 723				6,03	
ОК-02		600		600				0,36	
ОК-03		800		1 450				1,16	
								13,94 м²	
Примечание: 1. Изготовление окон и дверей определяется заказчиком, допускается изменение открывания окон и дверей; 2. При заказе оконных и дверных блоков необходим обмер по месту от изготовителя; 3. Оконные и дверные изделия изображены со стороны открывания.									
Инв. № подл.	Подп. и дата	Взам. инв. №	Лист			Изм.	№ Докум.	Подп.	Дата
			Ведомость оконных проёмов						
			#Название Организации						
						Лист			
						18			


Ведомость дверных проемов

Наименование Размеры проема Ш x В, мм Вид Площадь, м2

ДВ-1 1 000×2 200  2,20

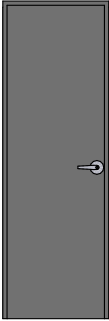ДВ-2 700×2 100  1,47

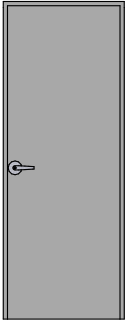ДВ-3 800×2 100  1,68

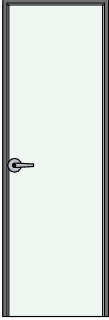ДП-1 700×2 100  1,47

8,50 м²

Примечание:

1. Изготовление окон и дверей определяется заказчиком, допускается изменение открывания окон и дверей;
2. При заказе оконных и дверных блоков необходим обмер по месту от изготовителя;
3. Оконные и дверные изделия изображены со стороны открывания.


Согласовано					
И-нв. № подл.	Взам. инв. №		Подп. и дата		

Лист	Изм.	№ Докум.	Подп.	Дата

Адрес:

Цветовое решение; Фасад в осях В-А

#Название Организации

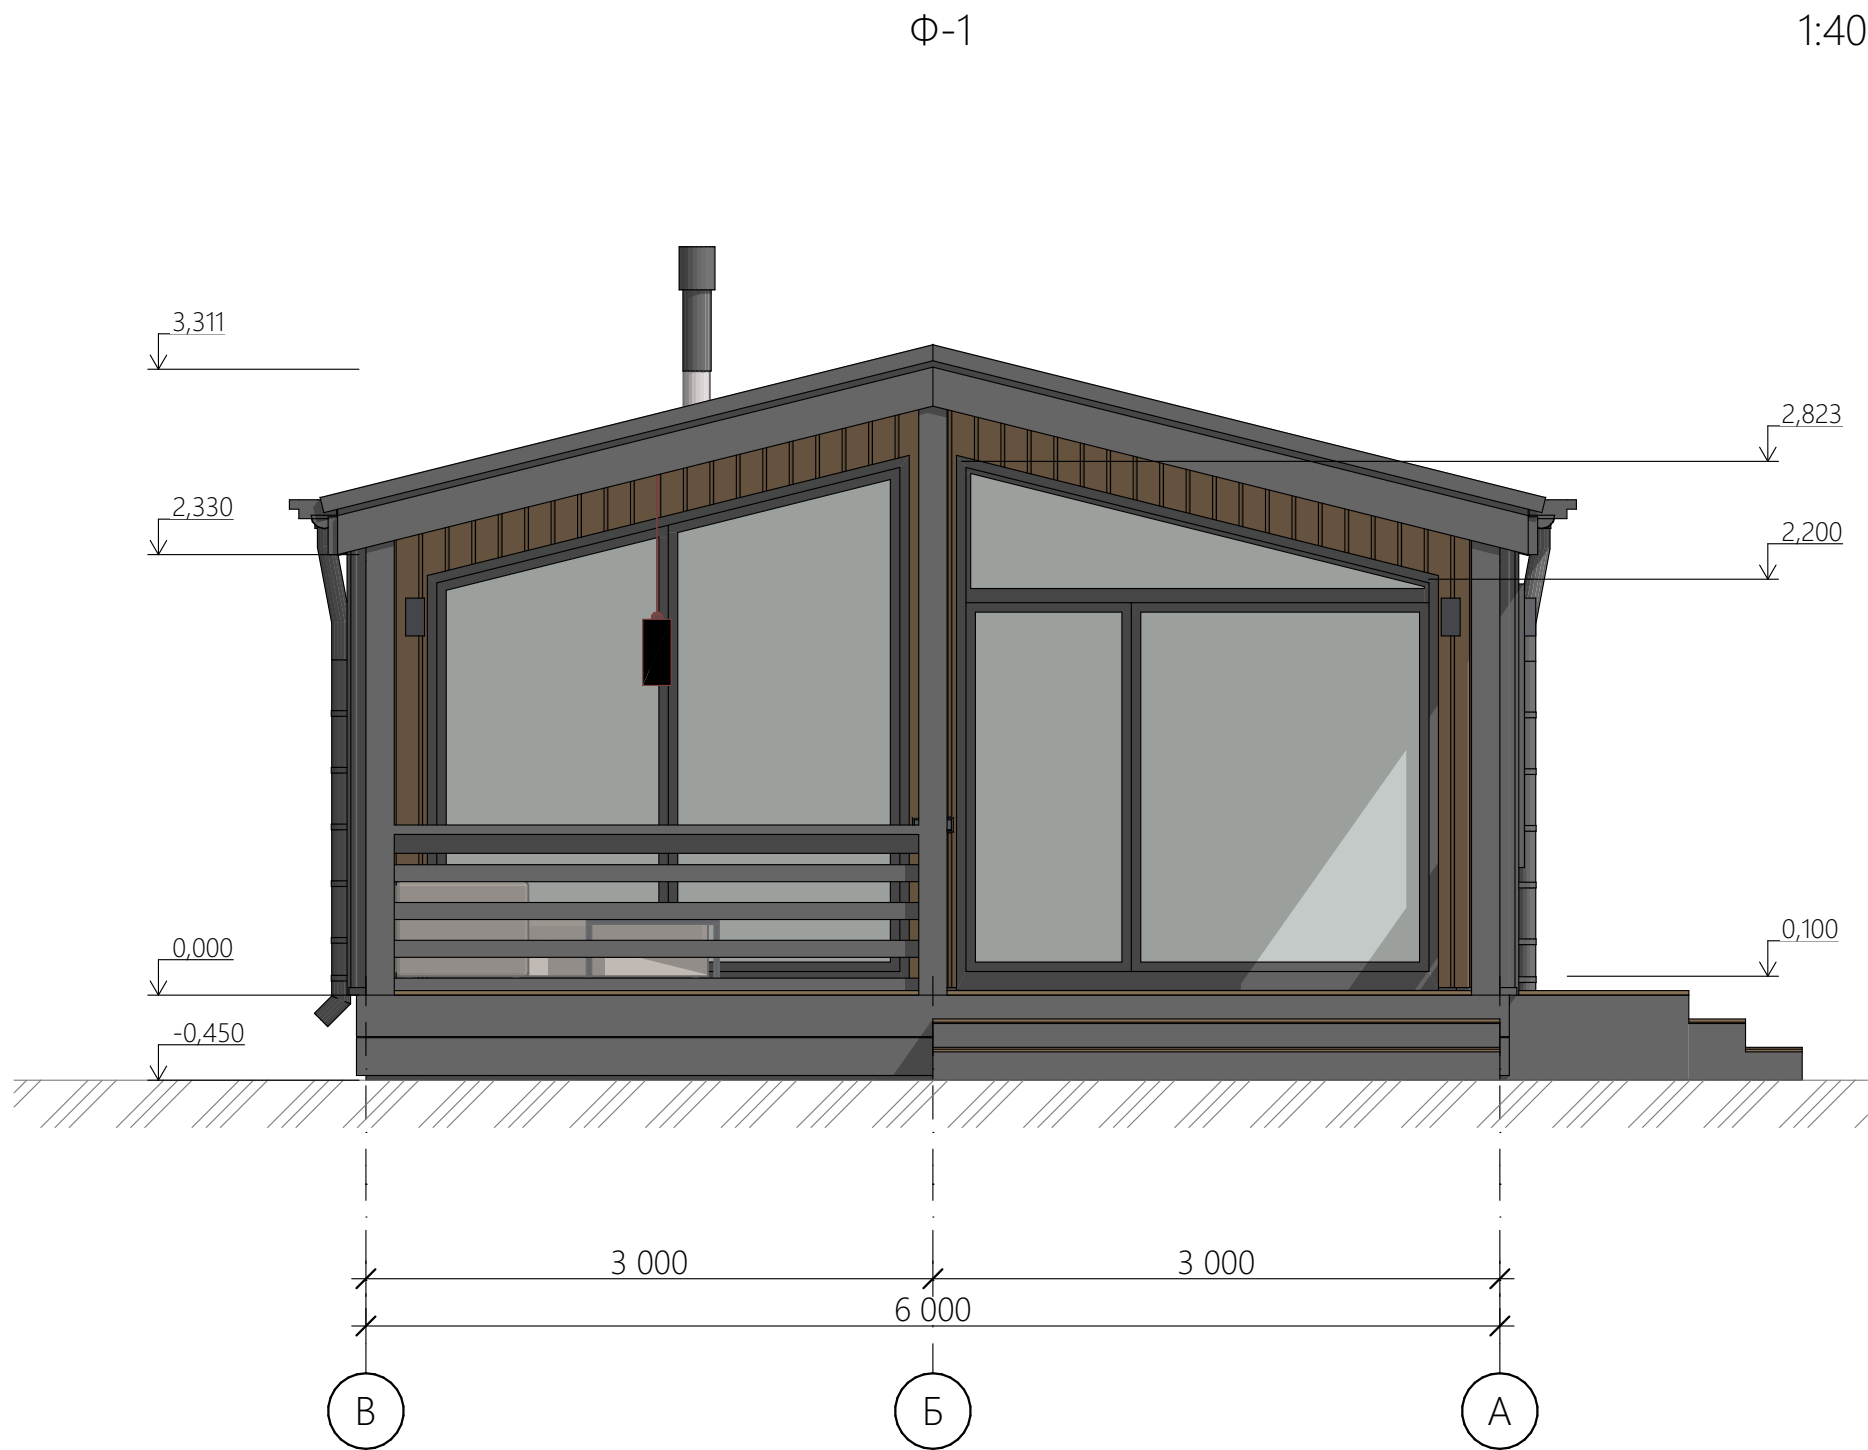

- Условные обозначения:
-  -Планкен (Цвет орех)
 -  -Террасная доска ДПК
 -  -Водосточная система, наличники, оконные рамы, кровля(RAL 7004)
 -  -Фальц

Согласовано				
И-нв. № подл.	Подп. и дата		Взам. инв. №	


Лист	Изм.	№ Докум.	Подп.	Дата

Адрес:

Цветовое решение; Фасад в осях 3-1

#Название Организации

21

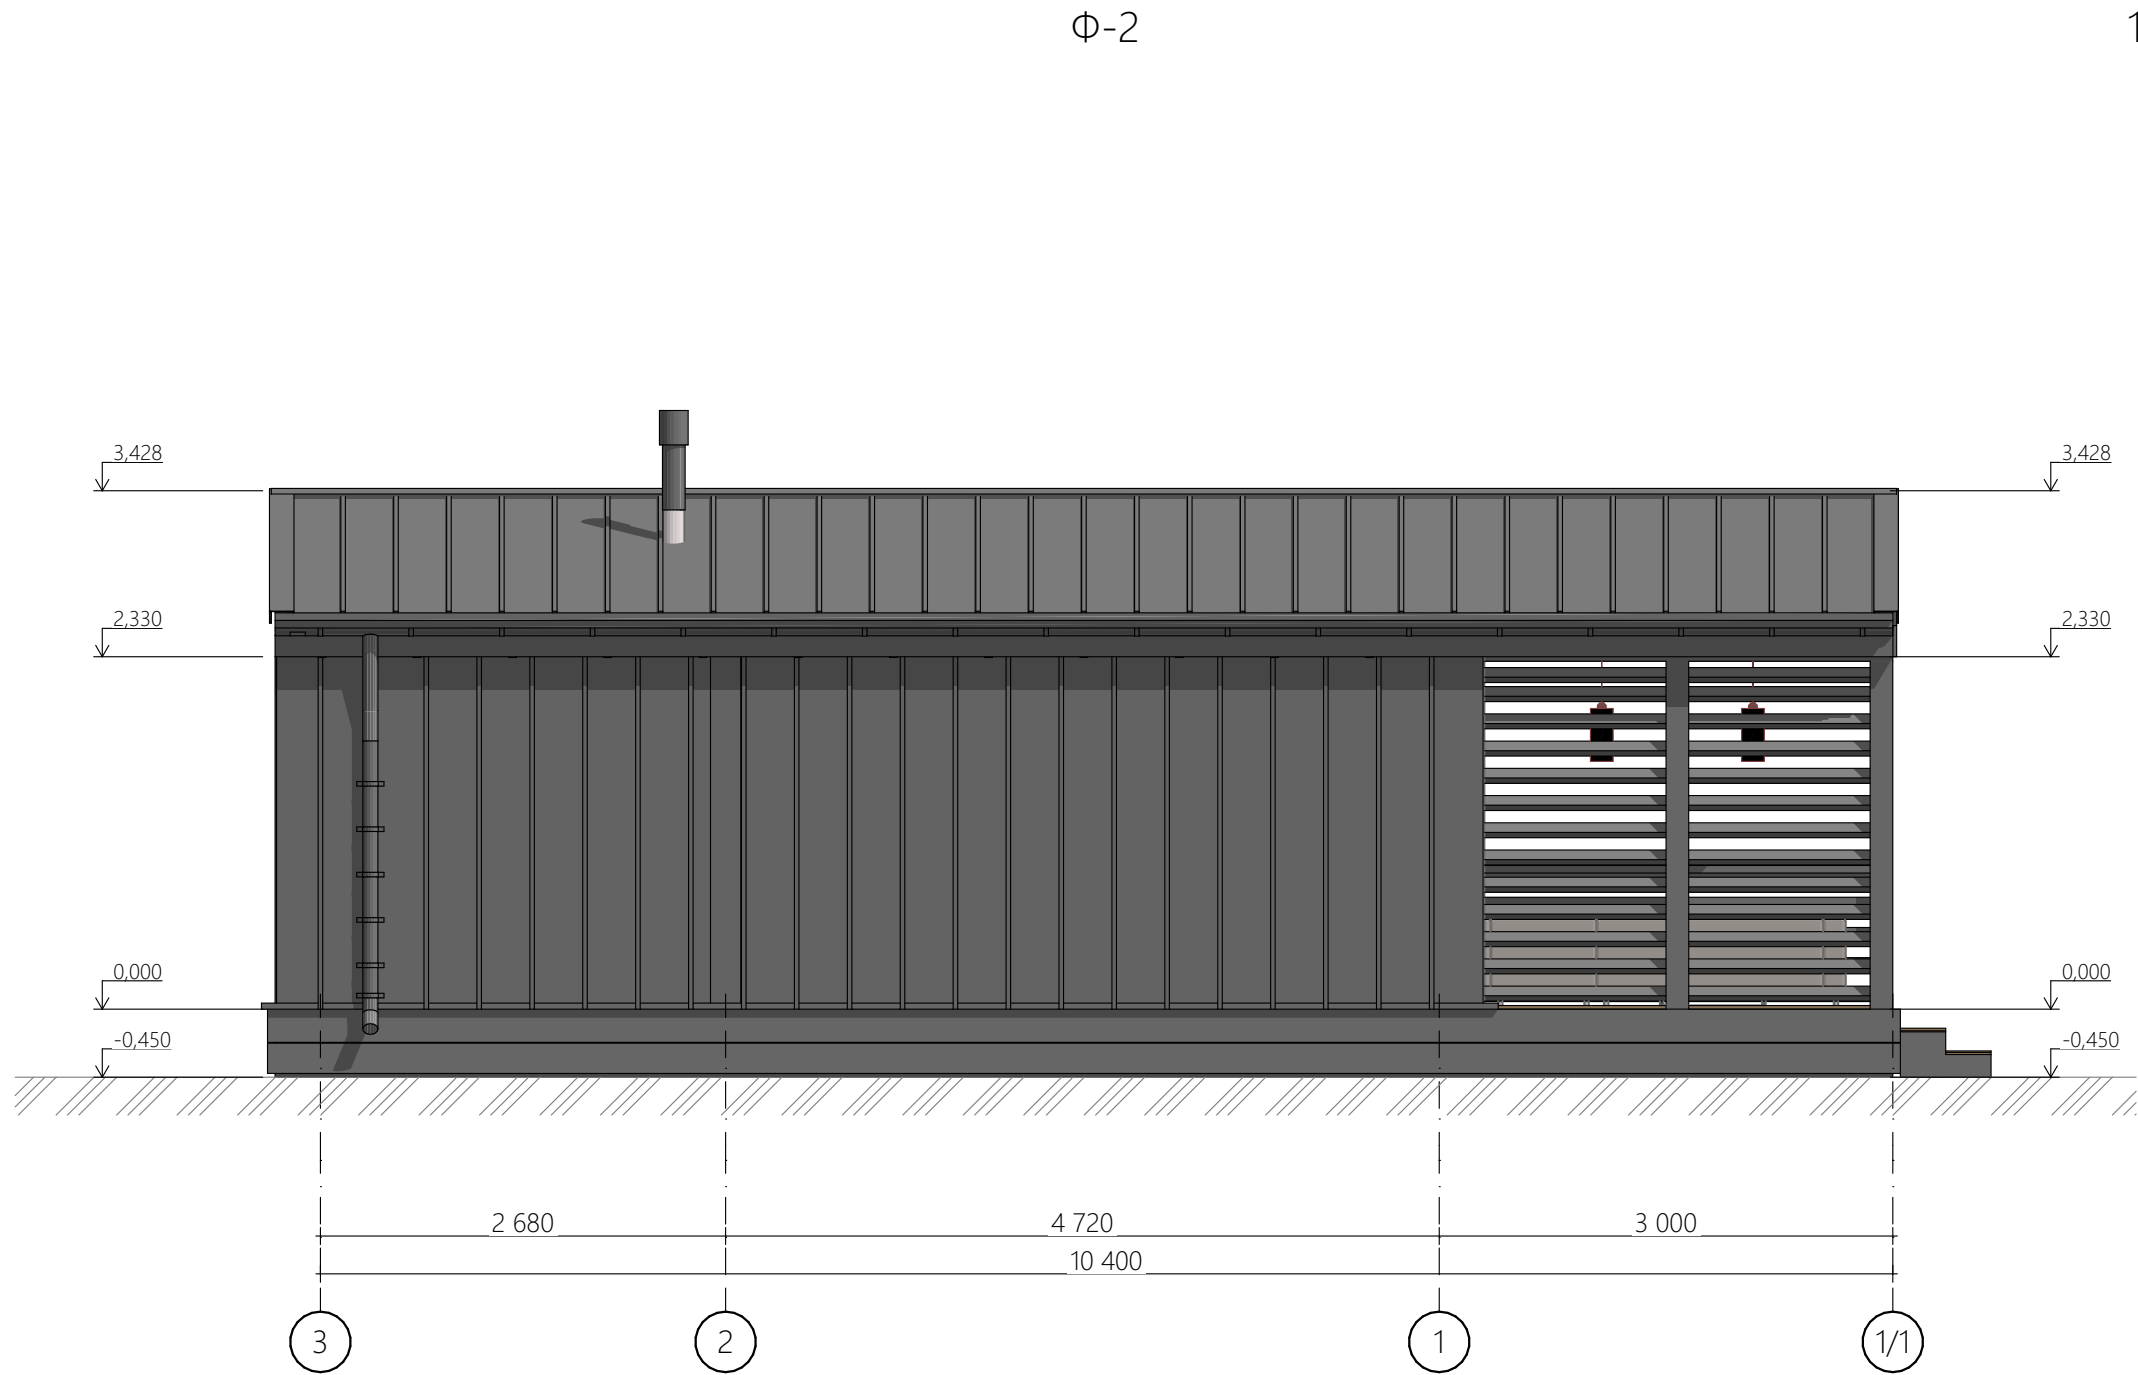

Условные обозначения:

-Планкен (Цвет орех)

-Террасная доска ДПК

-Водосточная система, наличники, оконные рамы, кровля(RAL 7004)

-Фальц

Согласовано


И-нв. № подл. Подп. и дата Взам. инв. №

Лист	Изм.	№ Докум.	Подп.	Дата

Адрес:

Аксометрия №1

#Название Организации

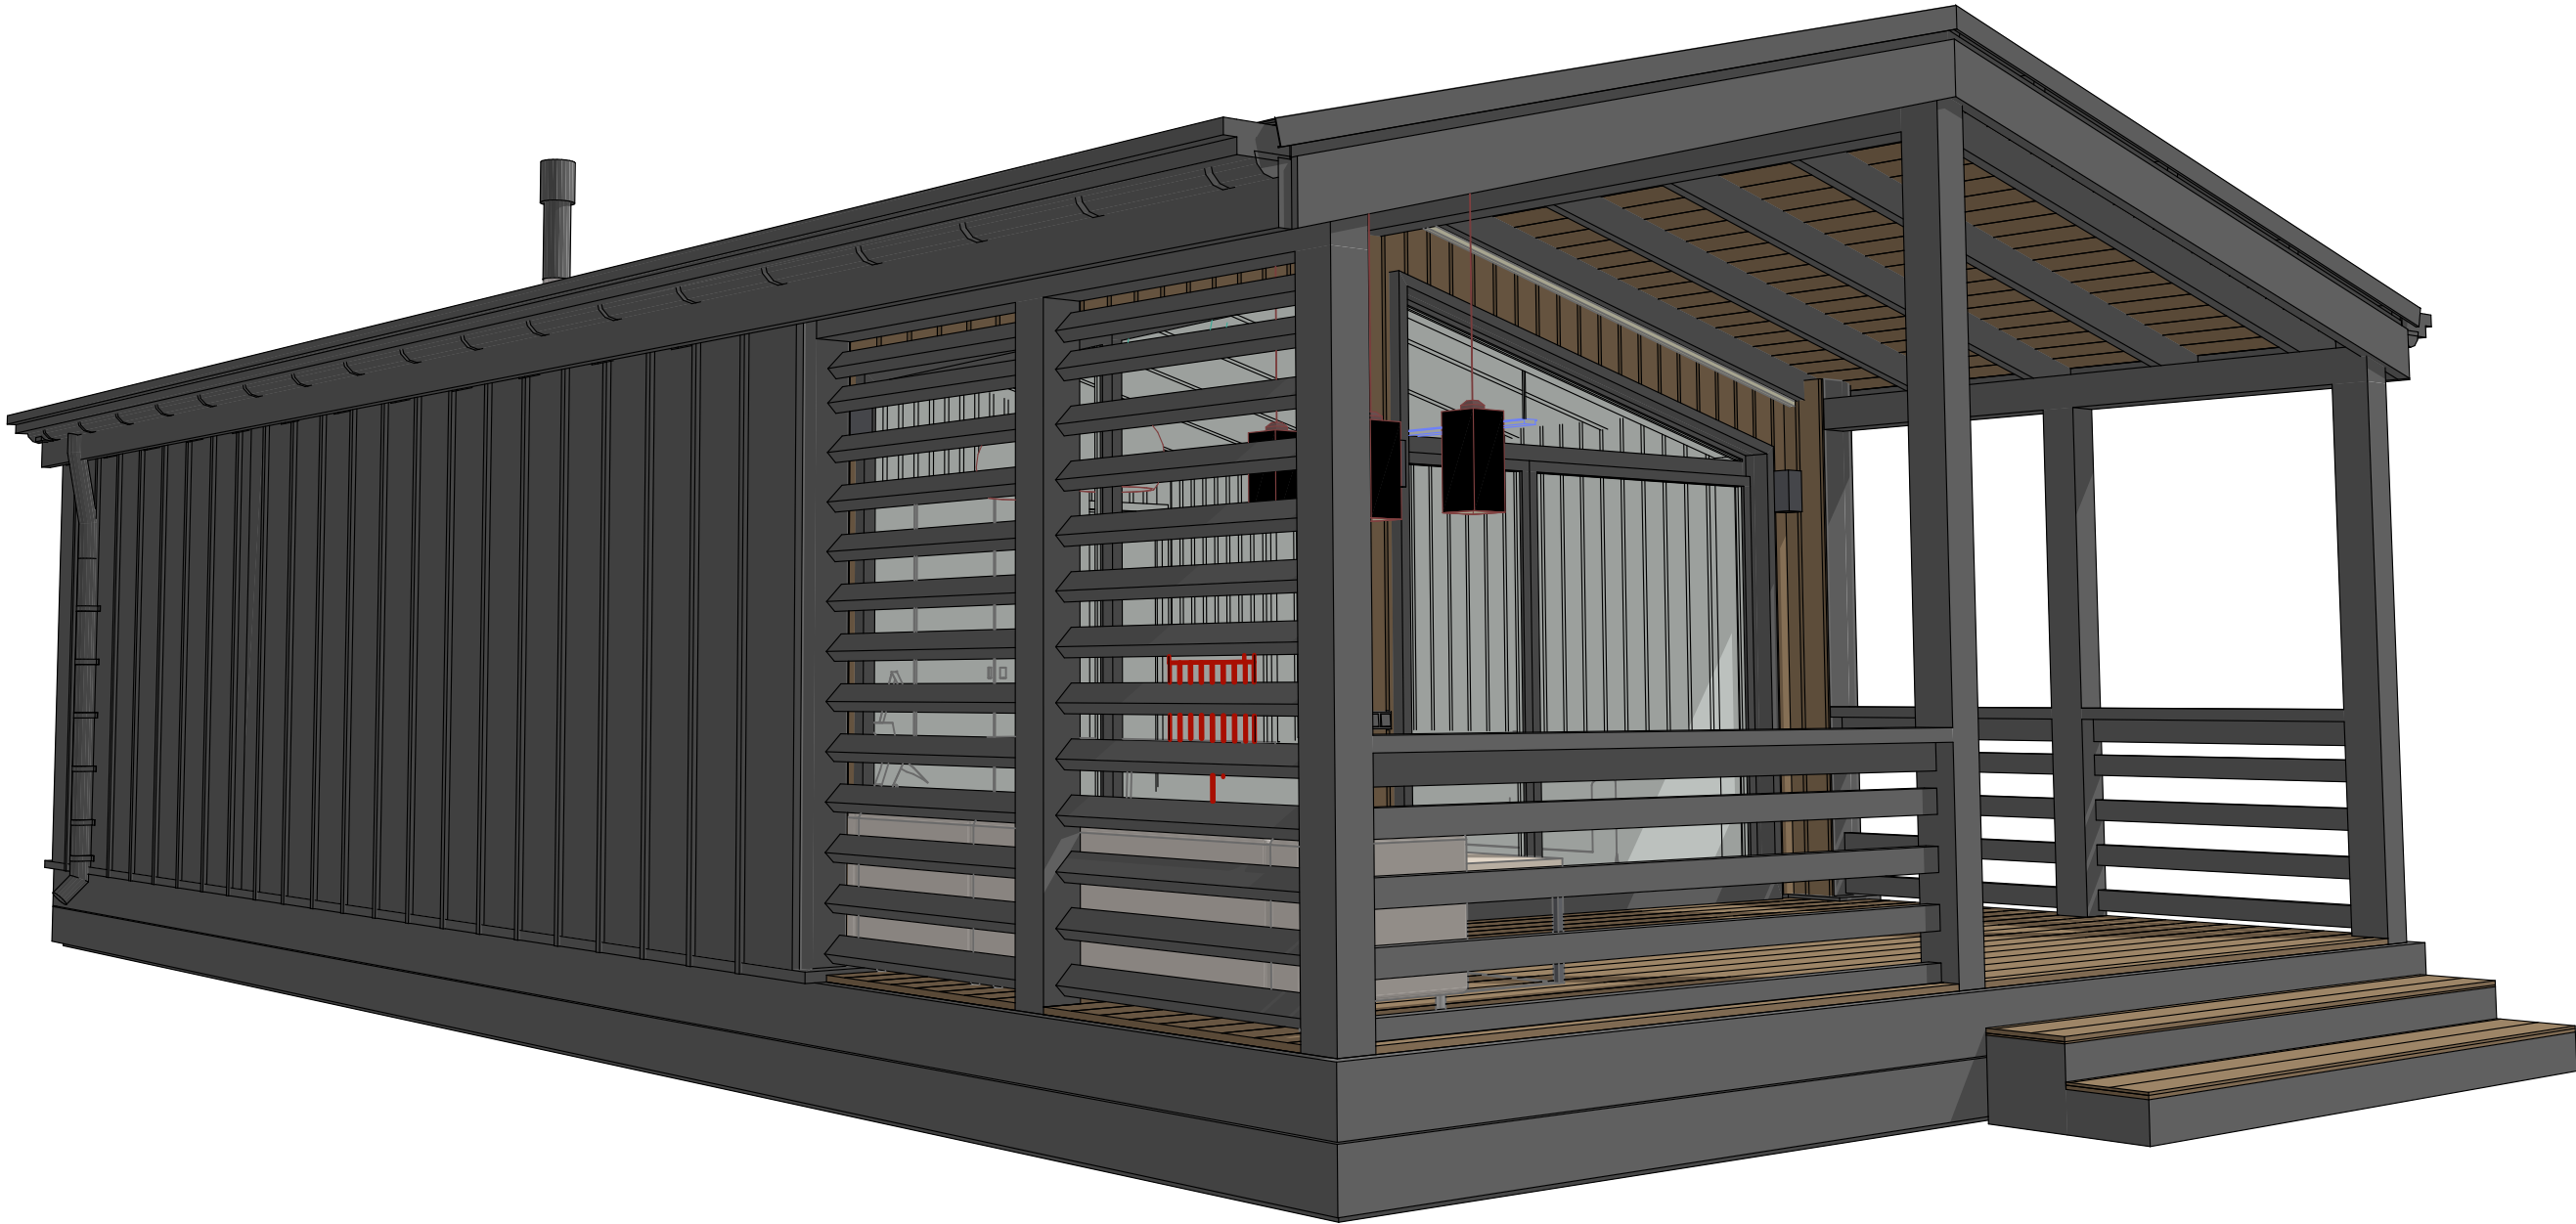


Согласовано				
Инва. № подл.	Подп. и дата	Взам. инв. №		

Лист	Изм.	№ Докум.	Подп.	Дата

Адрес:

Цветовое решение; Фасад в осях А-В

#Название Организации

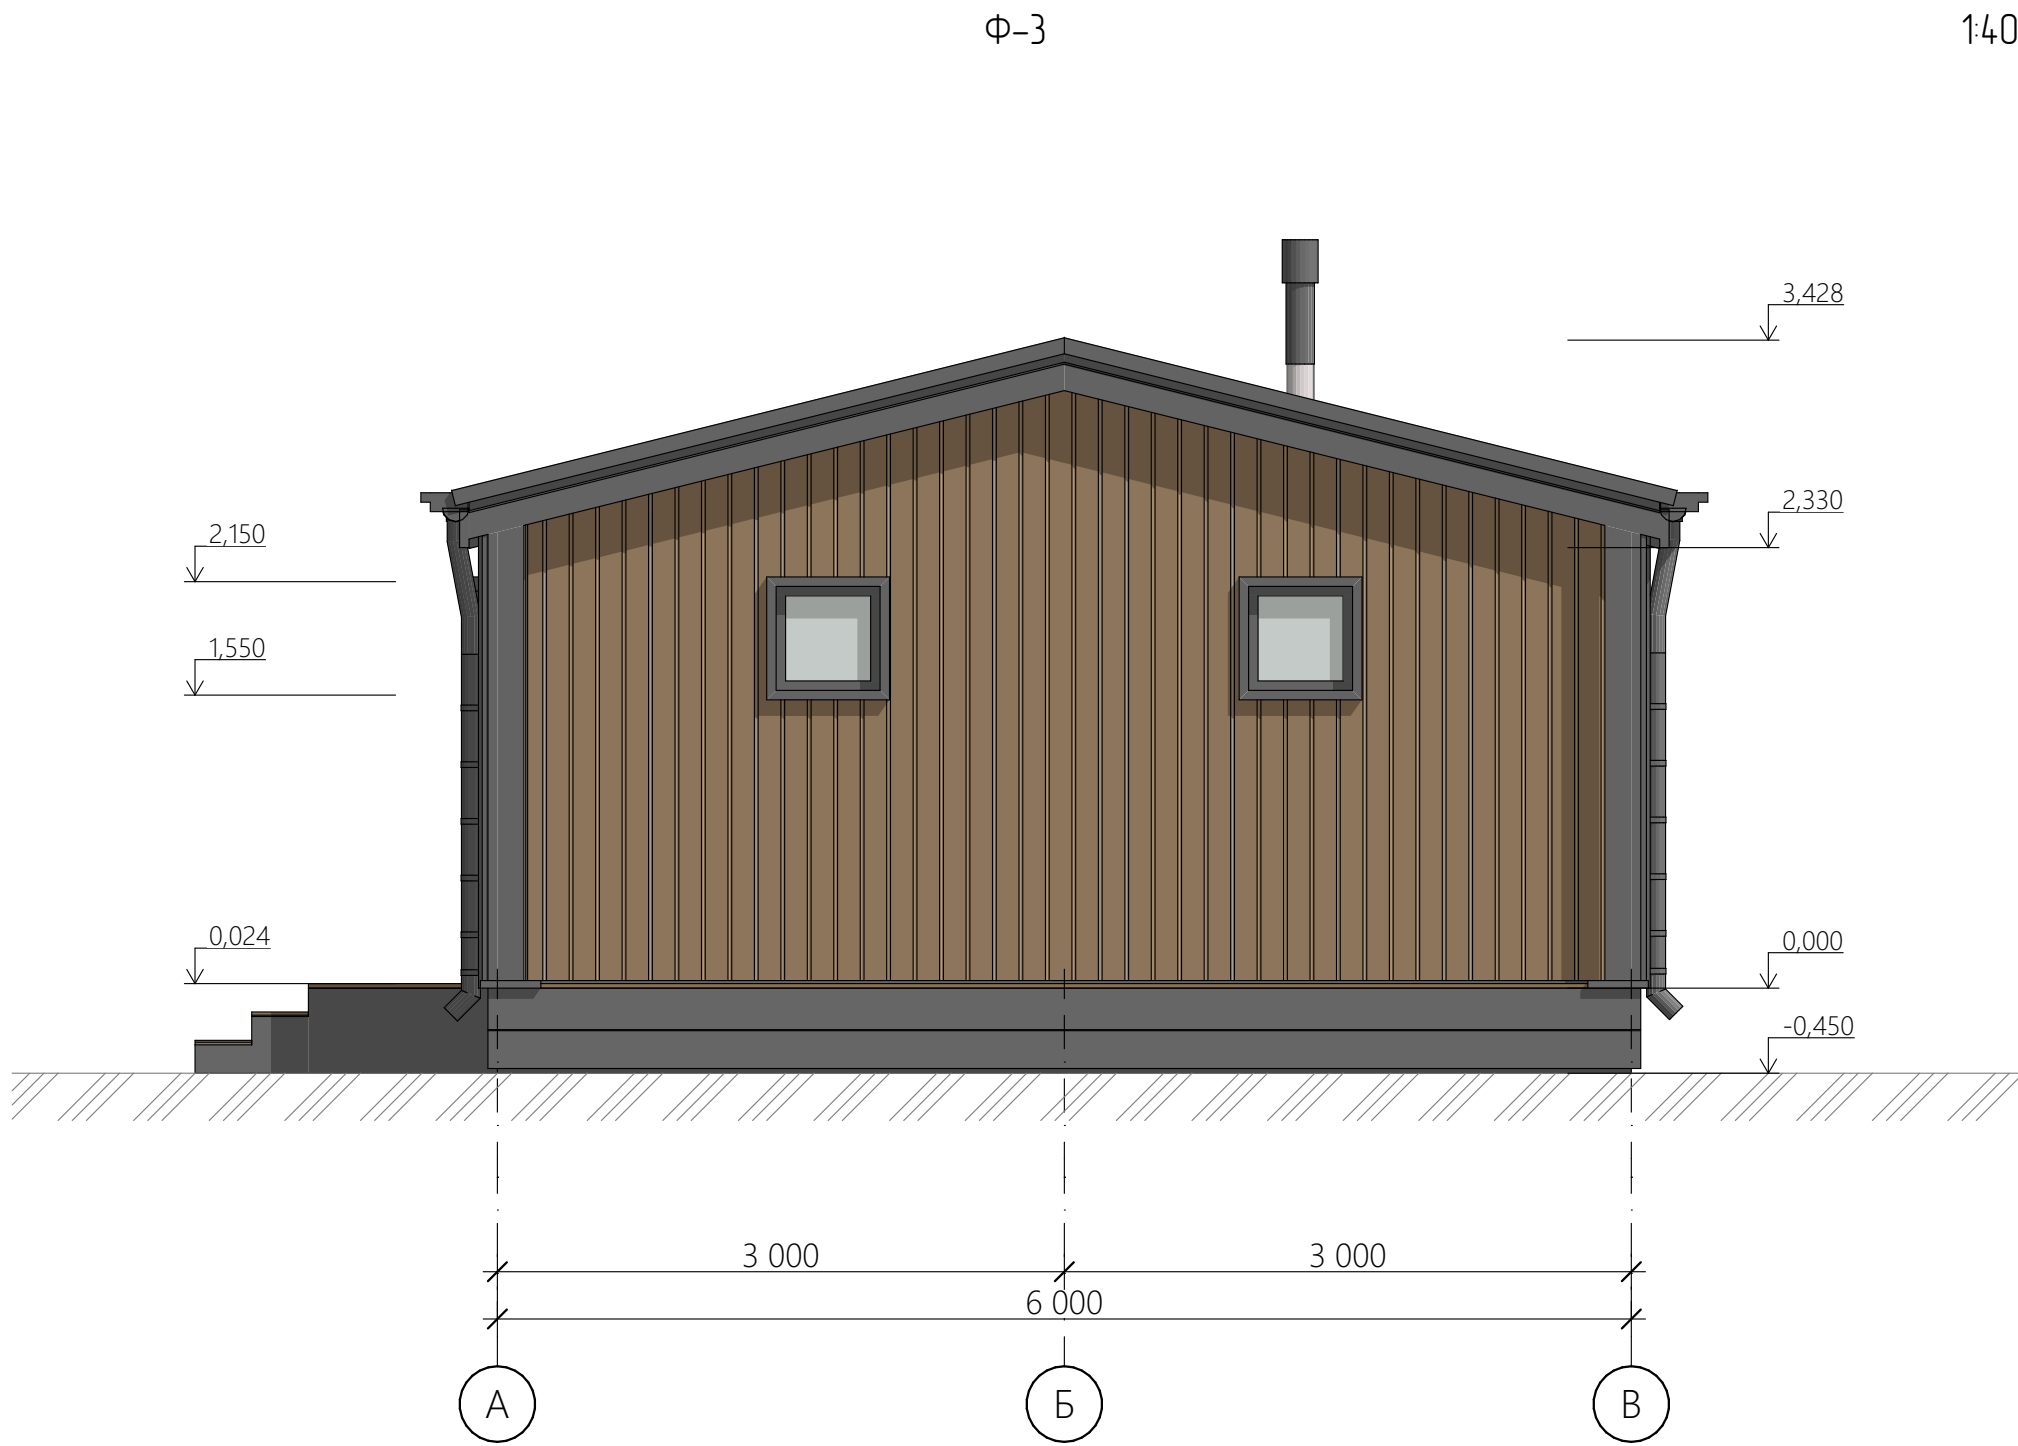

Условные обозначения:

-  -Планкен (Цвет орех)
-  -Террасная доска ДПК
-  -Водосточная система, наличники, оконные рамы, кровля(RAL 7004)
-  -Фальц

Согласовано				
И-нв. № подл.	Взам. инв. №		Подп. и дата	

Лист	Изм.	№ Докум.	Подп.	Дата

Адрес:

Цветовое решение; Фасад в осях 1-3

#Название Организации



-Планкен (Цвет орех)

-Террасная доска ДПК

-Водосточная система, наличники, оконные рамы, кровля(RAL 7004)

-Фальц

Согласовано				
Инва. № подл.	Подп. и дата	Взам. инв. №		



Лист	Изм.	№ Докум.	Подп.	Дата

Адрес:

Аксометрия №2

#Название Организации

Согласовано

Взам. инв. №

Подп. и дата

Инв. № подл.



Лист	Изм.	№ Докум.	Подп.	Дата

Адрес:

Визуализация №1

#Название Организации

Согласовано			

Инв. № подл.	Подп. и дата	Взам. инв. №	



Лист	Изм.	№ Докум.	Подп.	Дата

Адрес:

Визуализация №2

#Название Организации

Согласовано

Взам. инв. №

Подп. и дата

Инв. № подл.



Лист	Изм.	№ Докум.	Подп.	Дата

Адрес:

Визуализация №3

#Название Организации

Согласовано					
Инва. № подл.	Подп. и дата		Взам. инв. №		



Лист	Изм.	№ Докум.	Подп.	Дата

Адрес:

Визуализация №4

#Название Организации

Согласовано

Взам. инв. №

Подп. и дата

Инв. № подл.



Лист	Изм.	№ Докум.	Подп.	Дата

Адрес:

Визуализация №5

#Название Организации

