

ARCHITECTURE/
CONSTRUCTION



Название:
Разработал:
Принял:
г. Москва



Согласовано				
И-нв. № подл.	Подп. и дата	Взам. инв. №		

1. Общие данные:

1.1. Архитектурный проект разработан на основании требований и пожеланий заказчика.

Тип строения	Баня
Относительная отм. ±0.000	ур. верха лаг деревянного перекрытия
Общая площадь застройки, м2	60,91
Габаритные размеры каркаса здания	11,5х8,5 м
Этажность	1 этаж
Конструктивная схема	Деревянный каркас

2. Конструктивные решения:

2.1. Рабочие чертежи разработаны на основании задания на проектирование

Полезная нагрузка на перекрытие	150 кгс/м2	-
Нормативная глубина промерзания	1,2м	СП 22.13330.2016 СП 131.13330.2020
Нормативное ветровое давление	I район (23кгс/м2)	СП 22.13330.2016
Нормативный вес снегового покрова	III район (150кгс/м2)	СП 22.13330.2016
Температура наиболее холодной пятидневки	-29°С	СП 131.13330.2020

2.2. Конструктивное строение представляет собой сооружение:

- на свайном фундаменте
- несущими стенами из деревянного каркаса
- вальмовой кровлей по деревянным стропилам

2.3. Необходимо осуществлять технический надзор за производством строительных работ. Данные по проведённым работам необходимо систематически вносить в журнал работ.

По каждому из этапов работ необходимо осуществлять входной контроль материалов и вести приёмку.

Фундамент	винтовые сваи (д 108мм)
Несущие конструкции	деревянный каркас (140х45мм)
Стропильная система	строганая доска (190х45мм)
Тип крыши	односкатная
Покрытие кровли	Фальц

2.4. Все деревянные конструкции обработать огне-биозащитными септиками в соответствии со СП 28.13330.2017 "Защита строительных конструкций от коррозии".

2.5. Кровельные работы выполнять в соответствии с требованиями фирмы производителя.

2.6. Все работы вести в строгом соответствии с требованиями СНиП 12.03.2001 "Безопасность труда в строительстве".

2.7. При выполнении всех работ строго соблюдать меры противопожарной безопасности.

2.8. Возможна замена материалов аналогами.

*Решения, принятые в проекте и отображенные в чертежах, соответствуют требованиям экологических, санитарно - гигиенических, противопожарных и других норм, действующих на территории Российской Федерации, и обеспечивают безопасную для жизни и здоровья людей эксплуатацию объекта при соблюдении предусмотренных рабочих чертежей и мероприятий.

Лист	Изм.	№ Докум.	Подп.	Дата

Адрес:

Пояснительная записка

#Название Организации

Согласовано				
И-нв. № подл.	Подп. и дата	Взам. инв. №		

Лист	Наименование	Примечание
1	Пояснительная записка	
2	Ведомость чертежей	
3	Схема планировочной организации земельного участка	
4	Маркировочный план	
5	Размерный план	
6	План расстановки мебели и оборудования	
7	Зд-разрез	
8	План электрического теплого пола	
9	План покрытий пола	
10	Экспликация покрытий пола	
11	План покрытия отделки стен	
12	Экспликация отделки стен	
13	План размещения розеток стен	
14	План расстановки светильников и выключателей	
15	План кровли	
16	Разрез 1-1	
17	Разрез 2-2	
18	Ведомость оконных проёмов	
19	Ведомость дверных проёмов	
20	Цветовое решение; Фасад в осях В-А	
21	Цветовое решение; Фасад в осях 3-1	
22	Аксонометрия №1	
23	Цветовое решение; Фасад в осях А-В	
24	Цветовое решение; Фасад в осях 1-3	
25	Аксонометрия №2	
26	Визуализация №1	
27	Визуализация №2	
28	Визуализация №3	
29	Визуализация №4	
30	Визуализация №5	
31	Визуализация №6	

В основу архитектурно-планировочных решений положены требования технологических заданий и требования норм и правил строительного проектирования, действующих на территории РФ.

Основные параметры и требования разработаны на основании пожеланий и требований заказчика.

Архитектурные решения приняты в соответствии со следующими нормативными документами:

- Градостроительный кодекс российской федерации.
- Земельного Кодекса Российской Федерации.
- Федеральный закон от 22.07.2008 N 123 - ФЗ (ред. от 29.07.2017)"Технический регламент о требованиях пожарной безопасности.
- Федеральный закон № 384 - ФЗ «Технический регламент о безопасности зданий и сооружений».
- ГОСТ Р 21.1101-2013.«Основные требования к проектной и рабочей документации».
- Постановление правительства РФ от 16.02.2008 № 87 «Положение о составе разделов проектной документации и требованиях к их содержанию».
- СП 42.13330.2011 «Градостроительство. Планировка и застройка городских и сельских поселений».
- СП 131.13330.2018 «СНиП 23-01-99* Строительная климатология».
- СП 20.13330.2016 «СНиП 2.01.07-85* Нагрузки и воздействия».
- СП 22.13330.2016 «СНиП 2.02.01-83* Основания зданий и сооружений».
- СП 70.13330.2012 (с изменениями №1) «СНиП 3.03.01-87 Несущие и ограждающие конструкции».
- СП 64.13330.2017 «СНиП II-25-80 Деревянные конструкции».
- СП 17.13330.2017 «СНиП II-26-76 Кровли».
- СП 29.13330.2011 «СНиП 2.03.13-88 Полы».
- СП 28.13330.2017 «СНиП 2.03.11-85 Защита строительных конструкций от коррозии».
- СП 50.13330.2012 «СНиП 23-02-2003 Тепловая защита зданий».

Лист	Изм.	№ Докум.	Подп.	Дата

Адрес:



Ведомость чертежей

#Название Организации

- Граница участка
- Граница застройки участка
- 1 - Индивидуальный жилой дом
- 2 - Банный комплекс
- 3 - Беседка

Технико-экономические показатели

Наименование	Площадь, м²
Общая площадь застройки (ИЖС+баня+беседка)	142,36
Площадь участка (по топографической съемке)	620,85
Площадь застройки (баня)	60,36

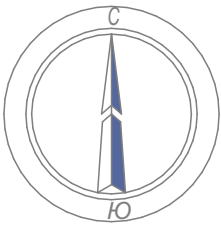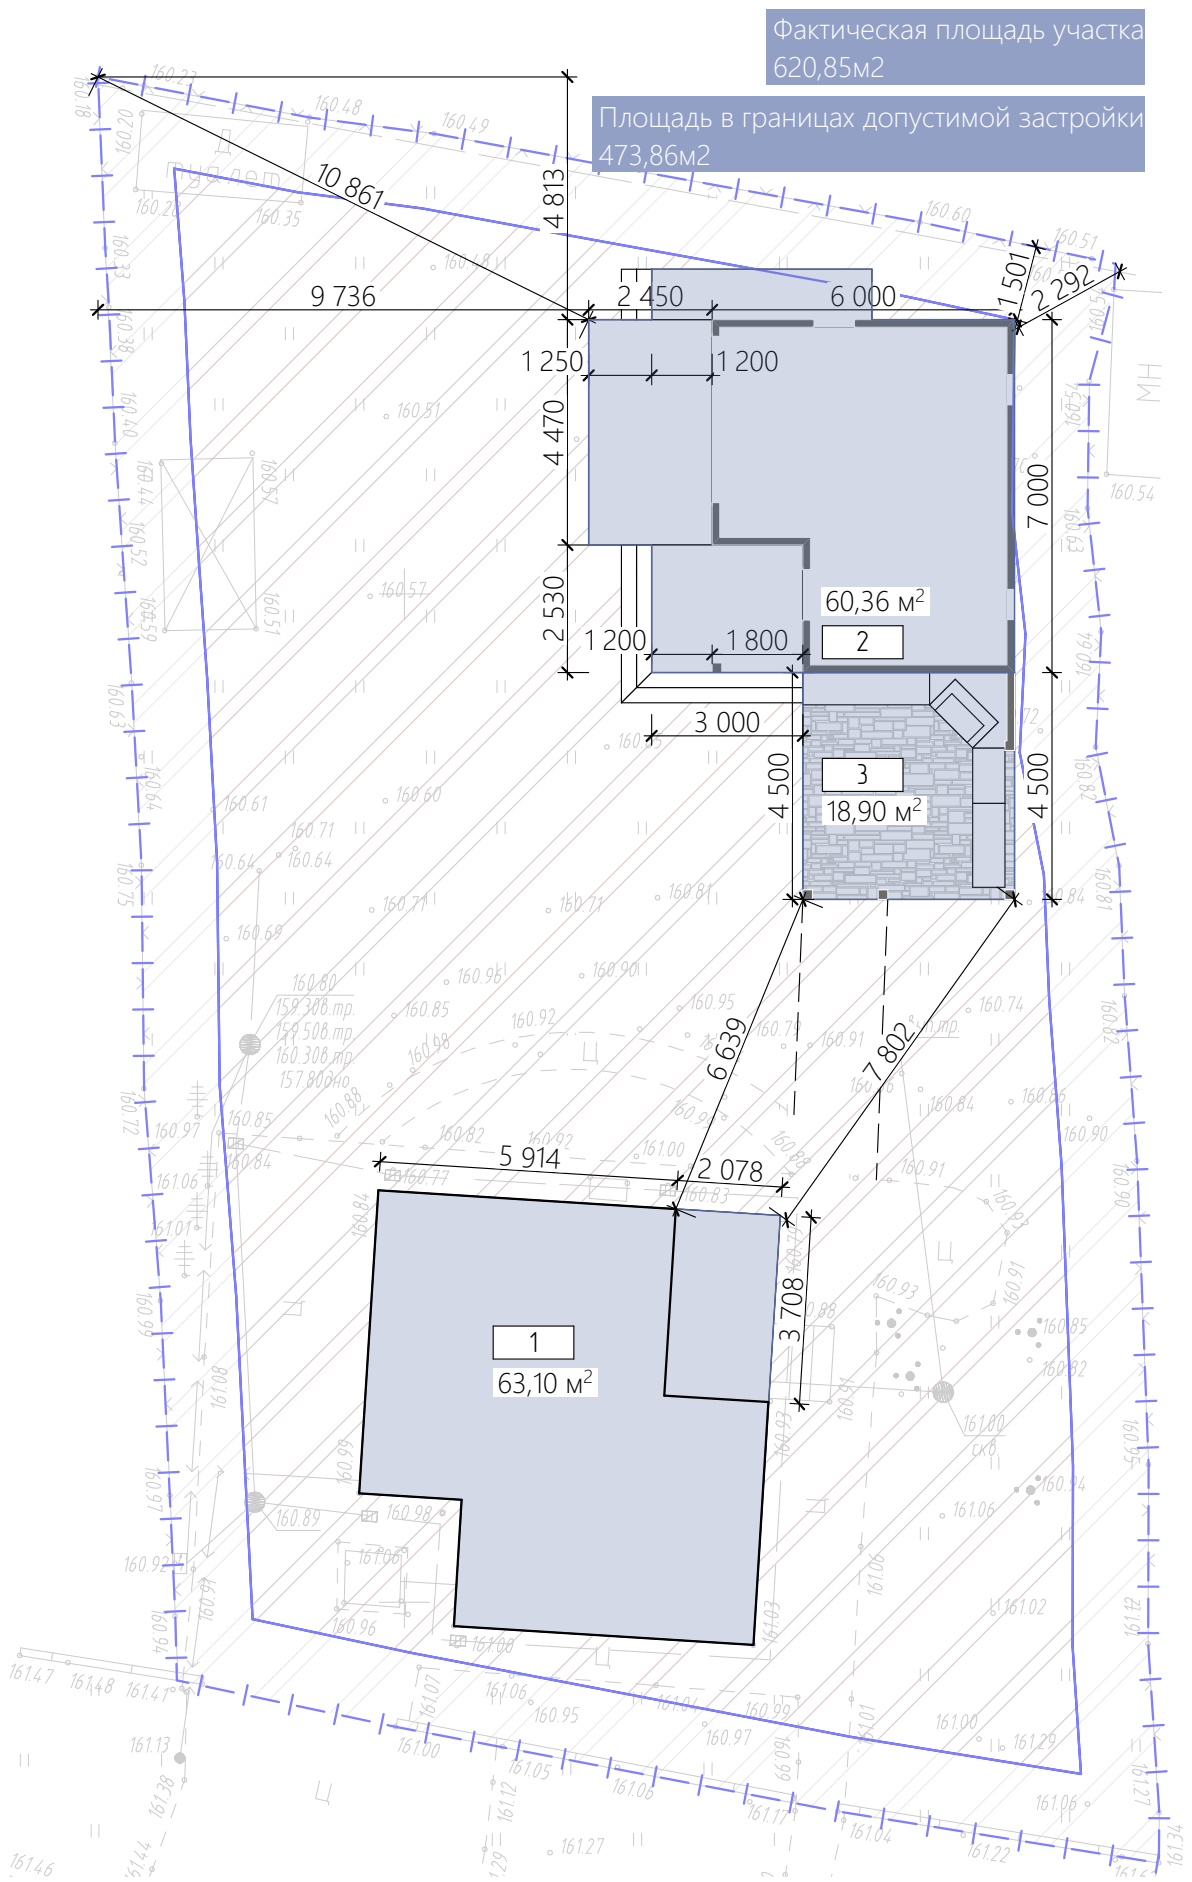


Согласовано				
И.нв. № подл.	Подп. и дата	Взам. инв. №		

Лист	Изм.	№ Докум.	Подп.	Дата

Адрес:

Схема планировочной организации земельного участка

#Название Организации

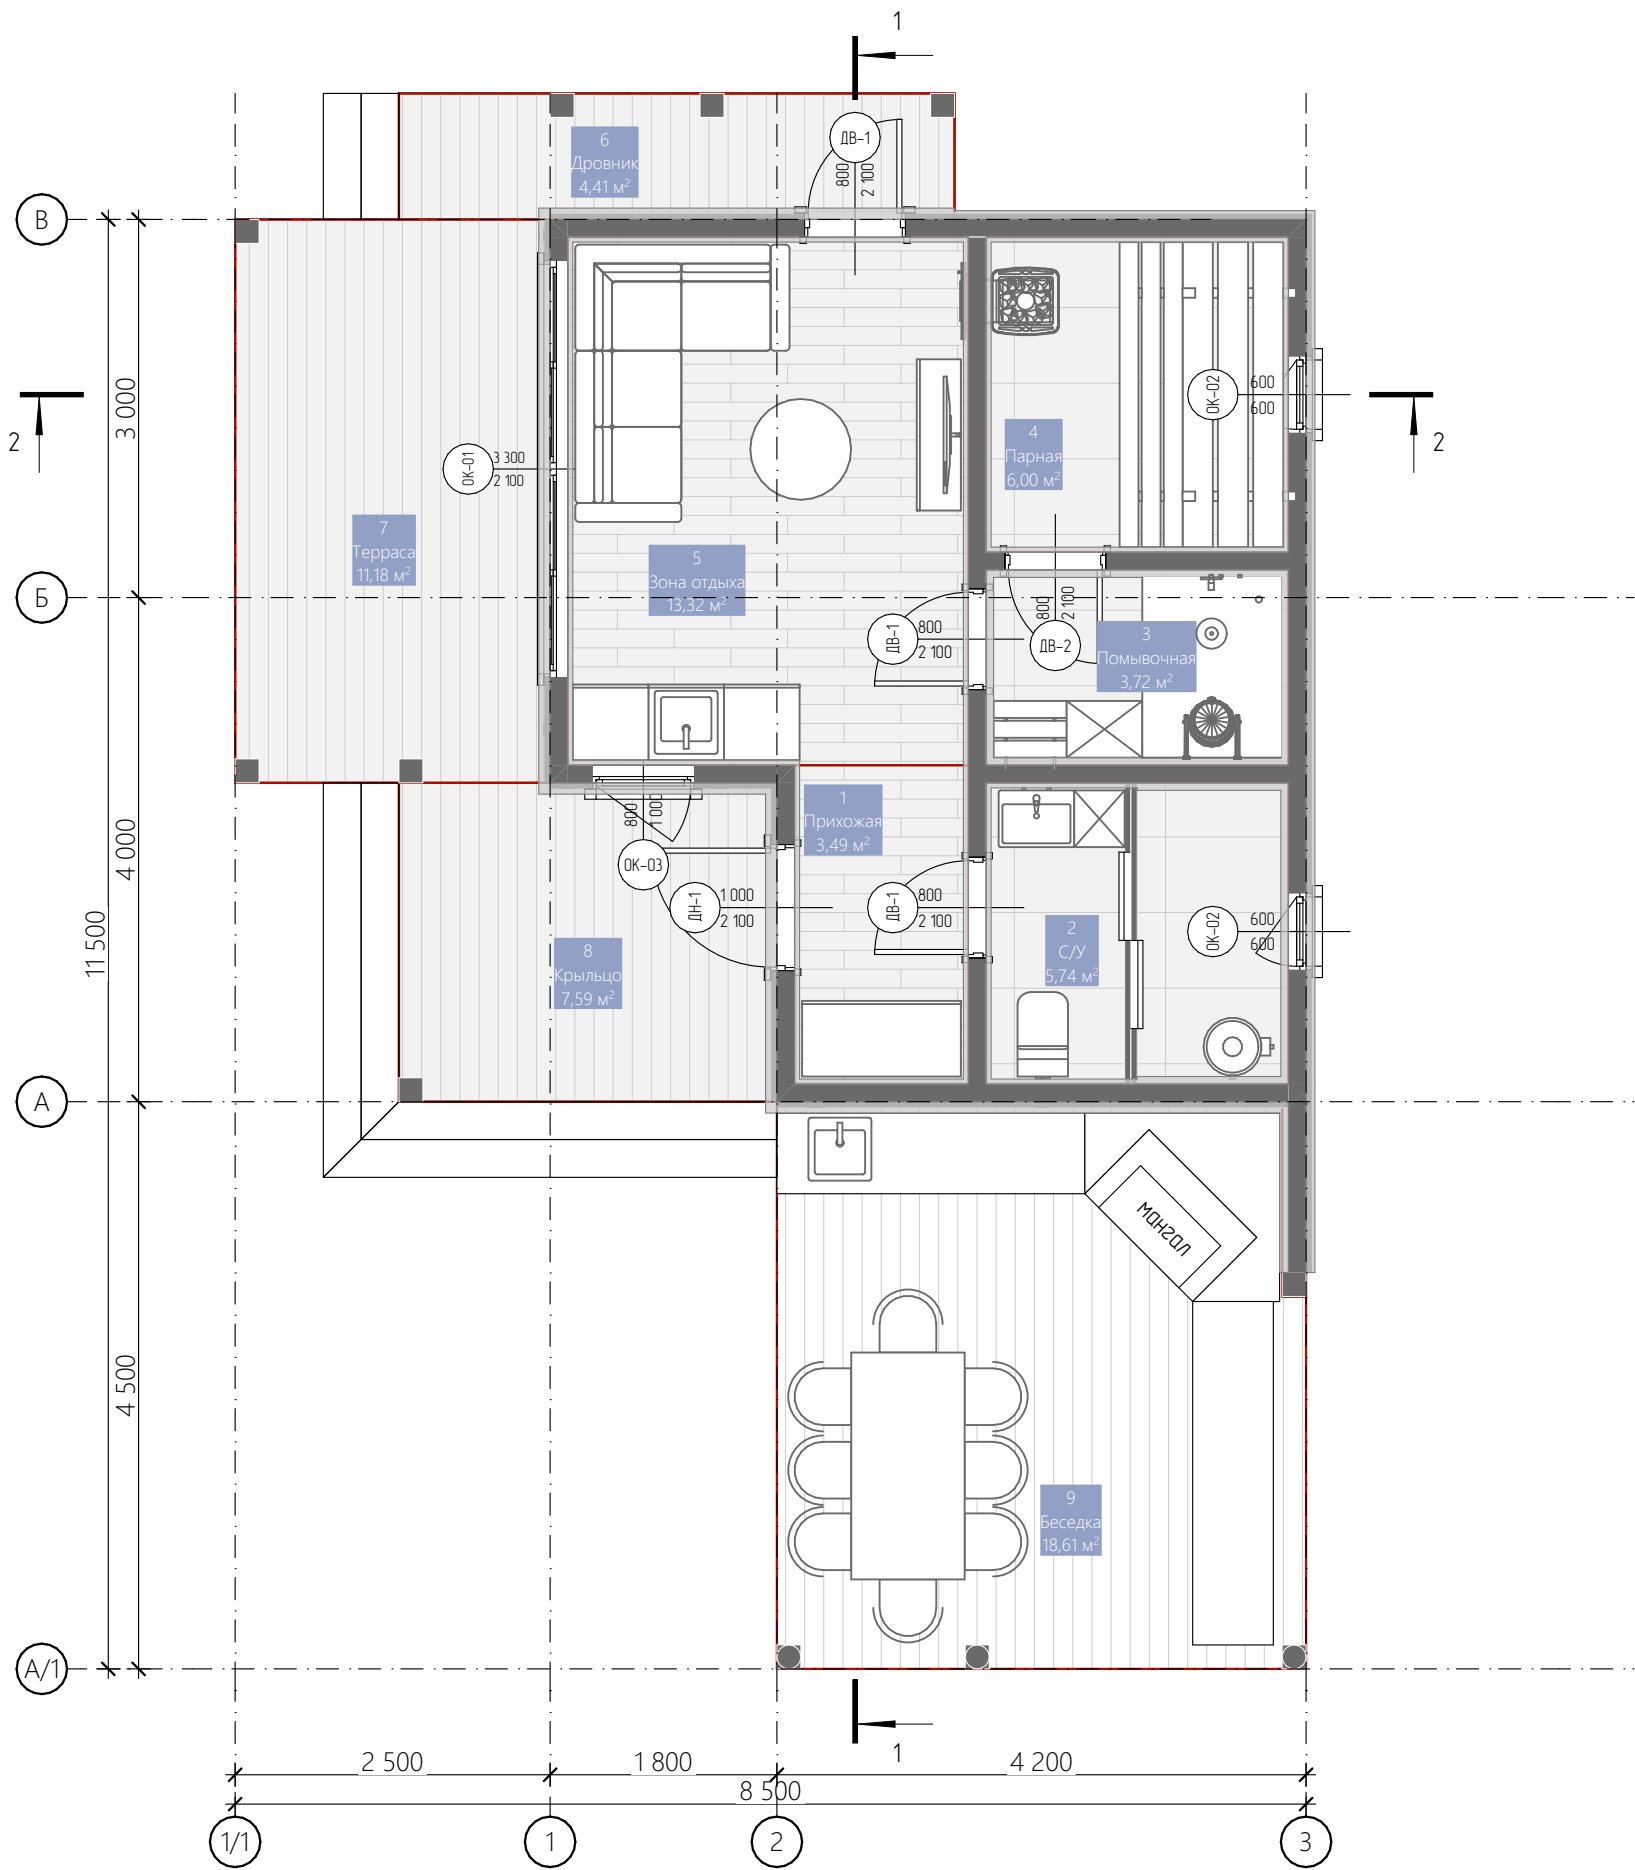

Экспликация помещений

№	Наименование	Площадь, кв. м.
1	Прихожая	3,49
2	С/У	5,74
3	Помывочная	3,72
4	Парная	6,00
5	Зона отдыха	13,32
6	Дровник	4,41
7	Терраса	11,18
8	Крыльцо	7,59
9	Беседка	18,61

74,06 м²

Наименование	Площадь, кв. м.
Площадь застройки	60,91

Примечание:

1. Вся индивидуальная мебель выполняется по отдельному проекту с детальной проработкой и калькуляцией. Чертежи предоставляет фирма-изготовитель столярных изделий.
2. Данный проект отдельно согласовывается с автором проекта и непосредственно с заказчиком.
3. Цветовое решение фасада и материалов отделки показаны в проекте приблизительно.
4. Количество ступеней показано условно.

Согласовано

Взам. инв. №

Подп. и дата


Инв. № подл.

Лист	Изм.	№ Докум.	Подп.	Дата

Адрес:

Маркировочный план

#Название Организации

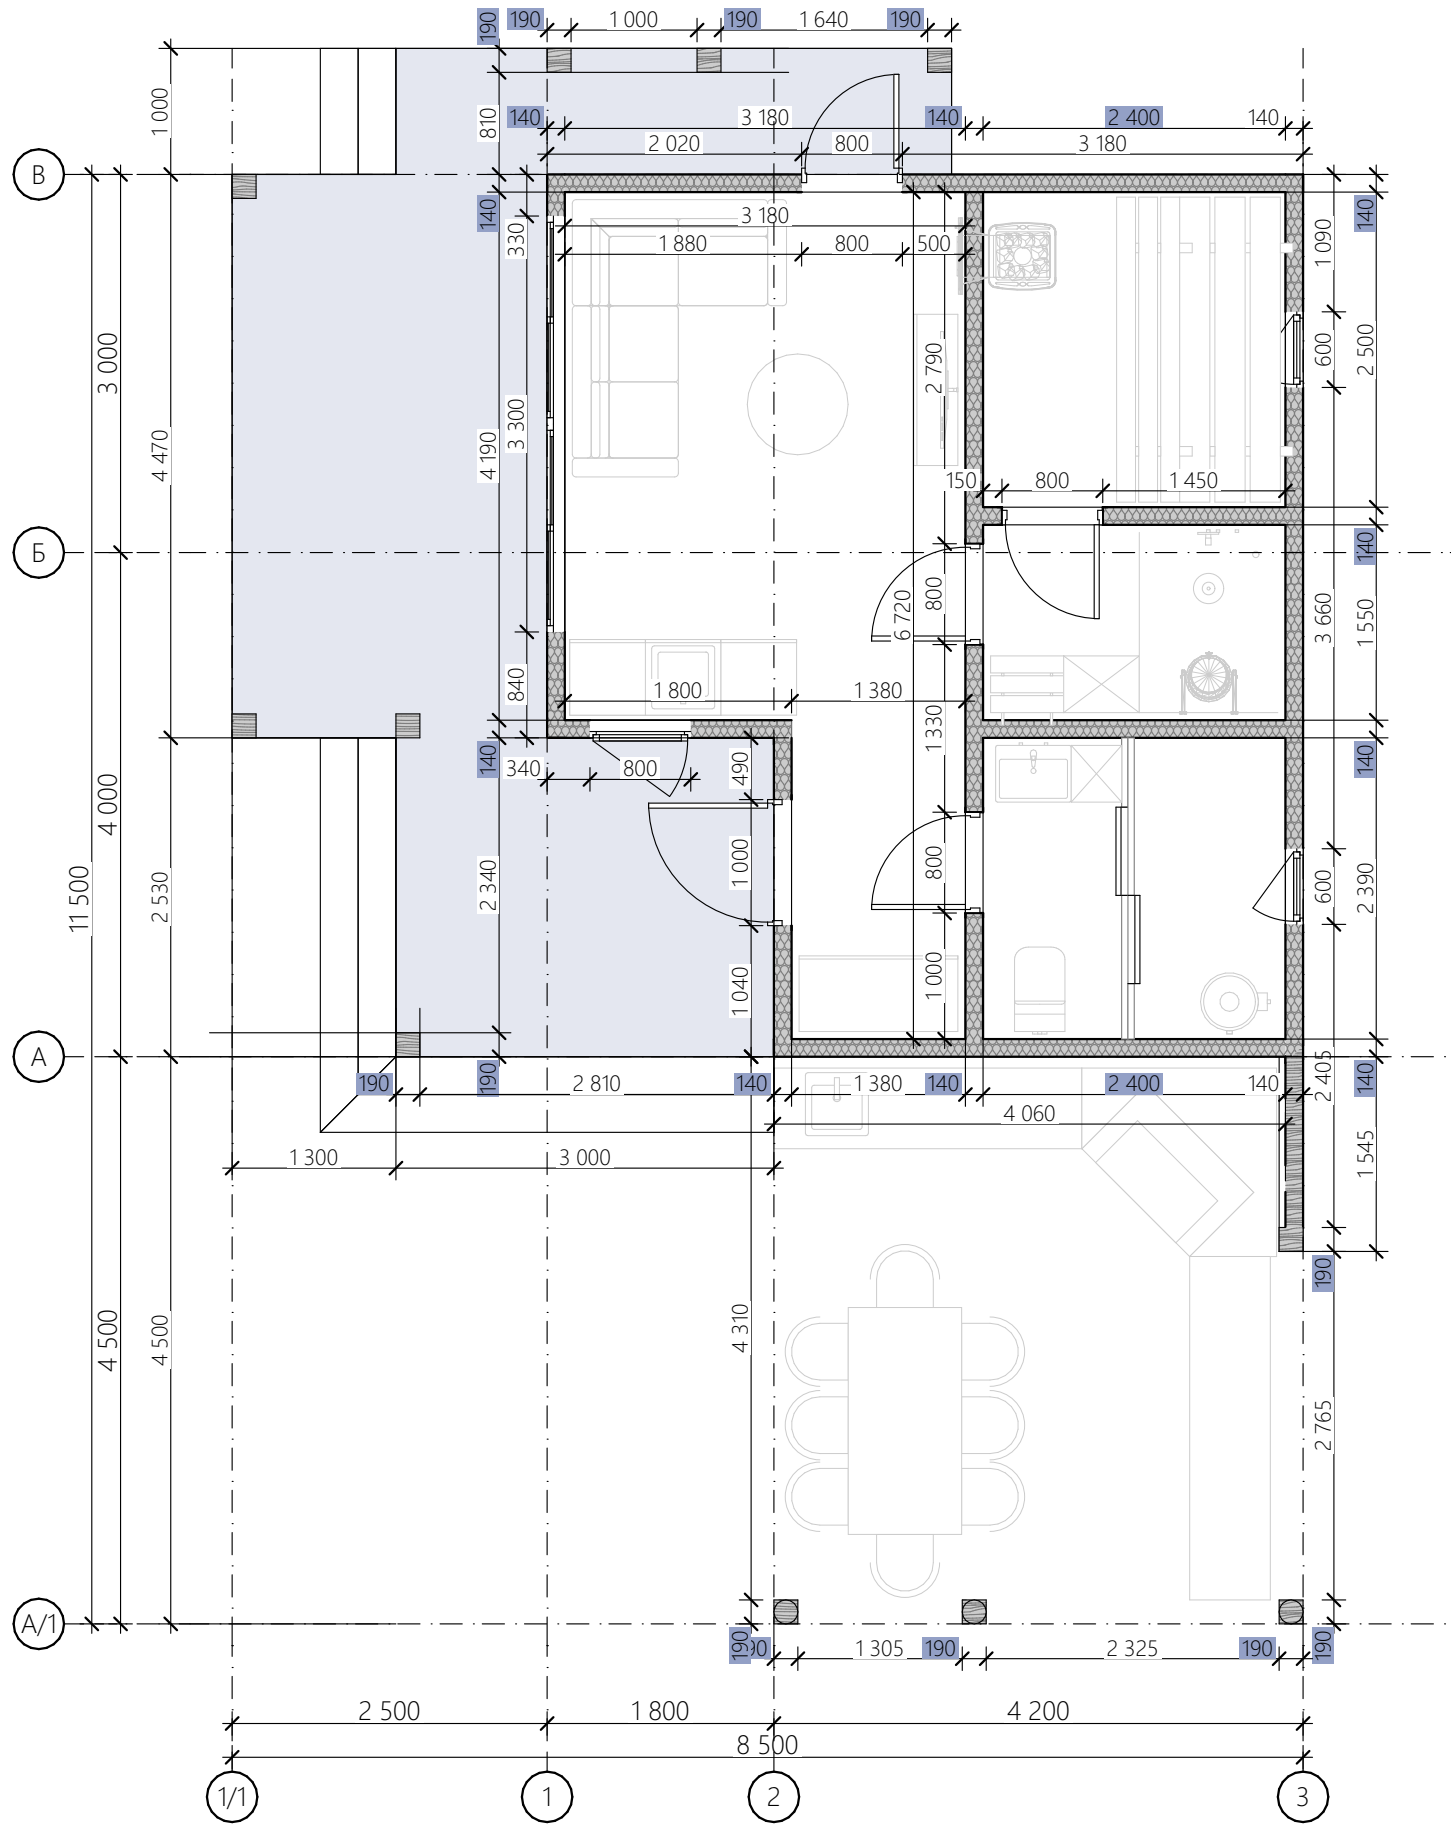

Примечание:


1. Представленные размеры
указаны без учета внешней и
внутренней отделки

Согласовано					
И-нв. № подл.	Подп. и дата	Взам. инв. №			

Лист	Изм.	№ Докум.	Подп.	Дата

Адрес:

Размерный план

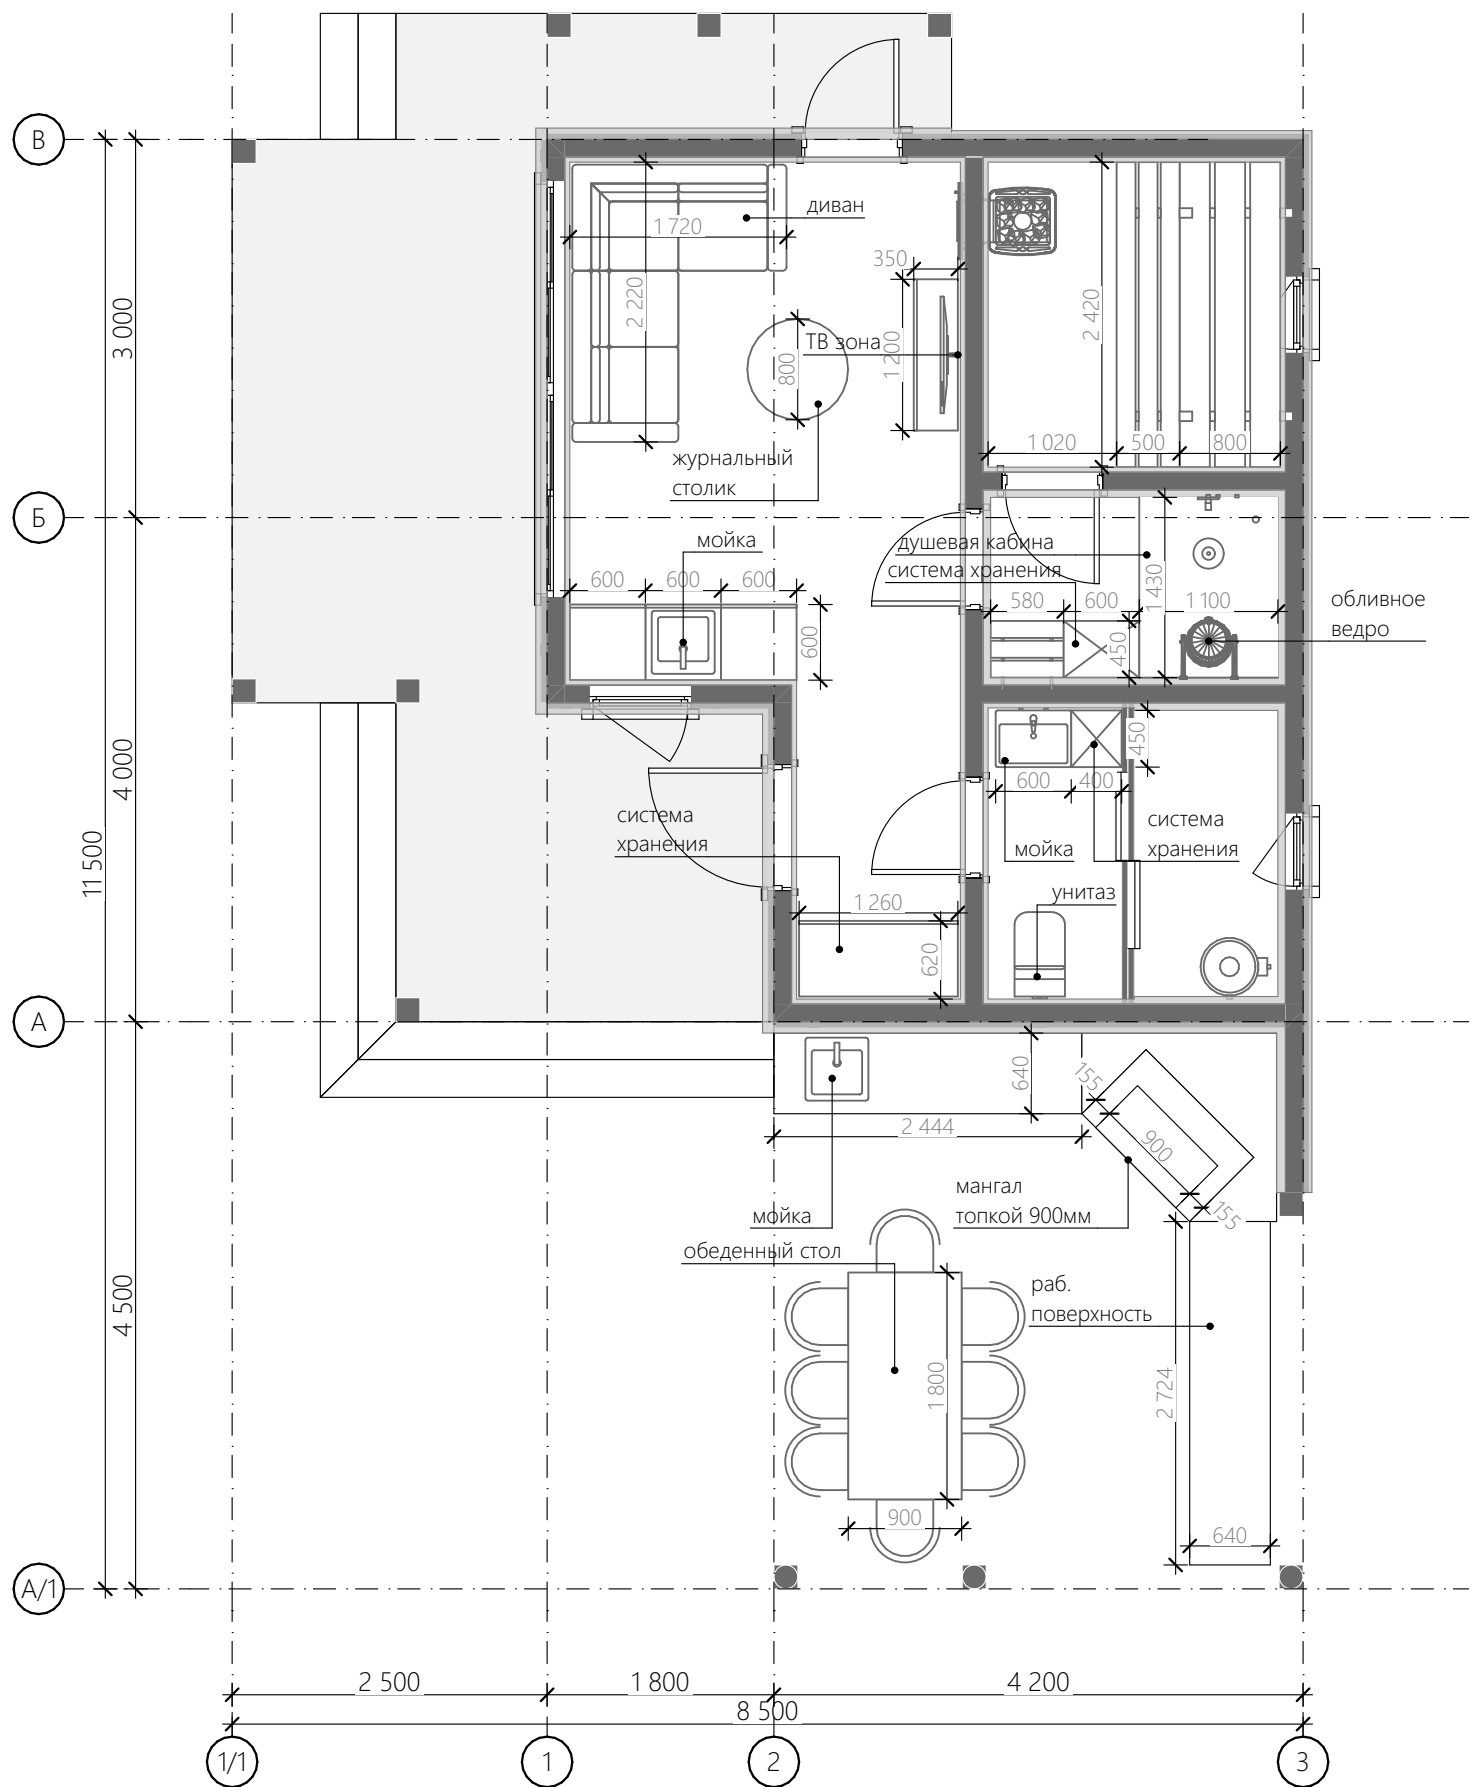

Примечание:

1. Вся индивидуальная мебель выполняется по отдельному проекту с детальной проработкой и калькуляцией. Чертежи предоставляет фирма-изготовитель столярных изделий.

2. Финальные размеры мебели и оборудования указаны ориентировочно — для точной компоновки требуется разработка дизайн-проекта.

Согласовано					
И/в. № подл.	Подп. и дата	Взам. инв. №			

Лист	Изм.	№ Докум.	Подп.	Дата

Адрес:

План расстановки мебели и оборудования

#Название Организации

6

Согласовано

Взам. инв. №

Подп. и дата


Инв. № подл.


Лист	Изм.	№ Докум.	Подп.	Дата

Адрес:


Зд-разрез

#Название Организации

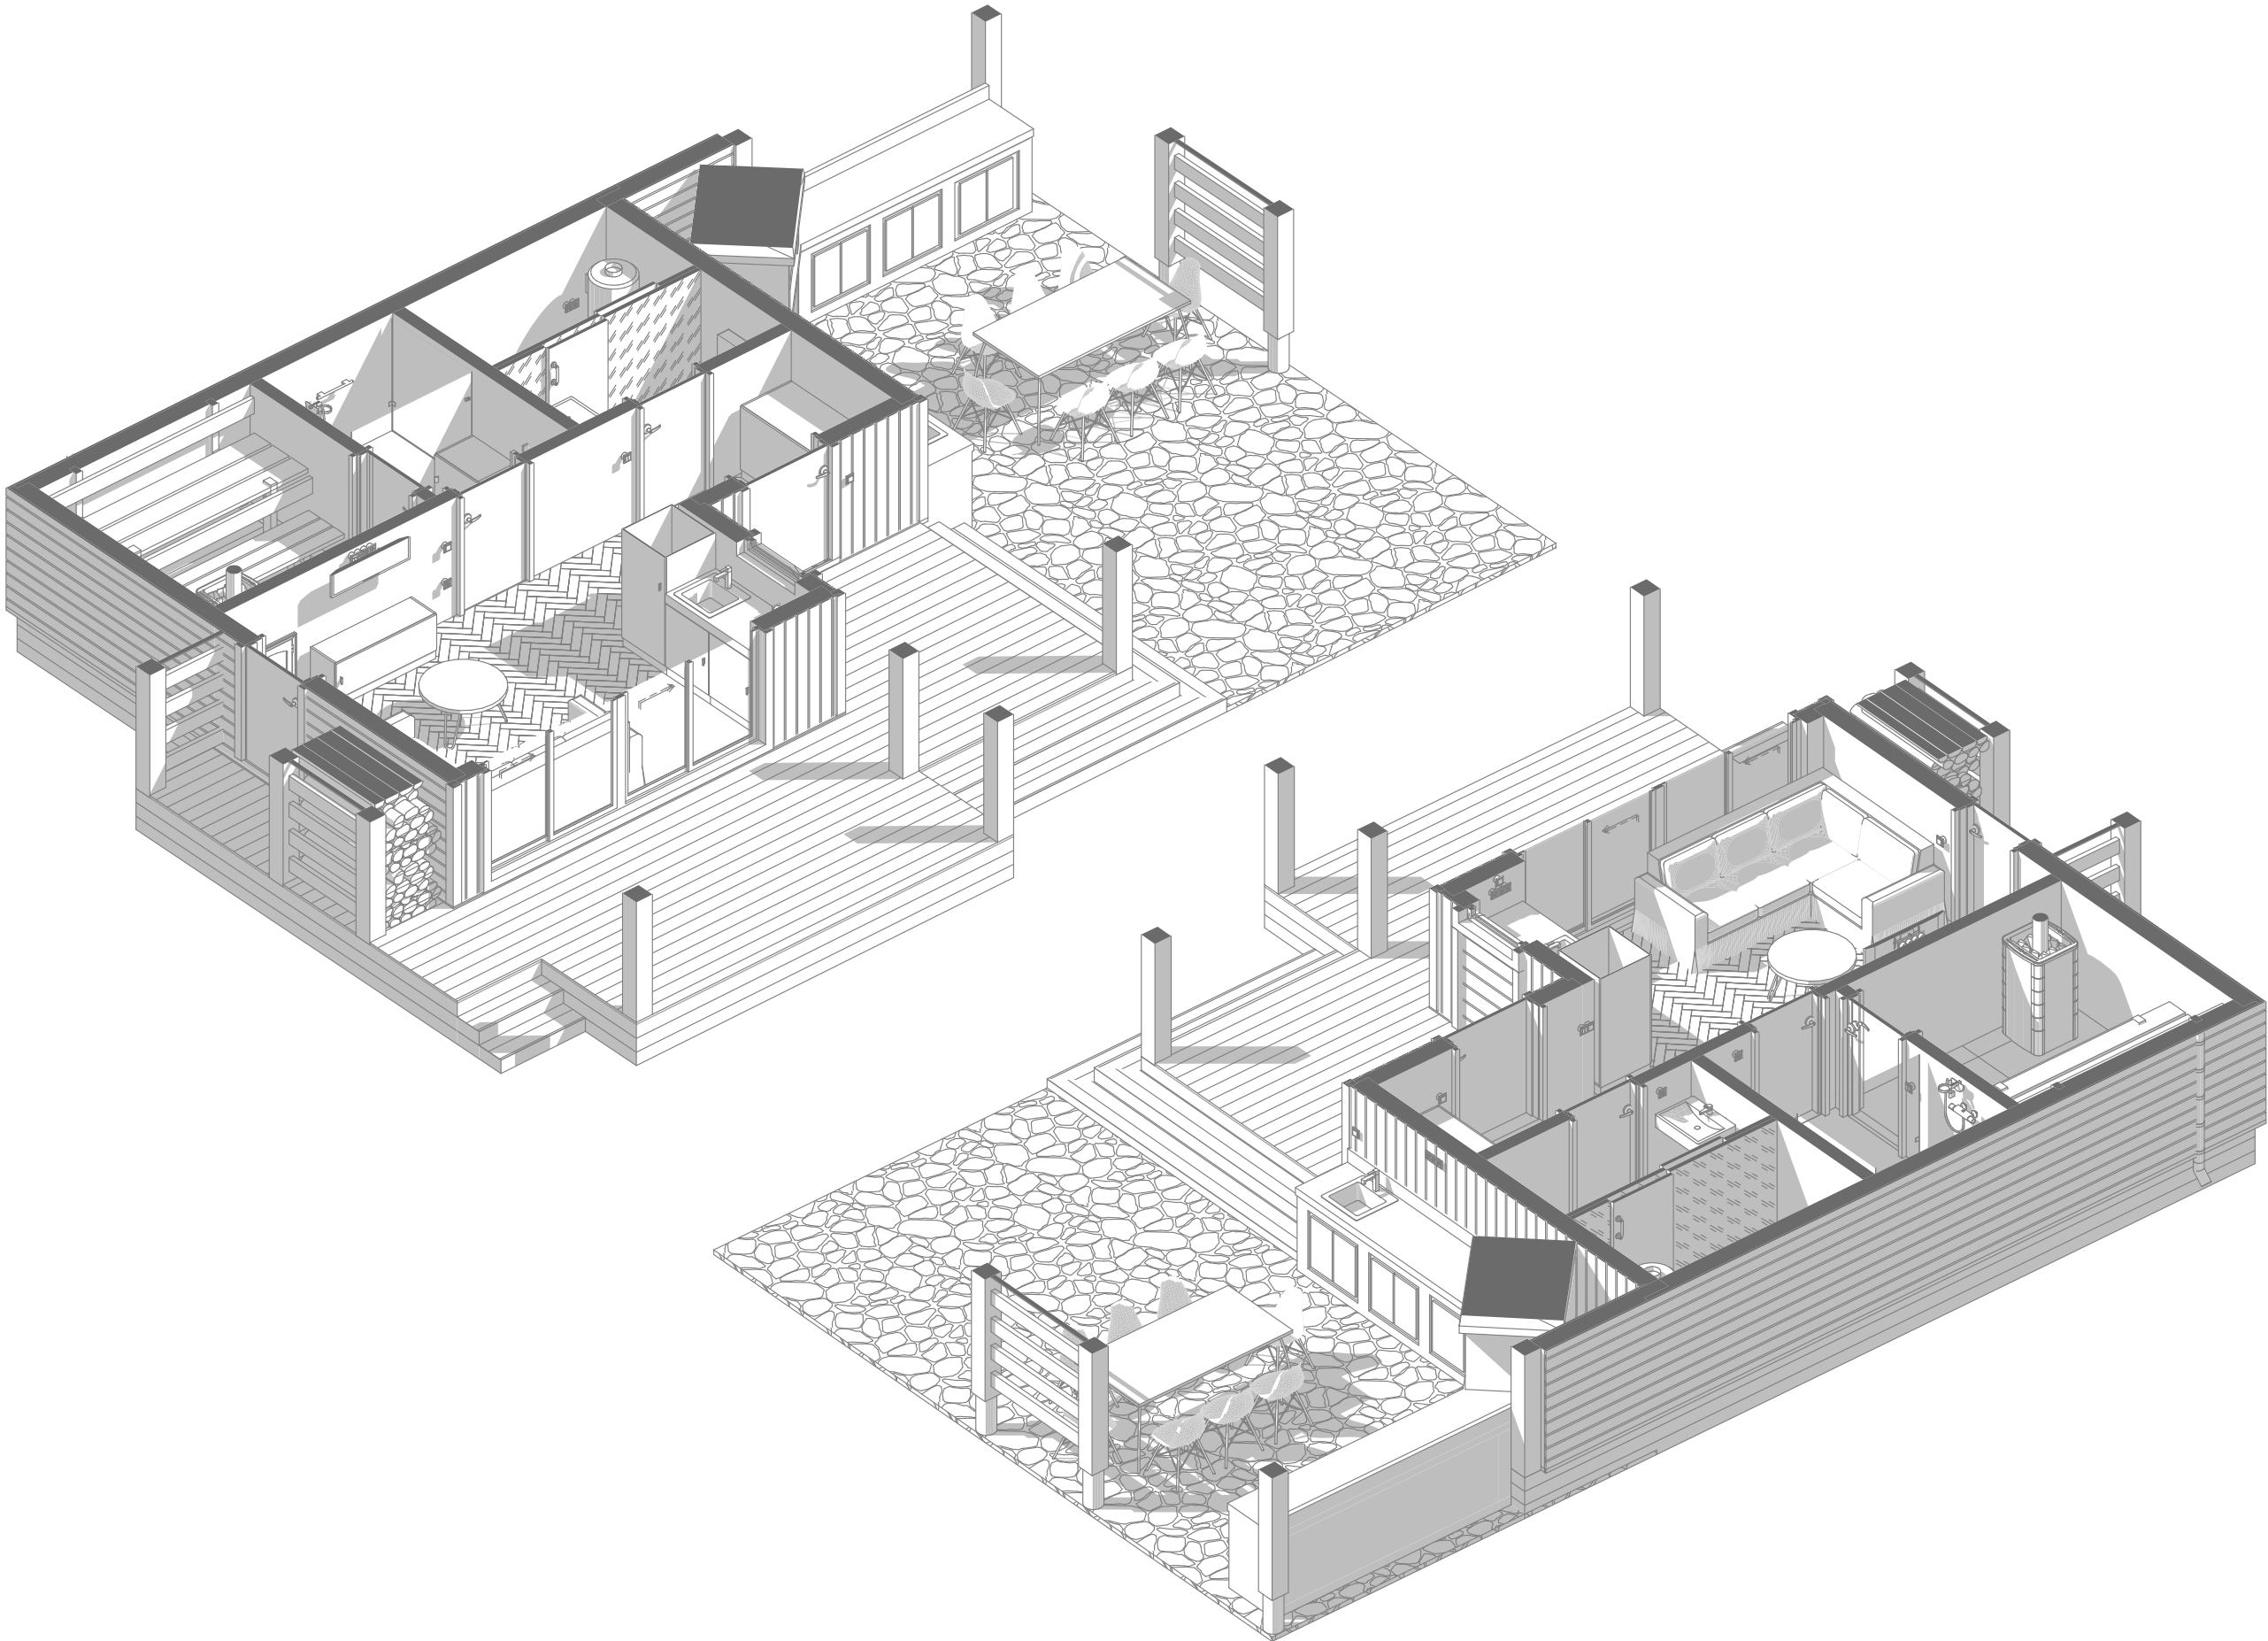

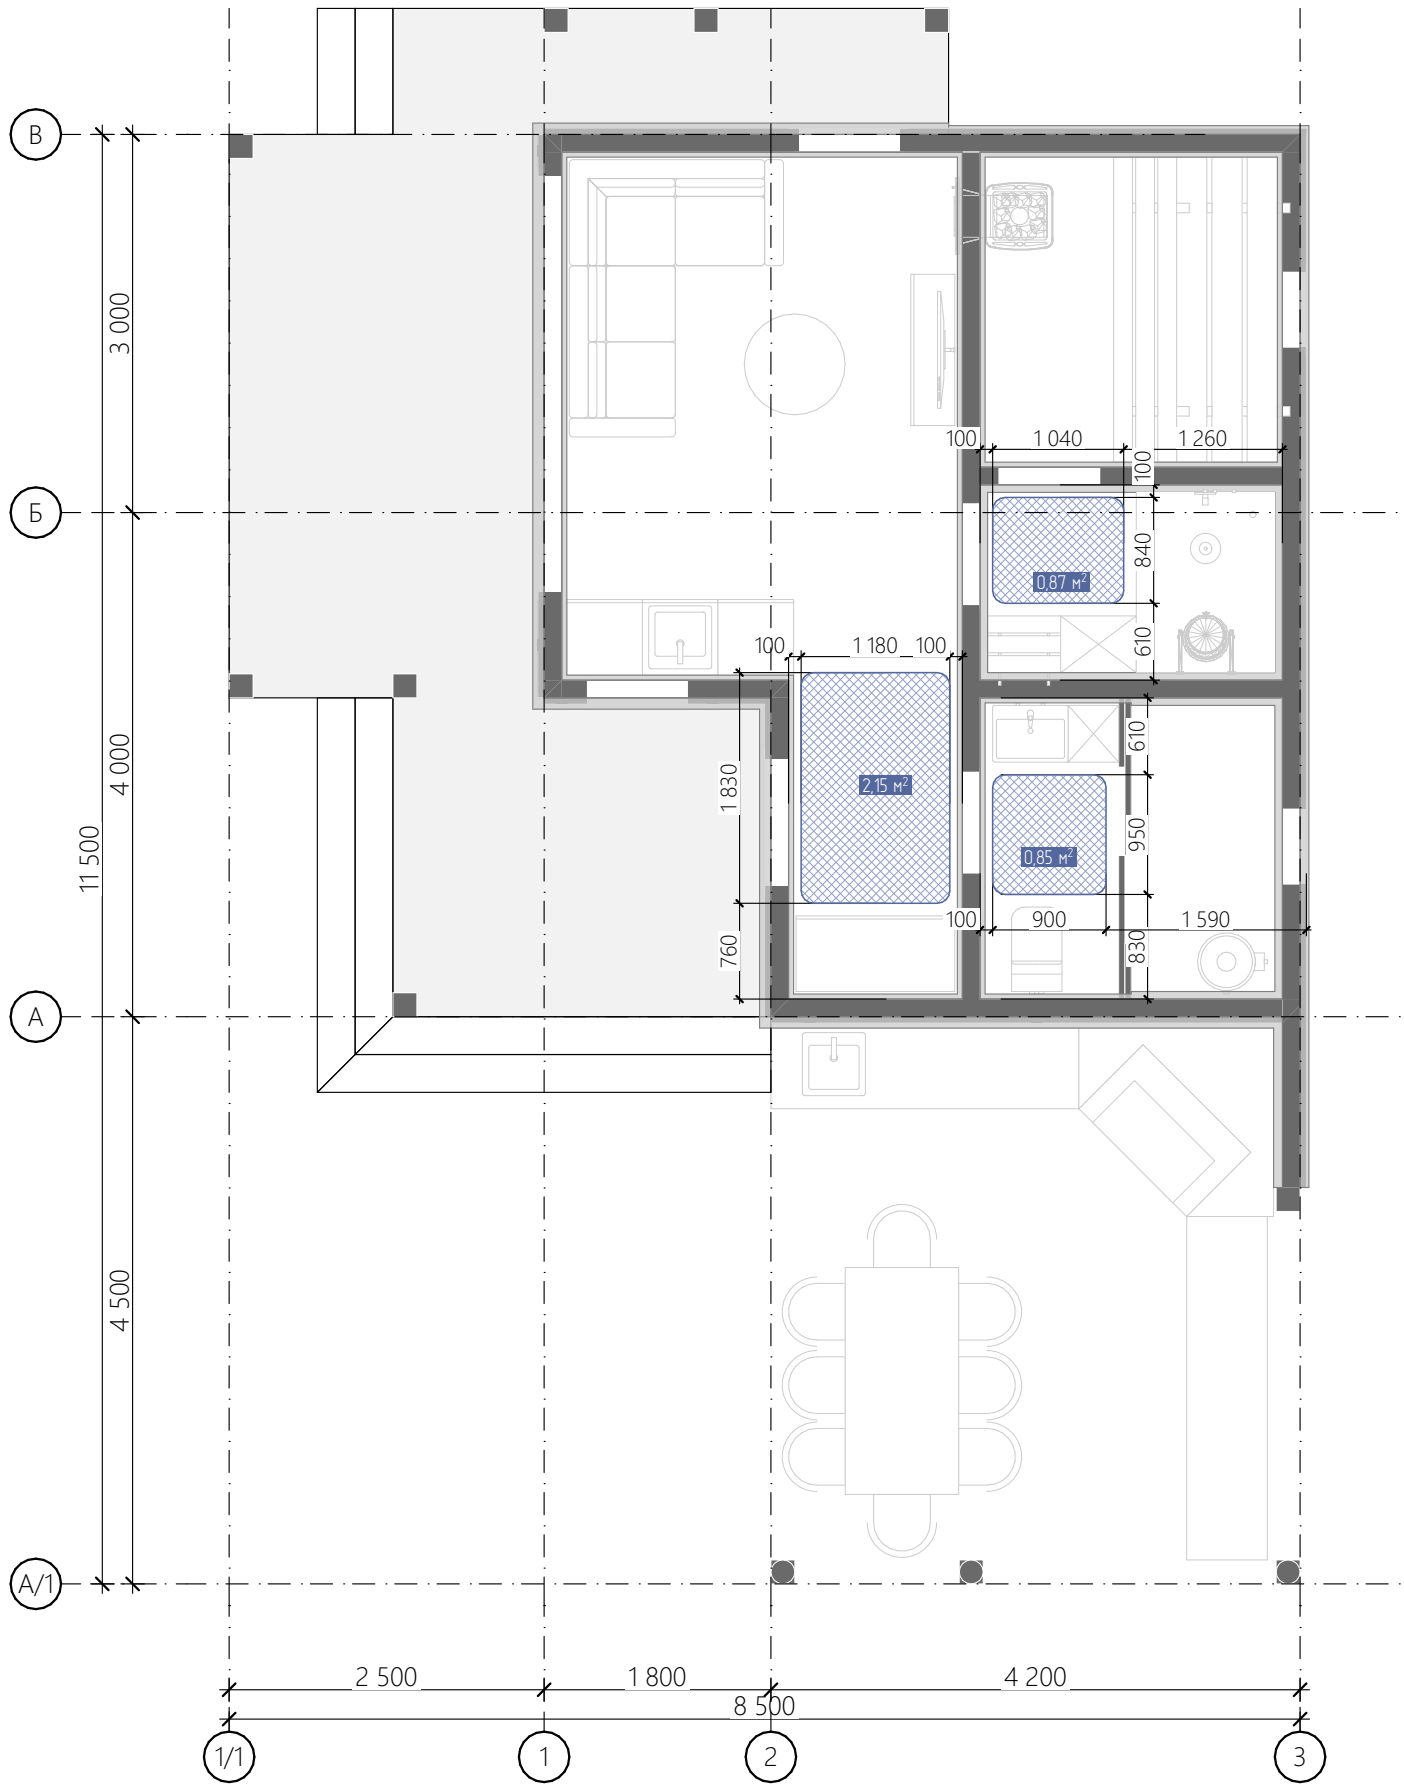

Условные обозначения

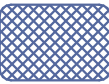 - Контур устройства
теплого пола

Экспликация теплого пола

Наименование зоны	Площадь, м2
Помывочная	0,87
Прихожая	2,15
С/у	0,85
3,87 м²	

Примечание:

1. Отображение носит схематичный характер. Фактическая реализация выполняется в соответствии с детальными проектными решениями инженерных сетей.

Согласовано				
И-нв. № подл.	Подп. и дата		Взам. инв. №	


Лист	Изм.	№ Докум.	Подп.	Дата

Адрес:

План электрического теплого
пола

#Название Организации

Условные обозначения

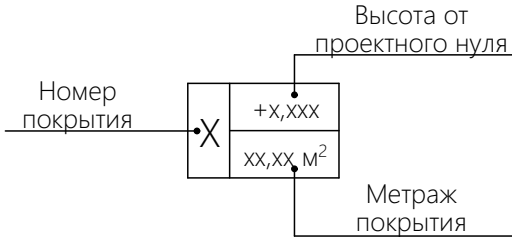


Ведомость покрытий пола

№	Наименование	м2
1	ДПК- террасная доска	23,07
2	ламинат	16,82
3	керамогранит	15,46

Примечание:

1. Приведённые цветовые решения носят рекомендательный характер. Фактический подбор оттенков и материалов выполняется на этапе реализации с учётом наличия продукции у поставщиков и утверждения заказчиком.

2. Пирог покрытия смотреть на след. листе.

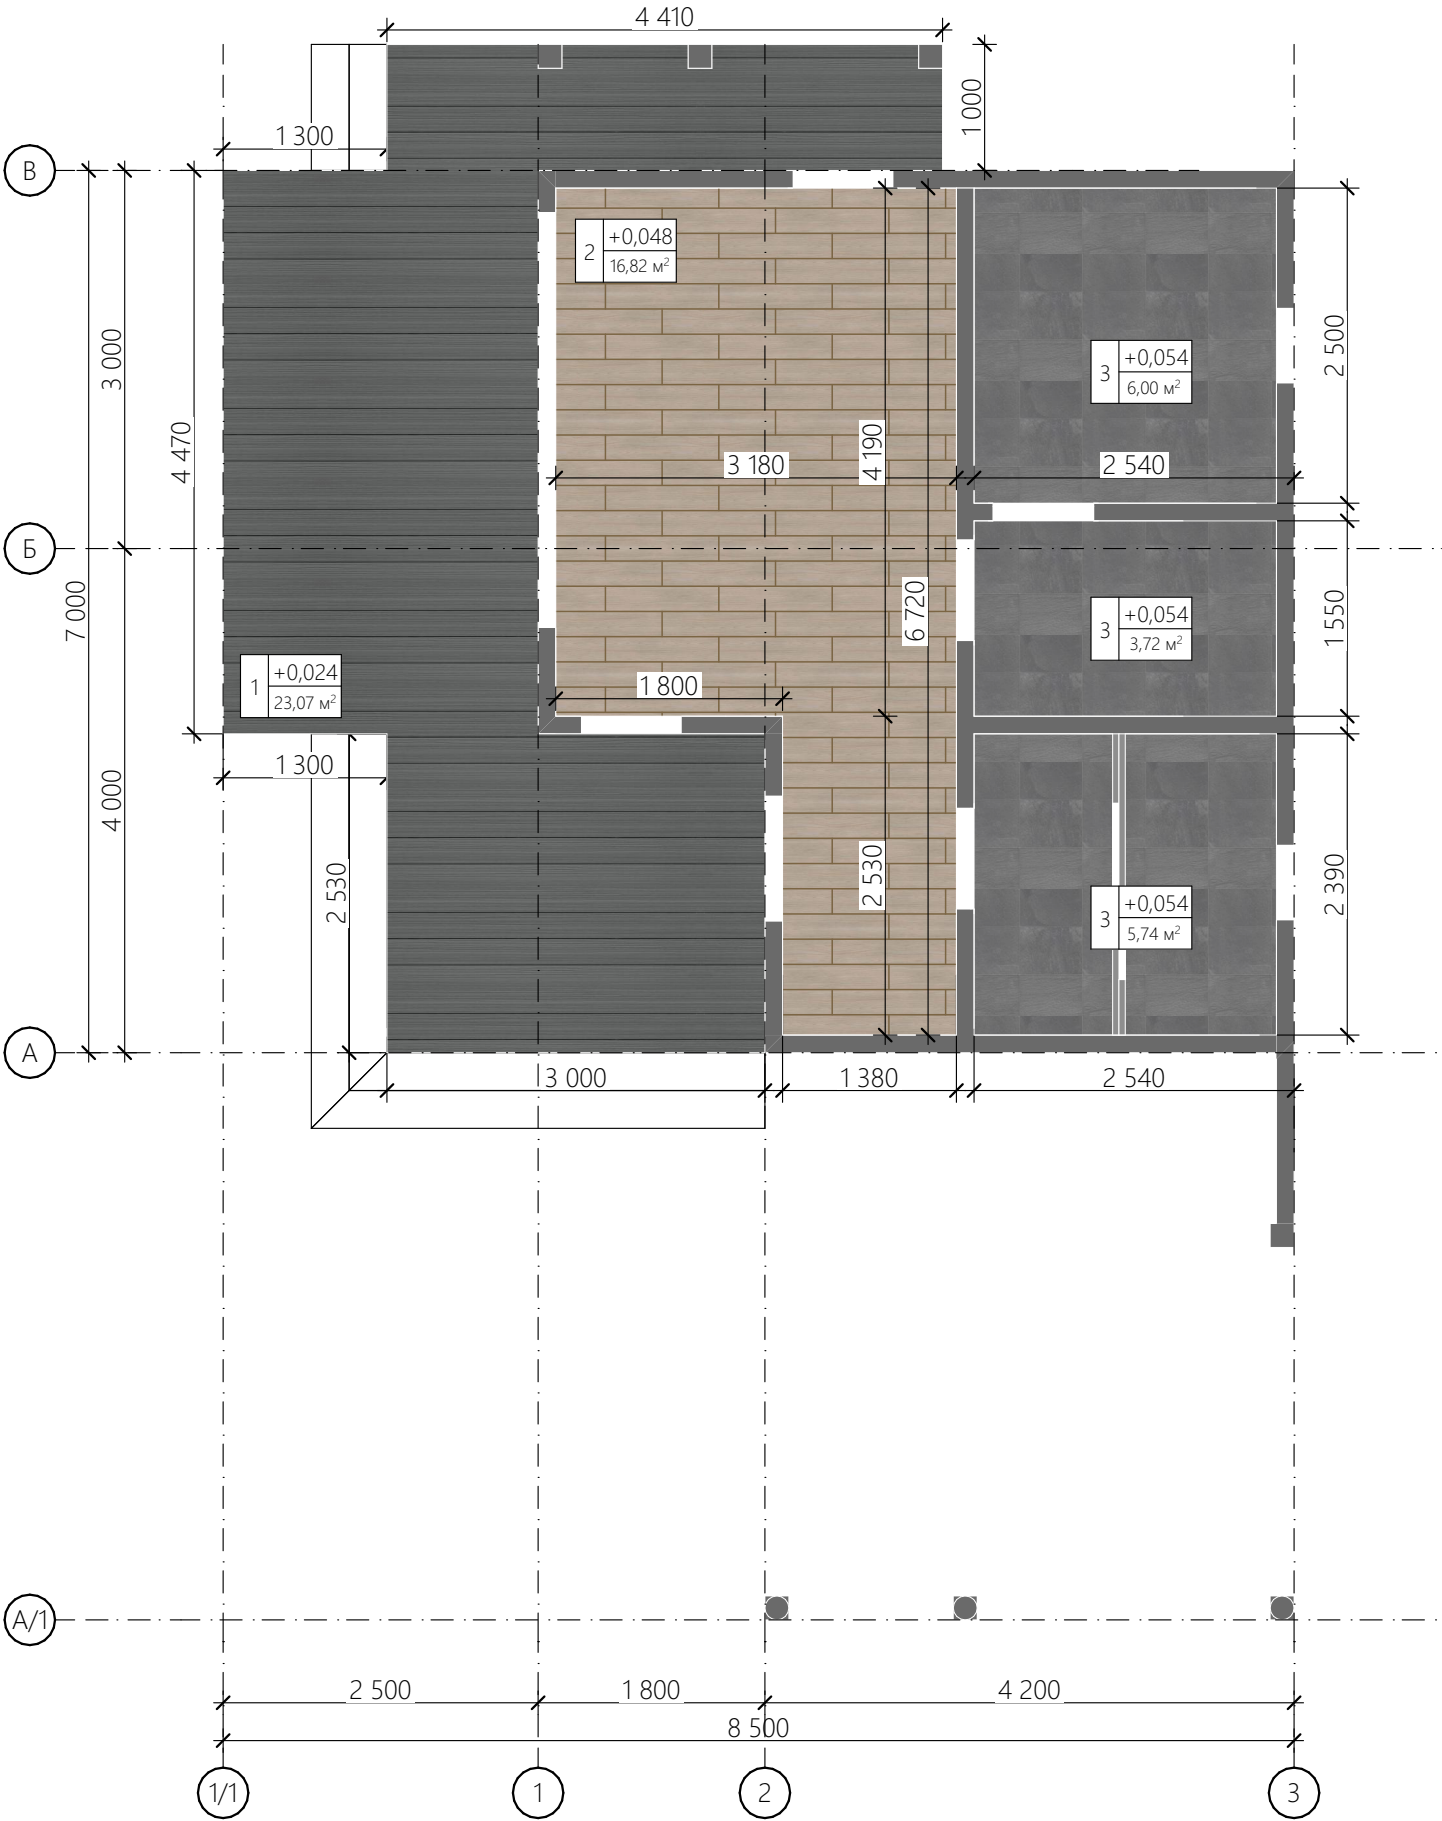

Согласовано

Инва. № подл.

Подп. и дата

Взам. инв. №




Лист	Изм.	№ Докум.	Подп.	Дата

Адрес:

План покрытий пола

#Название Организации

Экспликация покрытий пола

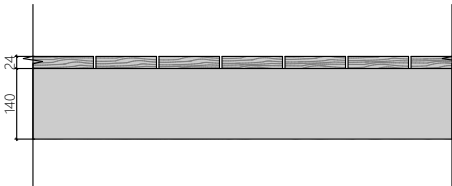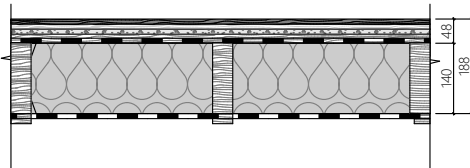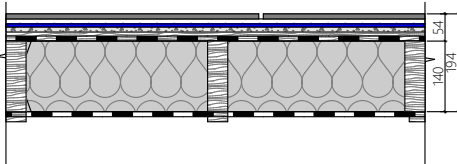№	Наименование	Разрез	Состав
1	Террасная доска		-Террасная доска 24мм -Лага, доска 140х45мм 140 мм
2	Ламинат		-Ламинат 10мм -Подложка под ламинат 10мм -ЦСП 10мм -ОСБ 18мм
3	Керамогранит		-Керамогранит 10мм -Клей 10мм (с устройством теплого эл. пола) -Руспанель 6мм -ЦСП 10мм -ОСБ 18мм

Согласовано			

Инв. № подл.	Подп. и дата	Взам. инв. №

Лист	Изм.	№ Докум.	Подп.	Дата	Экспликация покрытий пола	#Название Организации	Лист
							10

№	Наименование	Условное обозначение
---	--------------	----------------------


1	Планкен (20мм)	
---	----------------	---

2	Фиброцементный сайдинг	
---	------------------------	---

3	Имитация бруса (20мм)	
---	-----------------------	---

4	Вагонка (16мм)	
---	----------------	---

5	Керамогранит (10мм)	
---	---------------------	---

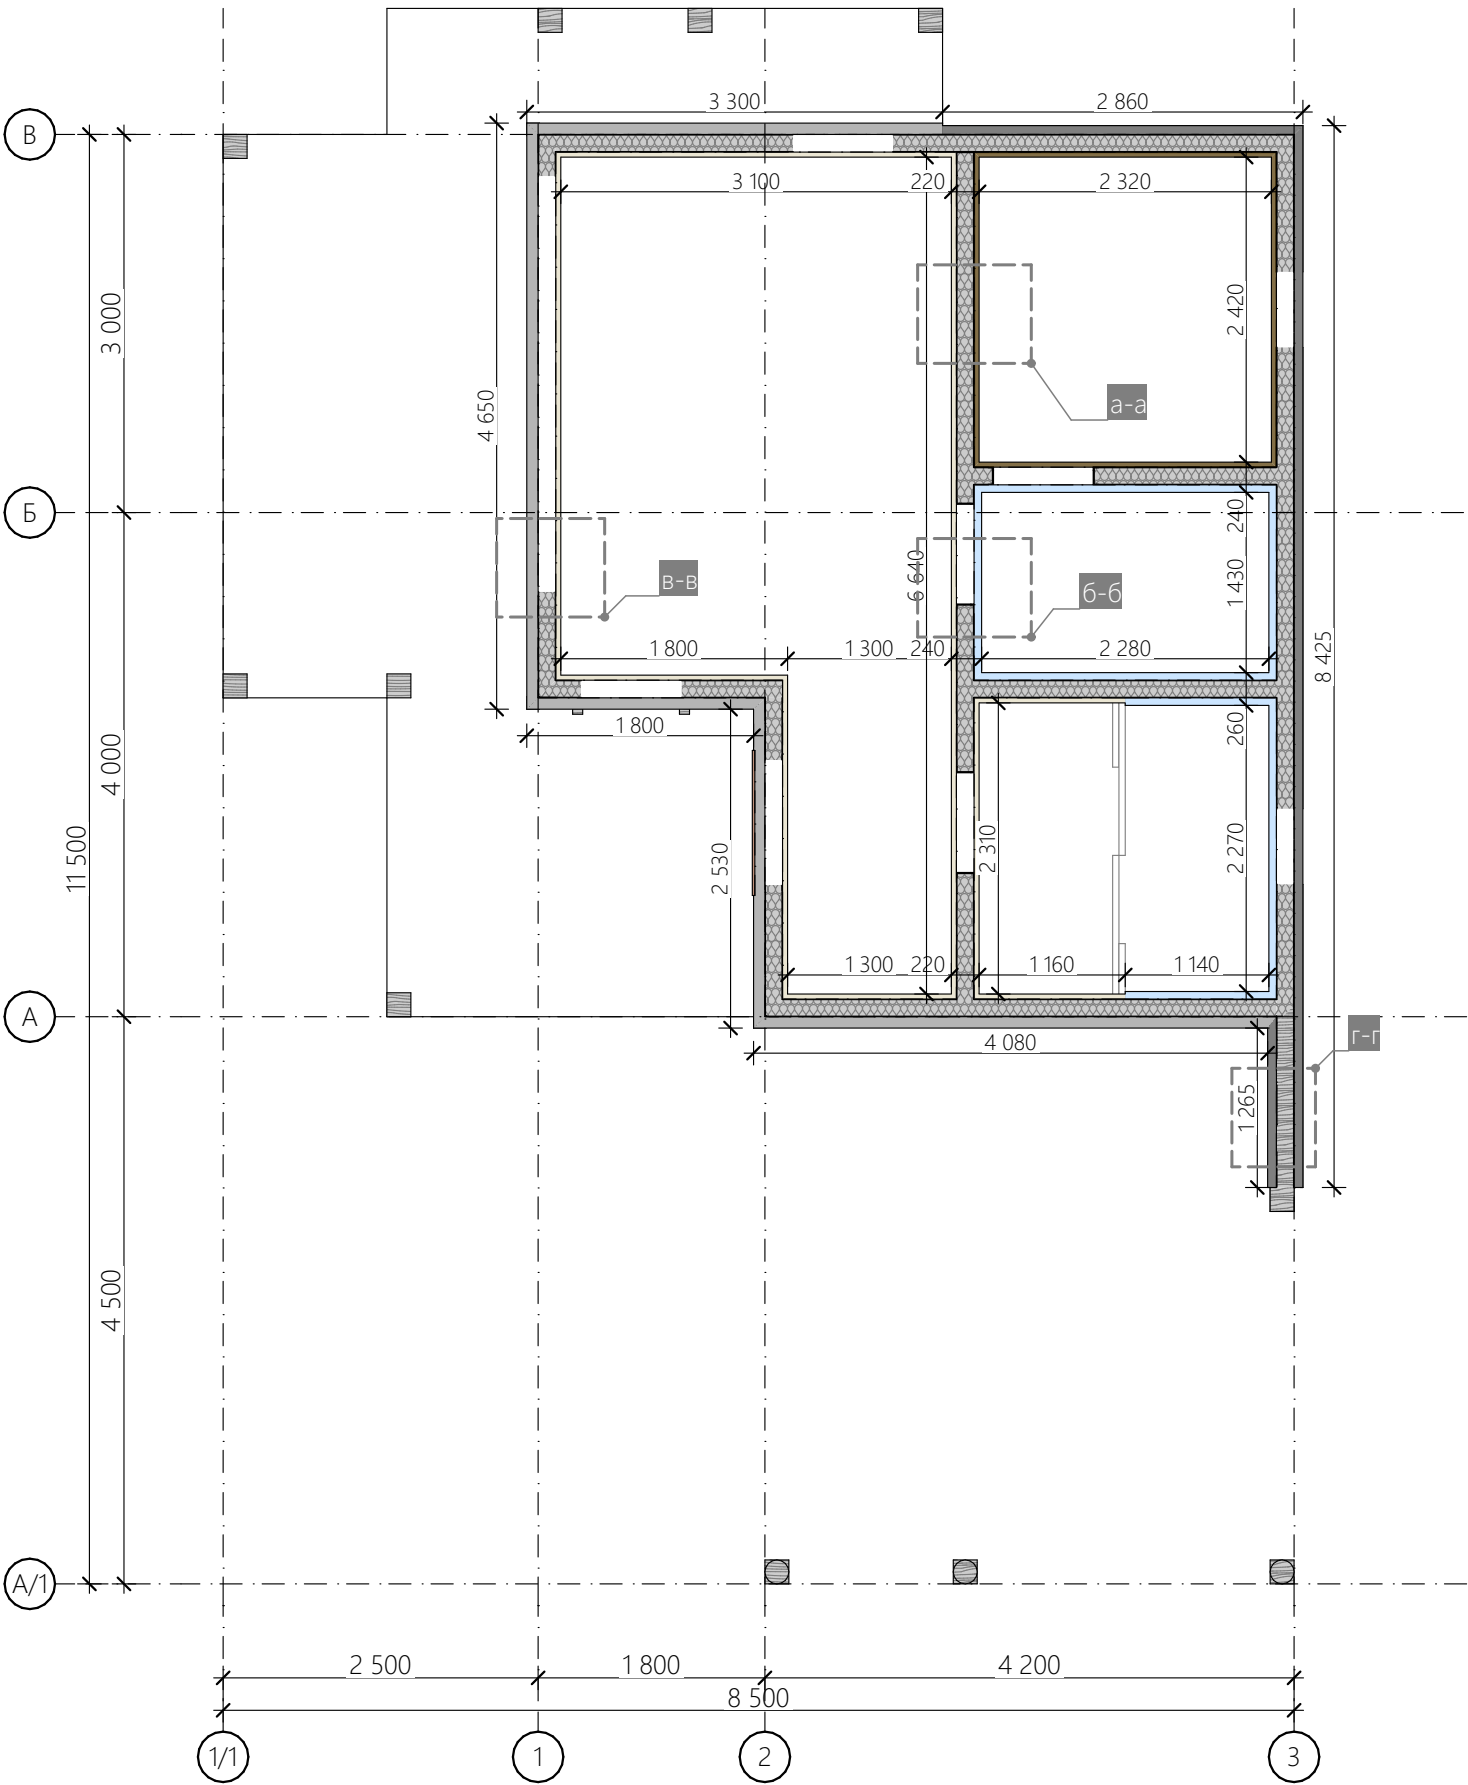

Примечание:

1. Сечение по стенам смотреть на след. листе

Согласовано				
И-в. № подл.	Подп. и дата	Взам. инв. №	Адрес:	

Лист	Изм.	№ Докум.	Подп.	Дата

Адрес:

План покрытия отделки стен

#Название Организации


Экспликация отделки стен

№ разреза

Сечение


Состав

a-a

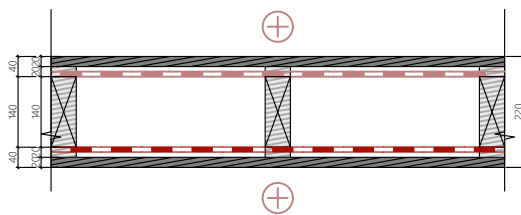


- | | |
|------------------------------|-------|
| -Имитация бруса | 20мм |
| -Вентбрусок (вертикально) | 50мм |
| -Пароизоляционная мембрана | |
| -Стойка каркаса (утепленная) | 140мм |
| -Пароизоляционная мембрана | |
| алюминиевая фольга | |
| -Вентбрусок (вертикально) | 50мм |
| - Вагонка | 20мм |

6-6

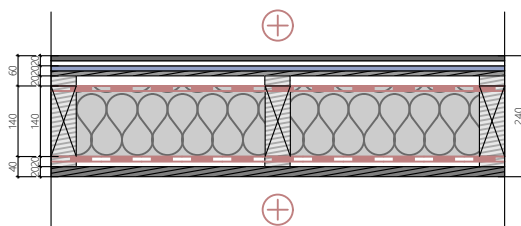


- | | |
|------------------------------|-------|
| -Керамогранит | 10мм |
| -Клей | 10мм |
| -Руспанель | 10мм |
| -ОСБ | 9мм |
| -Обрешётка | 20мм |
| -Пароизоляционная мембрана | |
| -Стойка каркаса (утепленная) | 140мм |
| -Пароизоляционная мембрана | |
| -Вентбрусок (вертикально) | 20мм |
| -Имитация бруса | 20мм |

B-B

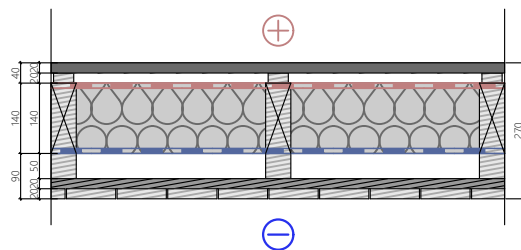

- | | |
|------------------------------|-------|
| -Имитация бруса | 20мм |
| -Вентбрусok (вертикально) | 50мм |
| -Пароизоляционная мембрана | |
| -Стойка каркаса (утепленная) | 140мм |
| -Гидроветрозащитная мембрана | |
| -Вентбрусok (вертикально) | 50мм |
| -Обрешётка | 20мм |
| -Планкен | 20мм |

「-」

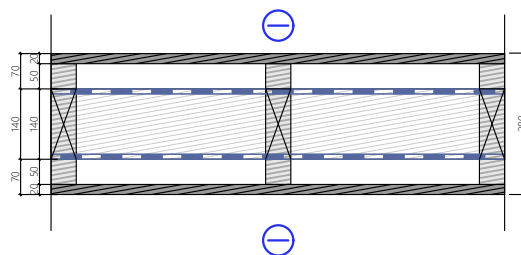

- | | |
|------------------------------|-------|
| -Фиброцементный сайдинг | 20мм |
| -Вентбрусок (вертикально) | 50мм |
| -Гидроветрозащитная мембрана | |
| -Стойка каркаса | 140мм |
| -Гидроветрозащитная мембрана | |
| -Вентбрусок (вертикально) | 50мм |
| -Фиброцементный сайдинг | 20мм |

Согласовано

Взам. инв. №

Подп. и дата

ИНВ. № подл.

Лист	Изм.	№ Докум.	Подп.	Дата

Экспликация отделки стен


#Название Организации

ЛИСТ

12

Условные обозначения:

-  - розетка 220V с заземлением
-  - розетка 220V с заземлением и влагозащитой
-  - розетка для ТВ
-  - интернет - розетка
-  - электровывод

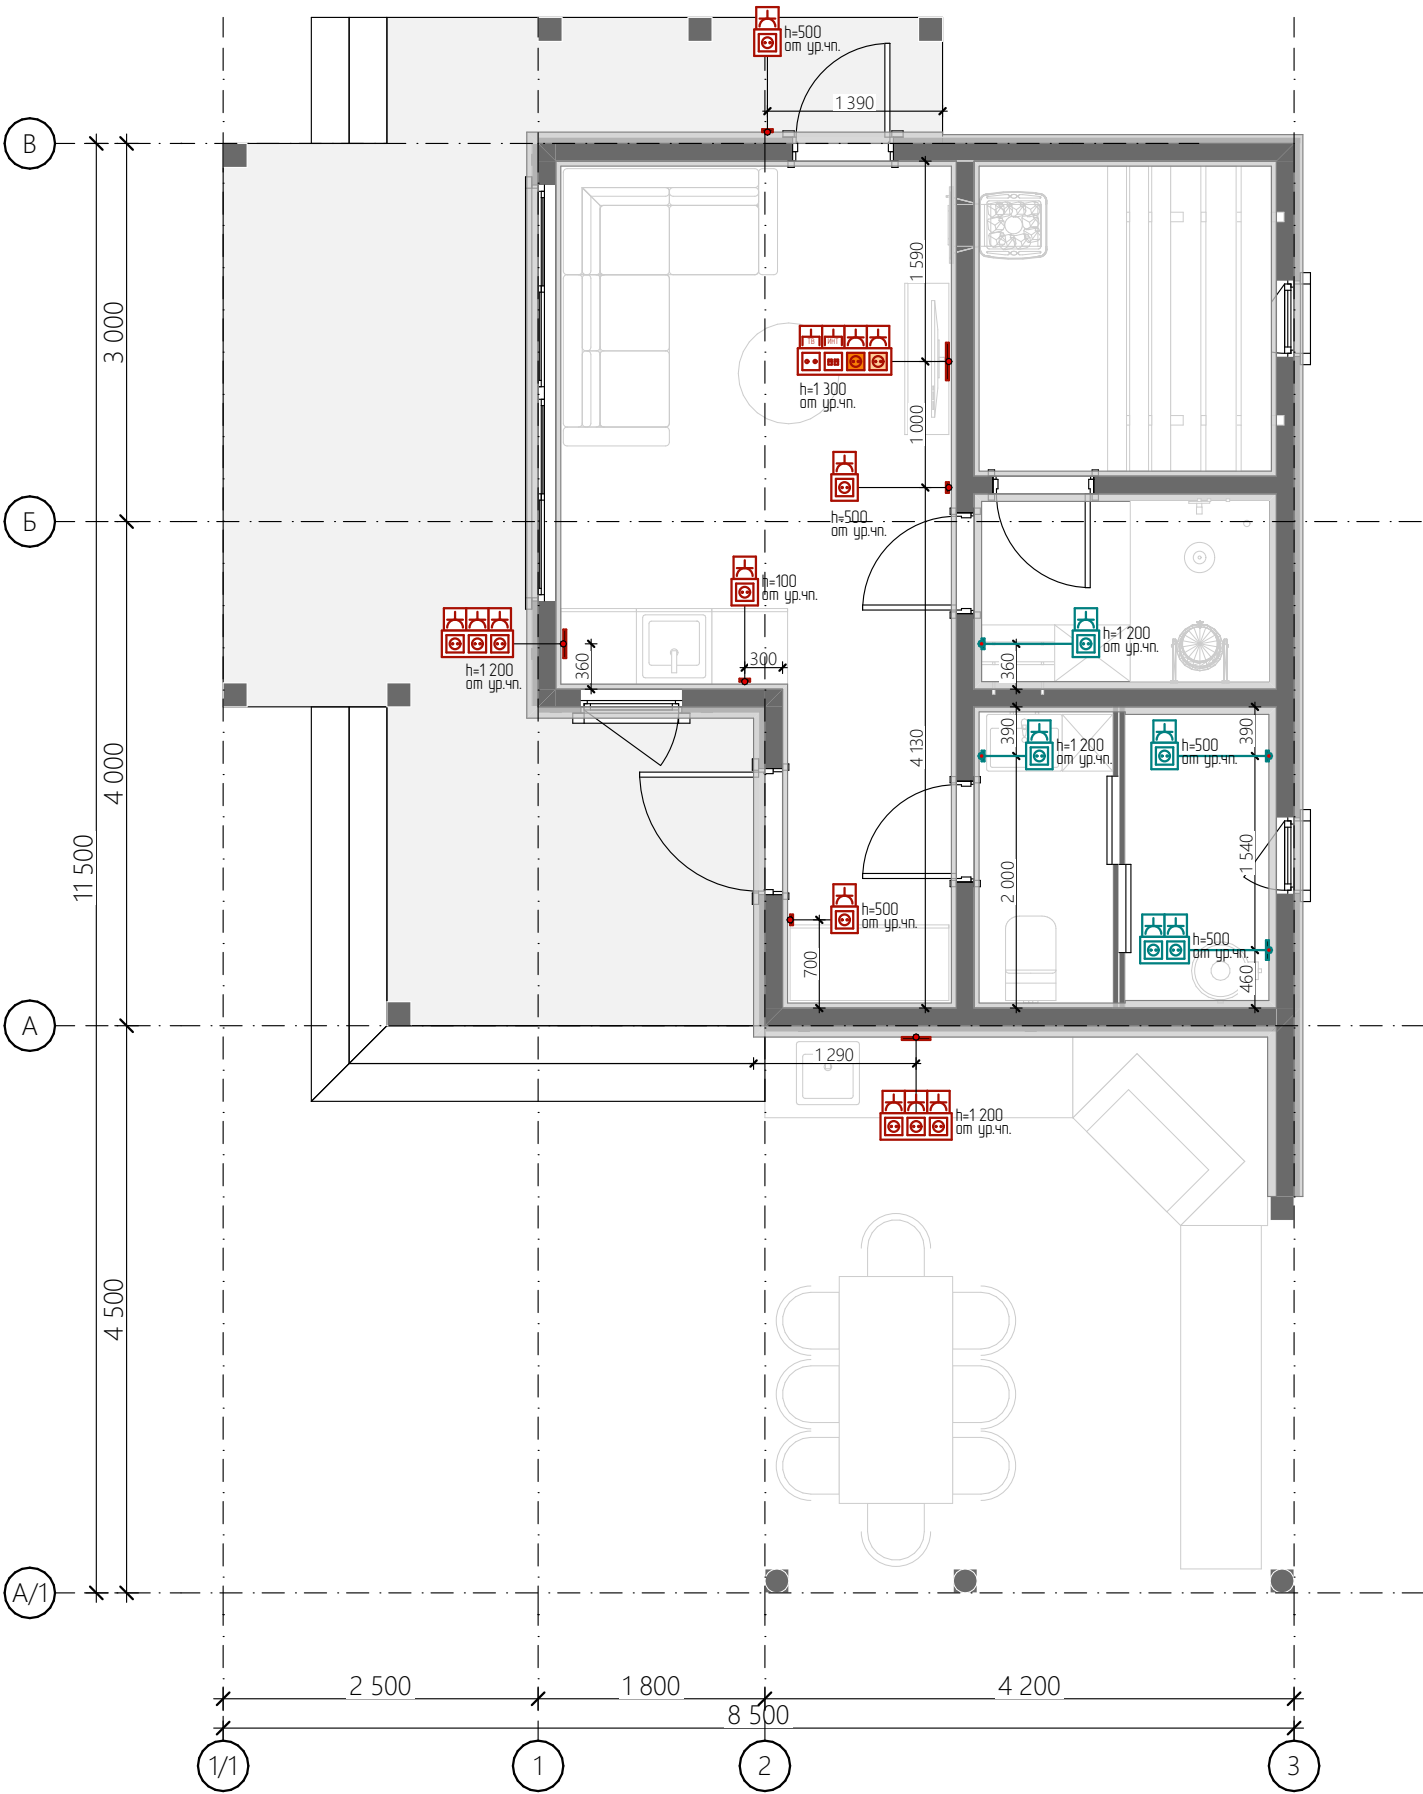

Примечание:

1. Схема размещения розеток является рекомендательной и требует согласования с заказчиком по месту.

2. Все высоты даны от чистового пола.

3. Все указанные размеры даются до центра позиций.

4. Отметки розеток, выключателей, выводов и др. оборудования, являются предварительными и уточняются после выбора финишных материалов и мебели.

5. Размеры уточняются дополнительно

Согласовано				
И-нв. № подл.	Подп. и дата	Взам. инв. №		

Лист	Изм.	№ Докум.	Подп.	Дата


Адрес:

План размещения розеток
стен

#Название Организации

Условные обозначения:

-  - выключатель одноклавишный
-  - выключатель двухклавишный
-  - люстра
-  - точечный светильник
-  - настенные бра
-  - контурная подсветка
-  - трековый светильник

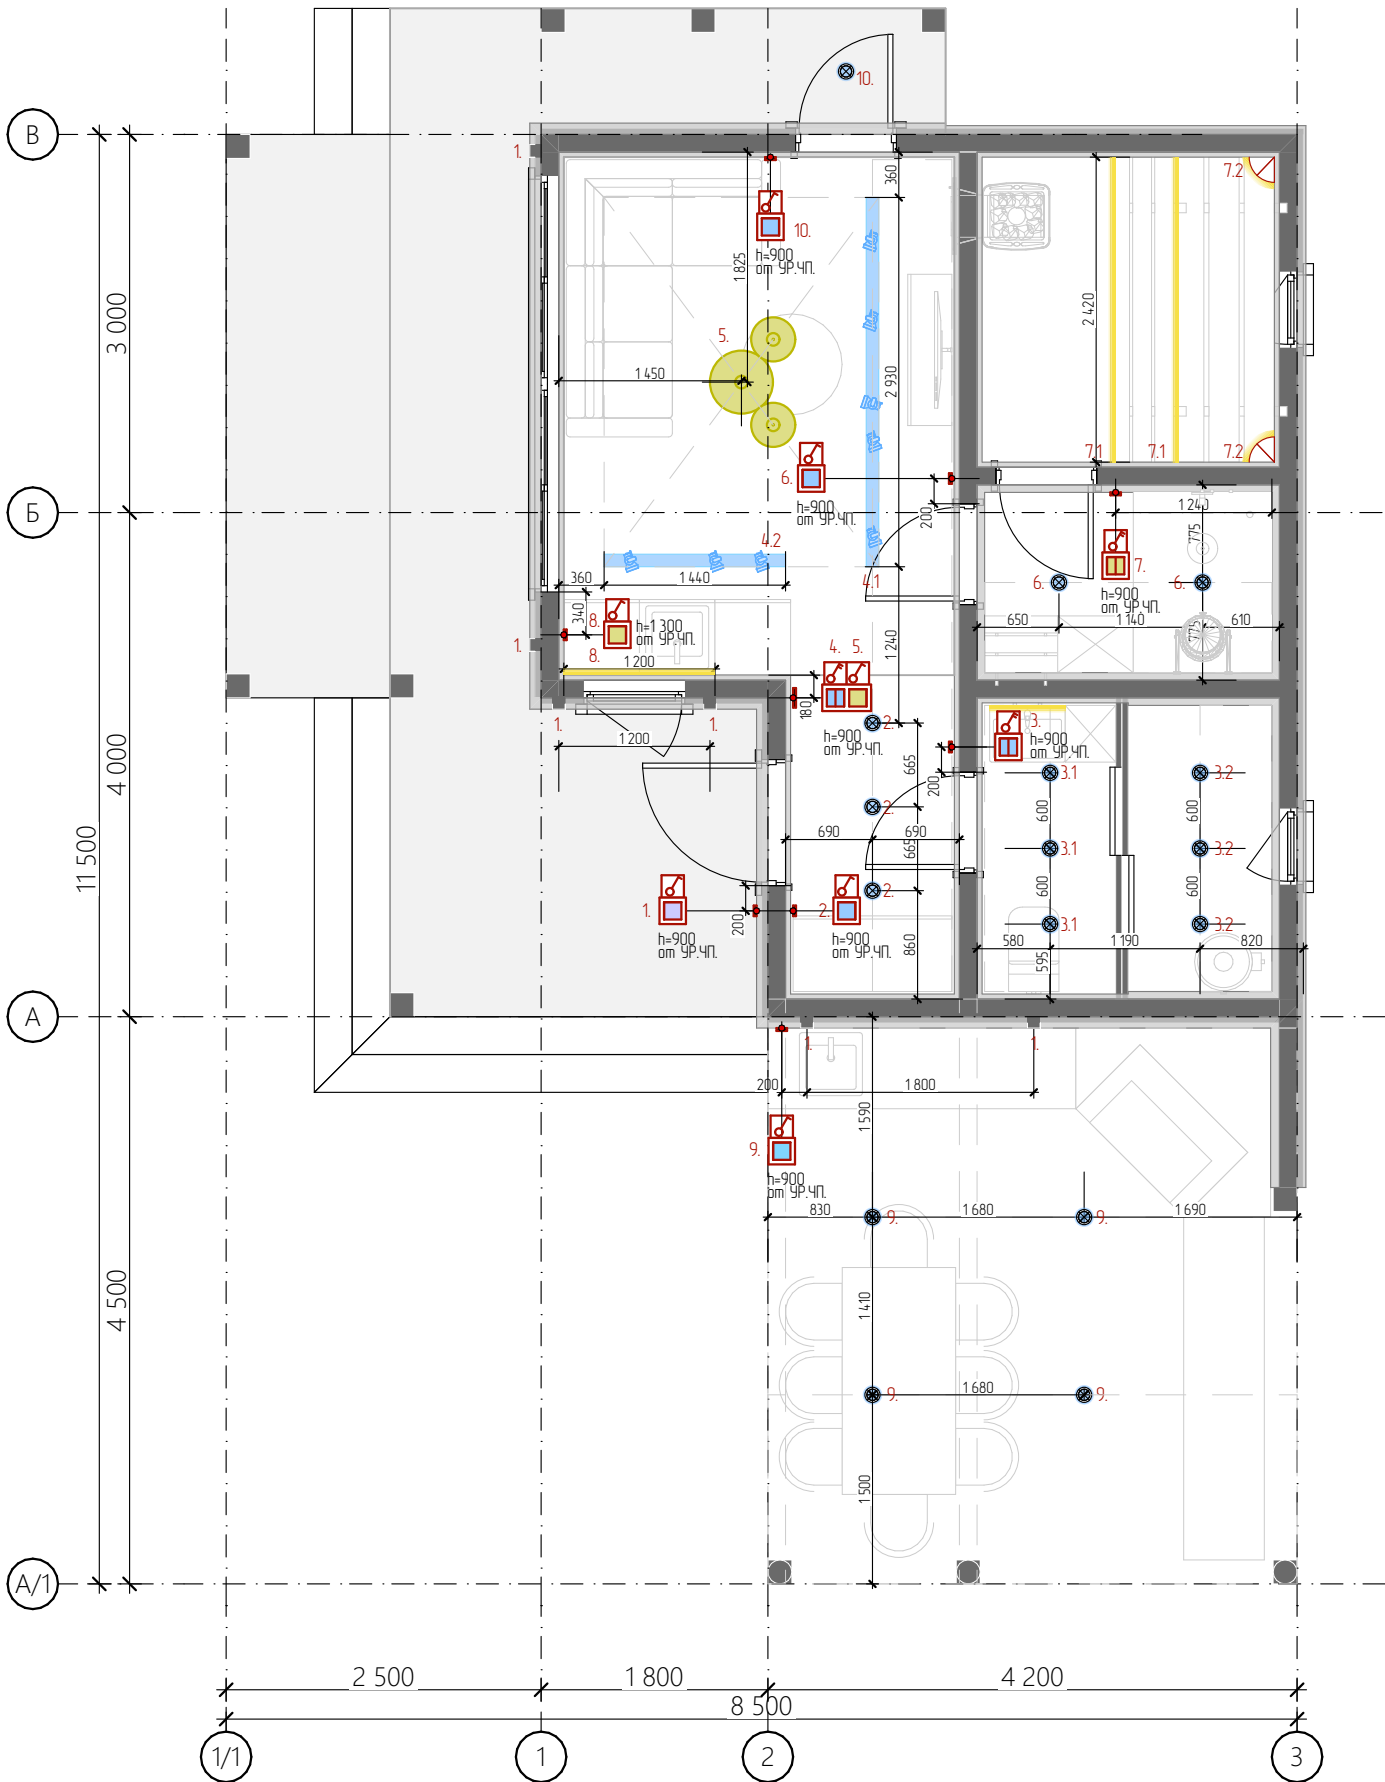

Примечание:

1. Схема размещения розеток является рекомендательной и требует согласования с заказчиком по месту.
2. Все высоты даны от чистового пола.
3. Все указанные размеры даются до центра позиций.
4. Отметки розеток, выключателей, выводов и др. оборудования, являются предварительными и уточняются после выбора финишных материалов и мебели.
5. Размеры уточняются дополнительно

Согласовано

Взам. инв. №

Подп. и дата


Инв. № подл.

Лист	Изм.	№ Докум.	Подп.	Дата

Адрес:

План расстановки
светильников и
выключателей


#Название Организации

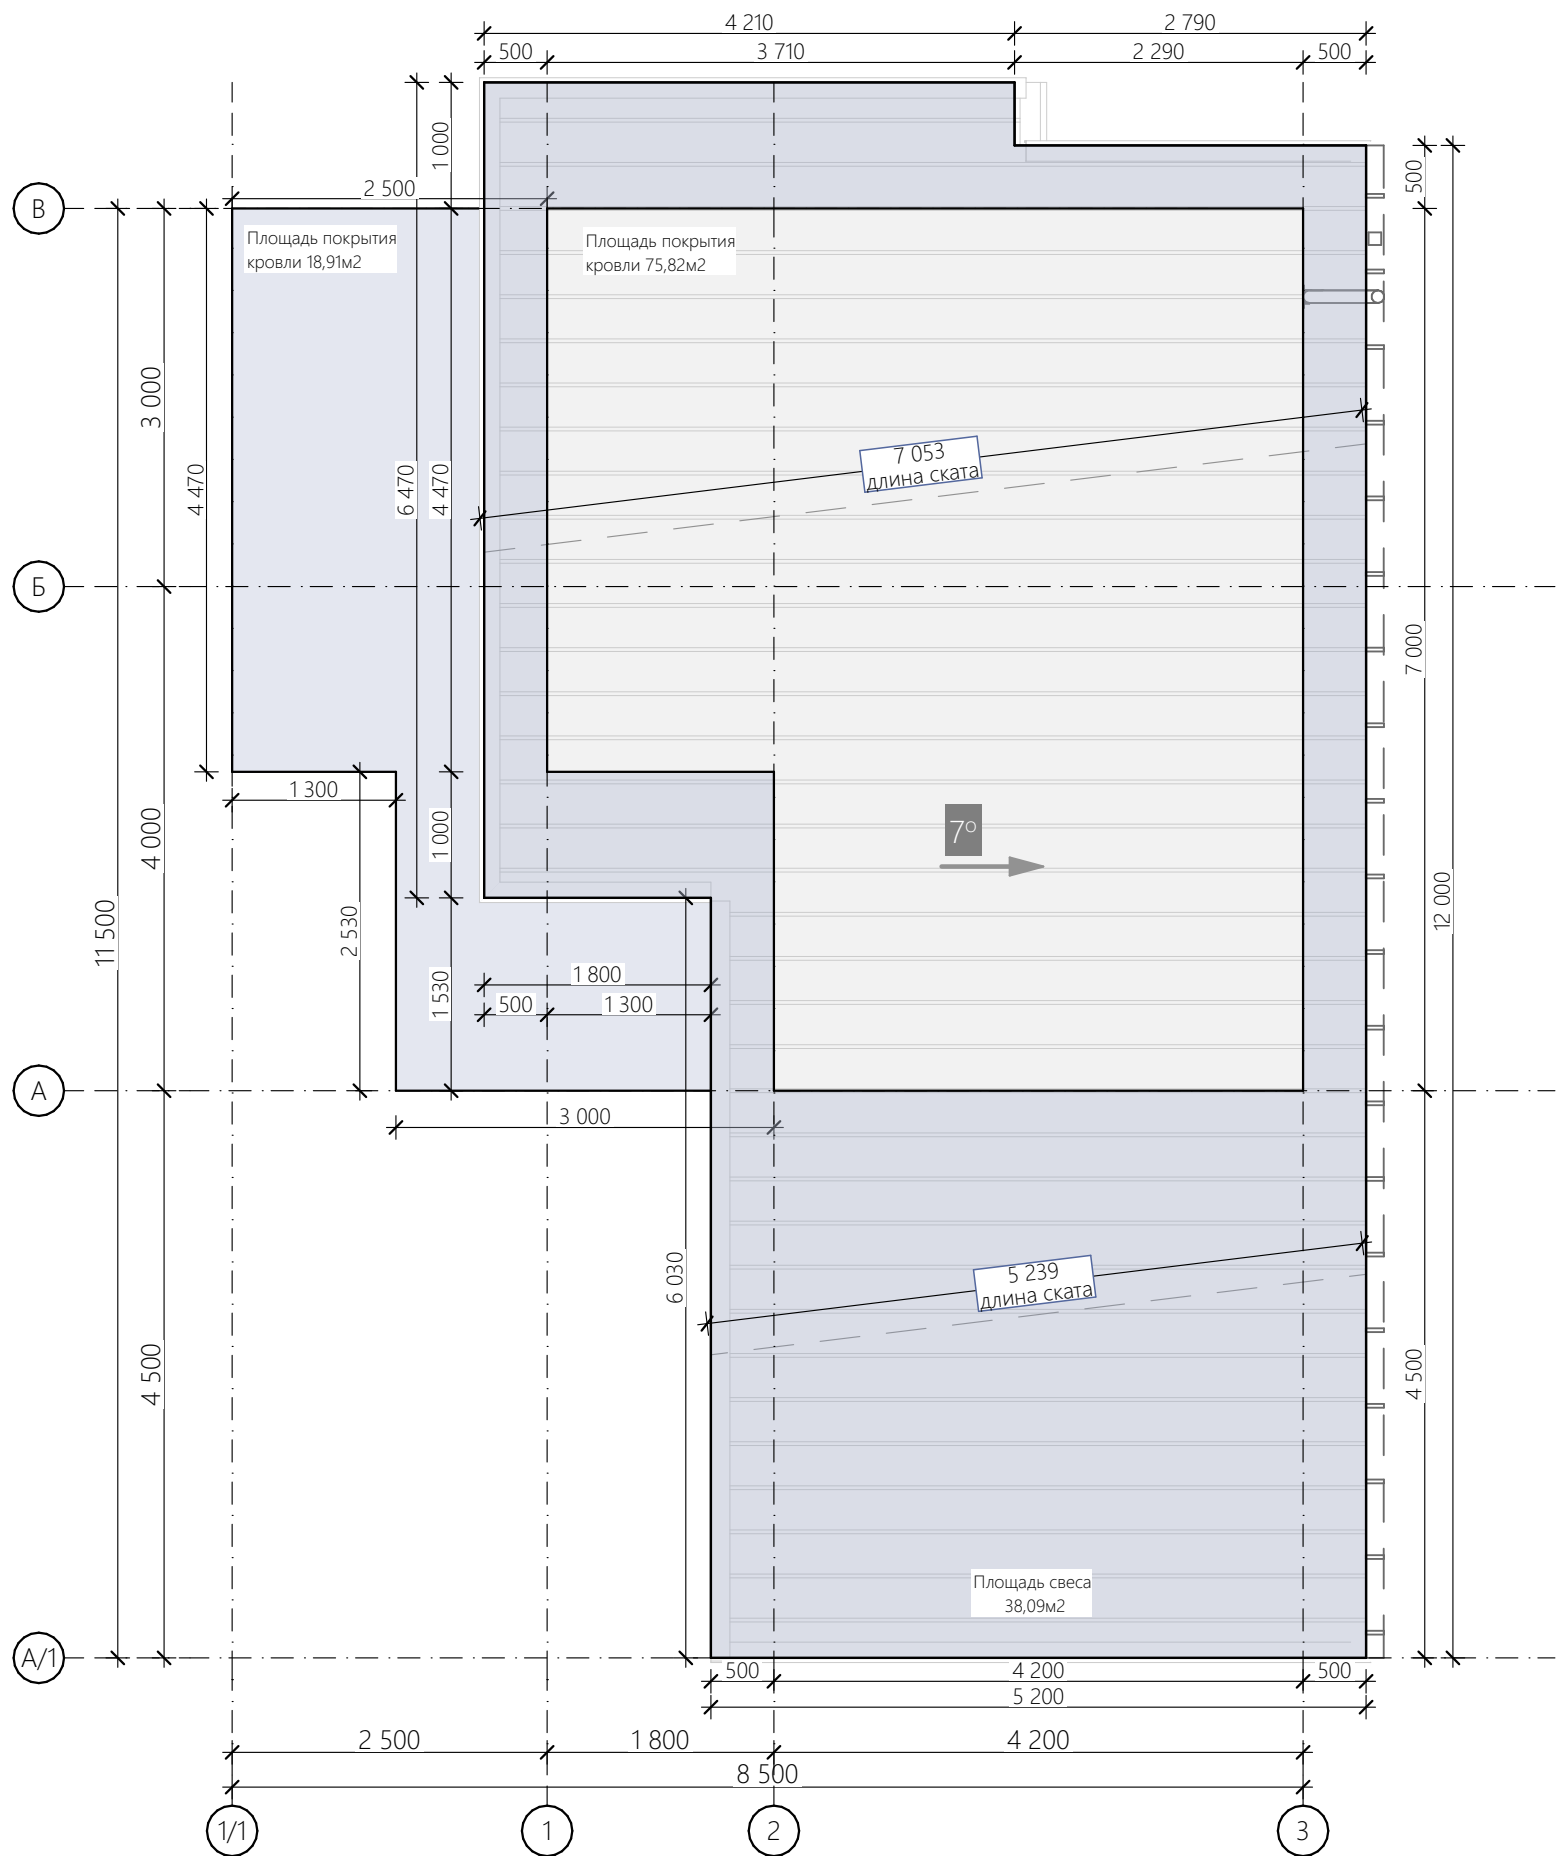

Условные обозначения:

- Кровля бани
- Подшив свесов бани

аксонометрия кровли:

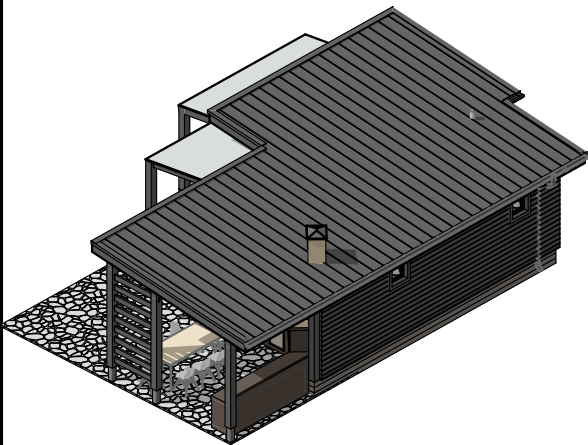

Согласовано				
И-нв. № подл.	Подп. и дата	Взам. инв. №		

Лист	Изм.	№ Докум.	Подп.	Дата

Адрес:

План кровли

#Название Организации

Согласовано

Взам. инв. №

Подп. и дата

Инв. № подл.

Лист	Изм.	№ Докум.	Подп.	Дата

Адрес:

Разрез 1-1


#Название Организации

Лист

16

Разрез 1-1

1:50

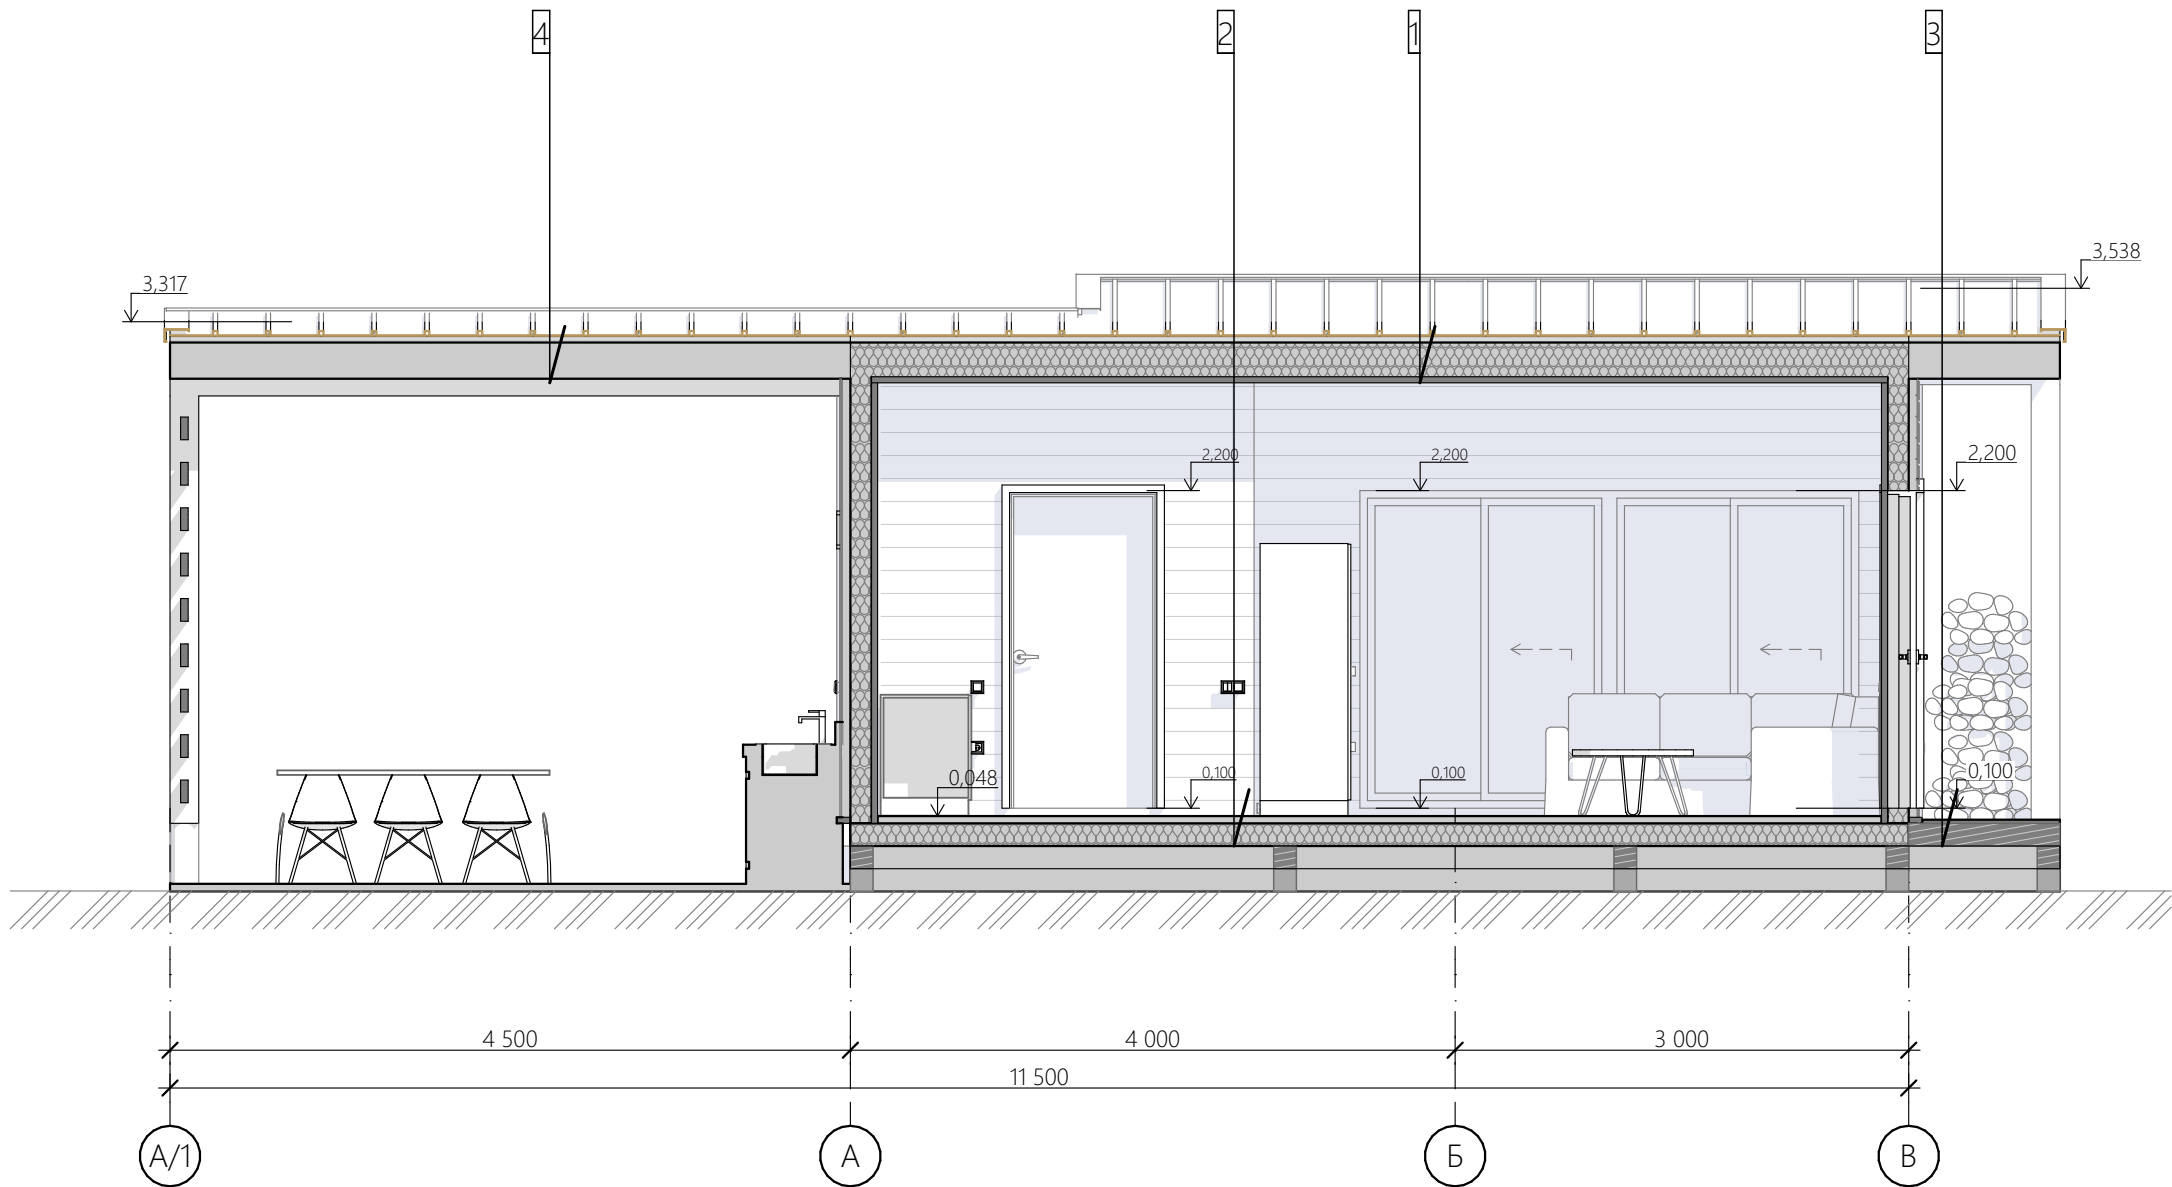


- | | | |
|---|------------------------------|-----------------|
| 1 | -Фальц | двойной стоячий |
| | -Обрешётка | 25x100мм |
| | -Контробрешётка | 50x50мм |
| | -Гидроветрозащитная мембрана | |
| | -Стропильная система | 190x45мм |
| | утепленная | |
| | -Пароизоляционная мембрана | |
| | -Обрешётка | 20мм |
| | -Имитация бруса | 20мм |
-
- | | | |
|---|------------------------------|-------|
| 2 | -Ламинат | 10мм |
| | -Подложка под ламинат | 10мм |
| | -ЦСП | 10мм |
| | -ОСБ | 18мм |
| | -Пароизоляционная мембрана | |
| | -Лаги перекрытия (утепл.) | 140мм |
| | -Гидроветрозащитная мембрана | |
| | -Просечка (сетка яч. 5x5) | |
| | -Обрешётка | 20мм |
-
- | | | |
|---|-----------------------|--------|
| 3 | -Террасная доска | 24мм |
| | -Лага, доска 140x45мм | 140 мм |
-
- | | | |
|---|------------------------------|-----------------|
| 4 | -Фальц | двойной стоячий |
| | -Обрешётка | 25x100мм |
| | -Контробрешётка | 50x50мм |
| | -Гидроветрозащитная мембрана | |
| | -Стропильная система | 190x45мм |
| | -Имитация бруса | 20мм |

Ведомость оконных проемов

Наименование шт Размеры проема Ш х В, мм Вид Площадь, м2


ОК-01 1 3 300×2 100 6,93

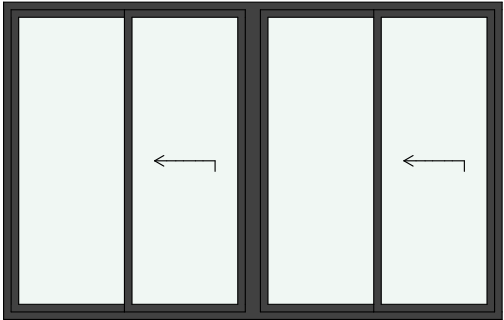

ОК-02 2 600×600 0,36



ОК-03 1 800×1 000 0,80

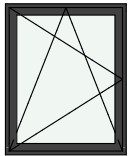

8,45 м²

Примечание:
1. Изготовление окон и дверей определяется заказчиком, допускается изменение открывания окон и дверей;
2. При заказе оконных и дверных блоков необходим обмер по месту от изготовителя;
3. Оконные и дверные изделия изображены со стороны открывания.

Ведомость дверных проемов

Наименование	шт.	Размеры проема	Ш х В, мм	Вид	Площадь, м2
--------------	-----	----------------	-----------	-----	-------------

ДВ-1	3	800×2 100			1,68
------	---	-----------	--	---	------

ДВ-2	1	800×2 100			1,68
------	---	-----------	--	---	------

ДН-1	1	1 000×2 100			2,10
------	---	-------------	--	--	------

8,82 м²

Примечание:

- 1. Изготовление окон и дверей определяется заказчиком, допускается изменение открывания окон и дверей;
- 2. При заказе оконных и дверных блоков необходим обмер по месту от изготовителя;
- 3. Оконные и дверные изделия изображены со стороны открывания.

Согласовано

Взам. инв. №

Подп. и дата

Инв. № подл.

Лист	Изм.	№ Докум.	Подп.	Дата

Адрес:

Цветовое решение; Фасад в
осях В-А

Условные обозначения:




-Планкен



-Террасная доска ДПК



-Водосточная система,
наличники, оконные
рамы, кровля(RAL 7004)

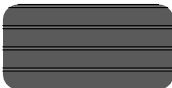

-Фиброцементный
сайдинг



#Название Организации

Лист

20

Согласовано


Взам. инв. №

Подп. и дата

Инв. № подл.

Ф-2

1:40

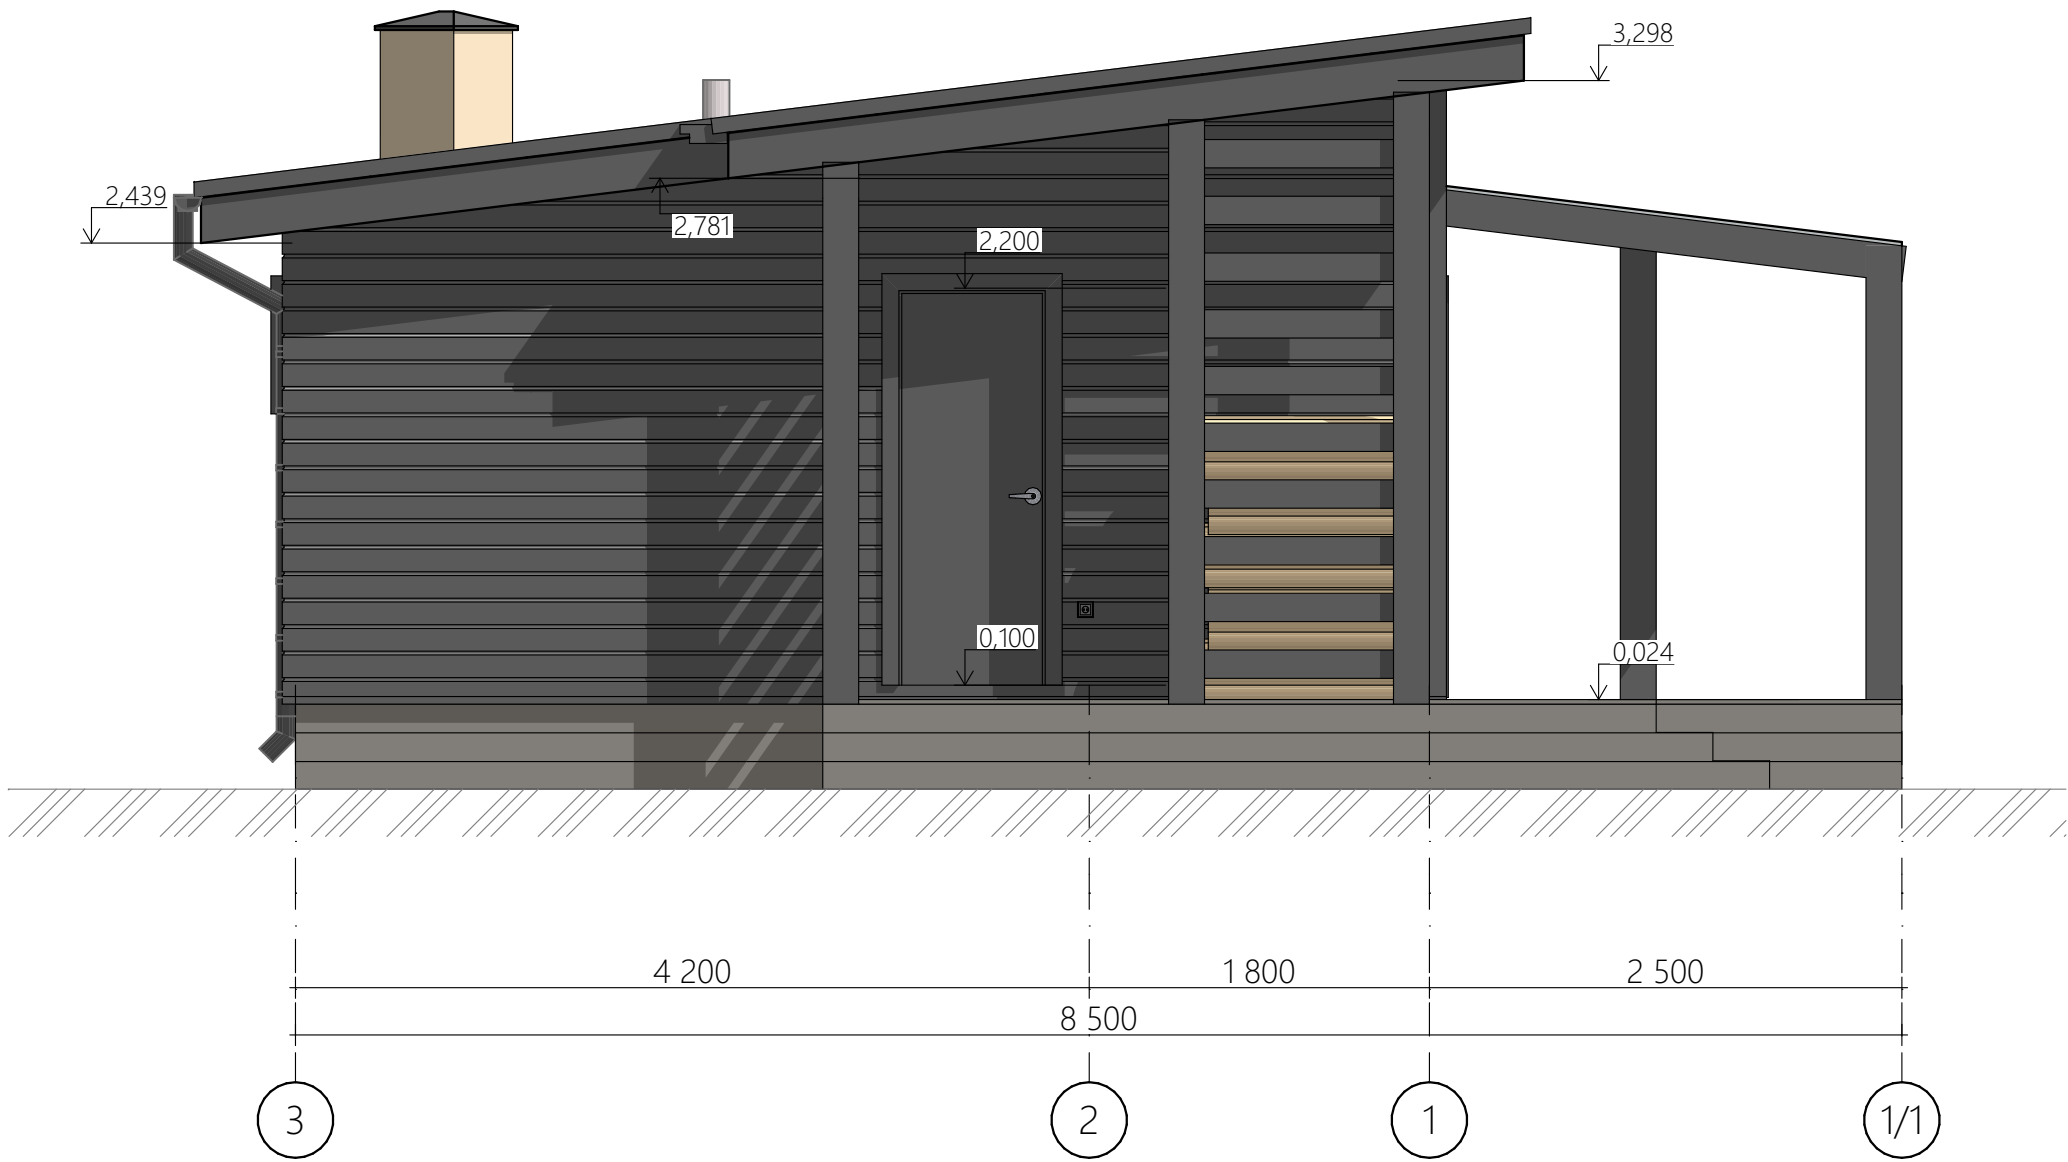

Условные обозначения:

- Планкен
- Террасная доска ДПК
- Водосточная система, наличники, оконные рамы, кровля(RAL 7004)
- Фиброцементный сайдинг


Лист	Изм.	№ Докум.	Подп.	Дата

Адрес:

Цветовое решение; Фасад в осях 3-1

#Название Организации

Согласовано

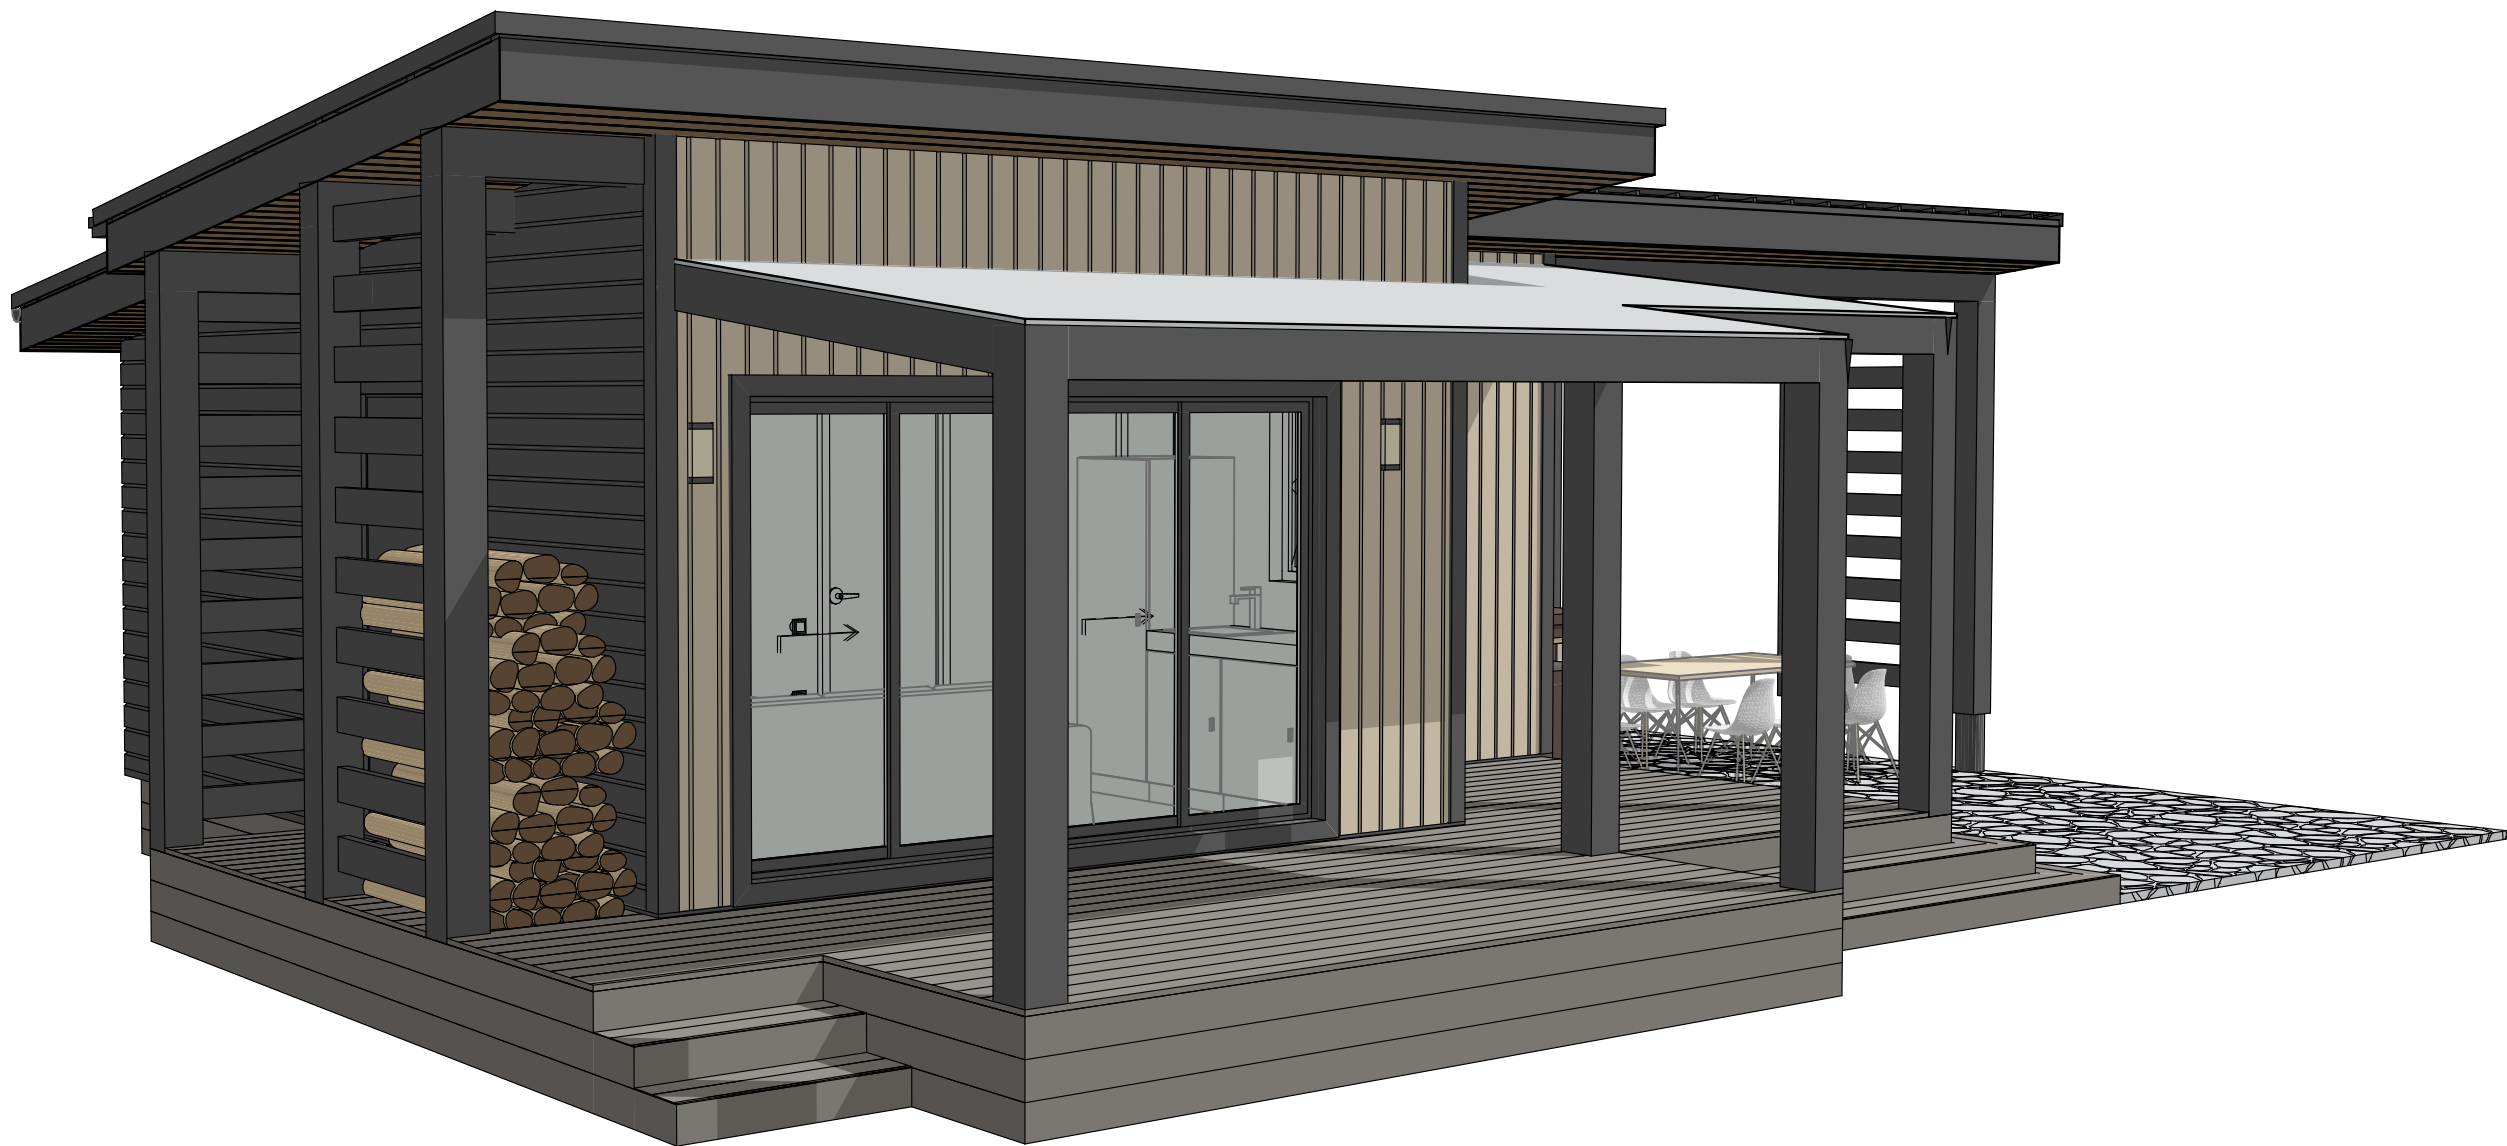

И.нв. № подл. Подп. и дата Взам. инв. №

Лист	Изм.	№ Докум.	Подп.	Дата

Адрес:

Аксометрия №1

#Название Организации

Лист
22


Согласовано				
И-нв. № подл.	Взам. инв. №		Подп. и дата	

Лист	Изм.	№ Докум.	Подп.	Дата


Адрес:

Цветовое решение; Фасад в осях 1-3

#Название Организации

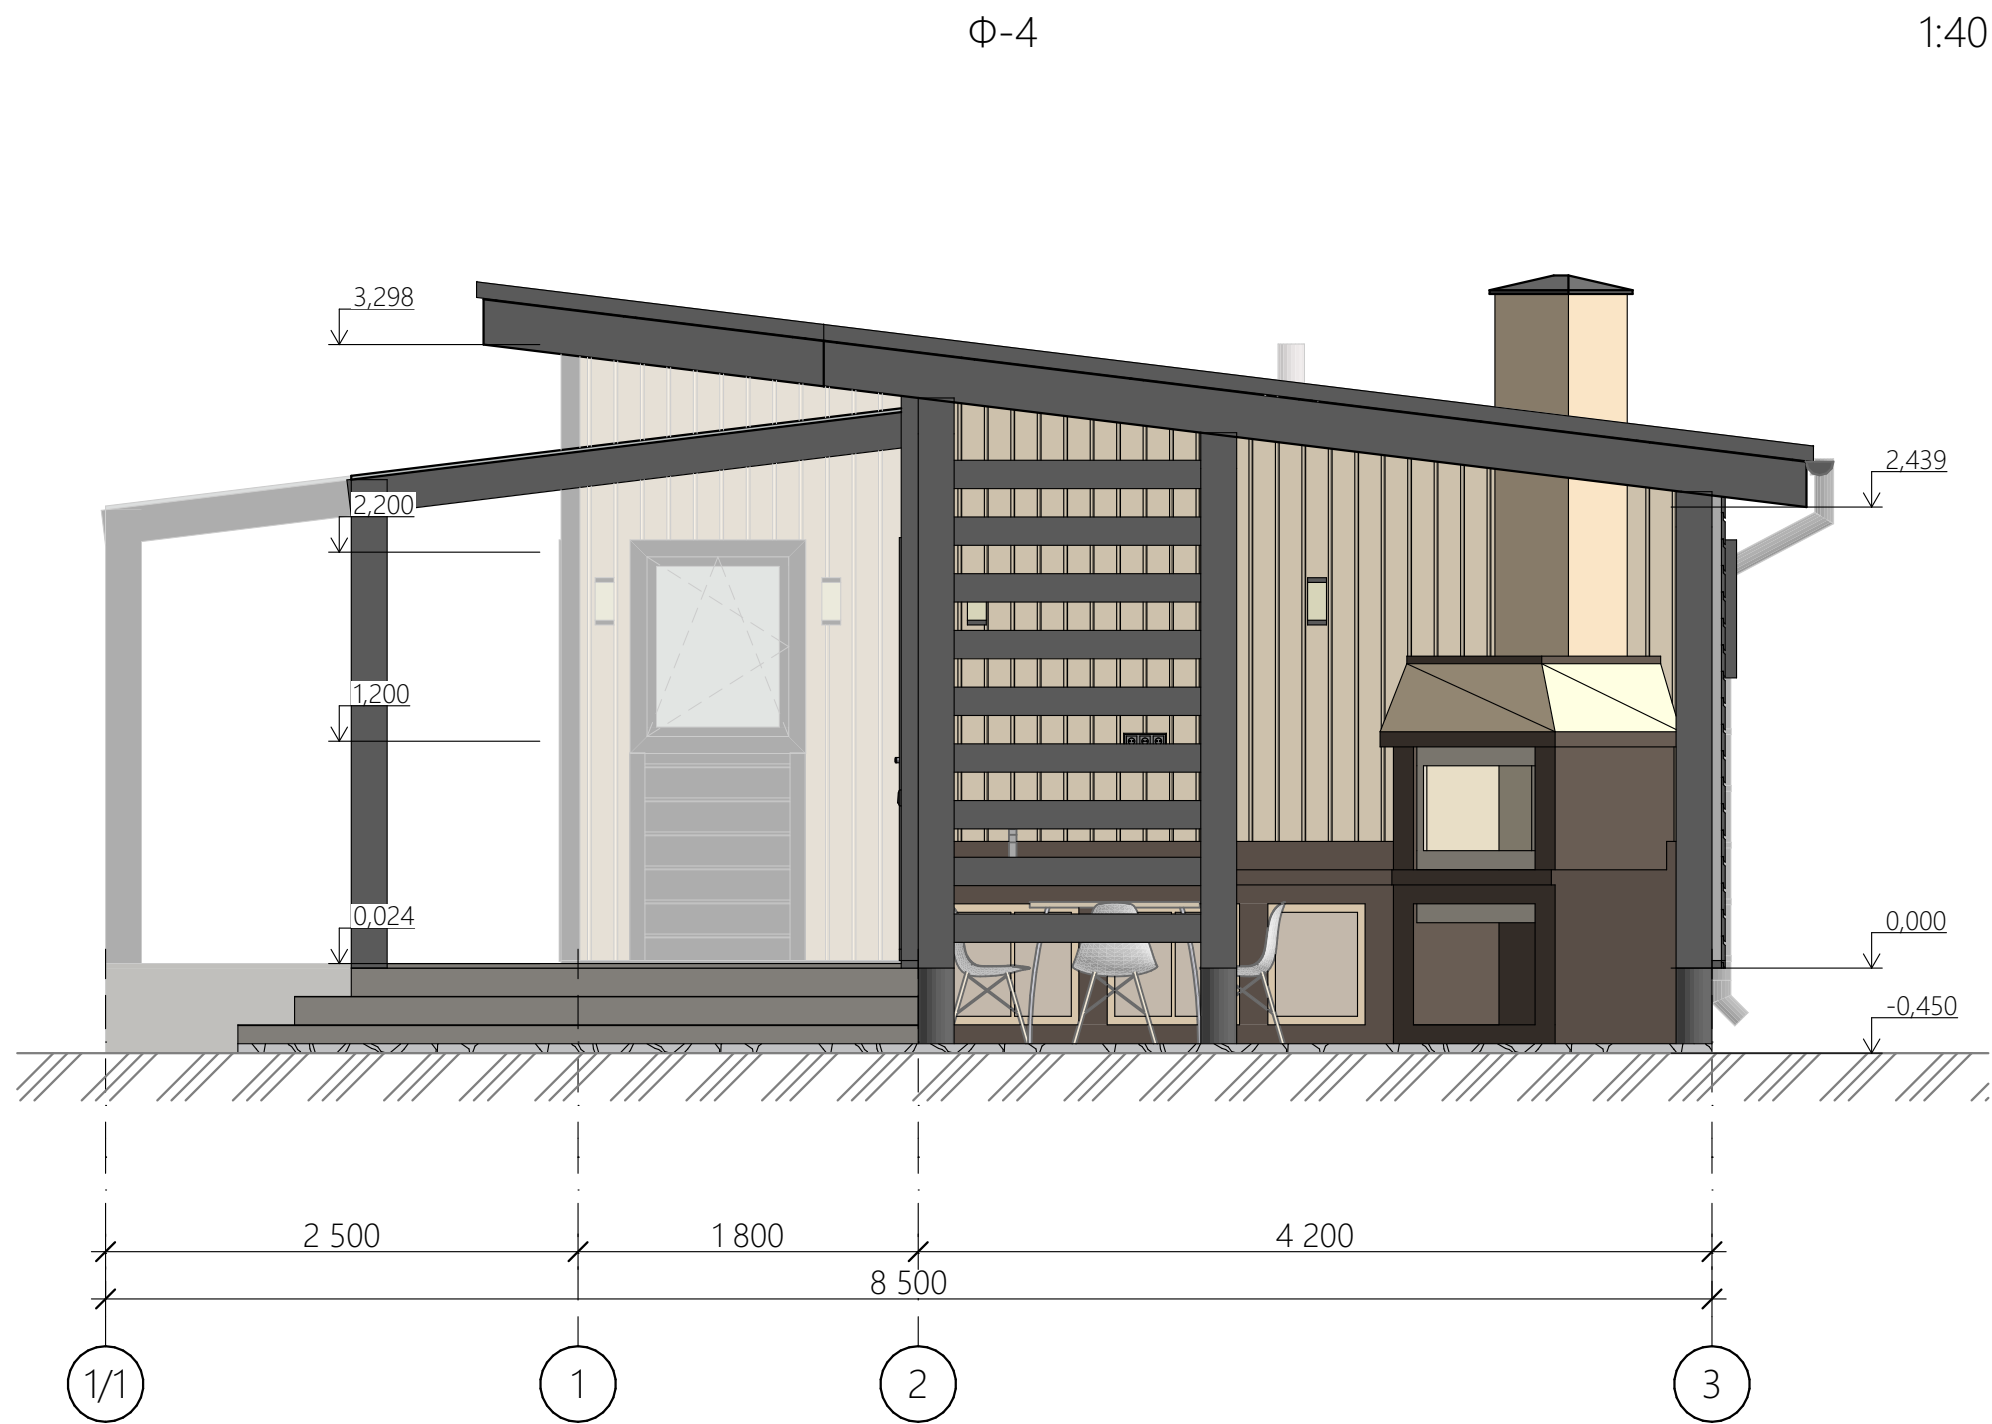

Согласовано

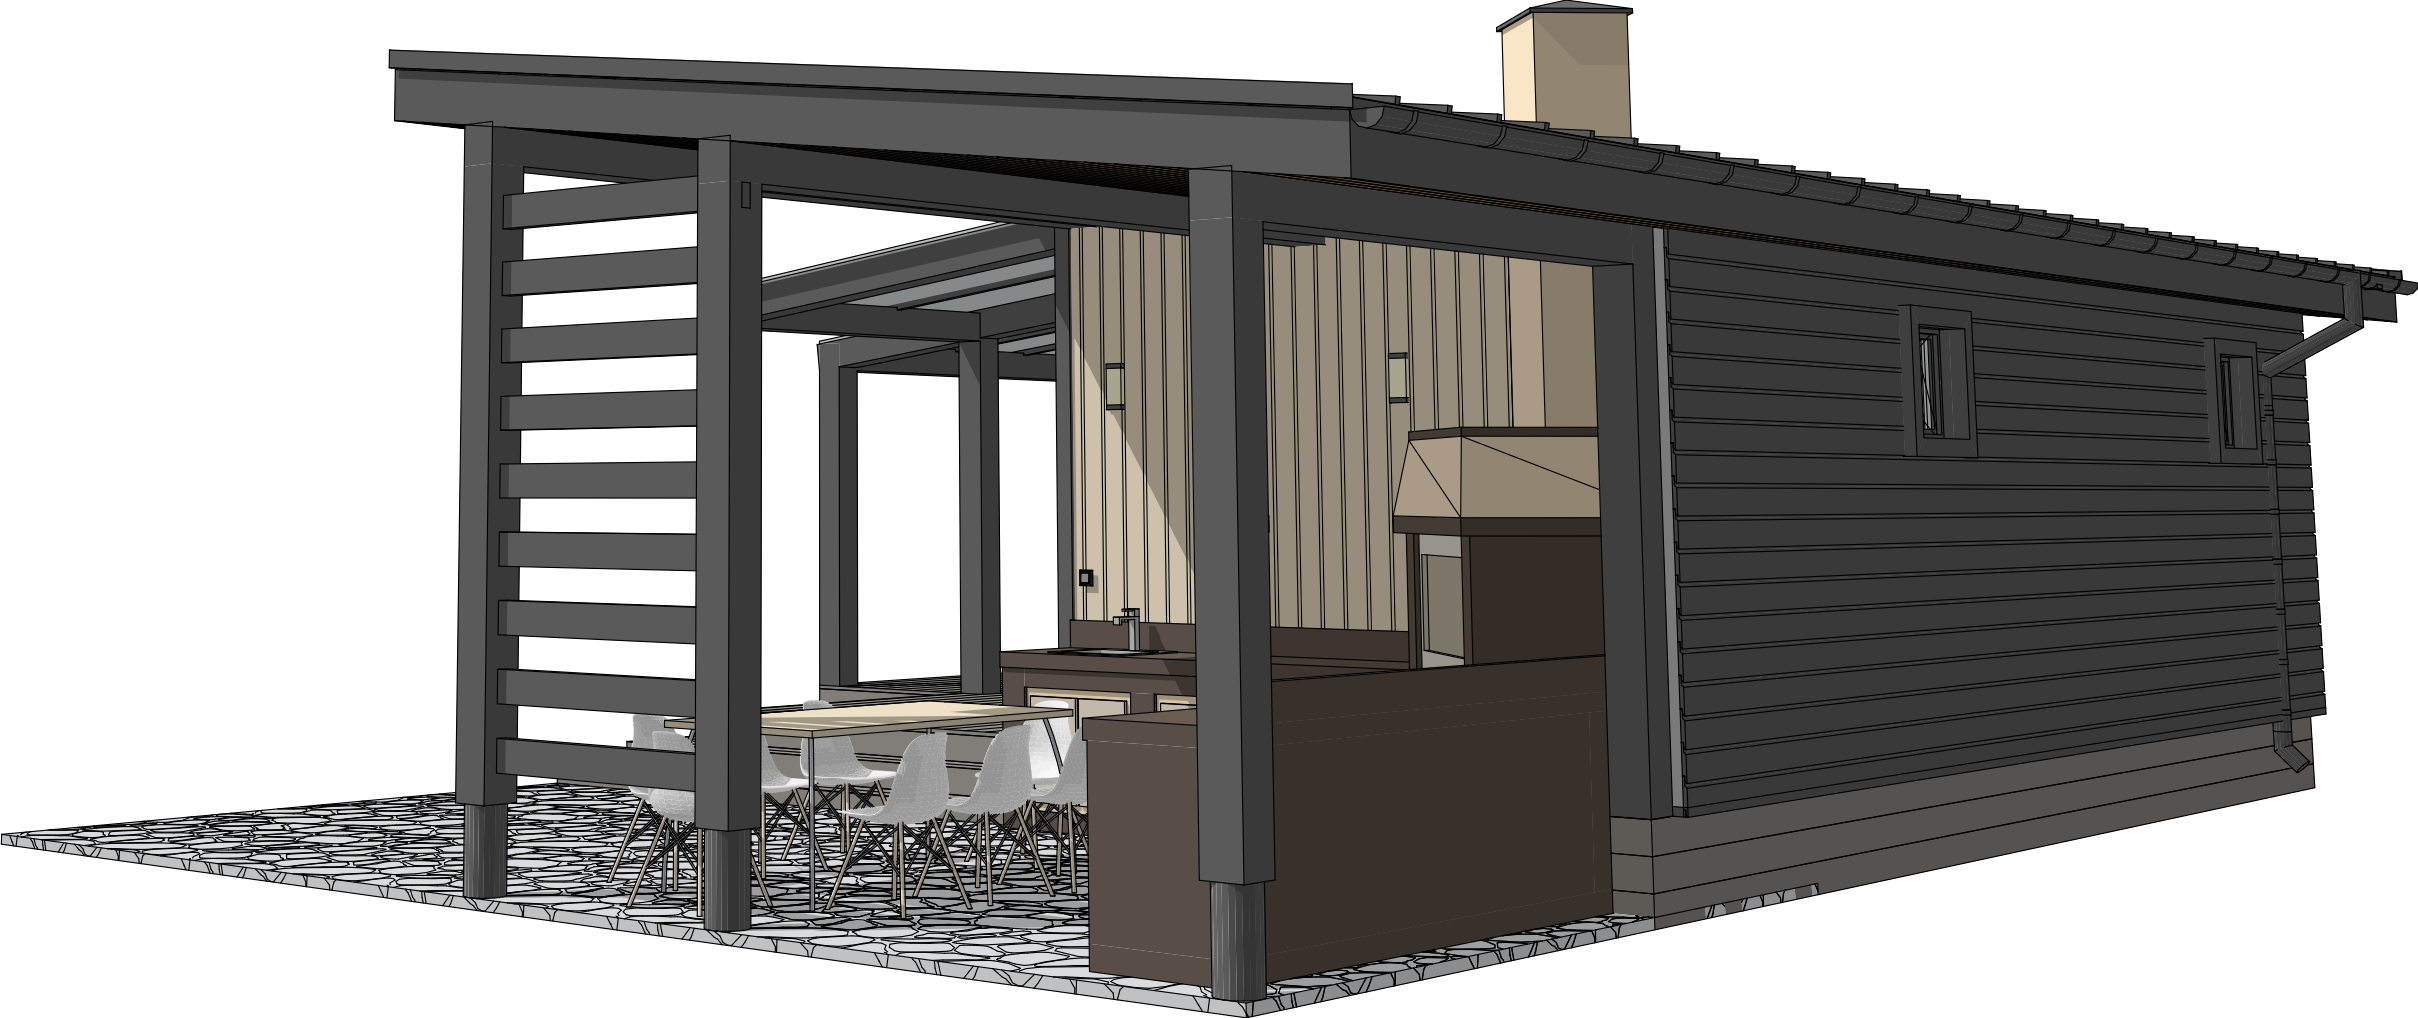

Инва. № подл. Подп. и дата Взам. инв. №

Лист	Изм.	№ Докум.	Подп.	Дата

Адрес:

Аксометрия №2

#Название Организации

Согласовано

Взам. инв. №

Подп. и дата

Инв. № подл.



Лист	Изм.	№ Докум.	Подп.	Дата

Адрес:

Визуализация №1

#Название Организации

Согласовано

Взам. инв. №

Подп. и дата

Инв. № подл.



Лист	Изм.	№ Докум.	Подп.	Дата

Адрес:

Визуализация №2

#Название Организации

Согласовано

Взам. инв. №

Подп. и дата

Инв. № подл.



Лист	Изм.	№ Докум.	Подп.	Дата

Адрес:

Визуализация №3

#Название Организации

Согласовано					
Инва. № подл.	Подп. и дата		Взам. инв. №		



Лист	Изм.	№ Докум.	Подп.	Дата

Адрес:

Визуализация №4

#Название Организации

Согласовано				

И-нв. № подл.	Подп. и дата	Взам. инв. №	



Лист	Изм.	№ Докум.	Подп.	Дата

Адрес:

Визуализация №5

#Название Организации

Согласовано

Взам. инв. №

Подп. и дата

Инв. № подл.



Лист	Изм.	№ Докум.	Подп.	Дата

Адрес:

Визуализация №6

#Название Организации