


ARCHITECTURE/
CONSTRUCTION

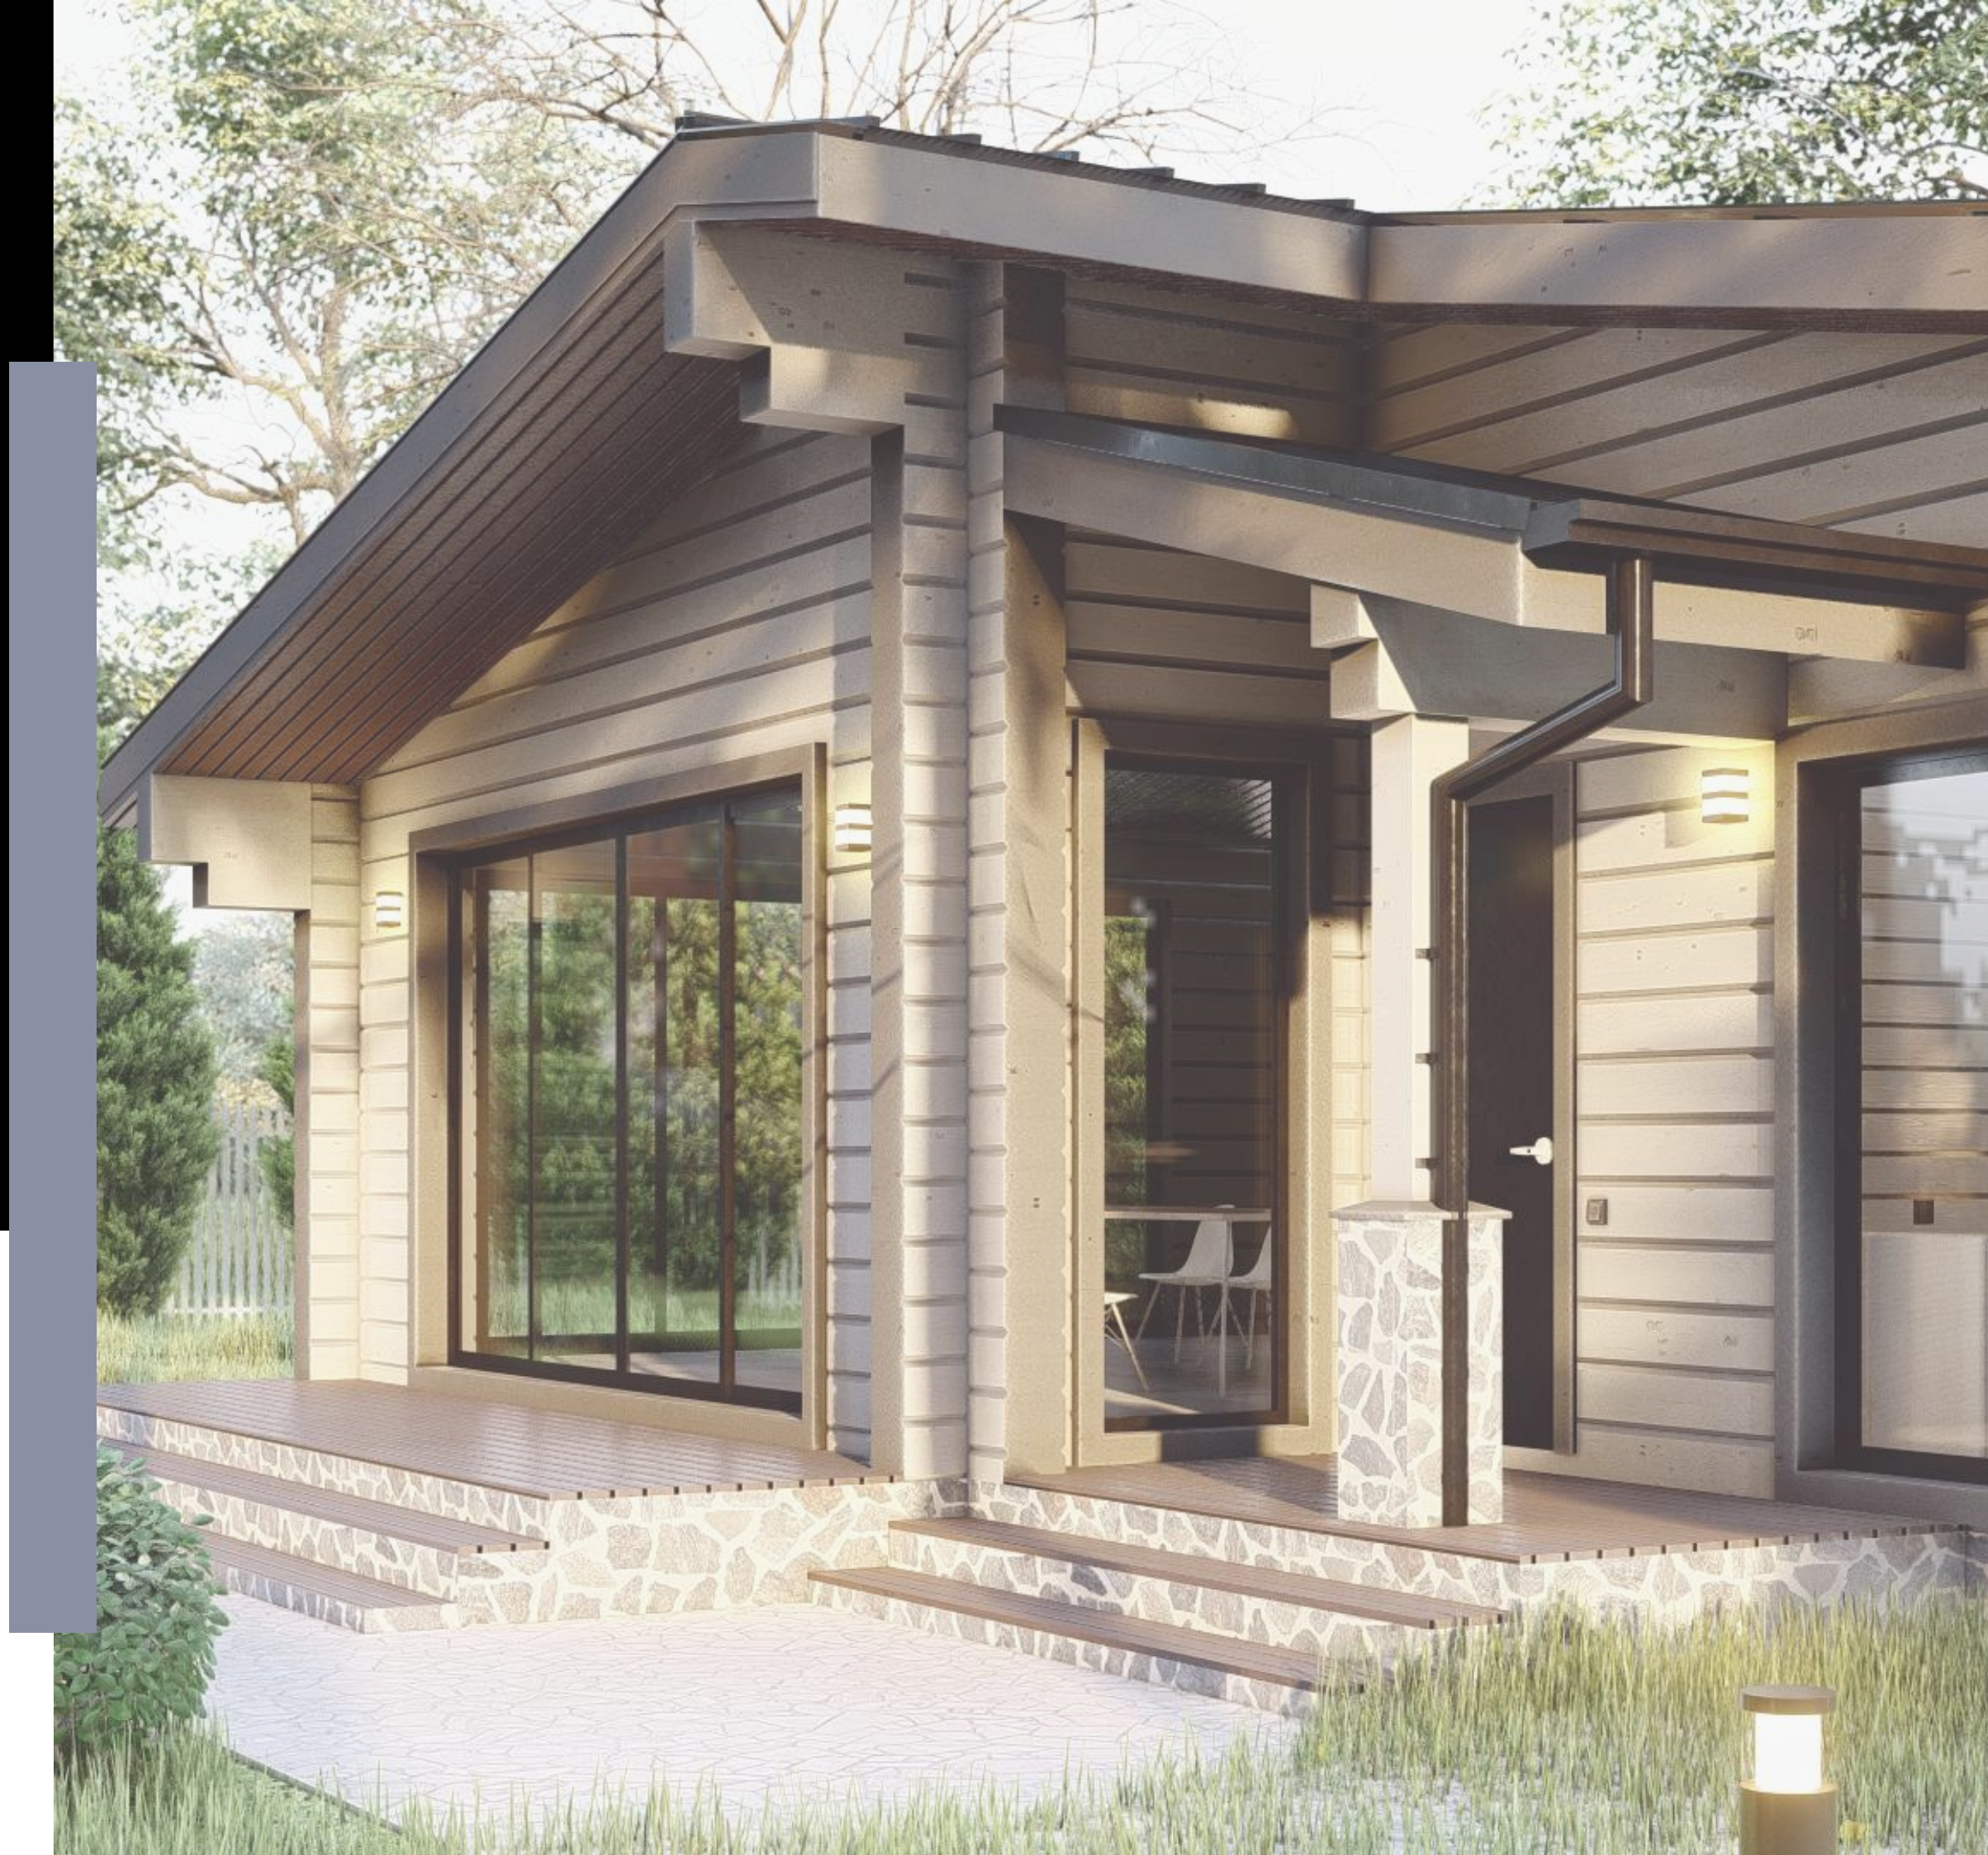

Название:
Разработал:
Принял:
г. Москва



1. Общие данные:

1.1. Архитектурный проект разработан на основании требований и пожеланий заказчика.

Тип строения	Баня
Относительная отм. ±0.000	ур. верха лаг деревянного перекрытия
Общая площадь застройки, м2	154,11
Габаритные размеры каркаса здания	12,04х14,6 м
Этажность	1 этаж
Конструктивная схема	Клееный брус

2. Конструктивные решения:

2.1. Рабочие чертежи разработаны на основании задания на проектирование

Полезная нагрузка на перекрытие	150 кгс/м2	-
Нормативная глубина промерзания	1,2м	СП 22.13330.2016 СП 131.13330.2020
Нормативное ветровое давление	I район (23кгс/м2)	СП 22.13330.2016
Нормативный вес снегового покрова	III район (150кгс/м2)	СП 22.13330.2016
Температура наиболее холодной пятидневки	-29°С	СП 131.13330.2020

2.2. Конструктивное строение представляет собой сооружение:

- на свайном фундаменте
- несущими стенами из деревянного каркаса
- вальмовой кровлей по деревянным стропилам

2.3. Необходимо осуществлять технический надзор за производством строительных работ. Данные по проведённым работам необходимо систематически вносить в журнал работ.

По каждому из этапов работ необходимо осуществлять входной контроль материалов и вести приёмку.

Фундамент	забивные сваи (150х150мм)
Несущие конструкции	клееный брус 240х200мм(h)
Стропильная система	строганая доска (190х45мм)
Тип крыши	Двускатная
Покрытие кровли	Фальц

2.4. Все деревянные конструкции обработать огне-биозащитными септиками в соответствии со СП 28.13330.2017 "Защита строительных конструкций от коррозии".

2.5. Кровельные работы выполнять в соответствии с требованиями фирмы производителя.

2.6. Все работы вести в строгом соответствии с требованиями СНиП 12.03.2001 "Безопасность труда в строительстве".

2.7. При выполнении всех работ строго соблюдать меры противопожарной безопасности.

2.8. Возможна замена материалов аналогами.

*Решения, принятые в проекте и отображенные в чертежах, соответствуют требованиям экологических, санитарно - гигиенических, противопожарных и других норм, действующих на территории Российской Федерации, и обеспечивают безопасную для жизни и здоровья людей эксплуатацию объекта при соблюдении предусмотренных рабочих чертежей и мероприятий.

Согласовано

Изм. № подл.

Подп. и дата

Взам. инв. №

Согласовано				
И-нв. № подл.	Подп. и дата	Взам. инв. №		

Лист	Наименование	Примечание
1	Пояснительная записка	
2	Ведомость чертежей	
3	Схема планировочной организации земельного участка	
4	Маркировочный план	
5	Размерный план	
6	План расстановки мебели и оборудования	
7	3д-разрез	
8	План электрического теплого пола	
9	План покрытий пола	
10	Экспликация покрытий пола	
11	План покрытия отделки стен	
12	Экспликация отделки стен	
13	План размещения розеток стен	
14	План расстановки светильников и выключателей	
15	План кровли бани	
16	План кровли террасы	
17	Разрез 1-1	
18	Разрез 2-2	
19	Ведомость оконных проёмов (начало)	
20	Ведомость оконных проёмов (окончание)	
21	Ведомость дверных проёмов	
22	Цветовое решение; Фасад в осях Г-А	
23	Цветовое решение; Фасад в осях З-1	
24	Аксометрия №1	
25	Цветовое решение; Фасад в осях А-Г	
26	Цветовое решение; Фасад в осях 1-3	
27	Аксометрия №2	
28	Визуализация №1	
29	Визуализация №2	
30	Визуализация №3	
31	Визуализация №4	

Лист	Изм.	№ Докум.	Подп.	Дата	Адрес:	Ведомость чертежей	#Название Организации	Лист
								2

Лист	Наименование	Примечание
32	Визуализация №5	
33	Визуализация №6	

В основу архитектурно-планировочных решений положены требования технологических заданий и требования норм и правил строительного проектирования, действующих на территории РФ.

Основные параметры и требования разработаны на основании пожеланий и требований заказчика.


- Архитектурные решения приняты в соответствии со следующими нормативными документами:
- Градостроительный кодекс российской федерации.
 - Земельного Кодекса Российской Федерации.
 - Федеральный закон от 22.07.2008 N 123 - ФЗ (ред. от 29.07.2017)"Технический регламент о требованиях пожарной безопасности.
 - Федеральный закон № 384 - ФЗ «Технический регламент о безопасности зданий и сооружений».
 - ГОСТ Р 21.1101-2013. «Основные требования к проектной и рабочей документации».
 - Постановление правительства РФ от 16.02.2008 № 87 «Положение о составе разделов проектной документации и требованиях к их содержанию».
 - СП 42.13330.2011 «Градостроительство. Планировка и застройка городских и сельских поселений».
 - СП 131.13330.2018 «СНиП 23-01-99* Строительная климатология».
 - СП 20.13330.2016 «СНиП 2.01.07-85* Нагрузки и воздействия».
 - СП 22.13330.2016 «СНиП 2.02.01-83* Основания зданий и сооружений».
 - СП 70.13330.2012 (с изменениями №1) «СНиП 3.03.01-87 Несущие и ограждающие конструкции».
 - СП 64.13330.2017 «СНиП II-25-80 Деревянные конструкции».
 - СП 17.13330.2017 «СНиП II-26-76 Кровли».
 - СП 29.13330.2011 «СНиП 2.03.13-88 Полы».
 - СП 28.13330.2017 «СНиП 2.03.11-85 Защита строительных конструкций от коррозии».
 - СП 50.13330.2012 «СНиП 23-02-2003 Тепловая защита зданий».

1:350

2 - Банный комплекс


Площадь застройки (баня)	154,11
--------------------------	--------

ИНВ. № подл.

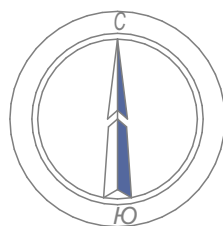

3

1:75

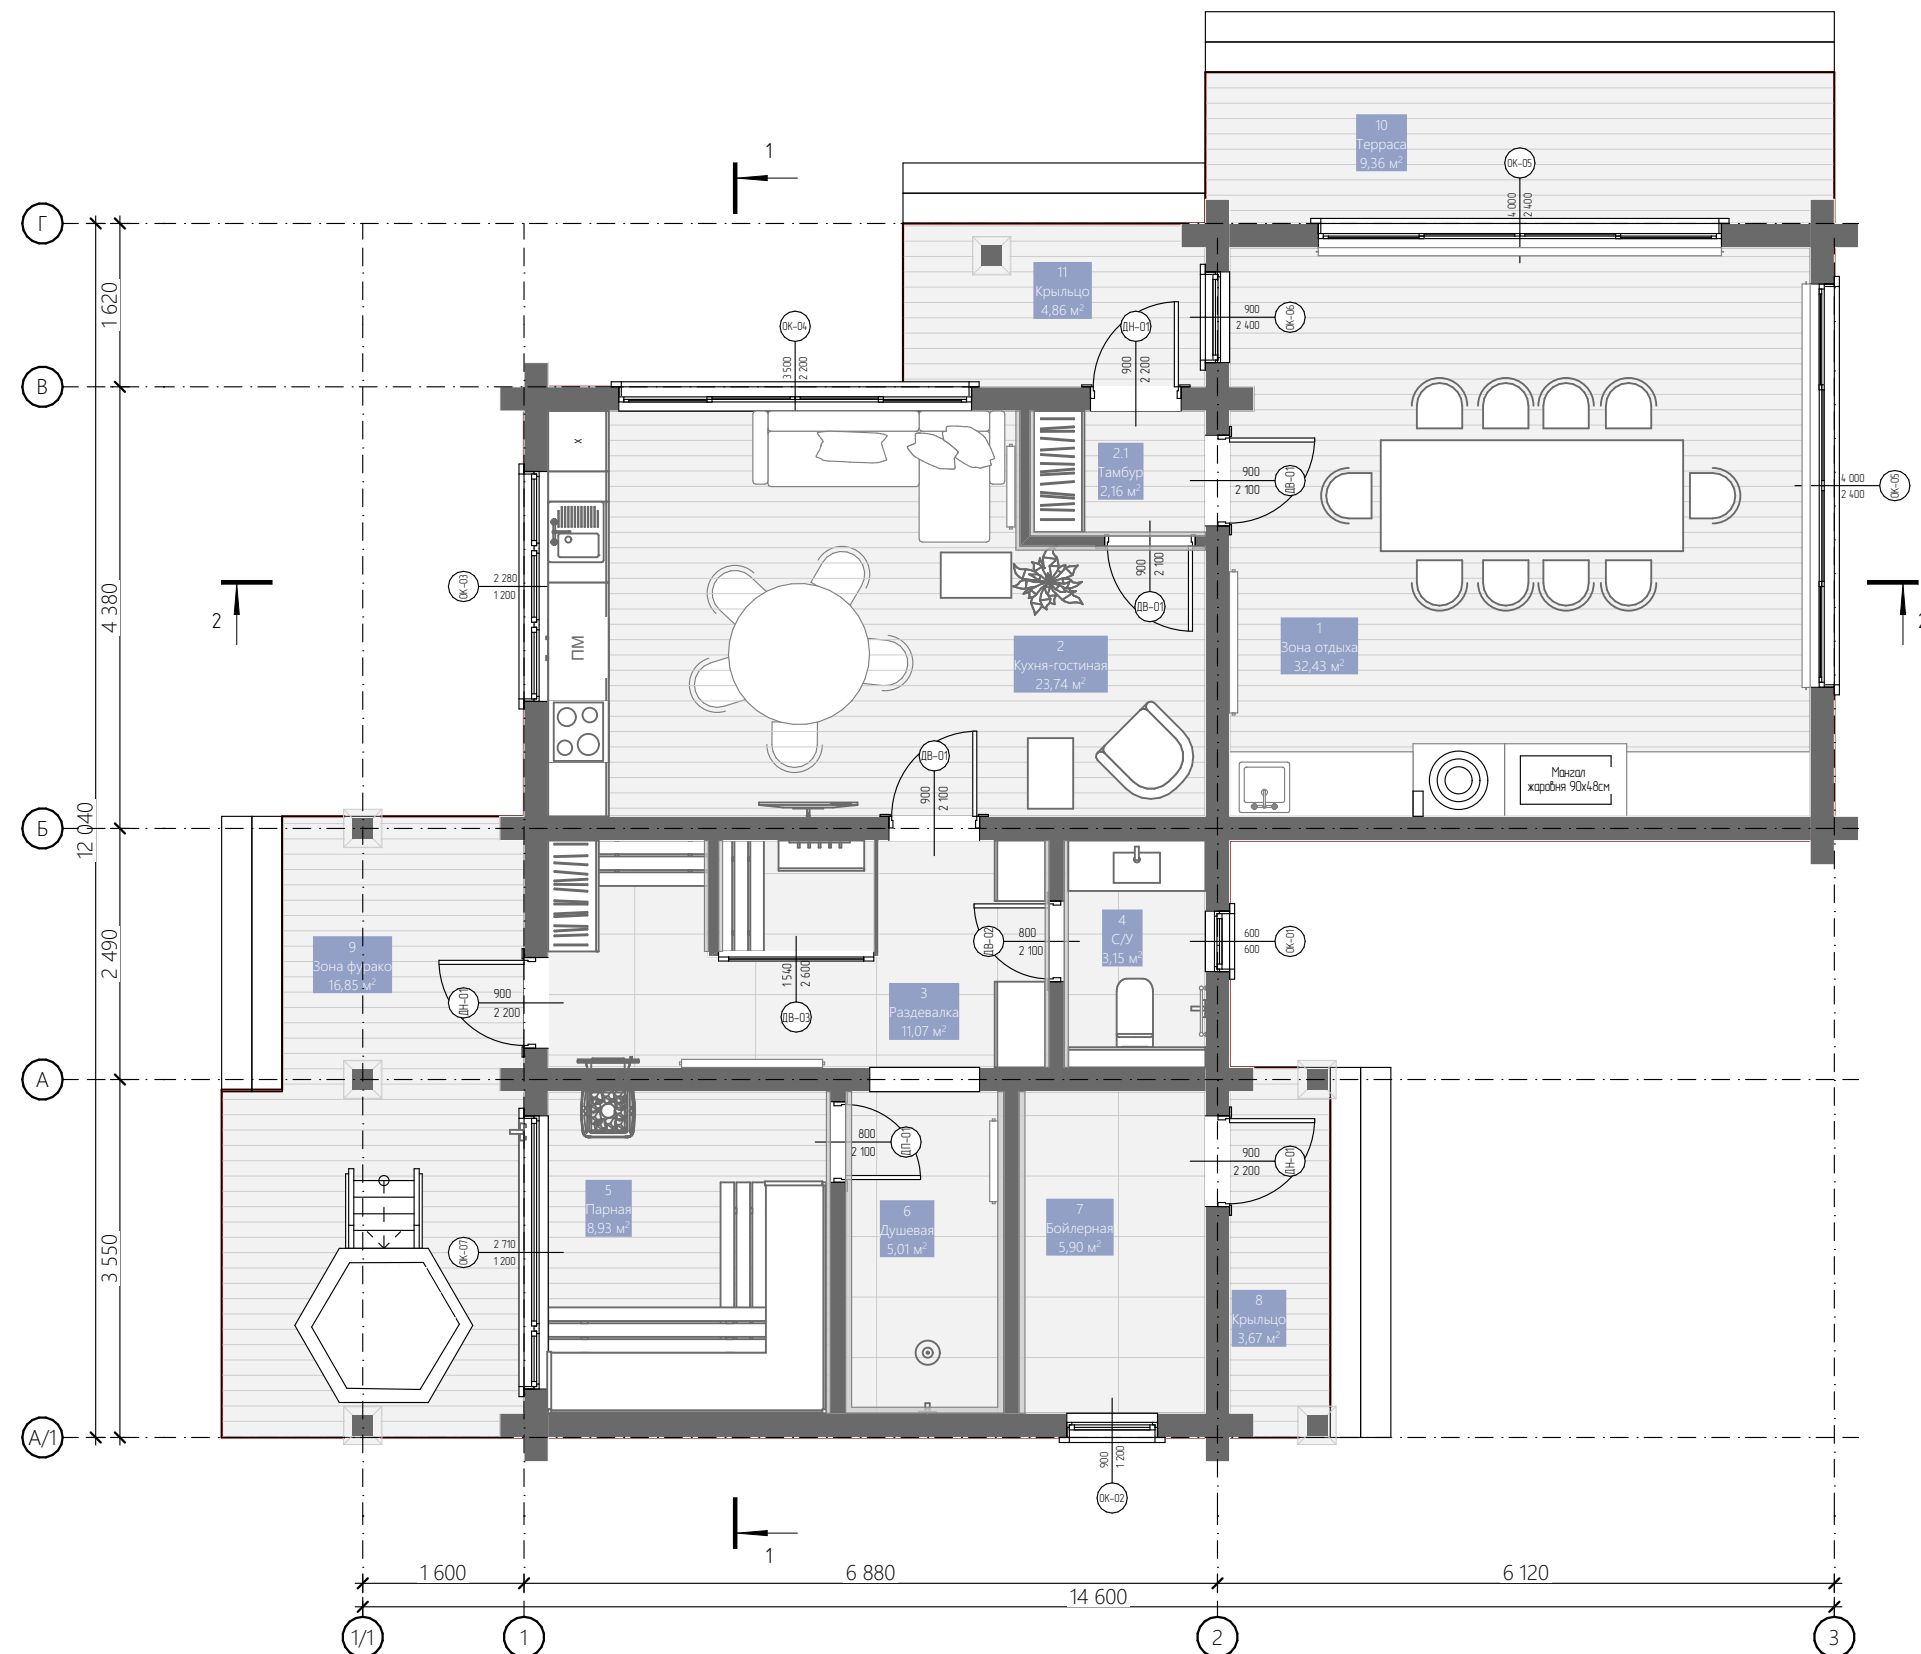


Экспликация помещений		
№	Наименование	Площадь, кв. м.
1	Зона отдыха	32,43
2	Кухня-гостиная	23,74
2.1	Тамбур	2,16
3	Раздевалка	11,07
4	С/У	3,15
5	Парная	8,93
6	Душевая	5,01
7	Бойлерная	5,90
8	Крыльцо	3,67
9	Зона фурако	16,85
10	Терраса	9,36
11	Крыльцо	4,86
		127,13 м ²
Наименование		Площадь, кв. м.
Площадь застройки		144,79
<u>Примечание:</u>		
1. Вся индивидуальная мебель выполняется по отдельному проекту с детальной проработкой и калькуляцией. Чертежи предоставляет фирма-изготовитель столярных изделий.		
2. Данный проект отдельно согласовывается с автором проекта и непосредственно с заказчиком.		
3. Цветовое решение фасада и материалов отделки показаны в проекте приблизительно.		
4. Количество ступеней показано условно.		
#Название Организации		Лист
		4

	Инв. № подл.	Подп. и дата	Взам. инв. №	Согласовано		

Размерный план

1:75

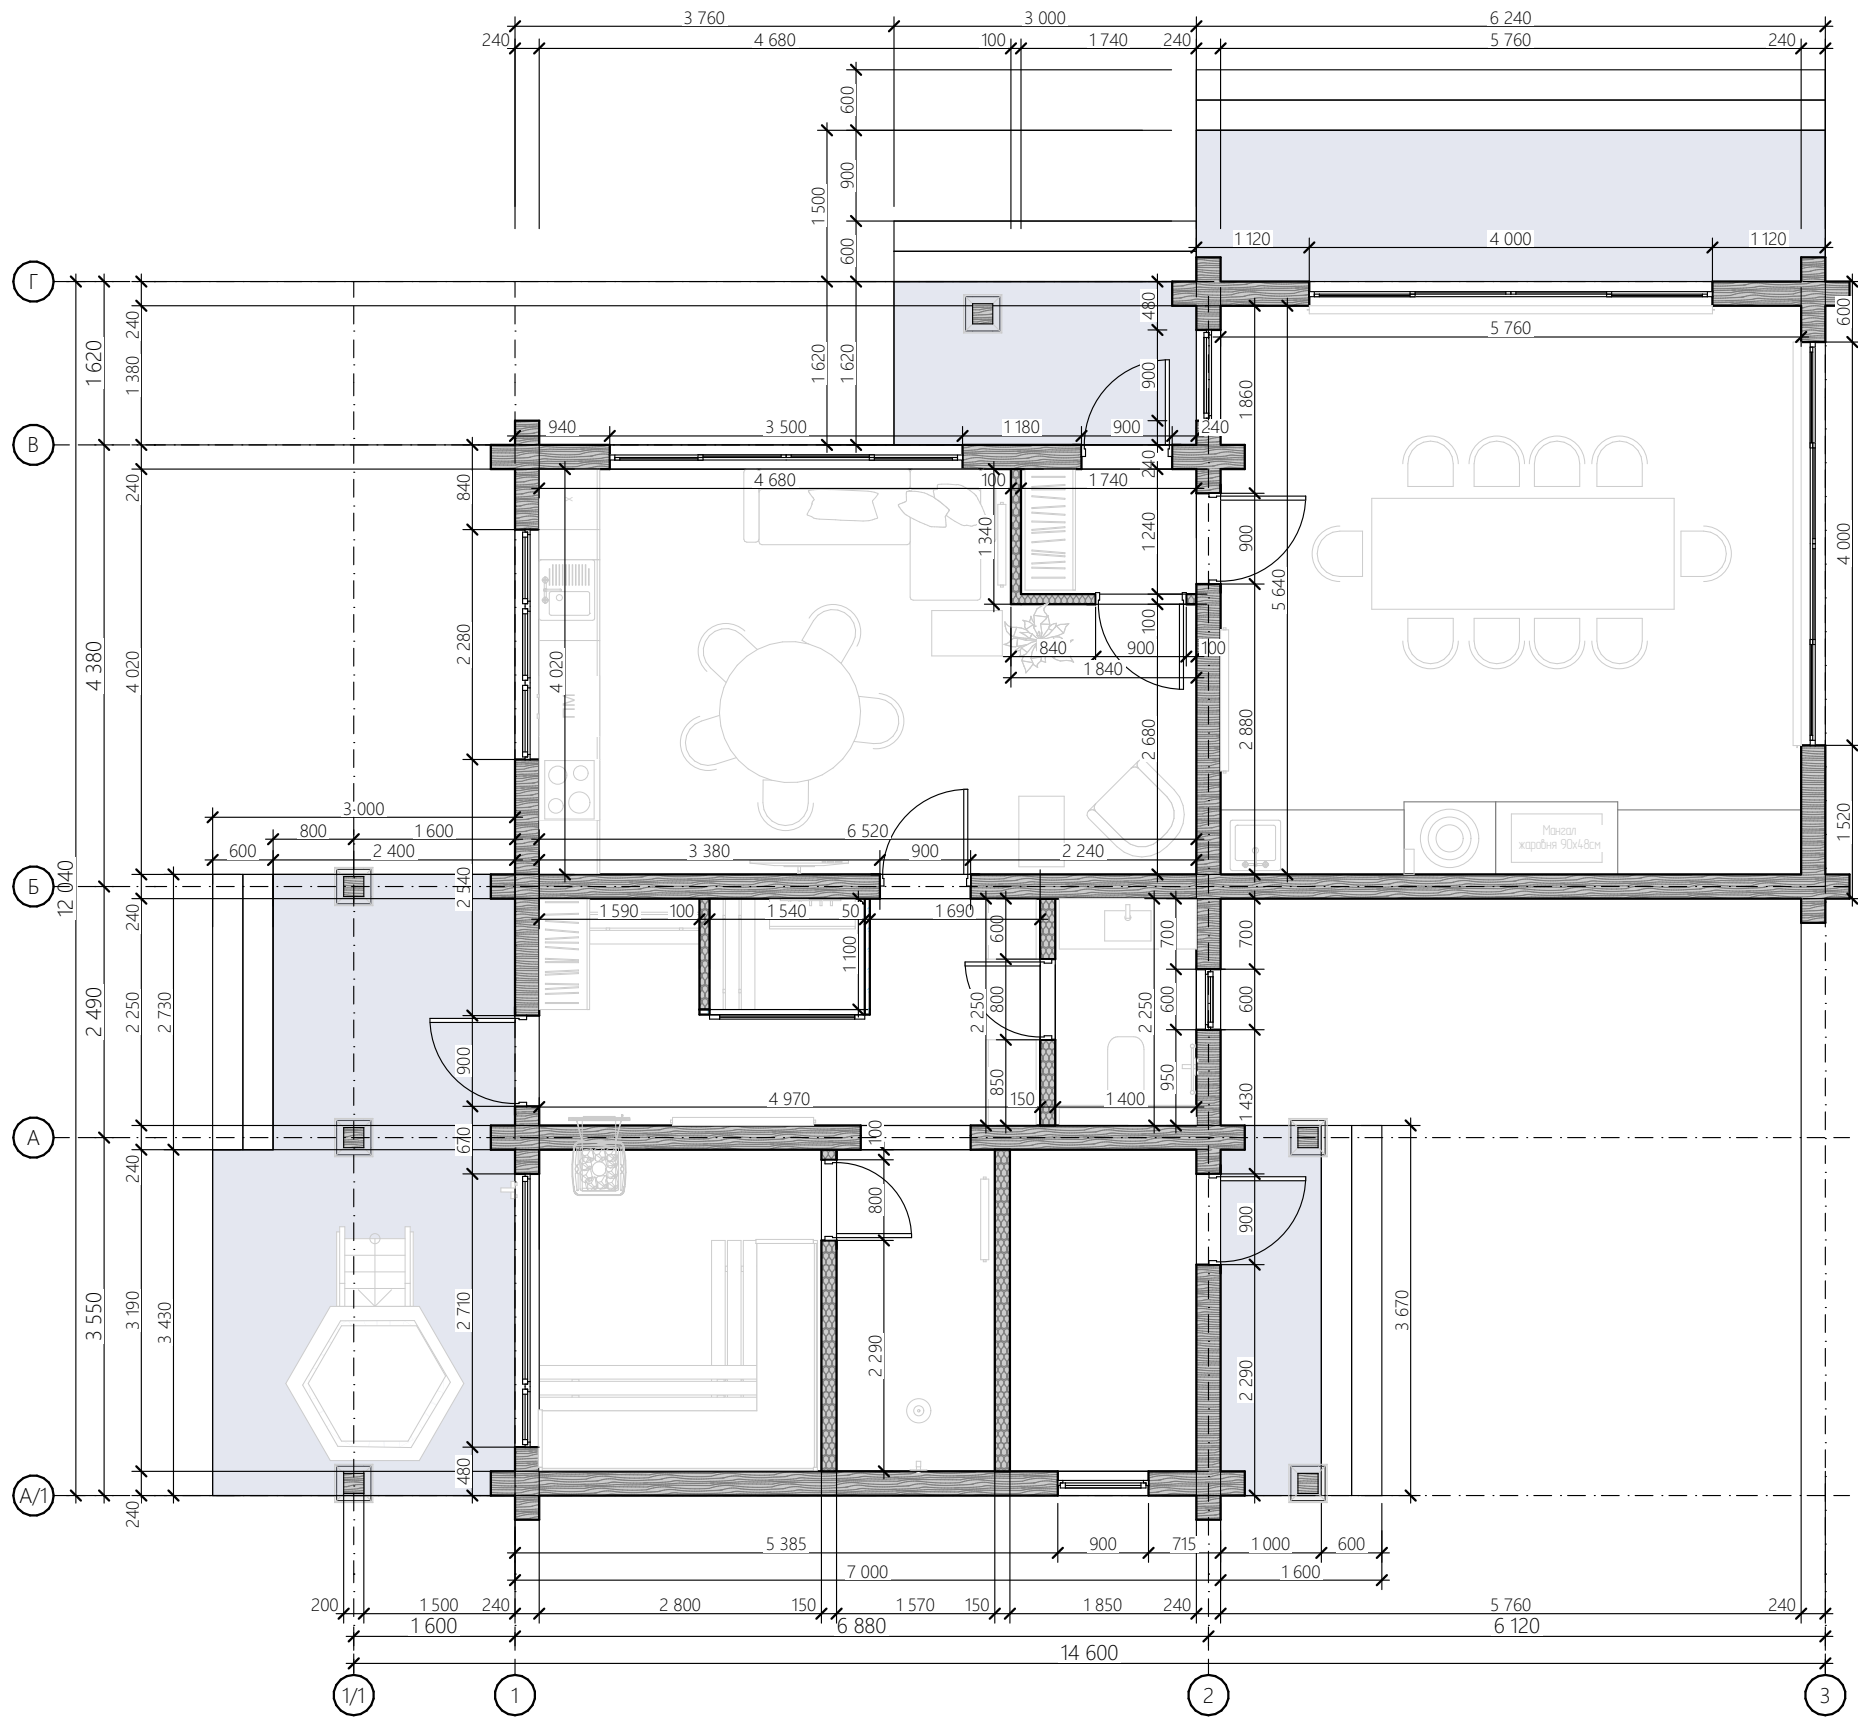

Примечание:
1. Представленные размеры
указаны без учета внешней и
внутренней отделки


Согласовано					
И-нв. № подл.	Подп. и дата	Взам. инв. №			

Лист	Изм.	№ Докум.	Подп.	Дата

Адрес:

Размерный план

#Название Организации

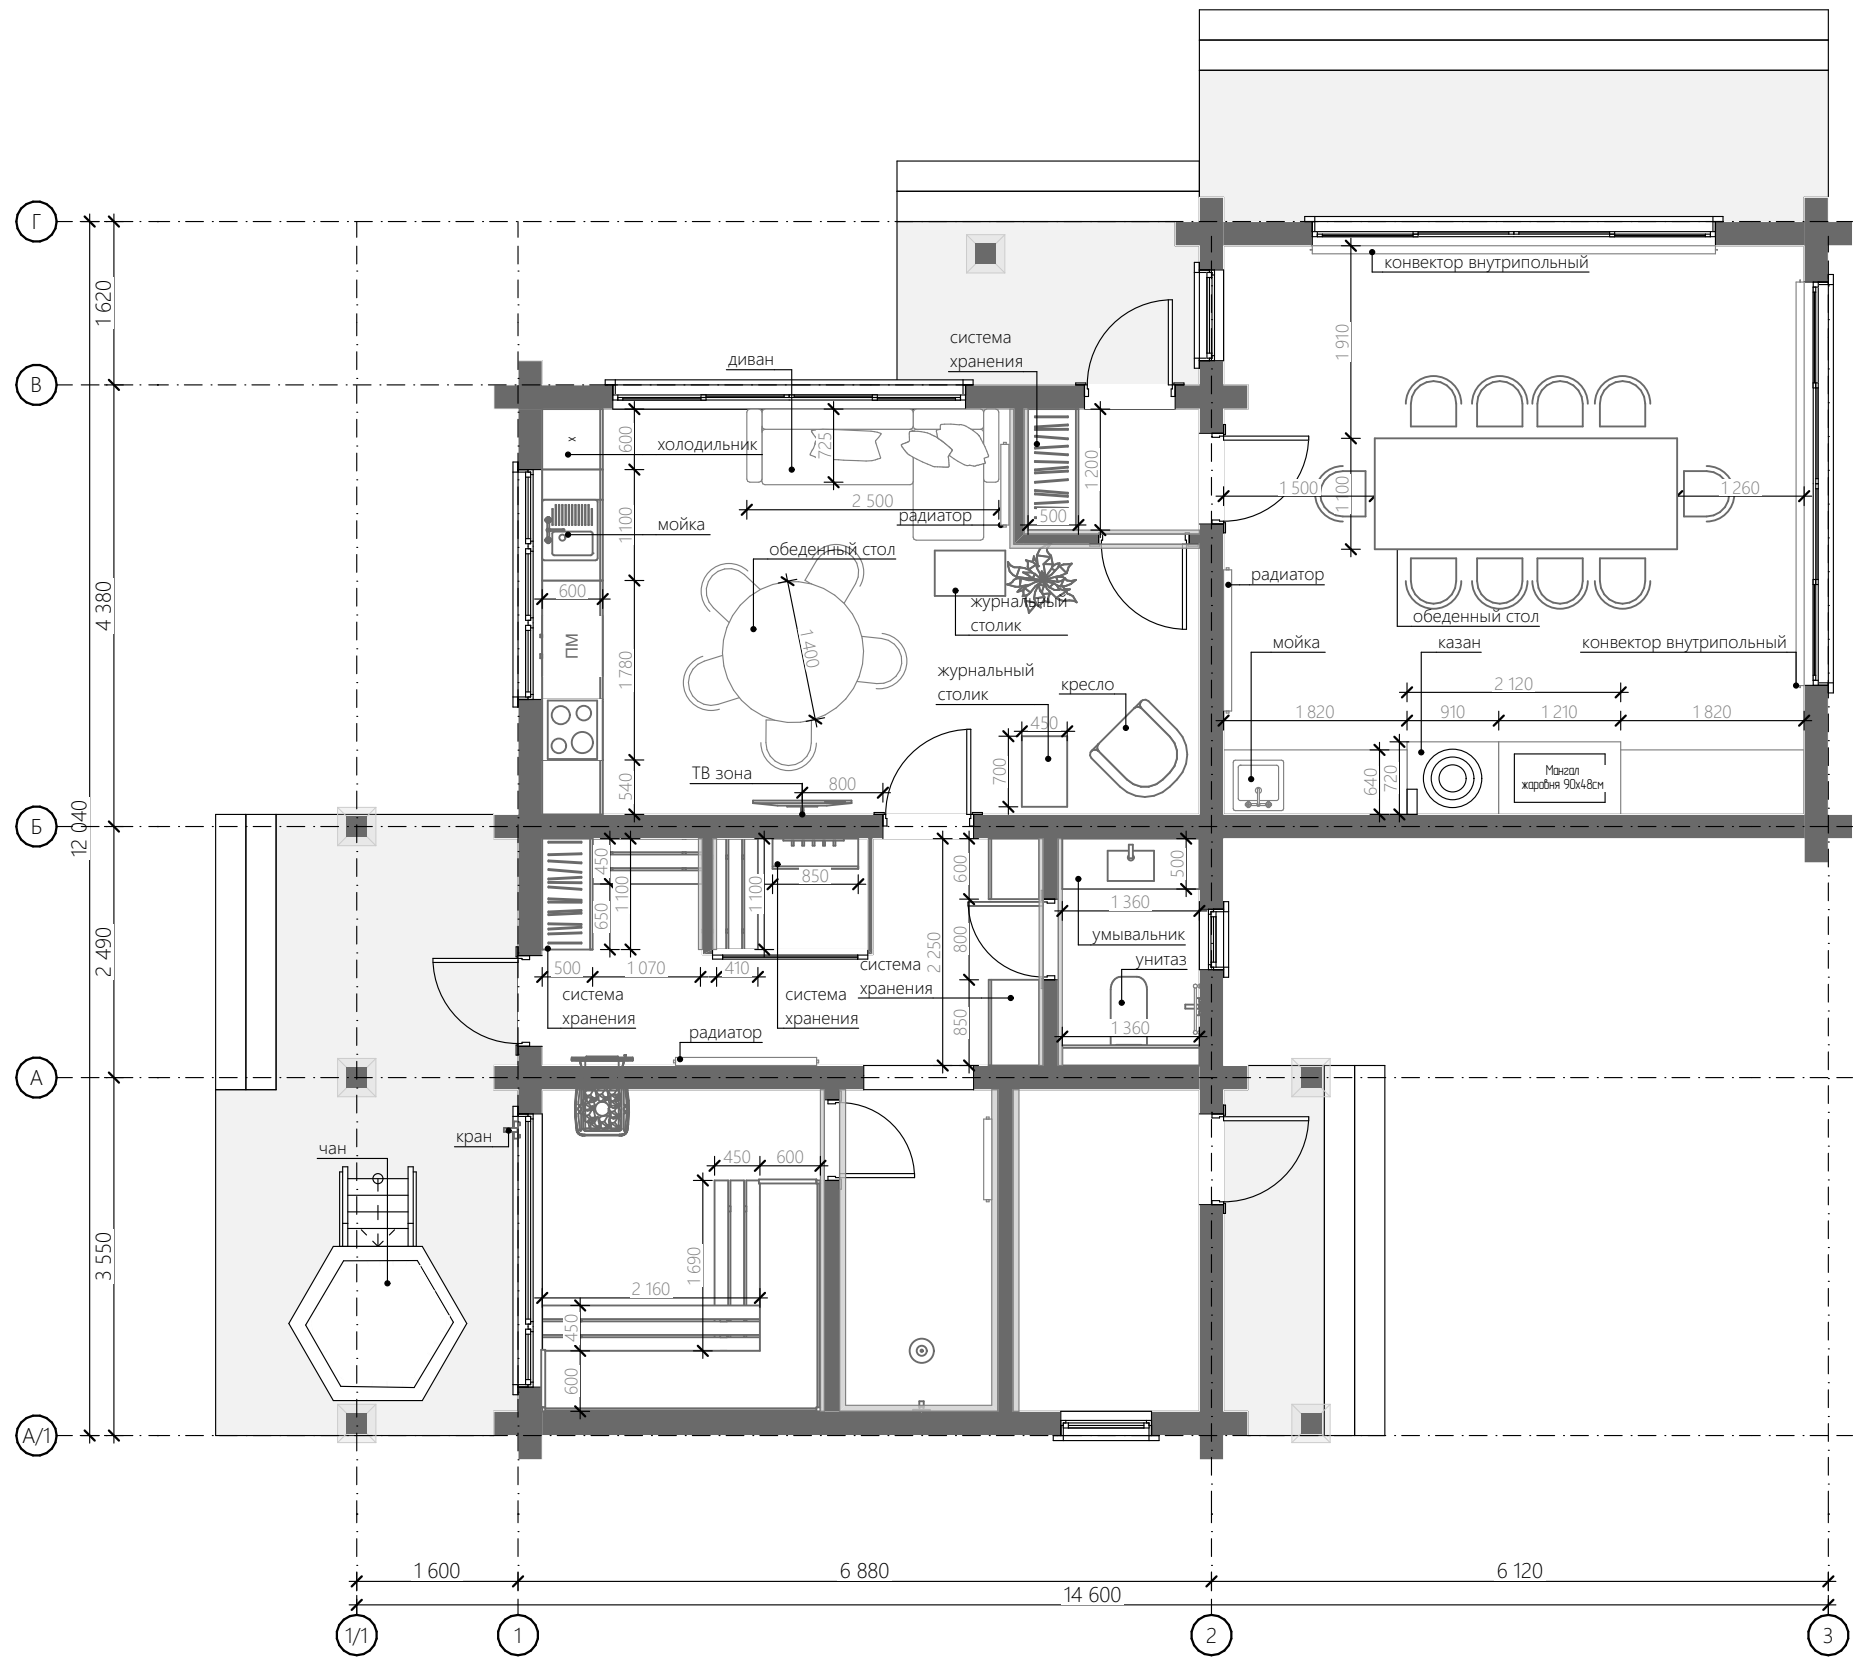

Примечание:

1. Вся индивидуальная мебель выполняется по отдельному проекту с детальной проработкой и калькуляцией. Чертежи предоставляет фирма-изготовитель столярных изделий.

2. Финальные размеры мебели и оборудования указаны ориентировочно — для точной компоновки требуется разработка дизайн-проекта.

Согласовано				
Взам. инв. №				
Подп. и дата				
Инв. № подл.				

Лист	Изм.	№ Докум.	Подп.	Дата

Адрес: _____

План расстановки мебели и оборудования


#Название Организации

Согласовано

Взам. инв. №

Подп. и дата

Инв. № подл.

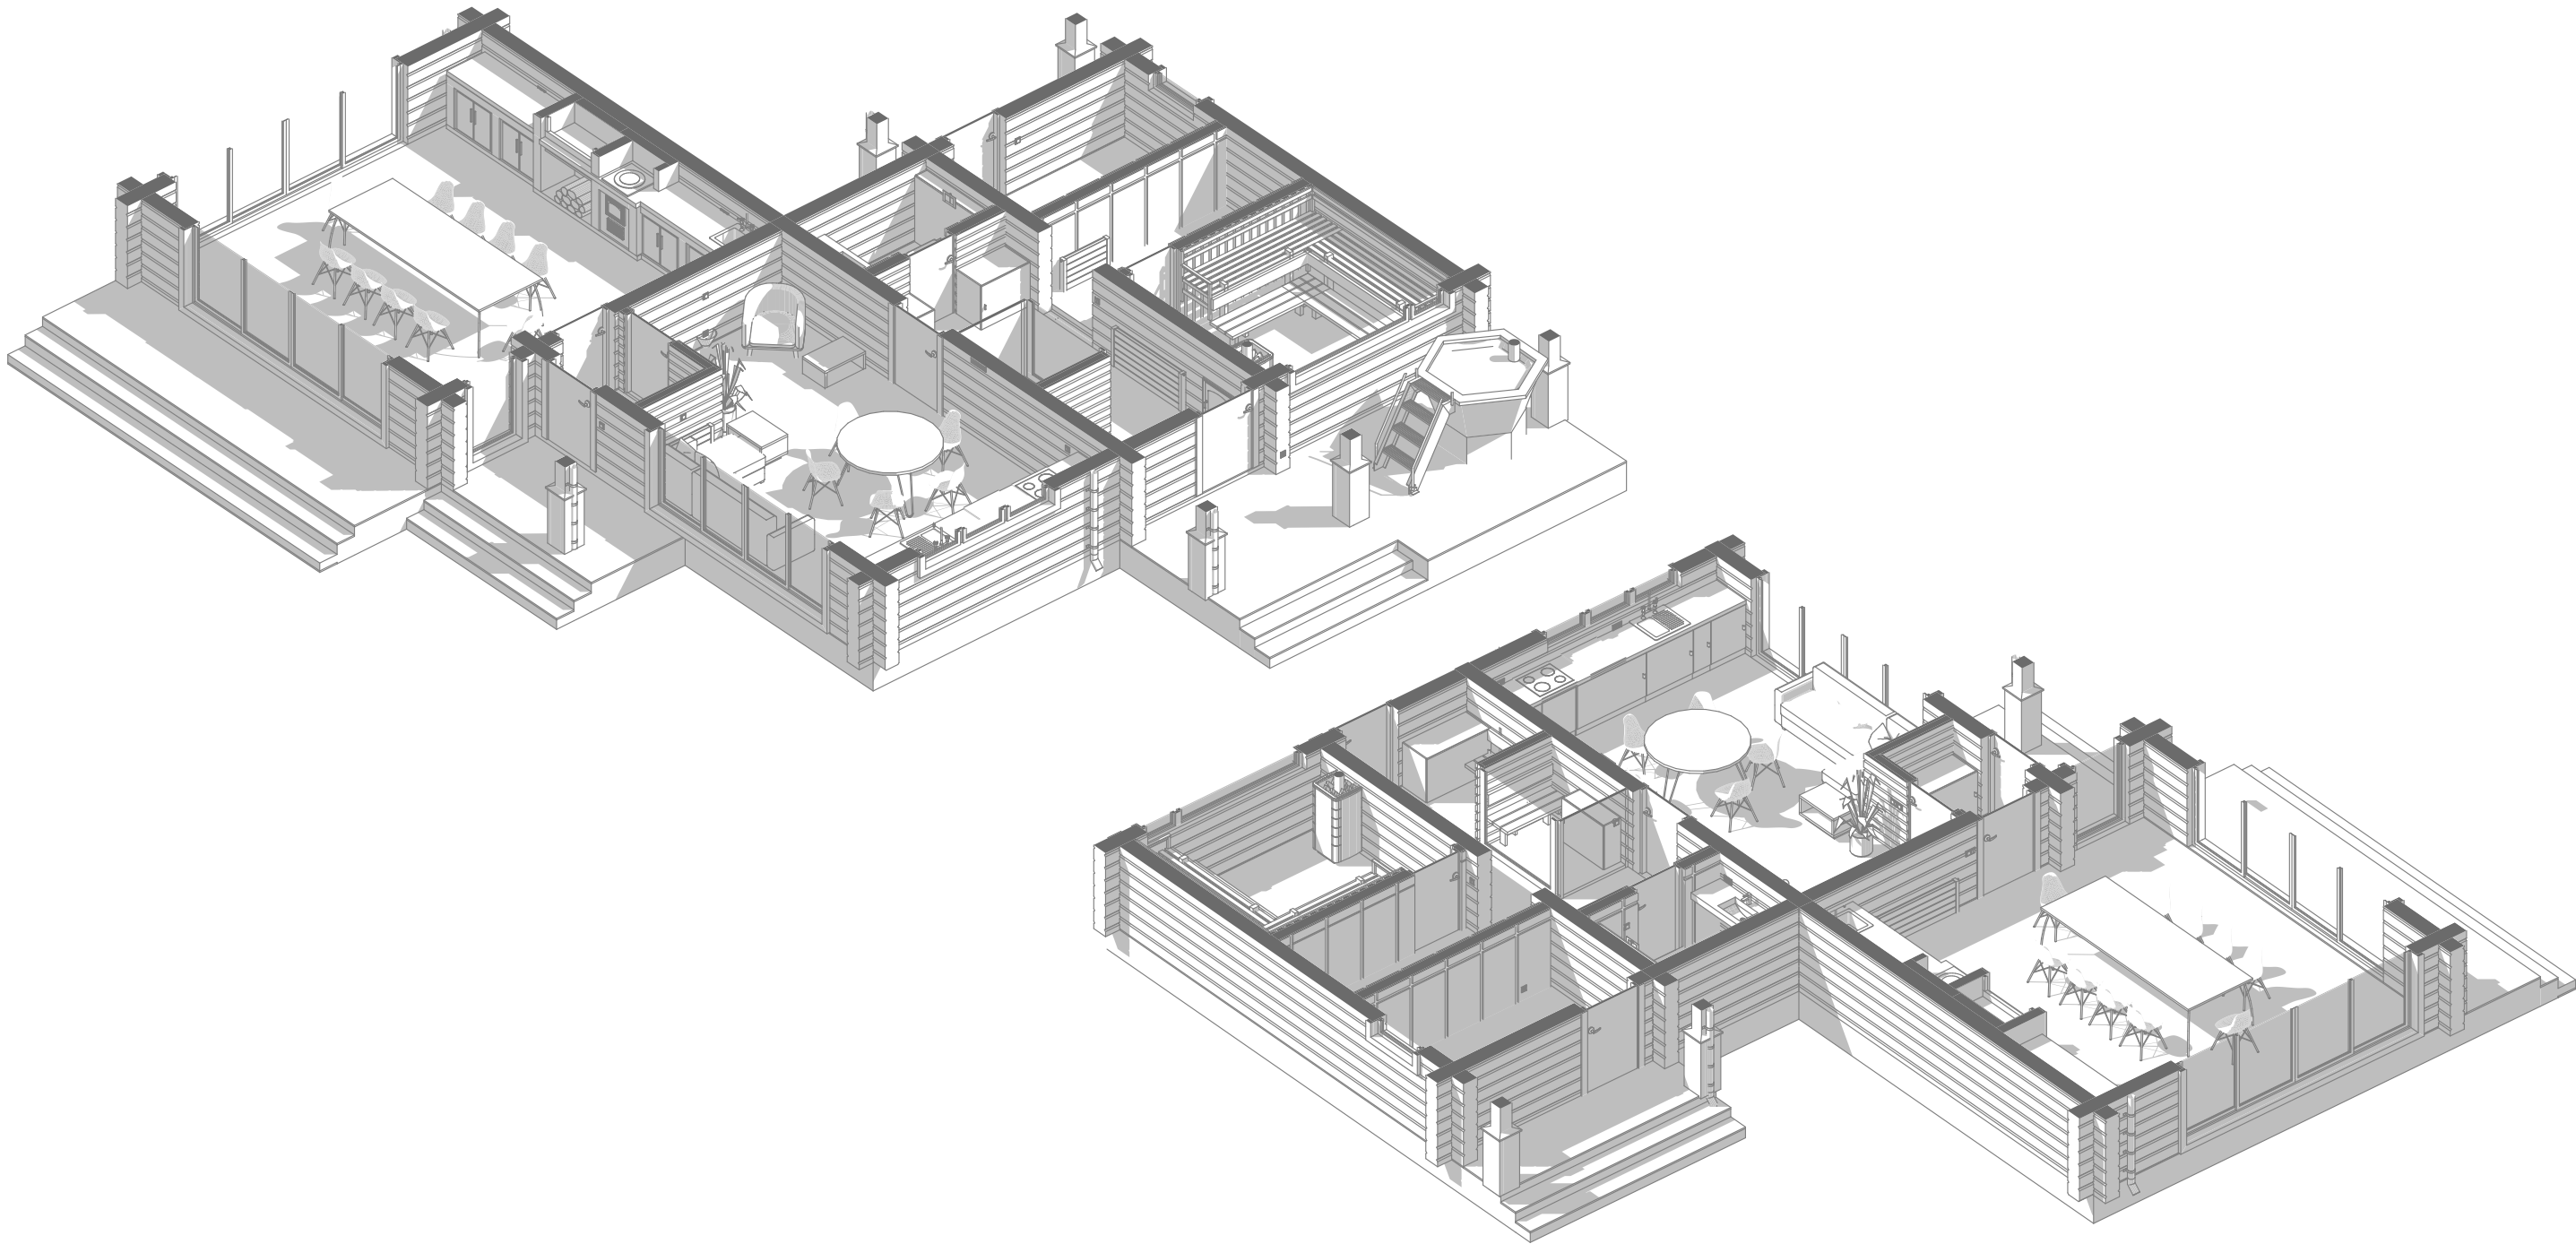


Лист	Изм.	№ Докум.	Подп.	Дата


Адрес:

Зд-разрез

#Название Организации

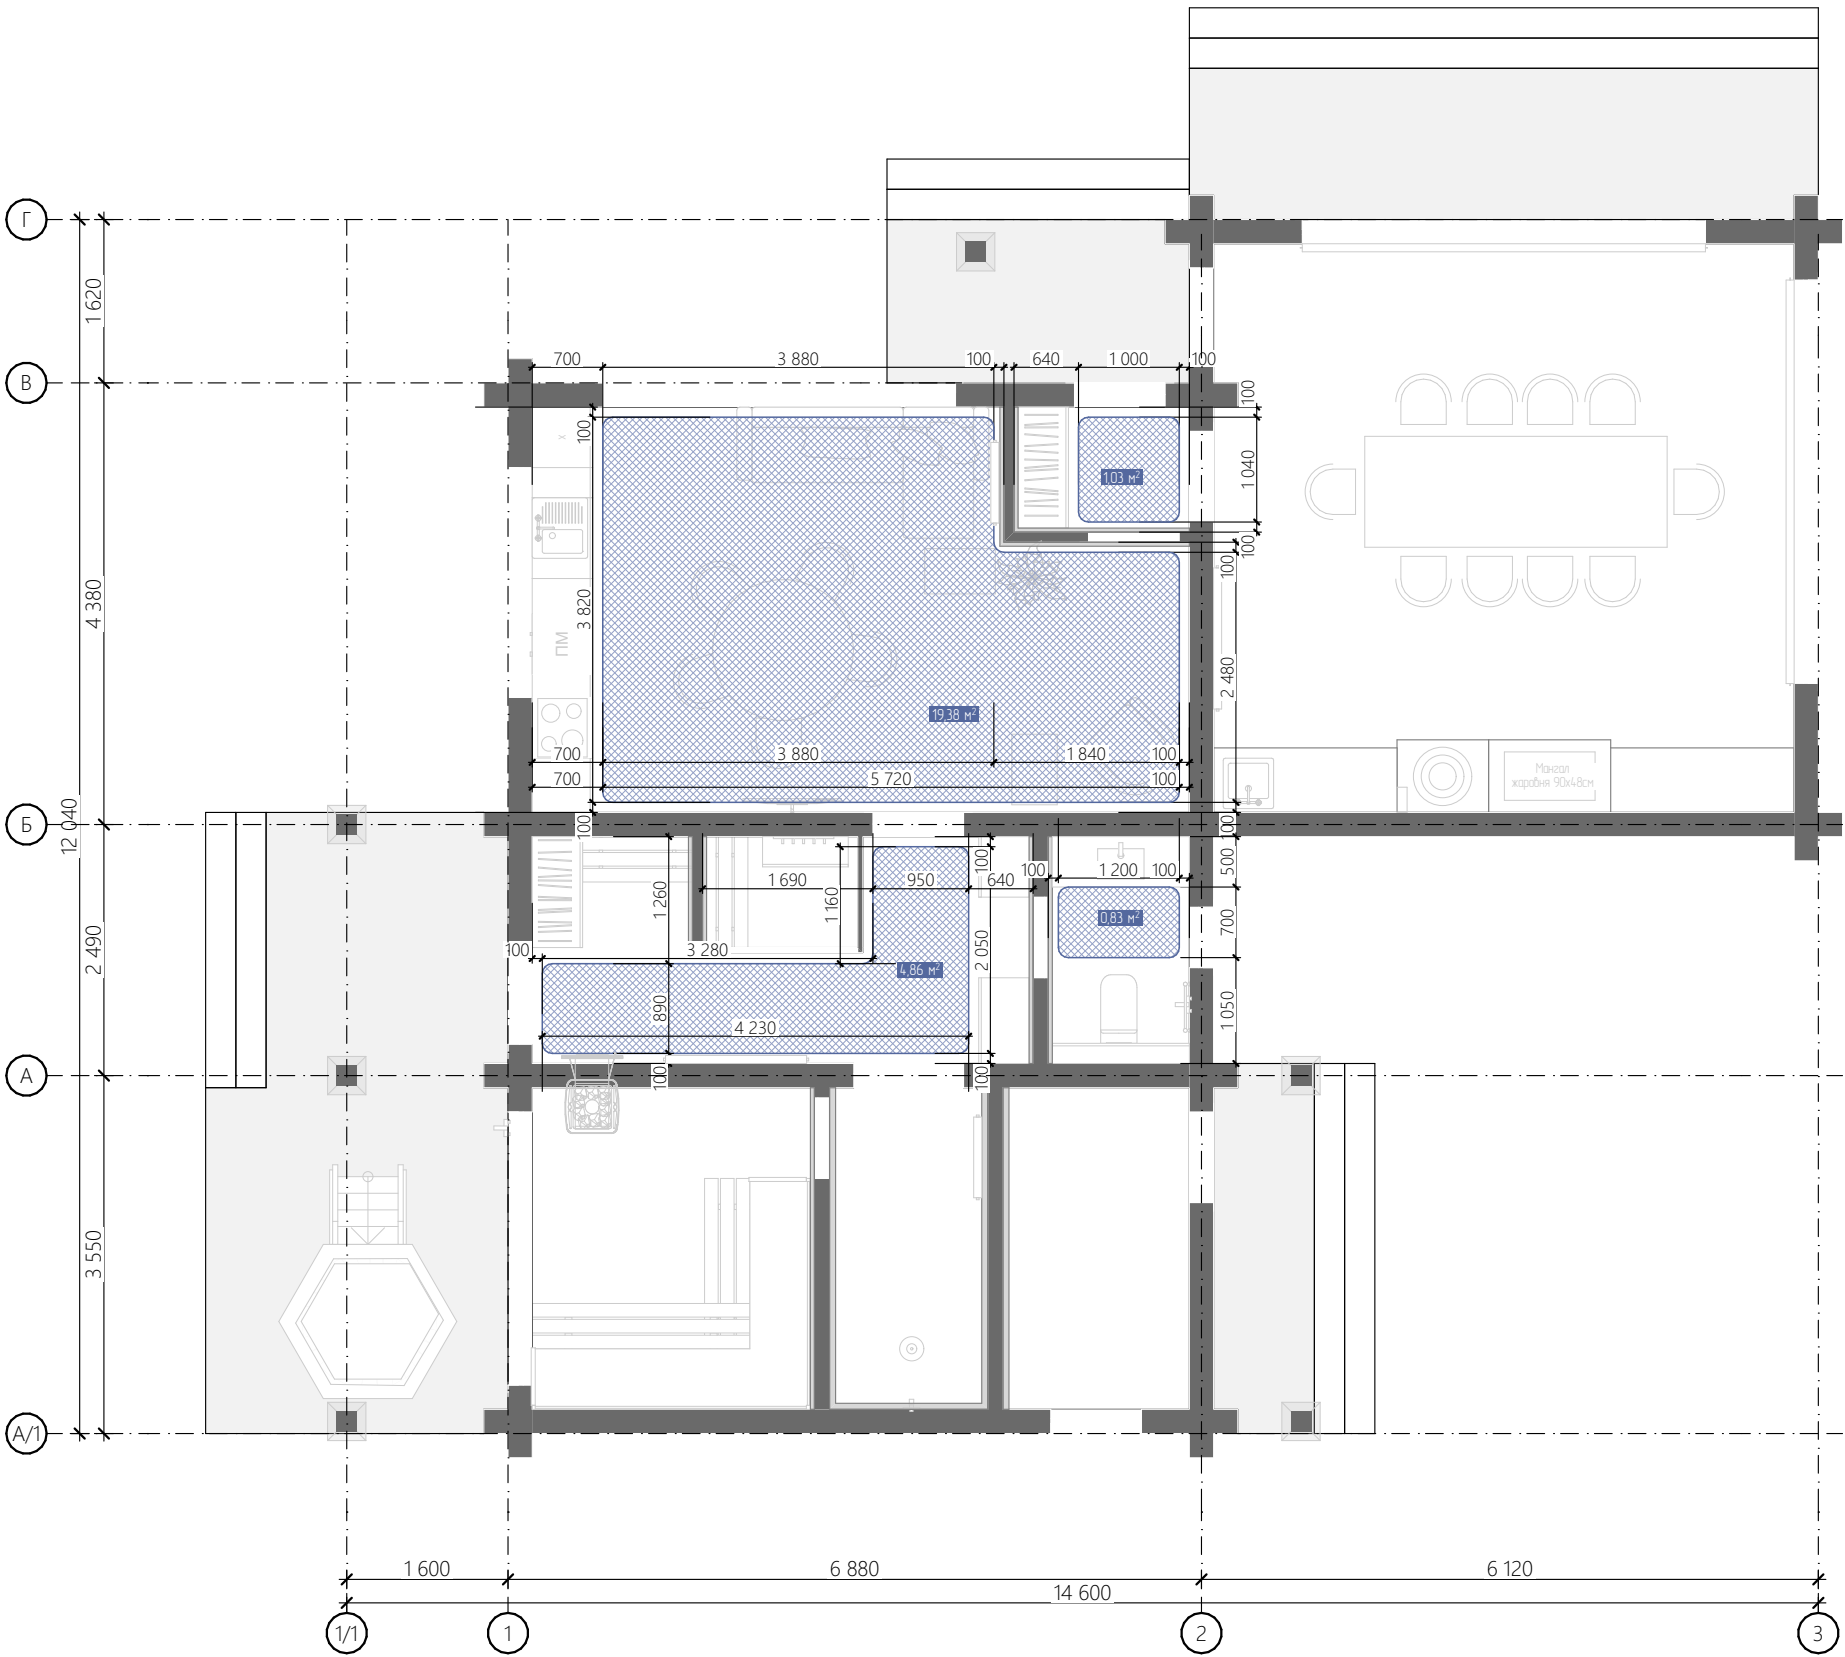

Условные обозначения

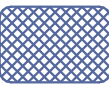 - Контур устройства
теплого пола

Экспликация теплого пола

Наименование зоны	Площадь, м2
Кухня-гостиная	19,38
Прихожая	1,03
Раздевалка	4,86
С/У	0,83
26,10 м²	

Примечание:

1. Отображение носит схематичный характер. Фактическая реализация выполняется в соответствии с детальными проектными решениями инженерных сетей.

Согласовано

Взам. инв. №

Подп. и дата

Инв. № подл.

Лист	Изм.	№ Докум.	Подп.	Дата


Адрес:

План электрического теплого
пола

#Название Организации



Условные обозначения

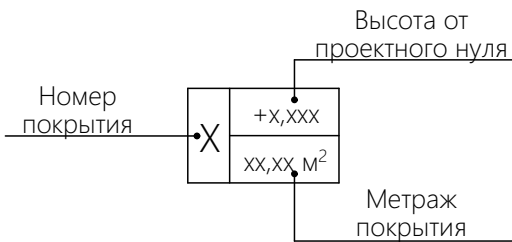

Ведомость покрытий пола

№	Наименование	м2
1	ДПК- террасная доска	34,01
2	ламинат	56,23
3	керамогранит	36,48

Примечание:

1. Приведённые цветовые решения носят рекомендательный характер. Фактический подбор оттенков и материалов выполняется на этапе реализации с учётом наличия продукции у поставщиков и утверждения заказчиком.

2. Пирог покрытия смотреть на след. листе.

Согласовано				
Взам. инв. №				
Подп. и дата				
Инв. № подл.				




Лист	Изм.	№ Докум.	Подп.	Дата

Адрес:

План покрытий пола

#Название Организации


Экспликация покрытий пола

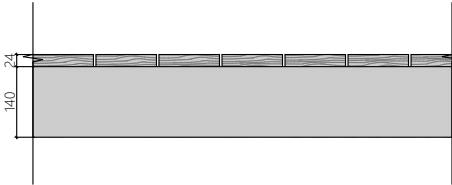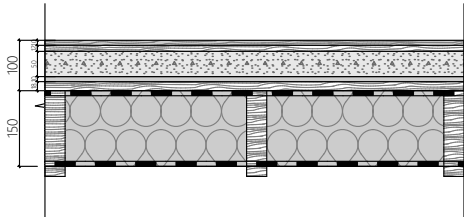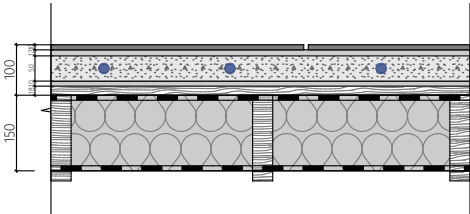№	Наименование	Разрез	Состав
1	Террасная доска		-Террасная доска 24мм -Лага, доска 140х45мм 140 мм
2	Ламинат		-Ламинат 10мм -Подложка под ламинат 10мм -Полусухая цементно-песчаная стяжка (с устройством теплого водяного пола) 50мм -ЦСП 10мм -ОСБ 18мм
3	Керамогранит		-Керамогранит 10мм -Клей 10мм -Полусухая цементно-песчаная стяжка (с устройством теплого водяного пола) 50мм -ЦСП 10мм -ОСБ 18мм

Согласовано			

Инв. № подл.	Подп. и дата	Взам. инв. №

Лист	Изм.	№ Докум.	Подп.	Дата	Экспликация покрытий пола	#Название Организации	Лист
							10

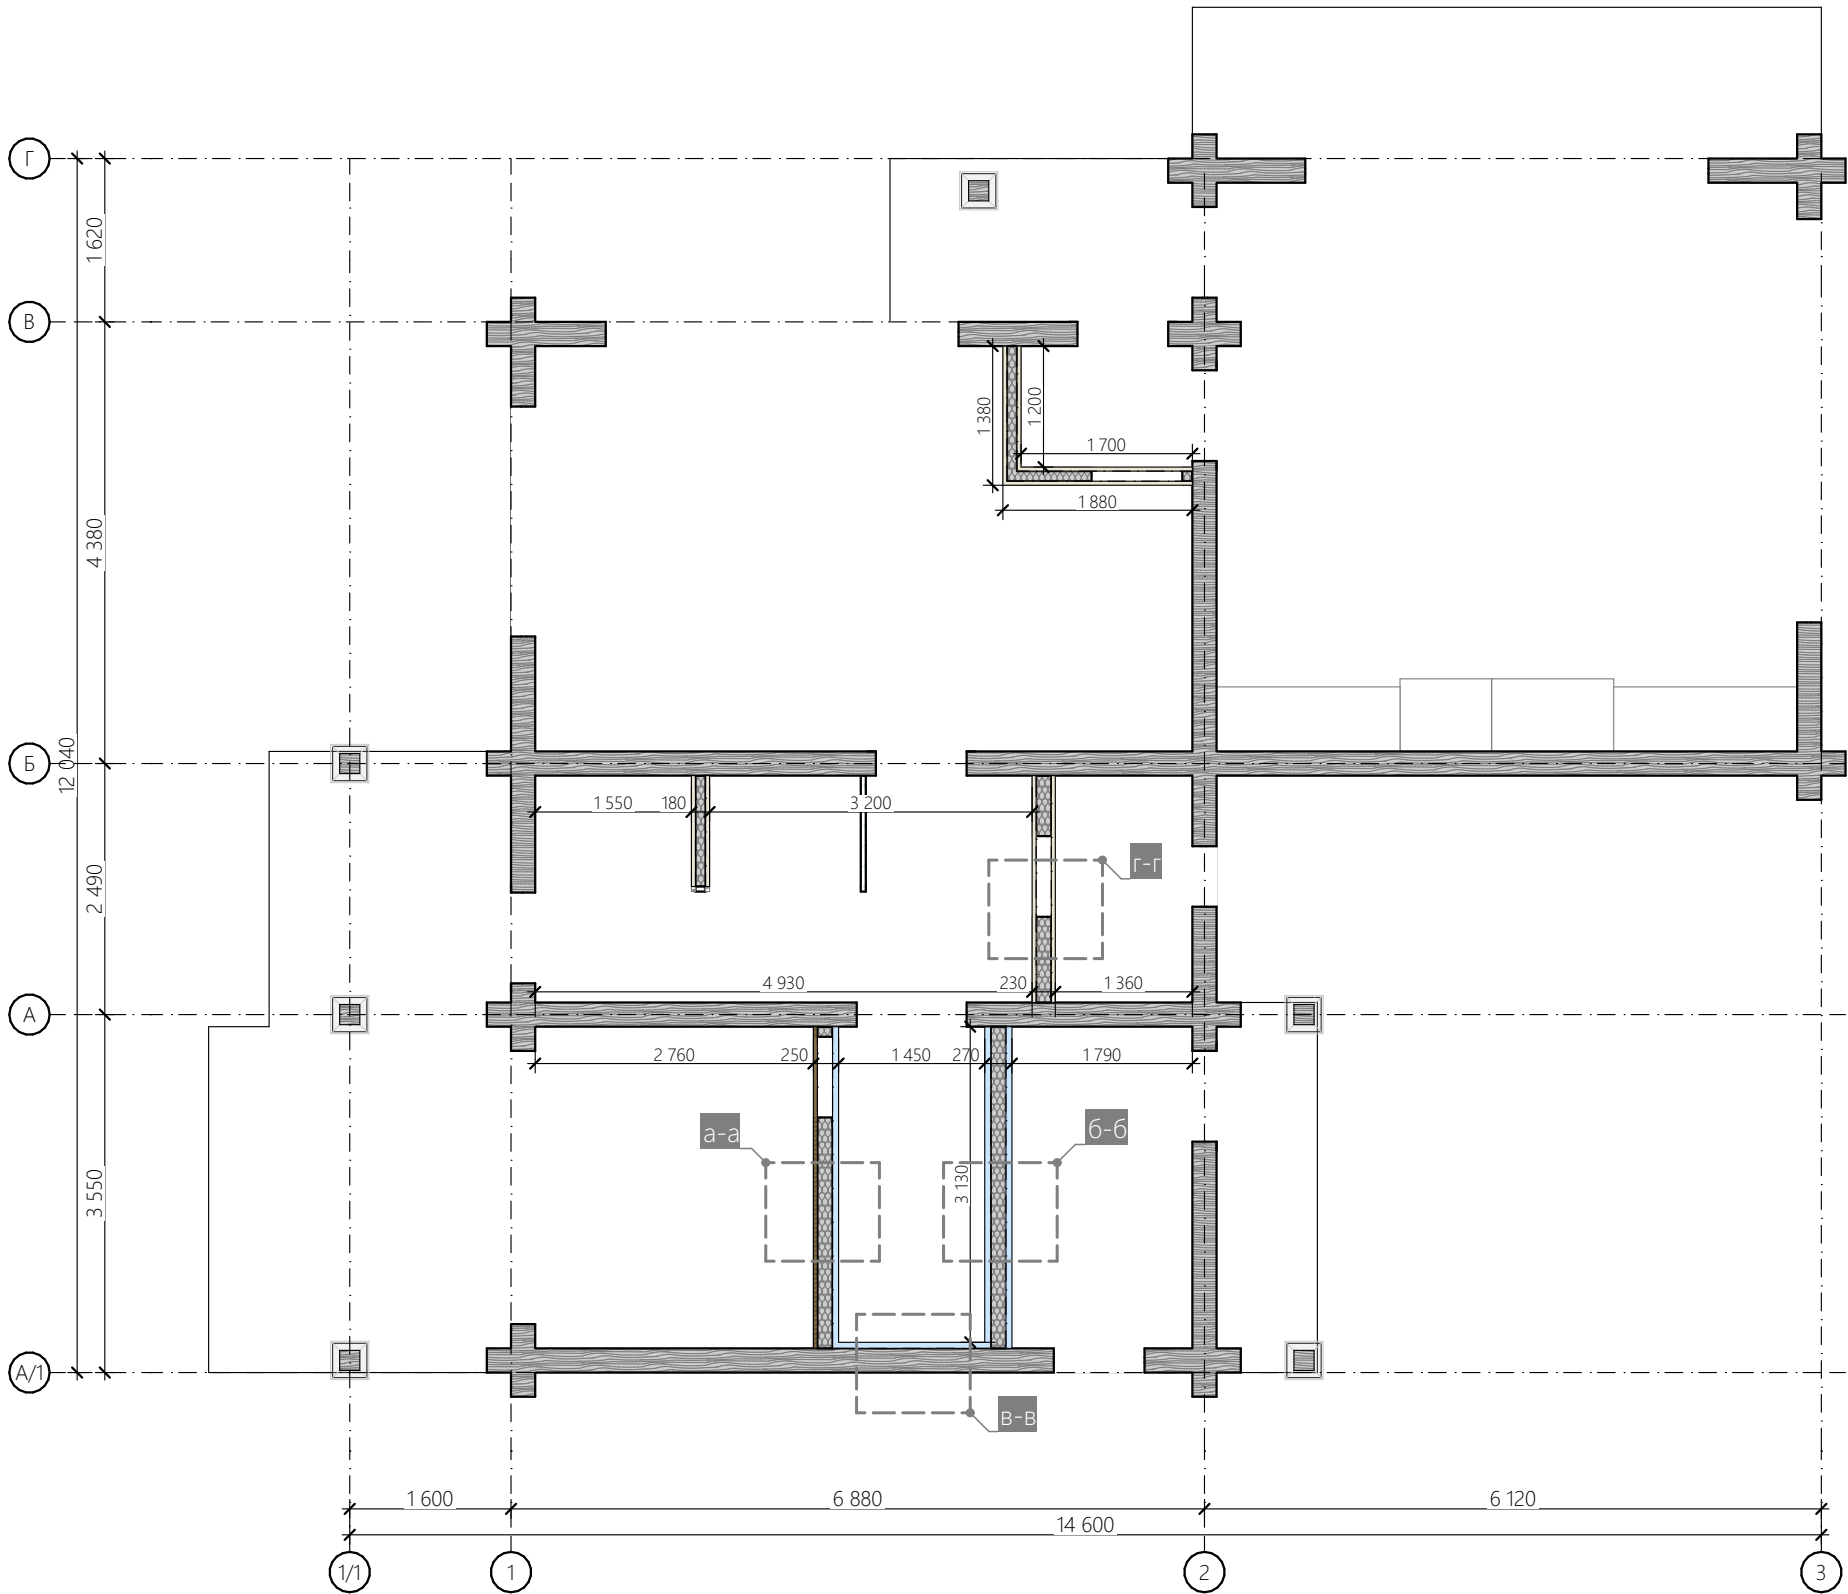

Ведомость покрытий стен

№	Наименование	Условное обозначение
1	Планкен (20мм)	
2	Фиброцементный сайдинг	
3	Имитация бруса (20мм)	
4	Вагонка (16мм)	
5	Керамогранит (10мм)	

Примечание:
1. Сечение по стенам смотреть на след. листе

Согласовано				
И-нв. № подл.	Взам. инв. №		Подп. и дата	

Лист	Изм.	№ Докум.	Подп.	Дата

Адрес:

План покрытия отделки стен

#Название Организации


Экспликация отделки стен

№ разреза

Сечение


Состав

а-а

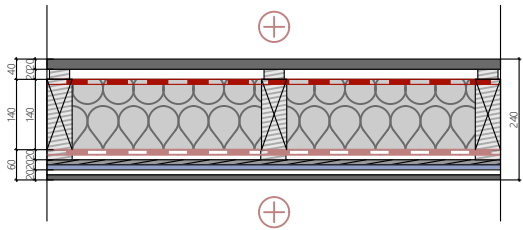


-Вагонка	20мм
-Обрешётка	20мм
-Пароизоляционная мембрана	
алюминиевая фольга	
-Стойка каркаса (утепленная)	140мм
-Пароизоляционная мембрана	
-Обрешётка	20мм
-ОСБ	9мм
-Рустанель	10мм
-Керамогранит+клей	20мм

б-б

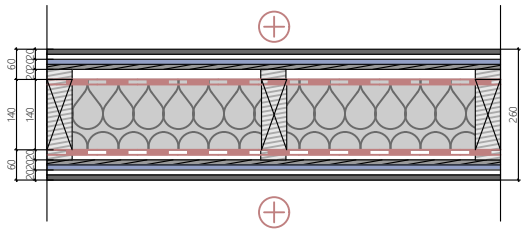


-Керамогранит+клей	20мм
-Рустанель	10мм
-ОСБ	9мм
-Обрешётка	20мм
-Пароизоляционная мембрана	
-Стойка каркаса (утепленная)	140мм
-Пароизоляционная мембрана	
-Обрешётка	20мм
-ОСБ	9мм
-Рустанель	10мм
-Керамогранит+клей	20мм

в-в

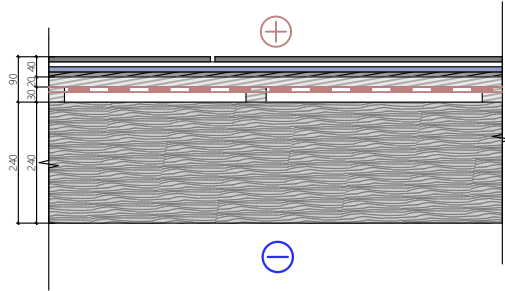

-Керамогранит+клей	20мм
-Рустанель	10мм
-ОСБ	9мм
-Обрешётка	20мм
-Пароизоляционная мембрана	
-Вент. брус	30мм
-Клееный брус	240мм

г-г

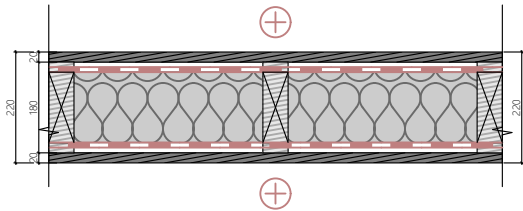

-Имитация бруса	20мм
-Вентбрус (вертикально)	50мм
-Пароизоляционная мембрана	
-Стойка каркаса (утепленная)	140мм
-Пароизоляционная мембрана	
-Вентбрус (вертикально)	50мм
-Имитация бруса	20мм

Согласовано

Взам. инв. №

Подп. и дата

Инв. № подл.

Лист	Изм.	№ Докум.	Подп.	Дата

Экспликация отделки стен

#Название Организации

Лист


12

План расстановки розеток

1:75

Условные обозначения:

-  - розетка 220V с заземлением
-  - розетка 220V с заземлением и влагозащитой
-  - розетка для ТВ
-  - интернет - розетка
-  - электровывод

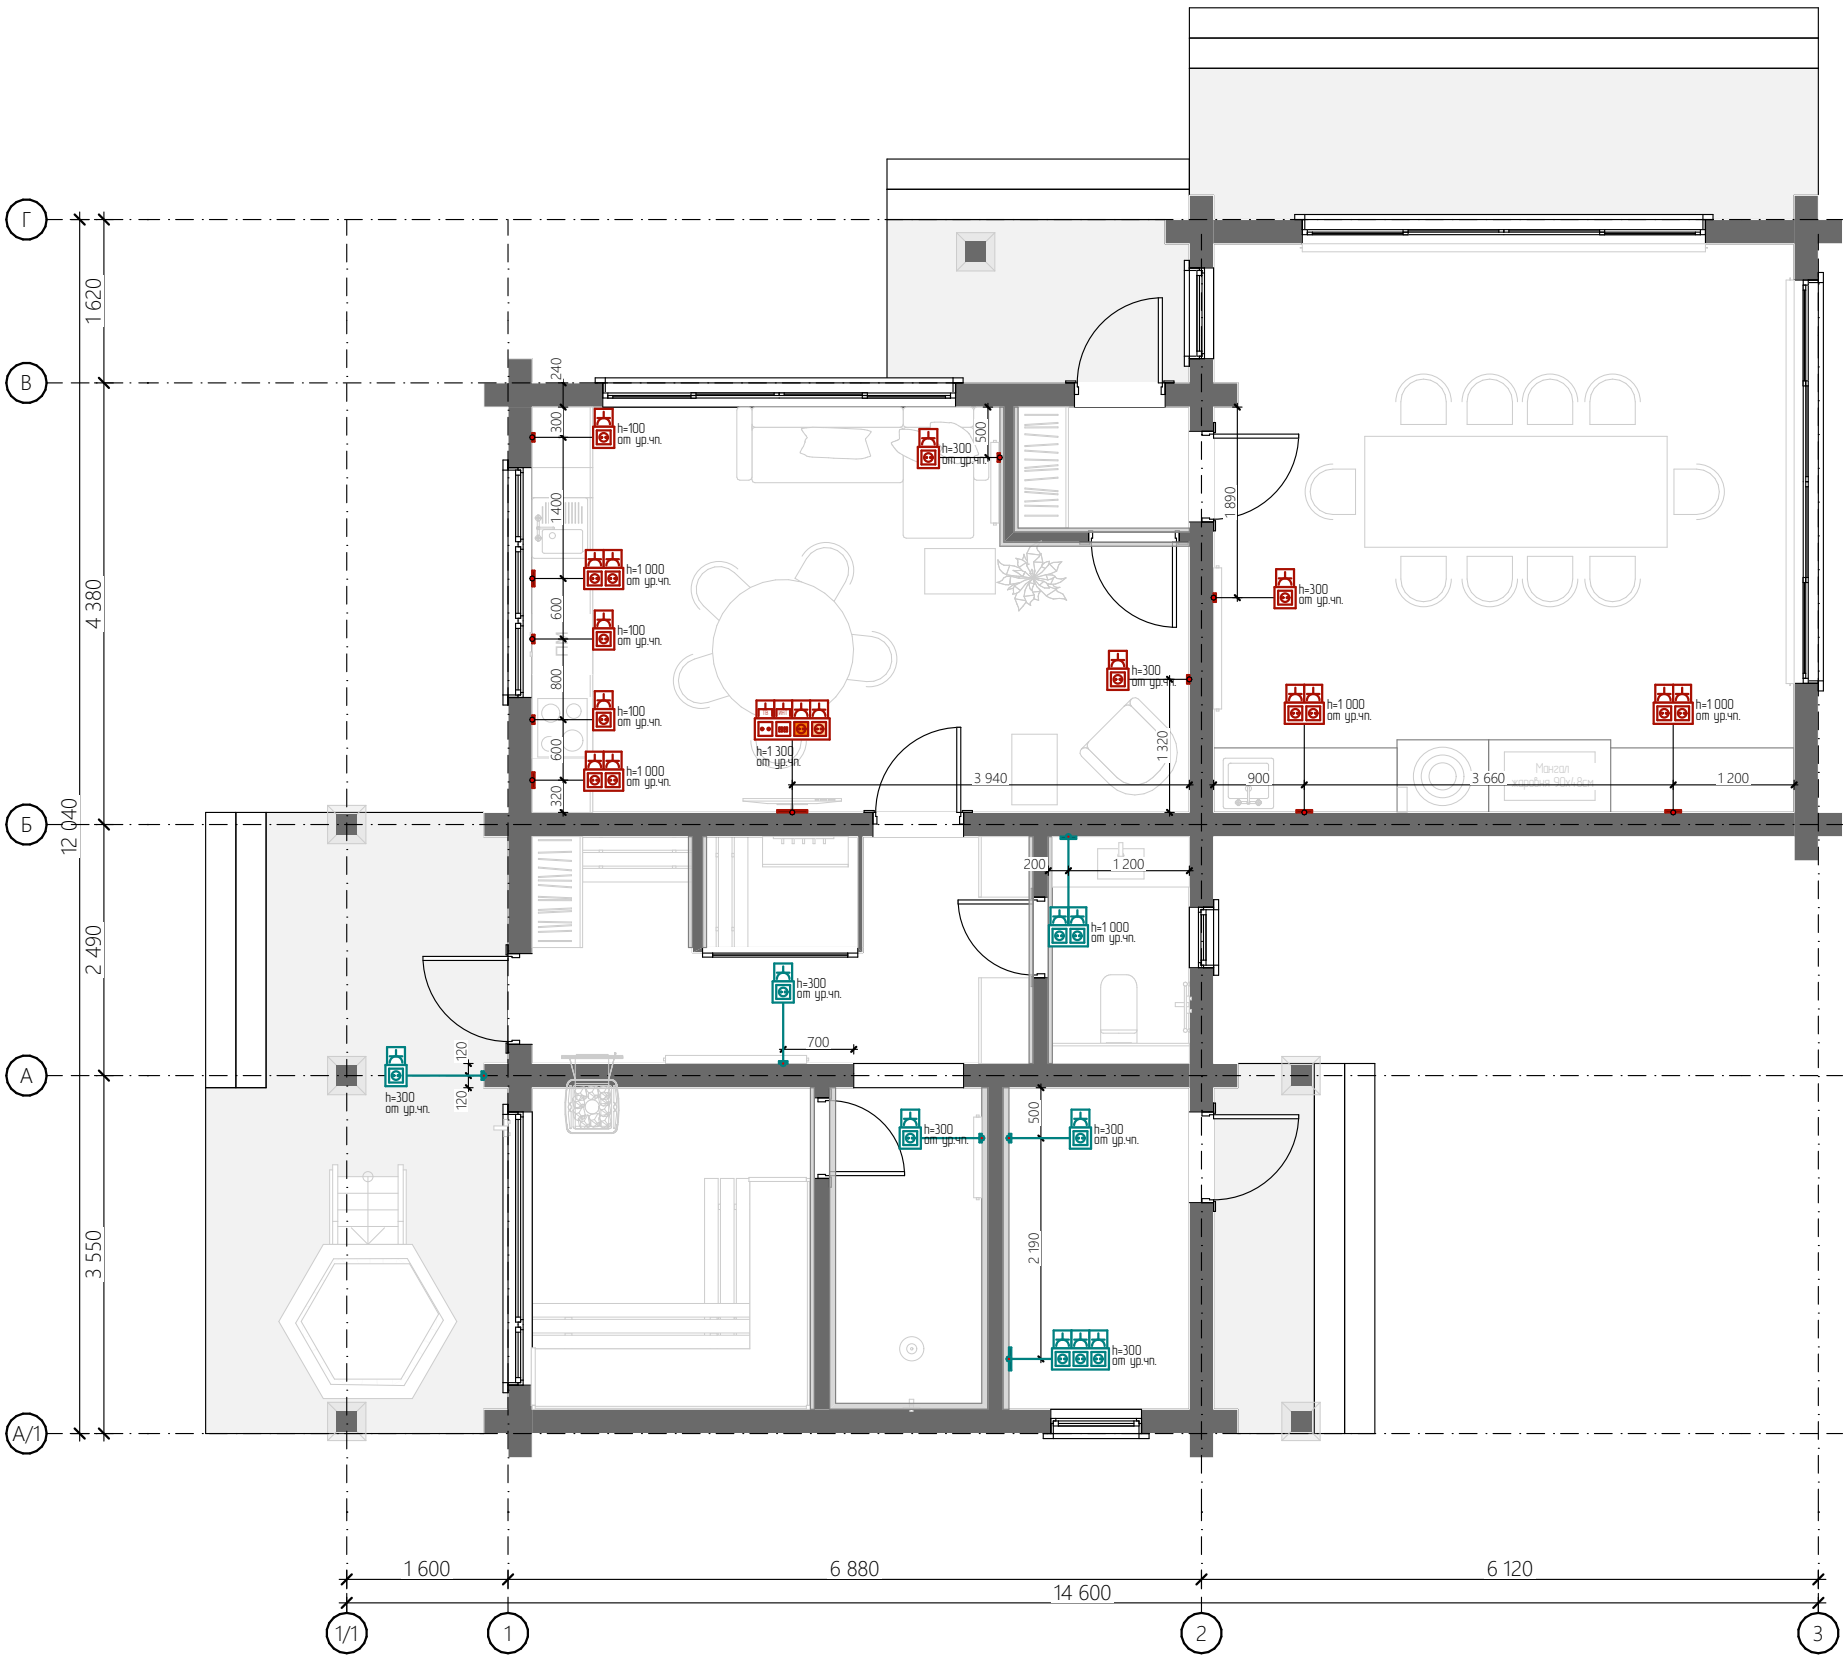

Примечание:

1. Схема размещения розеток является рекомендательной и требует согласования с заказчиком по месту.
2. Все высоты даны от чистового пола.
3. Все указанные размеры даются до центра позиций.
4. Отметки розеток, выключателей, выводов и др. оборудования, являются предварительными и уточняются после выбора финишных материалов и мебели.
5. Размеры уточняются дополнительно

Согласовано

Взам. инв. №

Подп. и дата

Инв. № подл.

Лист	Изм.	№ Докум.	Подп.	Дата

Адрес:

План размещения розеток
стен

#Название Организации

-  - выключатель одноклавишный
-  - выключатель двухклавишный
-  - люстра
-  - точечный светильник
-  - настенные бра
-  - контурная подсветка
-  - трековый светильник



Примечание:

1. Схема размещения розеток является рекомендательной и требует согласования с заказчиком по месту.
2. Все высоты даны от чистового пола.
3. Все указанные размеры даются до центра позиций.
4. Отметки розеток, выключателей, выводов и др. оборудования, являются предварительными и уточняются после выбора финишных материалов и мебели.
5. Размеры уточняются дополнительно

Согласовано				
И-нв. № подл.	Подп. и дата	Взам. инв. №		

Лист	Изм.	№ Докум.	Подп.	Дата

Адрес:

План расстановки
светильников и
выключателей


#Название Организации

План кровли бани


1:75

Условные обозначения:

- Кровля бани
- Подшив свесов бани

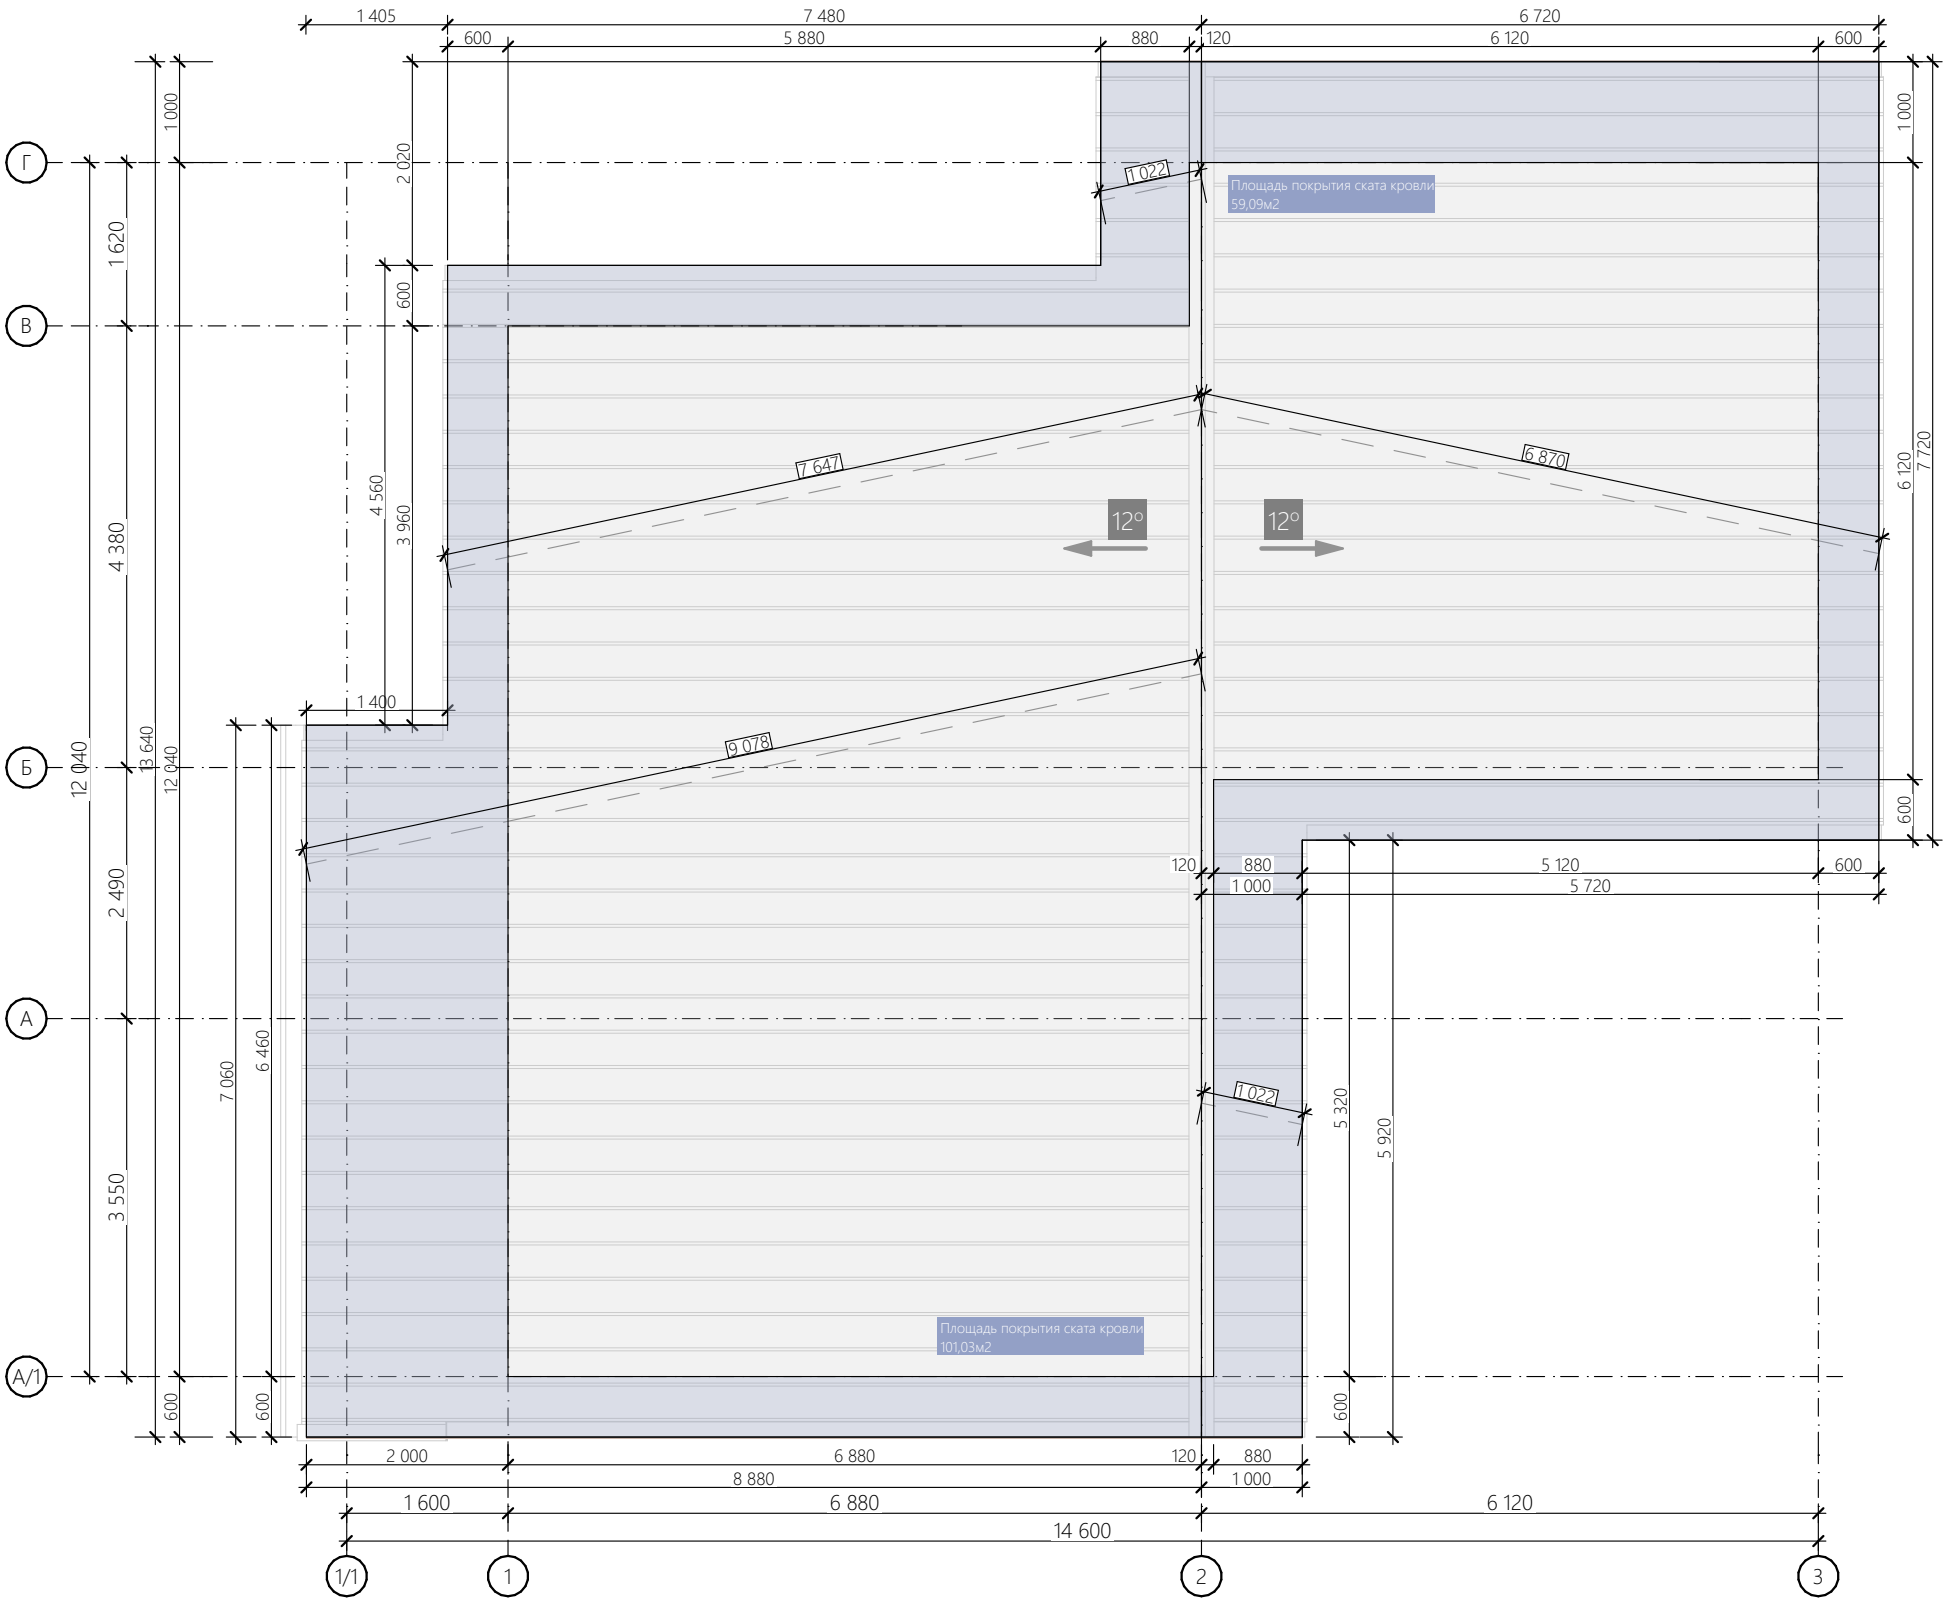

аксонометрия кровли:

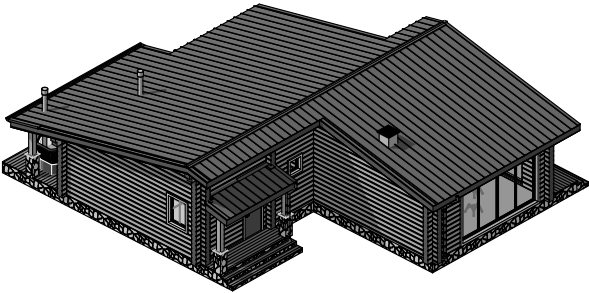

Согласовано				
И-нв. № подл.	Подп. и дата	Взам. инв. №		

Лист	Изм.	№ Докум.	Подп.	Дата

Адрес:

План кровли бани


#Название Организации

План кровли террасы


1:75

Условные обозначения:

- Кровля бани
- Подшив свесов бани

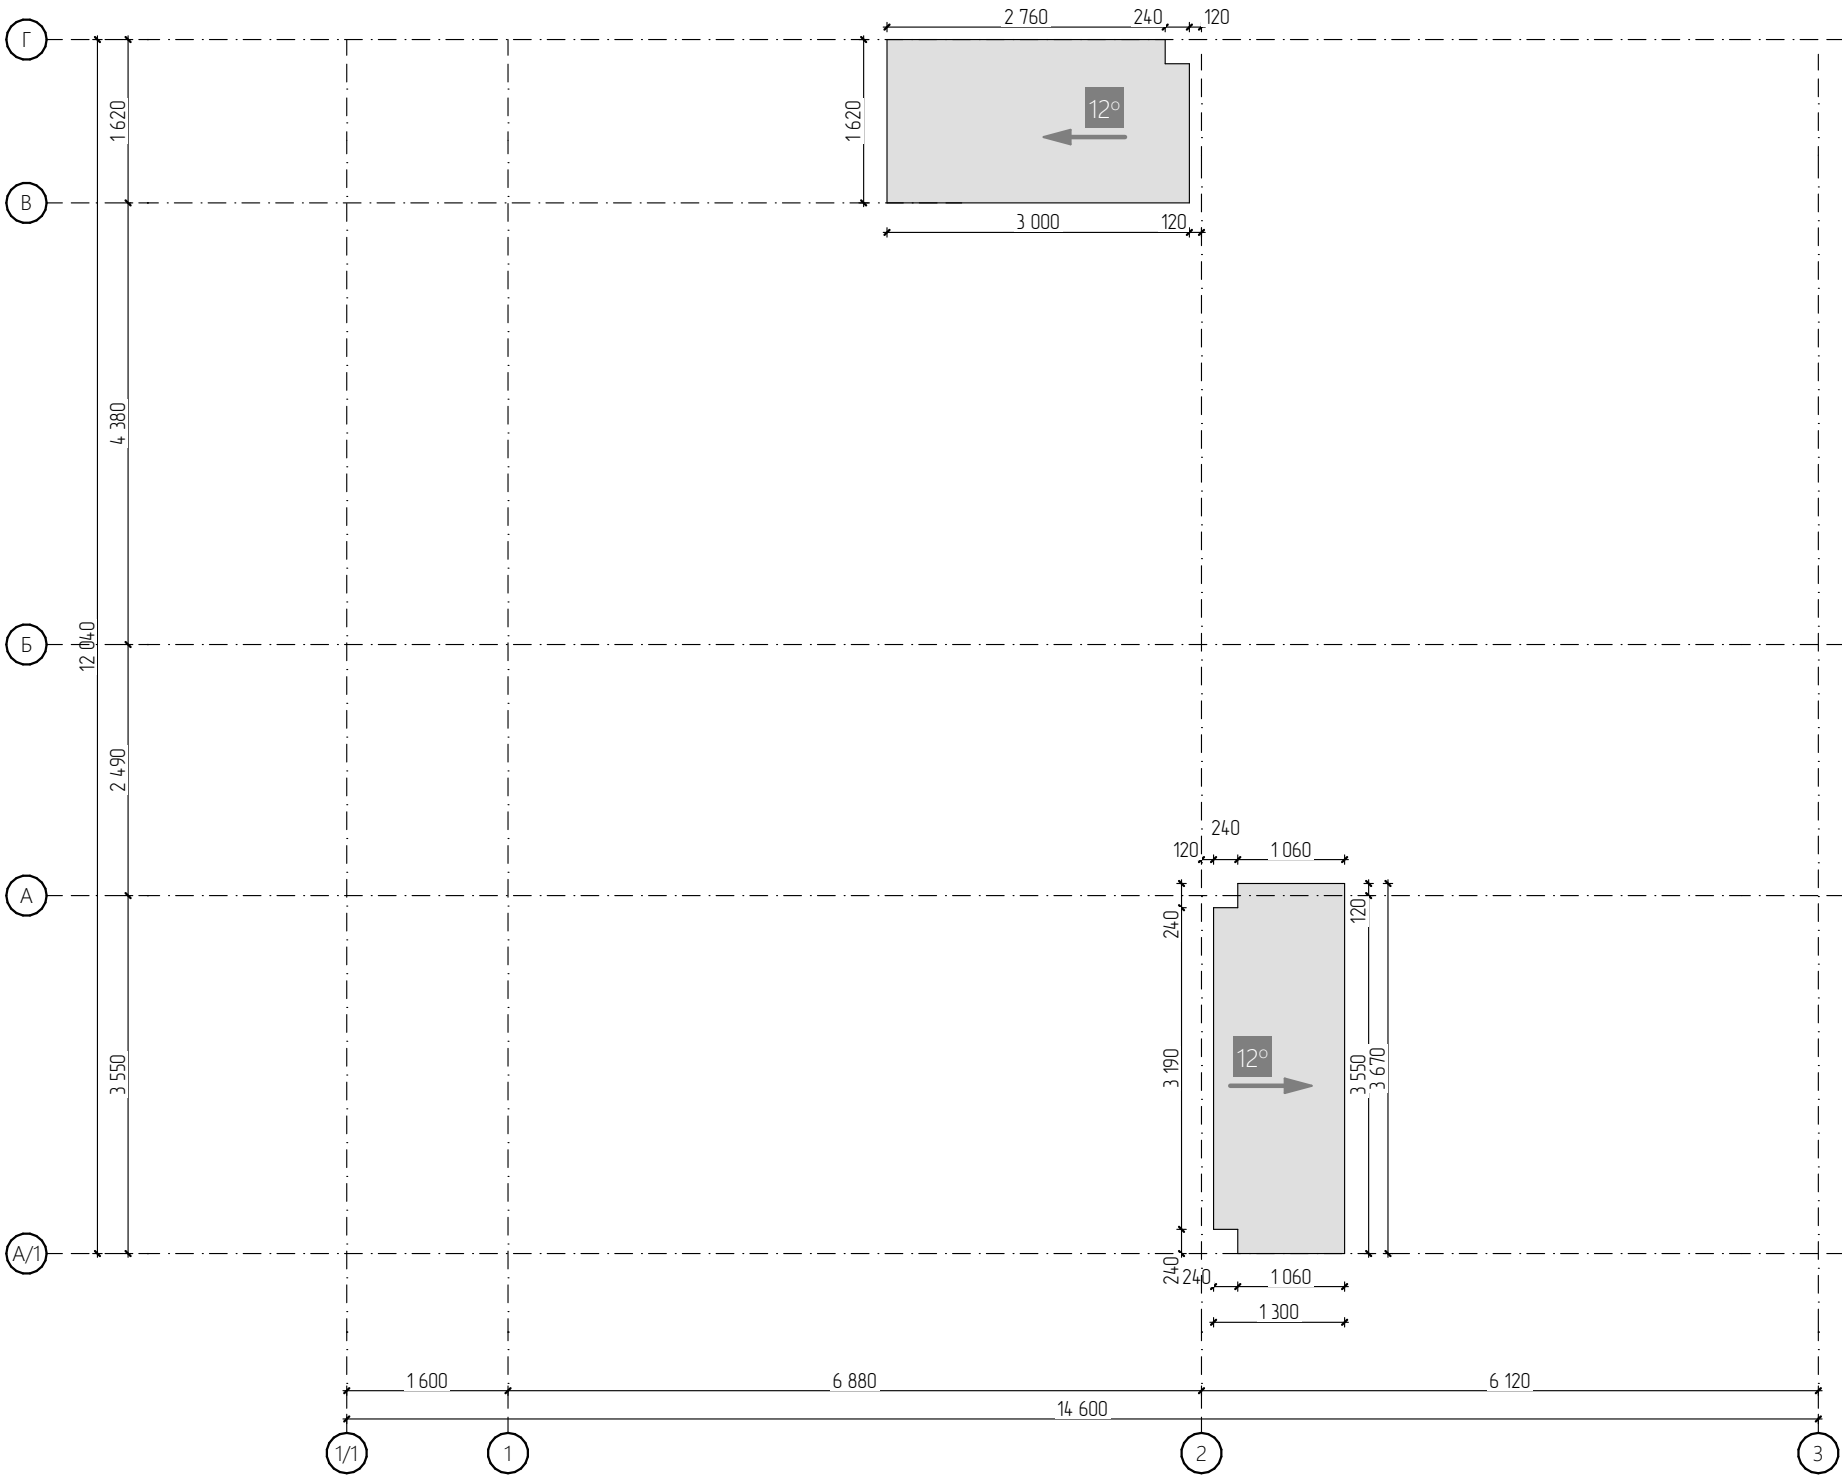

аксонометрия кровли:

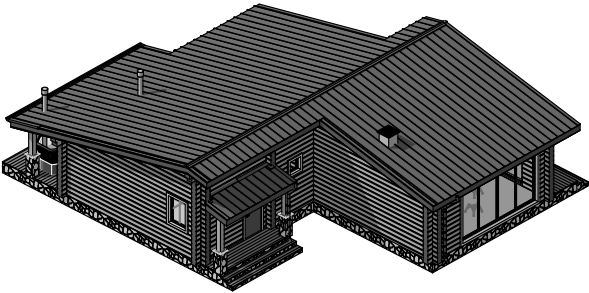

Согласовано				
И-нв. № подл.	Подп. и дата	Взам. инв. №		

Лист	Изм.	№ Докум.	Подп.	Дата

Адрес:

План кровли террасы

#Название Организации

Согласовано


Взам. инв. №

Подп. и дата

Инв. № подл.

Разрез 1-1

1:50

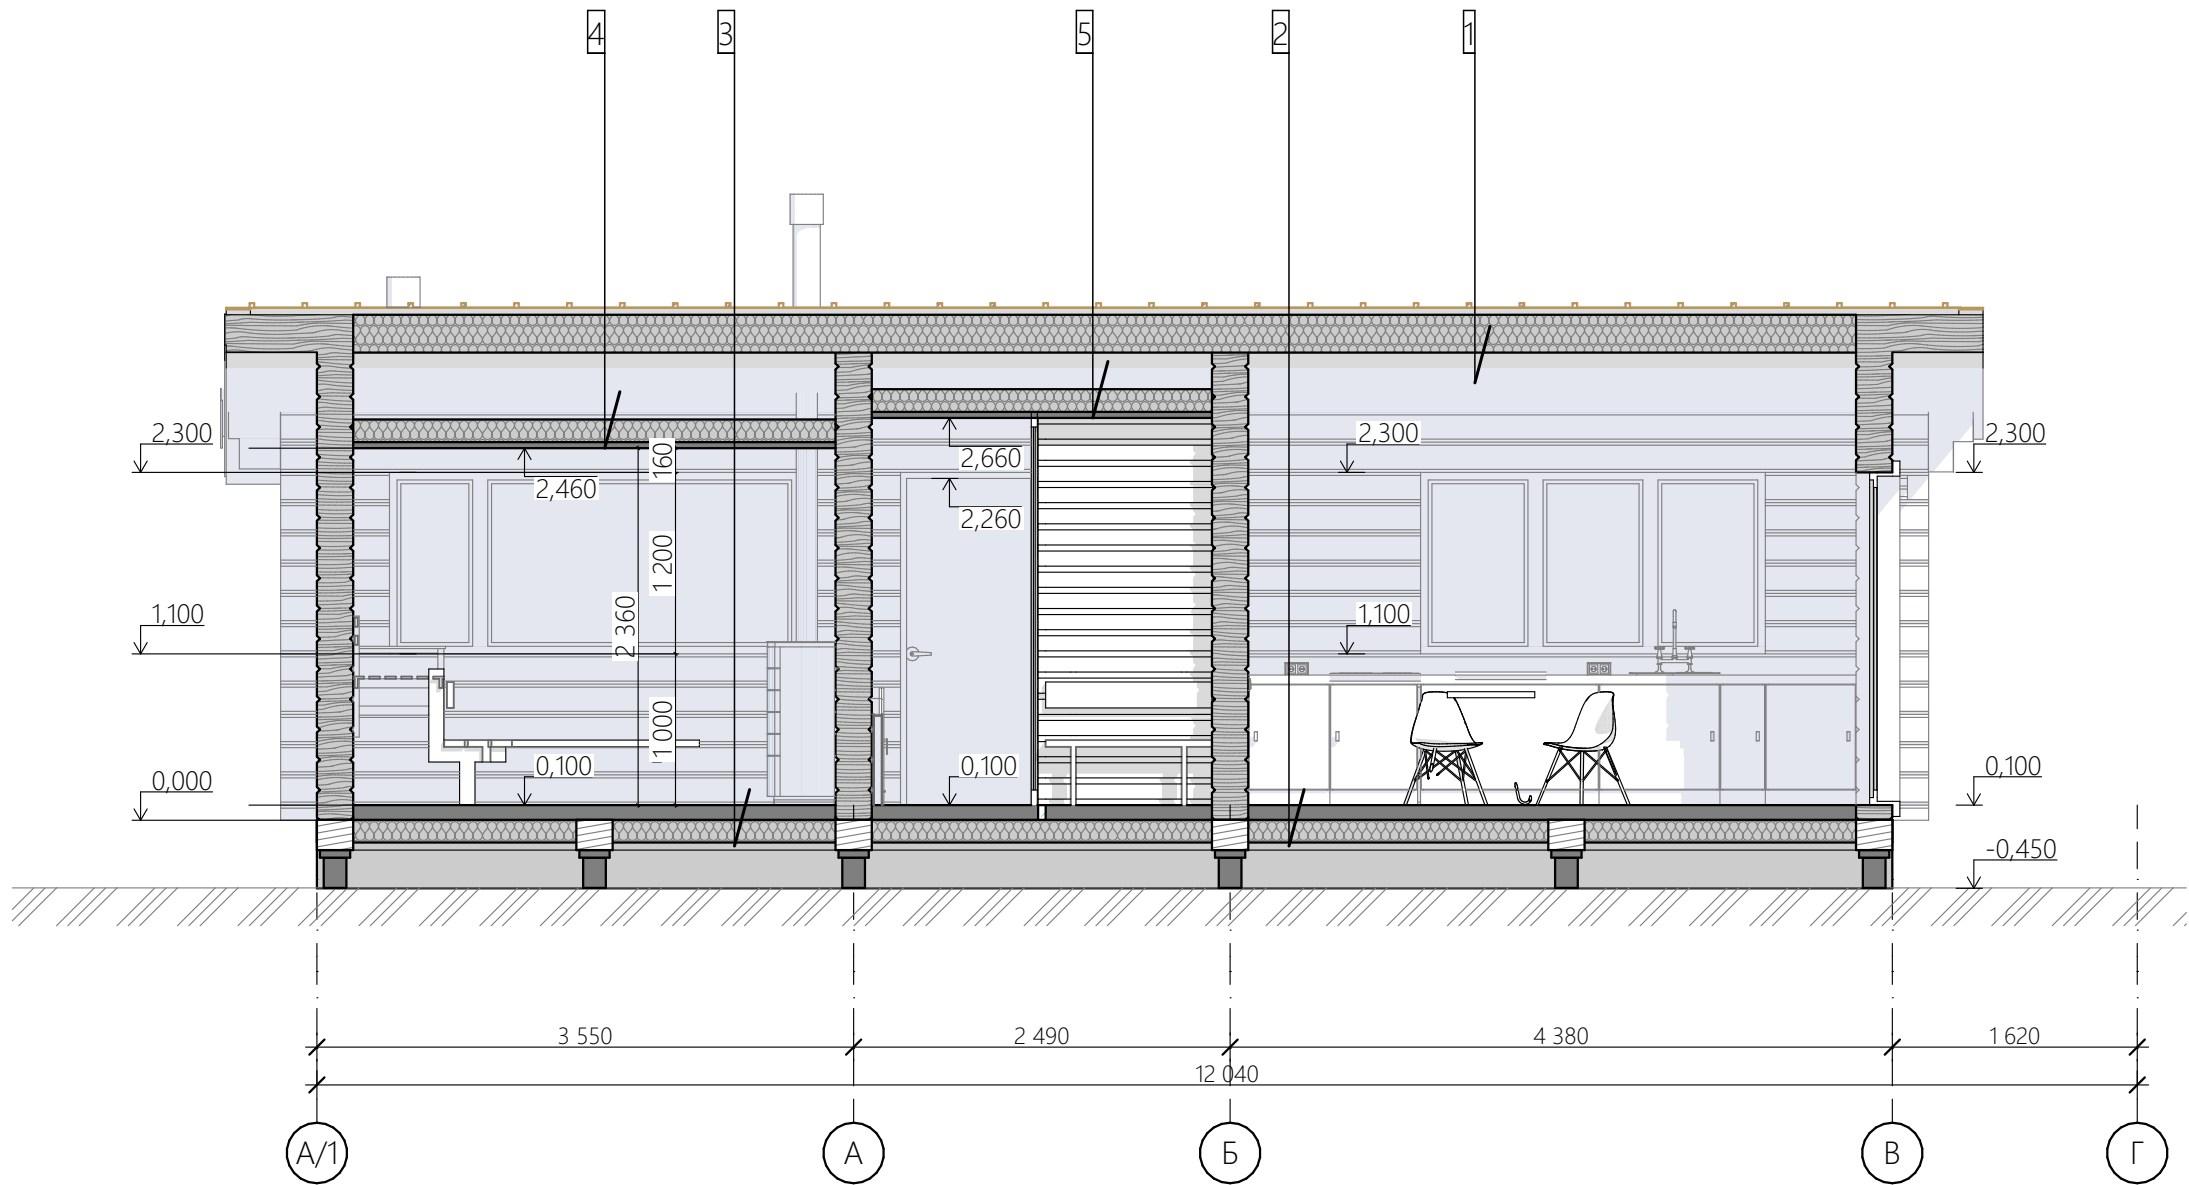

- | | | |
|---|------------------------------|-----------------|
| 1 | -Фальц | двойной стоячий |
| | -Обрешётка | 25x100мм |
| | -Контробрешётка | 50x50мм |
| | -Гидроветрозащитная мембрана | |
| | -Стропильная система | 190x45мм |
| | утепленная | |
| | -Пароизоляционная мембрана | |
| | -Обрешётка | 20мм |
| | -Имитация бруса | 20мм |

- | | | |
|---|------------------------------|-------|
| 2 | -Ламинат | 10мм |
| | -Подложка под ламинат | 10мм |
| | -Полусухая цементно-песчаная | |
| | стяжка | 50мм |
| | -ЦСП | 10мм |
| | -ОСБ | 18мм |
| | -Пароизоляционная мембрана | |
| | -Лаги перекрытия (утепл.) | 140мм |
| | -Гидроветрозащитная мембрана | |
| | -Просечка (сетка яч. 5x5) | |
| | -Обрешётка | 20мм |

- | | | |
|---|---------------------------------------|-------|
| 3 | -Керамогранит | 10мм |
| | -Клей | 10мм |
| | -Полусухая цементно-песчаная стяжка | |
| | (с устройством теплого водяного пола) | 50мм |
| | -ЦСП | 10мм |
| | -ОСБ | 18мм |
| | -Пароизоляционная мембрана | |
| | -Лаги перекрытия (утепл.) | 140мм |
| | -Гидроветрозащитная мембрана | |
| | -Просечка (сетка яч. 5x5) | |
| | -Обрешётка | 20мм |

- | | | |
|---|----------------------------|----------|
| 4 | -Лаги перекрытия | 140x45мм |
| | (утеплённые 150мм) | |
| | -Пароизоляционная мембрана | |
| | (алюминиевая фольга) | |
| | -Обрешётка | 20x40мм |
| | -Вагонка | 20мм |

- | | | |
|---|----------------------------|----------|
| 5 | -Лаги перекрытия | 140x45мм |
| | (утеплённые 150мм) | |
| | -Пароизоляционная мембрана | |
| | -Обрешётка | 20x40мм |
| | -Имитация бруса | 20мм |

Лист	Изм.	№ Докум.	Подп.	Дата

Адрес:

Разрез 1-1


#Название Организации

Лист

17

Разрез 2-2

1:55

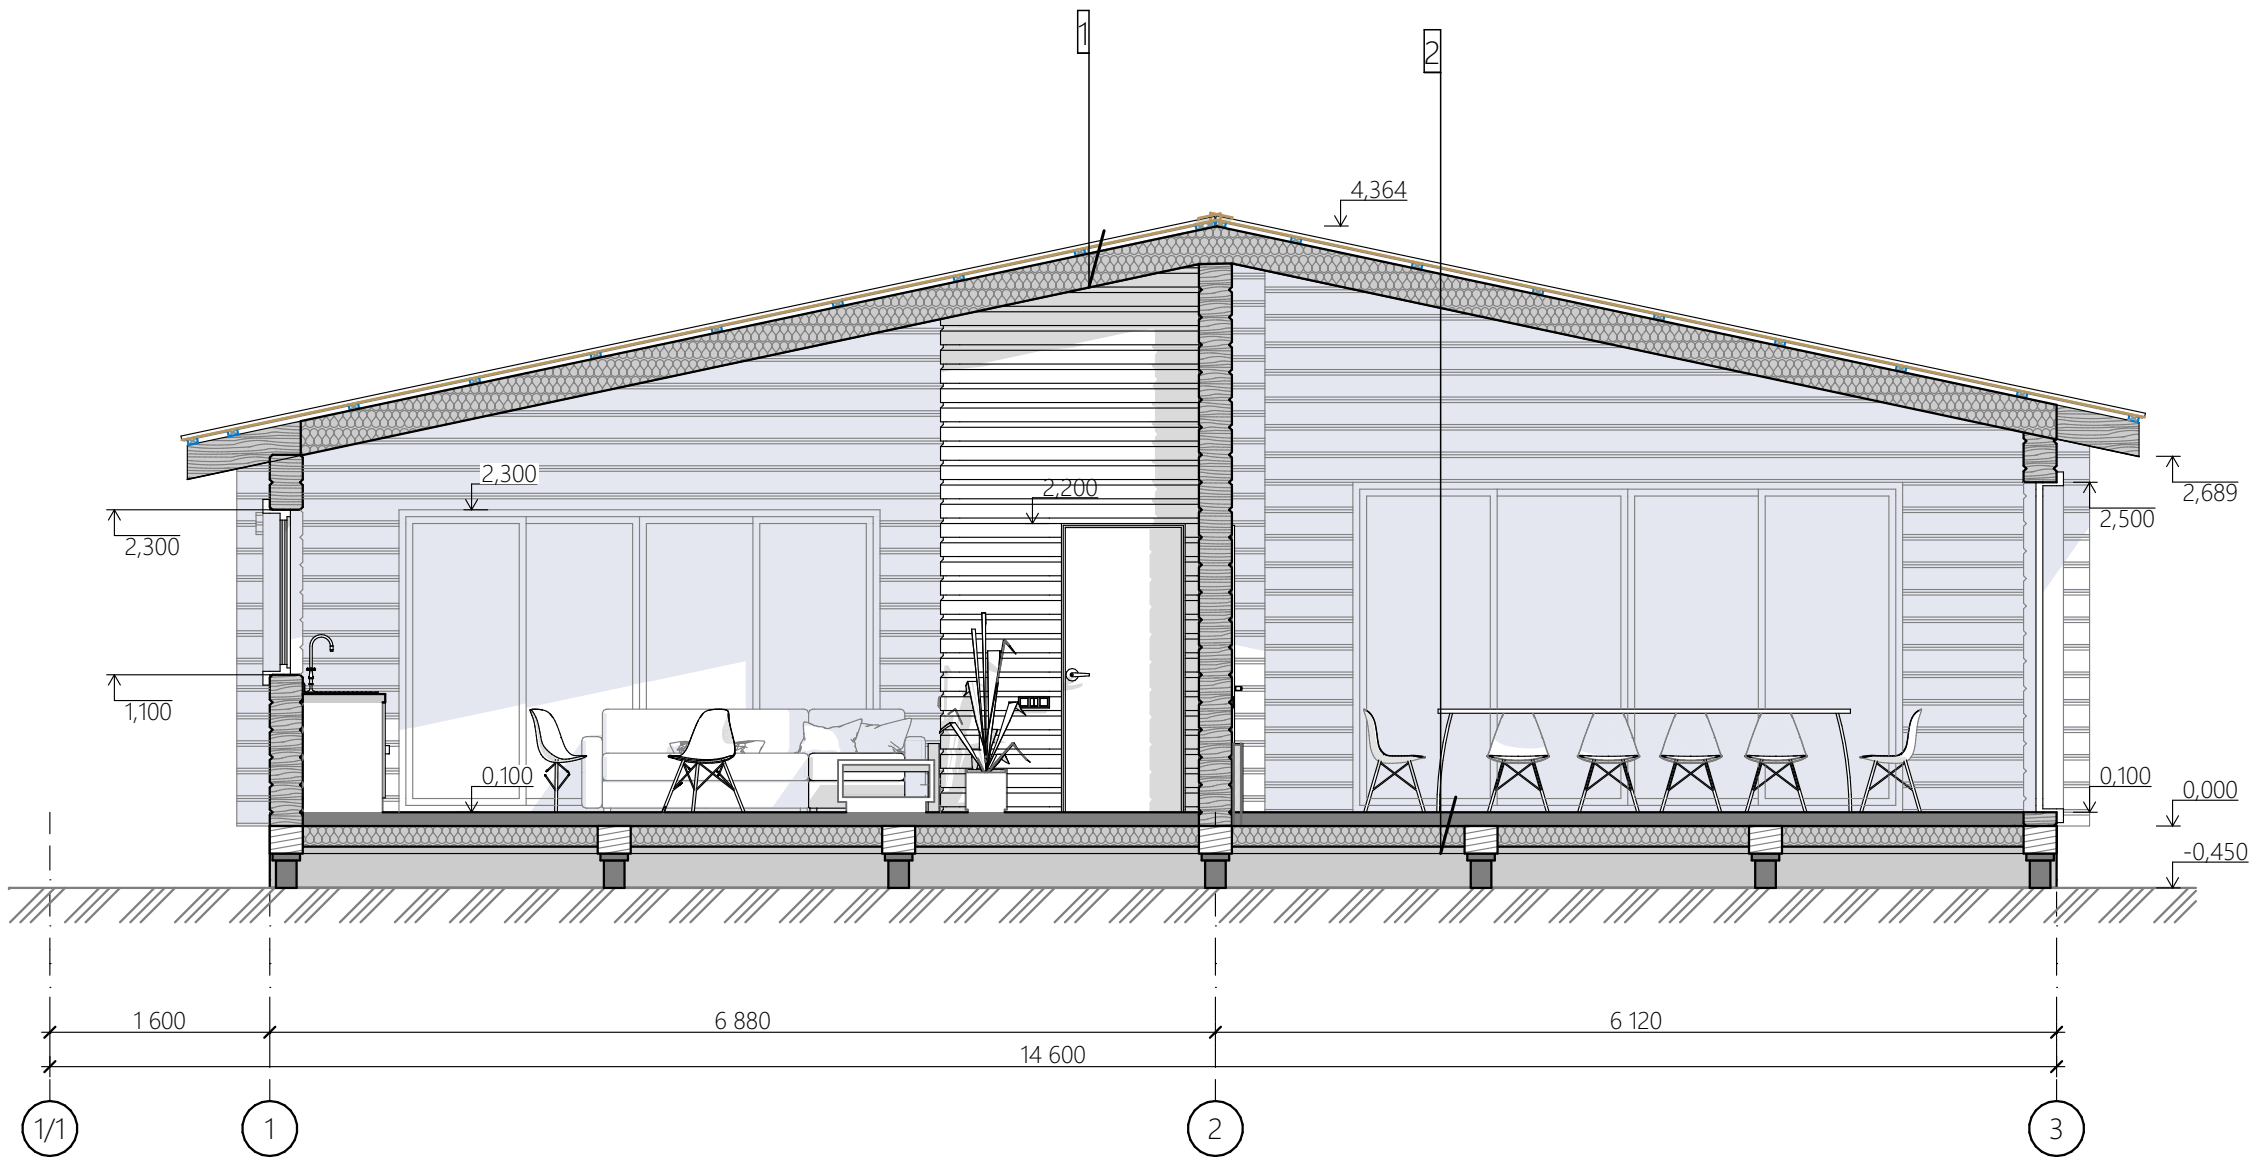

- 1
- Фальц двойной стоячий
 - Обрешётка 25x100мм
 - Контробрешётка 50x50мм
 - Гидроветрозащитная мембрана
 - Стропильная система 190x45мм
 - утепленная
 - Пароизоляционная мембрана
 - Обрешётка 20мм
 - Имитация бруса 20мм

- 2
- Ламинат 10мм
 - Подложка под ламинат 10мм
 - Полусухая цементно-песчаная
 - стяжка 50мм
 - ЦСП 10мм
 - ОСБ 18мм
 - Пароизоляционная мембрана
 - Лаги перекрытия (утепл.) 140мм
 - Гидроветрозащитная мембрана
 - Просечка (сетка яч. 5x5)
 - Обрешётка 20мм

Согласовано

Взам. инв. №

Подп. и дата


Инв. № подл.




Лист	Изм.	№ Докум.	Подп.	Дата

Адрес:

Разрез 2-2

#Название Организации

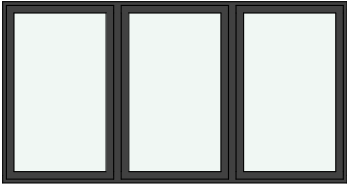Ведомость оконных проемов													
Наименование		шт	Размеры проема		Ш х В, мм		Вид		Площадь, м2				
OK-01		2	600×600						0,39				
OK-02		2	900×1 200						1,17				
OK-03		2	2 280×1 200						2,96				
Примечание: 1. Изготовление окон и дверей определяется заказчиком, допускается изменение открывания окон и дверей; 2. При заказе оконных и дверных блоков необходим обмер по месту от изготовителя; 3. Оконные и дверные изделия изображены со стороны открывания.													
Инв. № подл.		Подп. и дата	Взам. инв. №	Лист					Ведомость оконных проёмов (начало)		#Название Организации		Лист
				Изм.									19
				№ Докум.									

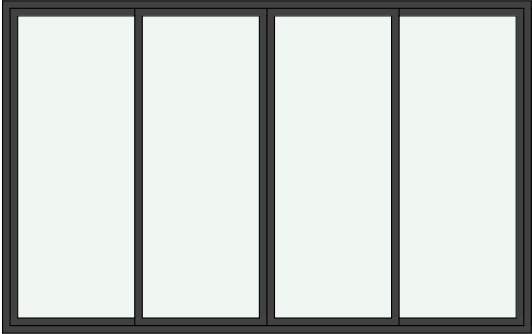
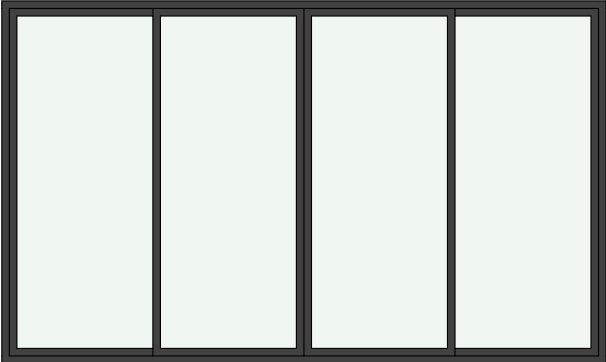
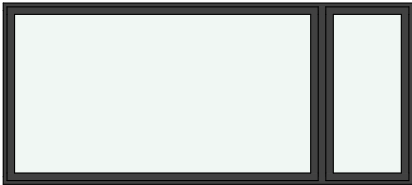
Ведомость оконных проемов										
Наименование		шт	Размеры проема		Ш х В, мм		Вид		Площадь, м2	
OK-04		2	3 500×2 200						8,34	
OK-05		4	4 000×2 400						10,40	
OK-06		2	900×2 400						2,34	
OK-07		2	2 710×1 200						3,52	
									79,04 м²	
Лист		Изм.	№ Докум.		Подп.	Дата	Ведомость оконных проёмов (окончание)		#Название Организации	Лист
										20

Согласовано

Ив. № подл.

Подп. и дата

Взам. инв. №

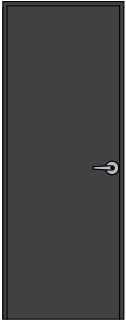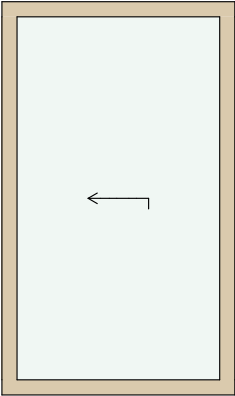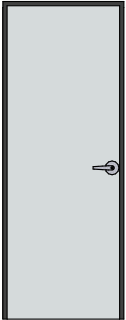Ведомость дверных проемов												
Наименование		шт.	Размеры проема		Ш х В, мм		Вид		Площадь, м2			
ДВ-01		6	900×2 100						1,89			
ДВ-02		2	800×2 100						1,68			
ДВ-03		2	1 540×2 600						4,00			
ДН-01		6	900×2 200						2,14			
ДП-01		2	800×2 100						1,68			
									39,54 м²			
Лист	Изм.	№ Докум.	Подп.	Дата	Ведомость дверных проёмов		#Название Организации		Лист			
									21			

Согласовано

Ив. № подл.

Подп. и дата

Взам. инв. №

Согласовано				

Инв. № подл.	Подп. и дата		Взам. инв. №	

Согласовано

Взам. инв. №

Подп. и дата


Инв. № подл.

Лист	Изм.	№ Докум.	Подп.	Дата

Адрес:


Цветовое решение; Фасад в осях Г-А

Условные обозначения:

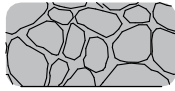-  -Клееный брус, краска ral 7004
-  -Натуральный камень
-  -Водосточная система, наличники, оконные рамы, кровля(RAL 7004)


Ф-1

1:55

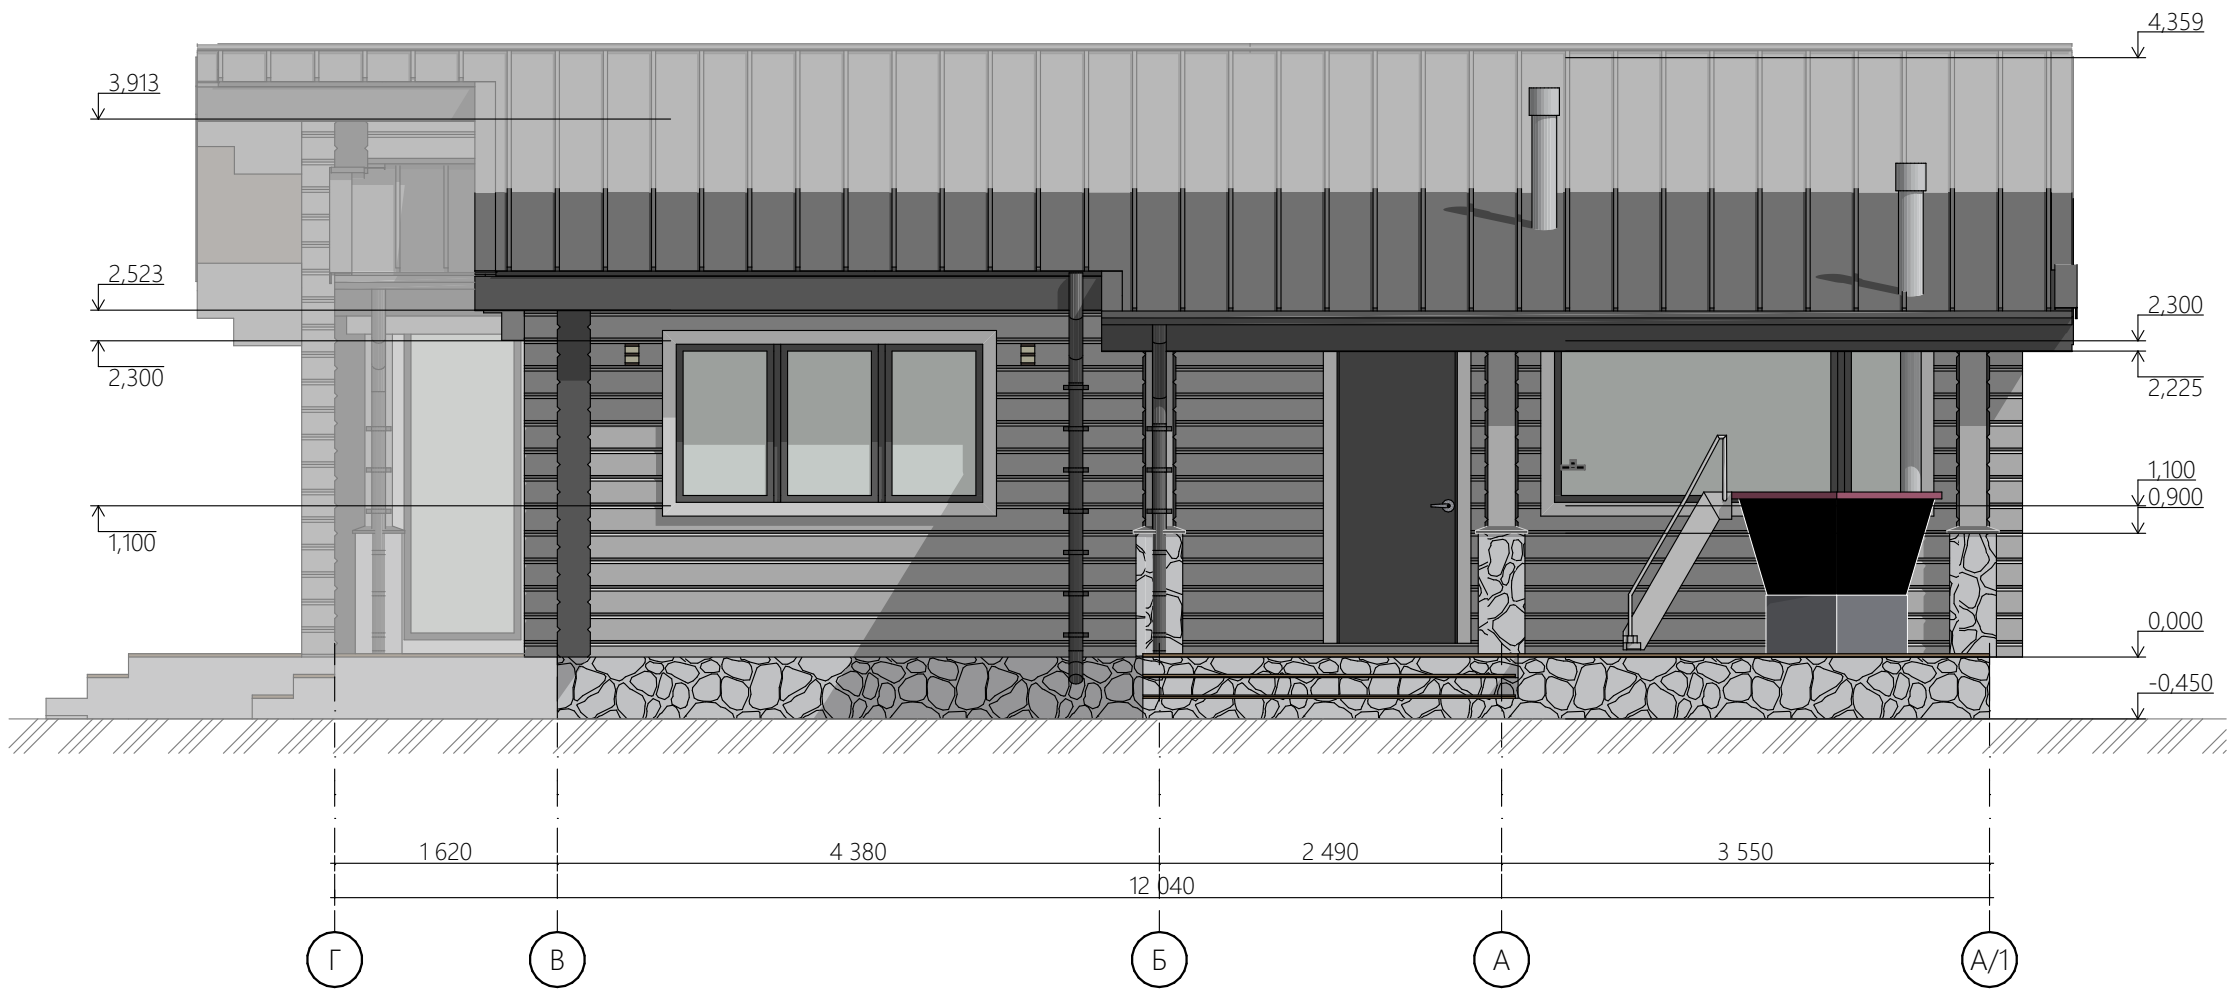

-  -Клееный брус,
краска ral 7004
-  -Натуральный камень
-  -Водосточная система,
наличники, оконные
рамы, кровля(RAL 7004)

1:60

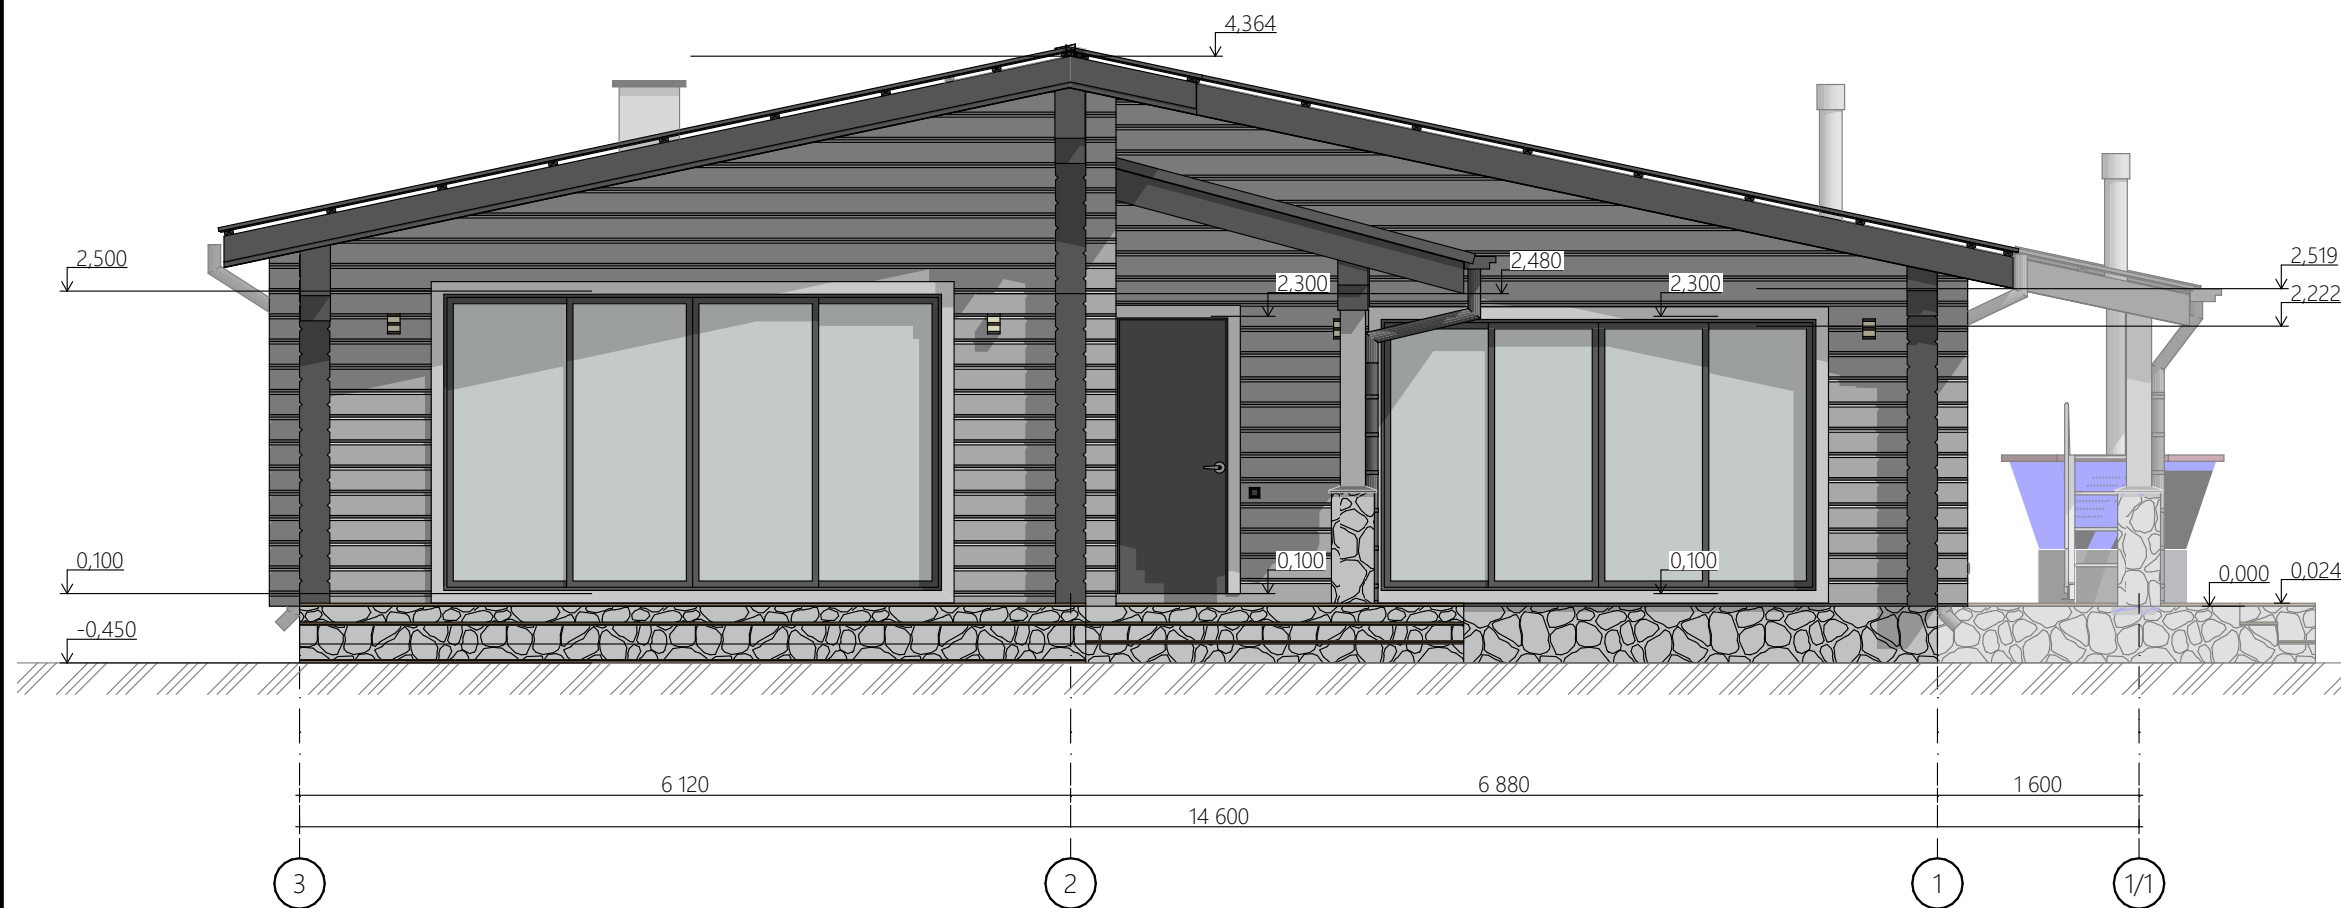

Согласовано

Взам. инв. №

Подп. и дата

ИНВ. № подл.

Лист	Изм.	№ Докум.	Подп.	Дата

Адрес:

Цветовое решение; Фасад в осях 3-1

#Название Организации

ИСТ


23

Согласовано

Взам. инв. №

Подп. и дата

Инв. № подл.

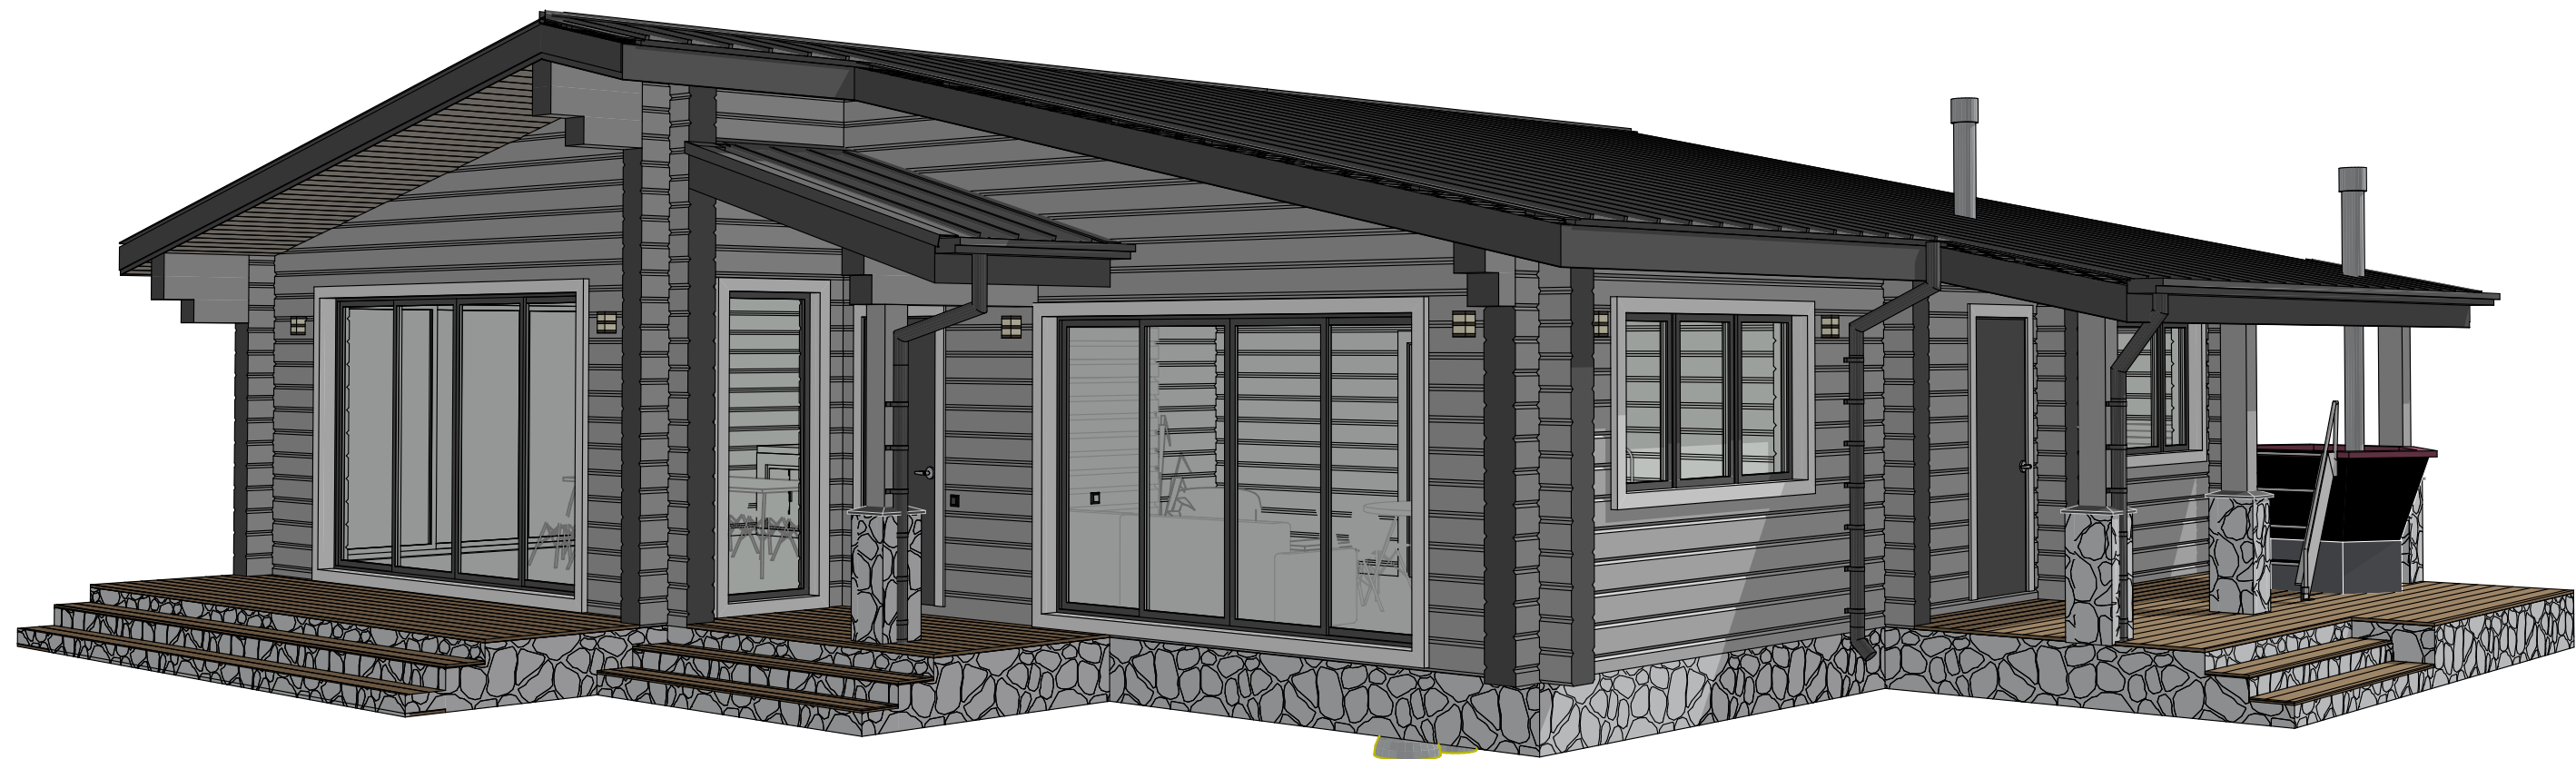

Лист	Изм.	№ Докум.	Подп.	Дата

Адрес:

Аксометрия №1	#Название Организации

Лист
24

Согласовано				
И-нв. № подл.	Подп. и дата	Взам. инв. №		



Условные обозначения:

- Клееный брус, краска ral 7004
- Натуральный камень
- Водосточная система, наличники, оконные рамы, кровля(RAL 7004)

Лист	Изм.	№ Докум.	Подп.	Дата

Адрес:

Цветовое решение; Фасад в осях А-Г

#Название Организации

Согласовано

Взам. инв. №

Подп. и дата

Инв. № подл.

Лист	Изм.	№ Докум.	Подп.	Дата


Адрес:

Цветовое решение; Фасад в
осях 1-3

Условные обозначения:



-Клееный брус,
краска ral 7004

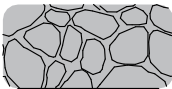


-Натуральный камень



-Водосточная система,
наличники, оконные
рамы, кровля(RAL 7004)

1:60

Ф-4

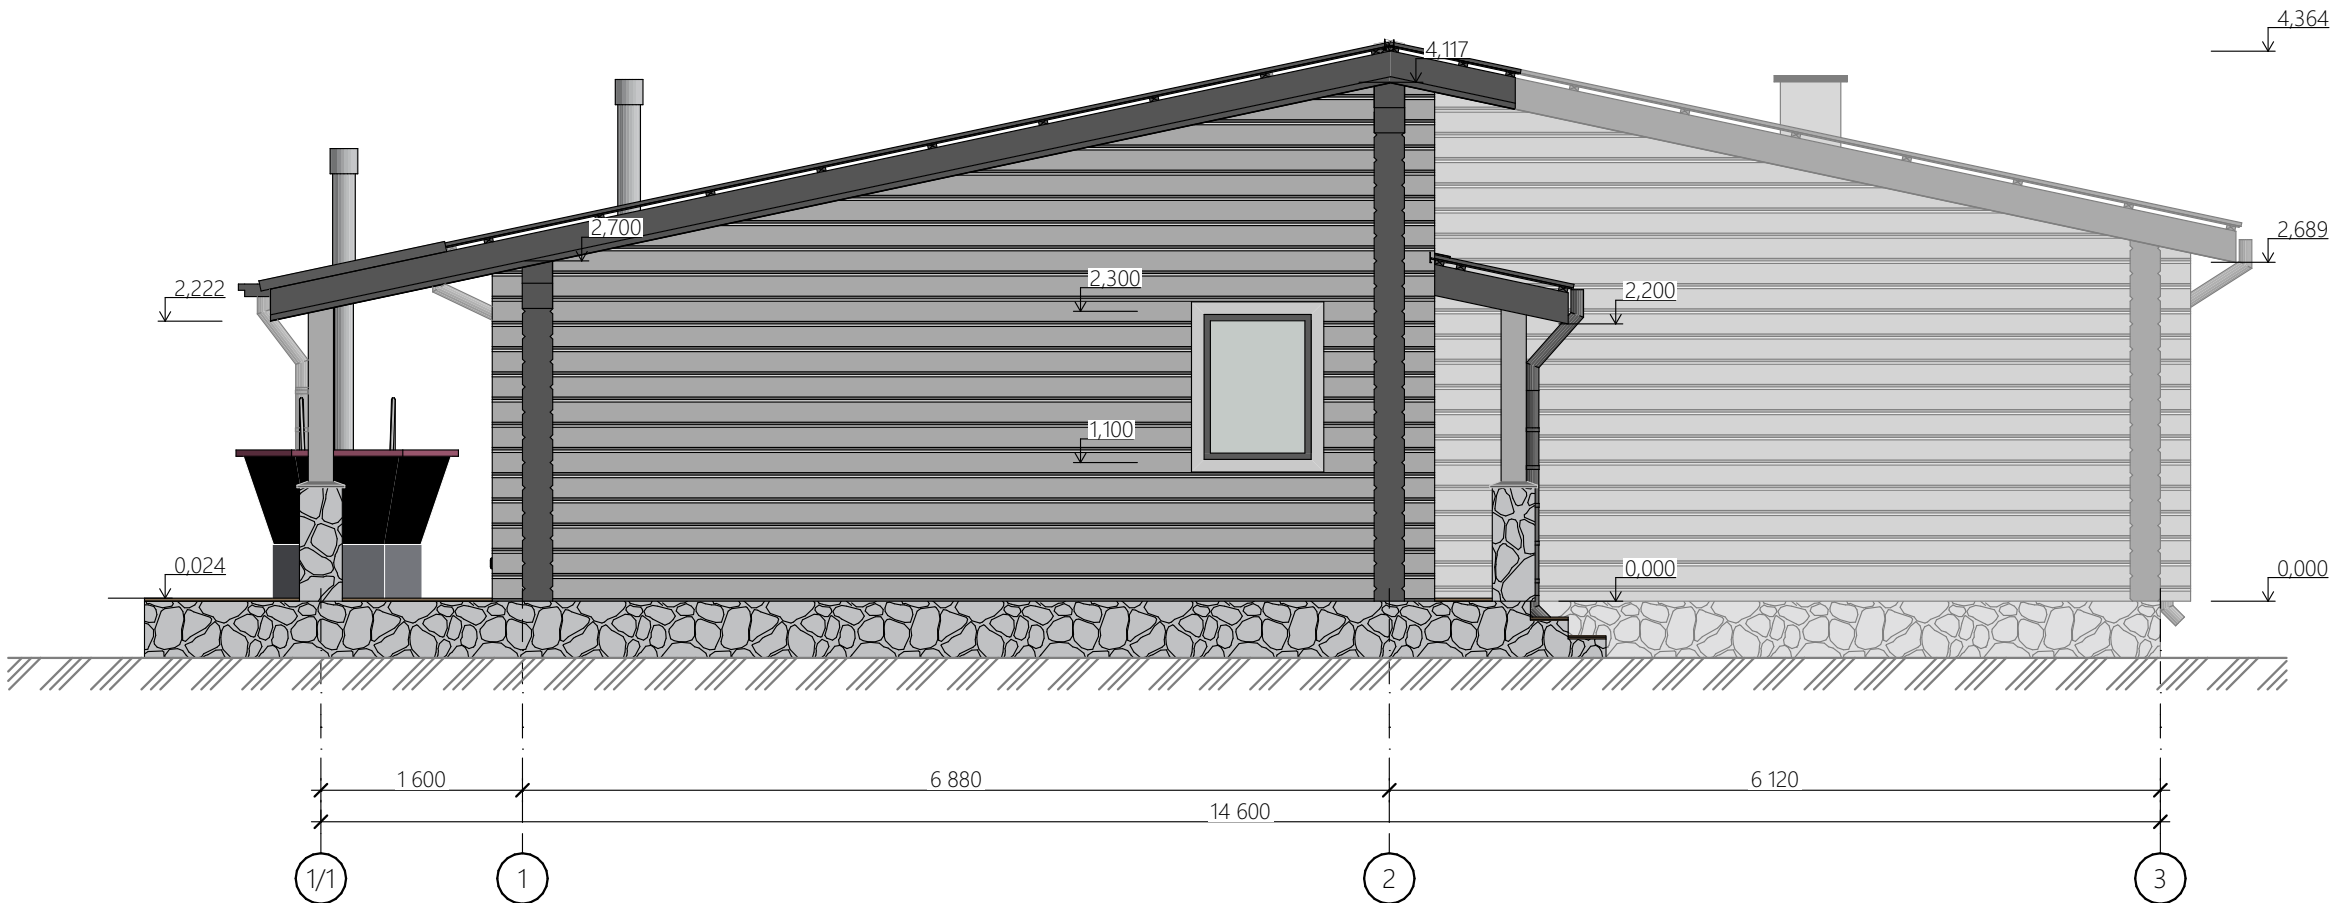


#Название Организации

Лист

26

Согласовано

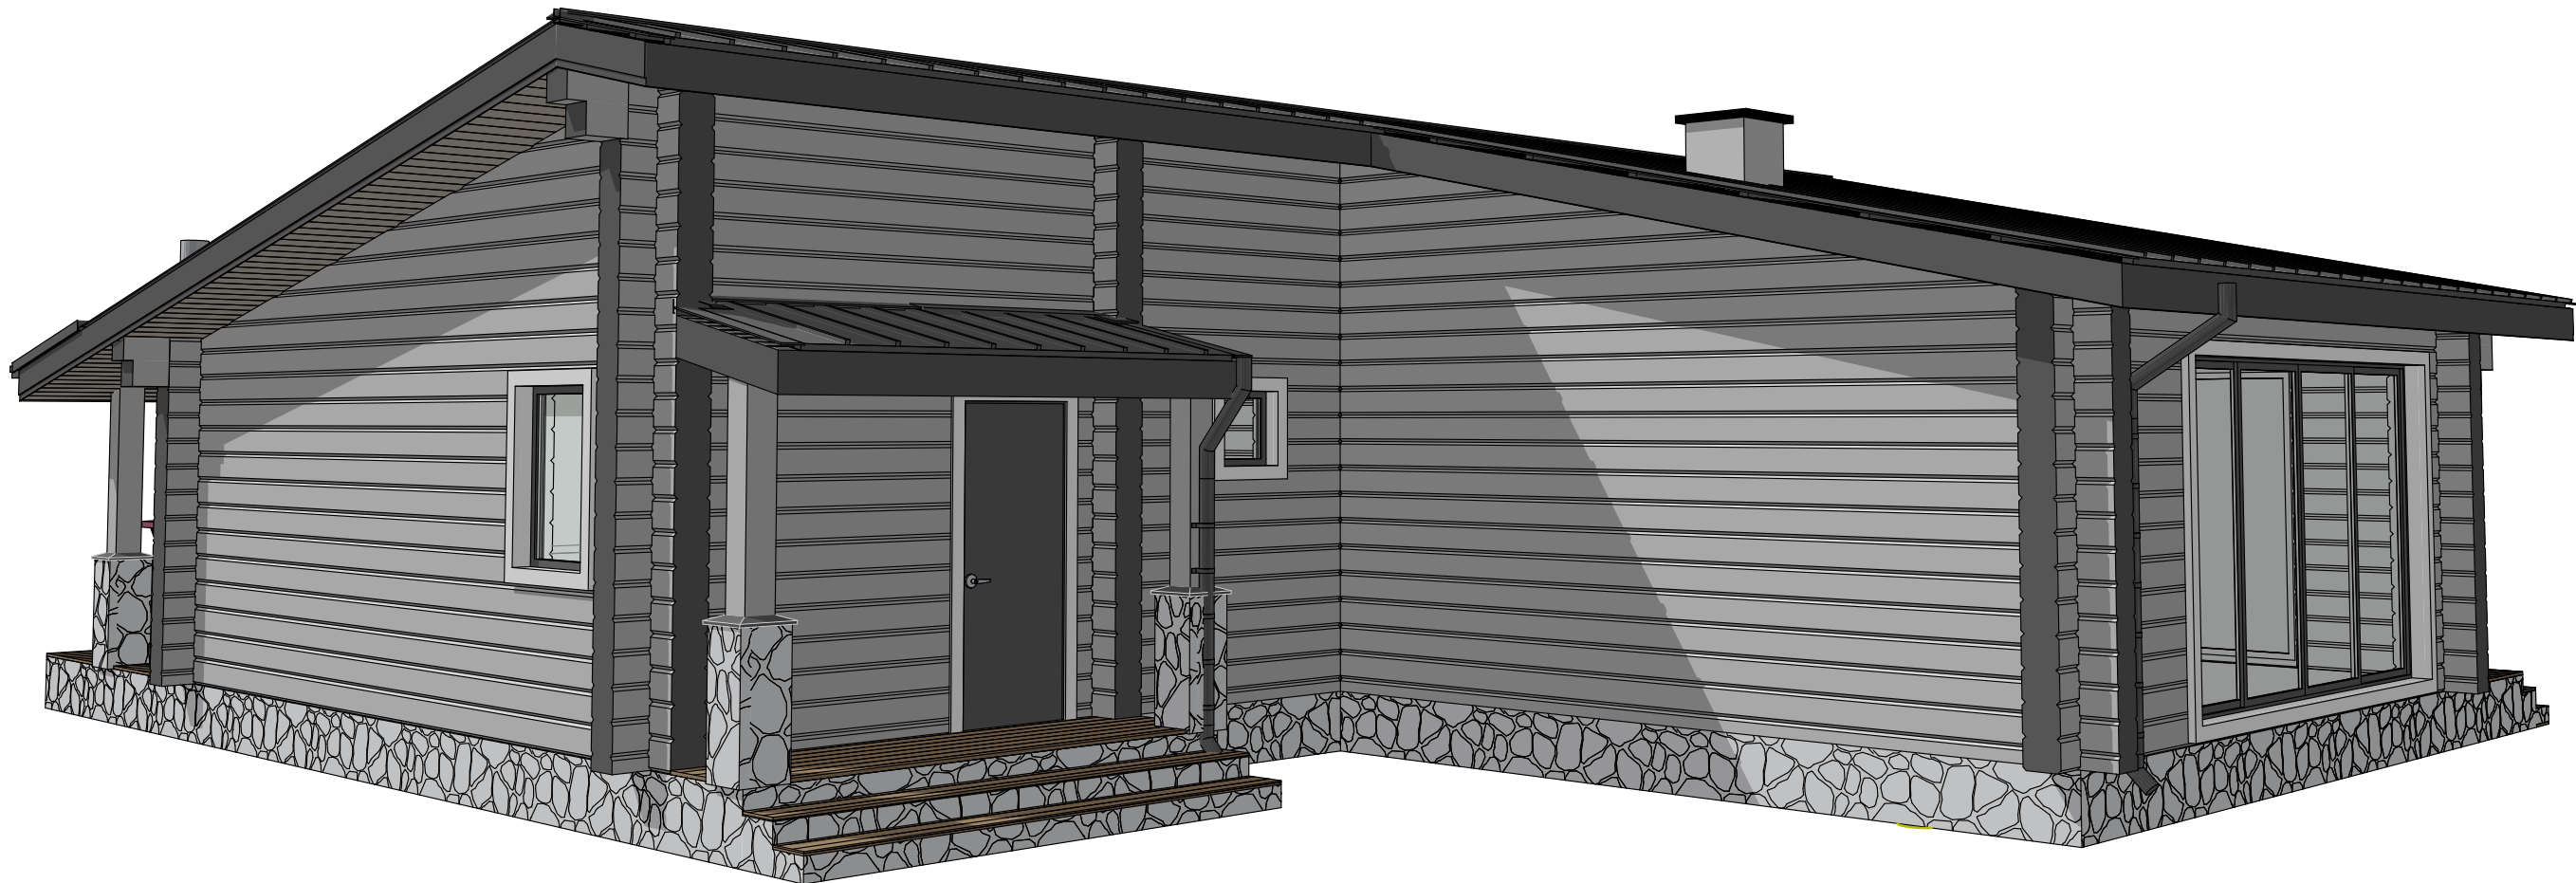

И.нв. № подл.

Подп. и дата

Взам. инв. №

Лист	Изм.	№ Докум.	Подп.	Дата

Адрес:

Аксометрия №2

#Название Организации

Согласовано

Взам. инв. №

Подп. и дата

Инв. № подл.



Лист	Изм.	№ Докум.	Подп.	Дата

Адрес:

Визуализация №1

#Название Организации

Согласовано

Изм. № подл.	Подп. и дата	Взам. инв. №



Лист	Изм.	№ Докум.	Подп.	Дата

Адрес:

Визуализация №2

#Название Организации

Согласовано

Взам. инв. №

Подп. и дата

Инв. № подл.



Лист	Изм.	№ Докум.	Подп.	Дата

Адрес:

Визуализация №3

#Название Организации

Согласовано

Взам. инв. №

Подп. и дата

Инв. № подл.



Лист	Изм.	№ Докум.	Подп.	Дата

Адрес:

Визуализация №4

#Название Организации

Согласовано

Взам. инв. №

Подп. и дата

Инв. № подл.



Лист	Изм.	№ Докум.	Подп.	Дата

Адрес:

Визуализация №5

#Название Организации

Согласовано

Взам. инв. №

Подп. и дата

Инв. № подл.



Лист	Изм.	№ Докум.	Подп.	Дата

Адрес:

Визуализация №6

#Название Организации