


ARCHITECTURE/
CONSTRUCTION



Название:
Разработал:
-
Принял:
-
г. Москва

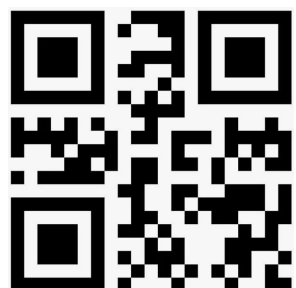

Согласовано				
И.нв. № подл.	Подп. и дата	Взам. инв. №		

Лист	Наименование	Примечание
1	Титульный	
2	Ведомость чертежей	
3	Пояснительная записка	
4	СПОЗУ	
5	Маркировочный план	
6	Размерный план	
7	План расстановки мебели и оборудования	
8	Зд-разрез	
9	План покрытия пола	
10	Пироги пола	
11	План теплого пола	
12	План покрытия стен	
13	Пироги стен	
14	План размещения розеток	
15	План размещения светильников и выключателей	
16	План крыши	
17	Ведомость оконных проемов	
18	Ведомость дверных проемов	
19	Разрез 1-1	
20	Разрез 2-2	
21	Фасад 1-5	
22	Фасад А-В	
23	Аксонометрия №1	
24	Фасад 5-1	
25	Фасад В-А	
26	Аксонометрия №2	
27	Визуализация	
28	Визуализация	
29	Визуализация	
30	Визуализация	
31	Визуализация	
32	Визуализация	
33	Визуализация	
34	Визуализация	

В основу архитектурно-планировочных решений положены требования технологических заданий и требования норм и правил строительного проектирования, действующих на территории РФ.

Основные параметры и требования разработаны на основании пожеланий и требований заказчика.

Архитектурные решения приняты в соответствии со следующими нормативными документами:

- Градостроительный кодекс российской федерации.
- Земельного Кодекса Российской Федерации.
- Федеральный закон от 22.07.2008 N 123 - ФЗ (ред. от 29.07.2017)"Технический регламент о требованиях пожарной безопасности.
- Федеральный закон № 384 - ФЗ «Технический регламент о безопасности зданий и сооружений».
- ГОСТ Р 21.1101-2013.«Основные требования к проектной и рабочей документации».
- Постановление правительства РФ от 16.02.2008 № 87 «Положение о составе разделов проектной документации и требованиях к их содержанию».
- СП 42.13330.2011 «Градостроительство. Планировка и застройка городских и сельских поселений».
- СП 131.13330.2018 «СНиП 23-01-99* Строительная климатология».
- СП 20.13330.2016 «СНиП 2.01.07-85* Нагрузки и воздействия».
- СП 22.13330.2016 «СНиП 2.02.01-83* Основания зданий и сооружений».
- СП 70.13330.2012 (с изменениями №1) «СНиП 3.03.01-87 Несущие и ограждающие конструкции».
- СП 64.13330.2017 «СНиП II-25-80 Деревянные конструкции».
- СП 17.13330.2017 «СНиП II-26-76 Кровли».
- СП 29.13330.2011 «СНиП 2.03.13-88 Полы».
- СП 28.13330.2017 «СНиП 2.03.11-85 Защита строительных конструкций от коррозии».
- СП 50.13330.2012 «СНиП 23-02-2003 Тепловая защита зданий».

Согласовано				
И.нв. № подл.	Подп. и дата	Взам. инв. №		

1. Общие данные:

1.1. Архитектурный проект разработан на основании требований и пожеланий заказчика.

Тип строения	Баня
Относительная отм. ±0.000	ур. верха фундаментной плиты
Общая площадь застройки, м2	94,60
Габаритные размеры каркаса здания	7,7х15 м
Этажность	1 этаж
Конструктивная схема	Деревянный каркас

2. Конструктивные решения:

2.1. Рабочие чертежи разработаны на основании задания на проектирование

Полезная нагрузка на перекрытие	150 кгс/м2	-
Нормативная глубина промерзания	1,2м	СП 22.13330.2016 СП 131.13330.2020
Нормативное ветровое давление	I район (23кгс/м2)	СП 22.13330.2016
Нормативный вес снегового покрова	III район (150кгс/м2)	СП 22.13330.2016
Температура наиболее холодной пятидневки	-29°С	СП 131.13330.2020

2.2. Конструктивное строение представляет собой сооружение:

- на свайном фундаменте
- несущими стенами из деревянного каркаса
- односкатной кровлей по деревянным стропилам

2.3. Необходимо осуществлять технический надзор за производством строительных работ. Данные по проведённым работам необходимо систематически вносить в журнал работ.

По каждому из этапов работ необходимо осуществлять входной контроль материалов и вести приёмку.

Фундамент	Ж/б монолитная плита (h=250мм)
Несущие конструкции	деревянный каркас (140х45мм)
Стропильная система	строганая доска (190х45мм)
Тип крыши	односкатная
Покрытие кровли	фальцевые листы

2.4. Все деревянные конструкции обработать огне-биозащитными септиками в соответствии со СП 28.13330.2017 "Защита строительных конструкций от коррозии".

2.5. Кровельные работы выполнять в соответствии с требованиями фирмы производителя.

2.6. Все работы вести в строгом соответствии с требованиями СНиП 12.03.2001 "Безопасность труда в строительстве".

2.7. При выполнении всех работ строго соблюдать меры противопожарной безопасности.

2.8. Возможна замена материалов аналогами.

*Решения, принятые в проекте и отображенные в чертежах, соответствуют требованиям экологических, санитарно - гигиенических, противопожарных и других норм, действующих на территории Российской Федерации, и обеспечивают безопасную для жизни и здоровья людей эксплуатацию объекта при соблюдении предусмотренных рабочих чертежей и мероприятий.

Условные обозначения:



- Граница участка
- Граница застройки участка
- 1

- Существующий индивидуальный жилой дом
- 2


- Банный комплекс (проектируемая постройка)

Технико-экономические показатели

Наименование	Площадь, м²
Площадь участка (по кадастровой документации)	1266,00
Общая площадь застройки (баня+ИЖД)	220,35
Площадь участка (по топографической съемке)	1179,56
Площадь застройки (баня)	125,75
Площадь застройки (ИЖД)	94,60

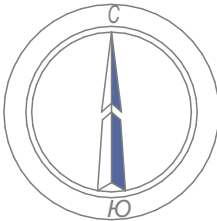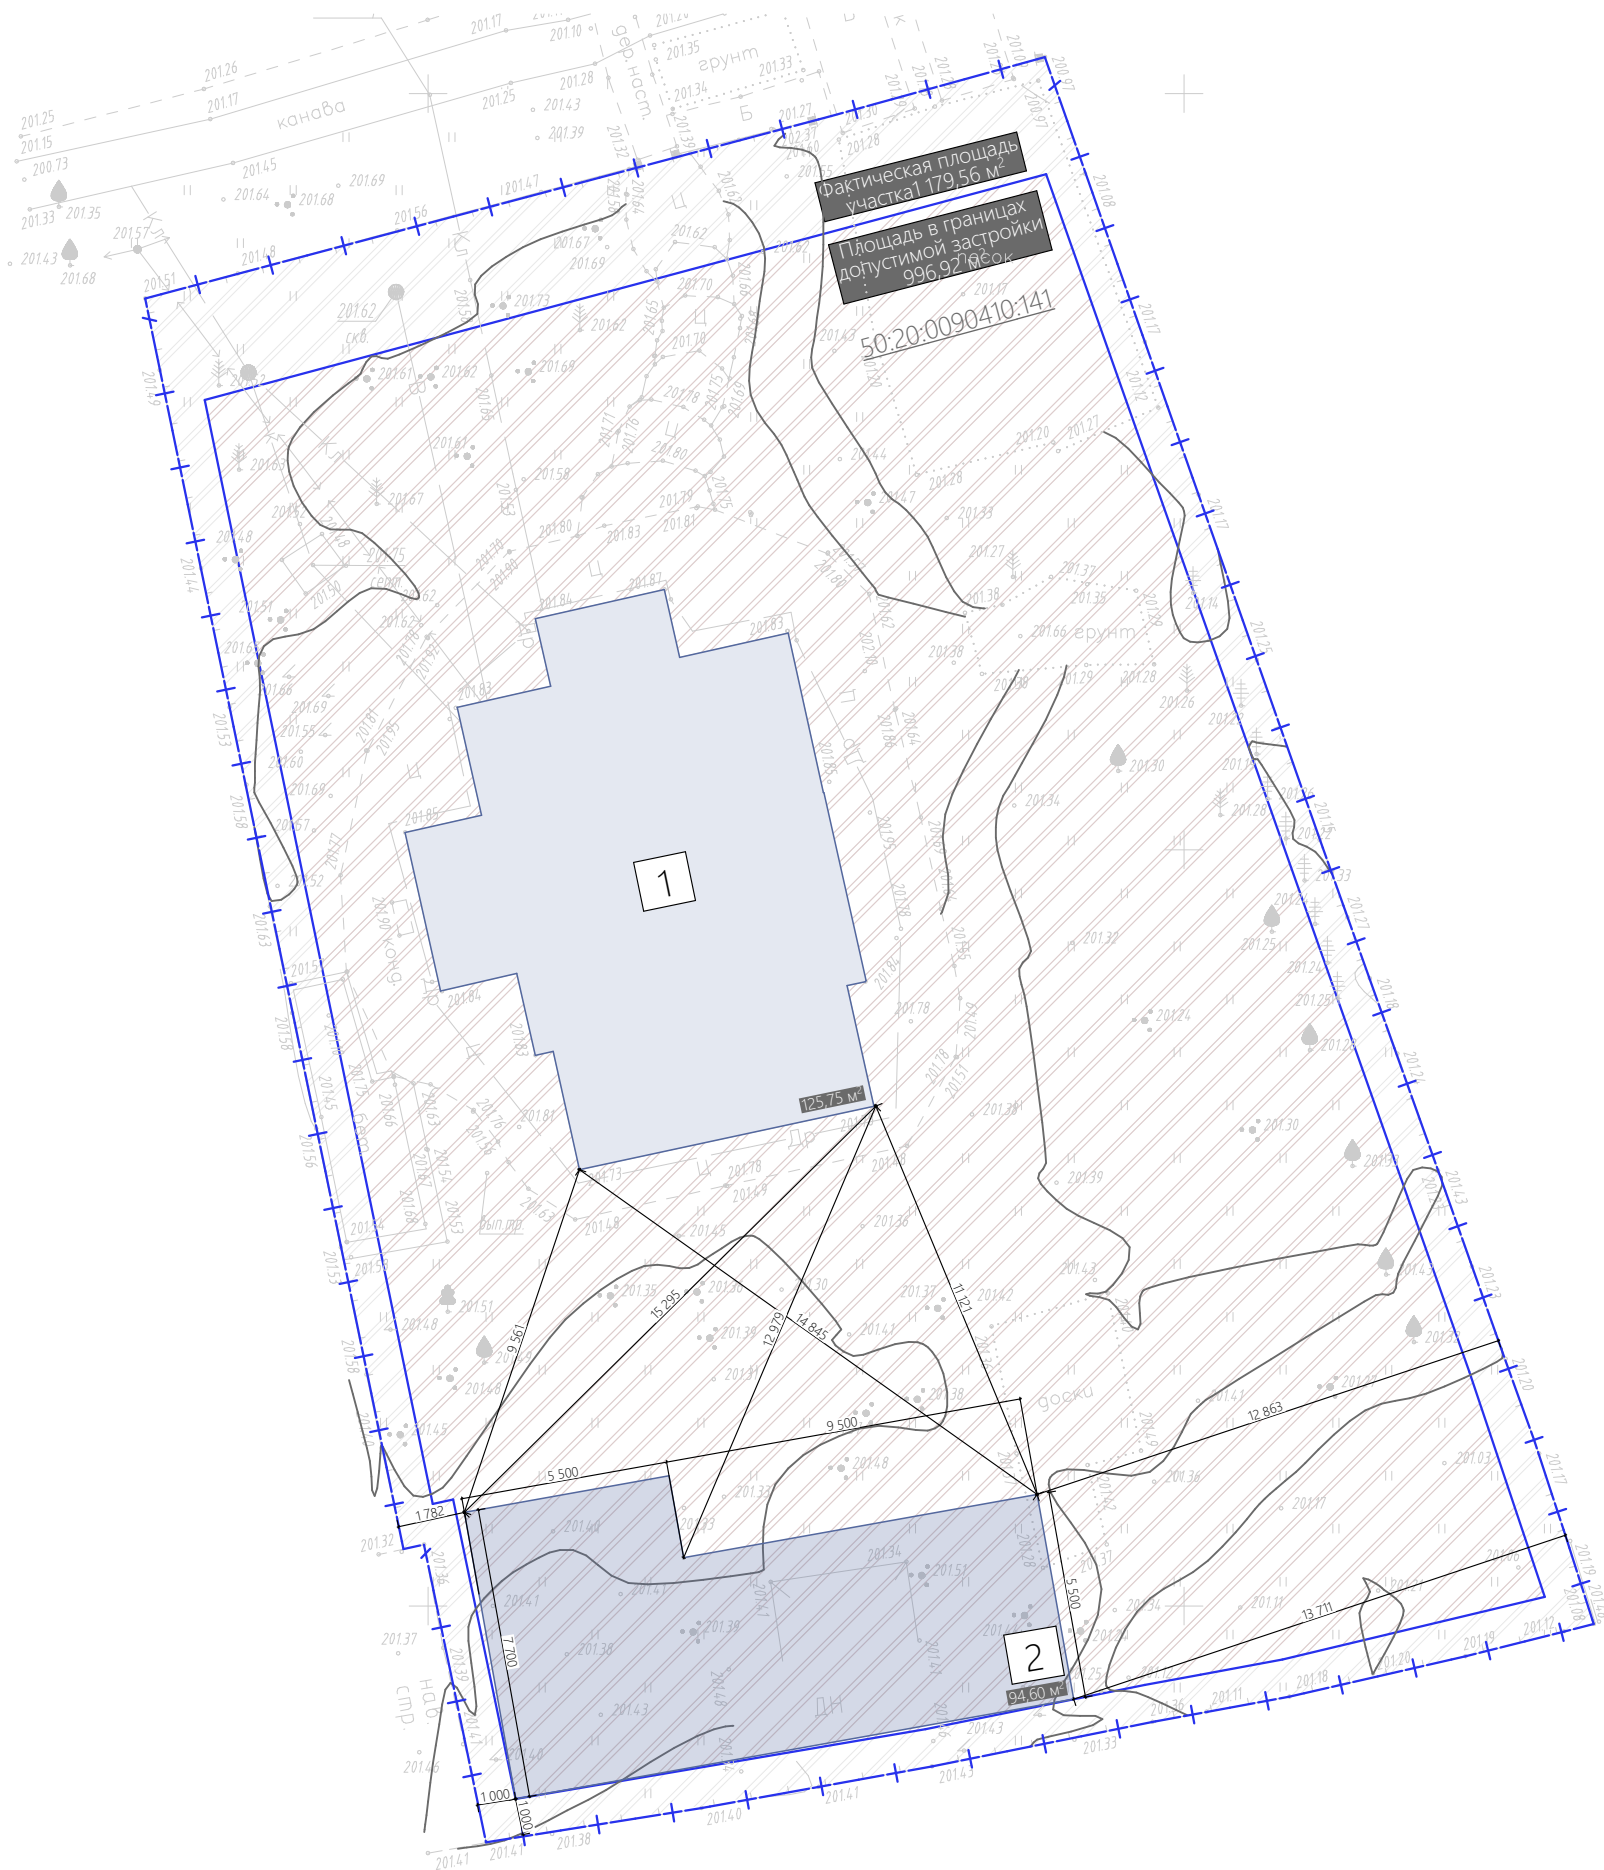

Согласовано				
Изм. № подл.	Взам. инв. №	Подп. и дата		

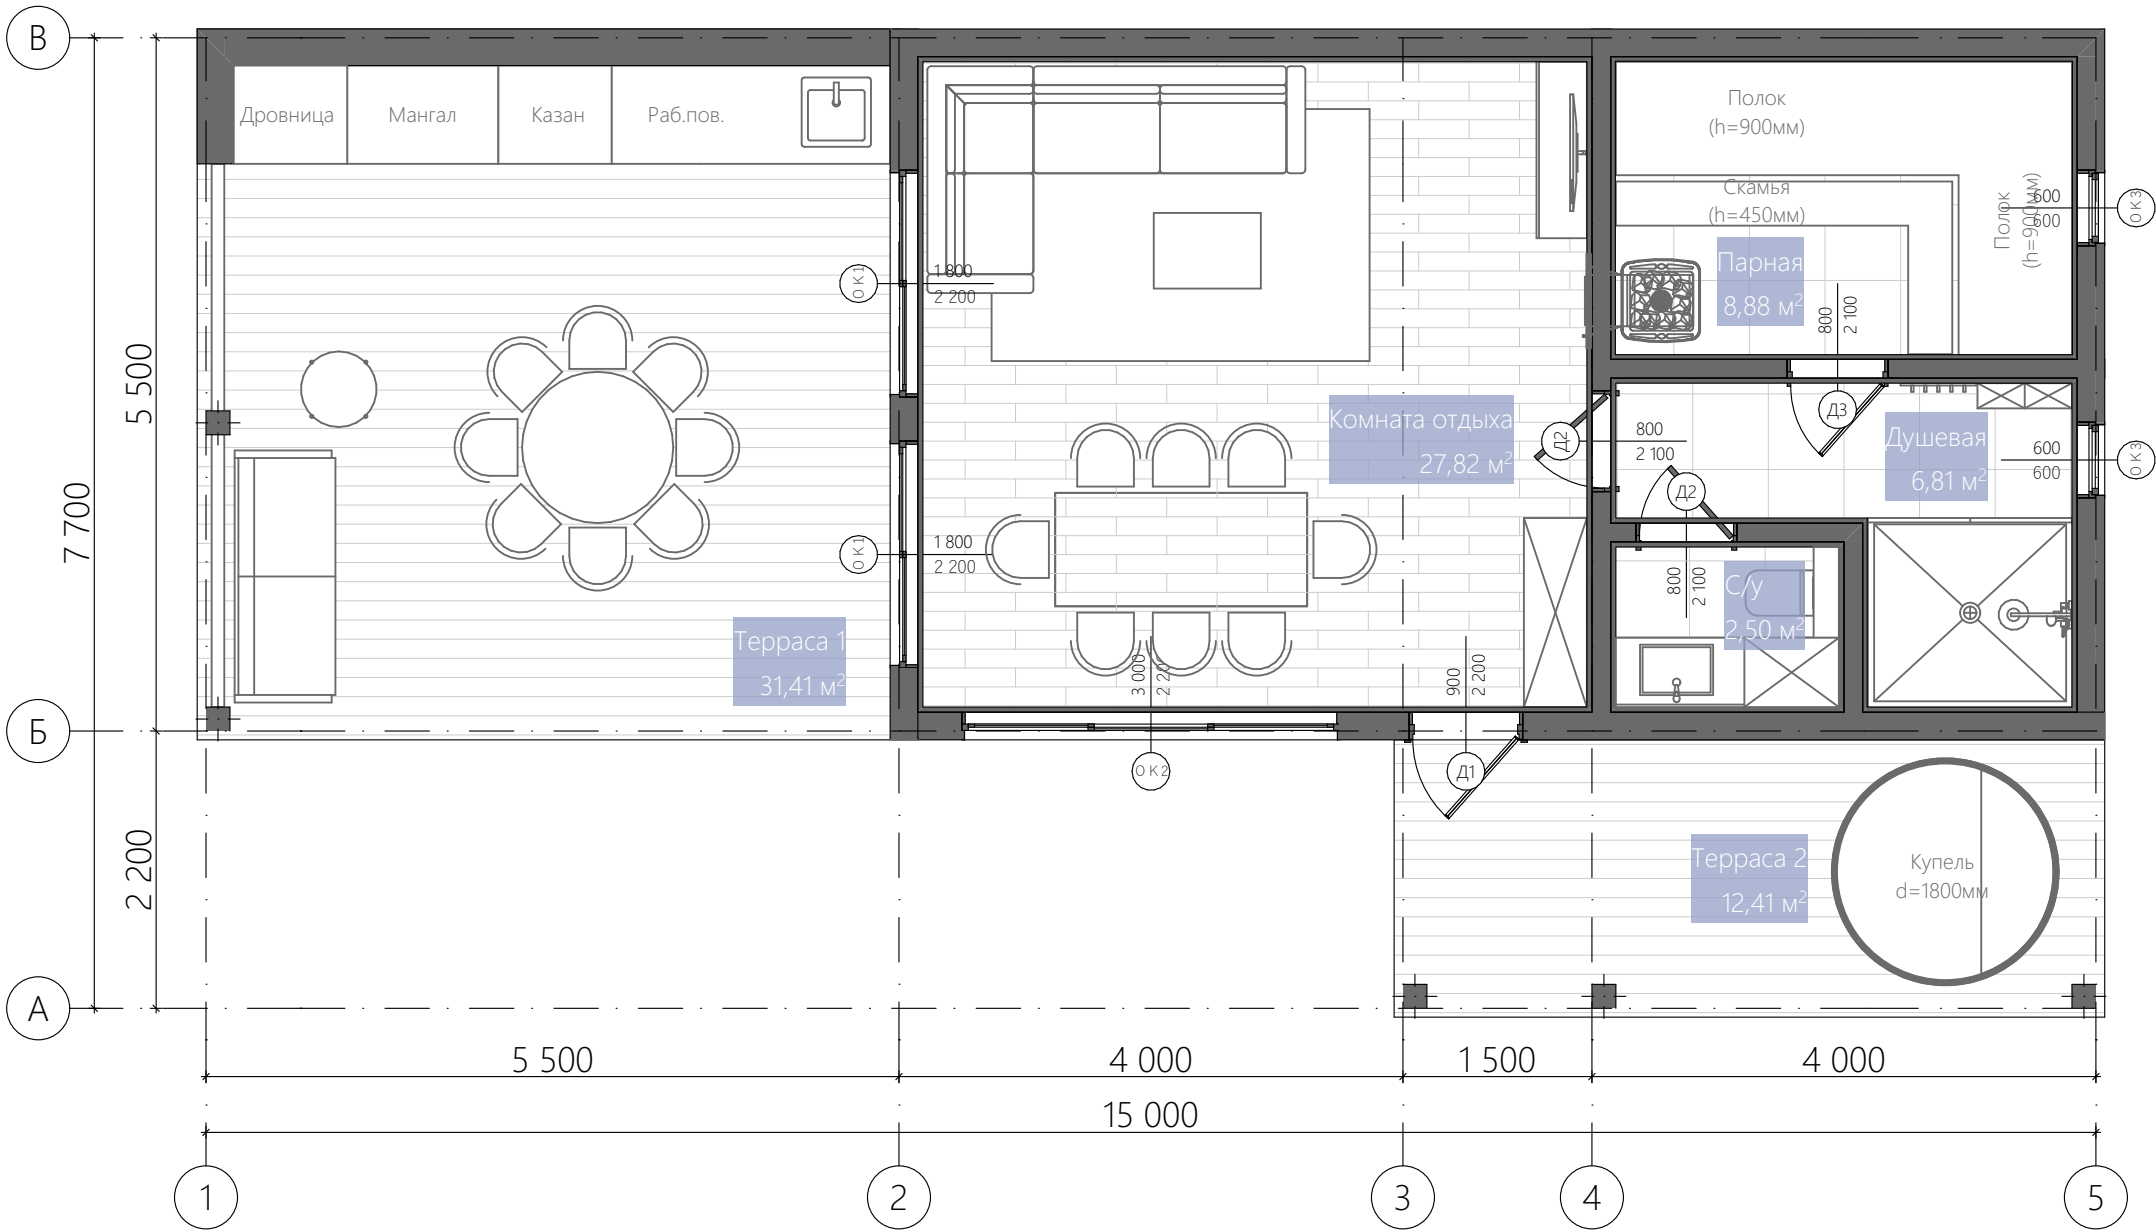

Экспликация помещений

№	Наименование	Площадь, кв.м.
1	Терраса 1	31,41
2	Терраса 2	12,41
3	Комната отдыха	27,82
4	Парная	8,88
5	Душевая	6,81
6	С/у	2,50
		89,83 м²

Наименование	Площадь, кв.м.
Площадь застройки	94,60

Примечание:


1. Вся индивидуальная мебель выполняется по отдельному проекту с детальной проработкой и калькуляцией. Чертежи предоставляет фирма-изготовитель столярных изделий.
2. Данный проект отдельно согласовывается с автором проекта и непосредственно с заказчиком.
3. Цветовое решение фасада и материалов отделки показаны в проекте приблизительно.
4. Количество ступеней показано условно.

Согласовано				
И-нв. № подл.	Подп. и дата	Взам. инв. №		

Лист	Изм.	№ Докум.	Подп.	Дата	Заречная улица, 46Б, село Никольское, Одинцовский городской округ, Московская область; 50:20:0090410:141

Размерный план

1:60

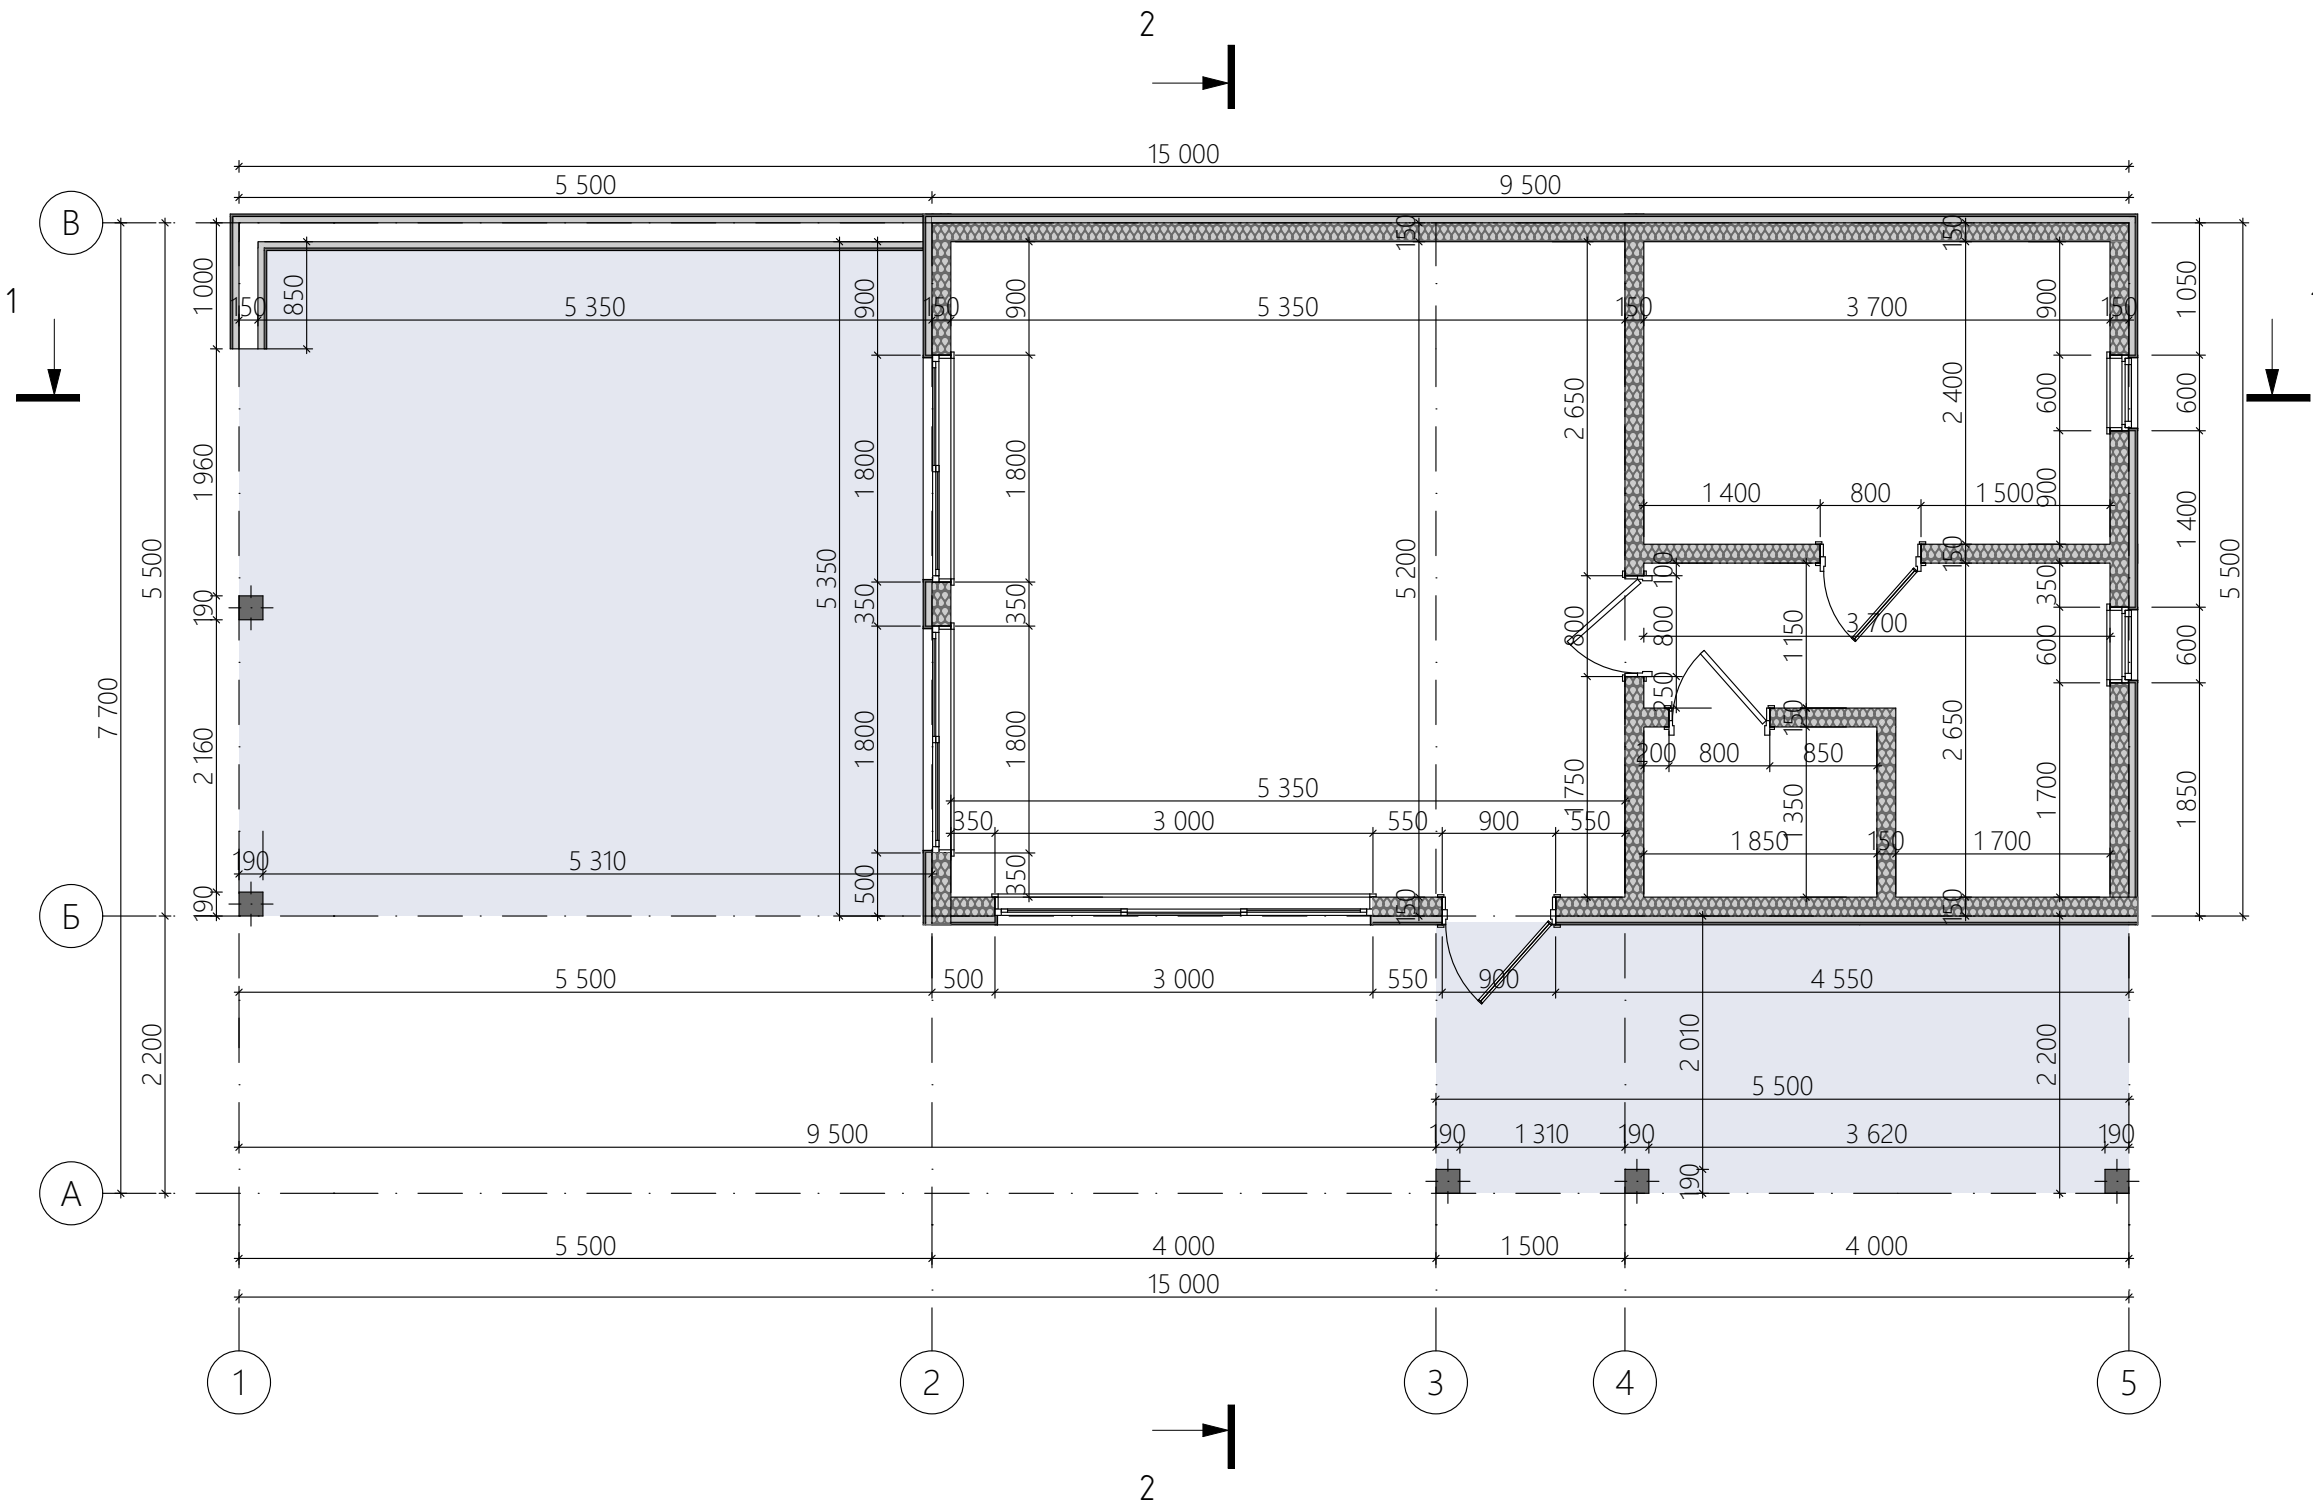

Примечание:

1. Представленные размеры указаны без учета внешней и внутренней отделки

Согласовано				
И-нв. № подл.	Подп. и дата	Взам. инв. №		

Лист	Изм.	№ Докум.	Подп.	Дата


Заречная улица, 46Б, село Никольское, Одинцовский городской округ, Московская область;
50:20:0090410:141

Размерный план

#Название Организации

План расстановки мебели и оборудования

1:60

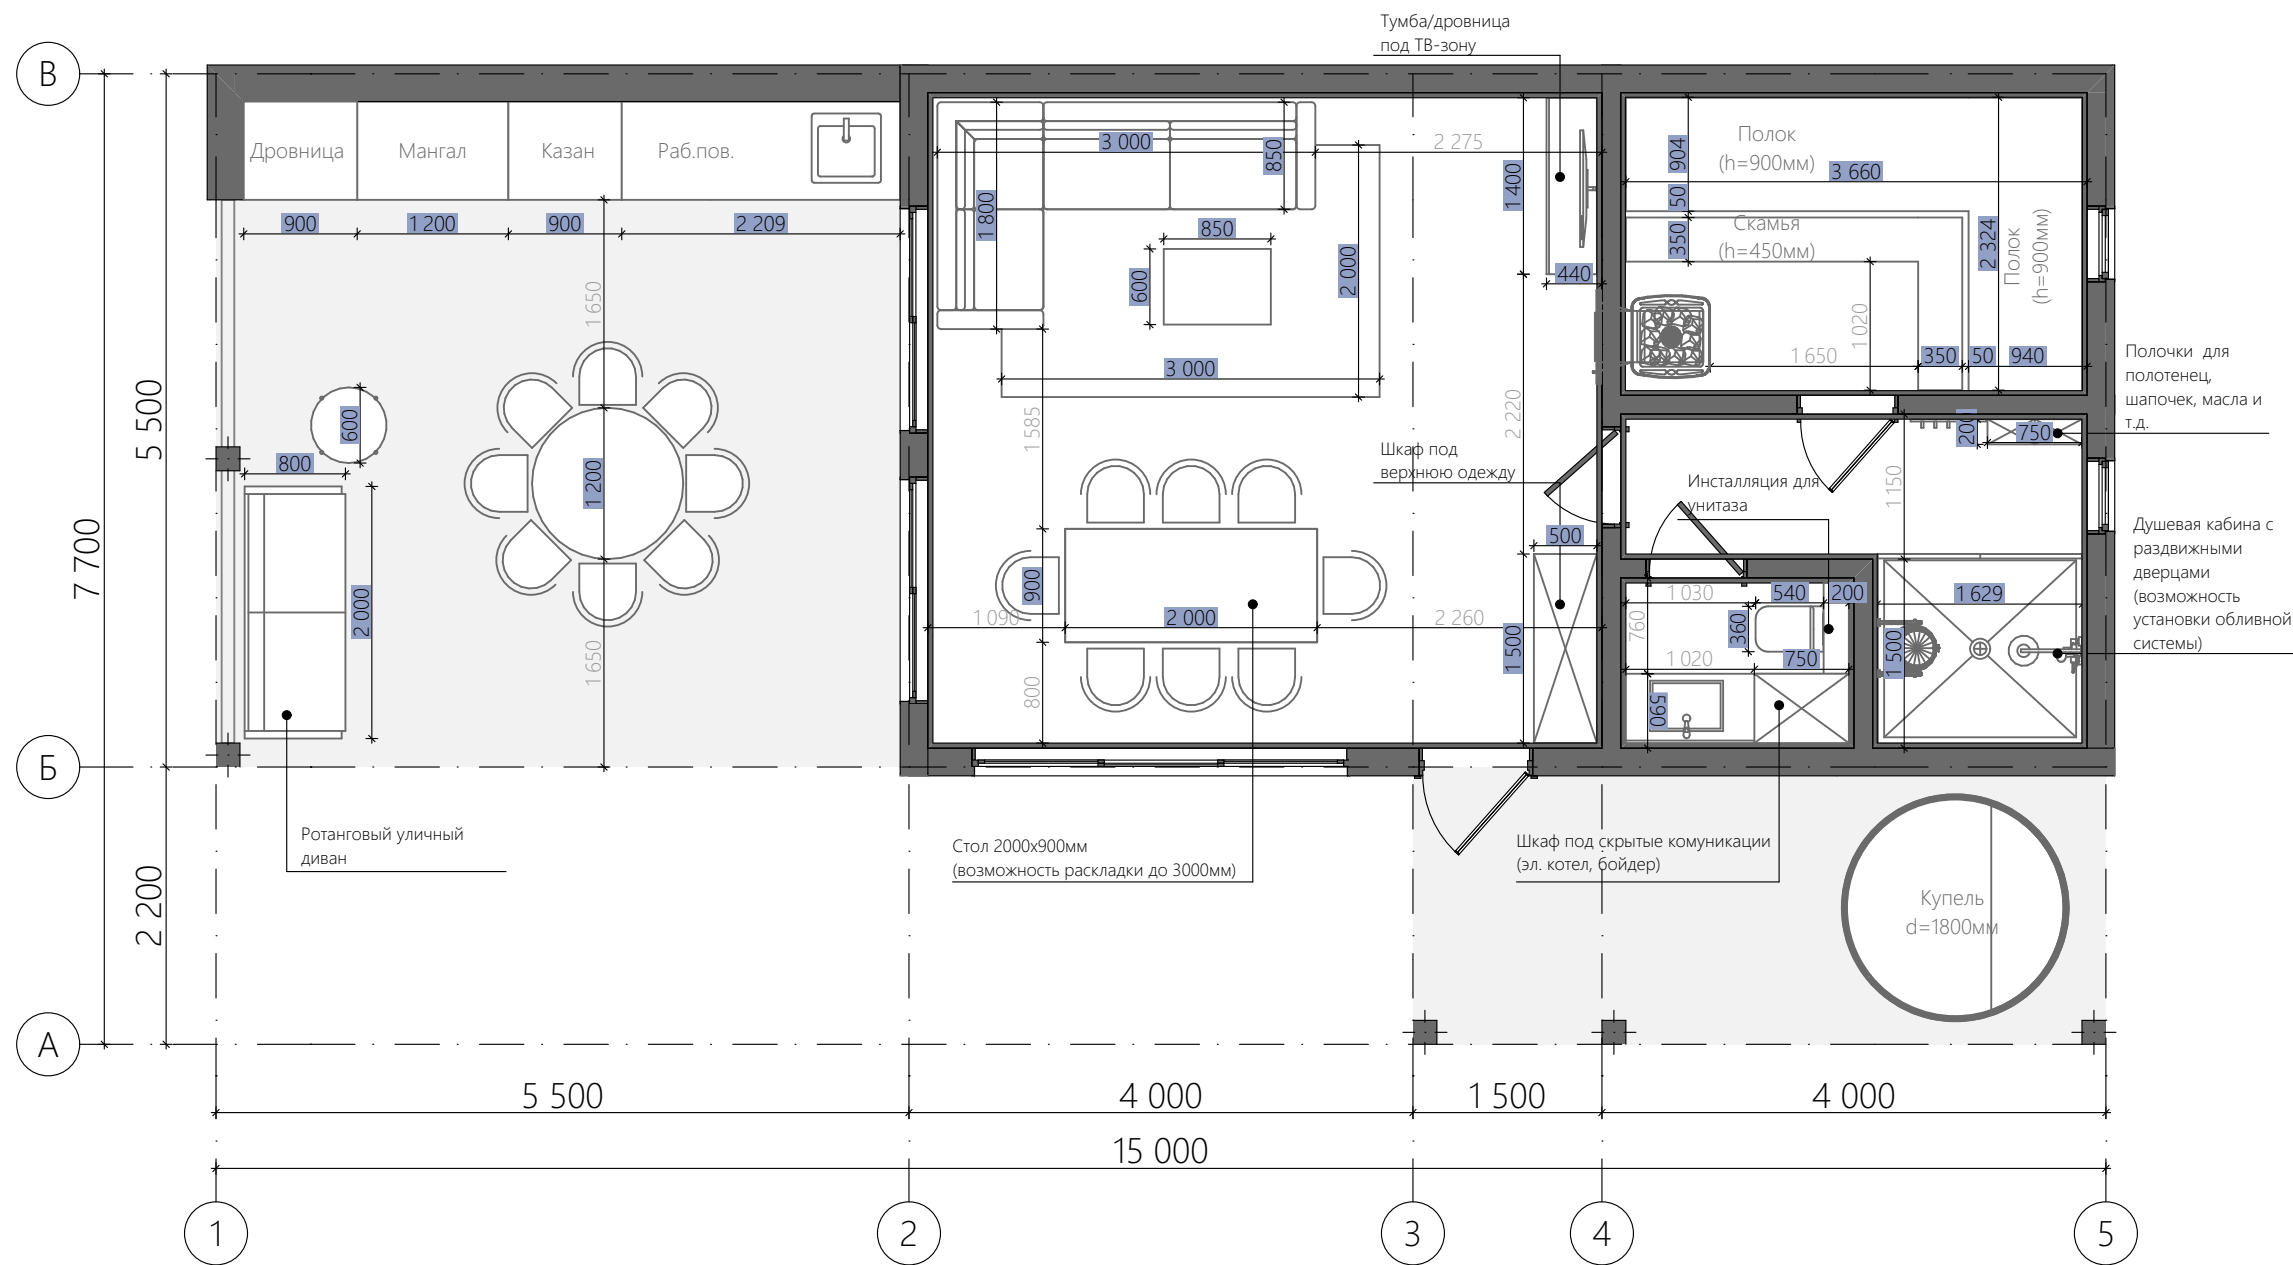

Примечание:

1. Вся индивидуальная мебель выполняется по отдельному проекту с детальной проработкой и калькуляцией. Чертежи предоставляет фирма-изготовитель столярных изделий.
2. Финальные размеры мебели и оборудования указаны ориентировочно — для точной компоновки требуется разработка дизайн-проекта.

Согласовано				
И-нв. № подл.	Взам. инв. №	Подп. и дата		

Лист	Изм.	№ Докум.	Подп.	Дата

Заречная улица, 46Б, село Никольское, Одинцовский городской округ, Московская область;
50:20:0090410:141

План расстановки мебели и оборудования


#Название Организации

Согласовано

Взам. инв. №

Подп. и дата

Инв. № подл.

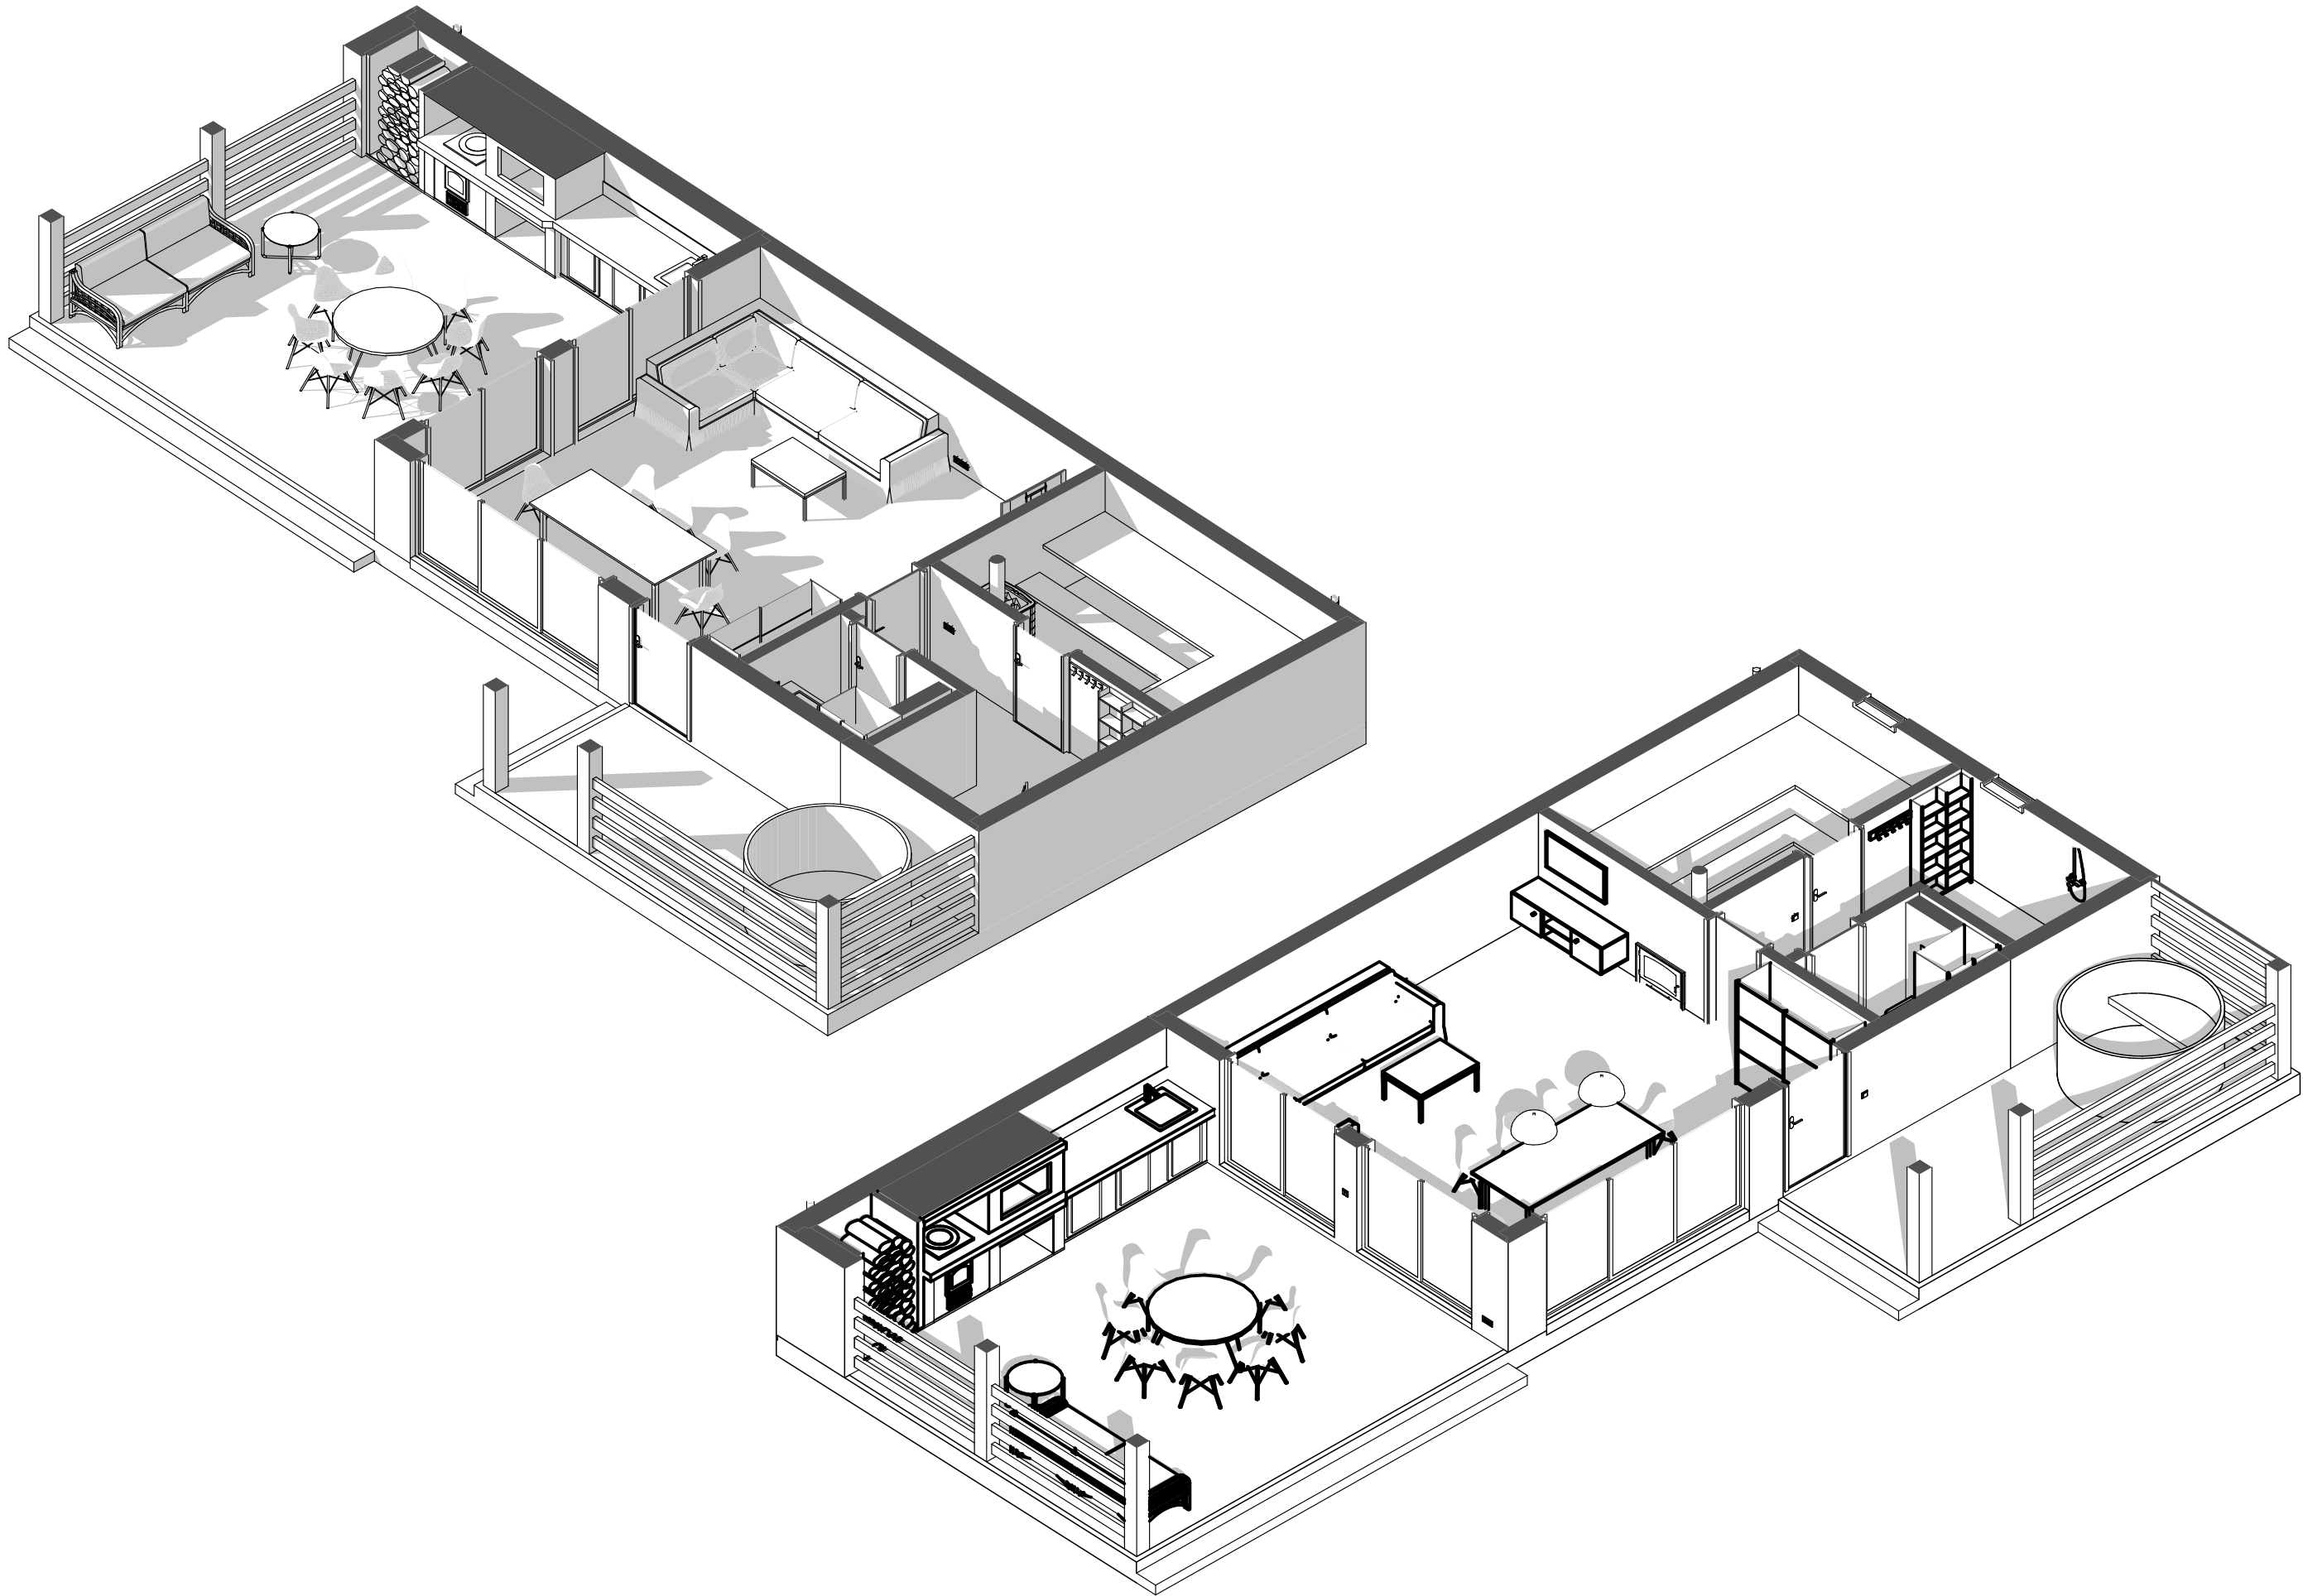

Лист	Изм.	№ Докум.	Подп.	Дата

Заречная улица, 46Б, село Никольское, Одинцовский городской округ, Московская область; 50:20:0090410:141

Зд-разрез


#Название Организации

План покрытия пола

1:60



Условные обозначения

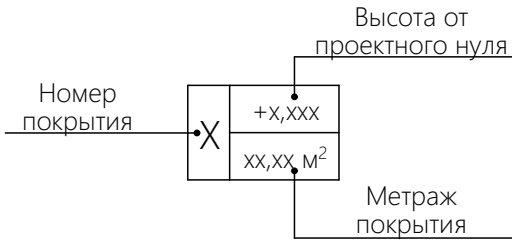

Экспликация покрытий пола

№	Наименование	Площадь, м²
1	Террасная доска	41,79
2	Кварцвинил	27,82
3	Керамогранит	18,19

Примечание:

1. Приведённые цветовые решения носят рекомендательный характер. Фактический подбор оттенков и материалов выполняется на этапе реализации с учётом наличия продукции у поставщиков и утверждения заказчиком.
2. Пирог покрытия смотреть на след. листе.

Согласовано

Взам. инв. №

Подп. и дата

Инв. № подл.

Лист	Изм.	№ Докум.	Подп.	Дата

Заречная улица, 46Б, село Никольское, Одинцовский городской округ, Московская область;
50:20:0090410:141

План покрытия пола

#Название Организации


Пироги пола

This image shows a single sheet of white paper with horizontal blue or grey ruling lines. A vertical margin line is positioned on the left side, creating a narrow left margin. The paper appears to be part of a binder or folder, as evidenced by the dark binding material visible along the top and right edges. The overall appearance is clean and unused.


10

План теплого пола

1:60

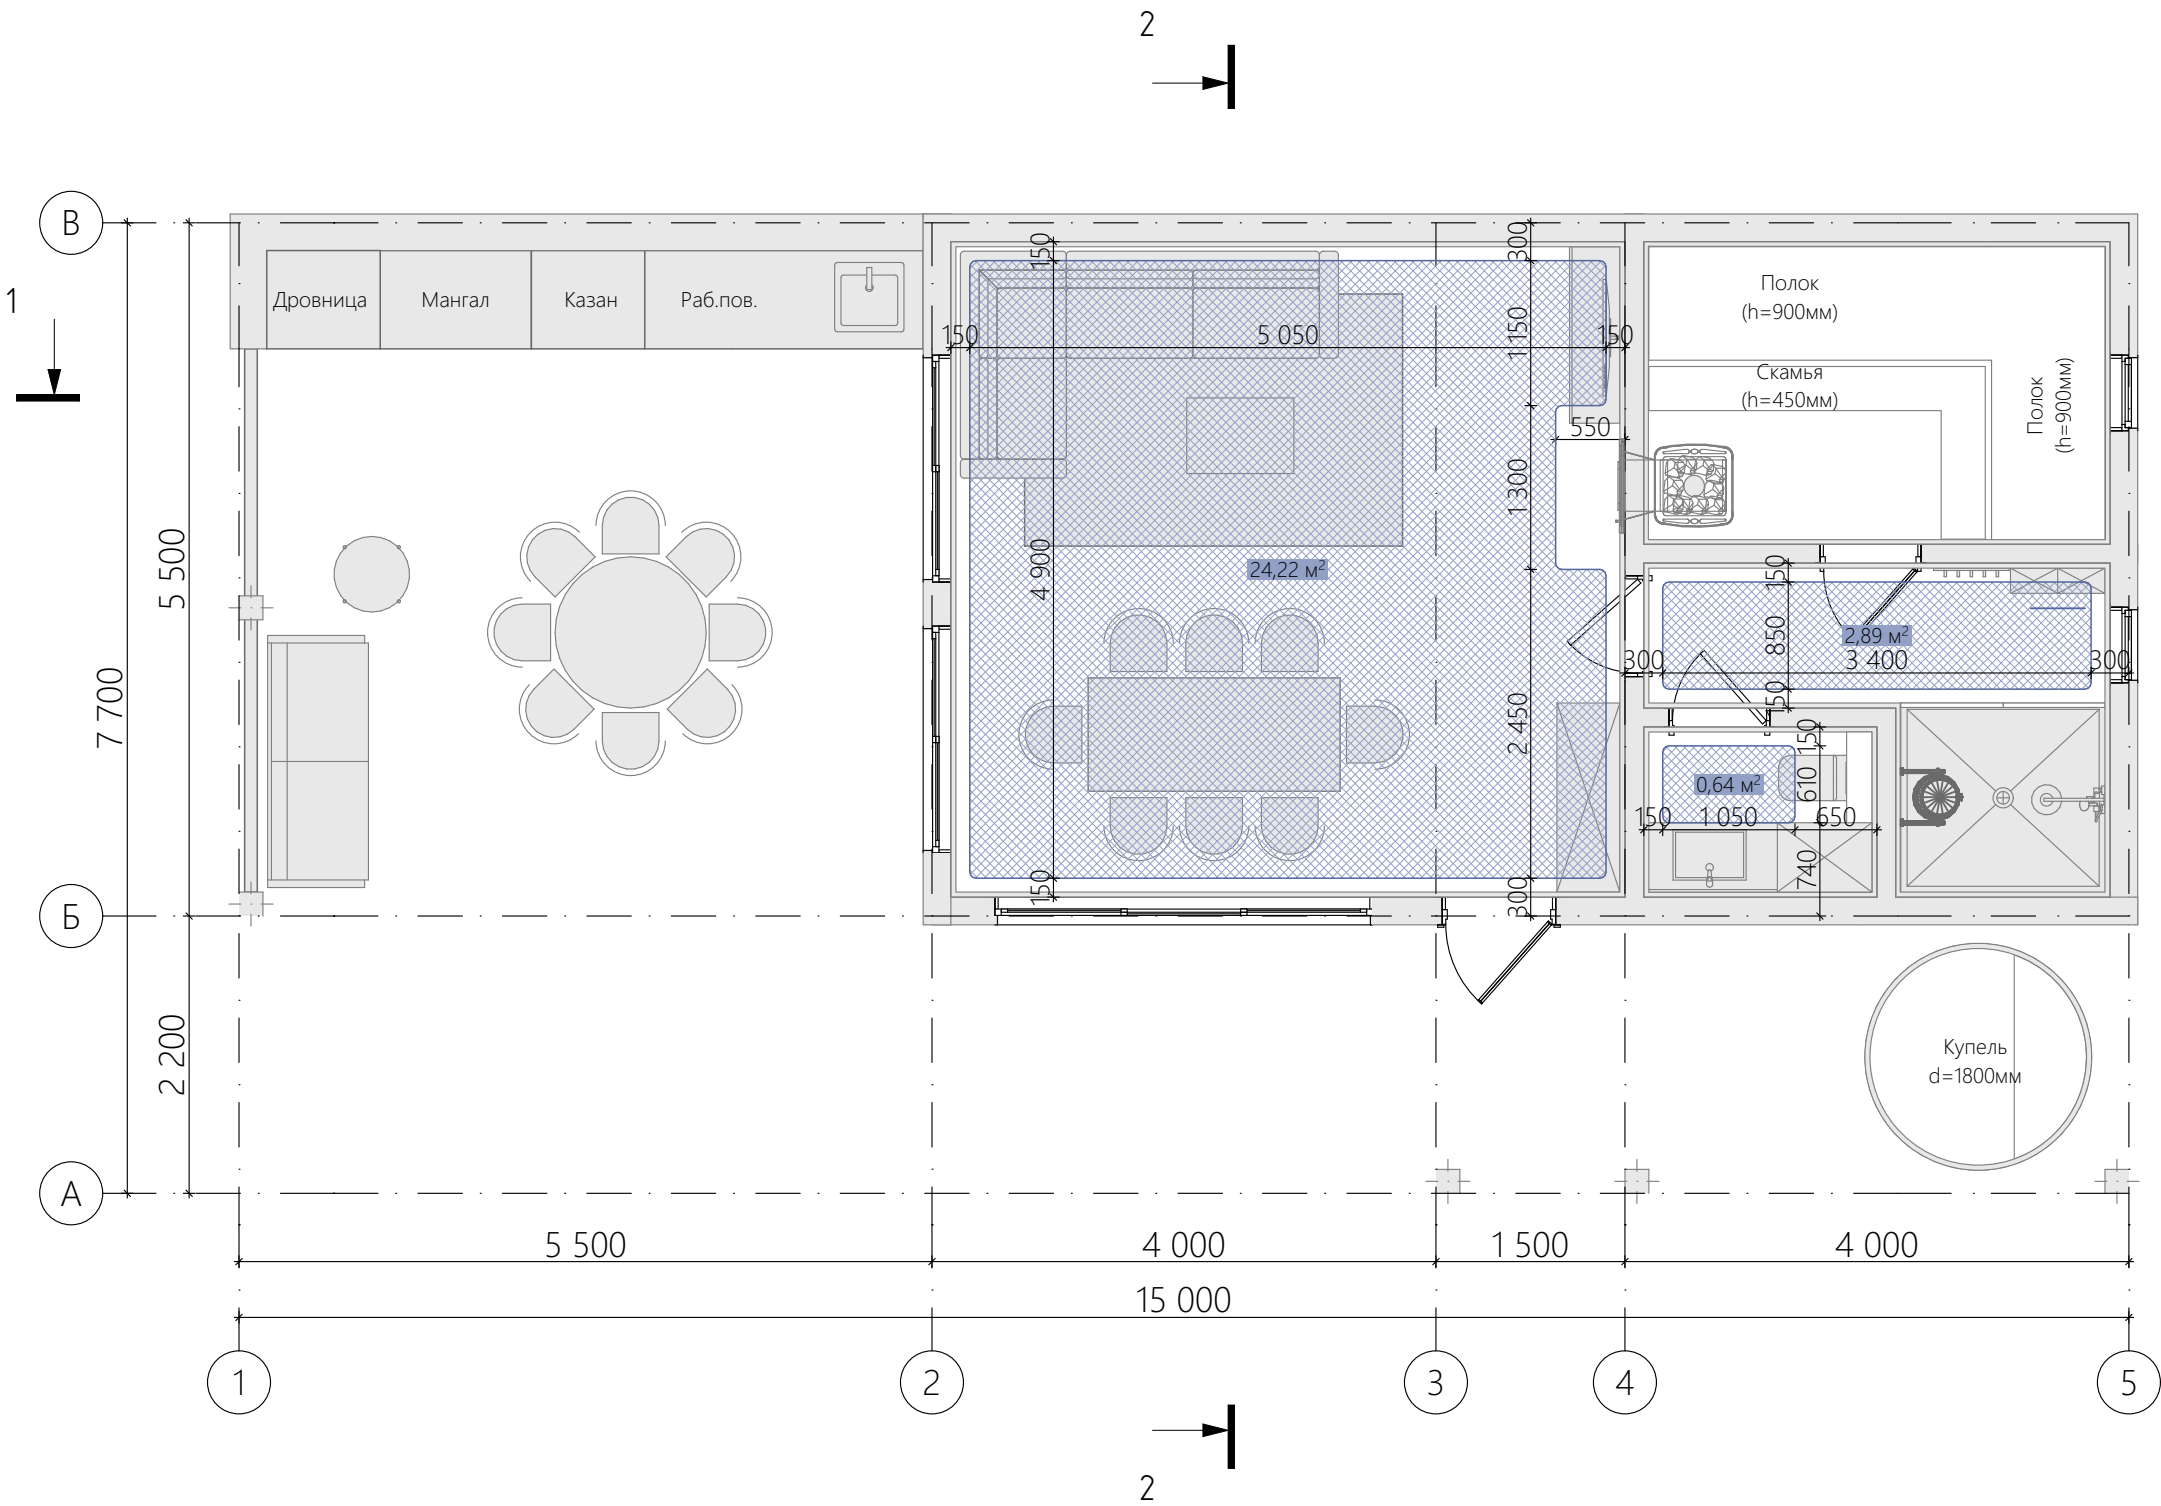

Условные обозначения

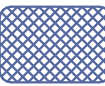 - Контур устройства теплого пола

Экспликация теплого пола

Наименование зоны	Площадь, м2
Душевая	2,89
Комната отдыха	24,22
С/у	0,64
27,75 м²	

Примечание:

1. Отображение носит схематичный характер. Фактическая реализация выполняется в соответствии с детальными проектными решениями инженерных сетей.

Согласовано

Взам. инв. №

Подп. и дата

Инв. № подл.

Лист	Изм.	№ Докум.	Подп.	Дата


Заречная улица, 46Б, село Никольское, Одинцовский городской округ, Московская область;
50:20:0090410:141

План теплого пола

#Название Организации

План покрытия стен

1:60

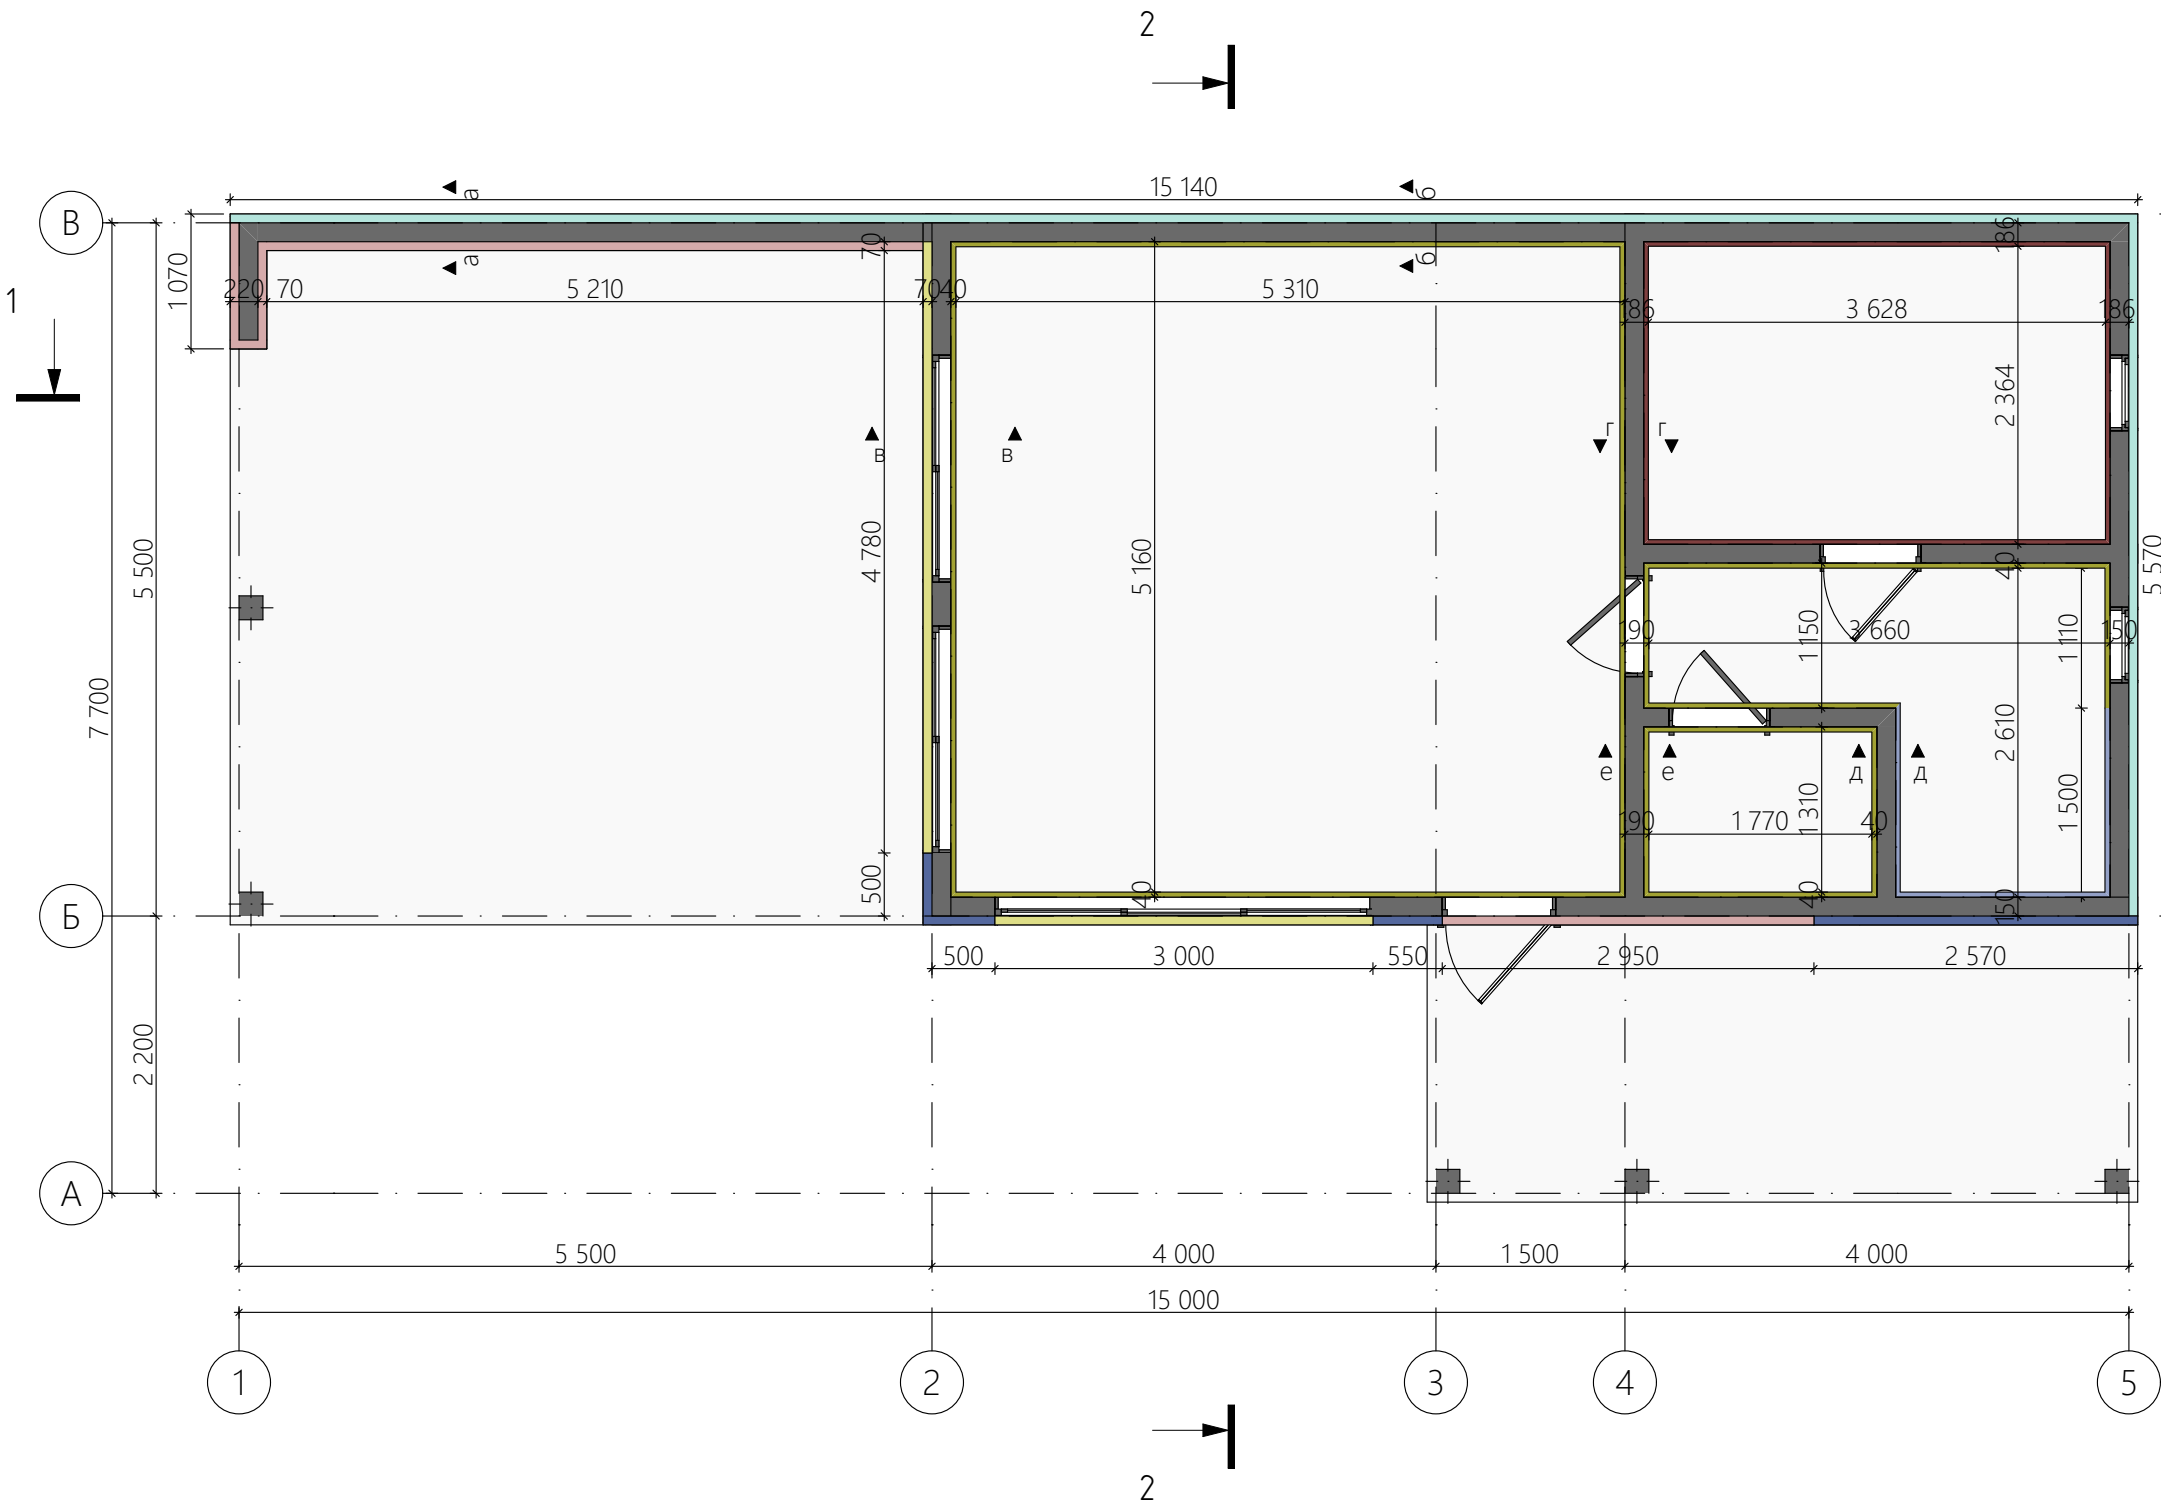

Экспликация покрытий стен

№	Наименование	Условное обозначение
1	Каньон (20мм)	
2	Фиброцементный сайдинг (20мм)	
3	Фиброцементные панели (20мм)	
4	Планкен (20мм)	
5	Имитация бруса (20мм)	
6	Вагонка (16мм)	
7	Керамогранит (10мм)	


Примечание:
1. Сечение по стенам смотреть на след. листе

Согласовано				
И-нв. № подл.	Подп. и дата	Взам. инв. №		

Лист	Изм.	№ Докум.	Подп.	Дата

План размещения розеток

1:60

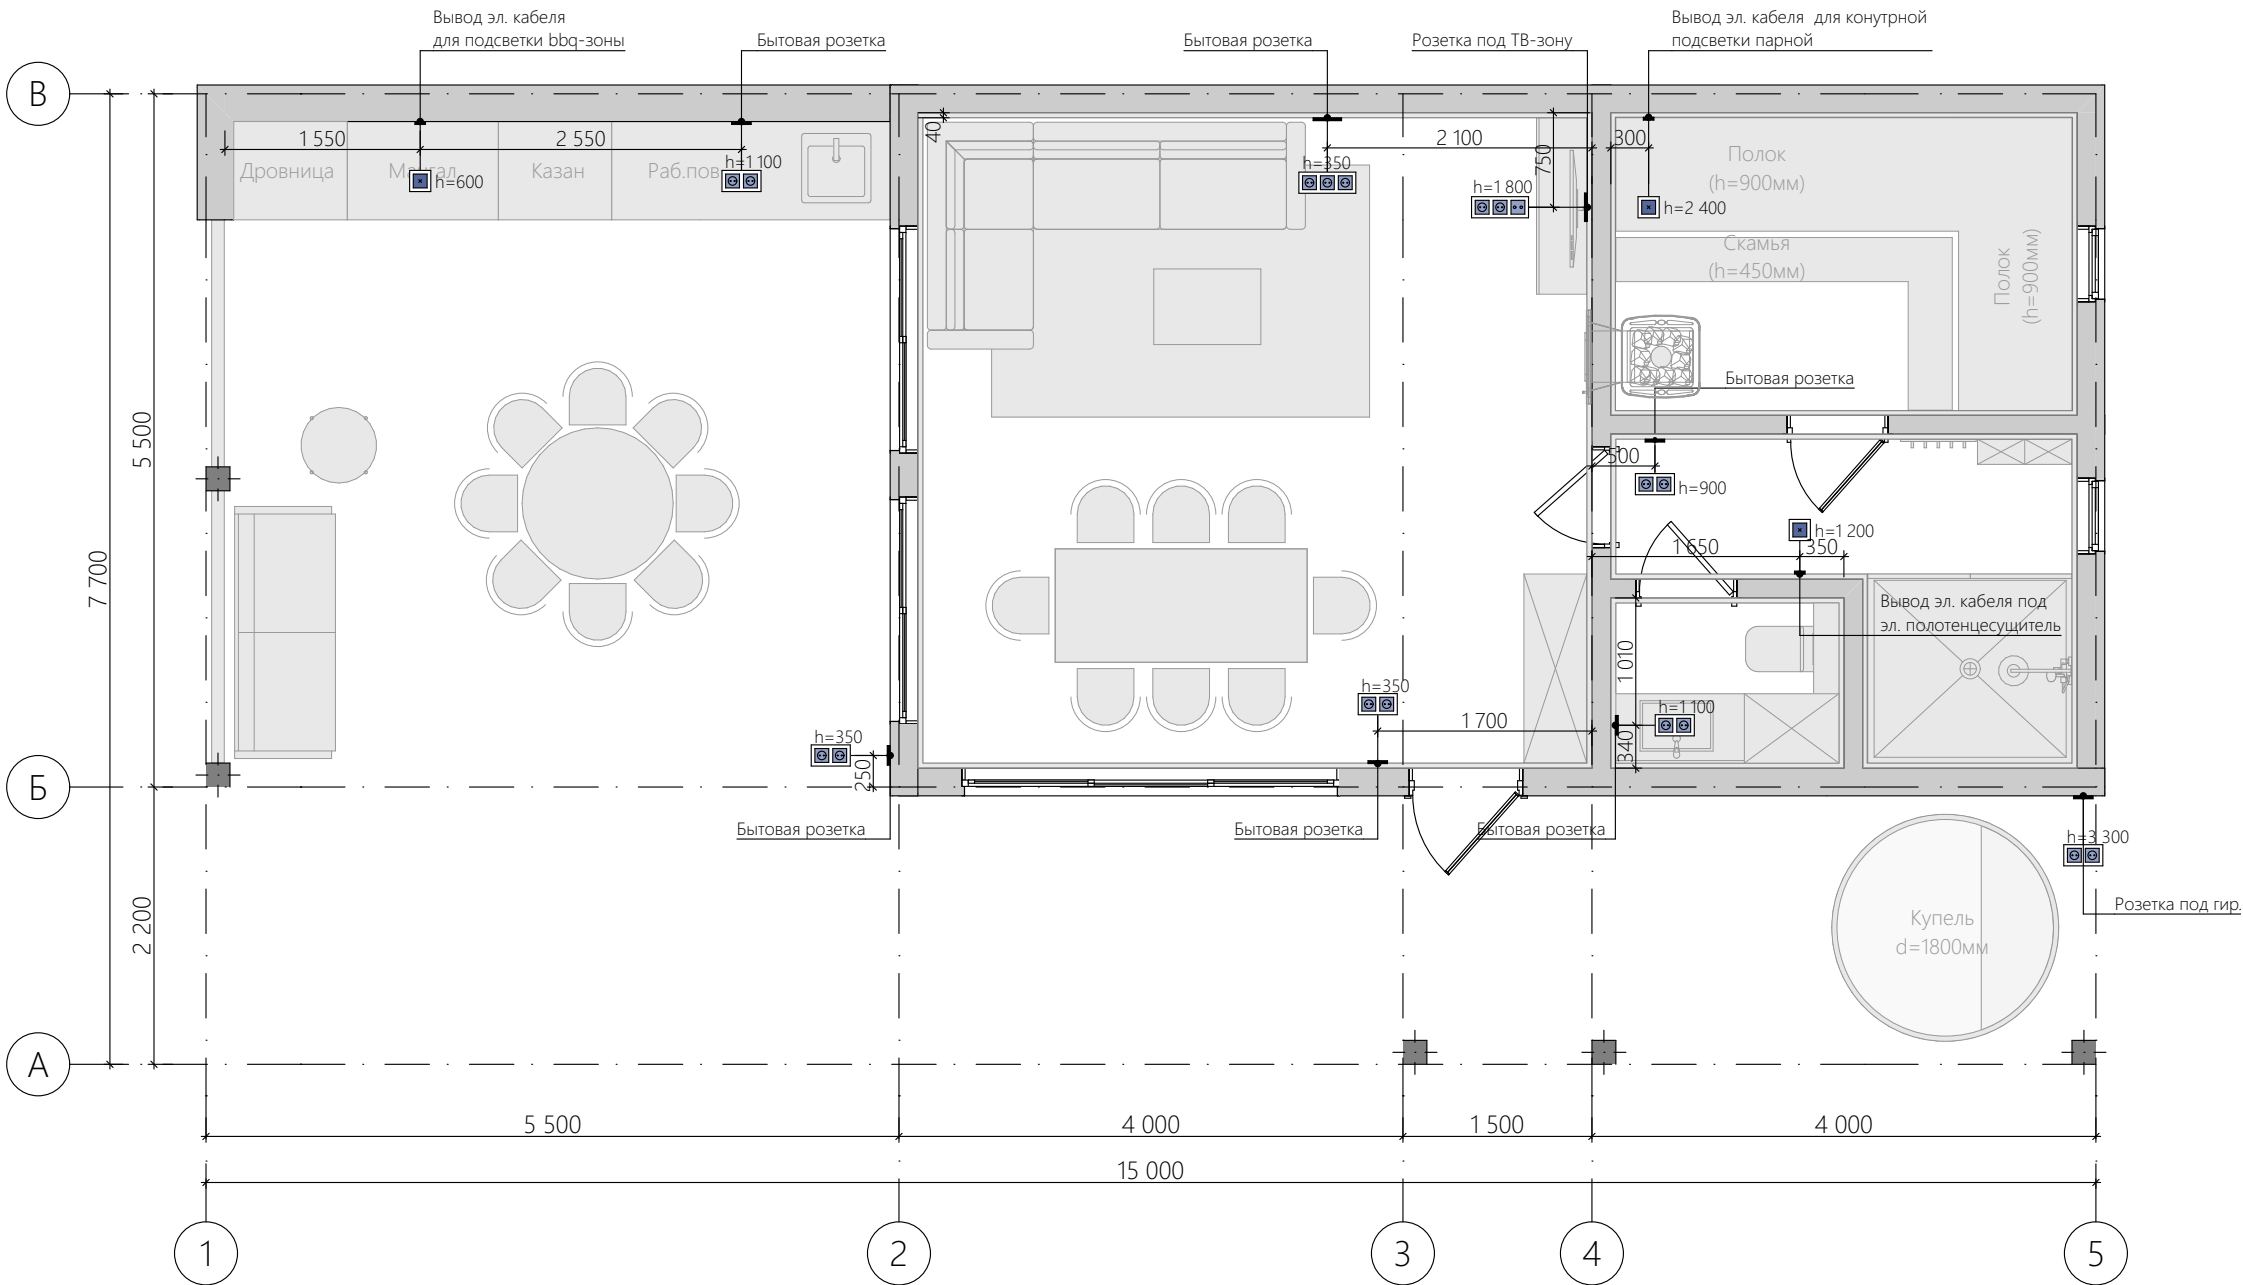

Экспликация розеток

Наименование	2д-вид	Кол-во
Розетка 220v (2 секции)		6
Розетка 220v (3 секции)		1
Розетка 220v+ТВ розетка (3 секции)		1
Эл. вывод (влагозащитная)		3
		11

Примечание:

1. Схема размещения розеток является рекомендательной и требует согласования с заказчиком по месту.
2. Все высоты даны от чистового пола.
3. Все указанные размеры даются до центра позиций.
4. Отметки розеток, выключателей, выводов и др. оборудования, являются предварительными и уточняются после выбора финишных материалов и мебели.
5. Размеры уточняются дополнительно

Согласовано

Взам. инв. №

Подп. и дата

Инв. № подл.

Лист	Изм.	№ Докум.	Подп.	Дата


Заречная улица, 46Б, село Никольское, Одинцовский городской округ, Московская область;
50:20:0090410:141

План размещения розеток

#Название Организации

План размещения светильников и выключателей

1:60

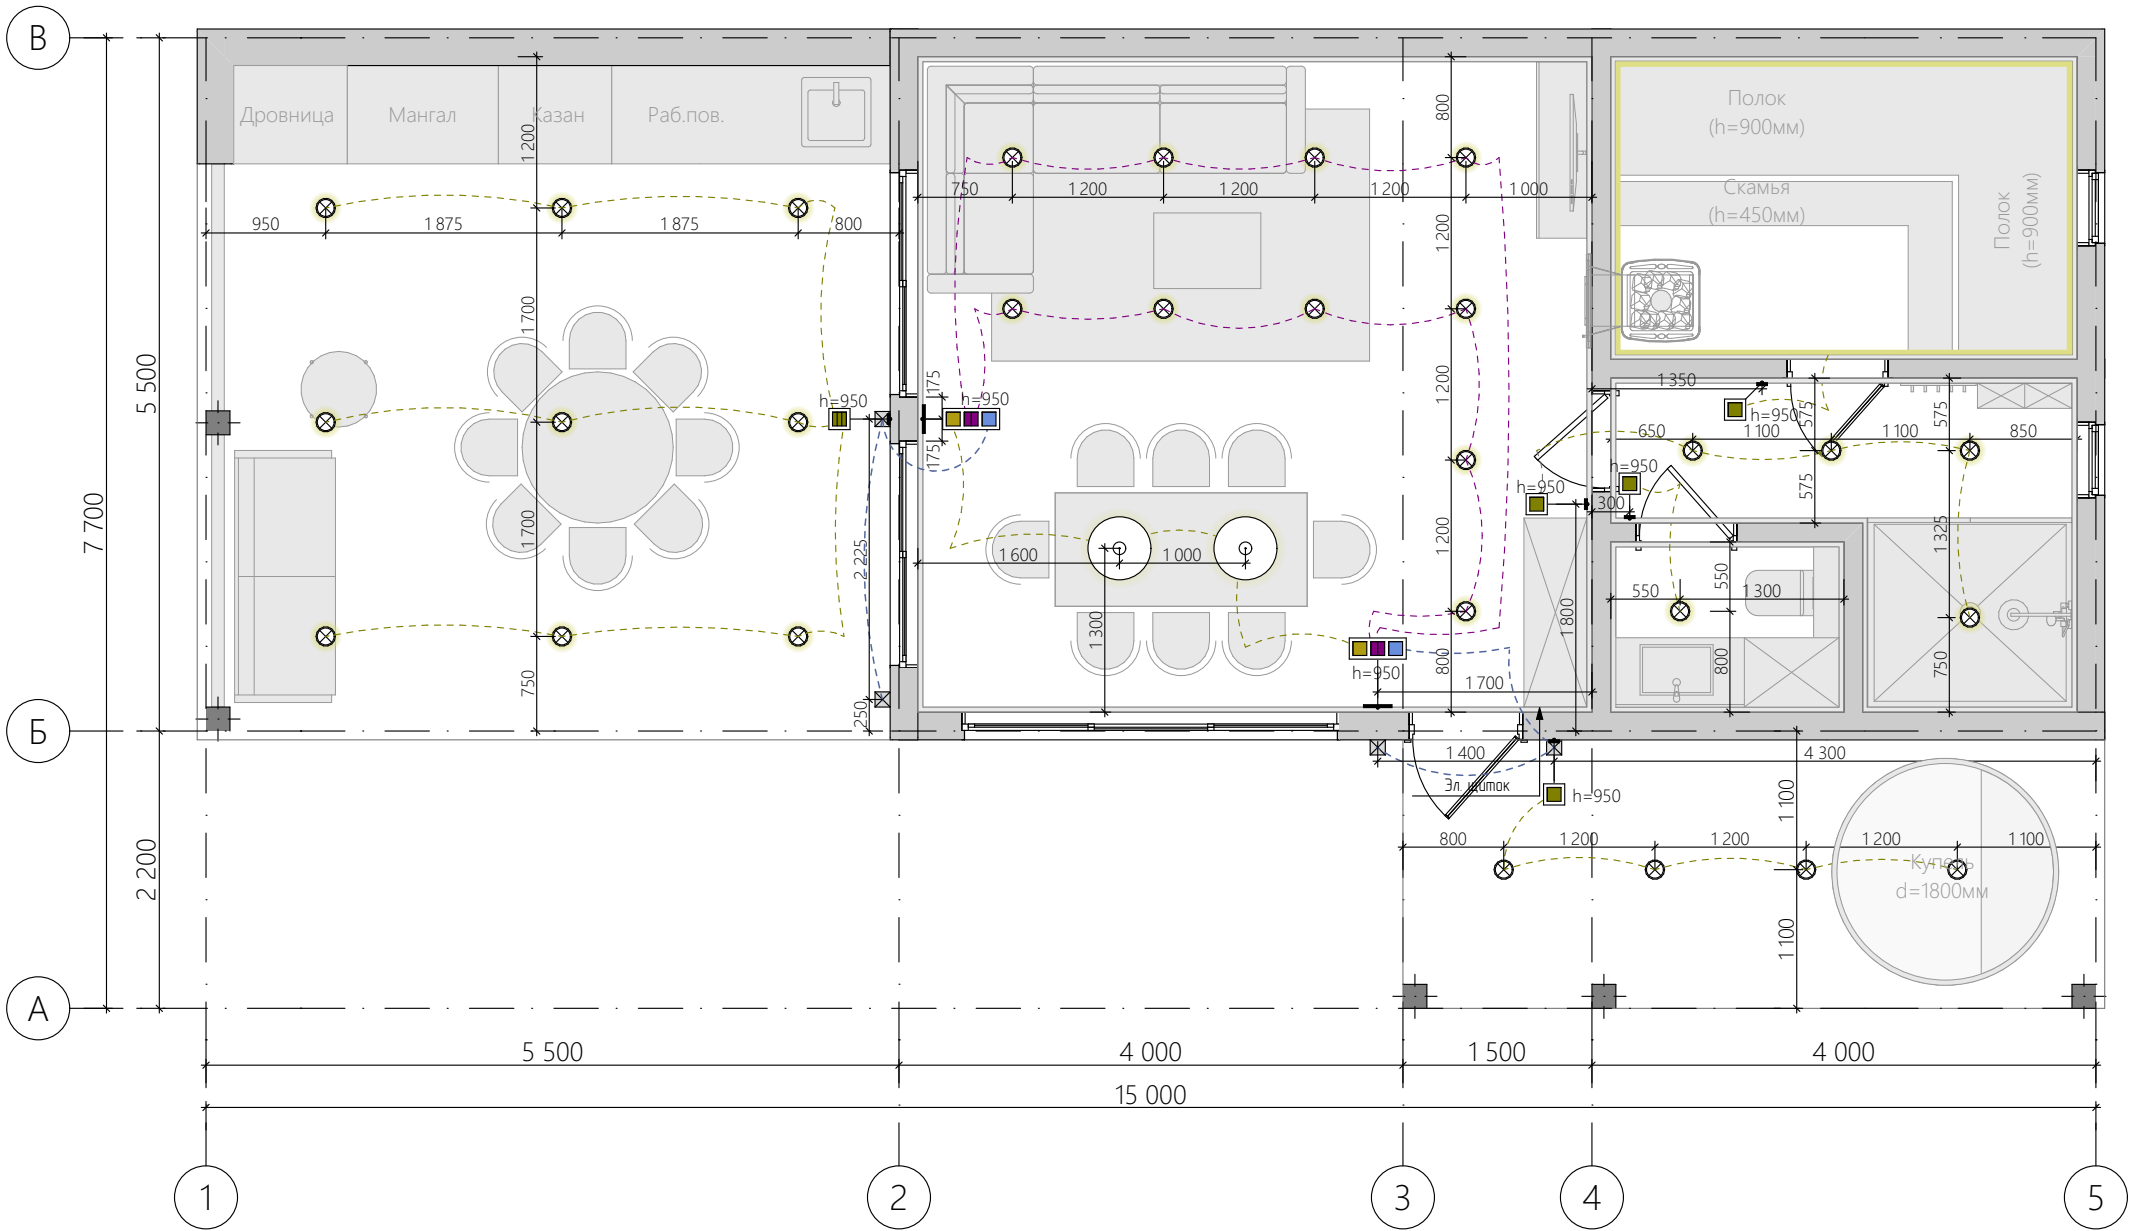

Экспликация светильников и выключателей

Наименование	2д-вид	Кол-во
--------------	--------	--------

Выключатель одно- и двухклавишный (3 секции)		2
--	--	---

Выключатель одноклавишный (1 секция)		4
--------------------------------------	--	---

Выключатель трехклавишный (1 секция)		1
--------------------------------------	--	---

Светильник подвесной		2
----------------------	--	---

Светильник точечный		28
---------------------	--	----

Уличный светильник		4
--------------------	--	---

41

Примечание:

1. Схема размещения розеток является рекомендательной и требует согласования с заказчиком по месту.
2. Все высоты даны от чистового пола.
3. Все указанные размеры даются до центра позиций.
4. Отметки розеток, выключателей, выводов и др. оборудования, являются предварительными и уточняются после выбора финишных материалов и мебели.
5. Размеры уточняются дополнительно

Согласовано

Взам. инв. №

Подп. и дата

Инв. № подл.

Лист	Изм.	№ Докум.	Подп.	Дата

Заречная улица, 46Б, село Никольское, Одинцовский городской округ, Московская область;
50:20:0090410:141

План размещения светильников и выключателей


#Название Организации

Лист

15

План крыши

1:60

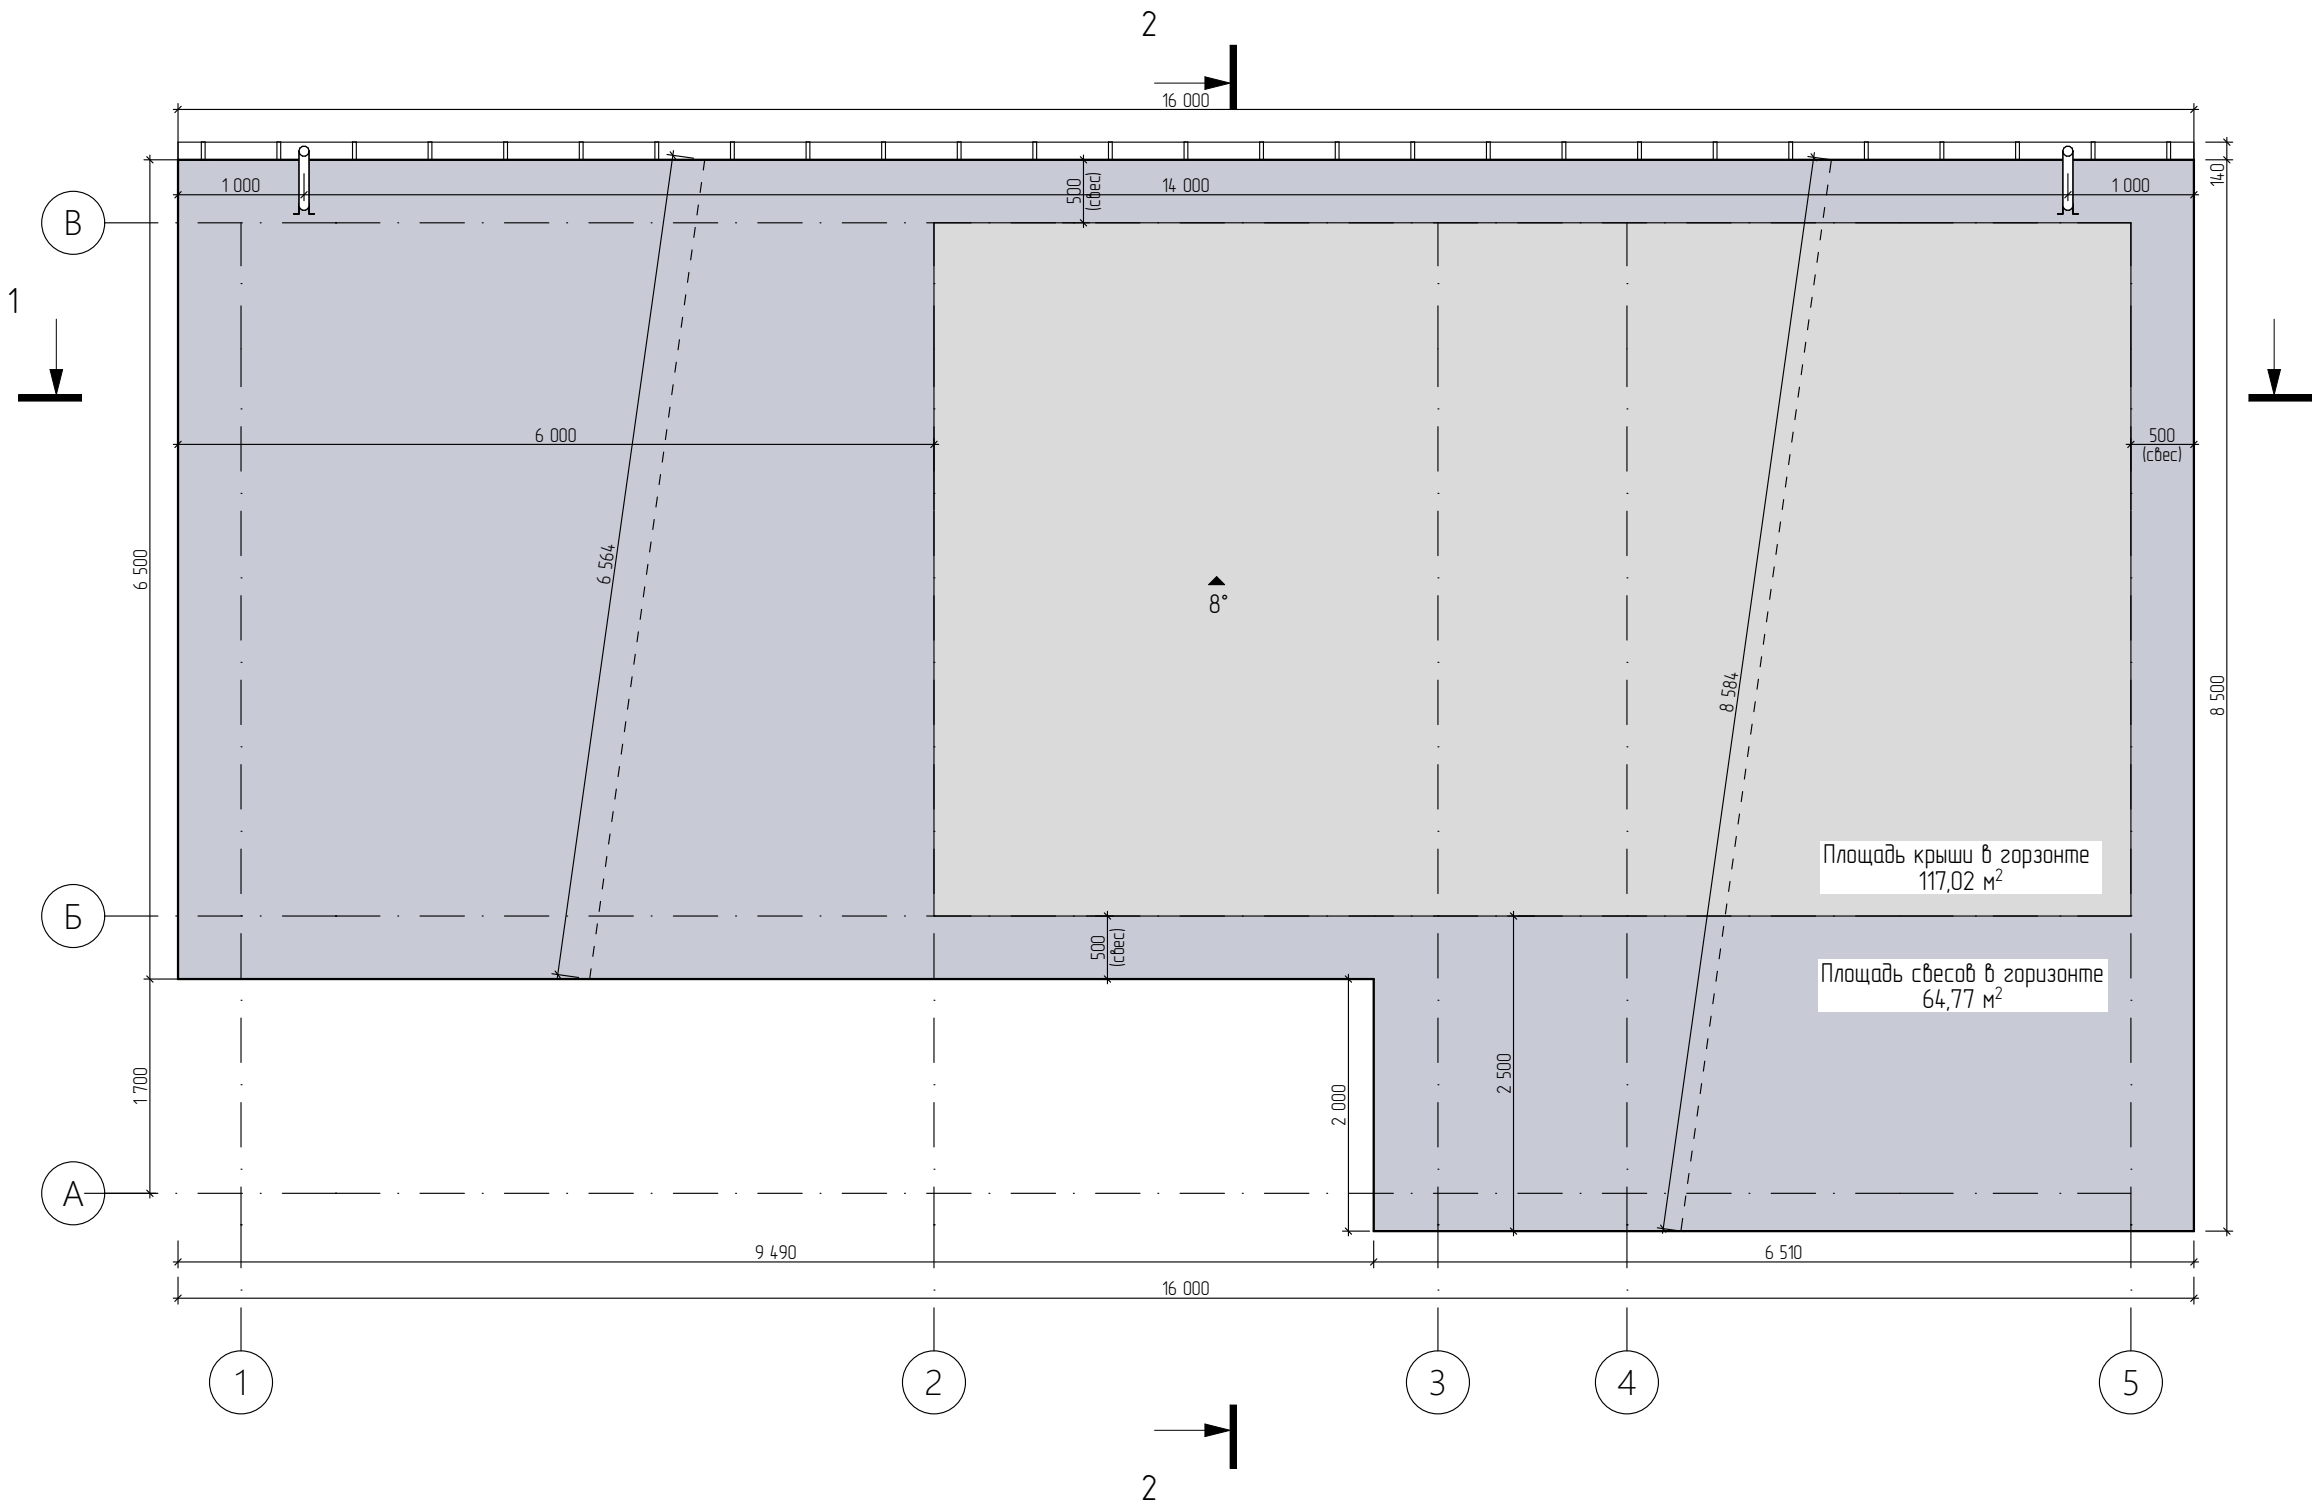


Условные обозначения:

- Крыша бани (уклон 8°)
- Подшив свесов бани

Площадь крыши бани (S , м²) = 118,17м²

Аксонометрия крыши

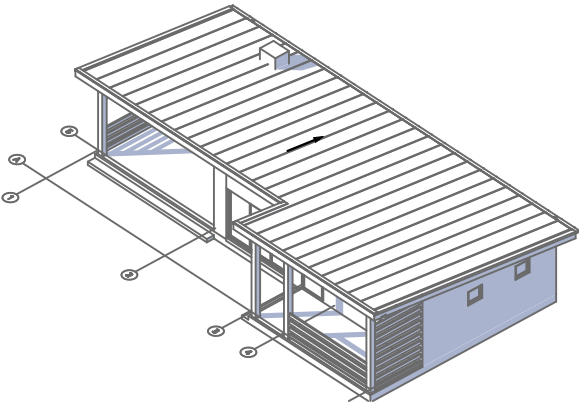


Согласовано				
И-нв. № подл.	Взам. инв. №	Подп. и дата		

Лист	Изм.	№ Докум.	Подп.	Дата

Заречная улица, 46Б, село Никольское, Одинцовский городской округ, Московская область; 50:20:0090410:141					План крыши		#Название Организации		Лист 16
---	--	--	--	--	------------	--	-----------------------	--	------------

Ведомость оконных проемов

1:1

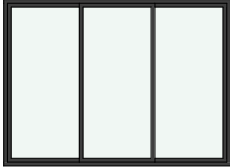Наименование	Размеры проема Ш х В, мм	Вид	Кол-во	Площадь, м2
ОК1	1 800×2 200		2	3,96
ОК2	3 000×2 200		1	6,60
ОК3	600×600		2	0,36
				15,24 м²

Согласовано				

Инв. № подл.	Подп. и дата	Взам. инв. №	

Примечание:

- 1. Изготовление окон и дверей определяется заказчиком, допускается изменение открывания окон и дверей;
- 2. При заказе оконных и дверных блоков необходим обмер по месту от изготовителя;
- 3. Оконные и дверные изделия изображены со стороны открывания.

Лист	Изм.	№ Докум.	Подп.	Дата	Ведомость оконных проемов	#Название Организации	Лист
							17


1:1

1. Изготовление окон и дверей определяется заказчиком, допускается изменение открывания окон и дверей;
2. При заказе оконных и дверных блоков необходим обмер по месту от изготовителя;
3. Оконные и дверные изделия изображены со стороны открывания.

Лист	Изм.	№ Докум.	Подп.	Дата	Ведомость дверных проемов	#Название Организации	Лист
							18

Разрез 1-1


1:50

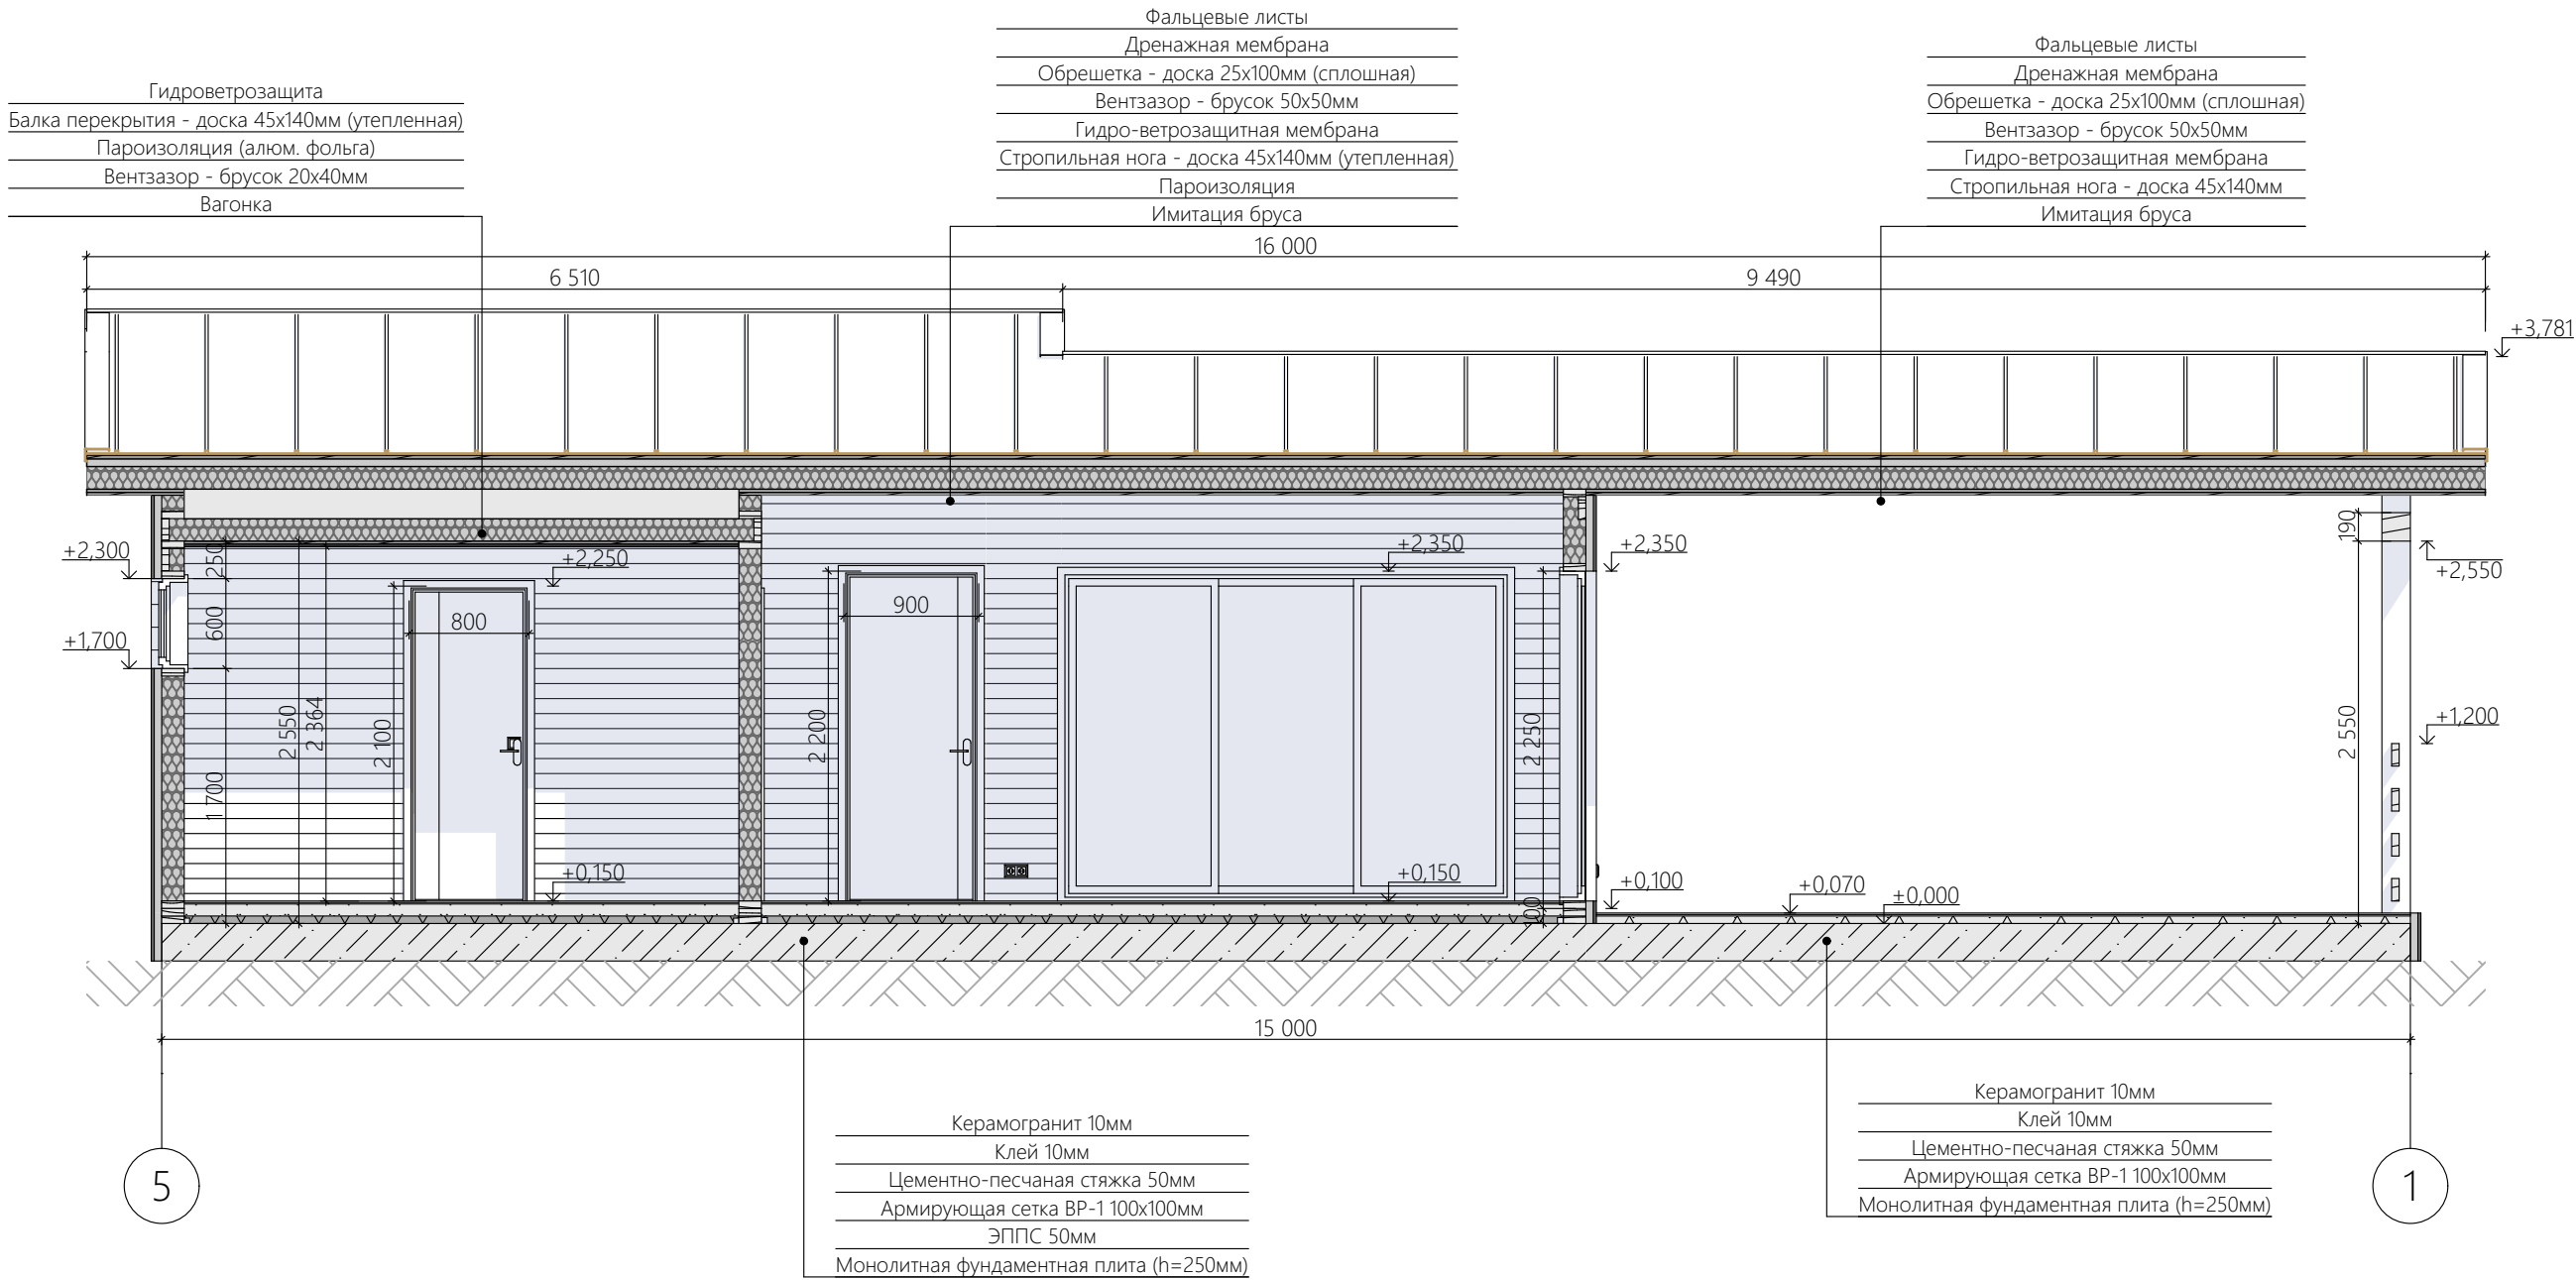

Согласовано				
И.нв. № подл.	Взам. инв. №	Подп. и дата		

Разрез 2-2

1:40

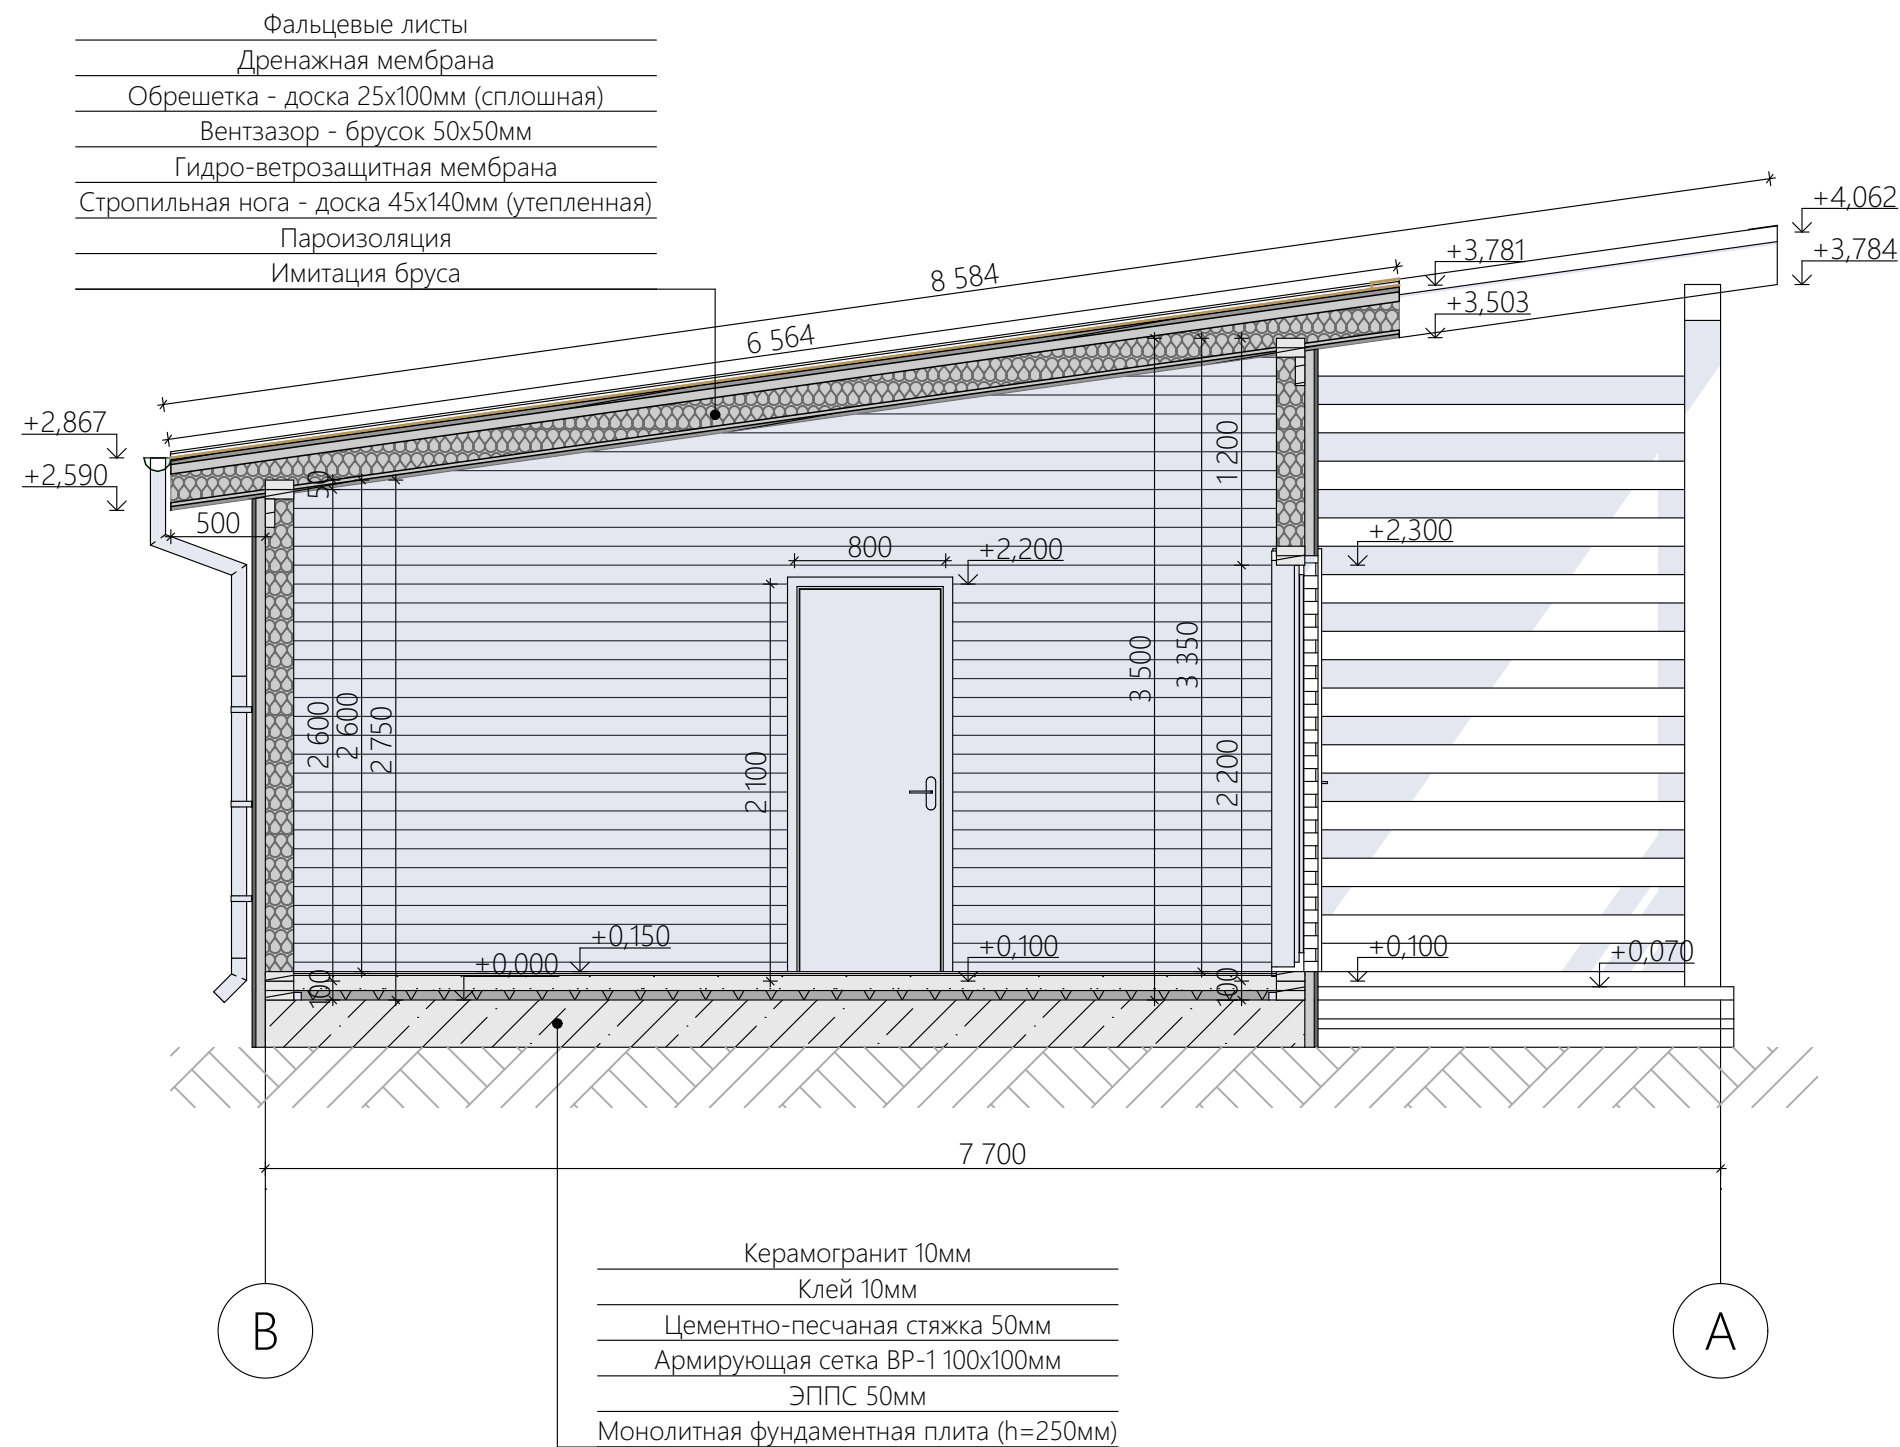


Согласовано				
И.нв. № подл.	Подп. и дата	Взам. инв. №		

Фасад 1-5

1:60

Условные обозначения:

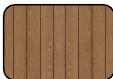
-  -Плакен (Цвет махагон)
-  -Террасная доска (ДПК. ВЕЛЬВЕТ. БРАЙТ. ШАЛЕ ЧЕРНЫЙ)
-  -Каньон (цвет черный)
-  -Фмброцементные панели (RAL 9001)
-  -Водосточная система, наличники, оконные рамы, фальцнвая кровля (RAL 9005)
-  -Фиброцементный сайдинг (RAL 9005)




Согласовано				
Инва. № подл.	Подп. и дата	Взам. инв. №		

Фасад А-В

1:40

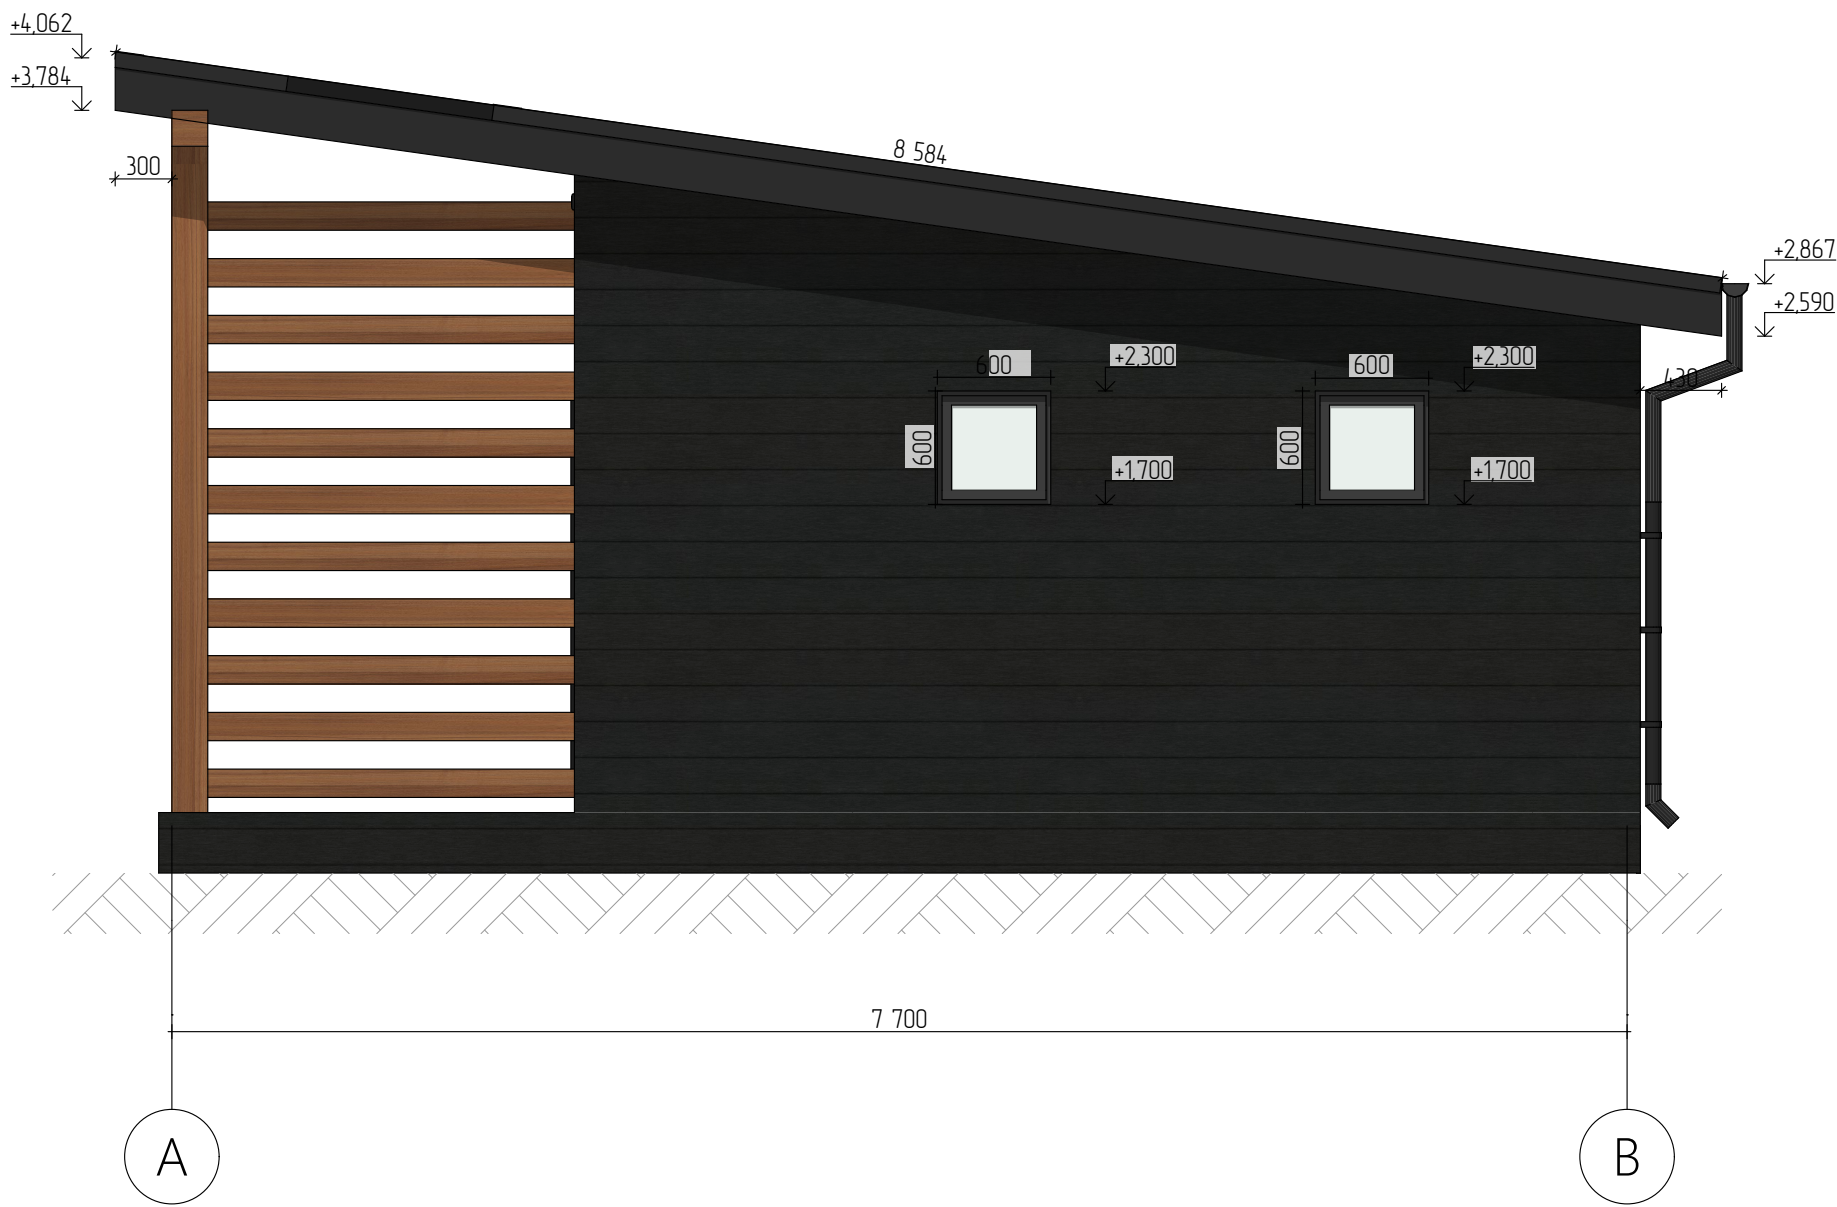

Условные обозначения:

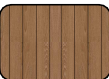-  -Плакен (Цвет махагон)
-  -Террасная доска (ДПК. ВЕЛЬВЕТ. БРАЙТ. ШАЛЕ ЧЕРНЫЙ)
-  -Каньон (цвет черный)
-  -Фмброцементные панели (RAL 9001)
-  -Водосточная система, наличники, оконные рамы, фальцновая кровля (RAL 9005)
-  -Фиброцементный сайдинг (RAL 9005)

Согласовано				
Инов. № подл.	Взам. инв. №			
	Подп. и дата			


Лист	Изм.	№ Докум.	Подп.	Дата	Заречная улица, 46Б, село Никольское, Одинцовский городской округ, Московская область; 50:20:0090410:141

Фасад А-В

#Название Организации	Лист 22
-----------------------	------------

Согласовано

Инов. № подл.	Подп. и дата	Взам. инв. №	

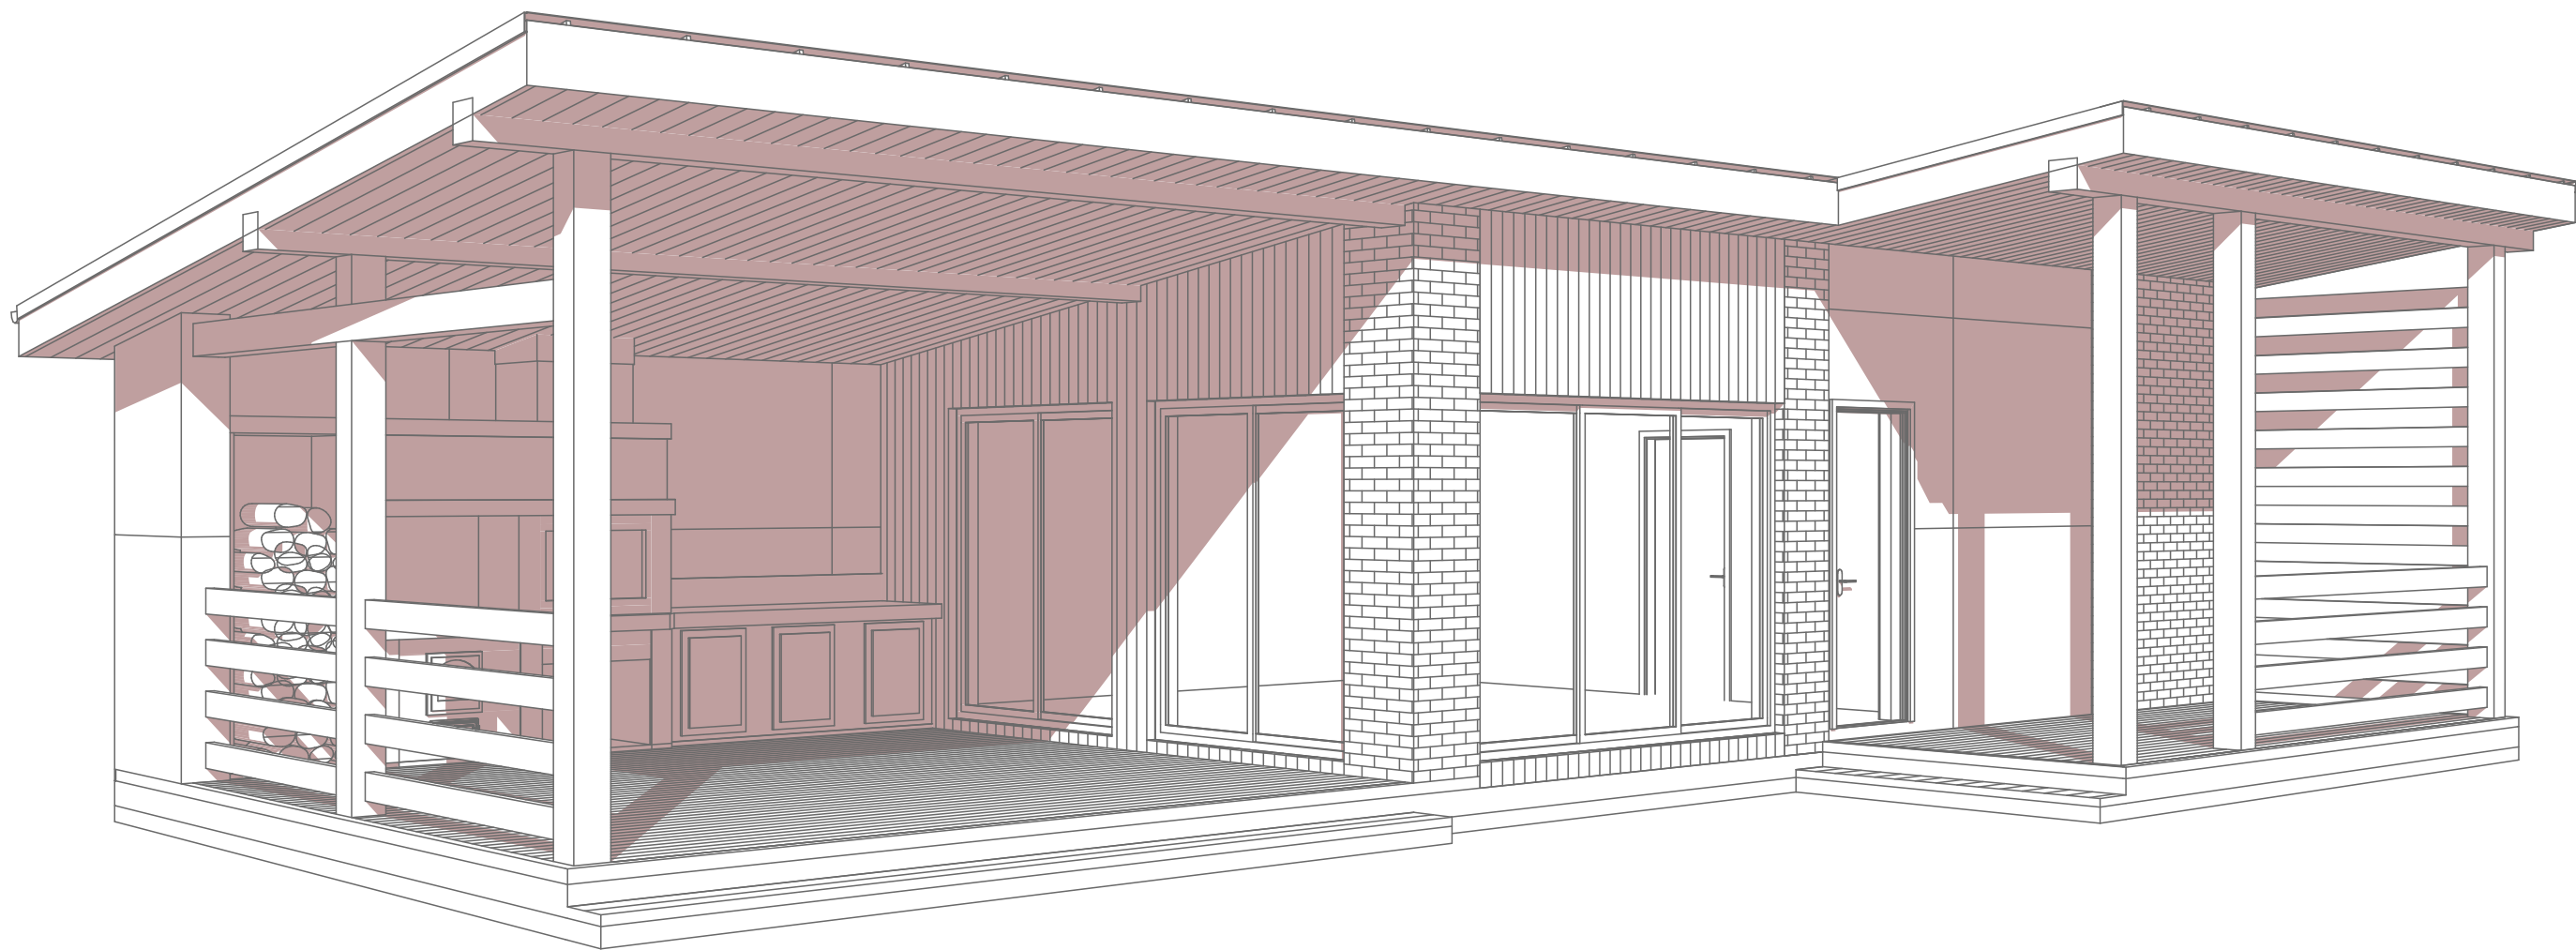

Лист	Изм.	№ Докум.	Подп.	Дата

Заречная улица, 46Б, село Никольское, Одинцовский городской округ, Московская область; 50:20:0090410:141


Аксометрия №1


#Название Организации

Фасад 5-1

1:60

Условные обозначения:

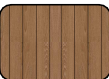
-  -Плакен (Цвет махагон)
-  -Террасная доска (ДПК. ВЕЛЬВЕТ. БРАЙТ. ШАЛЕ ЧЕРНЫЙ)
-  -Каньон (цвет черный)
-  -Фмброцементные панели (RAL 9001)
-  -Водосточная система, наличники, оконные рамы, фальцнвая кровля (RAL 9005)
-  -Фиброцементный сайдинг (RAL 9005)

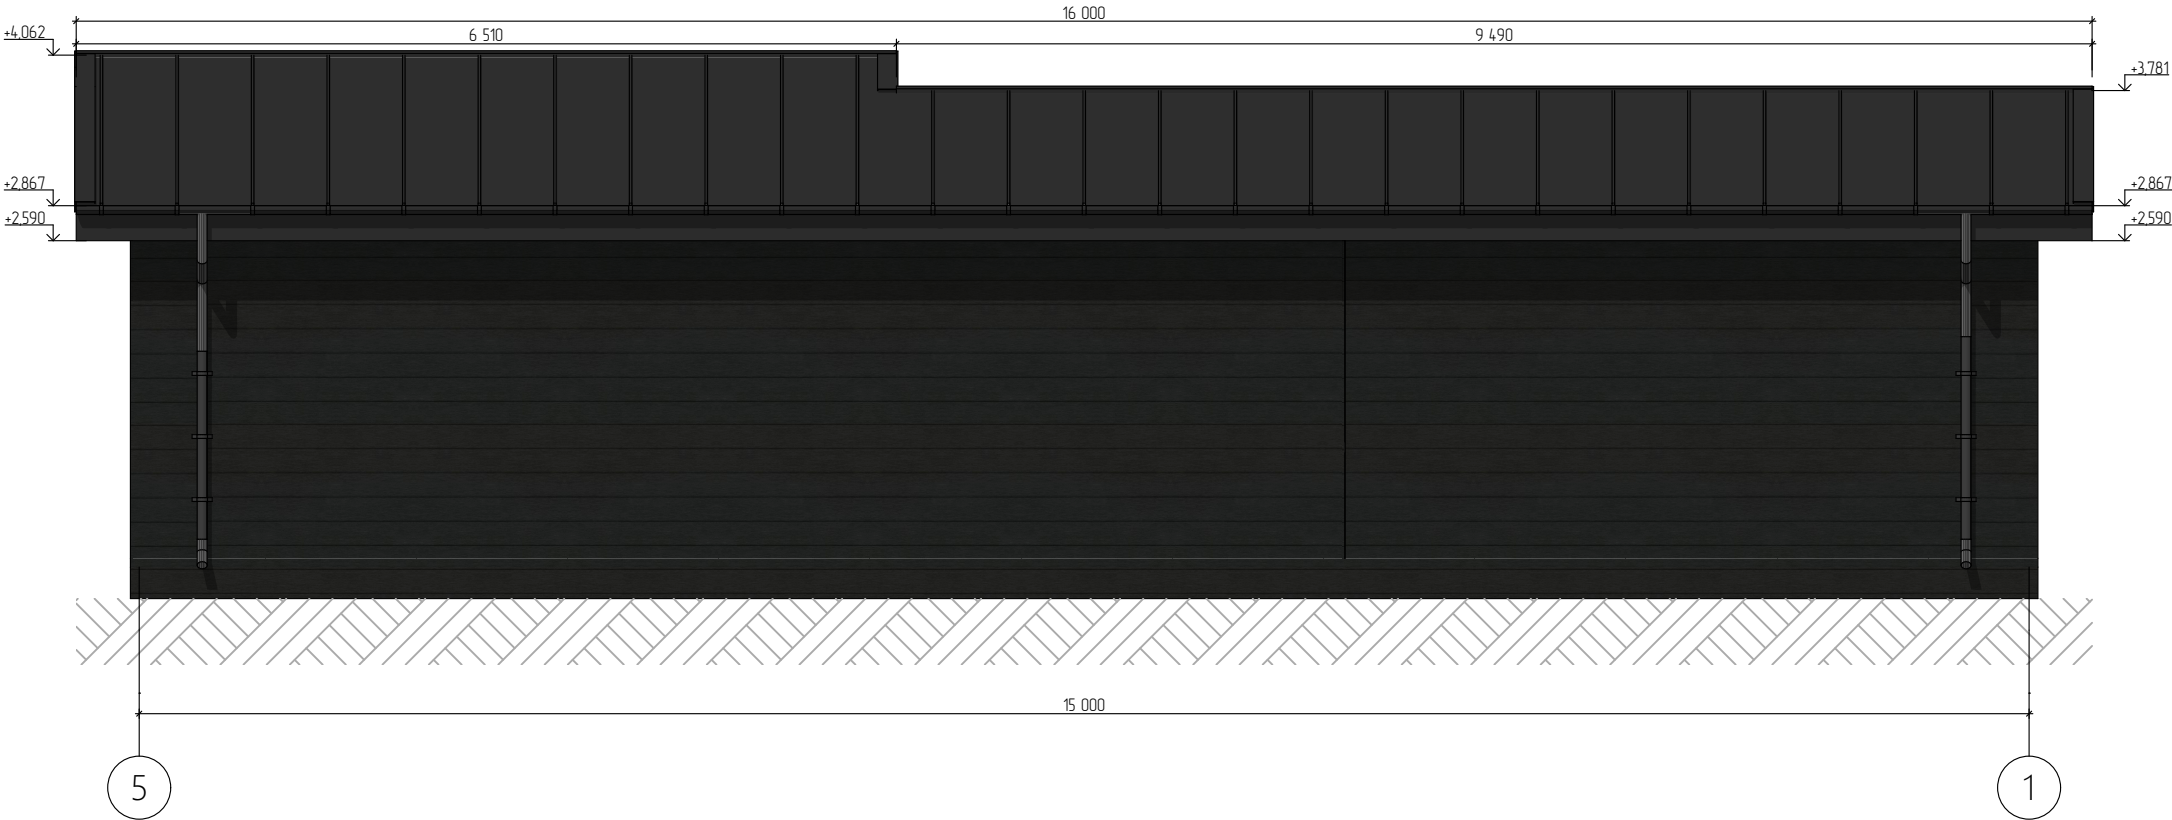


Согласовано				
Инов. № подл.	Подп. и дата	Взам. инв. №		

Фасад В-А

1:40

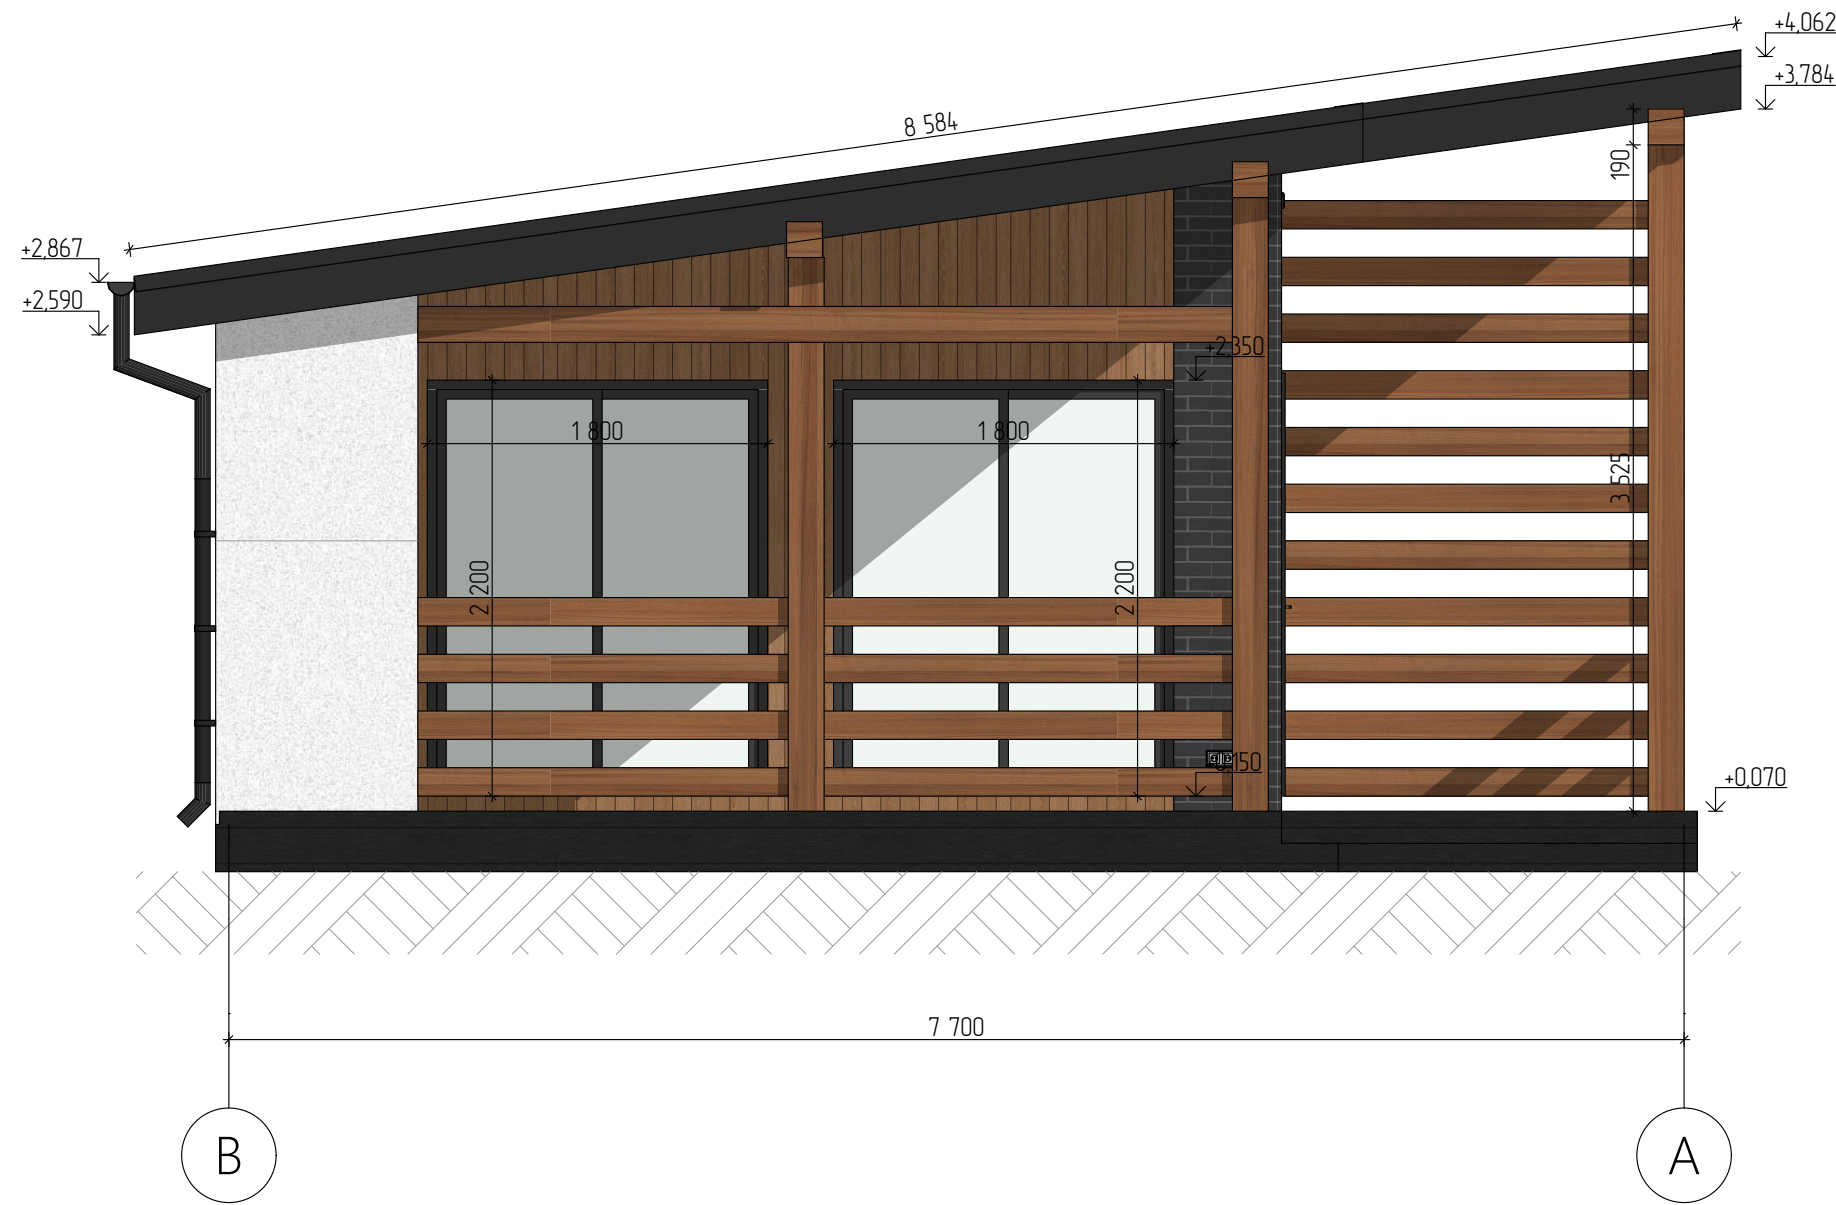


Условные обозначения:

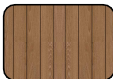-  -Плакен (Цвет махагон)
-  -Террасная доска (ДПК. ВЕЛЬВЕТ. БРАЙТ. ШАЛЕ ЧЕРНЫЙ)
-  -Каньон (цвет черный)
-  -Фмброцементные панели (RAL 9001)
-  -Водосточная система, наличники, оконные рамы, фальцнвая кровля (RAL 9005)
-  -Фиброцементный сайдинг (RAL 9005)

Согласовано				
Инов. № подл.	Взам. инв. №		Подп. и дата	

Согласовано			

Инов. № подл.	Подп. и дата	Взам. инв. №	

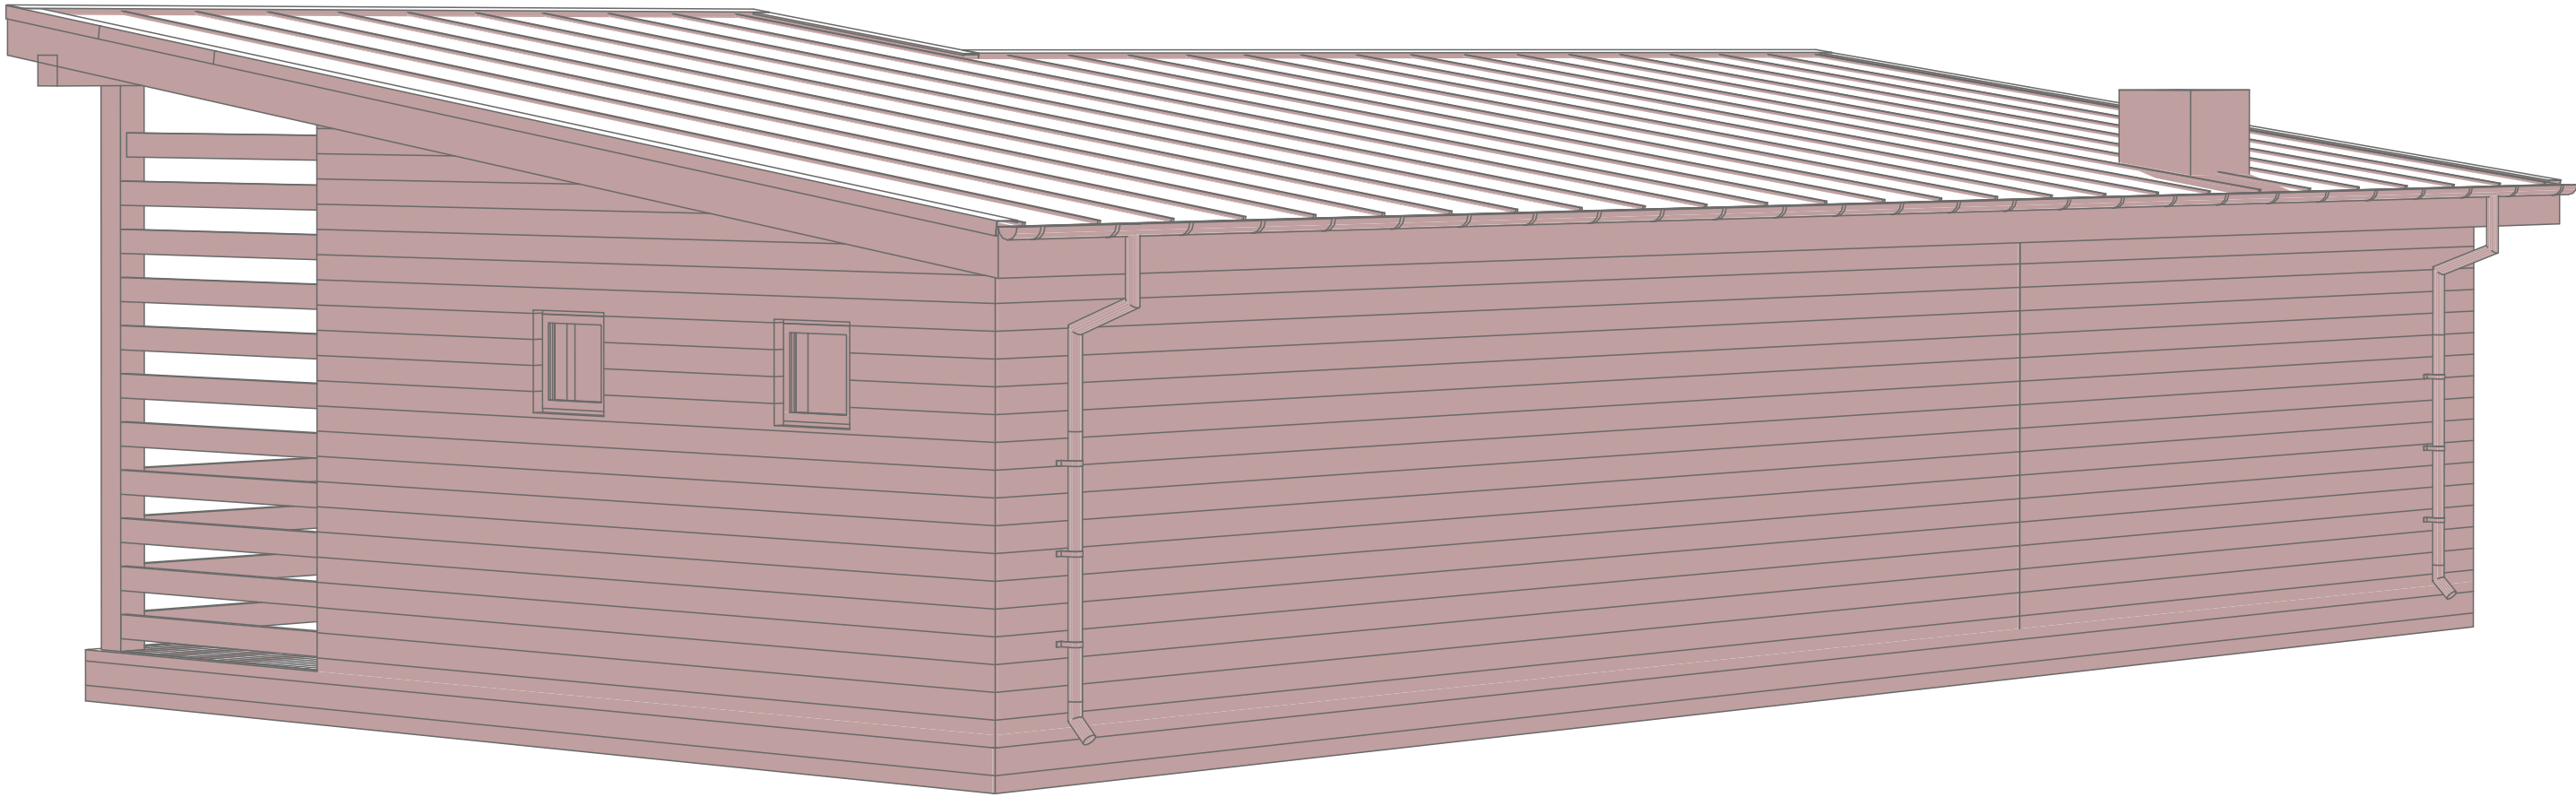

Лист	Изм.	№ Докум.	Подп.	Дата

Заречная улица, 46Б, село Никольское, Одинцовский городской округ, Московская область; 50:20:0090410:141					Аксонометрия №2		#Название Организации	Лист
								26

Согласовано

Взам. инв. №

Подп. и дата

Инв. № подл.



Лист	Изм.	№ Докум.	Подп.	Дата

Заречная улица, 46Б, село Никольское, Одинцовский городской округ, Московская область; 50:20:0090410:141

Визуализация

#Название Организации



Согласовано				
Инов. № подл.	Подп. и дата	Взам. инв. №		

Лист	Изм.	№ Докум.	Подп.	Дата

Заречная улица, 46Б, село Никольское, Одинцовский городской округ, Московская область; 50:20:0090410:141

Визуализация

#Название Организации

Согласовано					
Инва. № подл.	Подп. и дата	Взам. инв. №			



Лист	Изм.	№ Докум.	Подп.	Дата

Заречная улица, 46Б, село Никольское, Одинцовский городской округ, Московская область; 50:20:0090410:141

Визуализация

#Название Организации

Согласовано

Взам. инв. №

Подп. и дата

Инв. № подл.



Лист	Изм.	№ Докум.	Подп.	Дата

Заречная улица, 46Б, село Никольское, Одинцовский городской округ, Московская область; 50:20:0090410:141

Визуализация

#Название Организации

Согласовано

Взам. инв. №

Подп. и дата

Инв. № подл.



Лист	Изм.	№ Докум.	Подп.	Дата

Заречная улица, 46Б, село Никольское, Одинцовский городской округ, Московская область; 50:20:0090410:141

Визуализация

#Название Организации

Согласовано

Взам. инв. №

Подп. и дата

Инв. № подл.

Лист	Изм.	№ Докум.	Подп.	Дата

Заречная улица, 46Б, село Никольское, Одинцовский городской округ, Московская область; 50:20:0090410:141

Визуализация

#Название Организации



Согласовано					
Инва. № подл.	Подп. и дата	Взам. инв. №			



Лист	Изм.	№ Докум.	Подп.	Дата

Заречная улица, 46Б, село Никольское, Одинцовский городской округ, Московская область; 50:20:0090410:141

Визуализация

#Название Организации



Согласовано				
Инов. № подл.	Подп. и дата	Взам. инв. №		

Лист	Изм.	№ Докум.	Подп.	Дата

Заречная улица, 46Б, село Никольское, Одинцовский городской округ, Московская область; 50:20:0090410:141

Визуализация

#Название Организации