


ARCHITECTURE/
CONSTRUCTION



Название:
Разработал:
-
Принял:
-
г. Москва

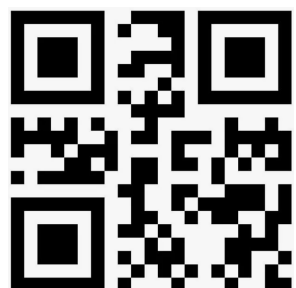

Согласовано				
Инва. № подл.	Взам. инв. №		Подп. и дата	

Лист	Наименование	Примечание
1	Титульный	
2	Ведомость чертежей	
3	Пояснительная записка	
4	СПОЗУ	
5	Маркировочный план	
6	Размерный план	
7	План расстановки мебели и оборудования	
8	3д-разрез	
9	План покрытия пола	
10	Пироги пола	
11	План покрытия стен	
12	Пироги стены	
13	План размещения розеток	
14	План размещения светильников и выключателей	
15	План крыши	
16	Ведомость заполнения оконных проемов	
17	Ведомость заполнения дверных проемов	
18	Разрез 1-1	
19	Разрез 2-2 и разрез 3-3	
20	Фасад 1-4	
21	Фасад А-Б, фасад Б-А	
22	Аксонометрия №1	
23	Фасад 4-1	
24	Аксонометрия №2	
25	Визуализация	
26	Визуализация	
27	Визуализация	
28	Визуализация	
29	Визуализация	
30	Визуализация	
31	Визуализация	
32	Визуализация	

В основу архитектурно-планировочных решений положены требования технологических заданий и требования норм и правил строительного проектирования, действующих на территории РФ.

Основные параметры и требования разработаны на основании пожеланий и требований заказчика.

Архитектурные решения приняты в соответствии со следующими нормативными документами:

- Градостроительный кодекс российской федерации.
- Земельного Кодекса Российской Федерации.
- Федеральный закон от 22.07.2008 N 123 - ФЗ (ред. от 29.07.2017)"Технический регламент о требованиях пожарной безопасности.
- Федеральный закон № 384 - ФЗ «Технический регламент о безопасности зданий и сооружений».
- ГОСТ Р 21.1101-2013.«Основные требования к проектной и рабочей документации».
- Постановление правительства РФ от 16.02.2008 № 87 «Положение о составе разделов проектной документации и требованиях к их содержанию».
- СП 42.13330.2011 «Градостроительство. Планировка и застройка городских и сельских поселений».
- СП 131.13330.2018 «СНиП 23-01-99* Строительная климатология».
- СП 20.13330.2016 «СНиП 2.01.07-85* Нагрузки и воздействия».
- СП 22.13330.2016 «СНиП 2.02.01-83* Основания зданий и сооружений».
- СП 70.13330.2012 (с изменениями №1) «СНиП 3.03.01-87 Несущие и ограждающие конструкции».
- СП 64.13330.2017 «СНиП II-25-80 Деревянные конструкции».
- СП 17.13330.2017 «СНиП II-26-76 Кровли».
- СП 29.13330.2011 «СНиП 2.03.13-88 Полы».
- СП 28.13330.2017 «СНиП 2.03.11-85 Защита строительных конструкций от коррозии».
- СП 50.13330.2012 «СНиП 23-02-2003 Тепловая защита зданий».

Лист	Изм.	№ Докум.	Подп.	Дата	Российская Федерация, Московская область, Можайский городской округ, город Можайск, улица Царская, 27; 50:18:0030306:1291	Ведомость чертежей	#Название Организации	Лист
								2

Согласовано				
Изм. № подл.	Подп. и дата	Взам. инв. №		

1. Общие данные:

1.1. Архитектурный проект разработан на основании требований и пожеланий заказчика.

Тип строения	баня/беседка
Относительная отм. ±0.000	ур. верха лаг перекрытия
Общая площадь застройки, м2	71,35
Габаритные размеры каркаса здания, м	16,3х4
Этажность	1 этаж
Конструктивная схема	деревянный каркас

2. Конструктивные решения:

2.1. Рабочие чертежи разработаны на основании задания на проектирование

Полезная нагрузка на перекрытие	150 кгс/м2	-
Нормативная глубина промерзания	1,2м	СП 22.13330.2016 СП 131.13330.2020
Нормативное ветровое давление	I район (23кгс/м2)	СП 22.13330.2016
Нормативный вес снегового покрова	III район (150кгс/м2)	СП 22.13330.2016
Температура наиболее холодной пятидневки	-29°С	СП 131.13330.2020

2.2. Конструктивное строение представляет собой сооружение:

- на свайном фундаменте
- несущими стенами из деревянного каркаса
- плоской кровлей по деревянным стропилам

2.3. Необходимо осуществлять технический надзор за производством строительных работ. Данные по проведённым работам необходимо систематически вносить в журнал работ.

По каждому из этапов работ необходимо осуществлять входной контроль материалов и вести приёмку.

Фундамент	винтовые сваи (d=108мм)
Несущие конструкции	деревянный каркас (140х45мм)
Стропильная система	строганая доска (190х45мм)
Тип крыши	плоская
Покрытие кровли	наплавляемая

2.4. Все деревянные конструкции обработать огне-биозащитными септиками в соответствии со СП 28.13330.2017 "Защита строительных конструкций от коррозии".


2.5. Кровельные работы выполнять в соответствии с требованиями фирмы производителя.

2.6. Все работы вести в строгом соответствии с требованиями СНиП 12.03.2001 "Безопасность труда в строительстве".

2.7. При выполнении всех работ строго соблюдать меры противопожарной безопасности.

2.8. Возможна замена материалов аналогами.

*Решения, принятые в проекте и отображенные в чертежах, соответствуют требованиям экологических, санитарно - гигиенических, противопожарных и других норм, действующих на территории Российской Федерации, и обеспечивают безопасную для жизни и здоровья людей эксплуатацию объекта при соблюдении предусмотренных рабочих чертежей и мероприятий.

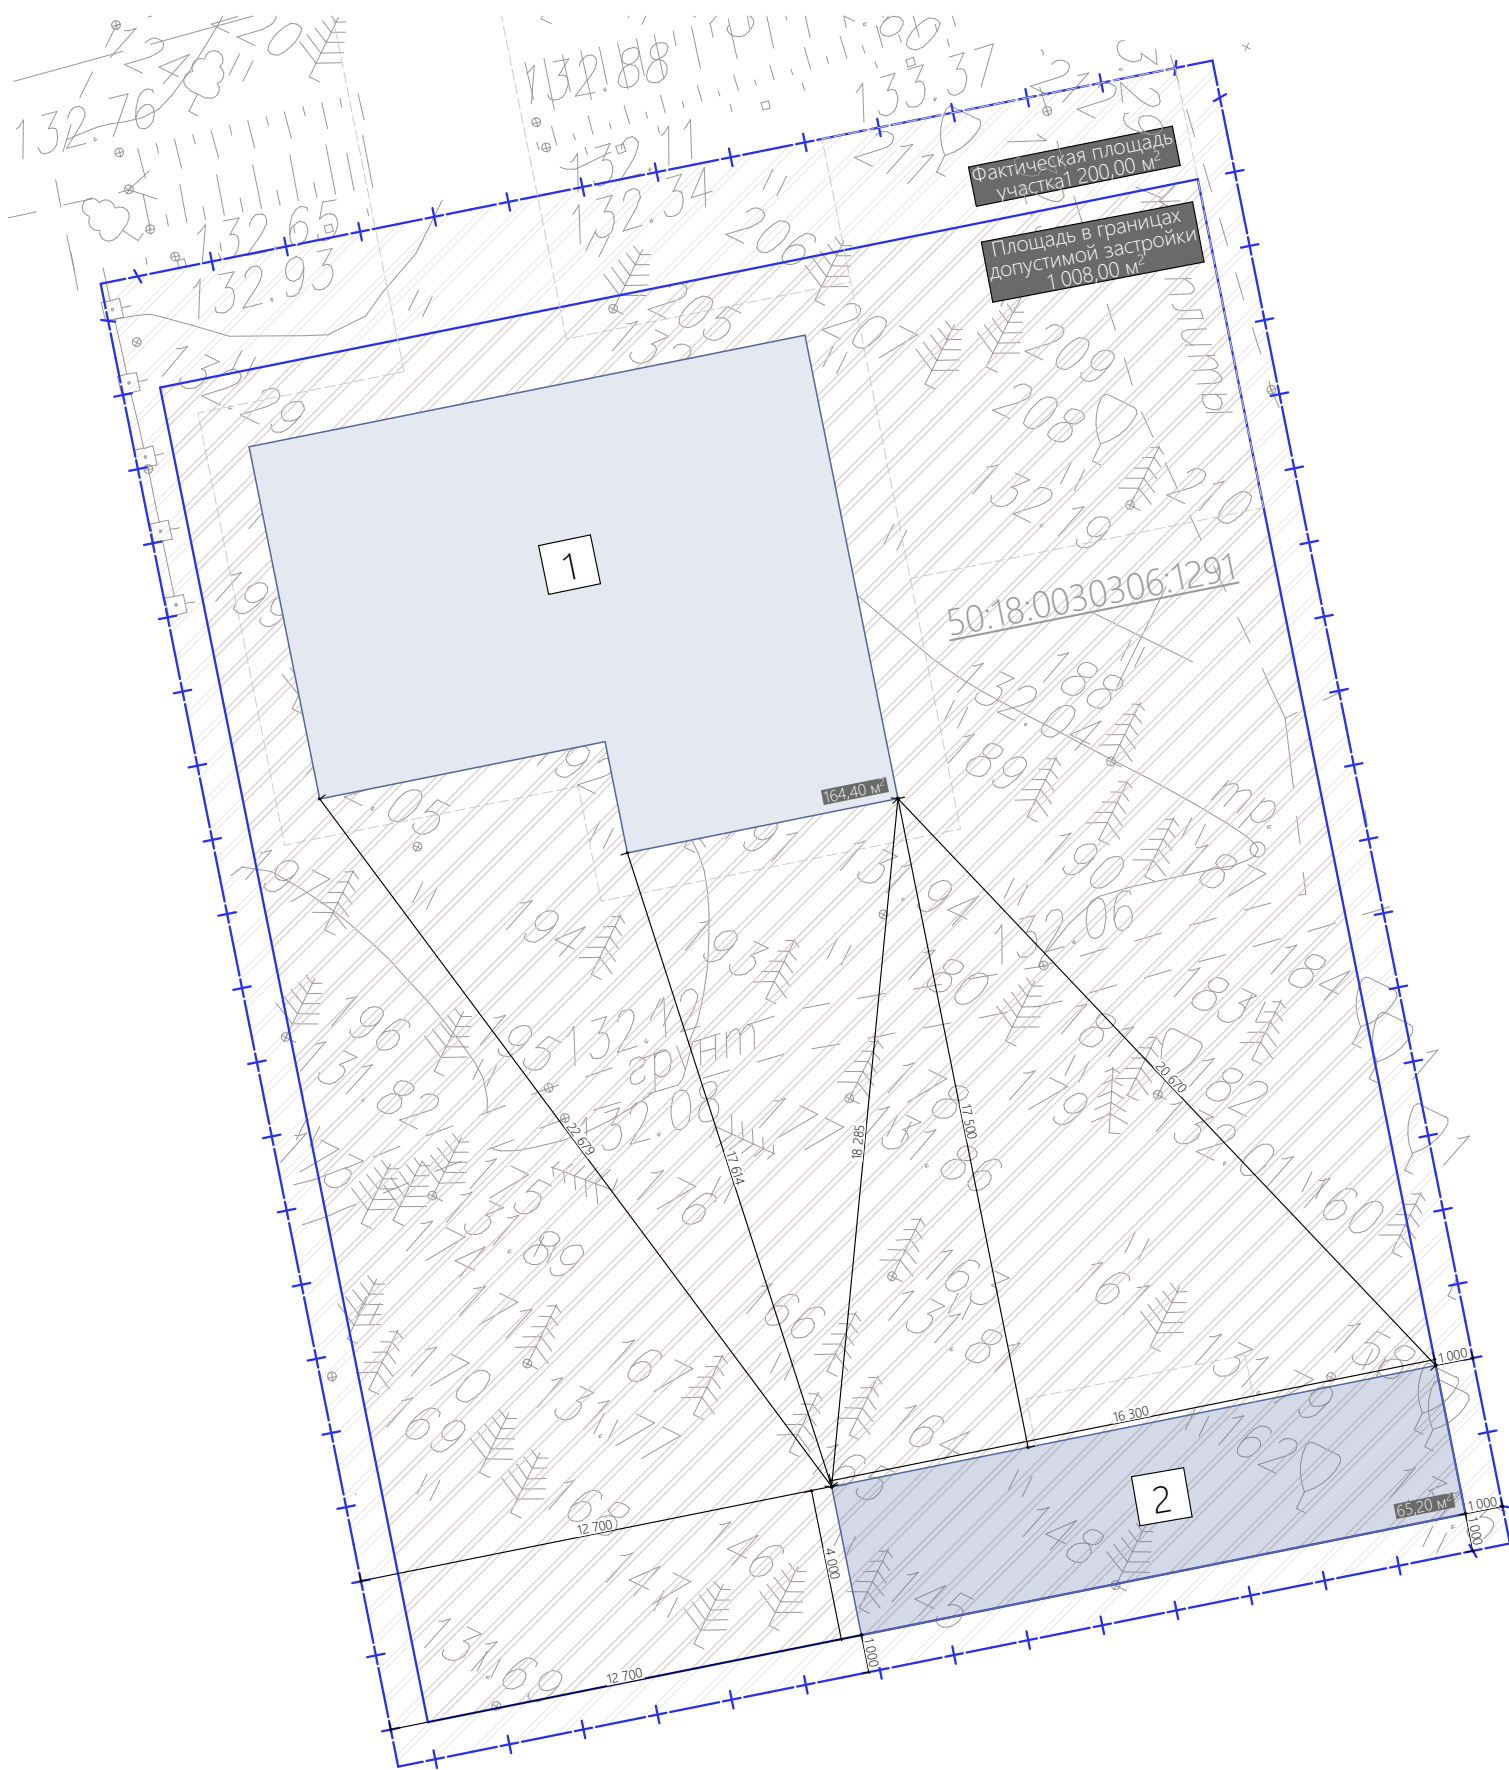


Условные обозначения:

- Граница участка
- Граница застройки участка
- Существующий индивидуальный жилой дом
- Банный комплекс (проектируемая постройка)

Технико-экономические показатели

Наименование	Площадь, м²
Площадь участка (по кадастровой документации)	1200,0
Общая площадь застройки (баня+ИЖД)	229,6
Площадь участка (по топографической съемке)	1200,0
Площадь застройки (баня)	65,2
Площадь застройки (ИЖД)	164,4

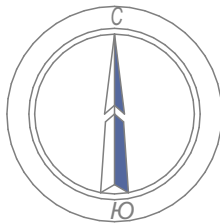


Согласовано				
И-нв. № подл.	Подп. и дата	Взам. инв. №		

Лист	Изм.	№ Докум.	Подп.	Дата	Российская Федерация, Московская область, Можайский городской округ, город Можайск, улица Царская, 27; 50:18:0030306.1291

СПОЗУ


#Название Организации	Лист
	4

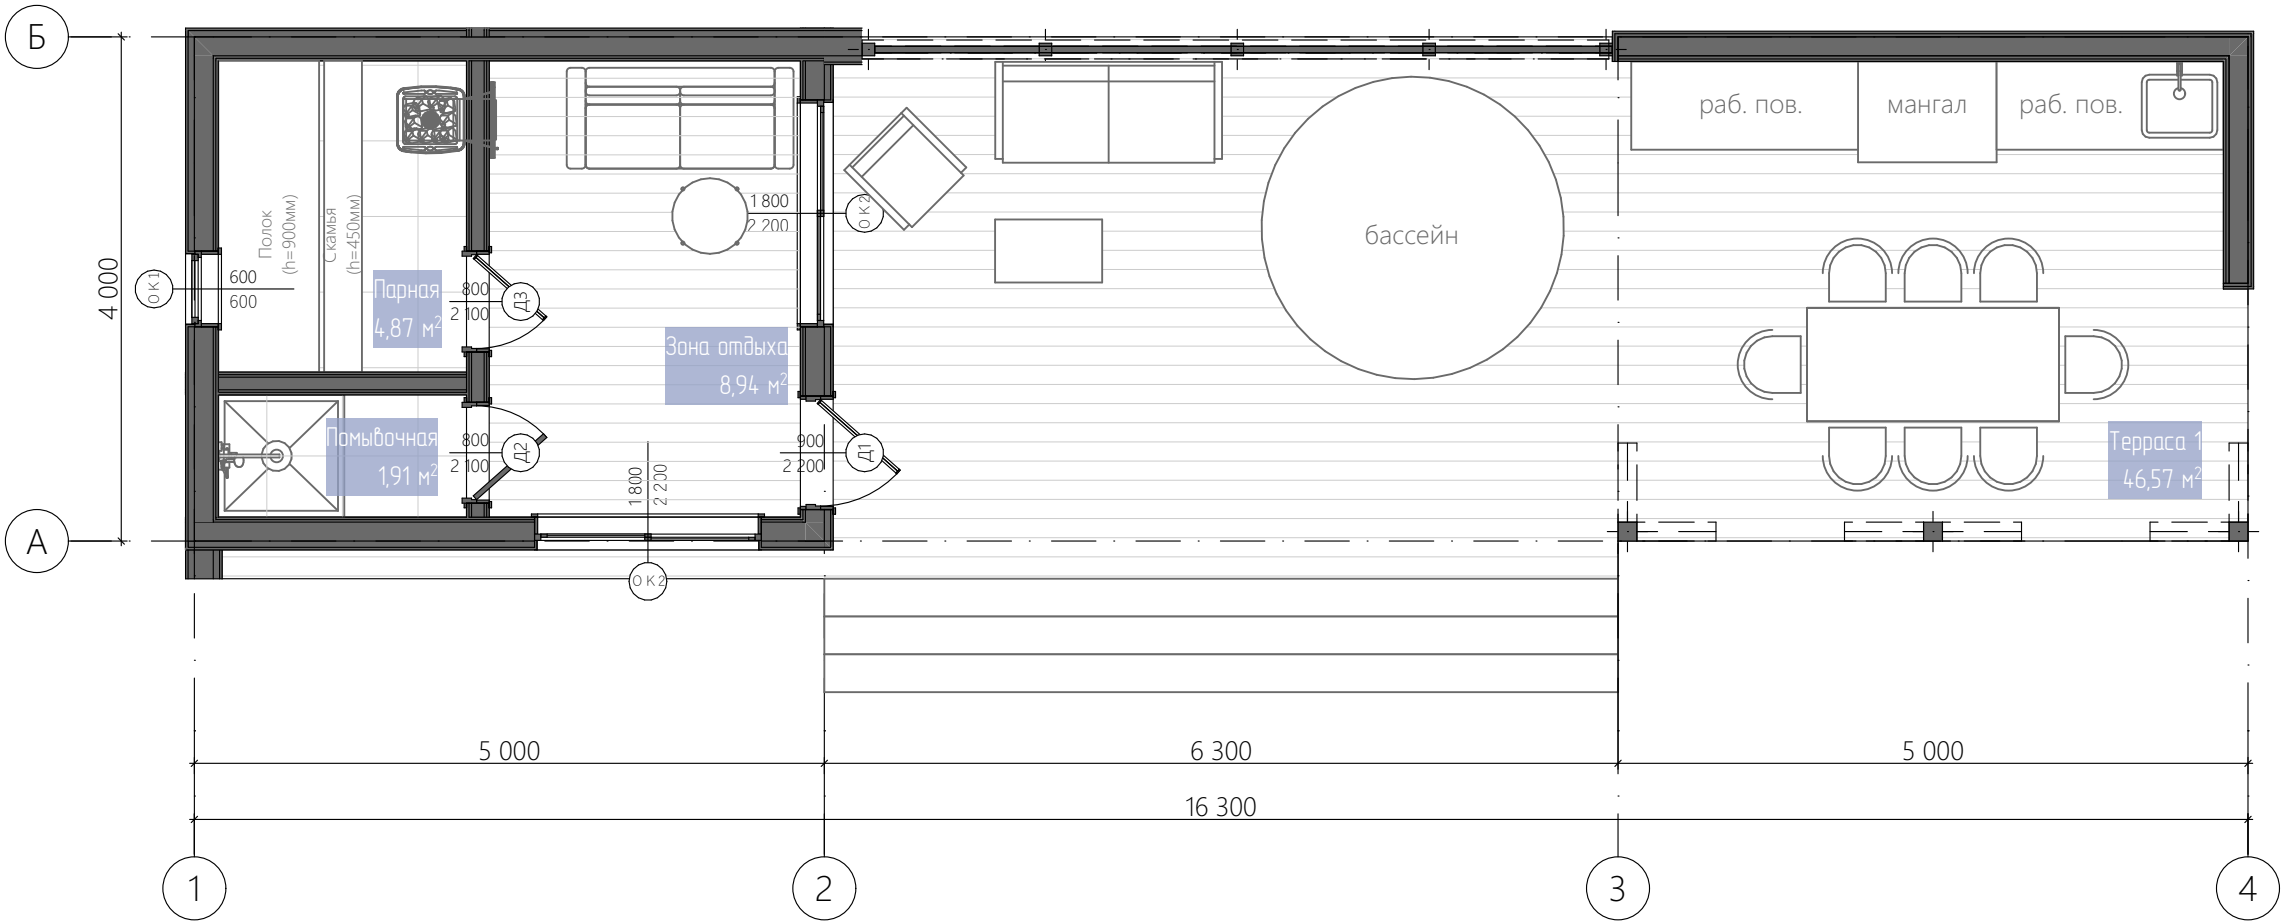

Экспликация помещений		
№	Название	Площадь, м2
1	Парная	4,87
2	Помывочная	1,91
3	Зона отдыха	8,94
4	Терраса 1	46,57
		62,29 м²
Название		Площадь, м2
Площадь застройки		71,35
Примечание:		
1. Вся индивидуальная мебель выполняется по отдельному проекту с детальной проработкой и калькуляцией. Чертежи предоставляет фирма-изготовитель столярных изделий.		
2. Данный проект отдельно согласовывается с автором проекта и непосредственно с заказчиком.		
3. Цветовое решение фасада и материалов отделки показаны в проекте приблизительно.		
4. Количество ступеней показано условно.		
#Название Организации		Лист
		5

Согласовано				
И-нв. № подл.	Подп. и дата	Взам. инв. №		

Лист	Изм.	№ Докум.	Подп.	Дата	Российская Федерация, Московская область, Можайский городской округ, город Можайск, улица Царская, 27; 50:18:0030306:1291

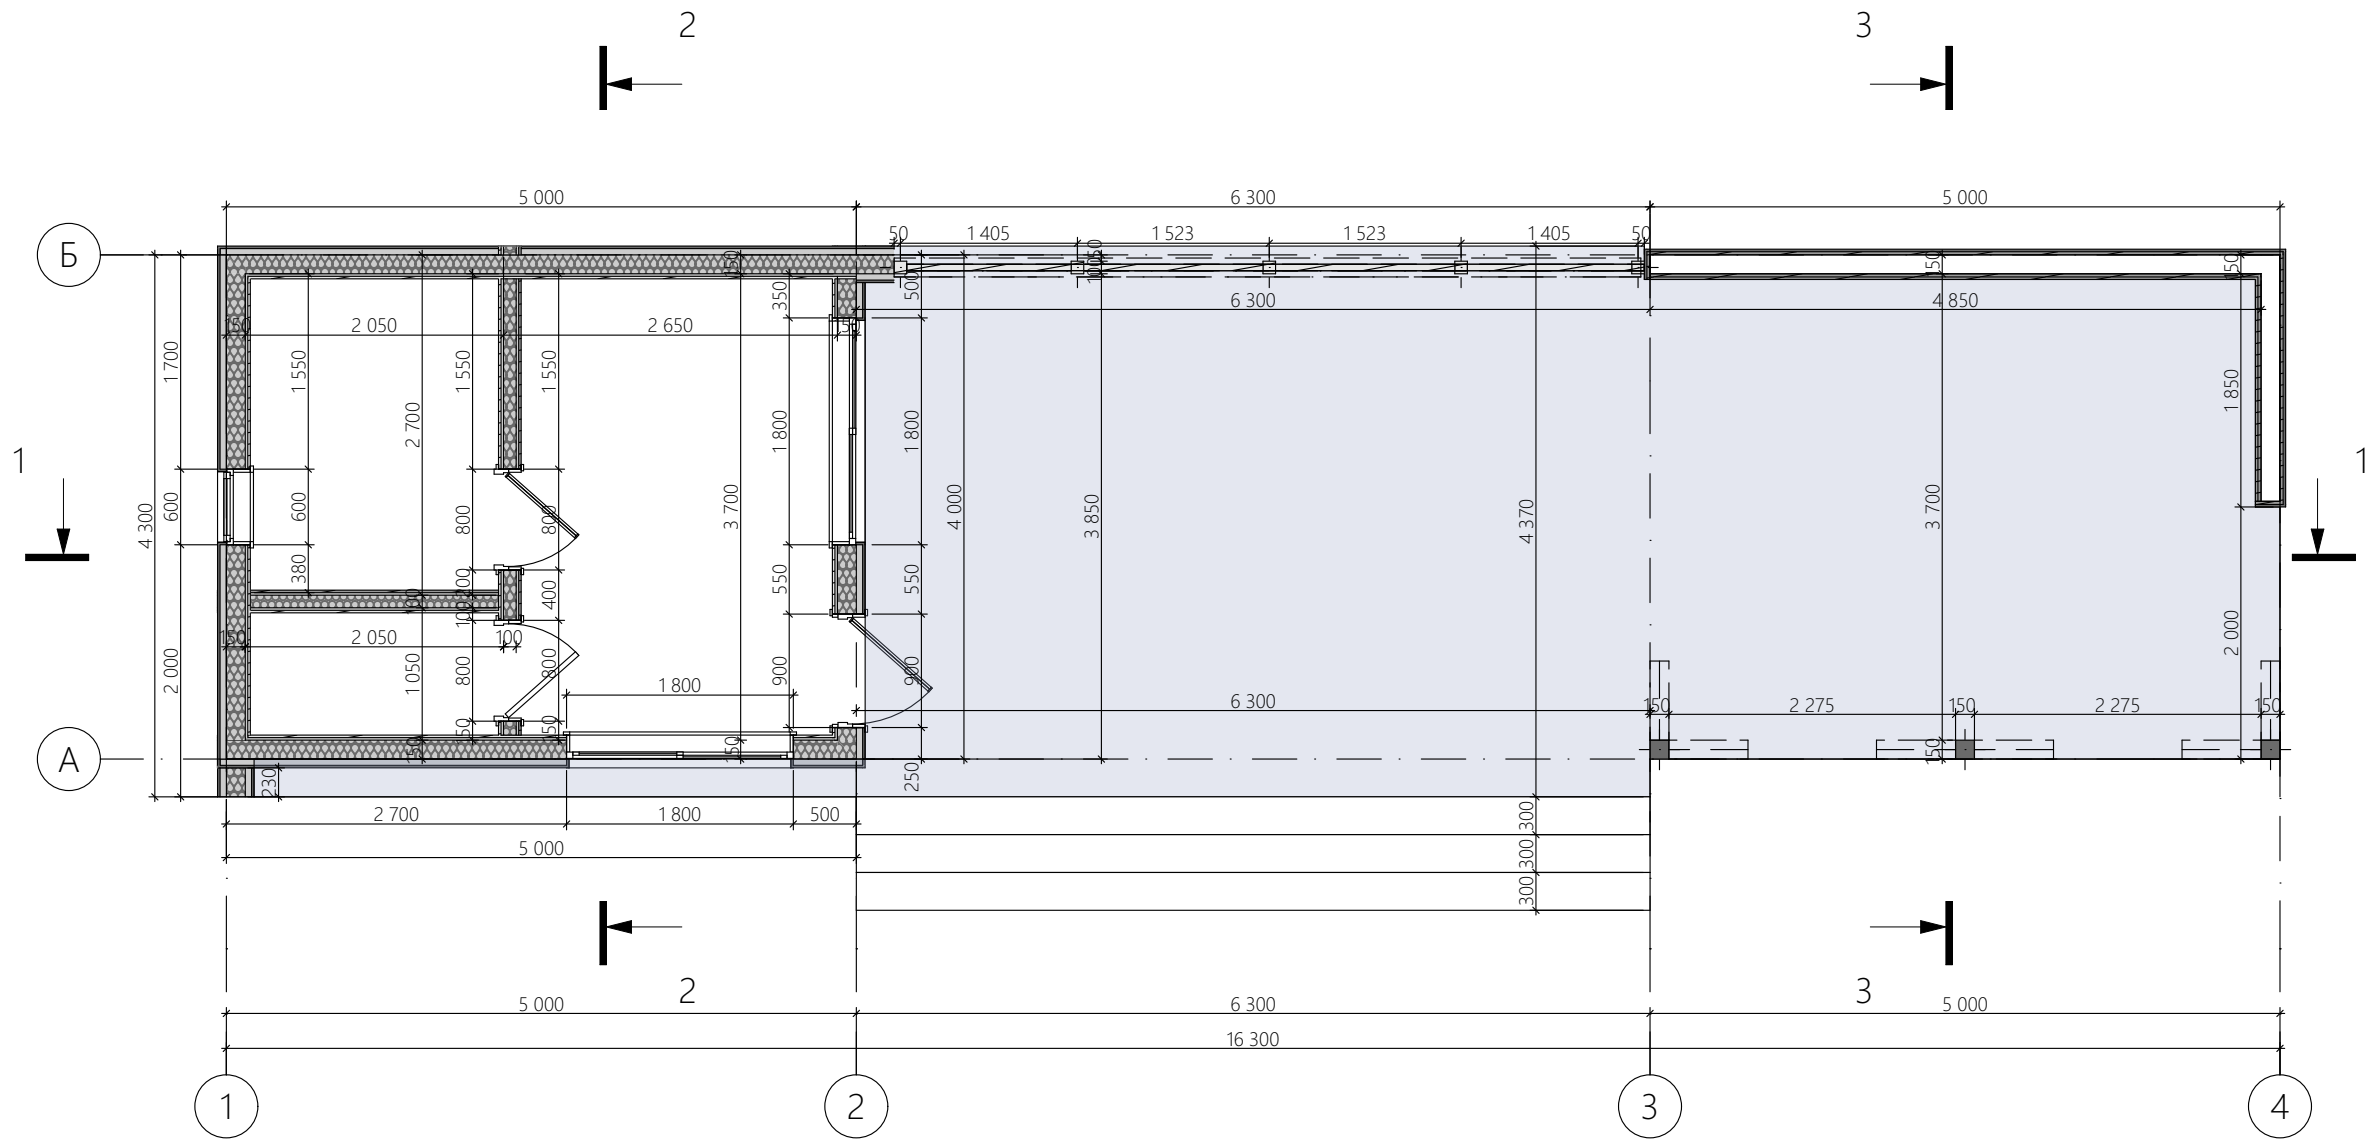

Согласовано				

Инов. № подл.	Подп. и дата	Взам. инв. №	


Лист	Изм.	№ Докум.	Подп.	Дата

Российская Федерация, Московская область, Можайский городской округ, город Можайск, улица Царская, 27; 50:18:0030306:1291

Размерный план

Примечание:
1. Представленные размеры указаны без учета внешней и внутренней отделки

#Название Организации	Лист
	6

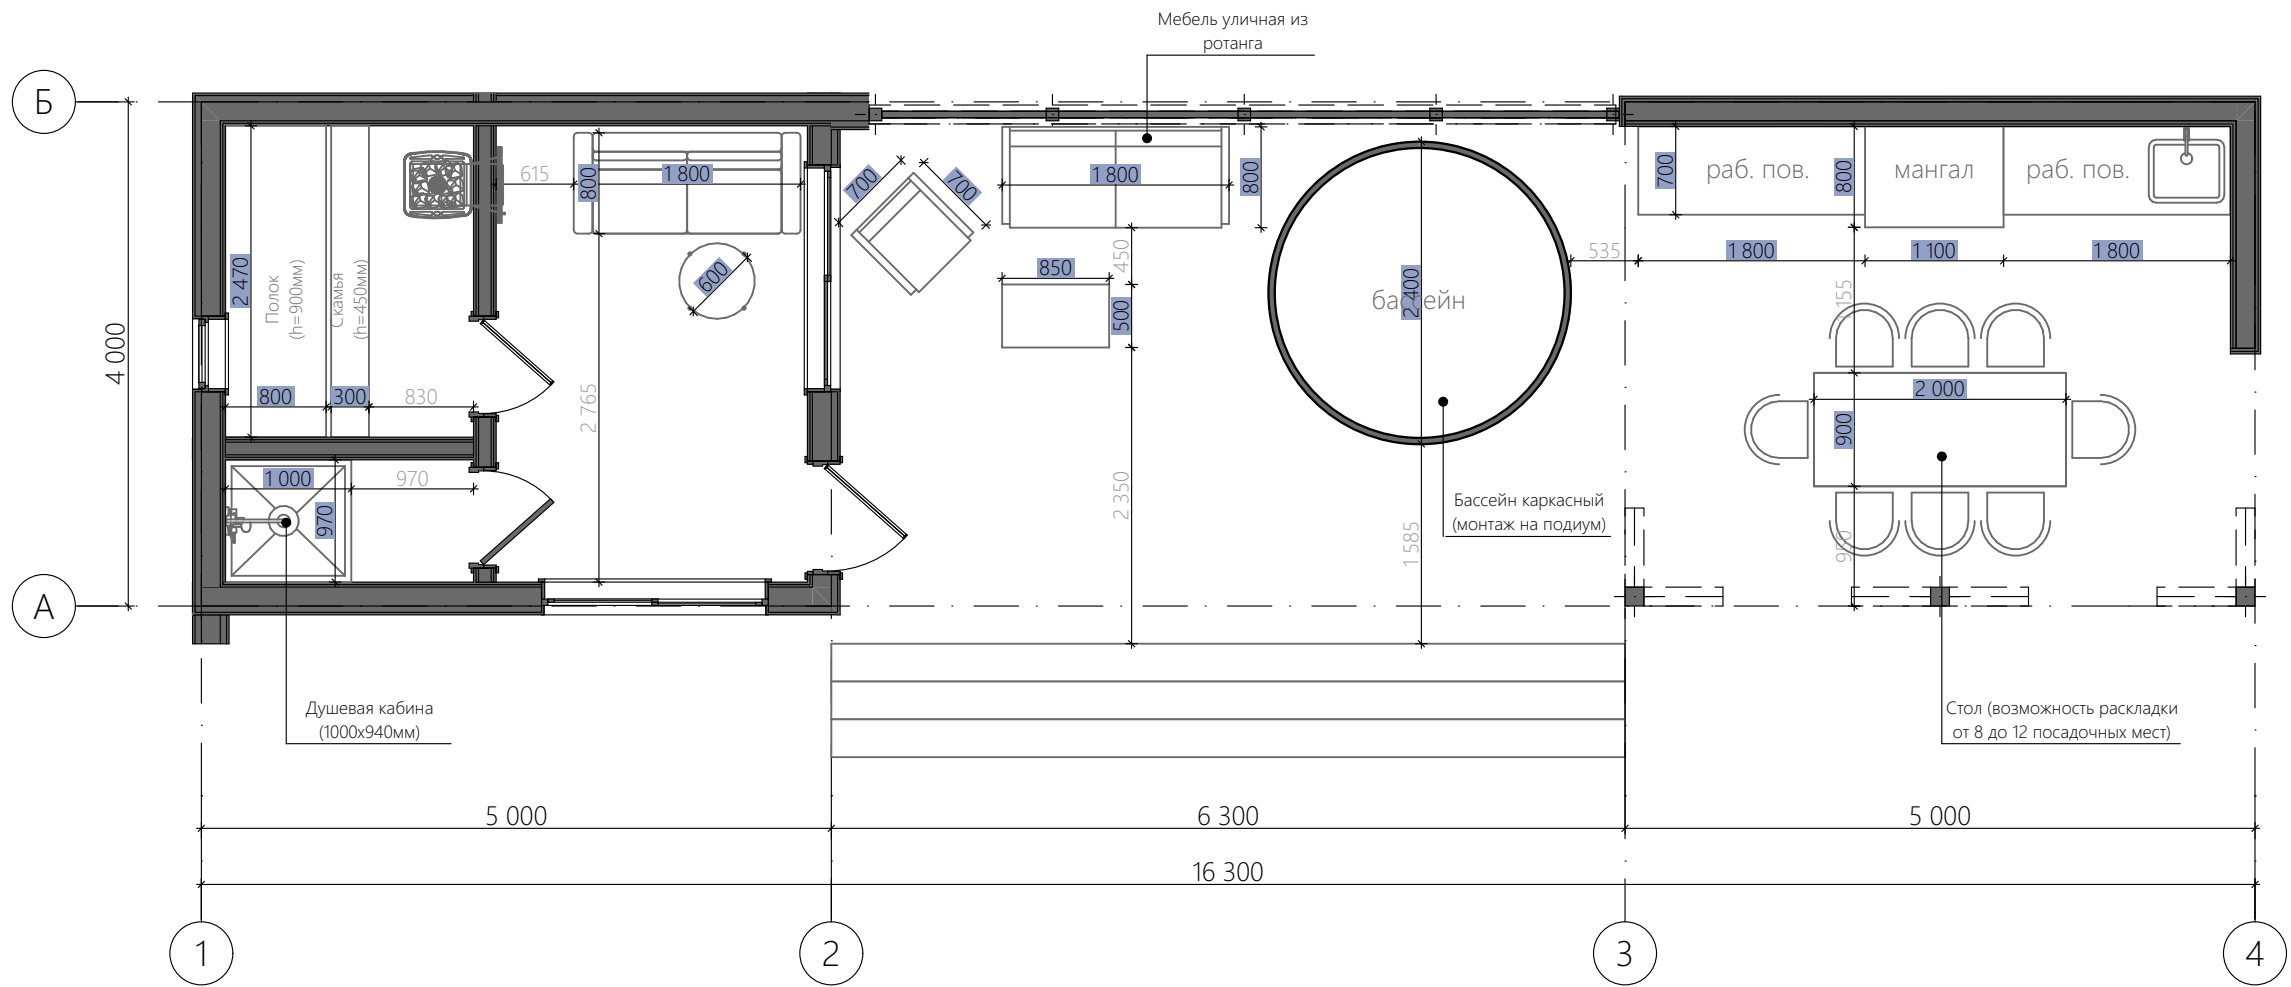

Примечание:

1. Вся индивидуальная мебель выполняется по отдельному проекту с детальной проработкой и калькуляцией. Чертежи предоставляет фирма-изготовитель столярных изделий.


2. Финальные размеры мебели и оборудования указаны ориентировочно — для точной компоновки требуется разработка дизайн-проекта.

Согласовано					
И-нв. № подл.	Подп. и дата	Взам. инв. №			
			Лист	Изм.	№ Докум.
			Подп.	Дата	Российская Федерация, Московская область, Можайский городской округ, город Можайск, улица Царская, 27; 50:18:0030306:1291

Душевая кабина
(1000х940мм)

1

Согласовано

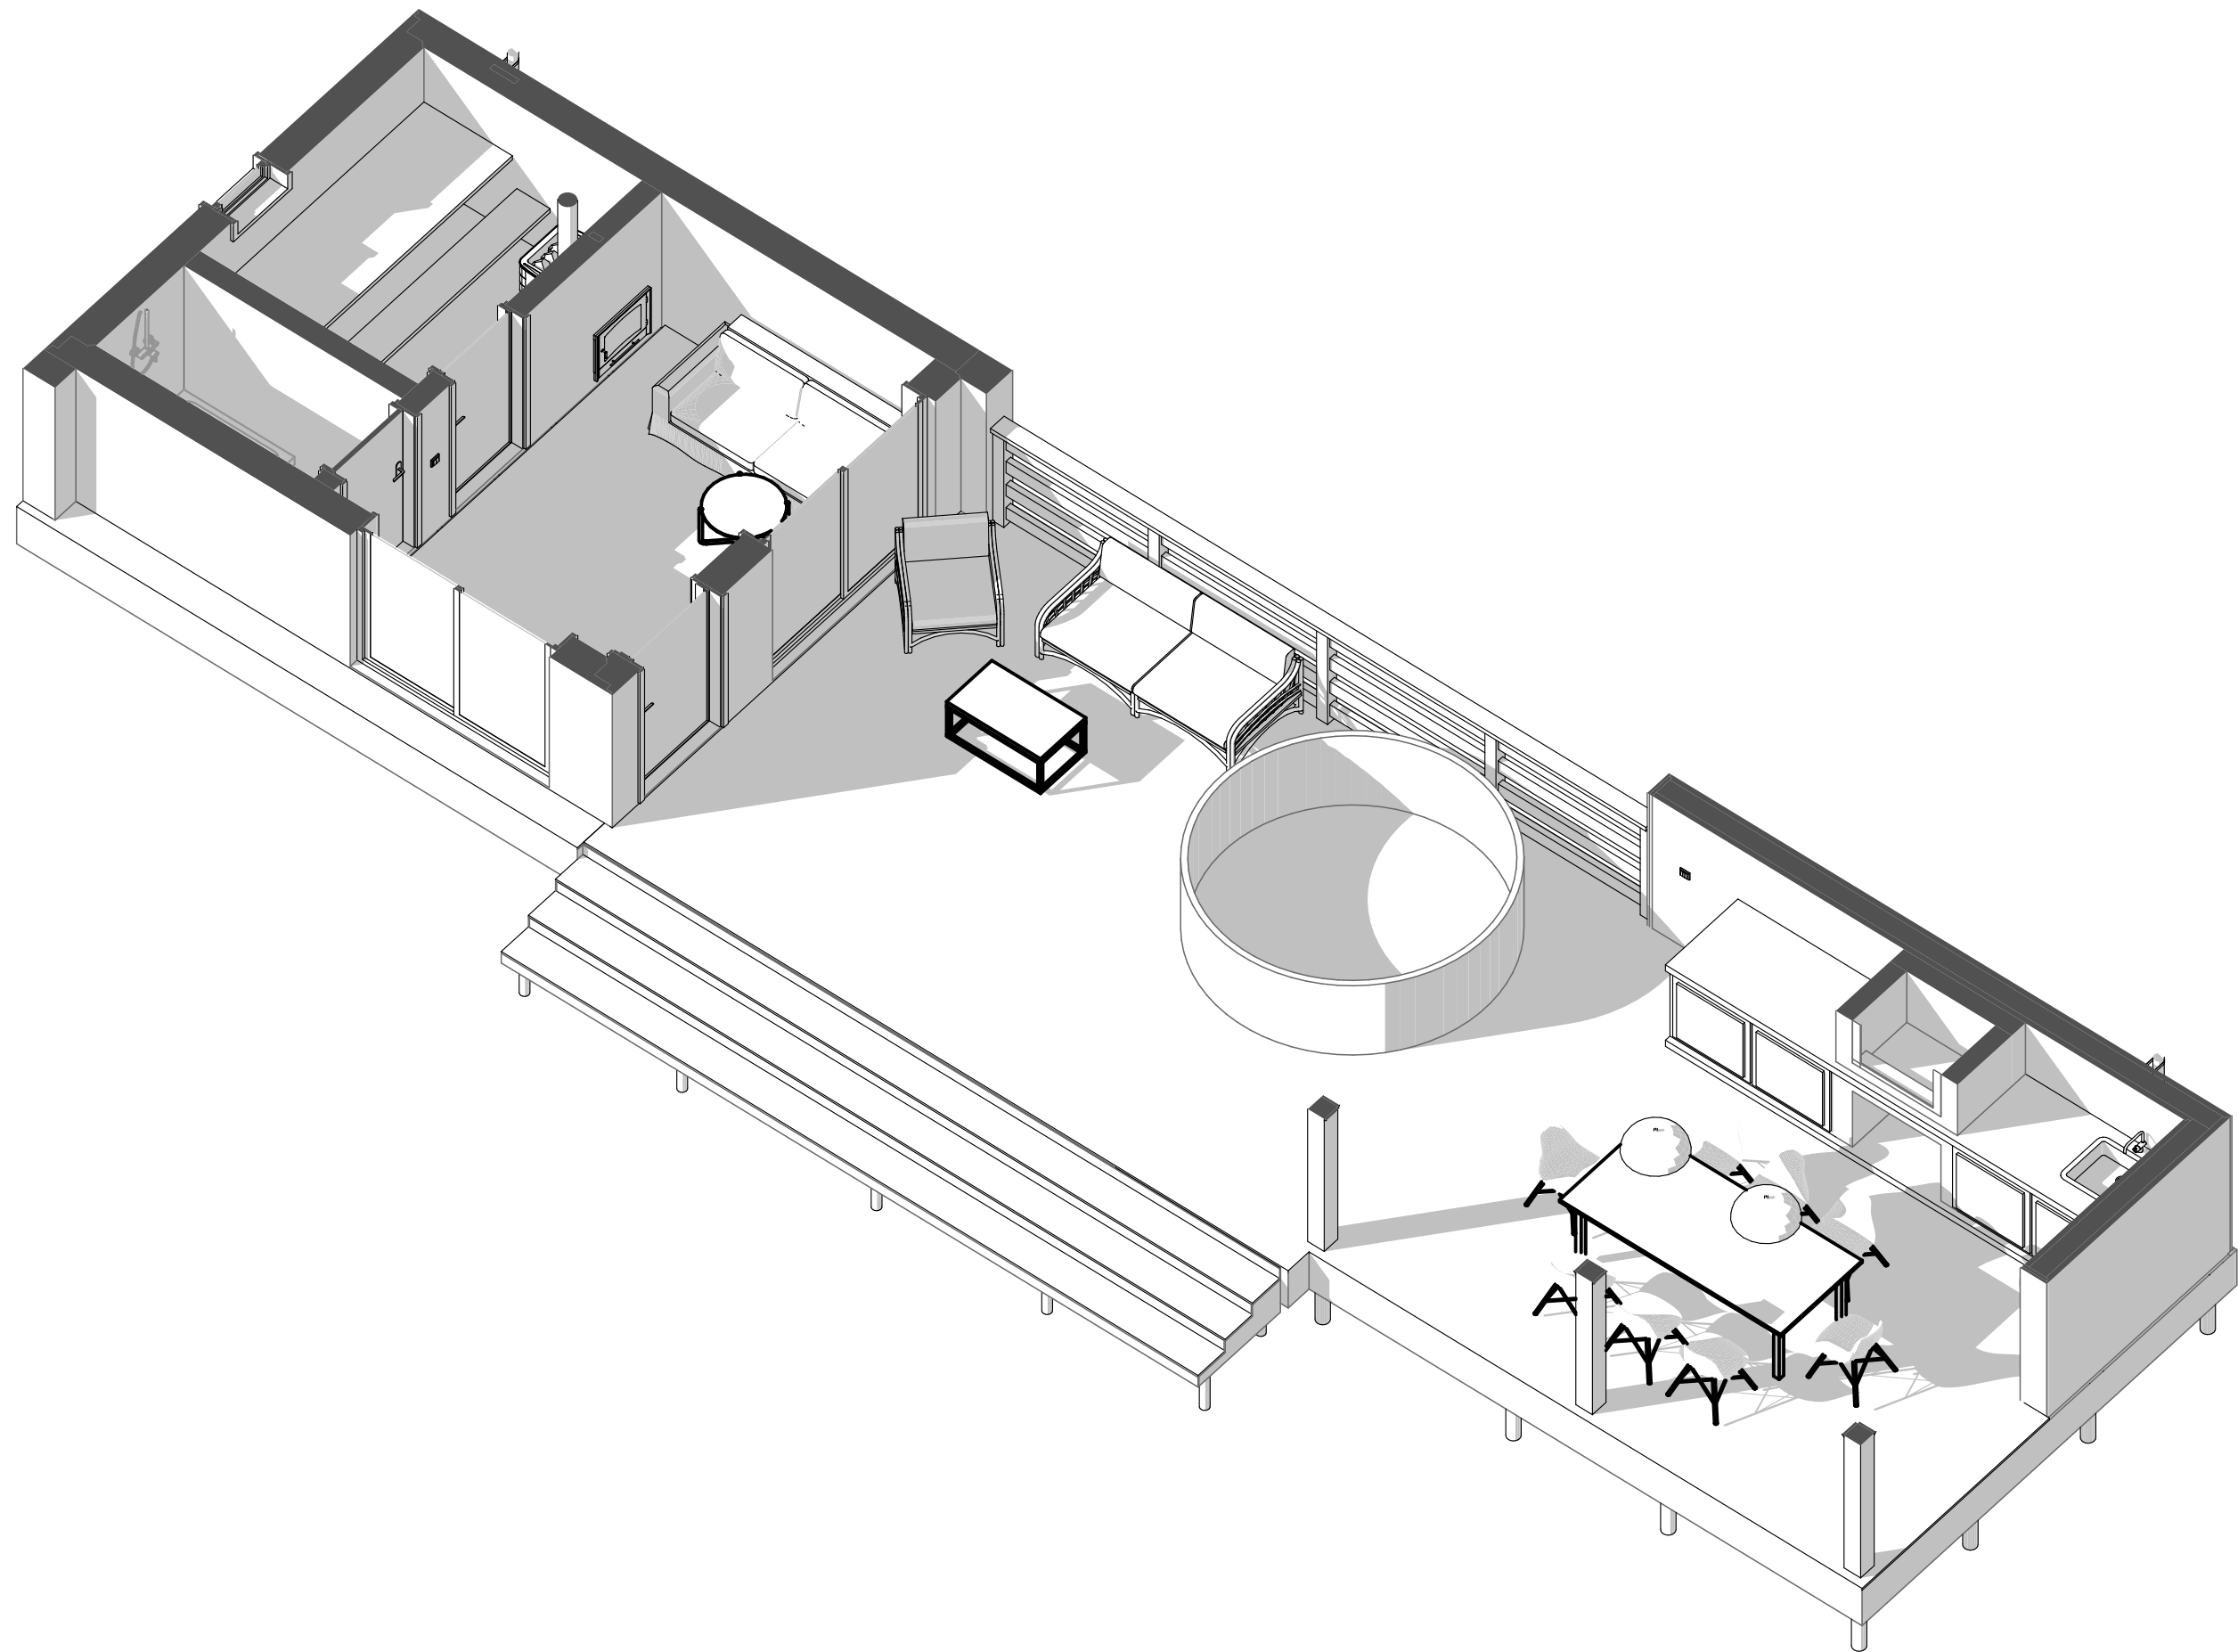

Инва. № подл. Подп. и дата Взам. инв. №

Лист	Изм.	№ Докум.	Подп.	Дата

Российская Федерация, Московская область, Можайский городской округ, город Можайск, улица Царская, 27;
50:18:0030306:1291


Зд-разрез

#Название Организации


Лист
8

План покрытия пола

1:60

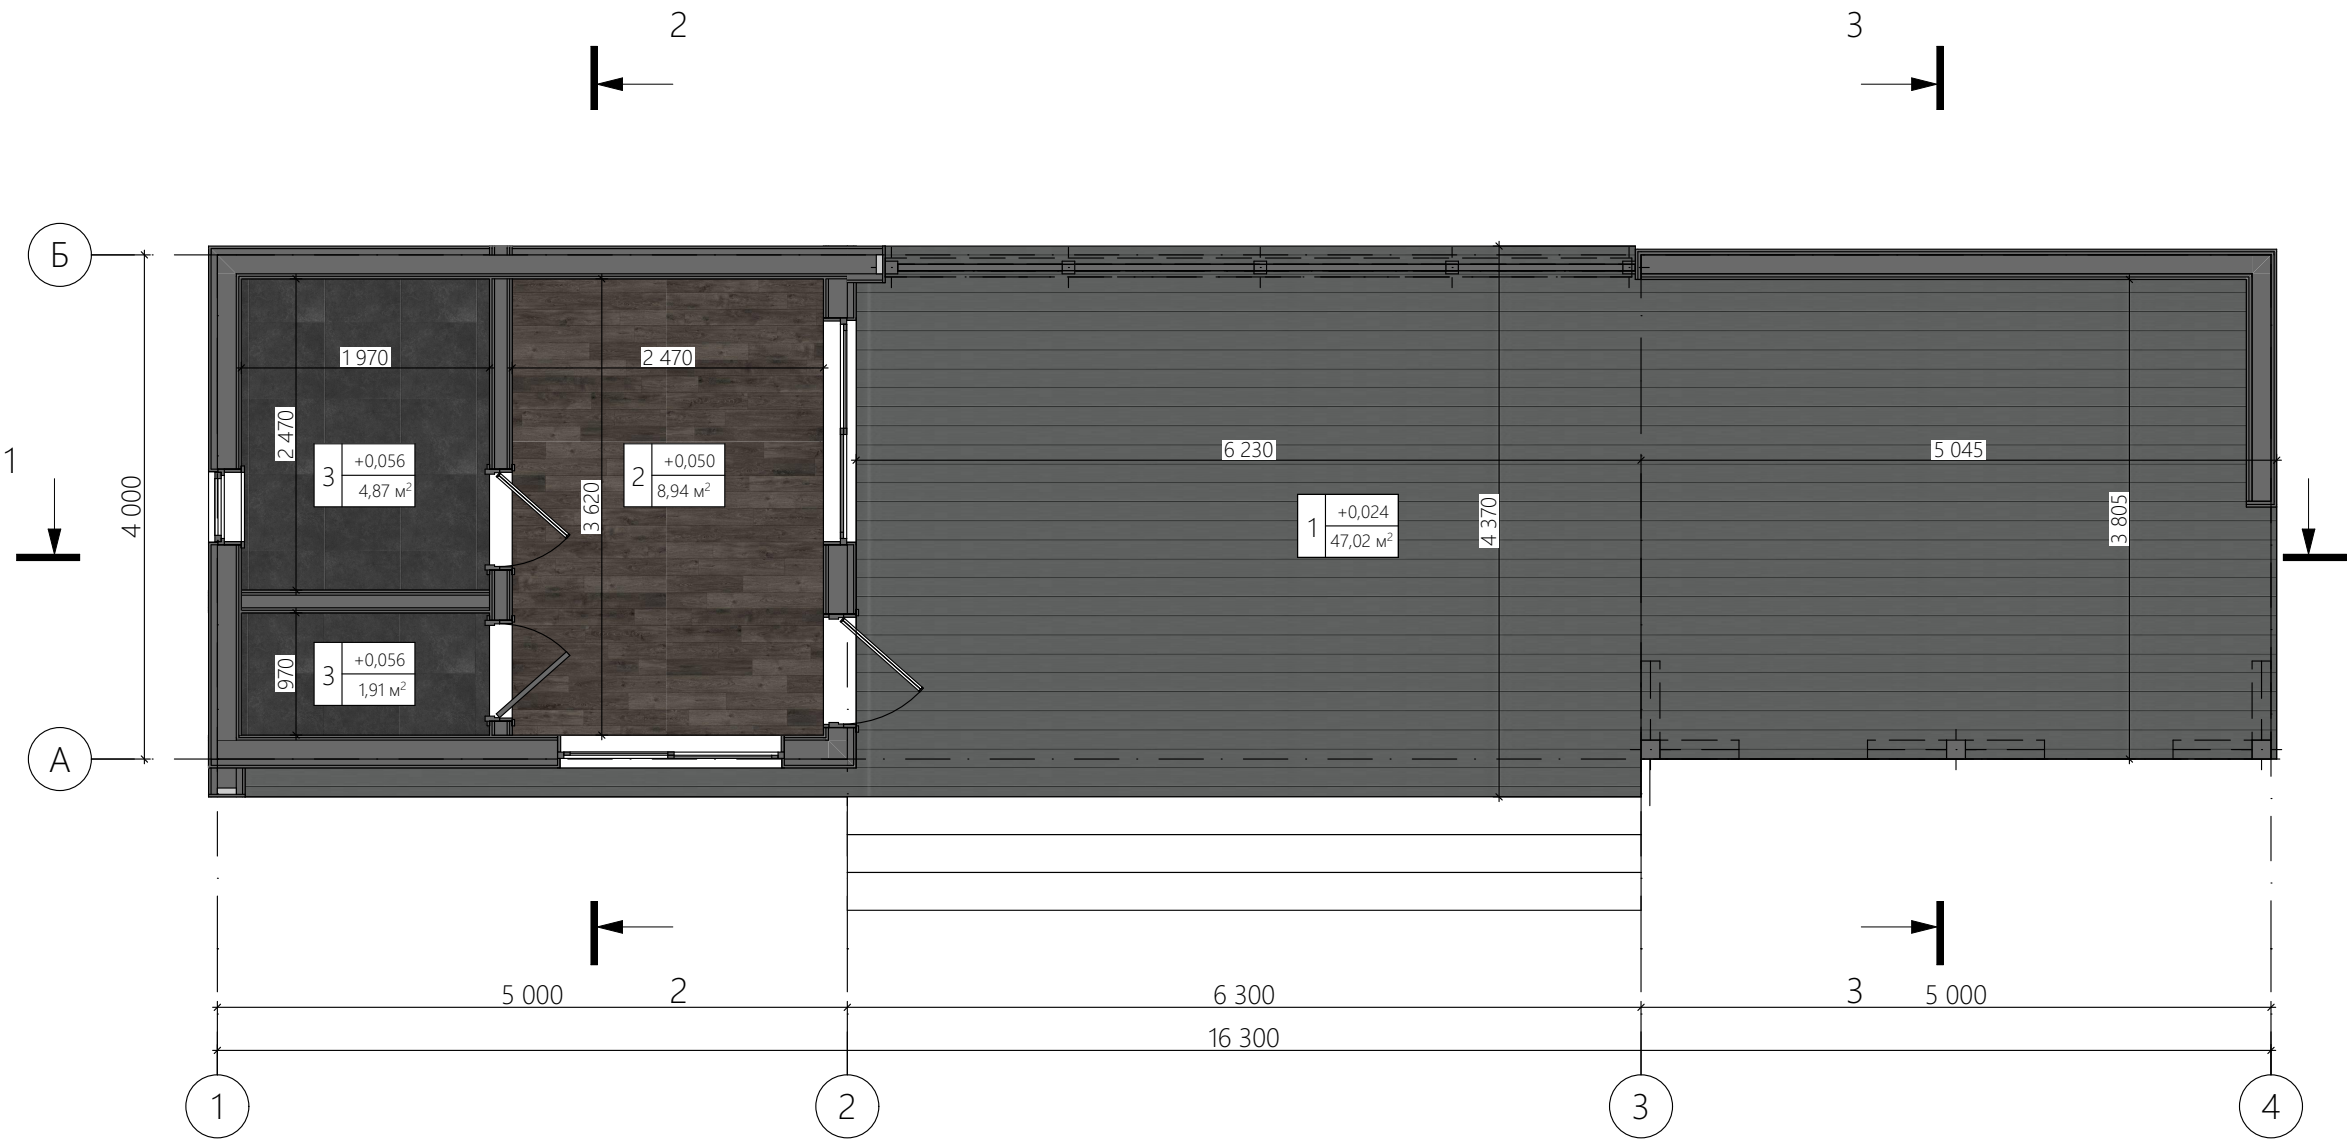

Условные обозначения

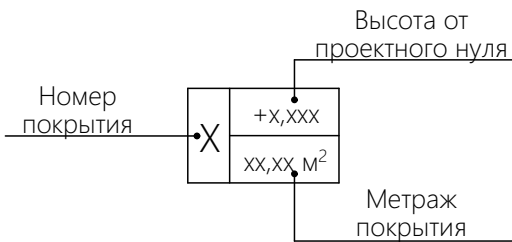

Экспликация покрытий пола

№	Наименование	Площадь, м²
1	Террасная доска	41,02
2	Шпунтованная доска	8,76
3	Керамогранит	6,55

Примечание:

1. Приведённые цветовые решения носят рекомендательный характер. Фактический подбор оттенков и материалов выполняется на этапе реализации с учётом наличия продукции у поставщиков и утверждения заказчиком.
2. Пирог покрытия смотреть на след. листе.

Согласовано

Взам. инв. №

Подп. и дата




Инв. № подл.

Лист	Изм.	№ Докум.	Подп.	Дата

Российская Федерация, Московская область, Можайский городской округ, город Можайск, улица Царская, 27; 50:18:0030306:1291

План покрытия пола


#Название Организации

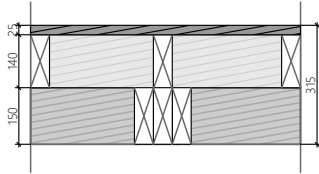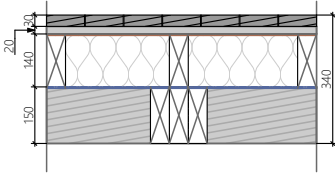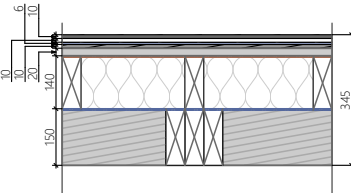Пироги пола									
№		Наименование		Разрез		Состав			
1		Террасная доска				-Террасная доска (ДПК)25мм -Лага перекрытия (шаг 400мм)140мм -Нижняя обвязка (тройная сращенная доска)150мм			
2		Шпунтованная доска				-Шпунтованная доска30мм -Обрешетка (шаг 400мм)20мм -Пароизоляционная мембрана -Лага перкрытия (шаг 600мм)140мм (с утеплителем в теле) -Гидро-ветрозащитная мембрана -Просейчка (ячейка 5х5мм) -Обрешетка (шаг 400мм)25мм -Нижняя обвязка (тройная сращенная доска)150мм			
3		Керамогранит				-Керамогранит10мм -Клей10мм -Руспанель6мм -ЦСП10мм -ОСБ20мм -Пароизоляционная мембрана -Лага перкрытия (шаг 600мм)140мм (с утеплителем в теле) -Гидро-ветрозащитная мембрана -Просейчка (ячейка 5х5мм) -Обрешетка (шаг 400мм)25мм -Нижняя обвязка (тройная сращенная доска)150мм			
Ив. № подл.		Подп. и дата		Взам. инв. №					
Лист		Изм.		№ Докум.		Подп.		Дата	
Пироги пола						#Название Организации			
						Лист			
						10			

Согласовано

План покрытия стен

1:60

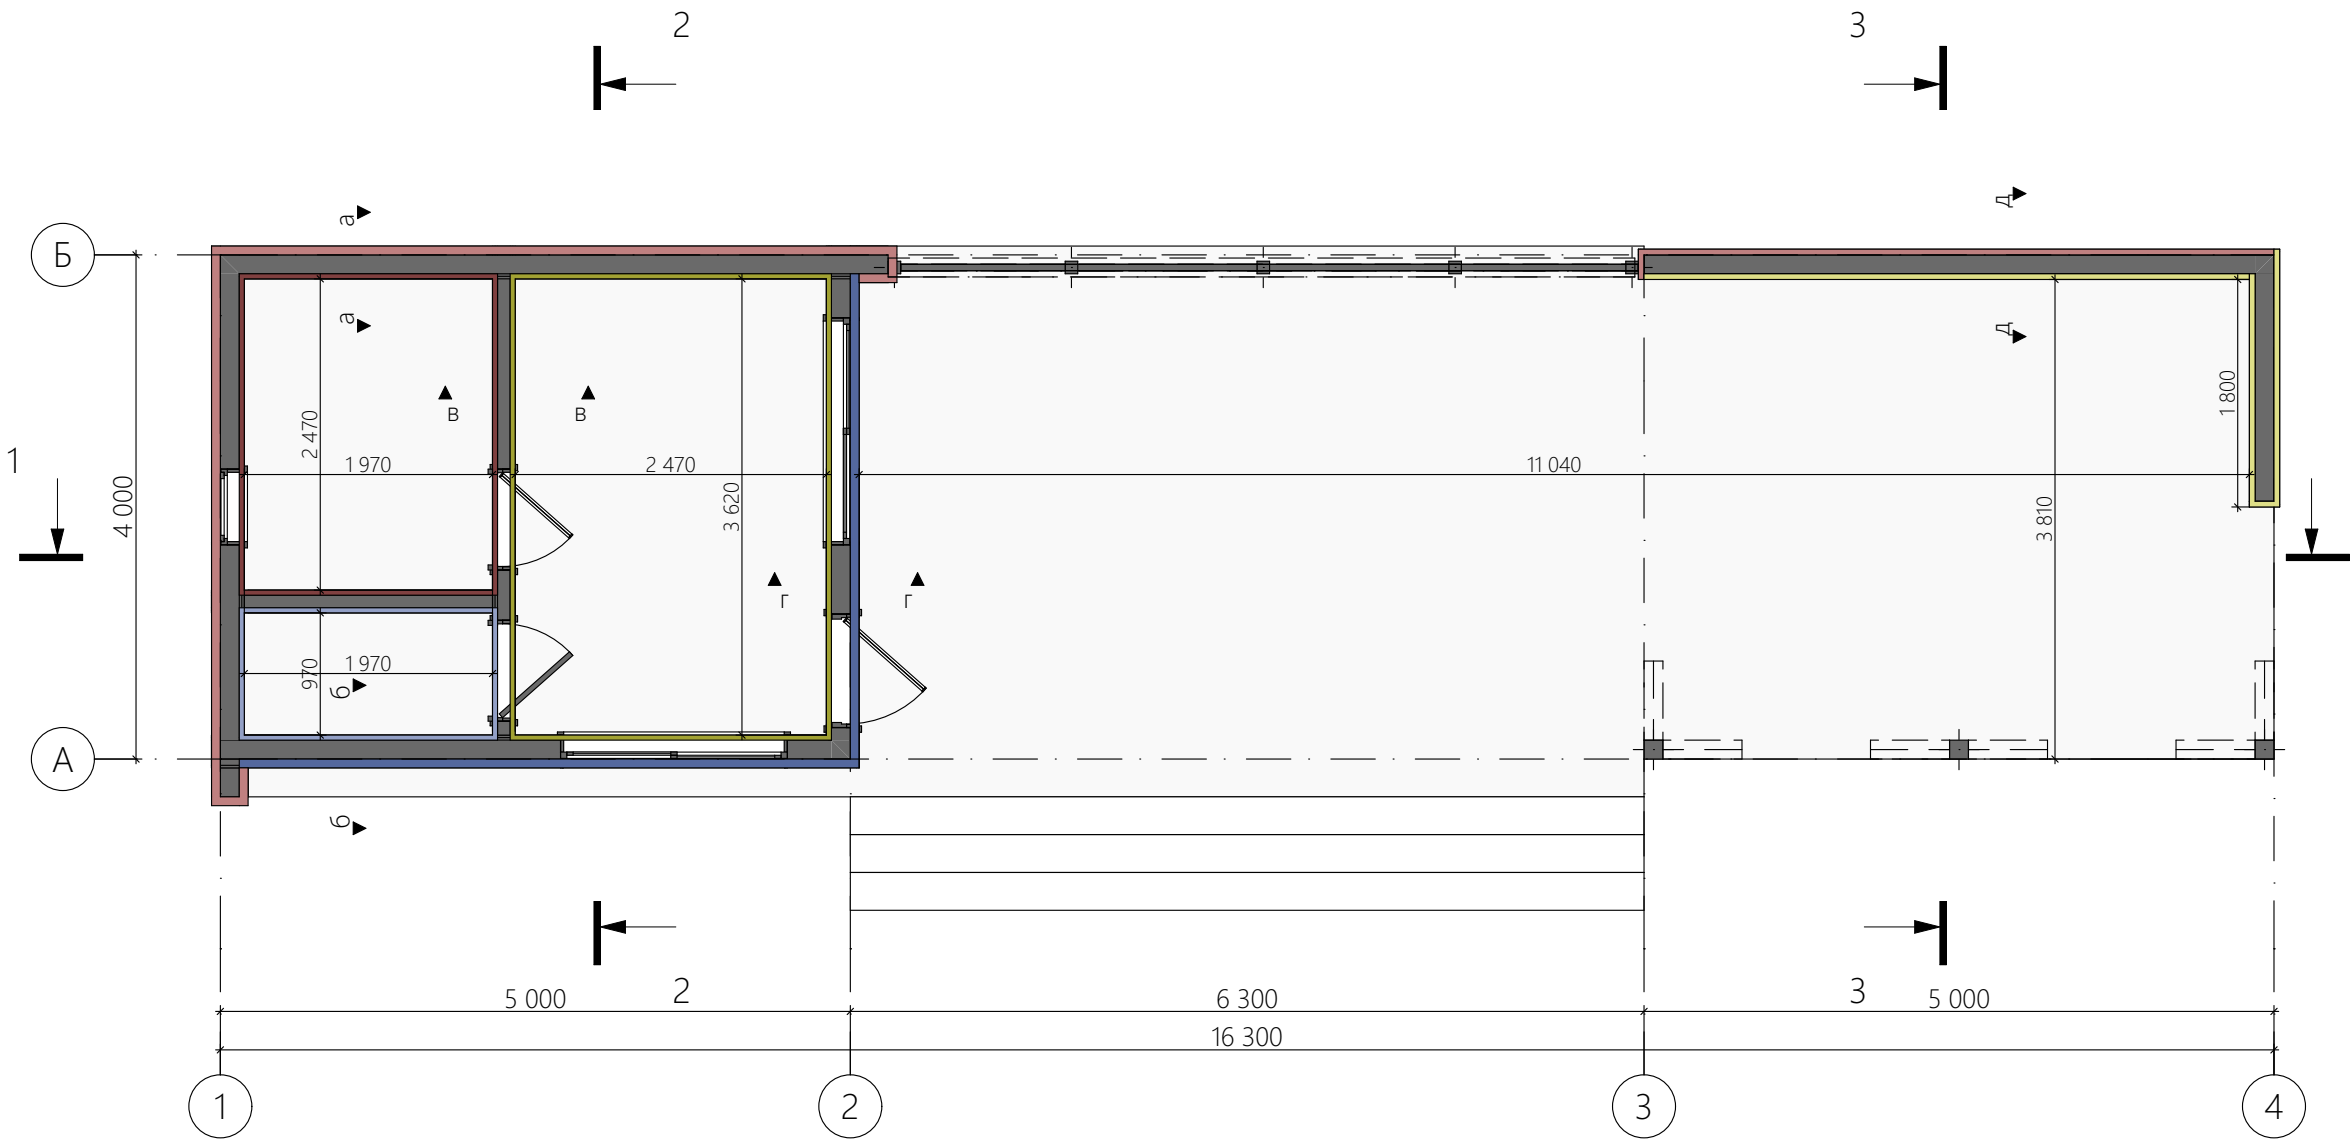

Экспликация покрытий стен

№	Наименование	Условное обозначение
1	Планкен (20мм)	
2	Фальцевые листы (20мм)	
3	Каньон (20мм)	
4	Имитация бруса (20мм)	
5	Вагонка (16мм)	
6	Керамогранит (10мм)	

Согласовано

Взам. инв. №

Подп. и дата

Инв. № подл.

Лист	Изм.	№ Докум.	Подп.	Дата

Российская Федерация, Московская область, Можайский городской округ, город Можайск, улица Царская, 27; 50:18:0030306:1291

План покрытия стен

#Название Организации


Пироги пола

№ разреза

Сечение


Состав

а-а

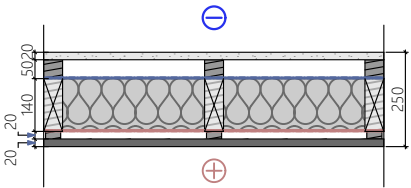


-Фиброцементный сайдинг	20мм
-Вентбрус (вертикально)	50мм
-Гидро-ветрозащитная мембрана	-
-Стойка каркаса (утепленная)	140мм
-Пароизоляционная мембрана (алюм. фольга)	-
-Вентбрус (вертикально)	20мм
-Вагонка	20мм

б-б

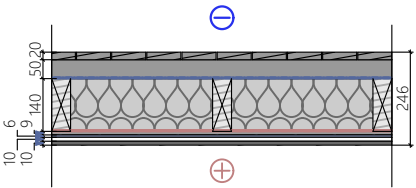


-Планкен	20мм
-Вентбрус (горизонтально)	50мм
-Гидро-ветрозащитная мембрана	-
-Стойка каркаса (утепленная)	140мм
-Пароизоляционная мембрана	-
-ОСБ	9мм
-Руспанель	6мм
-Клей	10мм
-Керамогранит	10мм

в-в

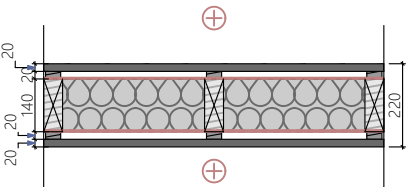


-Вагонка	20мм
-Вентбрус (вертикально)	20мм
-Пароизоляционная мембрана (алюм. фольга)	-
-Стойка каркаса (утепленная)	140мм
-Пароизоляционная мембрана	-
-Вентбрус (вертикально)	20мм
-Имитация бруса	20мм

г-г

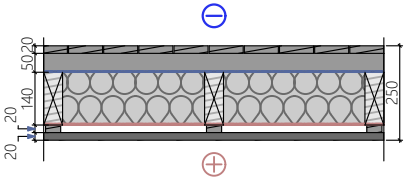

-Планкен	20мм
-Вентбрус (горизонтально)	50мм
-Гидро-ветрозащитная мембрана	-
-Стойка каркаса (утепленная)	140мм
-Пароизоляционная мембрана	-
-Вентбрус (вертикально)	20мм
-Имитация бруса	20мм

д-д

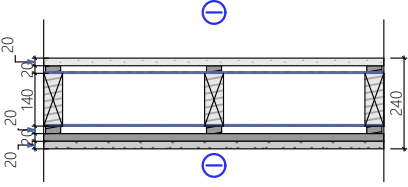

-Фиброцементные панели	20мм
-Вентбрус (ветикально)	20мм
-Гидро-ветрозащитная мембрана	-
-Стойка каркаса	140
-Гидро-ветрозащитная мембрана	-
-Вентбрус (вертикально)	20мм
-Вентбрус (горизонтально)	20мм
-Каньон	20мм

Согласовано

Взам. инв. №

Подп. и дата

Инв. № подл.


Лист	Изм.	№ Докум.	Подп.	Дата

Пироги стены

#Название Организации

План размещения розеток

1:60

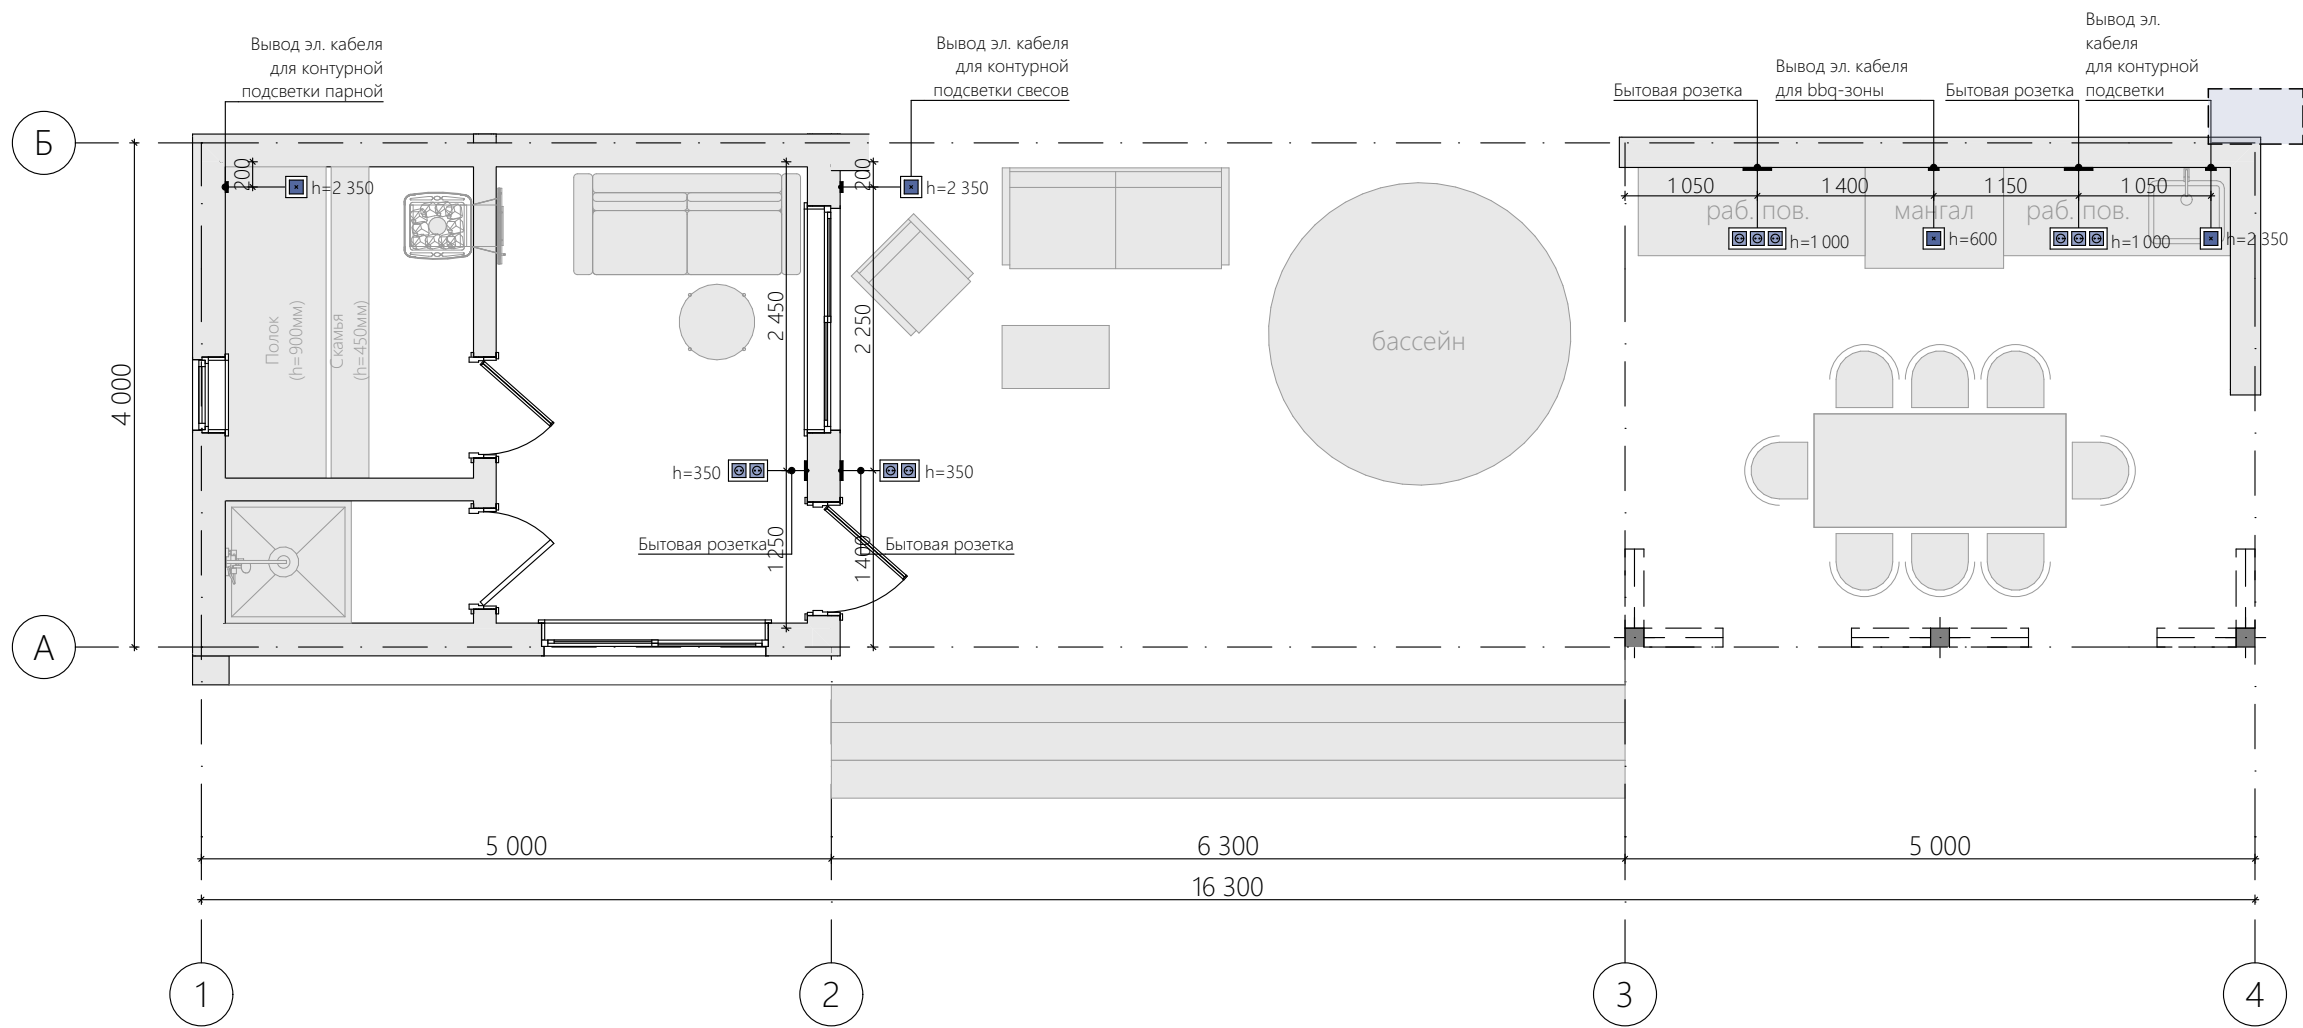

Экспликация розеток

Наименование	2д-вид	Кол-во
Розетка 220v (2 секции)		2
Розетка 220v (3 секции)		2
Эл. вывод (влагозащитная)		4
		8

Примечание:

1. Схема размещения розеток является рекомендательной и требует согласования с заказчиком по месту.
2. Все высоты даны от чистового пола.
3. Все указанные размеры даются до центра позиций.
4. Отметки розеток, выключателей, выводов и др. оборудования, являются предварительными и уточняются после выбора финишных материалов и мебели.
5. Размеры уточняются дополнительно

Согласовано

Взам. инв. №

Подп. и дата

Инв. № подл.

Лист	Изм.	№ Докум.	Подп.	Дата


Российская Федерация, Московская область, Можайский городской округ, город Можайск, улица Царская, 27; 50:18:0030306:1291

План размещения розеток

#Название Организации

План размещения светильников и выключателей

1:60

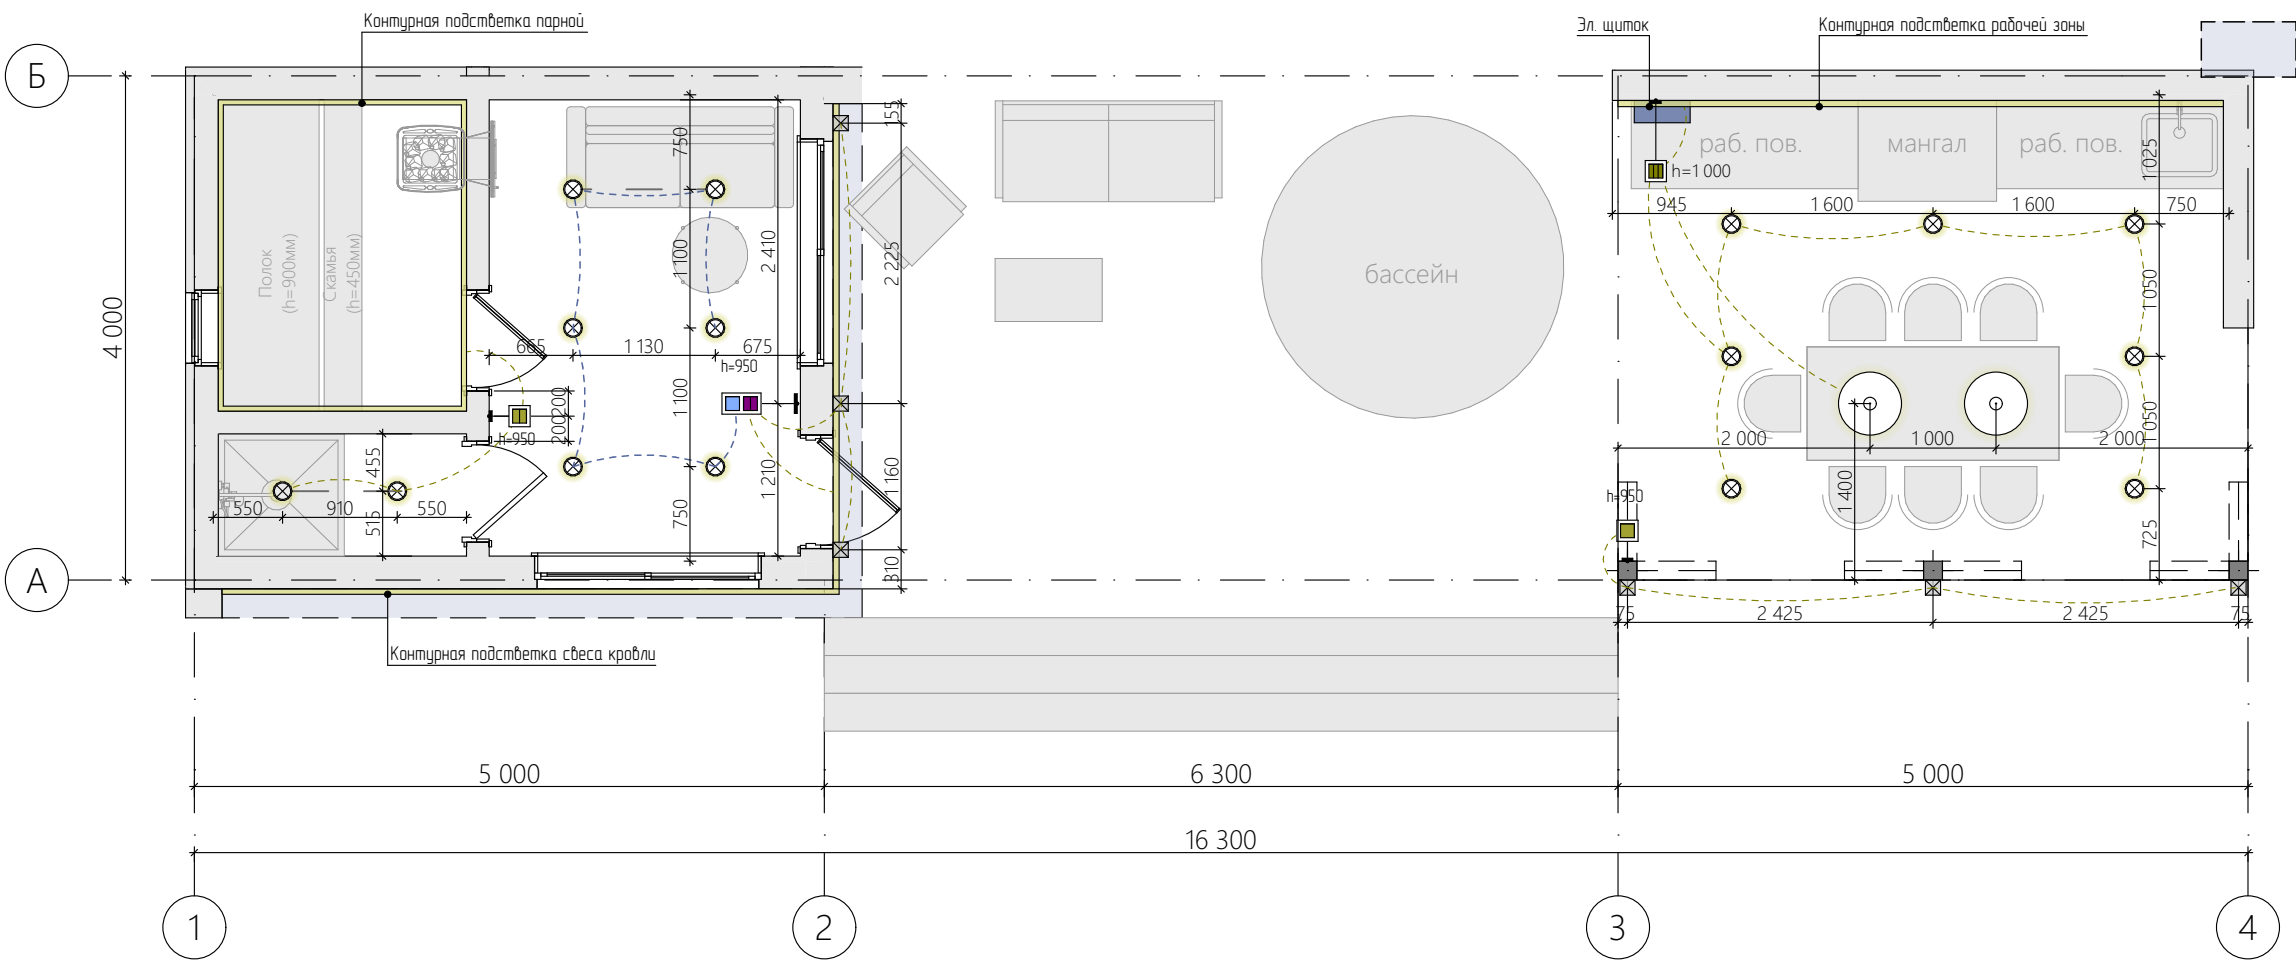

Экспликация светильников и выключателей

Наименование	2д-вид	Кол-во
Выключатель одно- и двухклавишный (2 секции)		1
Выключатель одноклавишный (1 секция)		1
Выключатель одноклавишный (2 секции)		1
Светильник подвесной		2
Точечный светильник		15
Уличный светильник		6
		26

Примечание:

1. Схема размещения розеток является рекомендательной и требует согласования с заказчиком по месту.
2. Все высоты даны от чистового пола.
3. Все указанные размеры даются до центра позиций.
4. Отметки розеток, выключателей, выводов и др. оборудования, являются предварительными и уточняются после выбора финишных материалов и мебели.
5. Размеры уточняются дополнительно

Согласовано

Взам. инв. №

Подп. и дата

Инв. № подл.

Лист	Изм.	№ Докум.	Подп.	Дата


Российская Федерация, Московская область, Можайский городской округ, город Можайск, улица Царская, 27; 50:18:0030306:1291

План размещения светильников и выключателей

#Название Организации

План крыши

1:60

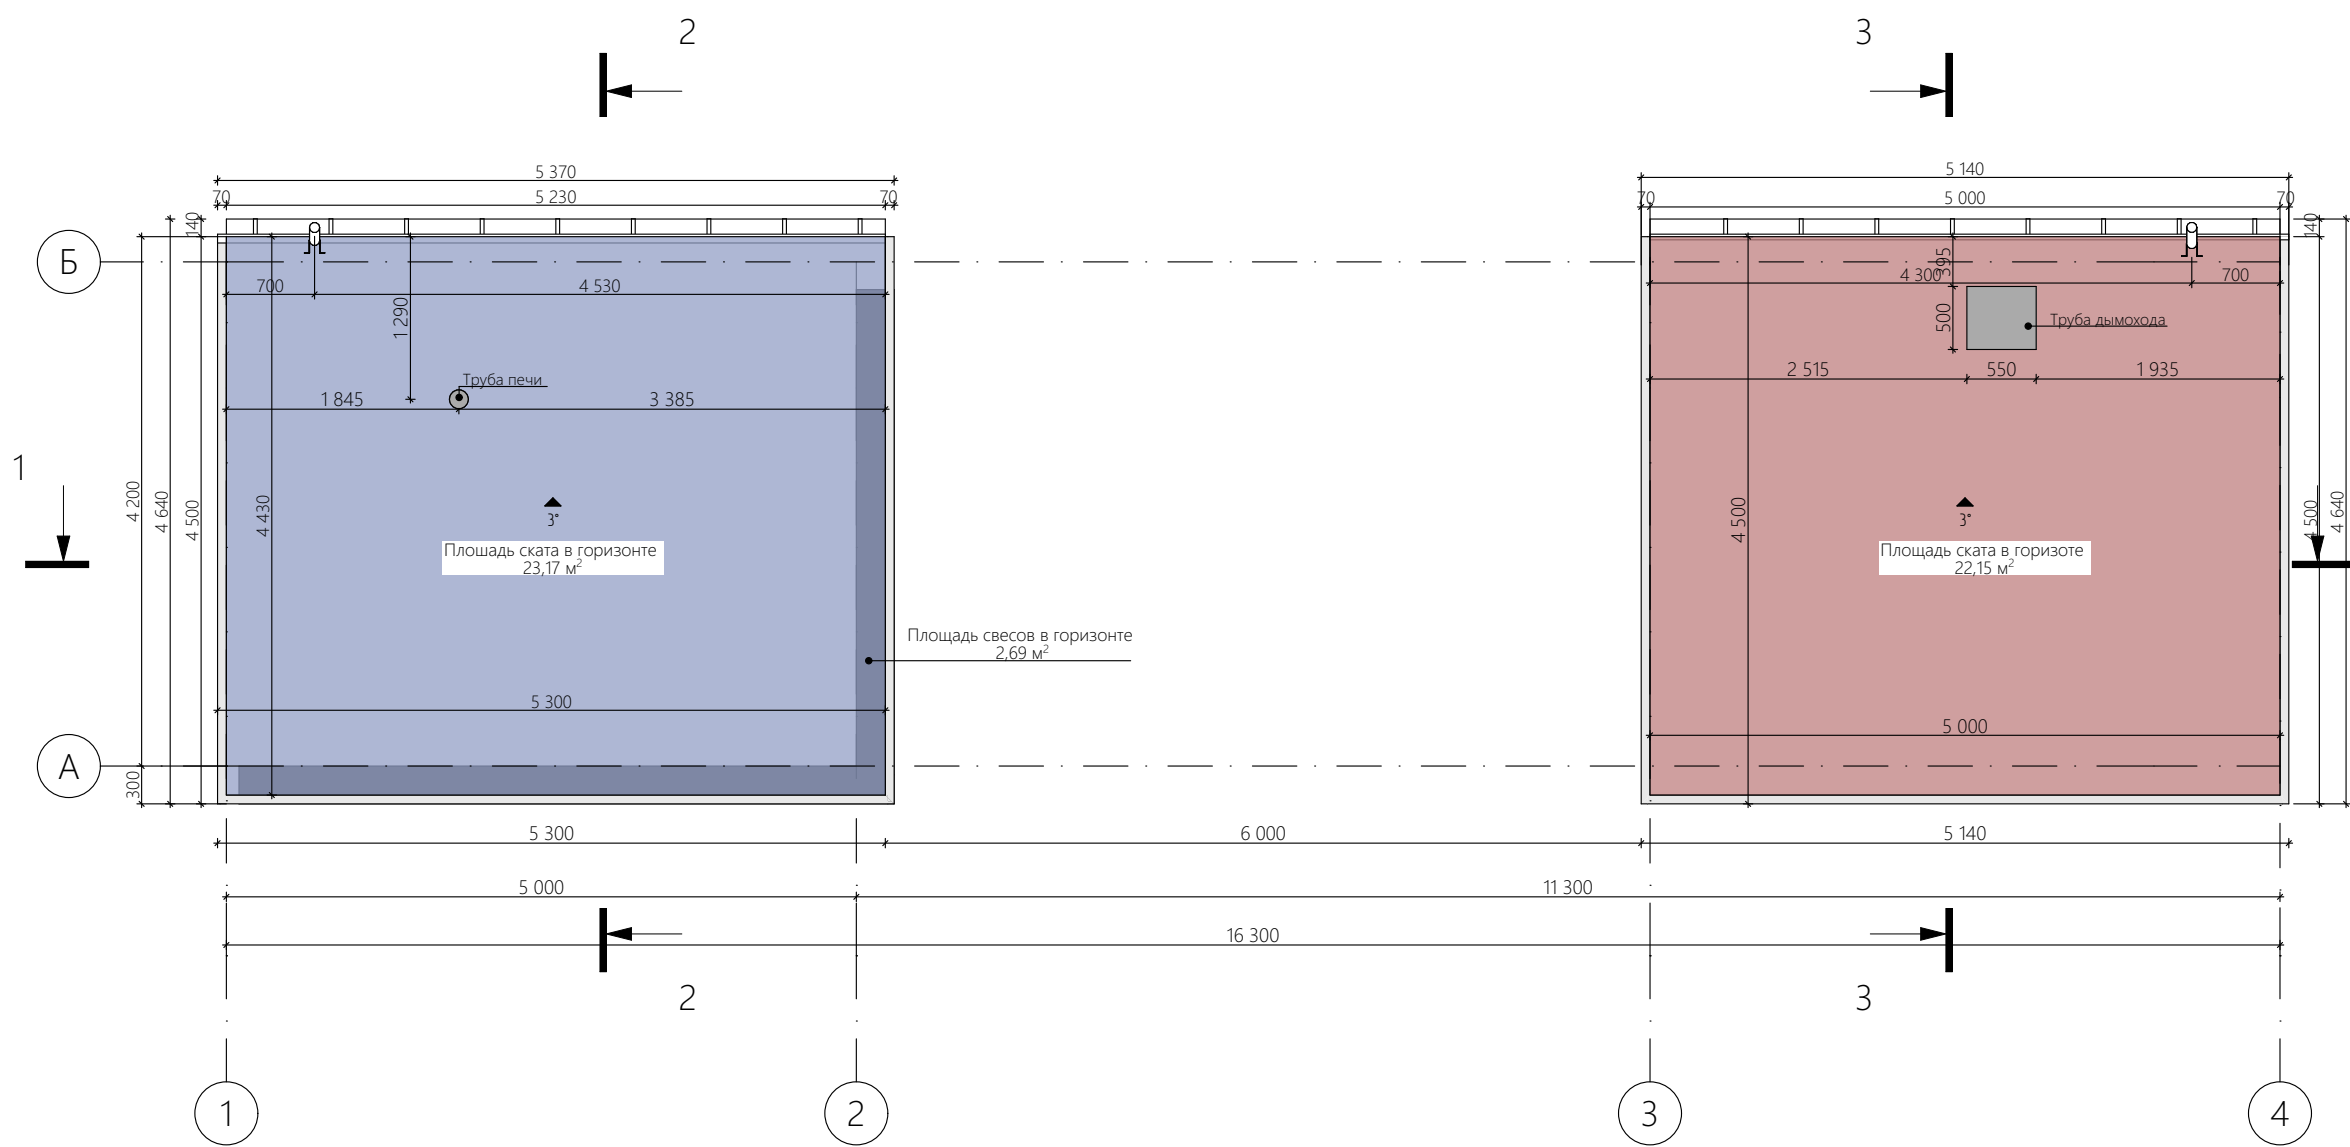


Условные обозначения:

-  - Крыша бани (уклон 3°)
-  - Подшив свесов бани
-  - Крыша беседки (уклон 3°)

Площадь крыши бани ($S, \text{м}^2$) = 23,17м²
Площадь крыши беседки ($S, \text{м}^2$) = 22,15м²

Аксонометрия крыши

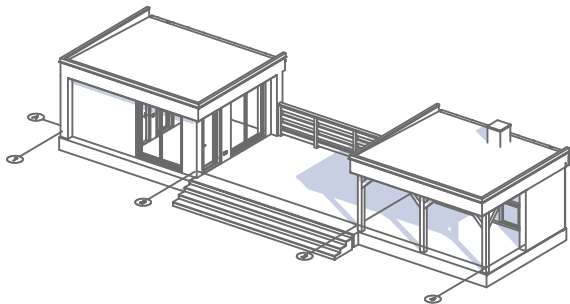

Согласовано

Взам. инв. №

Подп. и дата

Инв. № подл.

Лист	Изм.	№ Докум.	Подп.	Дата

Российская Федерация, Московская область, Можайский городской округ, город Можайск, улица Царская, 27; 50:18:0030306:1291

План крыши

#Название Организации

Лист


15

Ведомость оконных проемов

1:1

Наименование	Размеры проема Ш х В, мм	Кол-во	Вид	Площадь, м2
--------------	--------------------------	--------	-----	-------------

ОК1	600×600	2		0,00
-----	---------	---	---	------

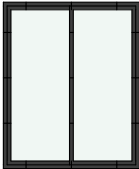ОК2	1 800×2 200	2		3,96
-----	-------------	---	---	------

8,28 м²

Примечание:

- 1. Изготовление окон и дверей определяется заказчиком, допускается изменение открывания окон и дверей;
- 2. При заказе оконных и дверных блоков необходим обмер по месту от изготовителя;
- 3. Оконные и дверные изделия изображены со стороны открывания.

Ведомость дверных проемов


1:1

Наименование	Размеры проема Ш х В, мм	Кол-во	Вид	Площадь, м2
--------------	--------------------------	--------	-----	-------------

Д1

900×2 200

1

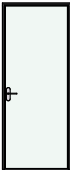


1,98

Д2

800×2 100

1

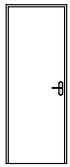


1,68

Д3

800×2 100

1

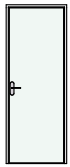

1,68

5,34 м²


Примечание:

1. Изготовление окон и дверей определяется заказчиком, допускается изменение открывания окон и дверей;
2. При заказе оконных и дверных блоков необходим обмер по месту от изготовителя;
3. Оконные и дверные изделия изображены со стороны открывания.

Лист	Изм.	№ Докум.	Подп.	Дата	Ведомость заполнения дверных проемов	#Название Организации	Лист
							17

Разрез 1-1


1:50

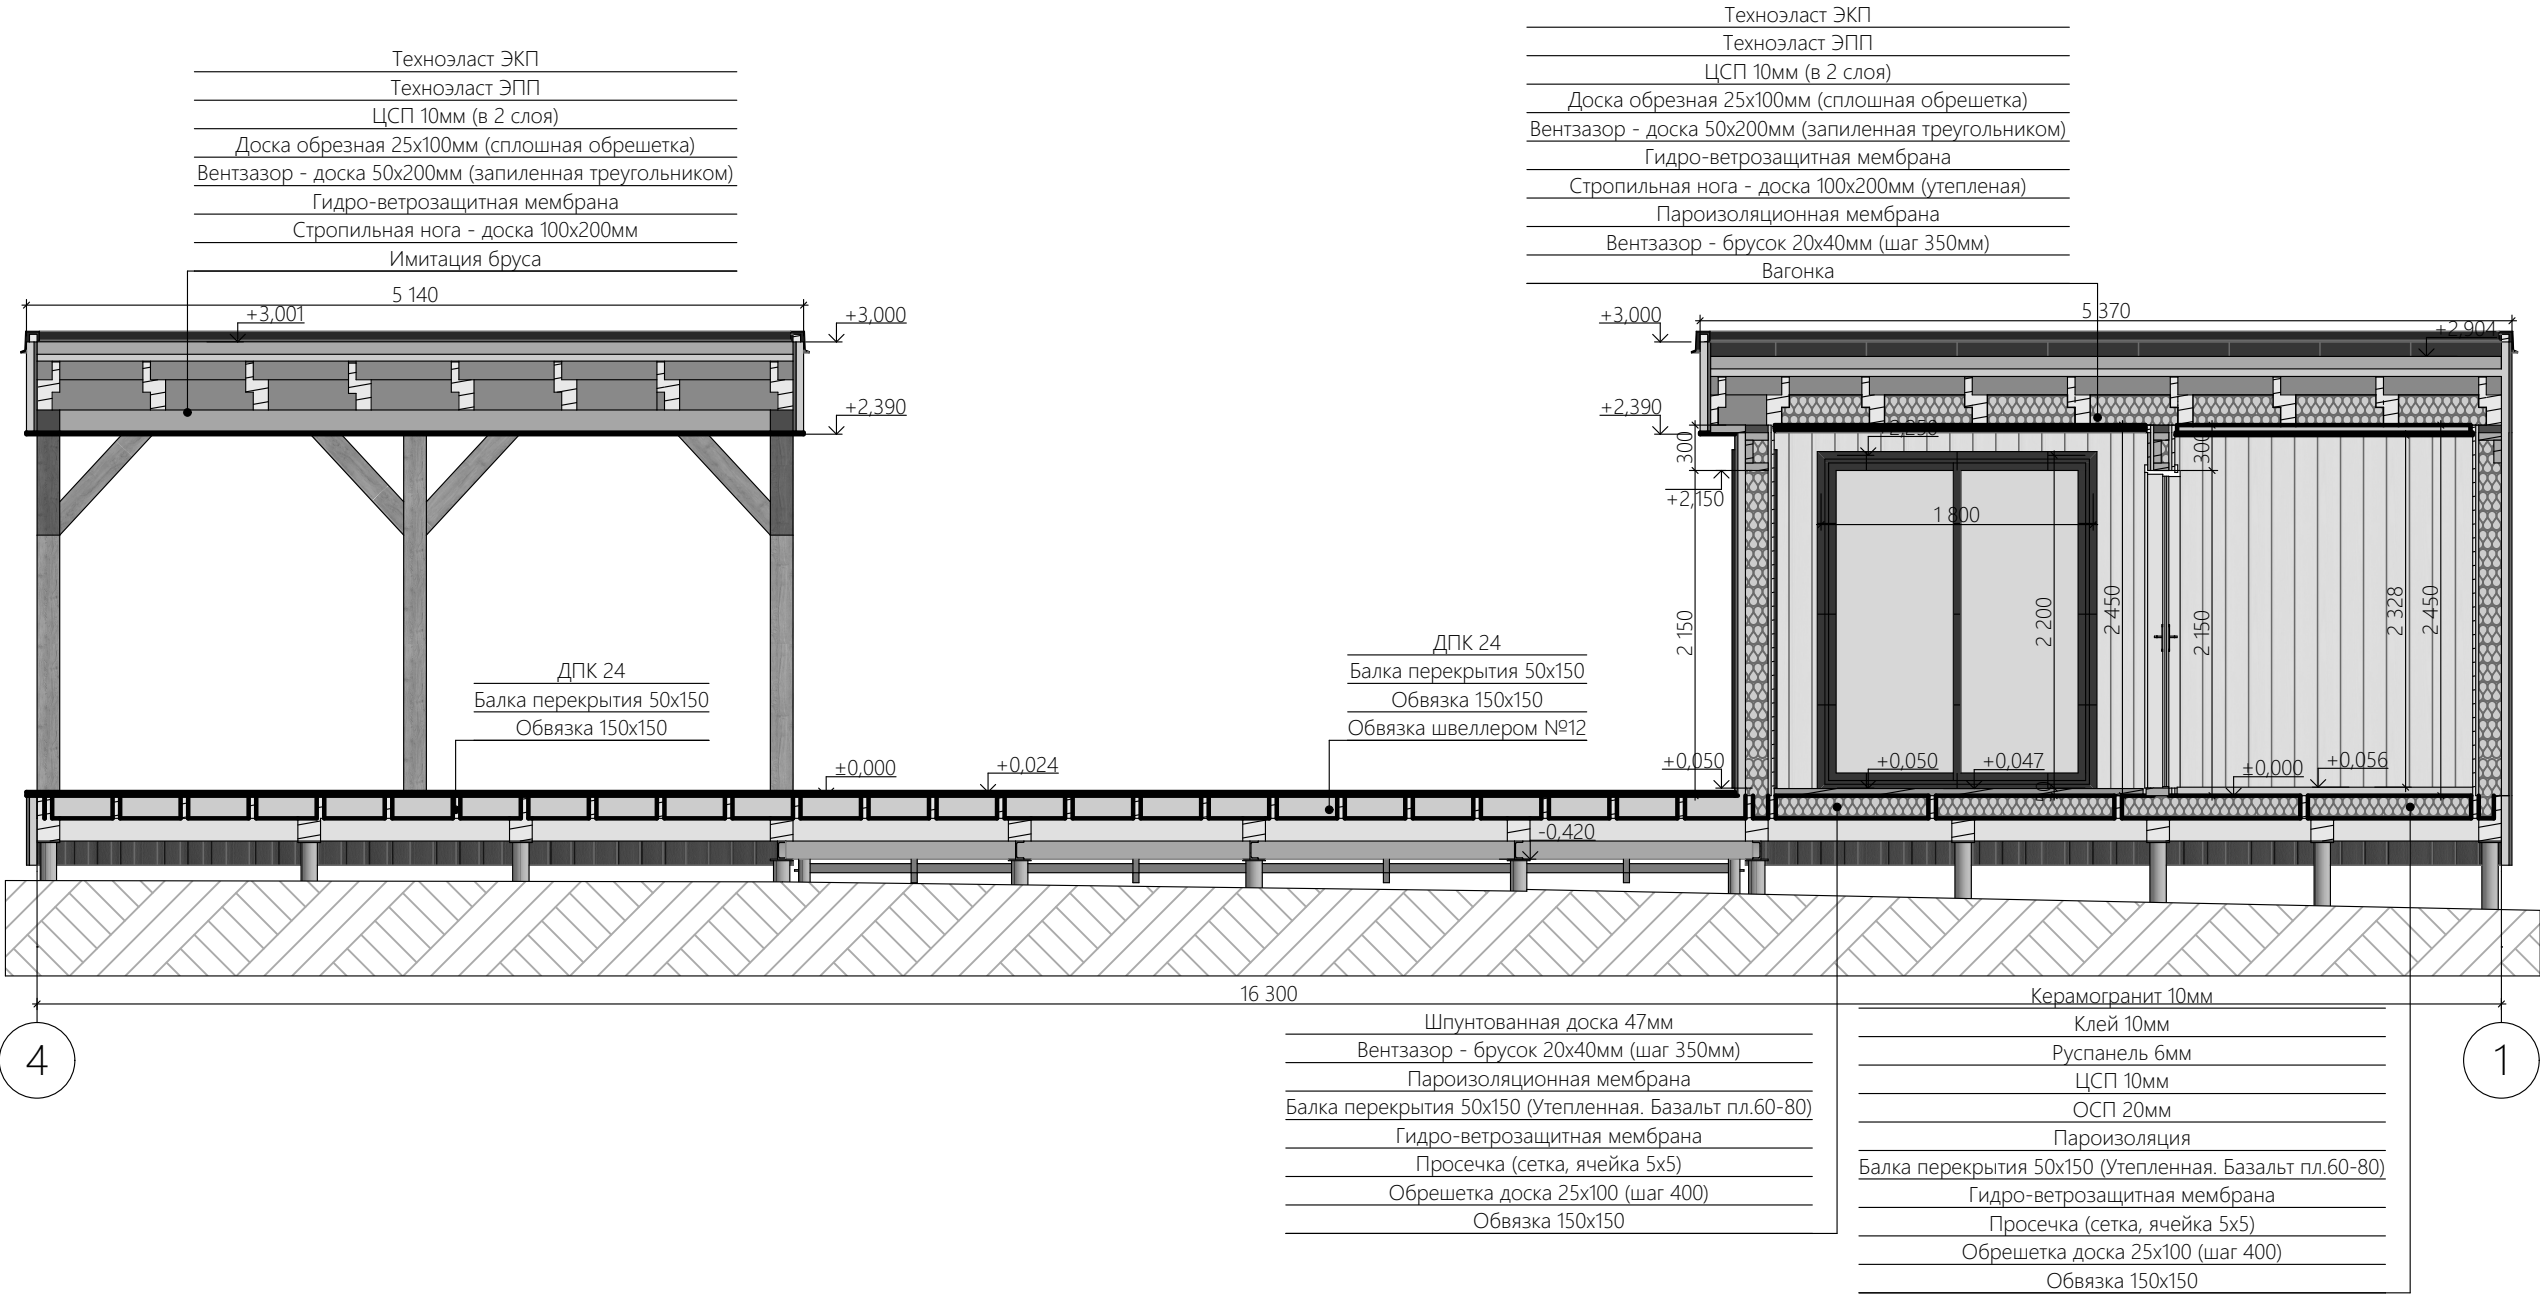

Согласовано				
Изм.	№	Взам.	инв.	№
Изм.	№	Подп.	и	дата
Изм.	№	Подп.	и	дата


Разрез 2-2

1:40

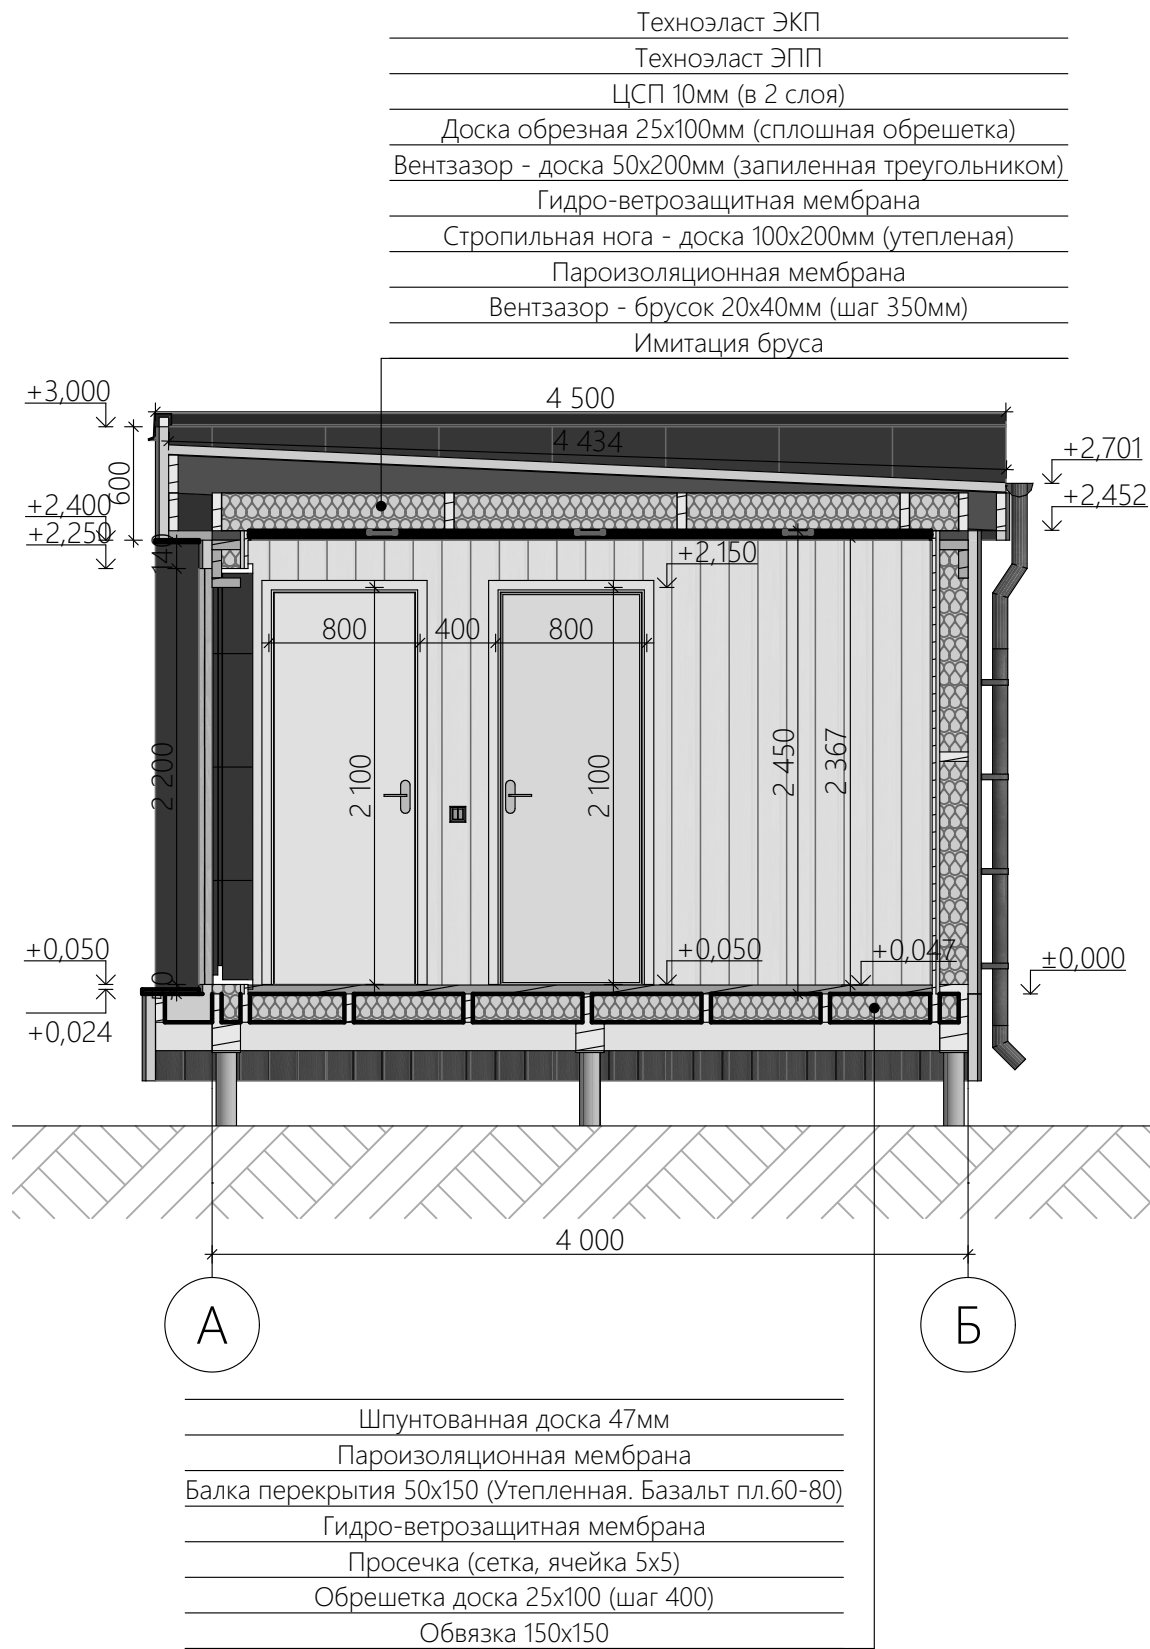

Разрез 3-3

1:40

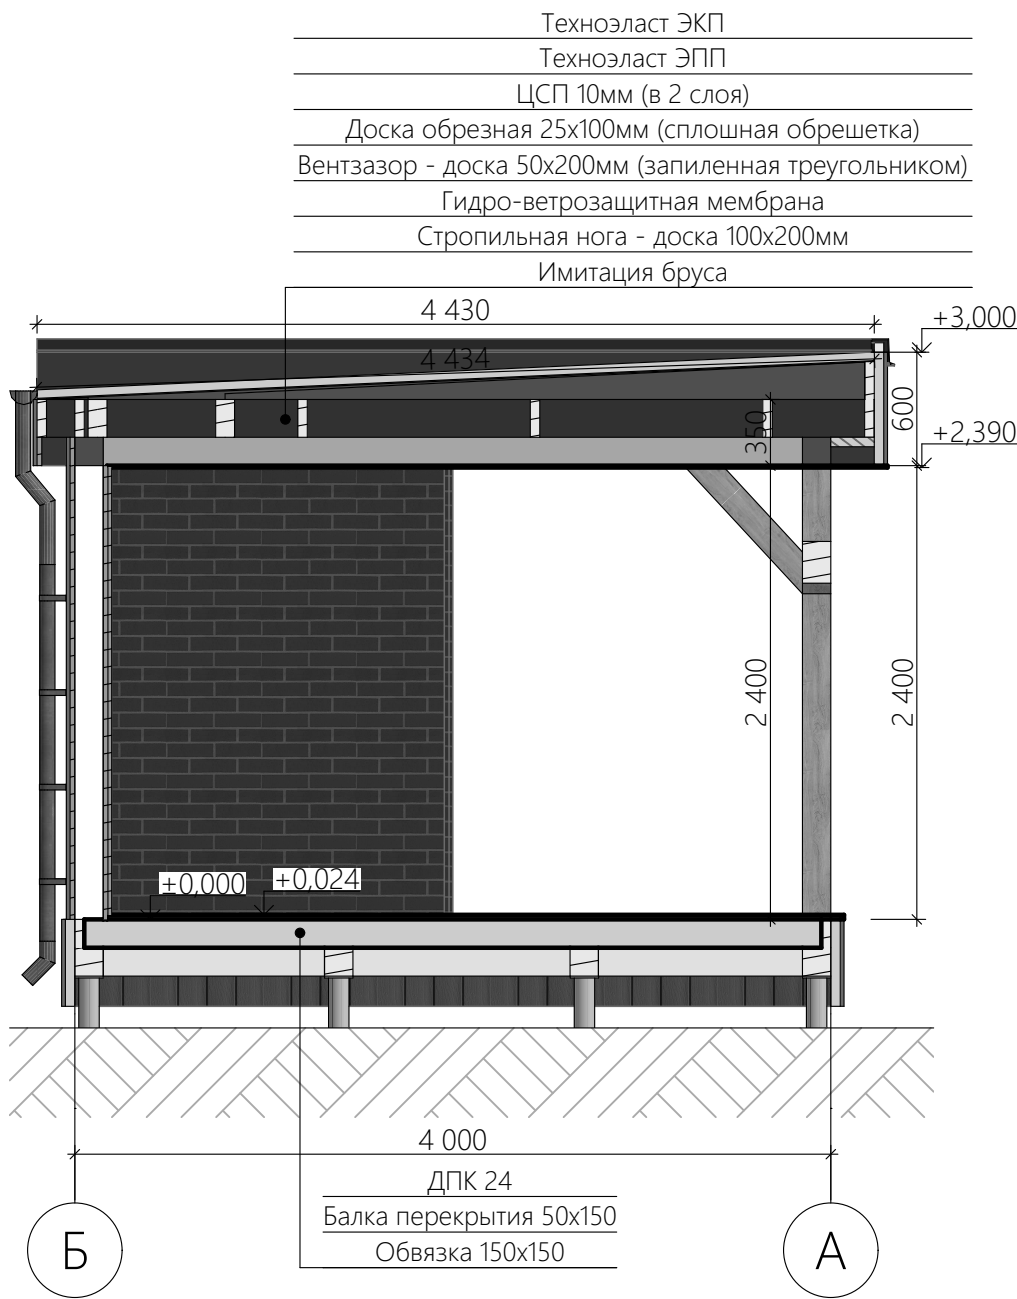

Согласовано

Взам. инв. №

Подп. и дата

Инв. № подл.

Лист	Изм.	№ Докум.	Подп.	Дата

Российская Федерация, Московская область, Можайский городской округ, город Можайск, улица Царская, 27;
50:18:0030306:1291


Разрез 2-2 и разрез 3-3


#Название Организации

Фасад 1-4

1:60

Условные обозначения:

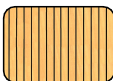-  -Плакен
-  -Террасная доска (ДПК. ВЕЛЬВЕТ. БРАЙТ. ШАЛЕ СЕРЫЙ)
-  -Водосточная система, наличники, оконные рамы (RAL 7024)
-  -Дерево крашенное
-  -Каньон

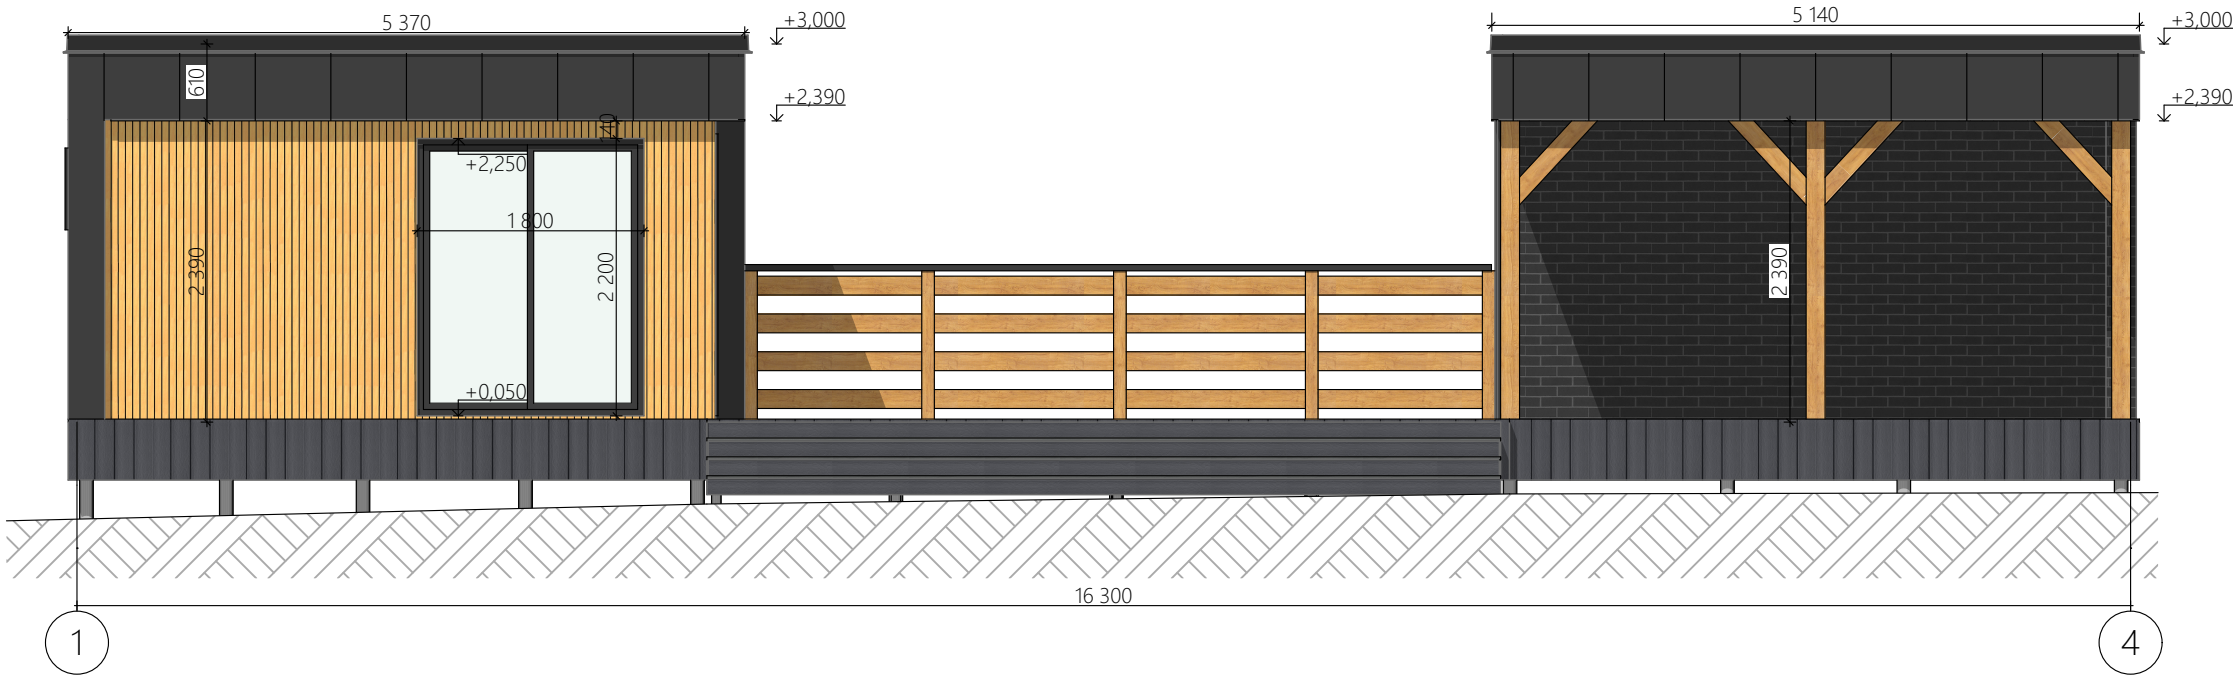

Согласовано				

Инов. № подл.	Подп. и дата	Взам. инв. №	

Лист	Изм.	№ Докум.	Подп.	Дата

Российская Федерация, Московская область, Можайский городской округ, город Можайск, улица Царская, 27; 50:18:0030306:1291


Фасад 1-4

#Название Организации

Согласовано				
Инов. № подл.	Подп. и дата	Взам. инв. №		

Фасад А-Б

1:50

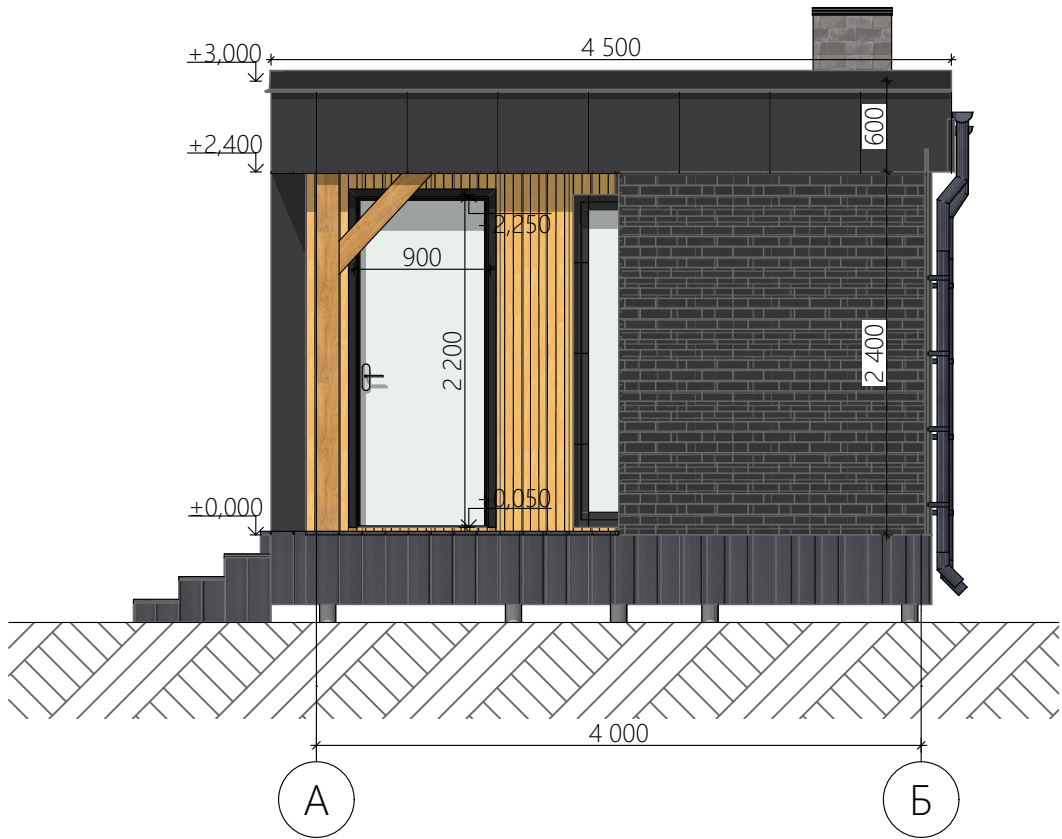


Фасад Б-А

1:50



Условные обозначения:

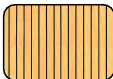-  -Плакен
-  -Террасная доска (ДПК. ВЕЛЬВЕТ. БРАЙТ. ШАЛЕ СЕРЫЙ)
-  -Водосточная система, наличники, оконные рамы (RAL 7024)
-  -Дерево крашенное
-  -Каньон

Лист	Изм.	№ Докум.	Подп.	Дата

Российская Федерация, Московская область, Можайский городской округ, город Можайск, улица Царская, 27; 50:18:0030306:1291

Фасад А-Б, фасад Б-А


#Название Организации

Согласовано

Взам. инв. №

Подп. и дата

Инв. № подл.

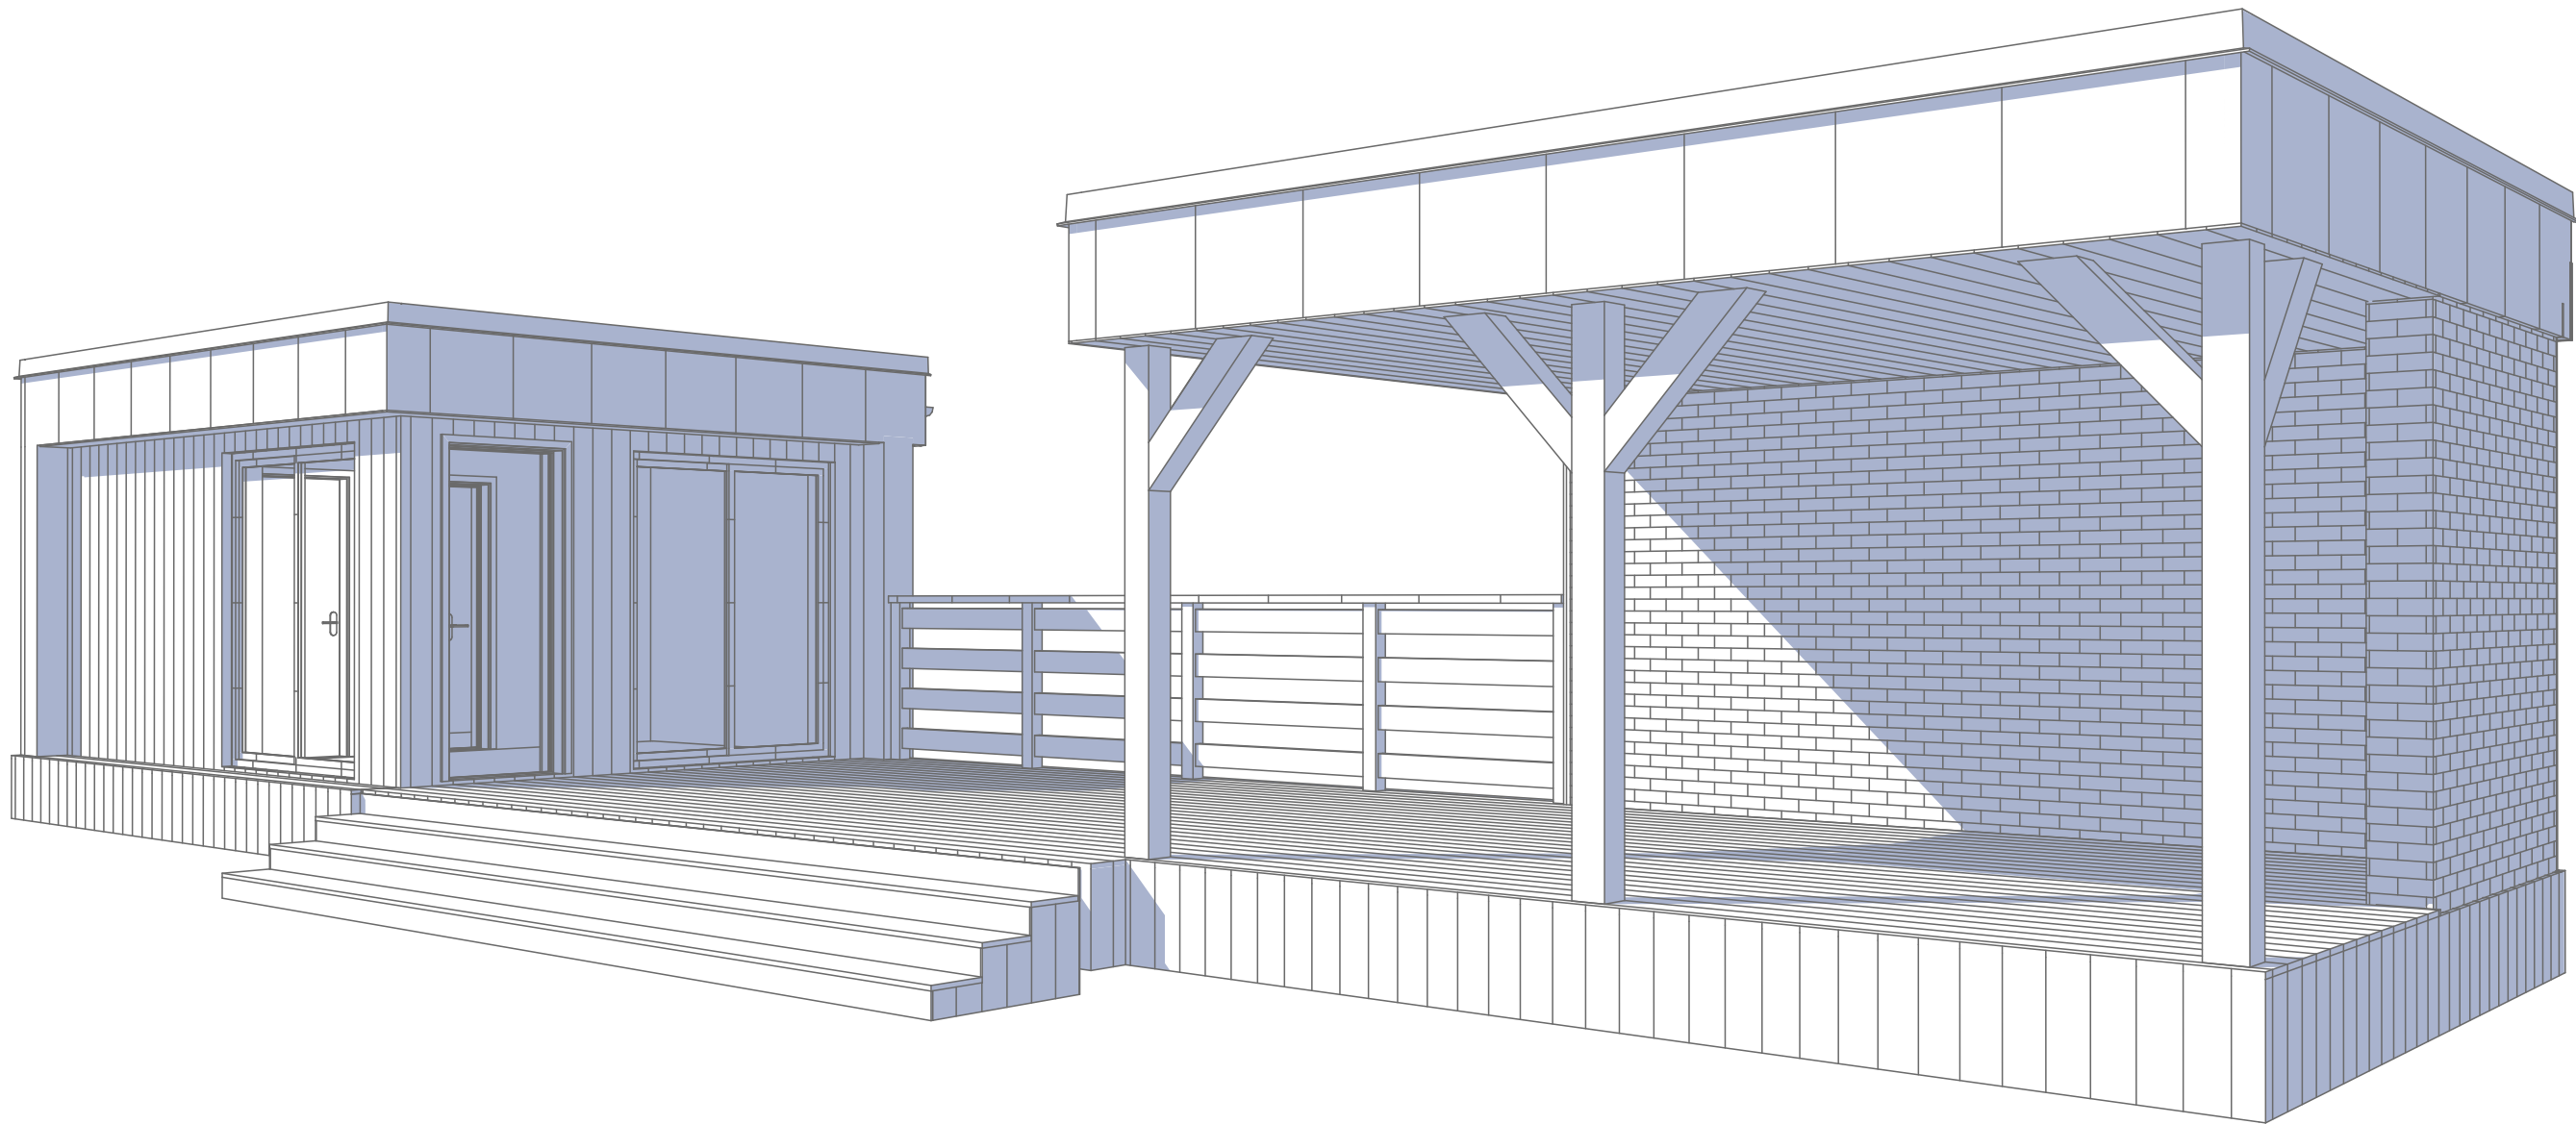

Лист	Изм.	№ Докум.	Подп.	Дата

Российская Федерация, Московская область, Можайский городской округ, город Можайск, улица Царская, 27;
50:18:0030306:1291


Аксометрия №1


#Название Организации

Фасад 4-1

1:60

Условные обозначения:

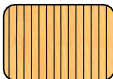-  -Плакен
-  -Террасная доска (ДПК. ВЕЛЬВЕТ. БРАЙТ. ШАЛЕ СЕРЫЙ)
-  -Водосточная система, наличники, оконные рамы (RAL 7024)
-  -Дерево крашенное
-  -Каньон

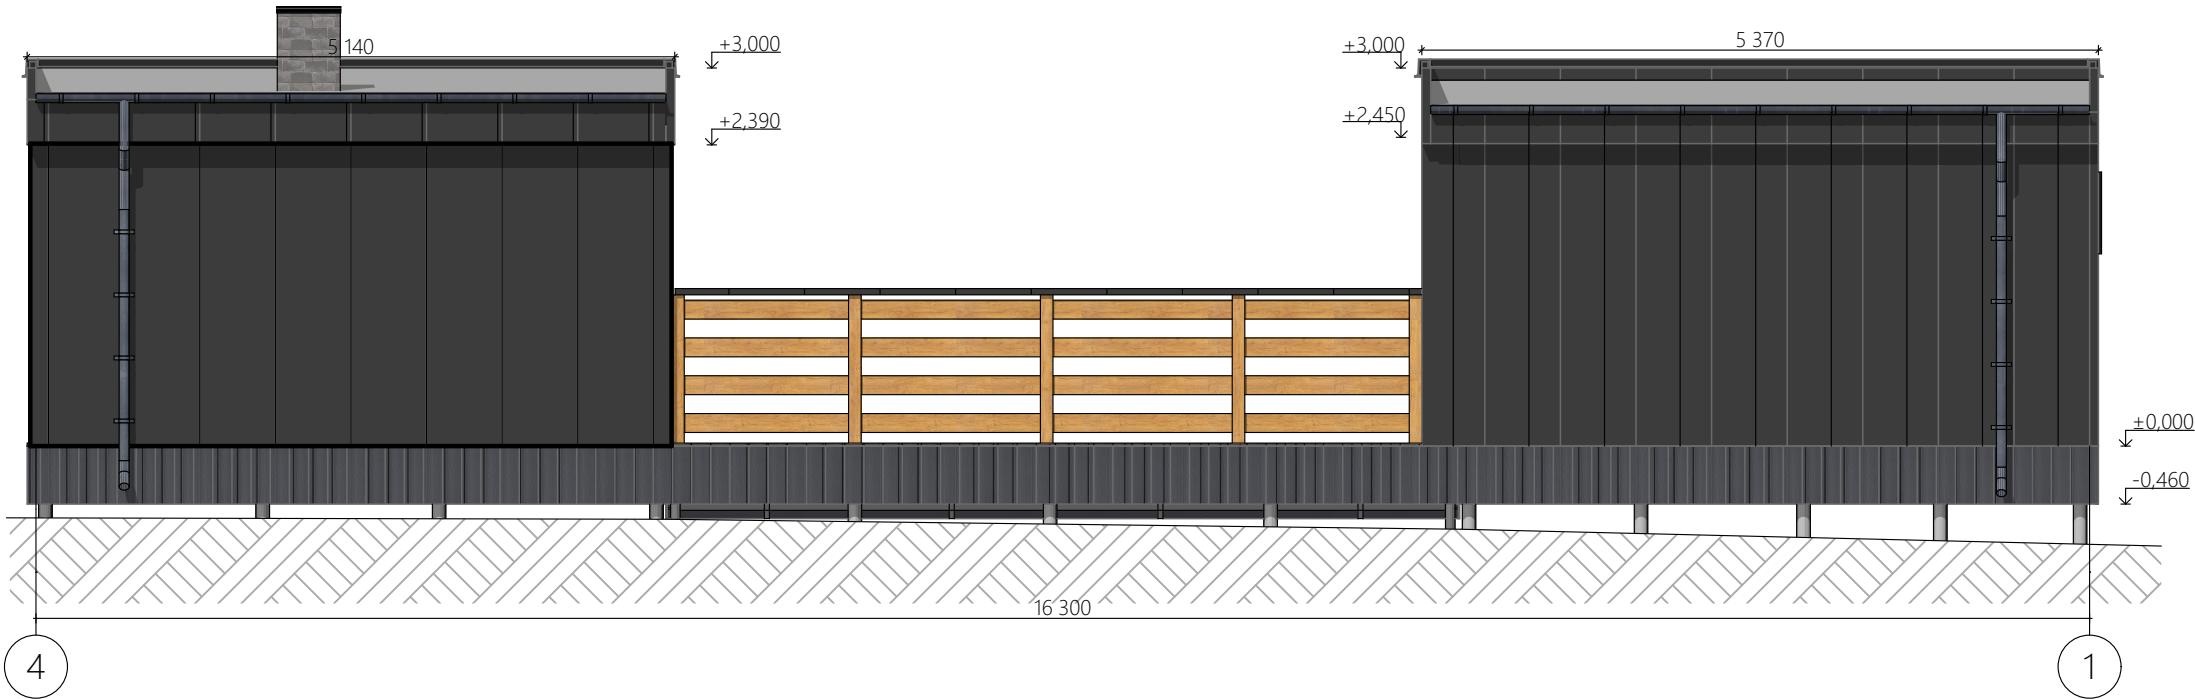

Согласовано				

Инов. № подл.	Подп. и дата	Взам. инв. №	

Лист	Изм.	№ Докум.	Подп.	Дата


Российская Федерация, Московская область, Можайский городской округ, город Можайск, улица Царская, 27; 50:18:0030306:1291

Фасад 4-1

#Название Организации

Согласовано			

Инов. № подл.	Подп. и дата	Взам. инв. №	

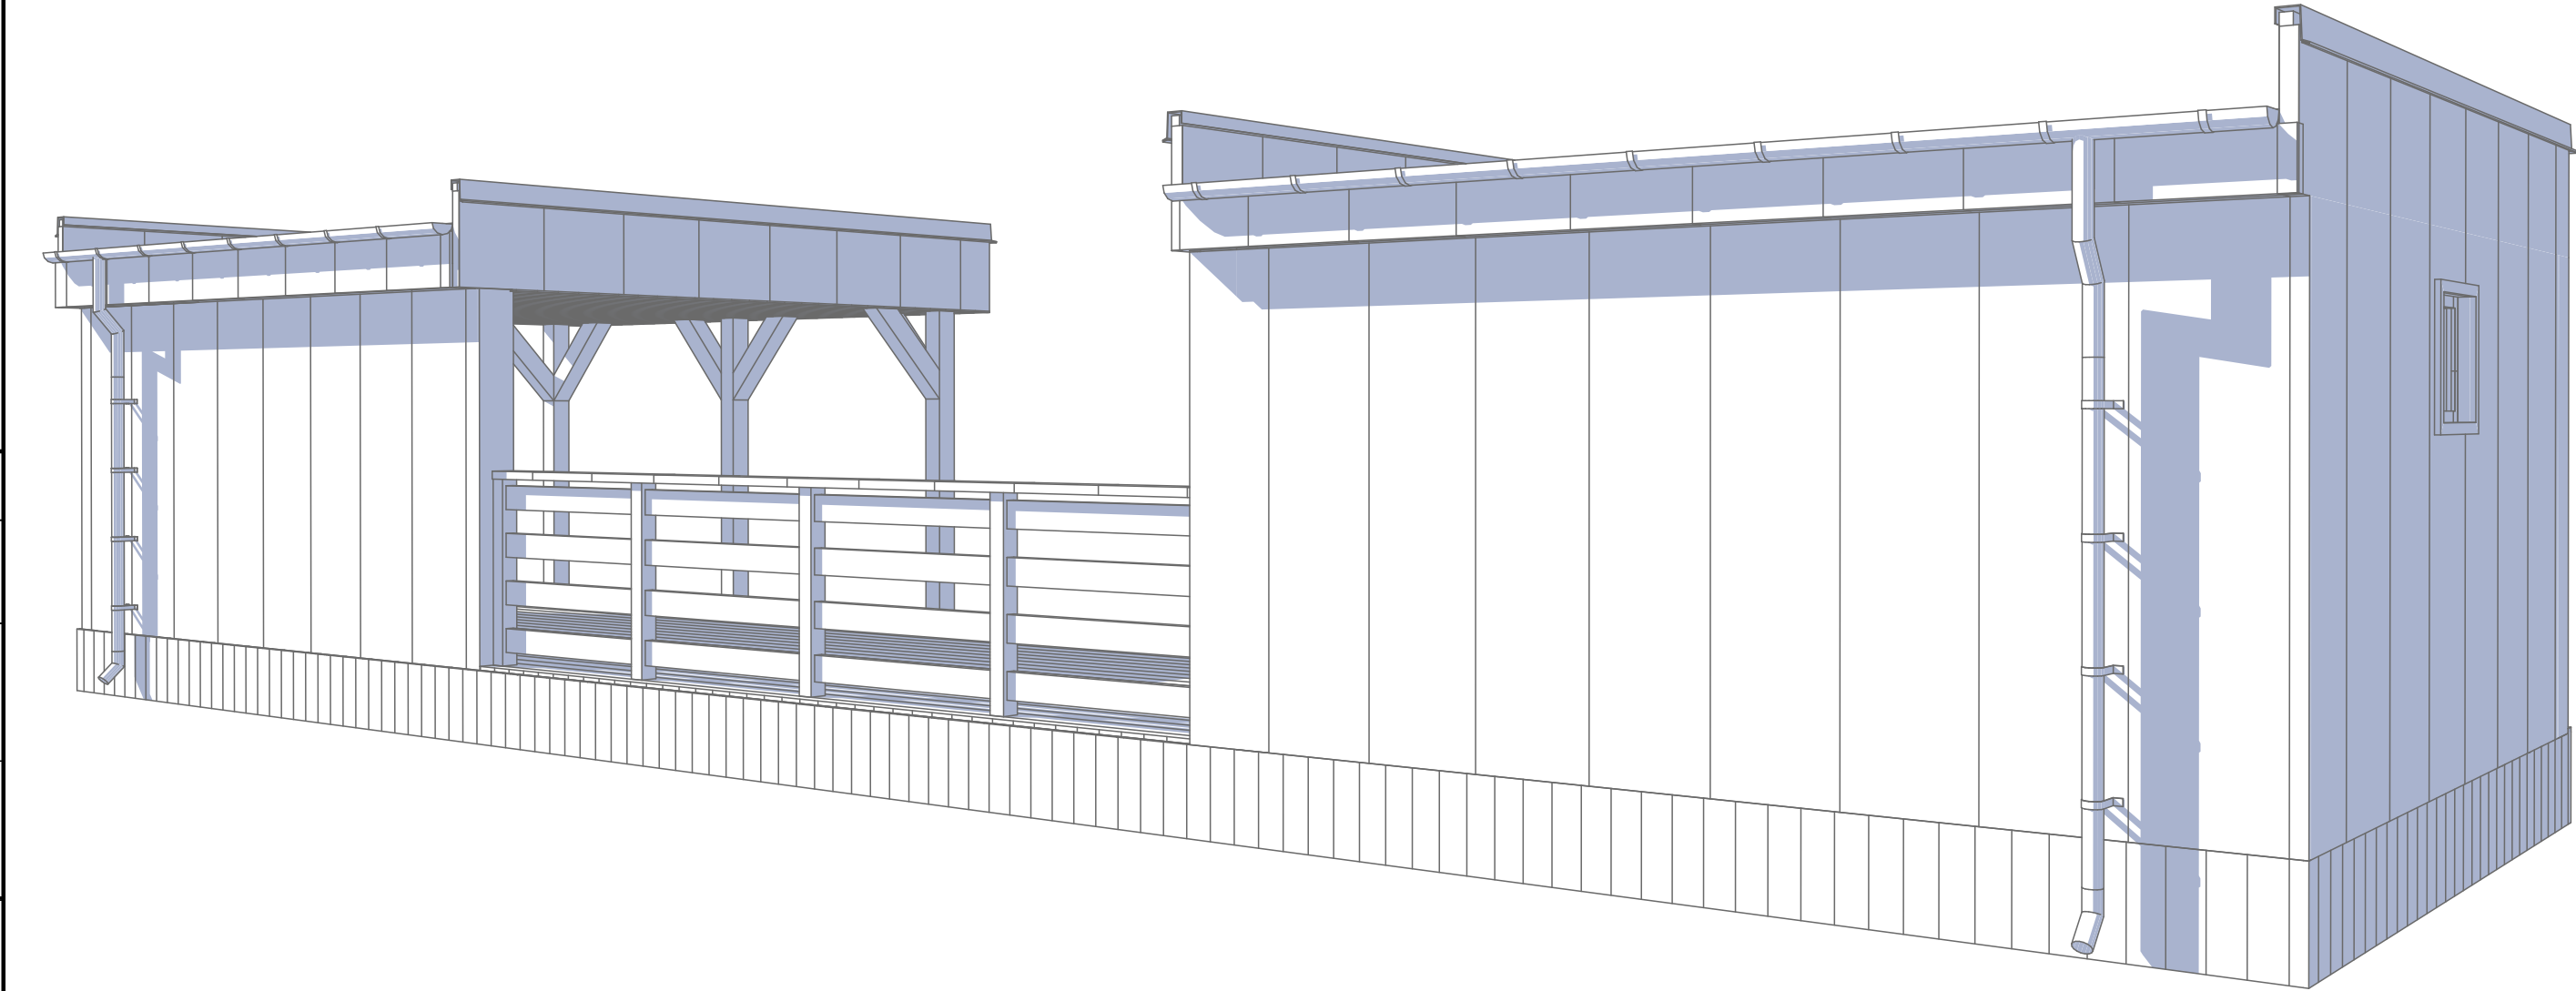

Лист	Изм.	№ Докум.	Подп.	Дата

Российская Федерация, Московская область, Можайский городской округ, город Можайск, улица Царская, 27;
50:18:0030306:1291

Аксометрия №2

#Название Организации

Согласовано

Взам. инв. №

Подп. и дата

Инв. № подл.



Лист	Изм.	№ Докум.	Подп.	Дата

Российская Федерация, Московская область, Можайский городской округ, город Можайск, улица Царская, 27;
50:18:0030306:1291

Визуализация

#Название Организации

Согласовано

Взам. инв. №

Подп. и дата

Инв. № подл.



Лист	Изм.	№ Докум.	Подп.	Дата

Российская Федерация, Московская область, Можайский городской округ, город Можайск, улица Царская, 27;
50:18:0030306:1291

Визуализация

#Название Организации

Согласовано					
Инва. № подл.	Подп. и дата		Взам. инв. №		



Лист	Изм.	№ Докум.	Подп.	Дата

Российская Федерация, Московская область, Можайский городской округ, город Можайск, улица Царская, 27;
50:18:0030306:1291

Визуализация

#Название Организации

Согласовано

Взам. инв. №

Подп. и дата

Инв. № подл.

Лист	Изм.	№ Докум.	Подп.	Дата

Российская Федерация, Московская область, Можайский городской округ, город Можайск, улица Царская, 27;
50:18:0030306:1291

Визуализация

#Название Организации



Согласовано					
Инва. № подл.	Подп. и дата		Взам. инв. №		



Лист	Изм.	№ Докум.	Подп.	Дата

Российская Федерация, Московская область, Можайский городской округ, город Можайск, улица Царская, 27;
50:18:0030306:1291

Визуализация

#Название Организации

Согласовано

Взам. инв. №

Подп. и дата

Инв. № подл.



Лист	Изм.	№ Докум.	Подп.	Дата

Российская Федерация, Московская область, Можайский городской округ, город Можайск, улица Царская, 27;
50:18:0030306:1291

Визуализация

#Название Организации

Согласовано

Взам. инв. №

Подп. и дата

Инв. № подл.



Лист	Изм.	№ Докум.	Подп.	Дата

Российская Федерация, Московская область, Можайский городской округ, город Можайск, улица Царская, 27;
50:18:0030306:1291

Визуализация

#Название Организации

Согласовано

Взам. инв. №

Подп. и дата

Инв. № подл.

Лист	Изм.	№ Докум.	Подп.	Дата

Российская Федерация, Московская область, Можайский городской округ, город Можайск, улица Царская, 27;
50:18:0030306:1291

Визуализация

#Название Организации

