

ARCHITECTURE/
CONSTRUCTION



Название:
-
Разработал:
-
Принял:
-
г. Москва



Согласовано			
И/в. № подл.	Подп. и дата	Взам. инв. №	

Лист	Наименование	Примечание
1	Титульный	
2	Ведомость чертежей	
3	Пояснительная записка	
4	СПОЗУ	
5	Маркировочный план	
6	Размерный план	
7	План расстановки мебели и оборудования	
8	3д-разрез	
9	План покрытия пола	
10	Пироги пола	
11	План покрытия стен	
12	Пироги стен	
13	План размещения розеток	
14	План размещения светильников и выключателей	
15	План крыши	
16	Ведомость оконных проемов	
17	Ведомость дверных проемов	
18	Разрез 1-1	
19	Разрез 2-2	
20	Фасад 1-3	
21	Фасад А-Б	
22	Аксонометрия №1	
23	Фасад Б-А	
24	Фасад 3-1	
25	Аксонометрия №2	
26	Визуализация	
27	Визуализация	
28	Визуализация	
29	Визуализация	
30	Визуализация	

В основу архитектурно-планировочных решений положены требования технологических заданий и требования норм и правил строительного проектирования, действующих на территории РФ.

Основные параметры и требования разработаны на основании пожеланий и требований заказчика.

Архитектурные решения приняты в соответствии со следующими нормативными документами:

- Градостроительный кодекс российской федерации.
- Земельного Кодекса Российской Федерации.
- Федеральный закон от 22.07.2008 N 123 - ФЗ (ред. от 29.07.2017)"Технический регламент о требованиях пожарной безопасности.
- Федеральный закон № 384 - ФЗ «Технический регламент о безопасности зданий и сооружений».
- ГОСТ Р 21.1101-2013.«Основные требования к проектной и рабочей документации».
- Постановление правительства РФ от 16.02.2008 № 87 «Положение о составе разделов проектной документации и требованиях к их содержанию».
- СП 42.13330.2011 «Градостроительство. Планировка и застройка городских и сельских поселений».
- СП 131.13330.2018 «СНиП 23-01-99* Строительная климатология».
- СП 20.13330.2016 «СНиП 2.01.07-85* Нагрузки и воздействия».
- СП 22.13330.2016 «СНиП 2.02.01-83* Основания зданий и сооружений».
- СП 70.13330.2012 (с изменениями №1) «СНиП 3.03.01-87 Несущие и ограждающие конструкции».
- СП 64.13330.2017 «СНиП II-25-80 Деревянные конструкции».
- СП 17.13330.2017 «СНиП II-26-76 Кровли».
- СП 29.13330.2011 «СНиП 2.03.13-88 Полы».
- СП 28.13330.2017 «СНиП 2.03.11-85 Защита строительных конструкций от коррозии».
- СП 50.13330.2012 «СНиП 23-02-2003 Тепловая защита зданий».

Лист	Изм.	№ Докум.	Подп.	Дата

МО, Мытищинский район, Новые Вешки, Зеленый бульвар 78		Ведомость чертежей		#Название Организации		Лист
						2

Согласовано				
И-нв. № подл.	Подп. и дата	Взам. инв. №		

1. Общие данные:

1.1. Архитектурный проект разработан на основании требований и пожеланий заказчика.

Тип строения	Баня
Относительная отм. ±0.000	ур. верха лаг перекрытия
Общая площадь застройки, м2	51,3
Габаритные размеры каркаса здания	9х5,7м
Этажность	1 этаж
Конструктивная схема	Деревянный каркас

2. Конструктивные решения:

2.1. Рабочие чертежи разработаны на основании задания на проектирование

Полезная нагрузка на перекрытие	150 кгс/м2	-
Нормативная глубина промерзания	1,2м	СП 22.13330.2016 СП 131.13330.2020
Нормативное ветровое давление	I район (23кгс/м2)	СП 22.13330.2016
Нормативный вес снегового покрова	III район (150кгс/м2)	СП 22.13330.2016
Температура наиболее холодной пятидневки	-29°С	СП 131.13330.2020

2.2. Конструктивное строение представляет собой сооружение:

- на свайном фундаменте
- несущими стенами из деревянного каркаса
- вальмовой кровлей по деревянным стропилам

2.3. Необходимо осуществлять технический надзор за производством строительных работ. Данные по проведённым работам необходимо систематически вносить в журнал работ.

По каждому из этапов работ необходимо осуществлять входной контроль материалов и вести приёмку.

Фундамент	сваи винтовые d=108мм
Несущие конструкции	деревянный каркас (140х45мм)
Стропильная система	строганая доска (190х45мм)
Тип крыши	вальмовая
Покрытие кровли	гибкая черепица

2.4. Все деревянные конструкции обработать огне-биозащитными септиками в соответствии со СП 28.13330.2017 "Защита строительных конструкций от коррозии".

2.5. Кровельные работы выполнять в соответствии с требованиями фирмы производителя.

2.6. Все работы вести в строгом соответствии с требованиями СНиП 12.03.2001 "Безопасность труда в строительстве".

2.7. При выполнении всех работ строго соблюдать меры противопожарной безопасности.



2.8. Возможна замена материалов аналогами.

*Решения, принятые в проекте и отображенные в чертежах, соответствуют требованиям экологических, санитарно - гигиенических, противопожарных и других норм, действующих на территории Российской Федерации, и обеспечивают безопасную для жизни и здоровья людей эксплуатацию объекта при соблюдении предусмотренных рабочих чертежей и мероприятий.

- Граница участка
- Граница застройки участка
- 1 - Существующий индивидуальный жилой дом
- 2 - Банный комплекс (проектируемая постройка)

Технико-экономические показатели

Наименование	Площадь, м²
Площадь участка (по кадастровой документации)	1500,0
Общая площадь застройки (баня+ИЖД)	299,64
Площадь участка (по топографической съемке)	1584,66
Площадь застройки (баня)	51,3
Площадь застройки (ИЖД)	248,34

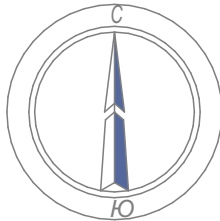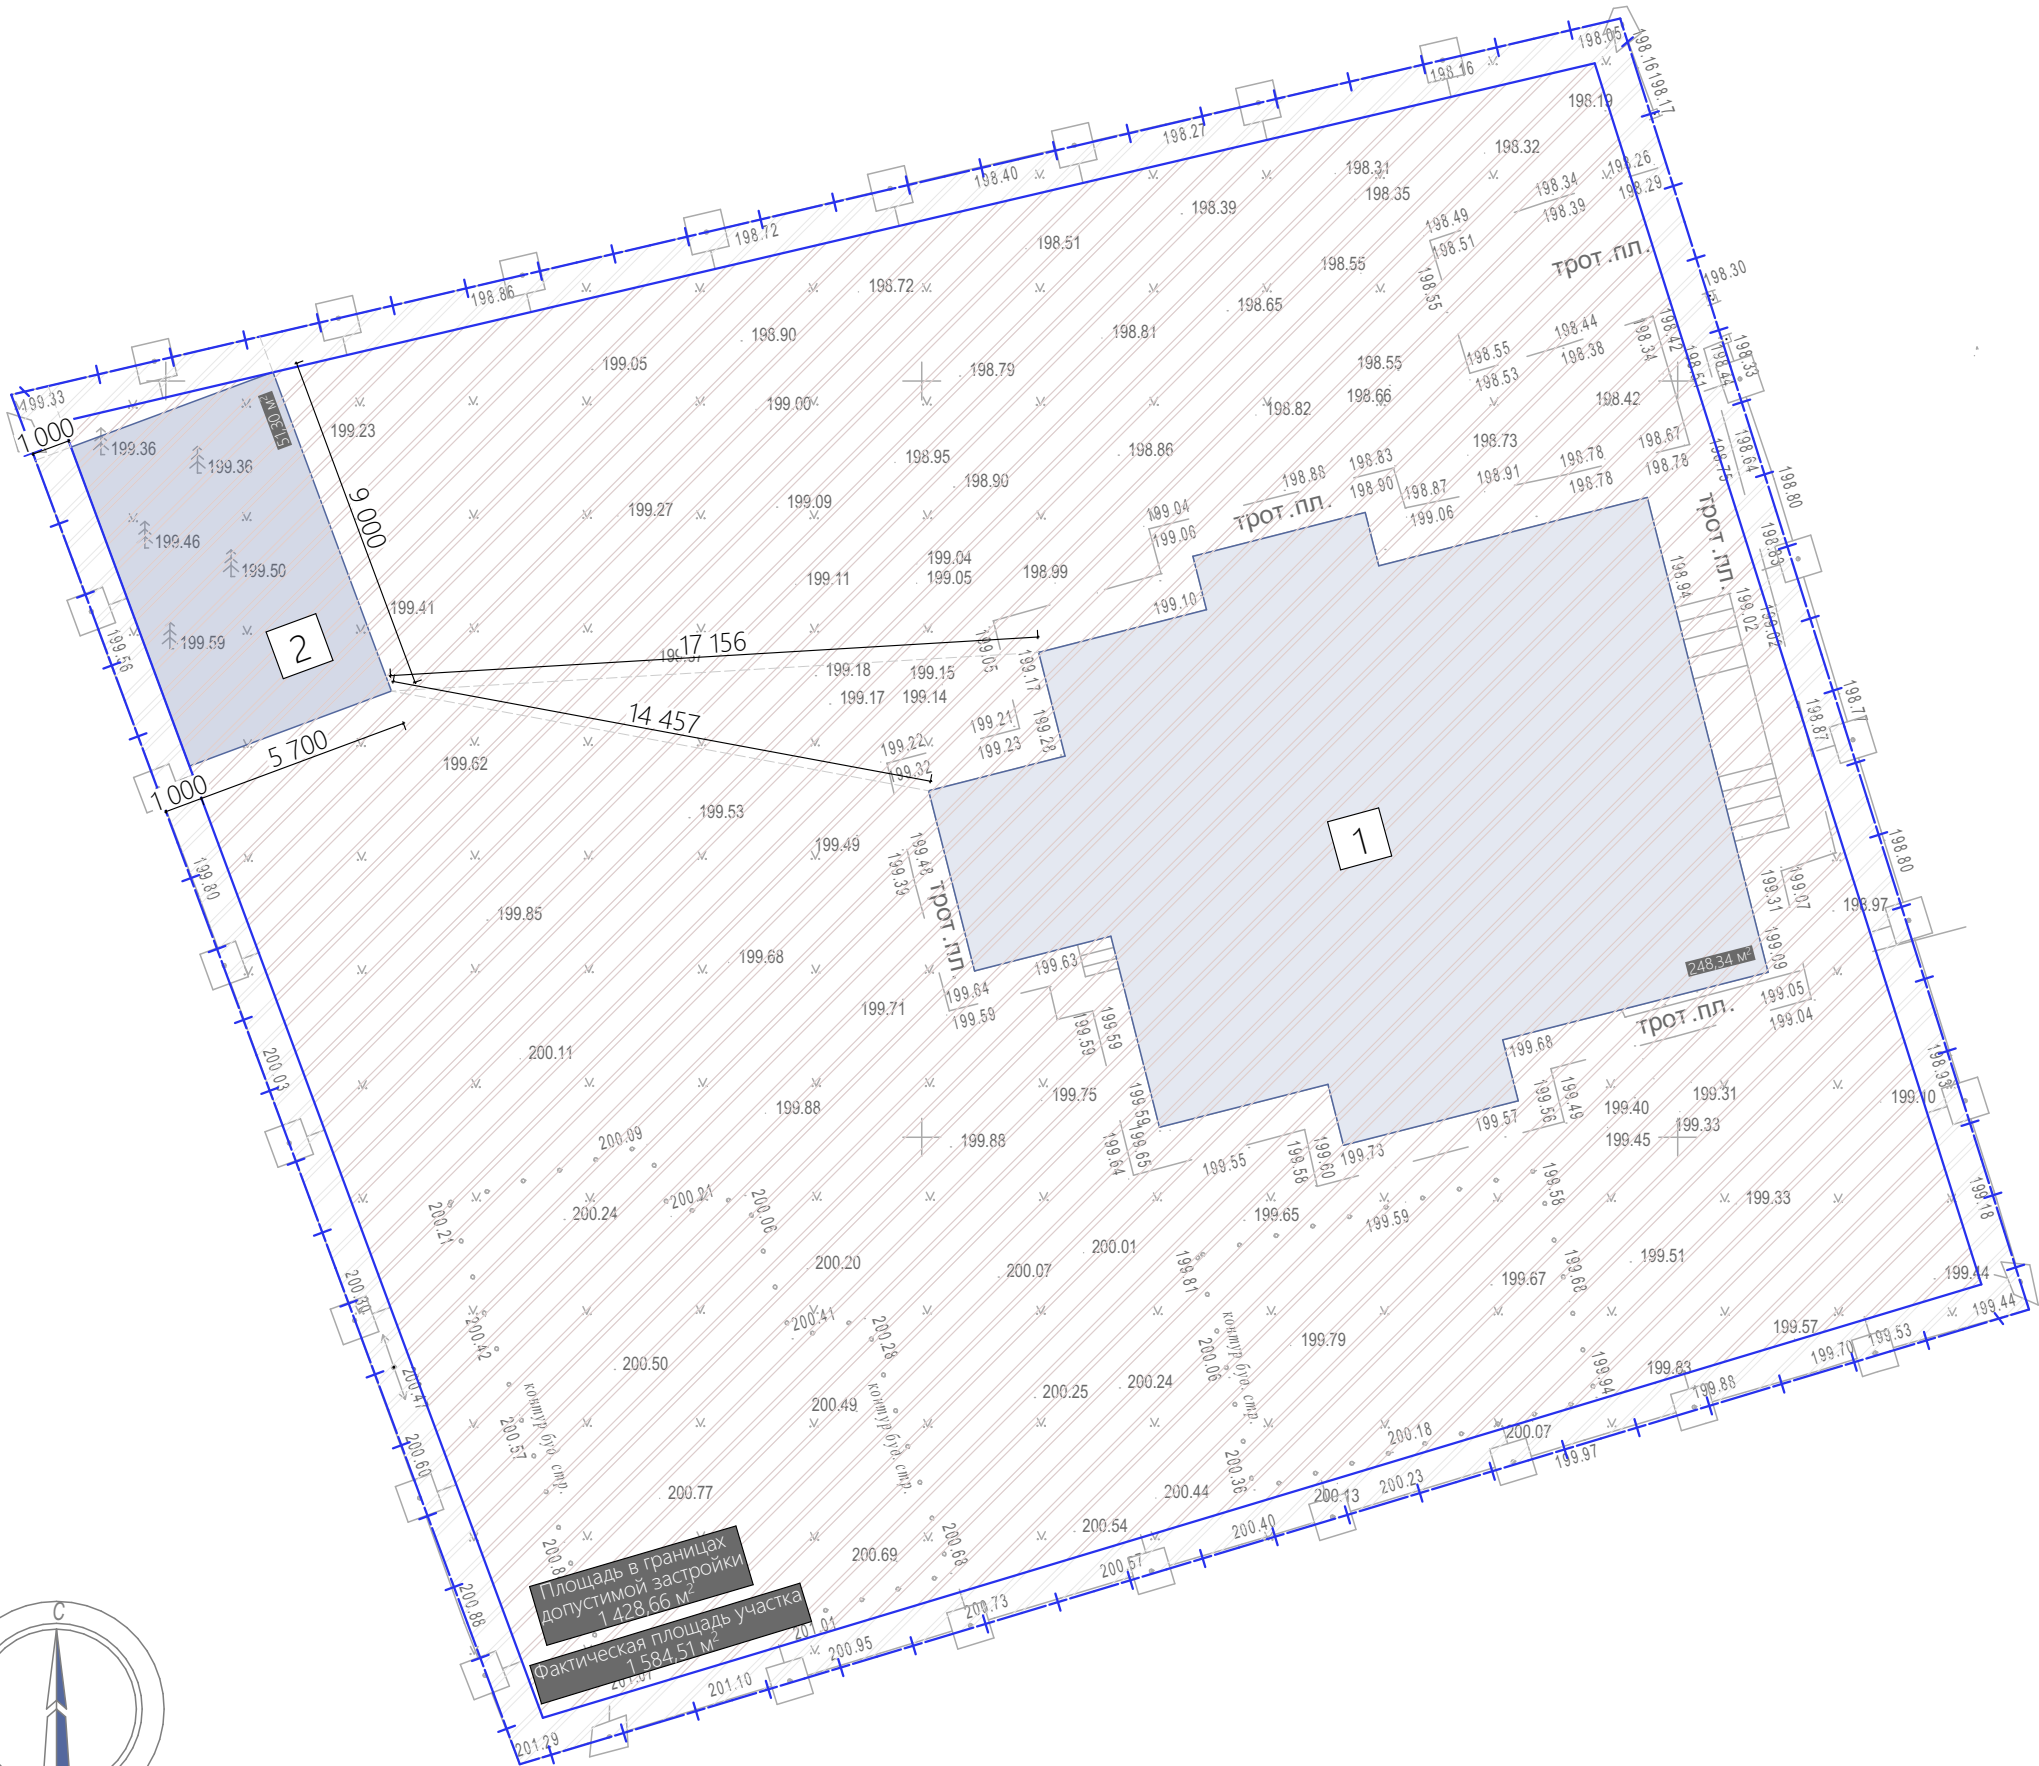

Площадь в границах
допустимой застройки
1 428,66 м²
Фактическая площадь участка
1 584,51 м²


Согласовано				
И-нв. № подл.	Подп. и дата	Взам. инв. №		

Лист	Изм.	№ Докум.	Подп.	Дата

Согласовано				
И-нв. № подл.	Подп. и дата	Взам. инв. №		

Маркировочный план

1:50

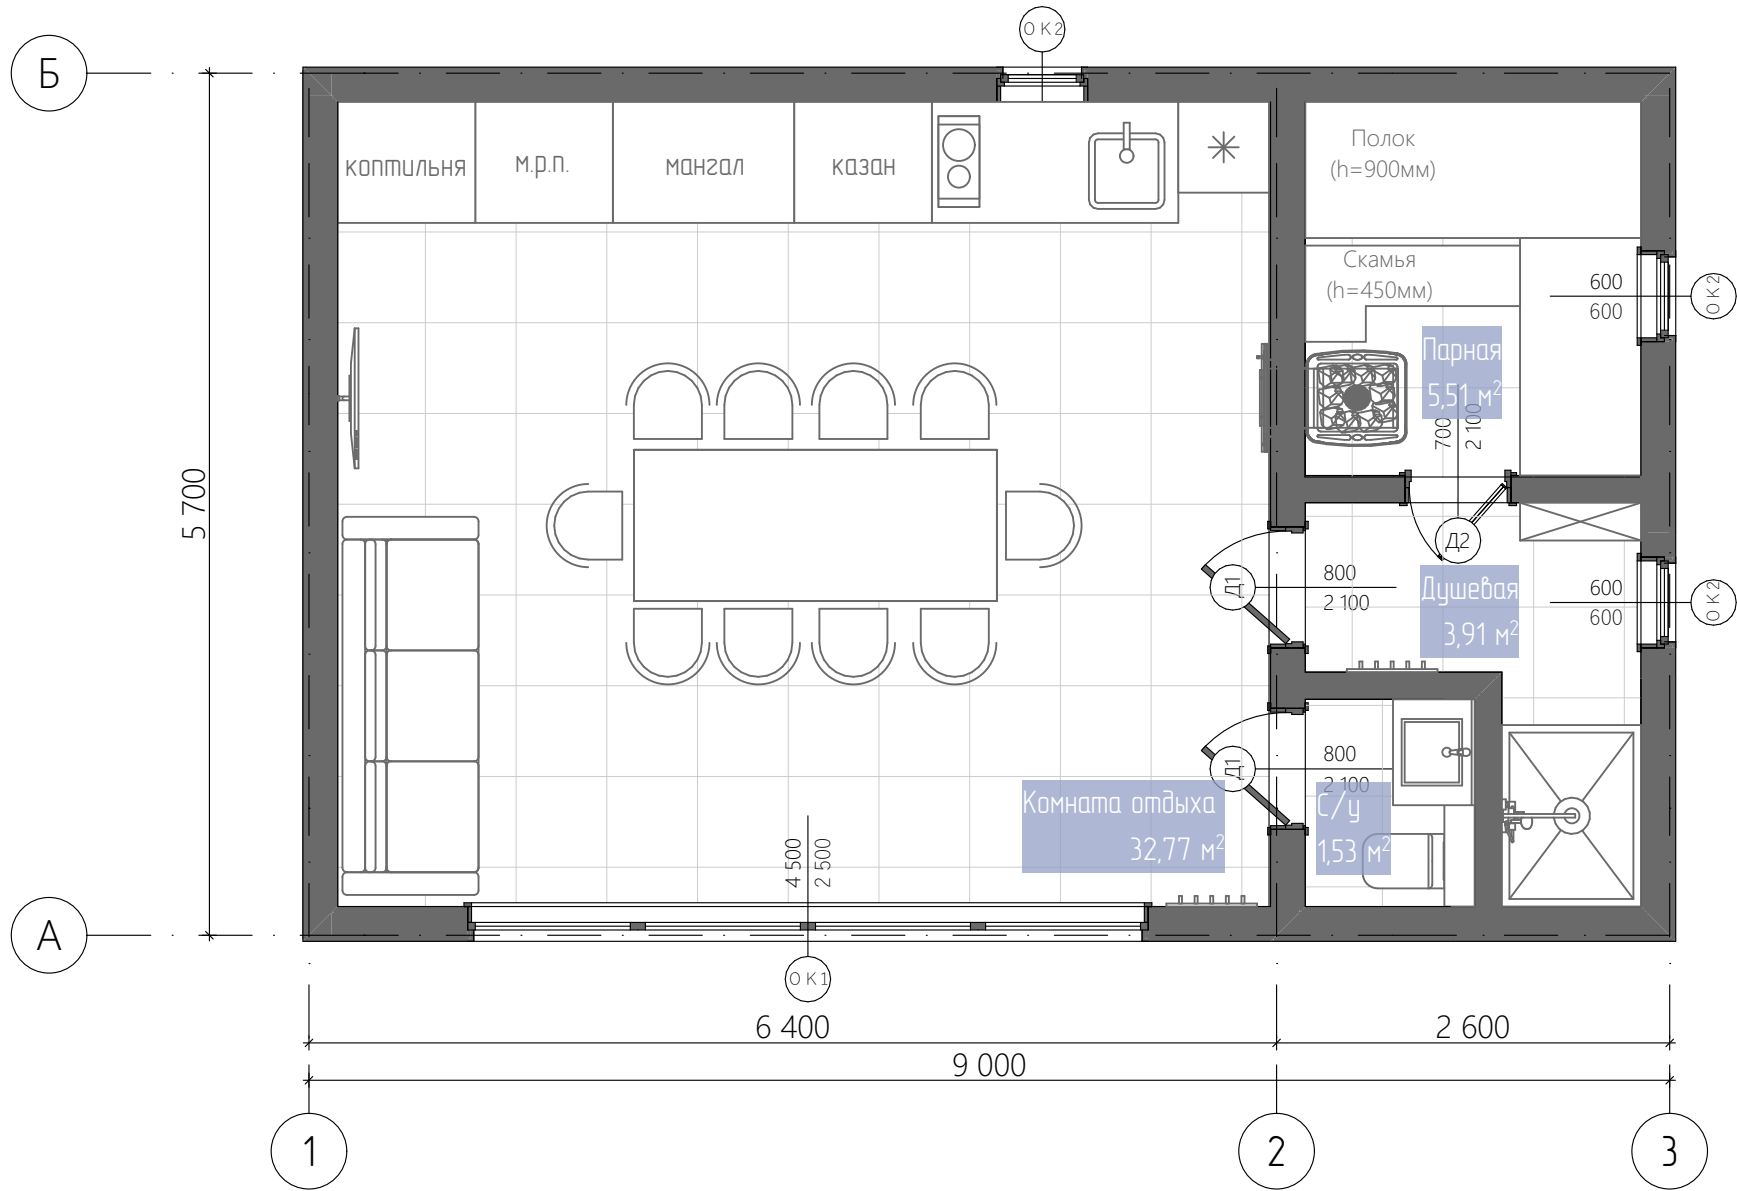

Экспликация помещений

№	Наименование	Площадь, кв.м.
1	Комната отдыха	32,77
2	С/у	1,53
3	Душевая	3,91
4	Парная	5,51
		43,72 м²
Наименование		Площадь, кв.м.
Площадь застройки		51,30

Примечание:

1. Вся индивидуальная мебель выполняется по отдельному проекту с детальной проработкой и калькуляцией. Чертежи предоставляет фирма-изготовитель столярных изделий.
2. Данный проект отдельно согласовывается с автором проекта и непосредственно с заказчиком.
3. Цветовое решение фасада и материалов отделки показаны в проекте приблизительно.
4. Количество ступеней показано условно.


Лист	Изм.	№ Докум.	Подп.	Дата

МО, Мытищинский район, Новые Вешки, Зеленый бульвар 78

Маркировочный план

#Название Организации

1:50

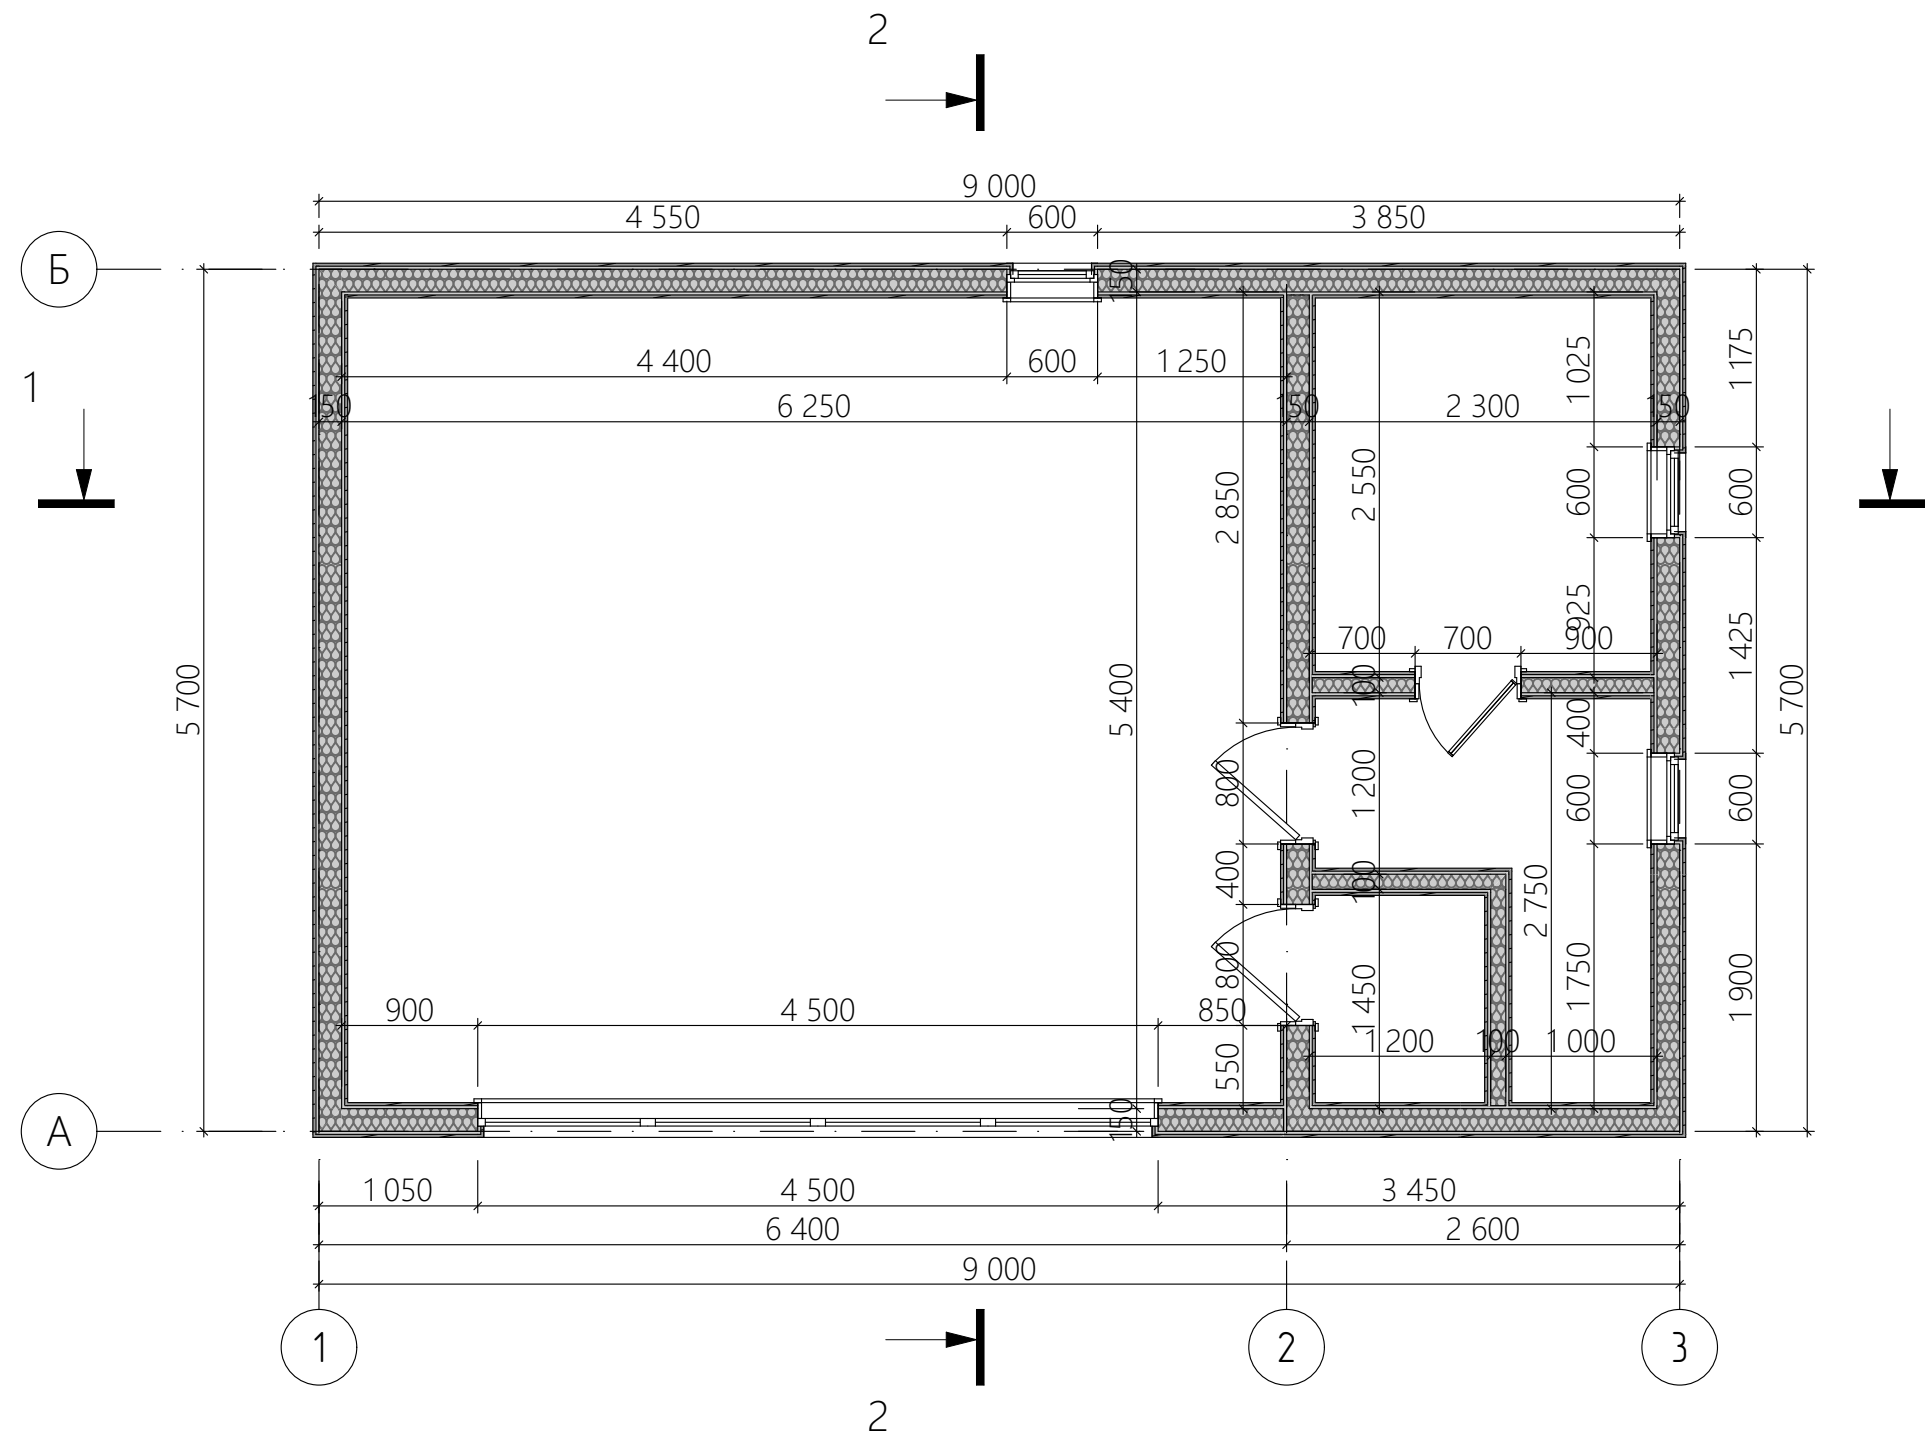

1. Представленные размеры указаны без учета внешней и внутренней отделки

Инв. № подл.	Подп. и дата	Взам. инв. №	Согласовано	


Лист	Изм.	№ Докум.	Подп.	Дата

МО, Мытищинский район, Новые Вешки, Зеленый бульвар 78

Размерный план

#Название Организации

6

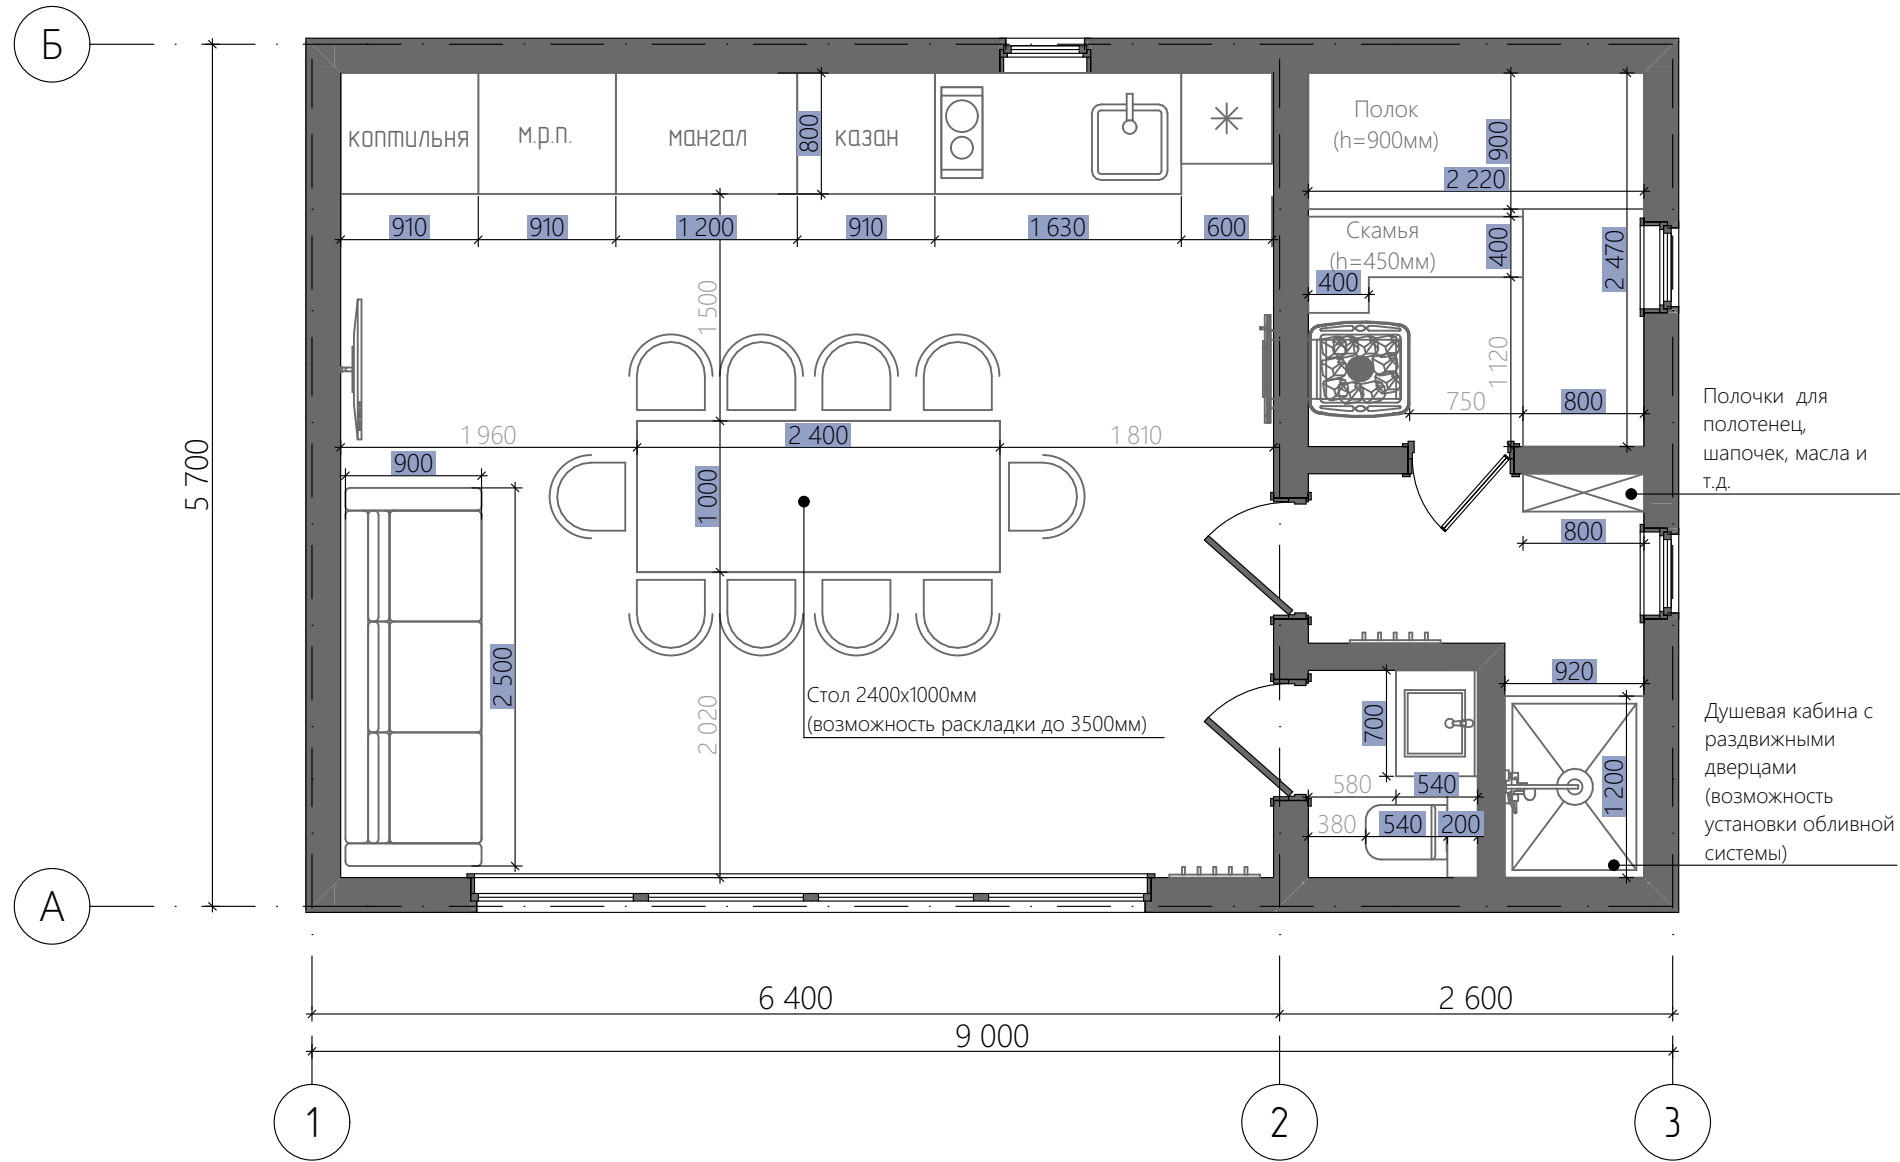

Примечание:

1. Вся индивидуальная мебель выполняется по отдельному проекту с детальной проработкой и калькуляцией. Чертежи предоставляет фирма-изготовитель столярных изделий.

2. Финальные размеры мебели и оборудования указаны ориентировочно — для точной компоновки требуется разработка дизайн-проекта.

Согласовано				
И-нв. № подл.	Взам. инв. №	Подп. и дата		

Лист	Изм.	№ Докум.	Подп.	Дата

МО, Мытищинский район, Новые Вешки, Зеленый бульвар 78		План расстановки мебели и оборудования	
--	--	--	--

#Название Организации	Лист
	7

Согласовано

Взам. инв. №

Подп. и дата


Инв. № подл.

Лист	Изм.	№ Докум.	Подп.	Дата

МО, Мытищинский район, Новые Вешки, Зеленый бульвар 78

Зд-разрез

#Название Организации

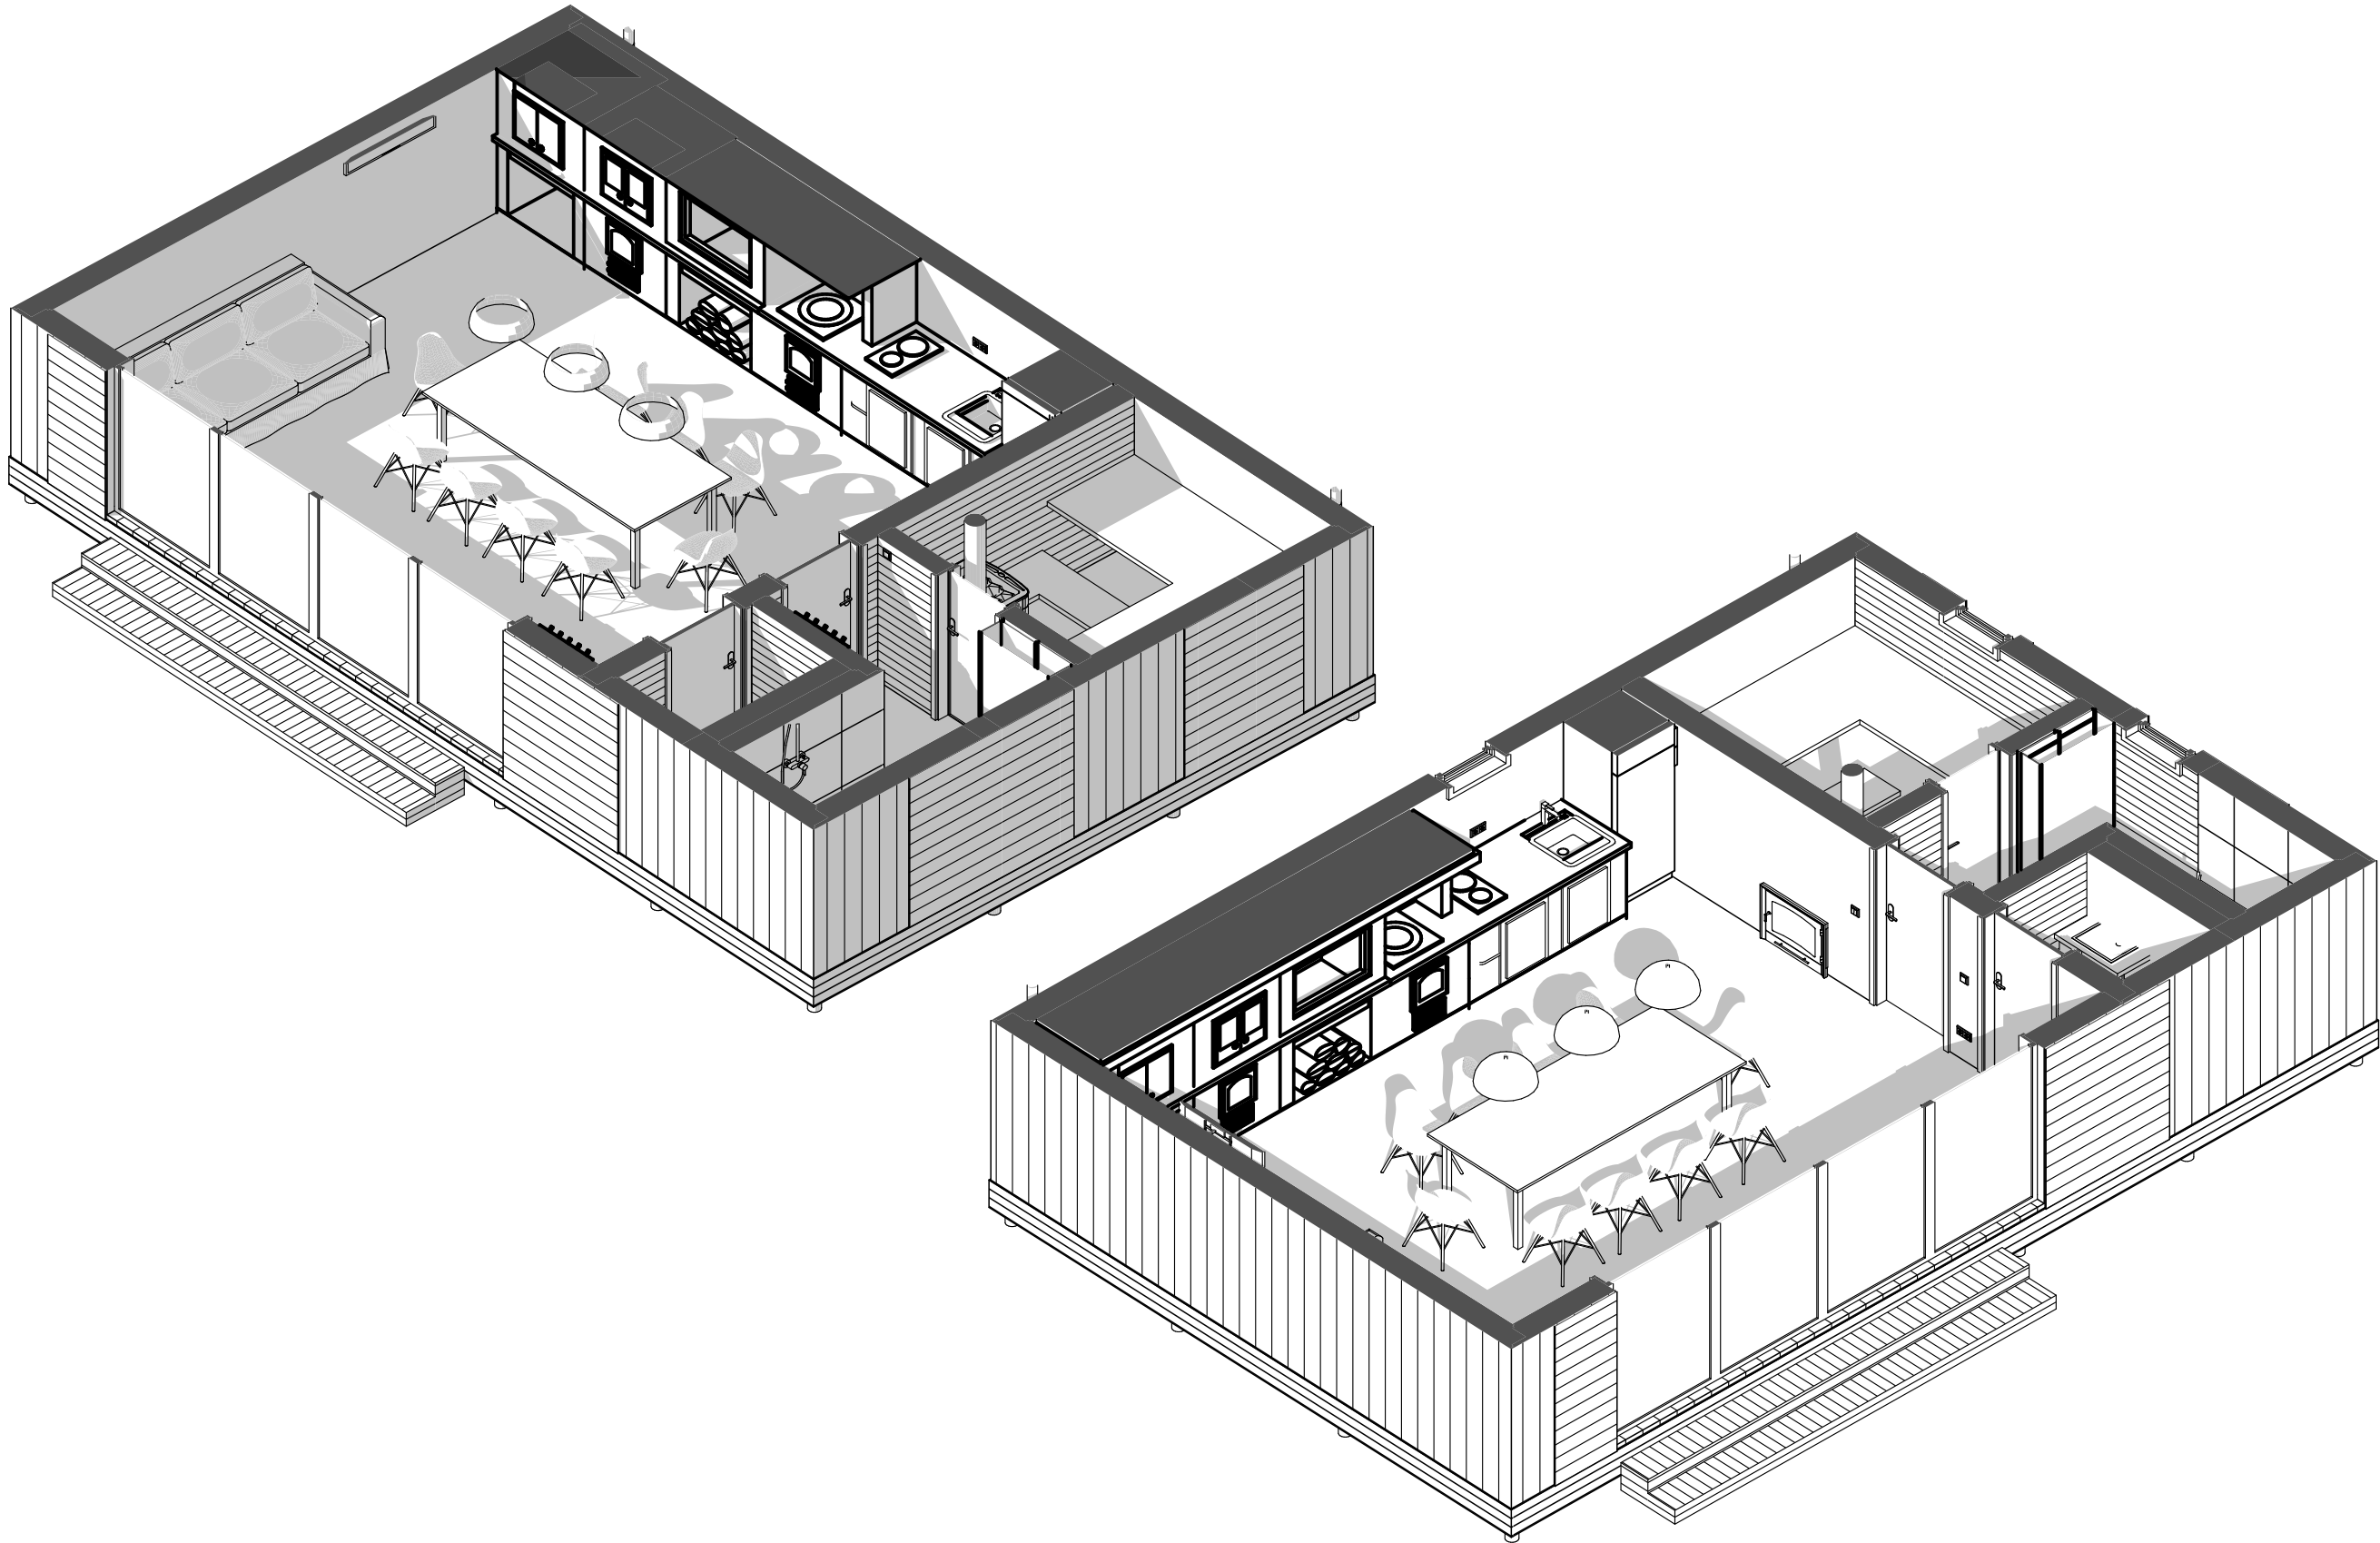

1:50

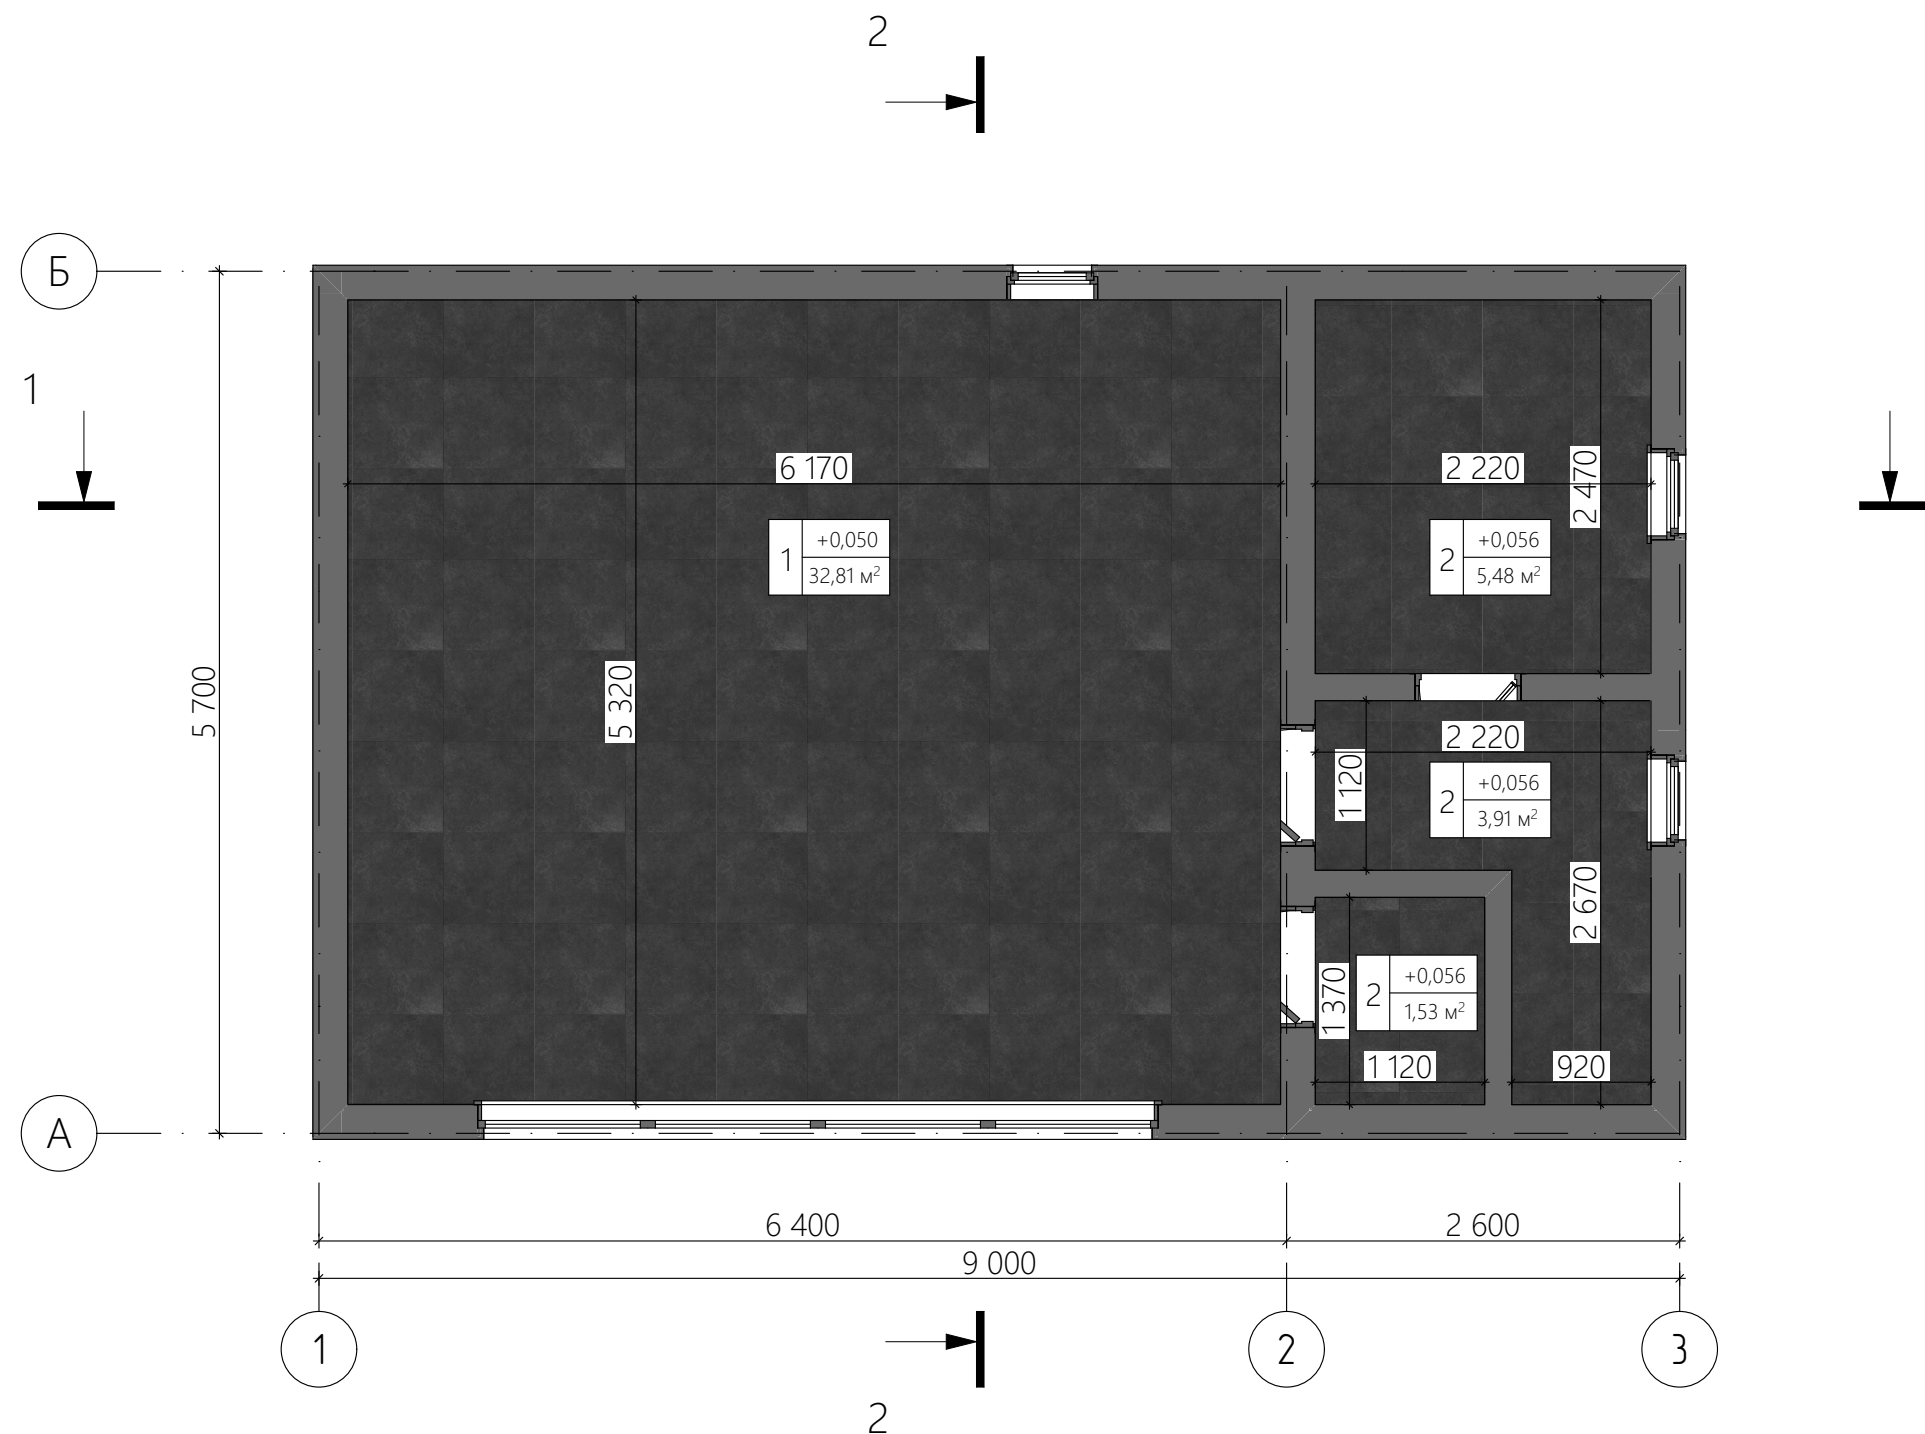


Схема подсчета площади покрытия:

- Вход: Номер покрытия
- Процессор: умножение (X)
- Операнды:
 - Высота от проектного нуля (+х,xxx)
 - Метр (xx,xx м²)
- Выход: Метраж покрытия

№	Наименование	Площадь, м ²
---	--------------	----------------------------

1	Керамогранит	43,68
---	--------------	-------

Примечание:

1. Приведённые цветовые решения носят рекомендательный характер. Фактический подбор оттенков и материалов выполняется на этапе реализации с учётом наличия продукции у поставщиков и утверждения заказчиком.
2. Пирог покрытия смотреть на след. листе.

Лист	Изм.	№ Докум.	Подп.	Дата

МО, Мытищинский район, Новые Вешки, Зеленый бульвар 78

План покрытия пола

#Название Организации

9

Согласовано

Взам. инв. №

Подп. и дата

ИНВ. № подл.


Пироги пола

[illegible]

Лист	Изм.	№ Докум.	Подп.	Дата	Пирог	#Название Организации	Лист
							10

План покрытия стен

1:50

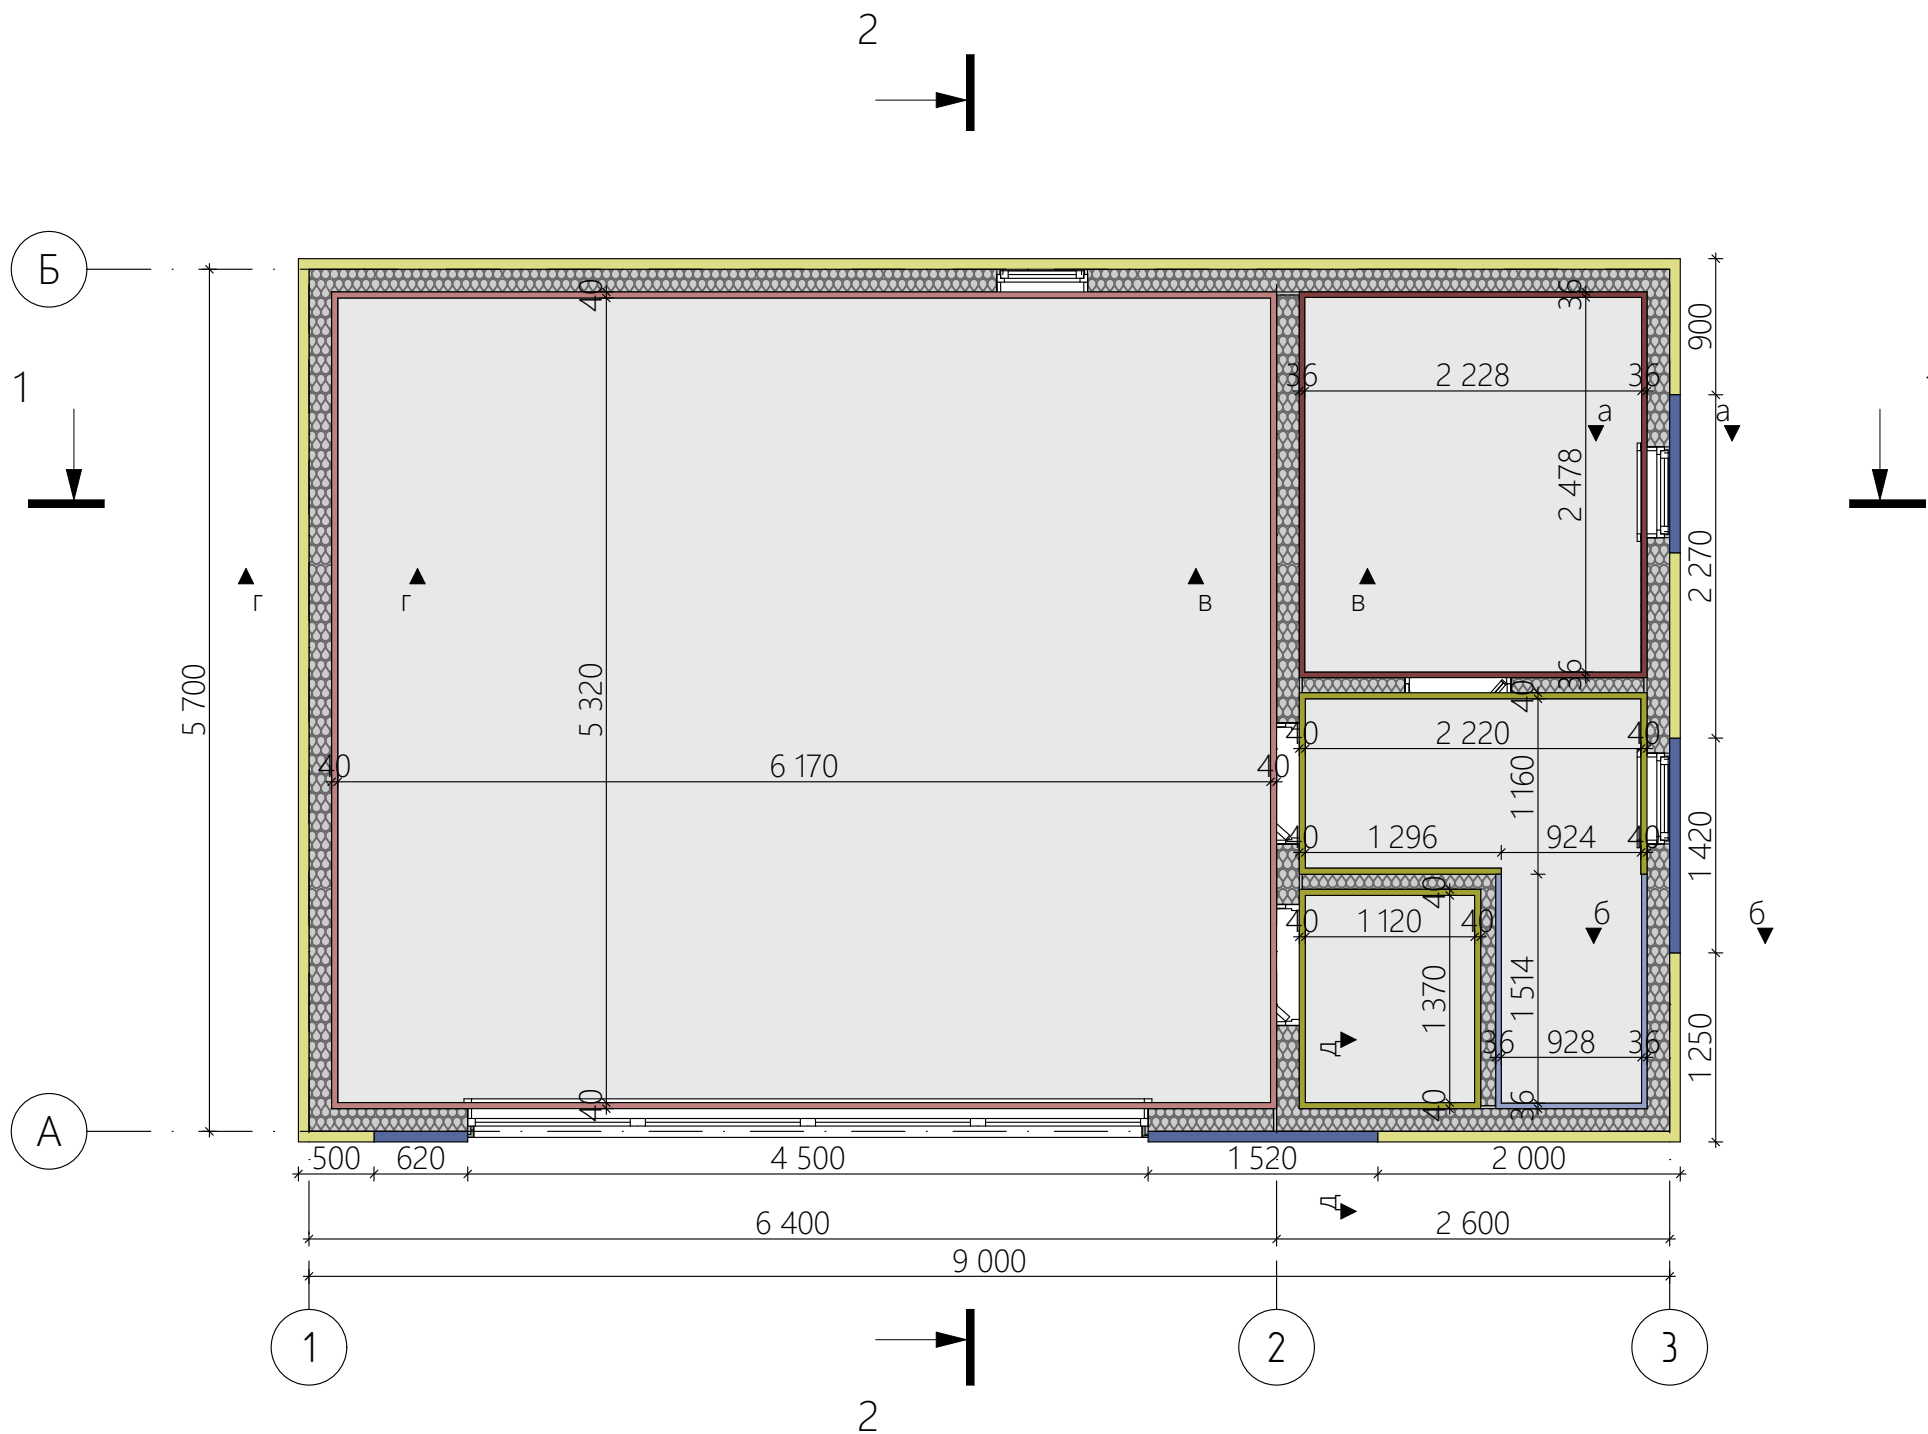

Экспликация покрытий стен

№	Наименование	Условное обозначение
1	Планкен (20мм)	
2	Фиброцементный сайдинг (20мм)	
3	Имитация бруса (20мм)	
4	Вагонка (16мм)	
5	Керамогранит (10мм)	
6	Гибкая керамика (5мм)	

Согласовано				
И-нв. № подл.	Взам. инв. №	Подп. и дата		

Лист	Изм.	№ Докум.	Подп.	Дата

МО, Мытищинский район, Новые Вешки, Зеленый бульвар 78

План покрытия стен

#Название Организации


Пироги стен

№ разреза

Сечение


Состав

а-а

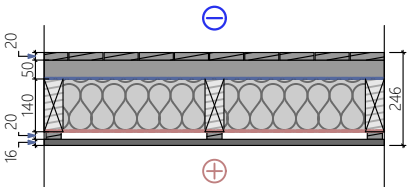


- Планкен 20мм
- Вентбрус (горизонтально) 50мм
- Гидро-ветрозащитная мембрана -
- Стойка каркаса (утепленная) 140мм
- Пароизоляционная мембрана (алюм. фольга) -
- Вентбрус (вертикально) 20мм
- Вагонка 16мм

б-б

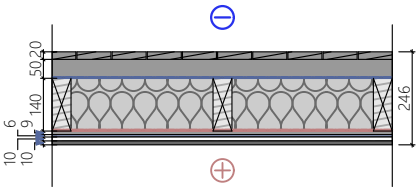


- Планкен 20мм
- Вентбрус (горизонтально) 50мм
- Гидро-ветрозащитная мембрана -
- Стойка каркаса (утепленная) 140мм
- Пароизоляционная мембрана -
- ОСБ 9мм
- Рупанель 6мм
- Клей 10мм
- Керамогранит 10мм

в-в

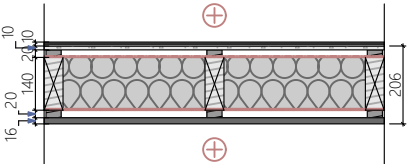


- Гибкая керамика 5мм
- Клей 5мм
- ЦСП 10мм
- Вентбрус (вертикально) 20мм
- Пароизоляционная мембрана -
- Стойка каркаса (утепленная) 140мм
- Пароизоляционная мембрана (алюм. фольга) -
- Вентбрус (вертикально) 20мм
- Вагонка 16мм

г-г

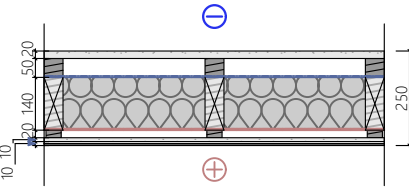

- Фиброцементный сайдинг 20мм
- Вентбрус (вертикально) 50мм
- Гидро-ветрозащитная мембрана -
- Стойка каркаса (утепленная) 140мм
- Пароизоляционная мембрана -
- Вентбрус (вертикально) 20мм
- ЦСП 10мм
- Клей 5мм
- Гибкая керамика 5мм

д-д

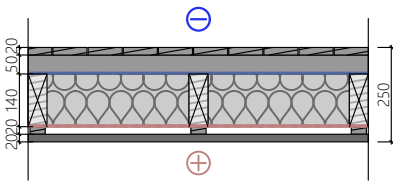

- Планкен 20мм
- Вентбрус (горизонтально) 20мм
- Гидро-ветрозащитная мембрана -
- Стойка каркаса (утепленная) 140
- Пароизоляционная мембрана -
- Вентбрус (вертикально) 20мм
- Имитация бруса 20мм

Согласовано

Взам. инв. №

Подп. и дата

Инв. № подл.

Лист	Изм.	№ Докум.	Подп.	Дата

Пироги стен


#Название Организации

Лист

12

План размещения розеток

1:50

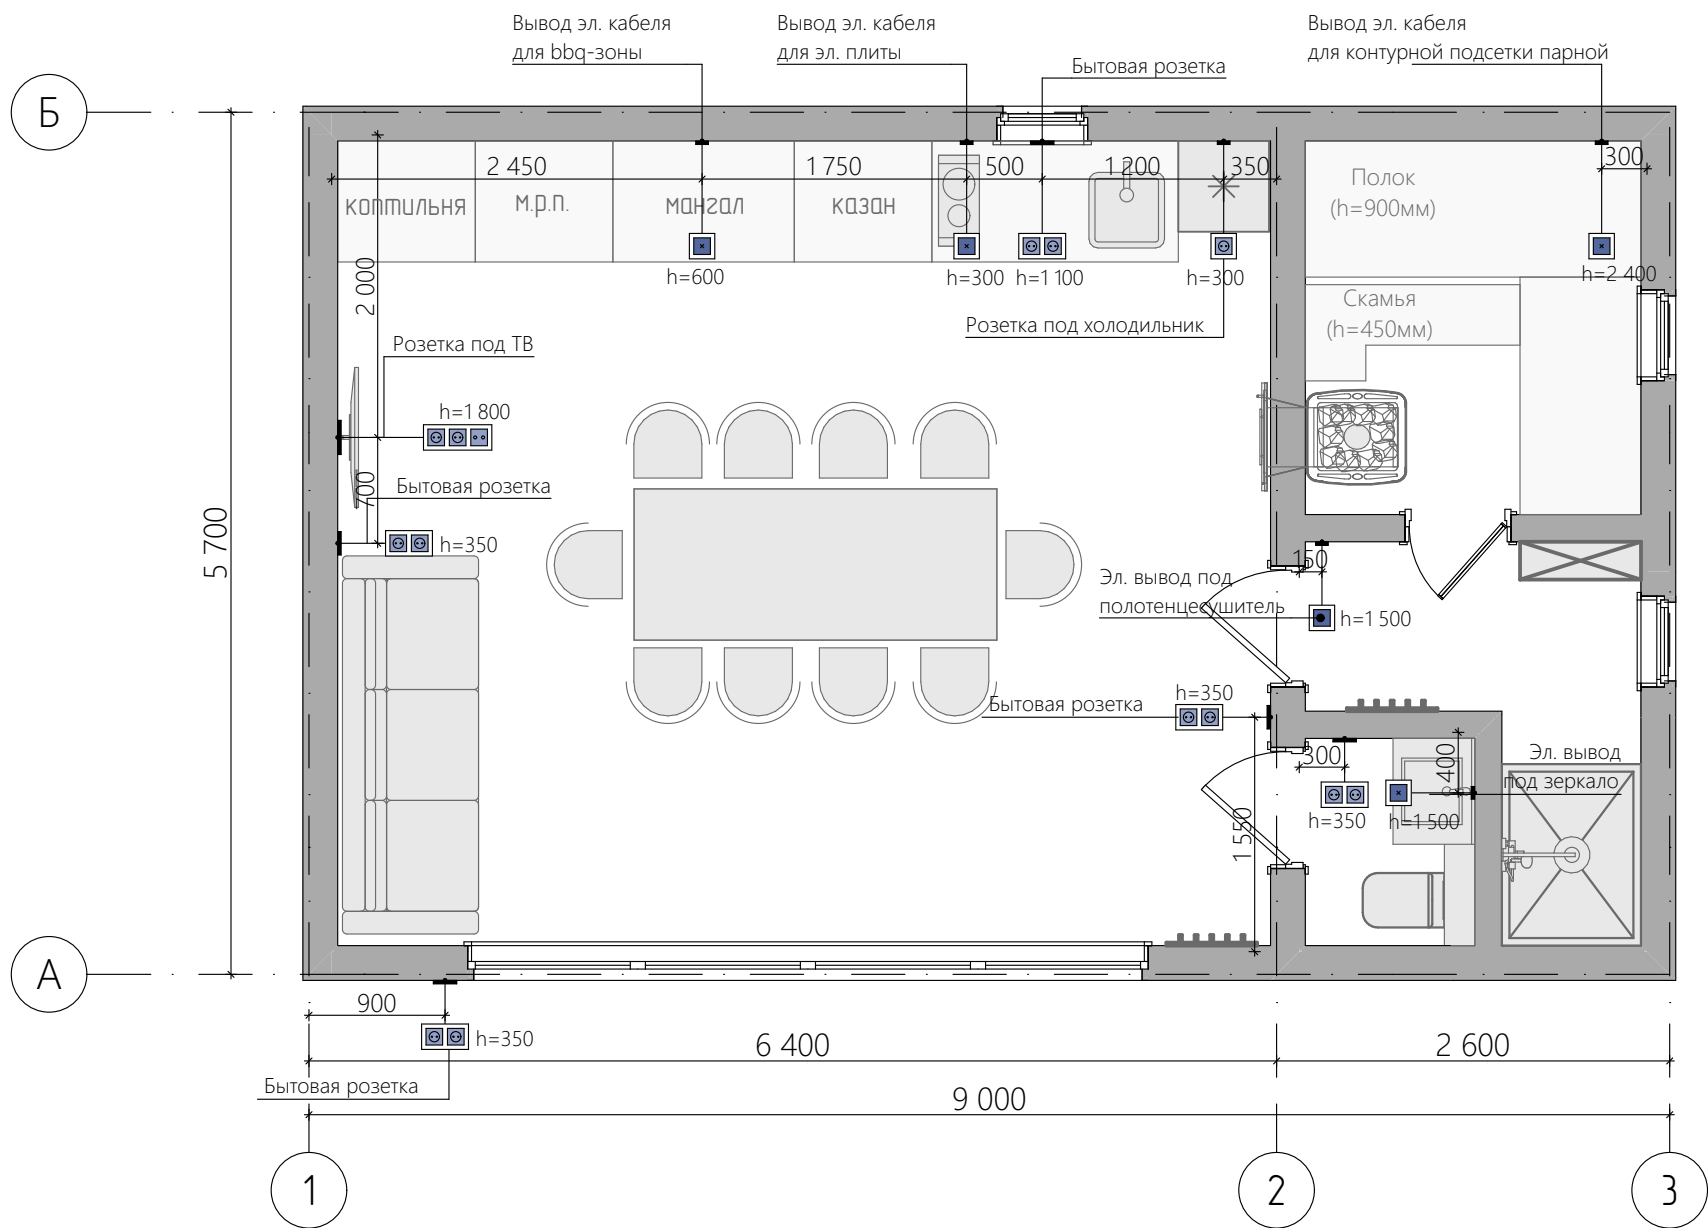

Экспликация розеток

Наименование	2д-вид	Кол-во
Розетка 220v (рамка 1 секции)		1
Розетка 220v (рамка 2 секции)		5
Розетка 220v+ТВ розетка (рамка 2 секции)		1
Эл. вывод		3
Эл. вывод (влагозащитная)		2
		12

Примечание:

1. Схема размещения розеток является рекомендательной и требует согласования с заказчиком по месту.
2. Все высоты даны от чистового пола.
3. Все указанные размеры даются до центра позиций.
4. Отметки розеток, выключателей, выводов и др. оборудования, являются предварительными и уточняются после выбора финишных материалов и мебели.
5. Размеры уточняются дополнительно

Согласовано

Взам. инв. №

Подп. и дата

Инв. № подл.

Лист	Изм.	№ Докум.	Подп.	Дата


МО, Мытищинский район, Новые Вешки, Зеленый бульвар 78

План размещения розеток

#Название Организации

План размещения светильников и выключателей

1:50

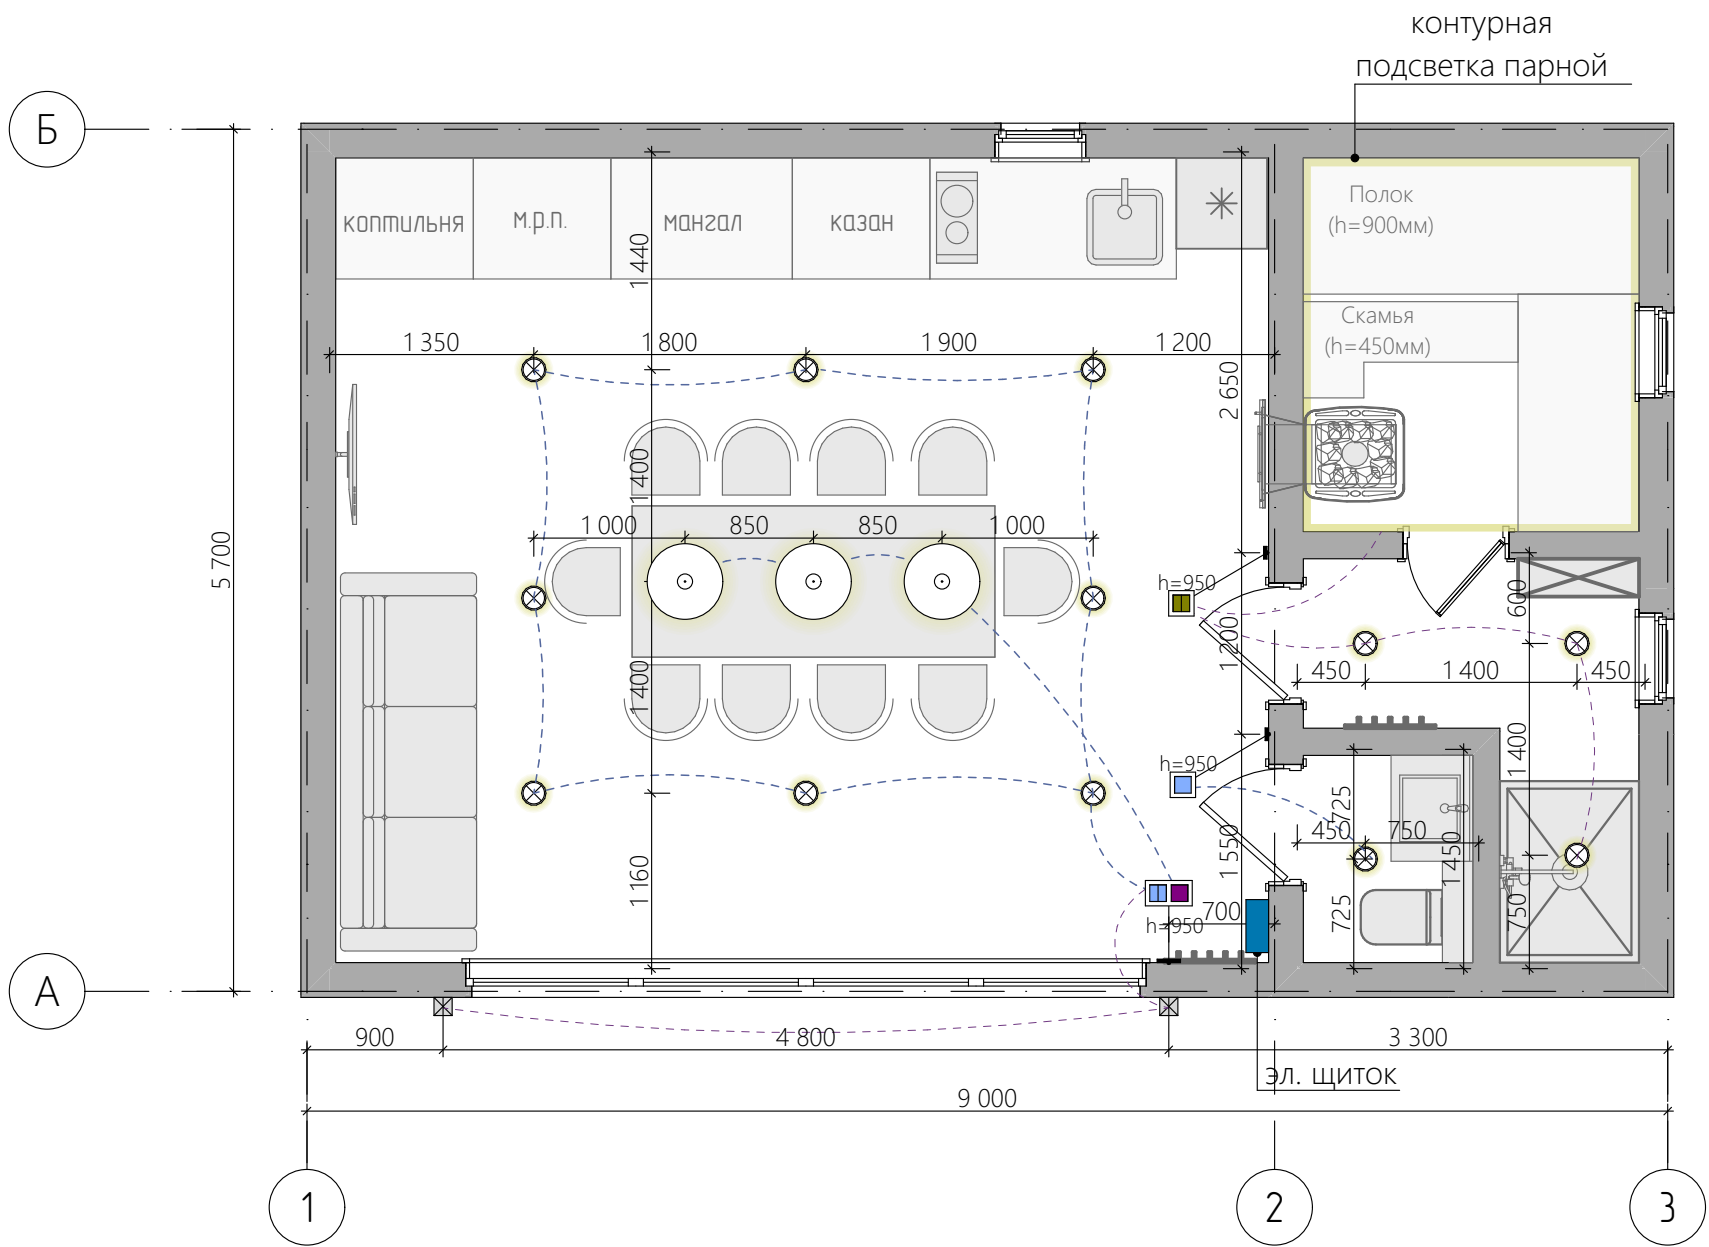

Экспликация светильников и выключателей

Наименование	2д-вид	Кол-во
--------------	--------	--------

Выключатель двухклавишный (рамка 1 секции)		1
--	--	---

Выключатель одно- и двухклавишный (рамка 2 секции)		1
--	--	---

Выключатель одноклавишный (рамка 1 секции)		1
--	--	---

Светильник точечный		12
---------------------	--	----

Светильник подвесной		3
----------------------	--	---

Уличный светильник		2
--------------------	--	---

20

Примечание:

1. Схема размещения розеток является рекомендательной и требует согласования с заказчиком по месту.
2. Все высоты даны от чистового пола.
3. Все указанные размеры даются до центра позиций.
4. Отметки розеток, выключателей, выводов и др. оборудования, являются предварительными и уточняются после выбора финишных материалов и мебели.
5. Размеры уточняются дополнительно

Лист	Изм.	№ Докум.	Подп.	Дата


МО, Мытищинский район, Новые Вешки, Зеленый бульвар 78

План размещения светильников и выключателей

#Название Организации

План крыши

1:50

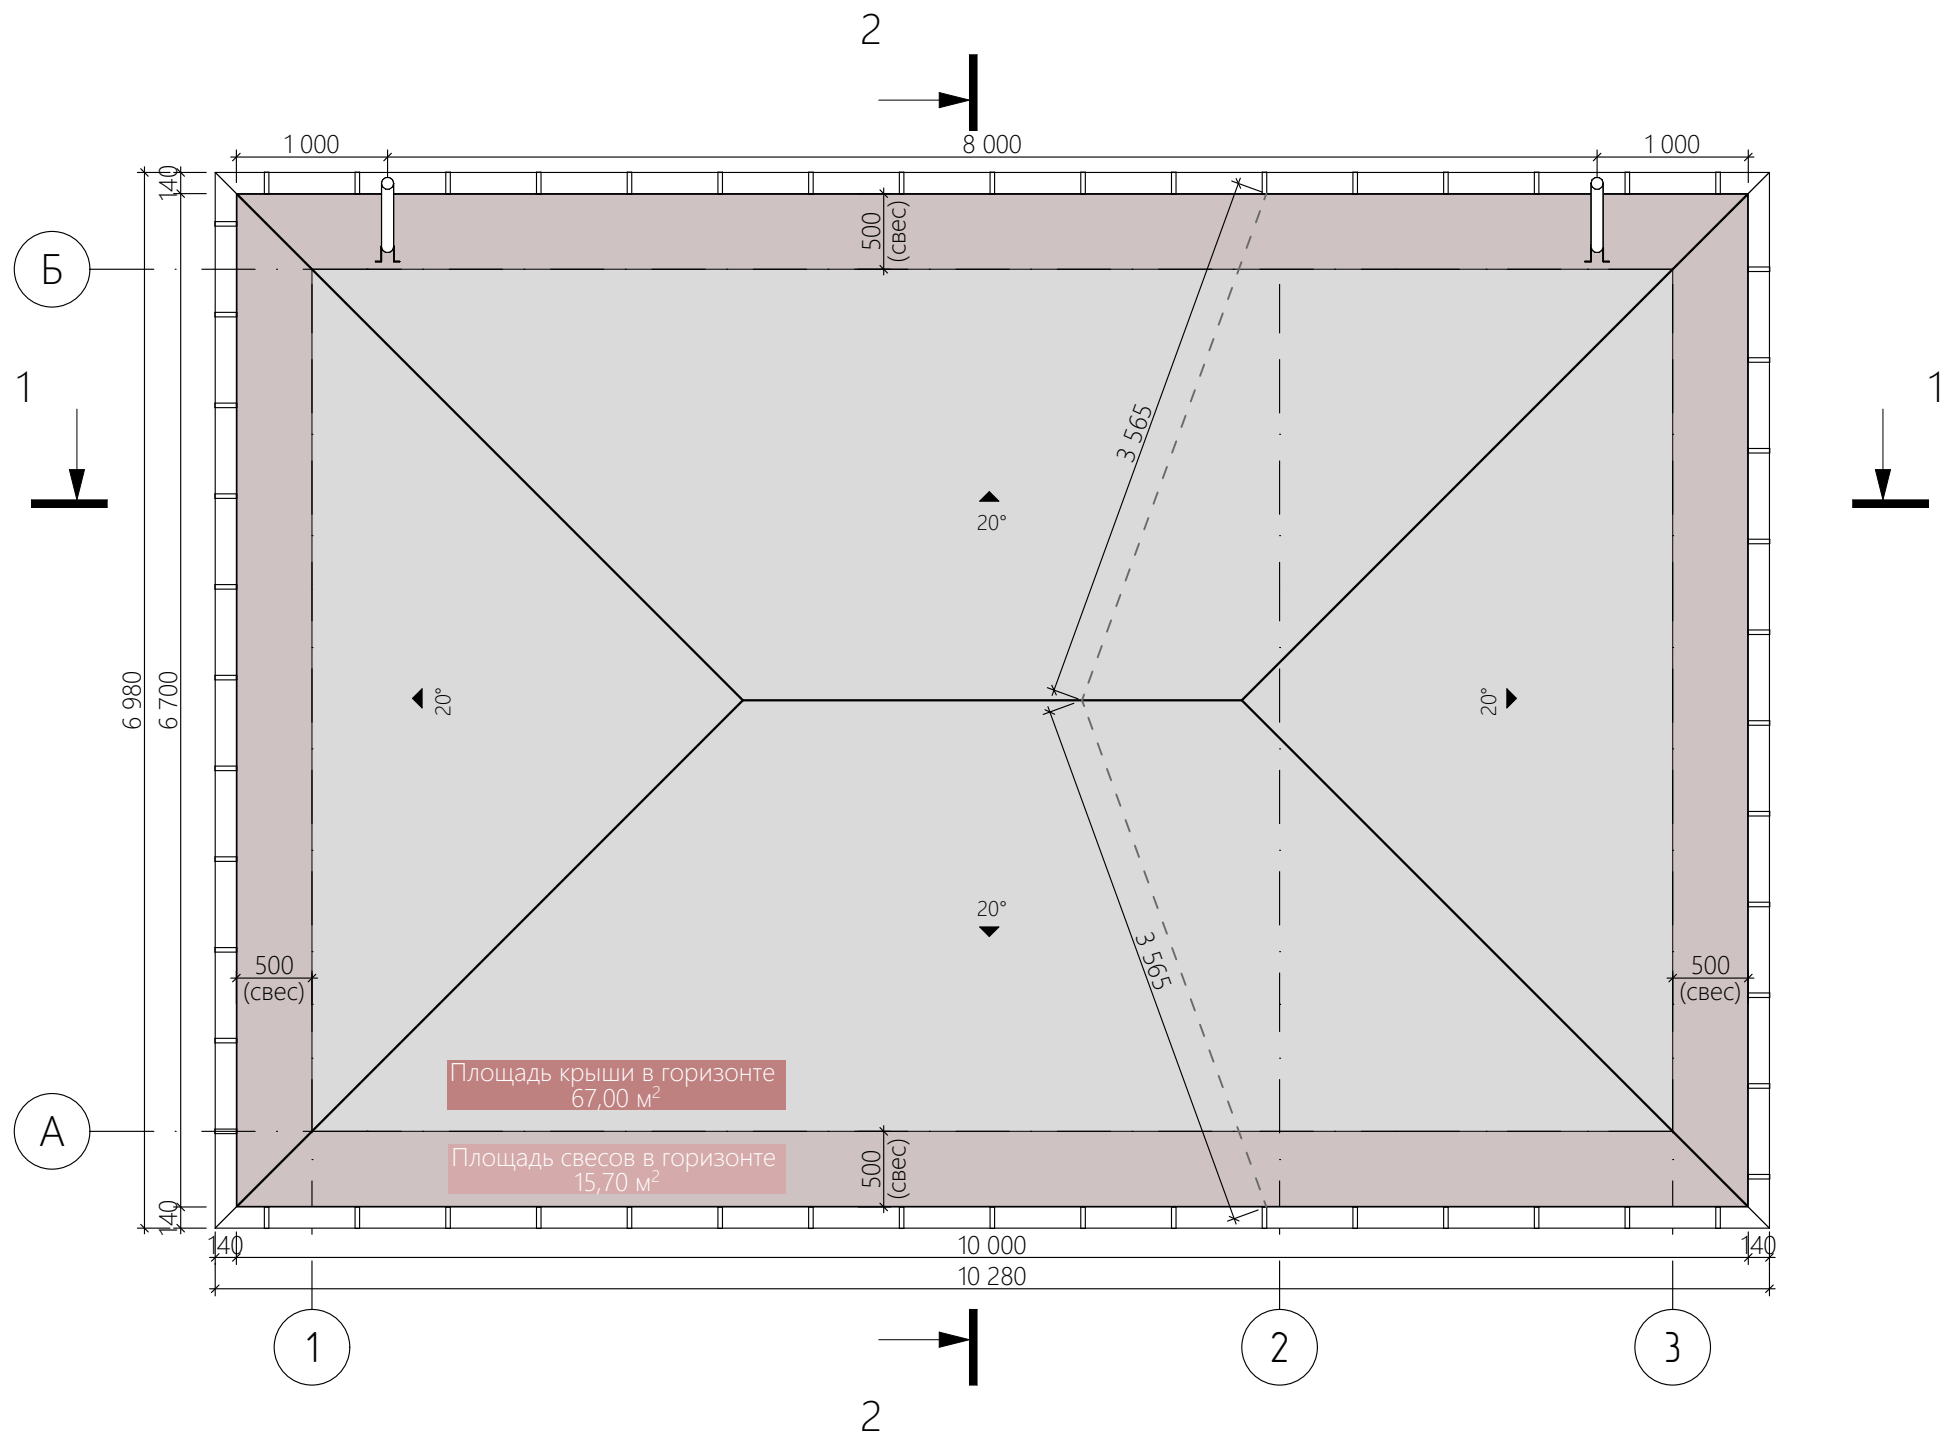


Условные обозначения:

- Крыша бани (уклон 20°)
- Подшив свесов бани

Площадь крыши бани (S, м²) = 71,3м²

Аксонометрия крыши

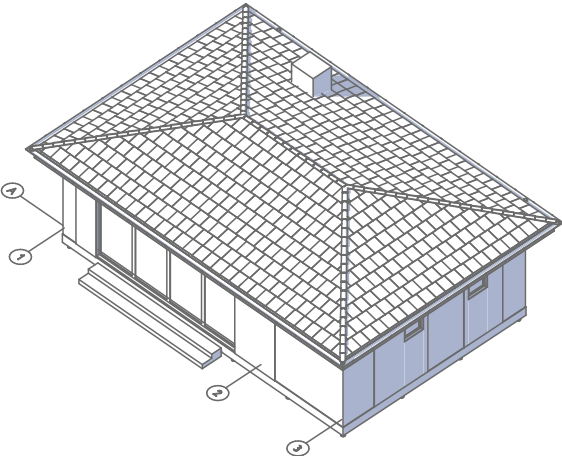

Согласовано					
И-нв. № подл.	Подп. и дата	Взам. инв. №			

Лист	Изм.	№ Докум.	Подп.	Дата

МО, Мытищинский район, Новые Вешки, Зеленый бульвар 78

План крыши

#Название Организации

1:1

Наименование	Размеры проема Ш x В, мм	Вид	Кол-во	Площадь, м2
--------------	--------------------------	-----	--------	-------------

--	--	--	--



12,33 m²

Согласовано

И№в. №	Подп. и дата	Взам. инв. №
--------	--------------	--------------

1. Изготовление окон и дверей определяется заказчиком, допускается изменение открывания окон и дверей;
2. При заказе оконных и дверных блоков необходим обмер по месту от изготовителя;
3. Оконные и дверные изделия изображены со стороны открывания.

Лист	Изм.	№ Докум.	Подп.	Дата	Ведомость оконных проемов	#Название Организации	Лист
							16

1:1


Инв. № подл.	Подп. и дата	Взам. инв. №

1. Изготовление окон и дверей определяется заказчиком, допускается изменение открывания окон и дверей;
2. При заказе оконных и дверных блоков необходим обмер по месту от изготовителя;
3. Оконные и дверные изделия изображены со стороны открывания.

Лист	Изм.	№ Докум.	Подп.	Дата	Ведомость дверных проемов	#Название Организации	Лист
							17

Разрез 1-1

1:40

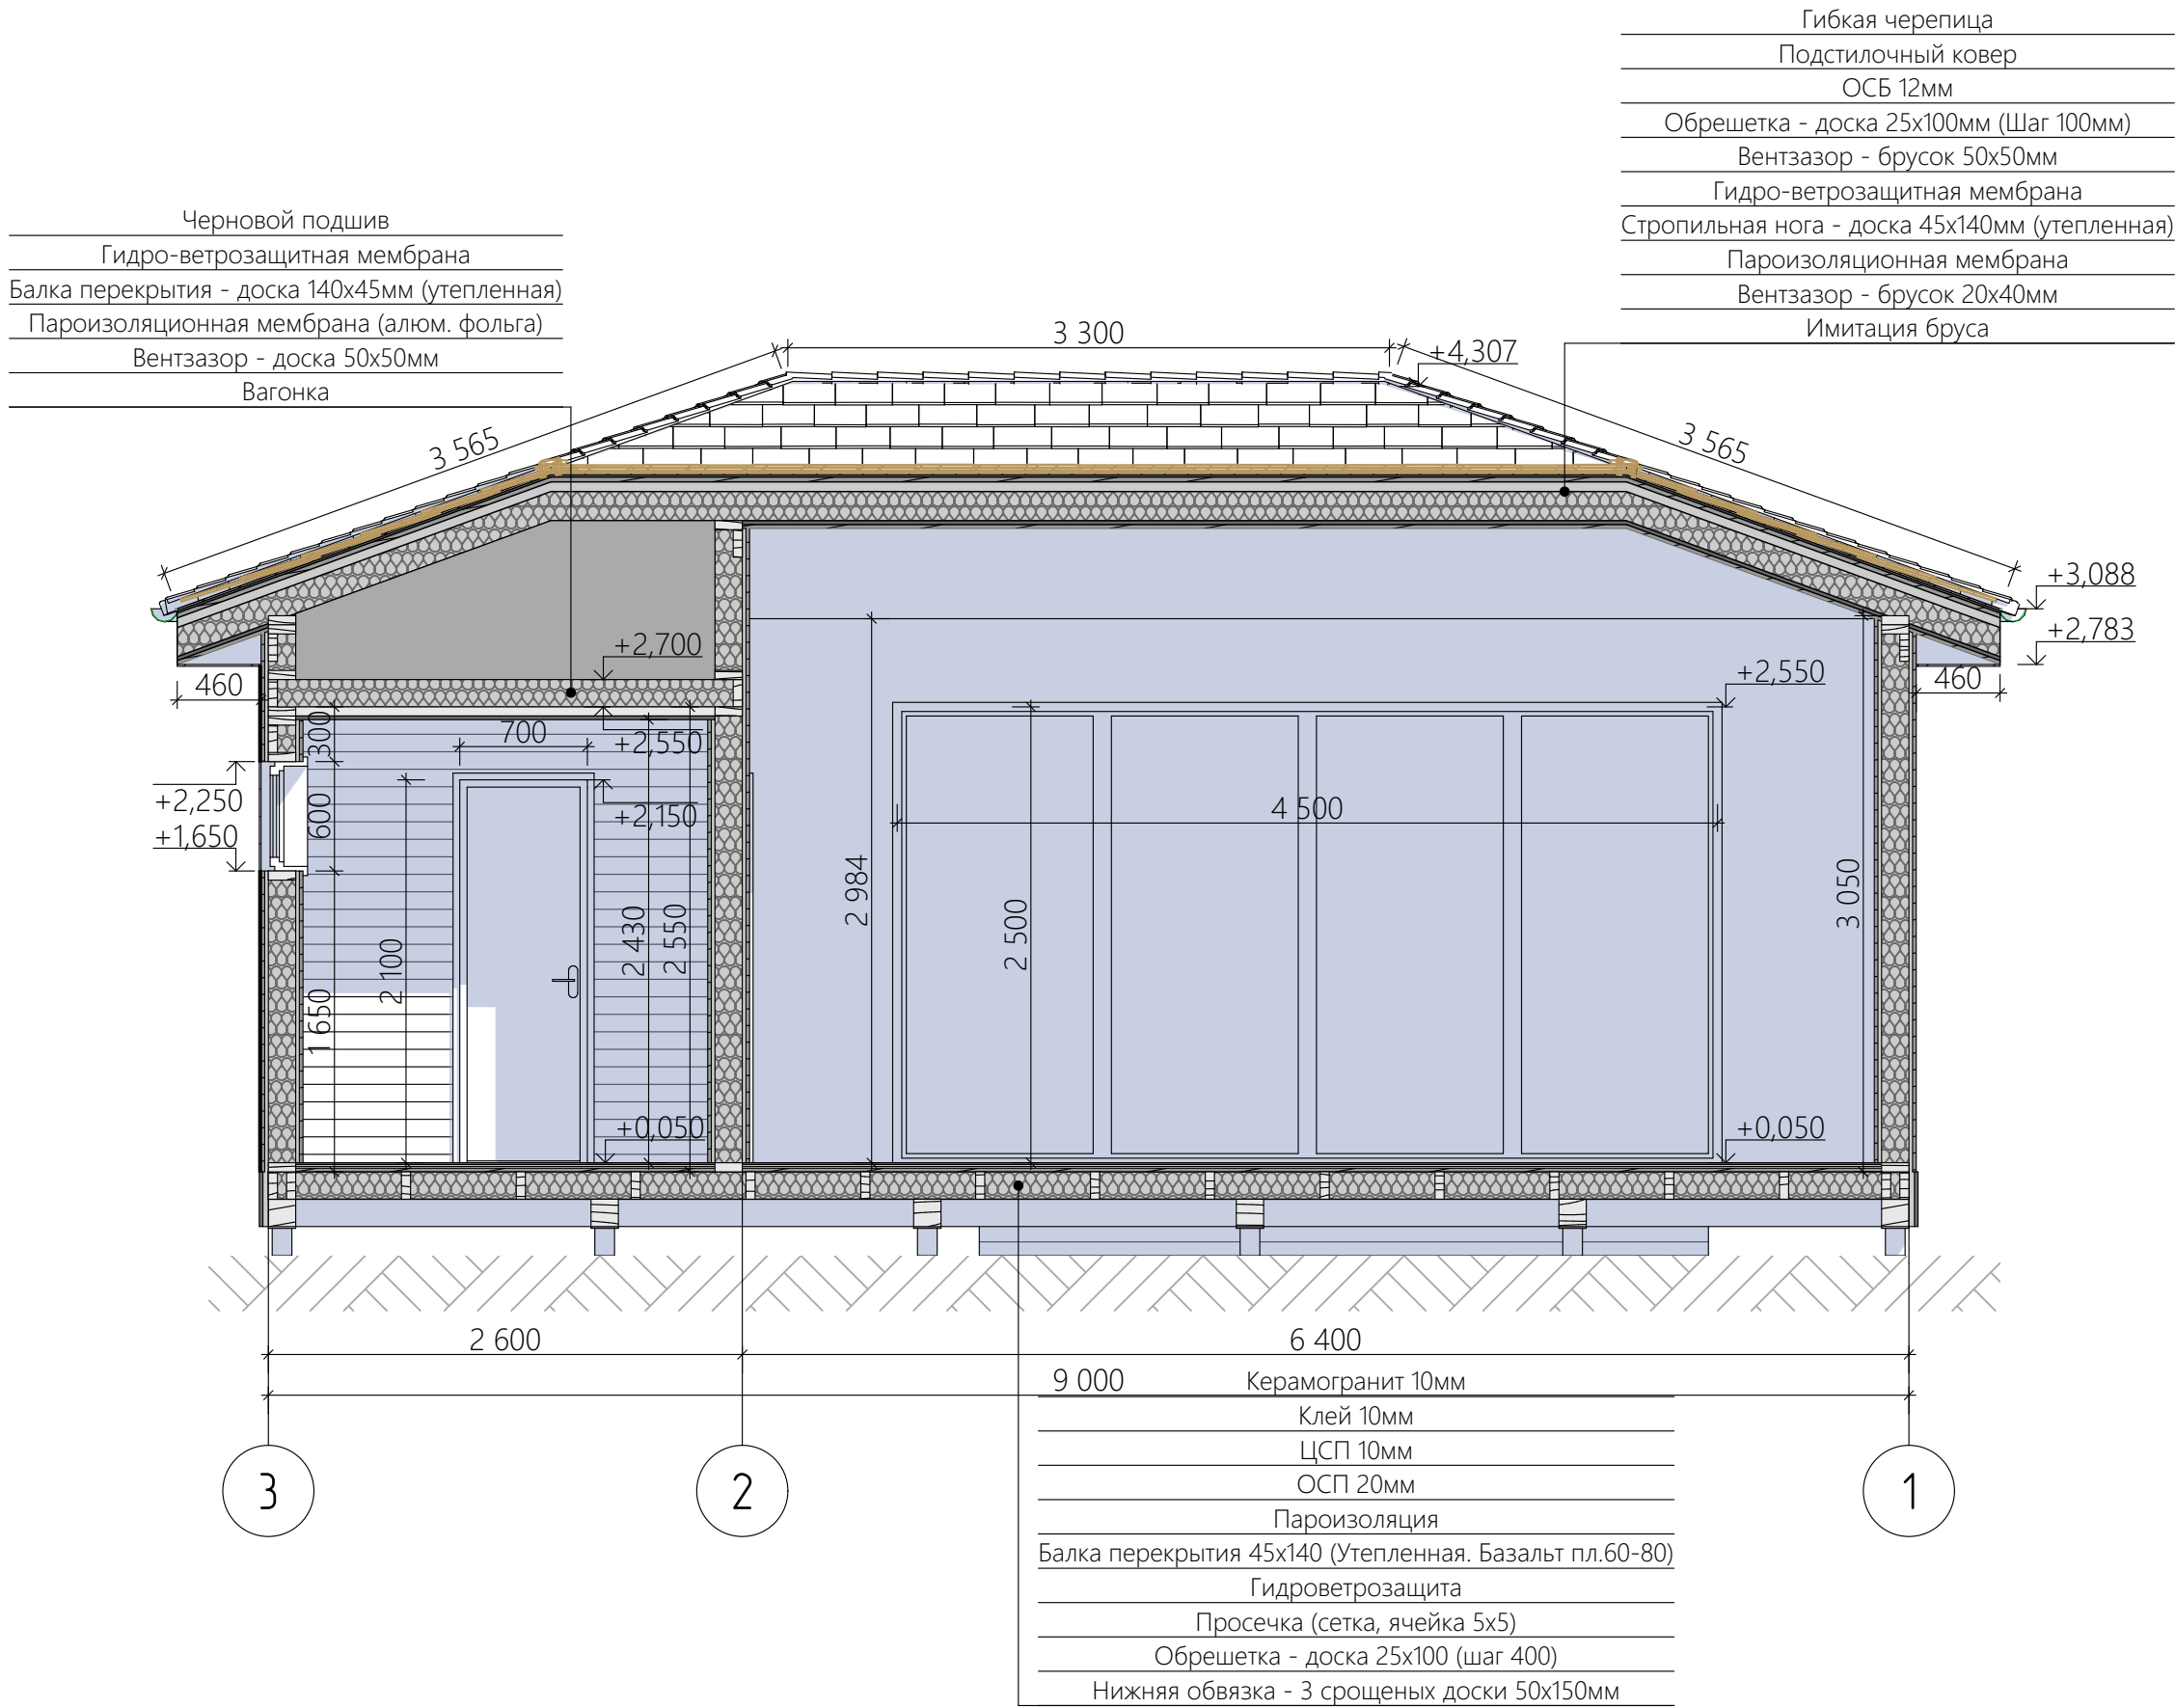

Согласовано				
Взам. инв. №				
Подп. и дата				
Инв. № подл.				

Лист	Изм.	№ Докум.	Подп.	Дата

МО, Мытищинский район, Новые Вешки, Зеленый бульвар 78
--


Разрез 1-1

#Название Организации

Лист
18

Разрез 2-2

1:40

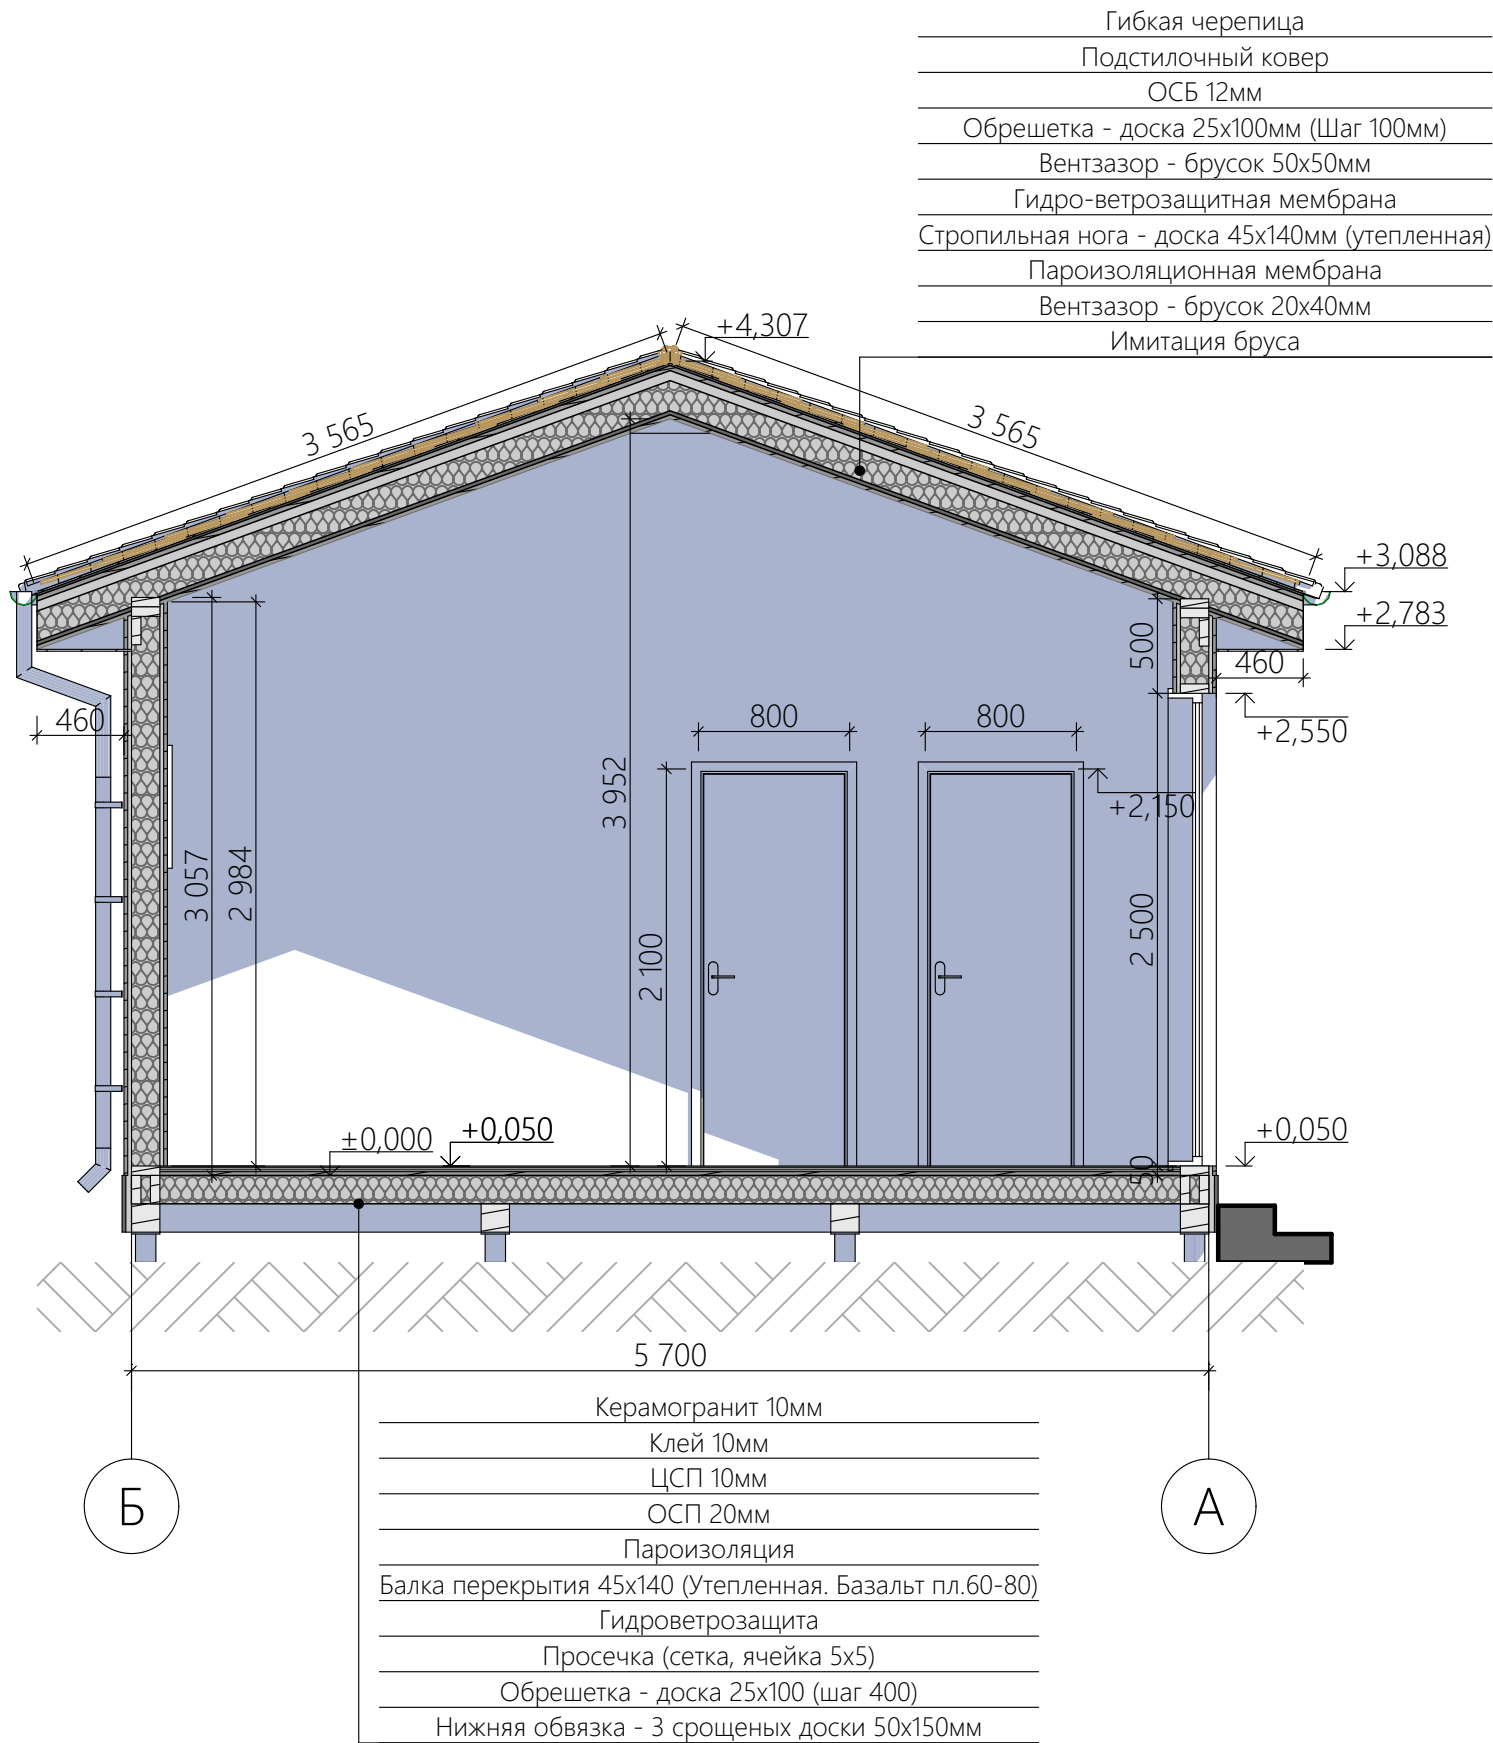

Согласовано					
И-нв. № подл.	Подп. и дата	Взам. инв. №			

Лист	Изм.	№ Докум.	Подп.	Дата

МО, Мытищинский район, Новые Вешки, Зеленый бульвар 78

Разрез 2-2


#Название Организации

Фасад 1-3

1:40

Условные обозначения:

- Фиброцементный сайдинг (RAL 7024)
- Террасная доска (Экодек кантри серый)
- Водосточная система, металлочерепица лобовая рамы, наличники (RAL 7024)
- Планкен (цвет махагон)

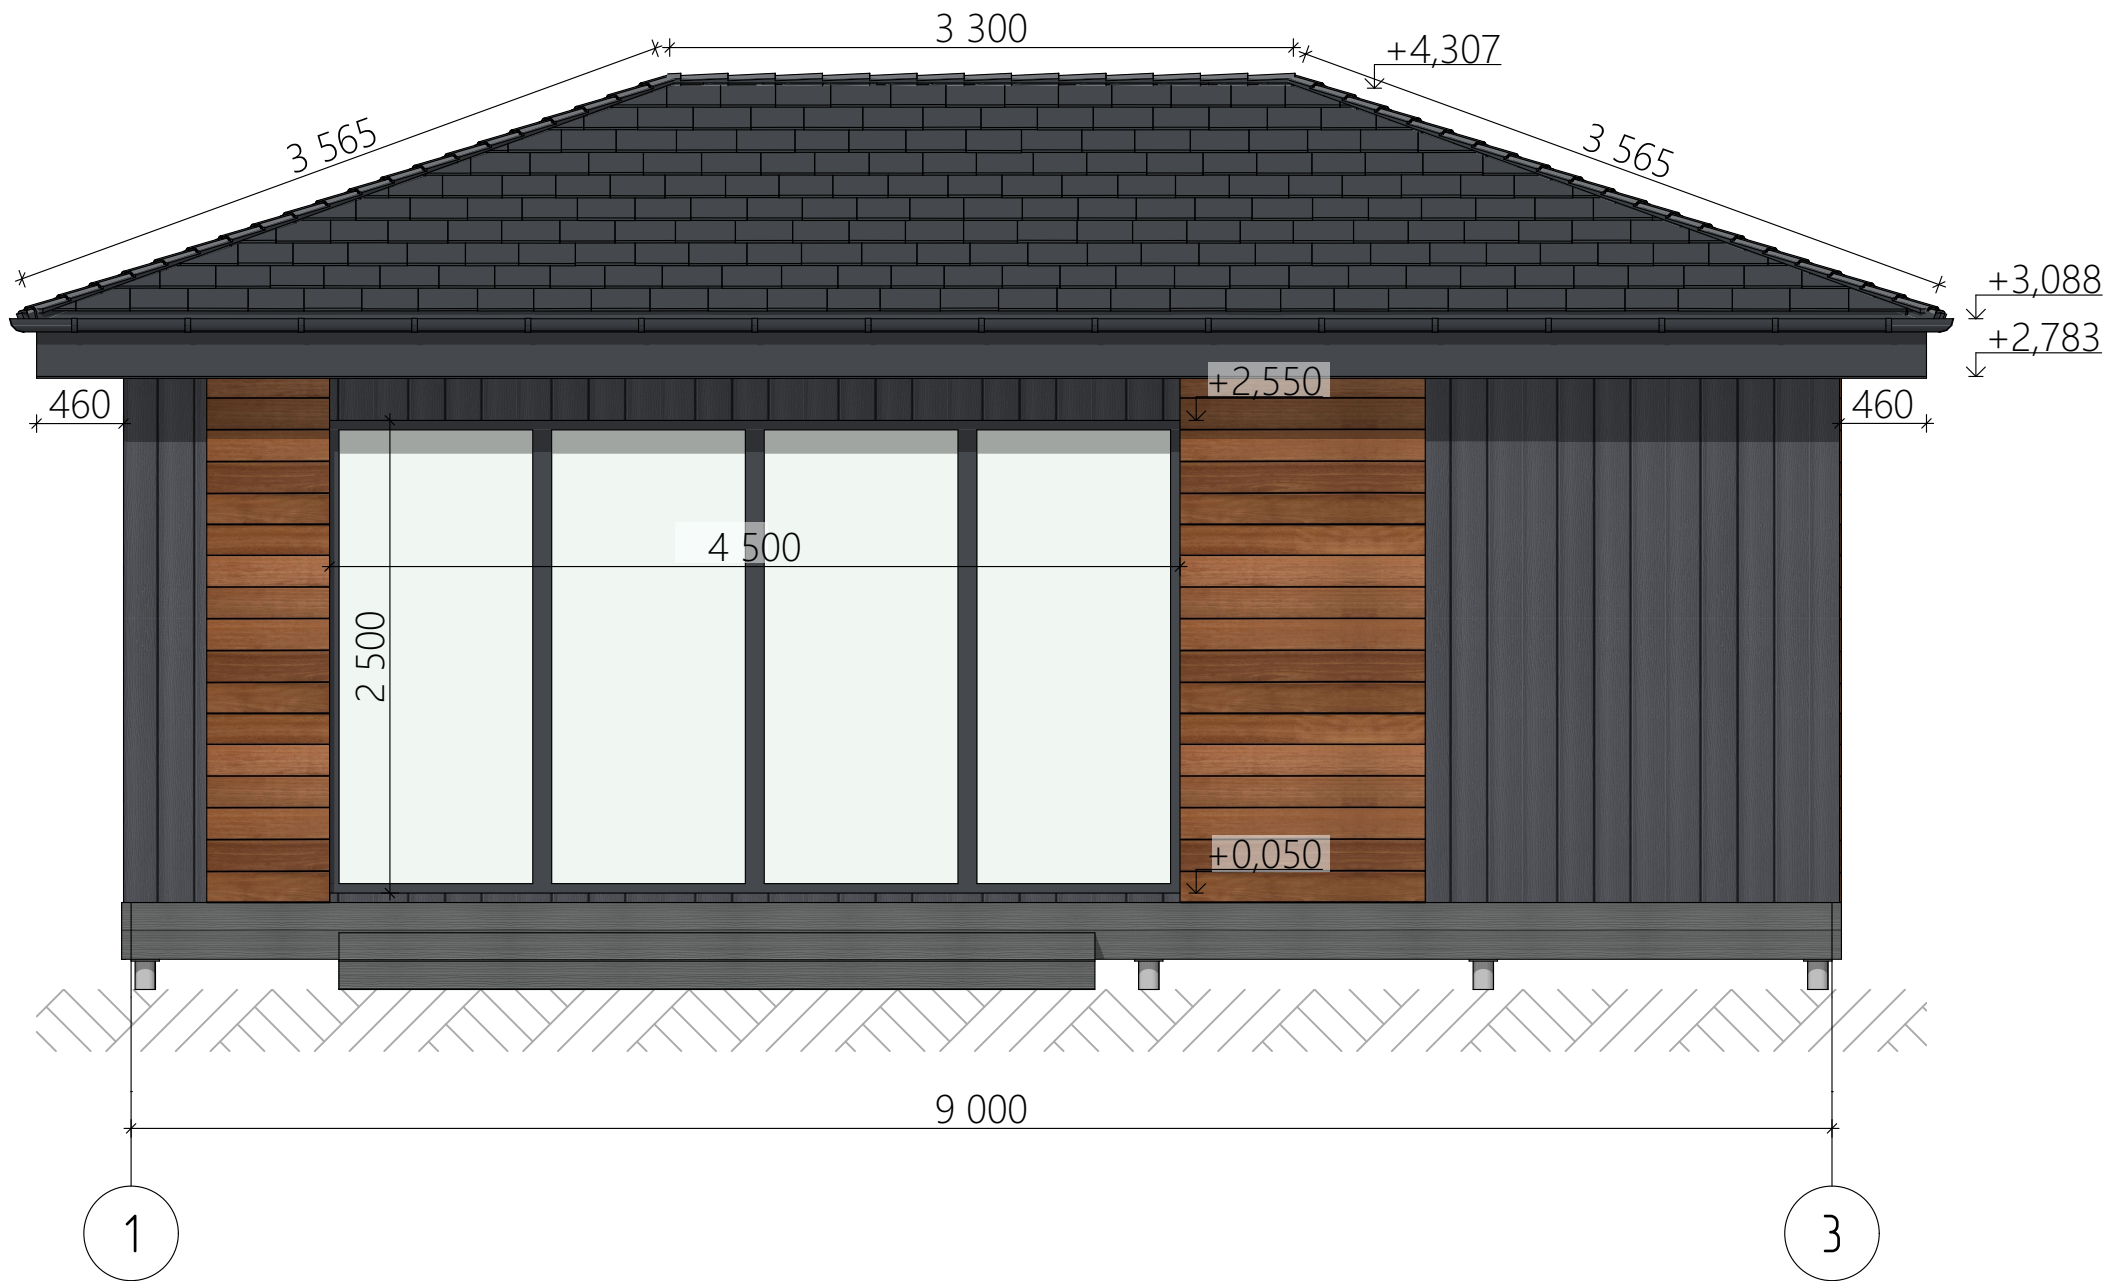

Согласовано				
И-в. № подл.	Взам. инв. №	Подп. и дата		

Лист	Изм.	№ Докум.	Подп.	Дата

МО, Мытищинский район, Новые Вешки, Зеленый бульвар 78

Фасад 1-3


#Название Организации

Фасад А-Б

1:40

Условные обозначения:

- Фиброцементный сайдинг (RAL 7024)
- Террасная доска (Экодек кантри серый)
- Водосточная система, металлочерепица лобовая рамы, наличники (RAL 7024)
- Планкен (цвет махагон)

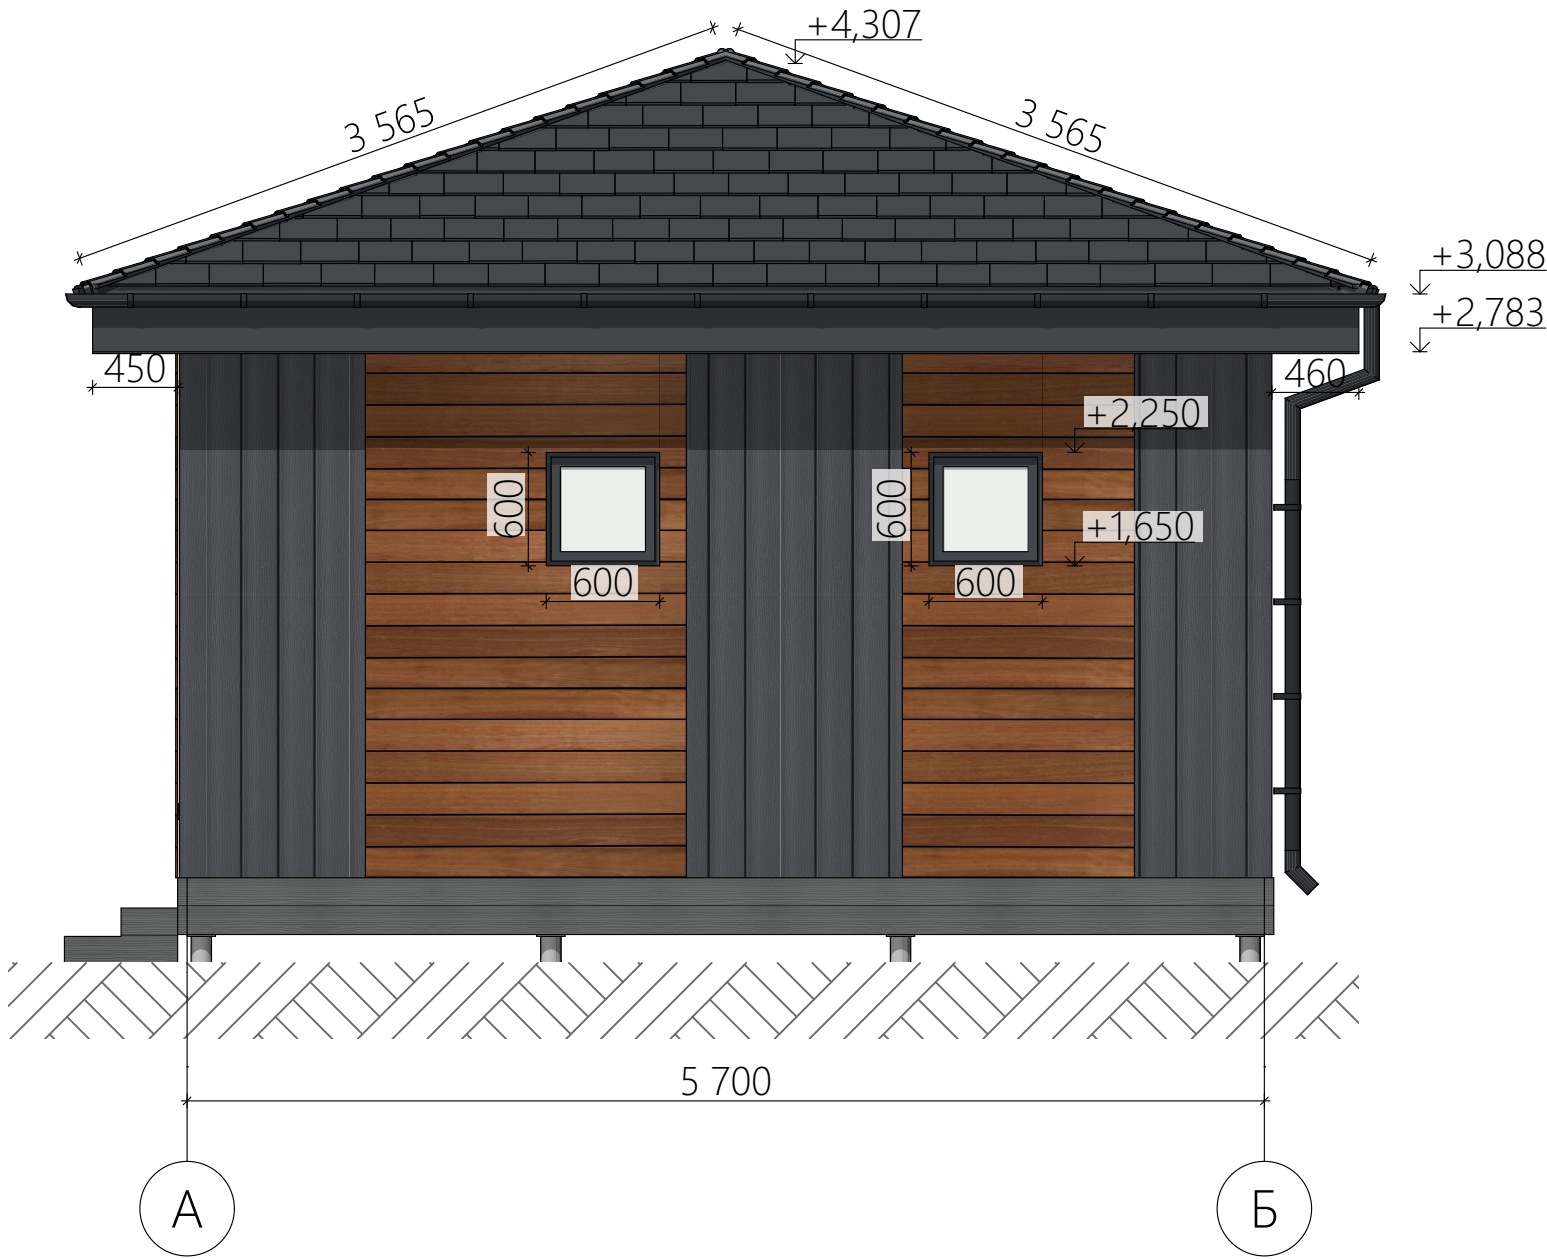

Согласовано					
И-нв. № подл.	Подп. и дата	Взам. инв. №			

Лист	Изм.	№ Докум.	Подп.	Дата

МО, Мытищинский район, Новые Вешки, Зеленый бульвар 78

Фасад А-Б


#Название Организации

Согласовано

Взам. инв. №

Подп. и дата

Инв. № подл.

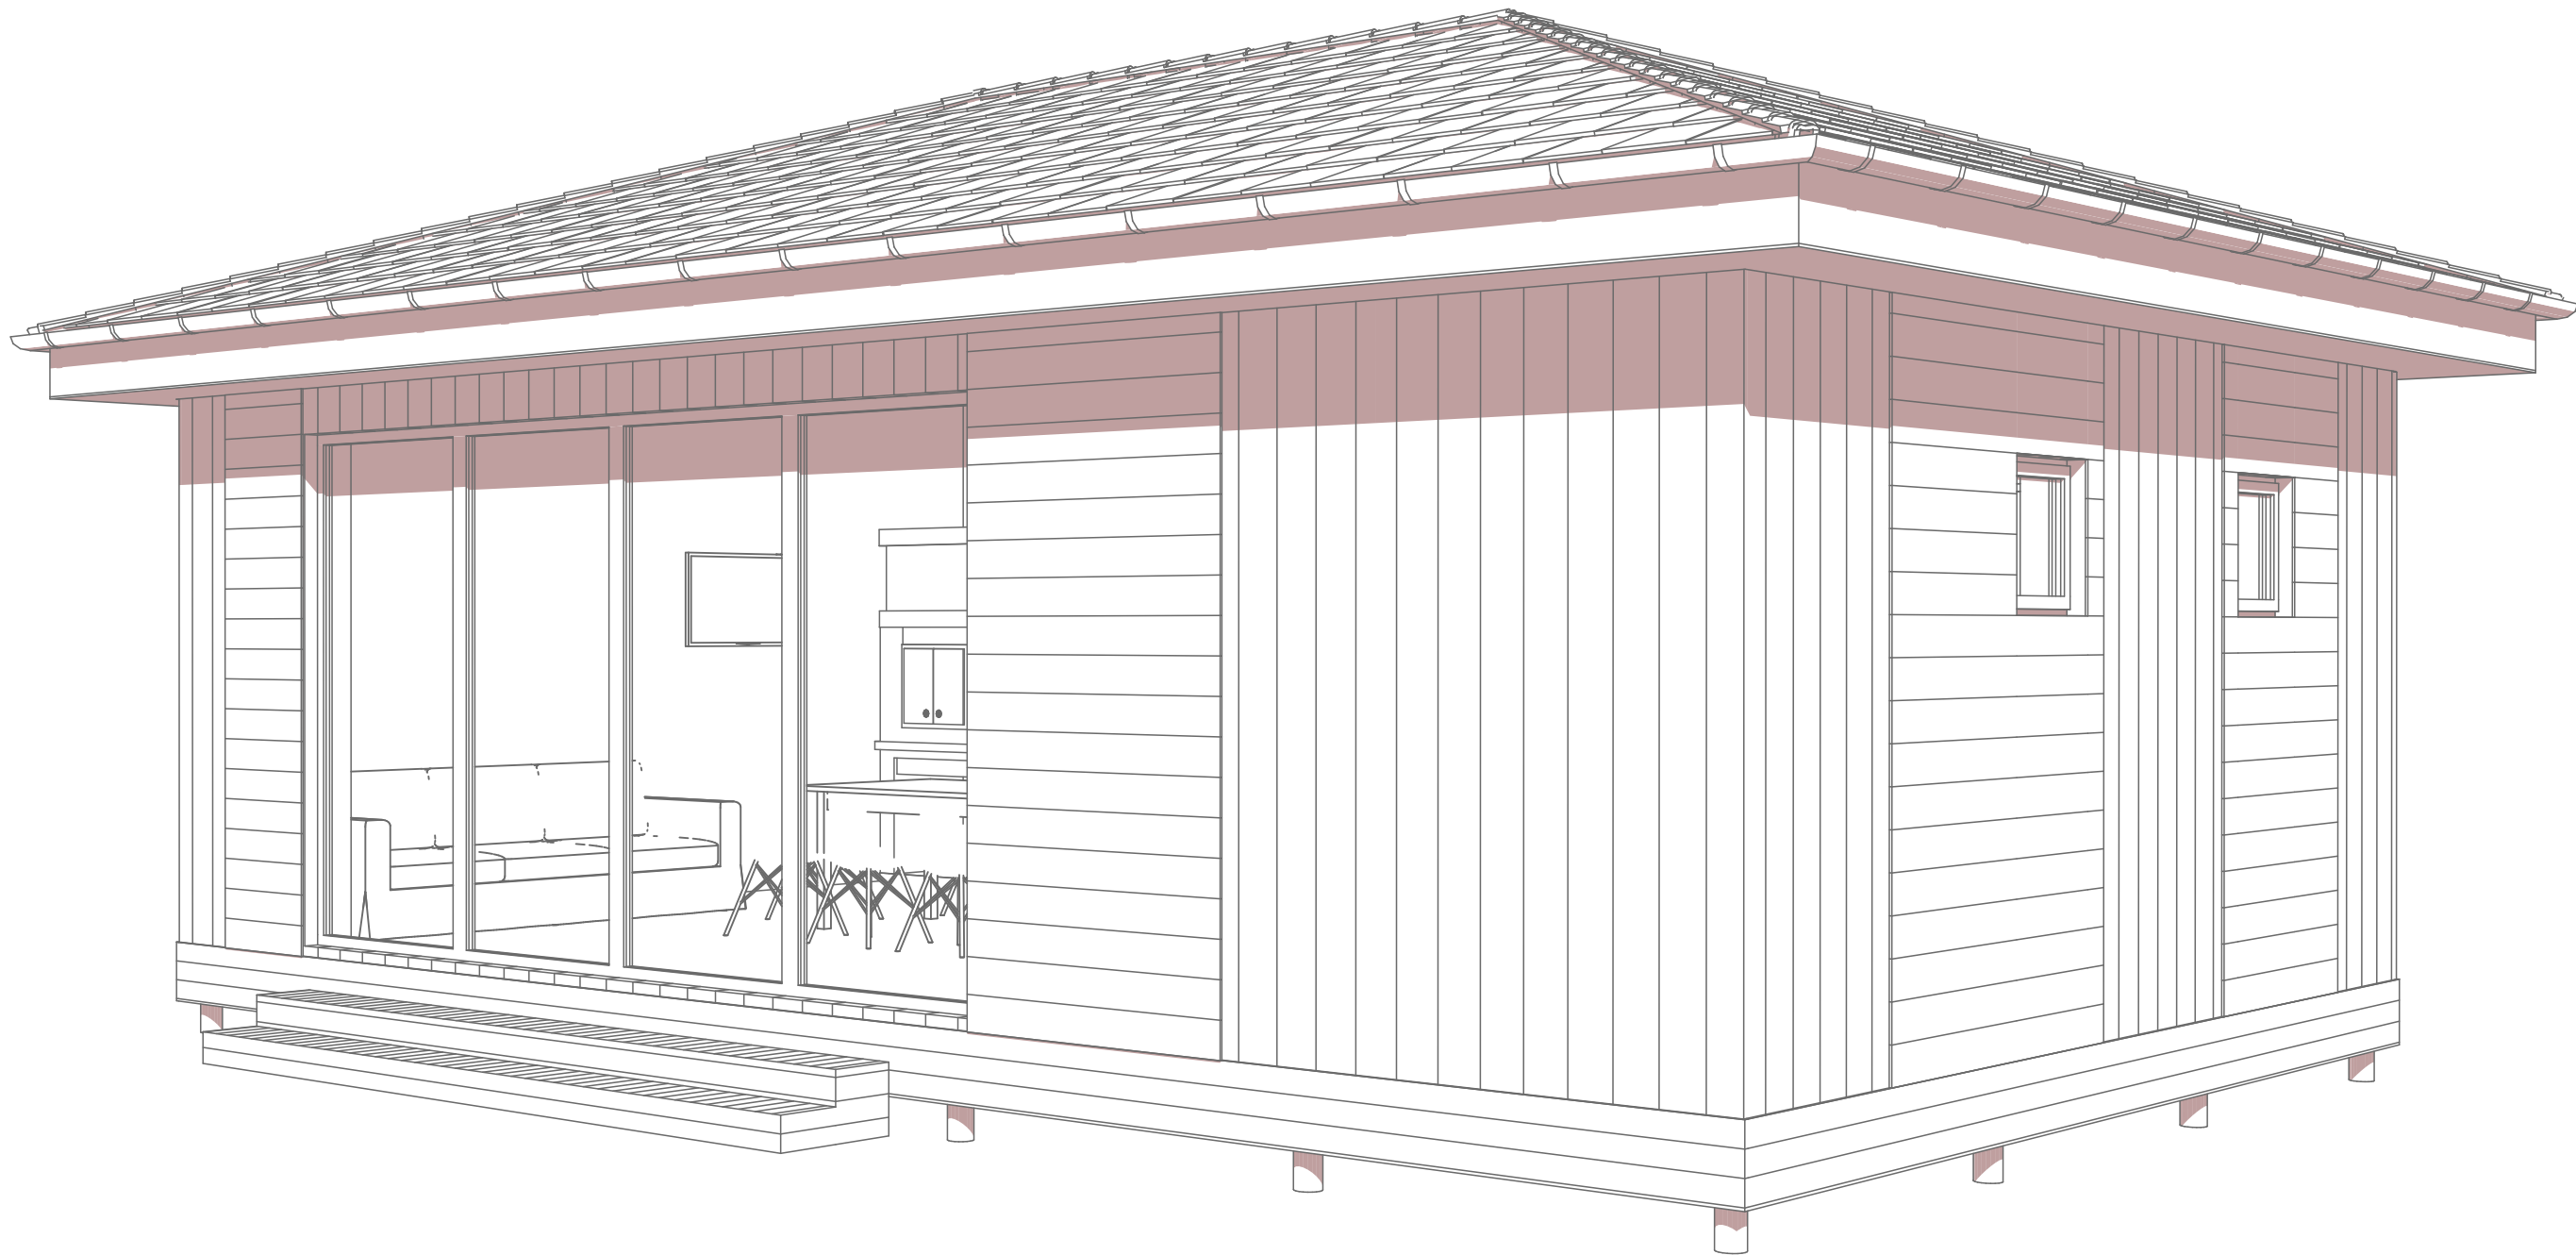

Лист	Изм.	№ Докум.	Подп.	Дата

МО, Мытищинский район, Новые Вешки, Зеленый бульвар 78

Аксонометрия №1


#Название Организации

Фасад Б-А

1:40

Условные обозначения:

- Фиброцементный сайдинг (RAL 7024)
- Террасная доска (Экодек кантри серый)
- Водосточная система, металлочерепица лобовая рамы, наличники (RAL 7024)
- Планкен (цвет махагон)

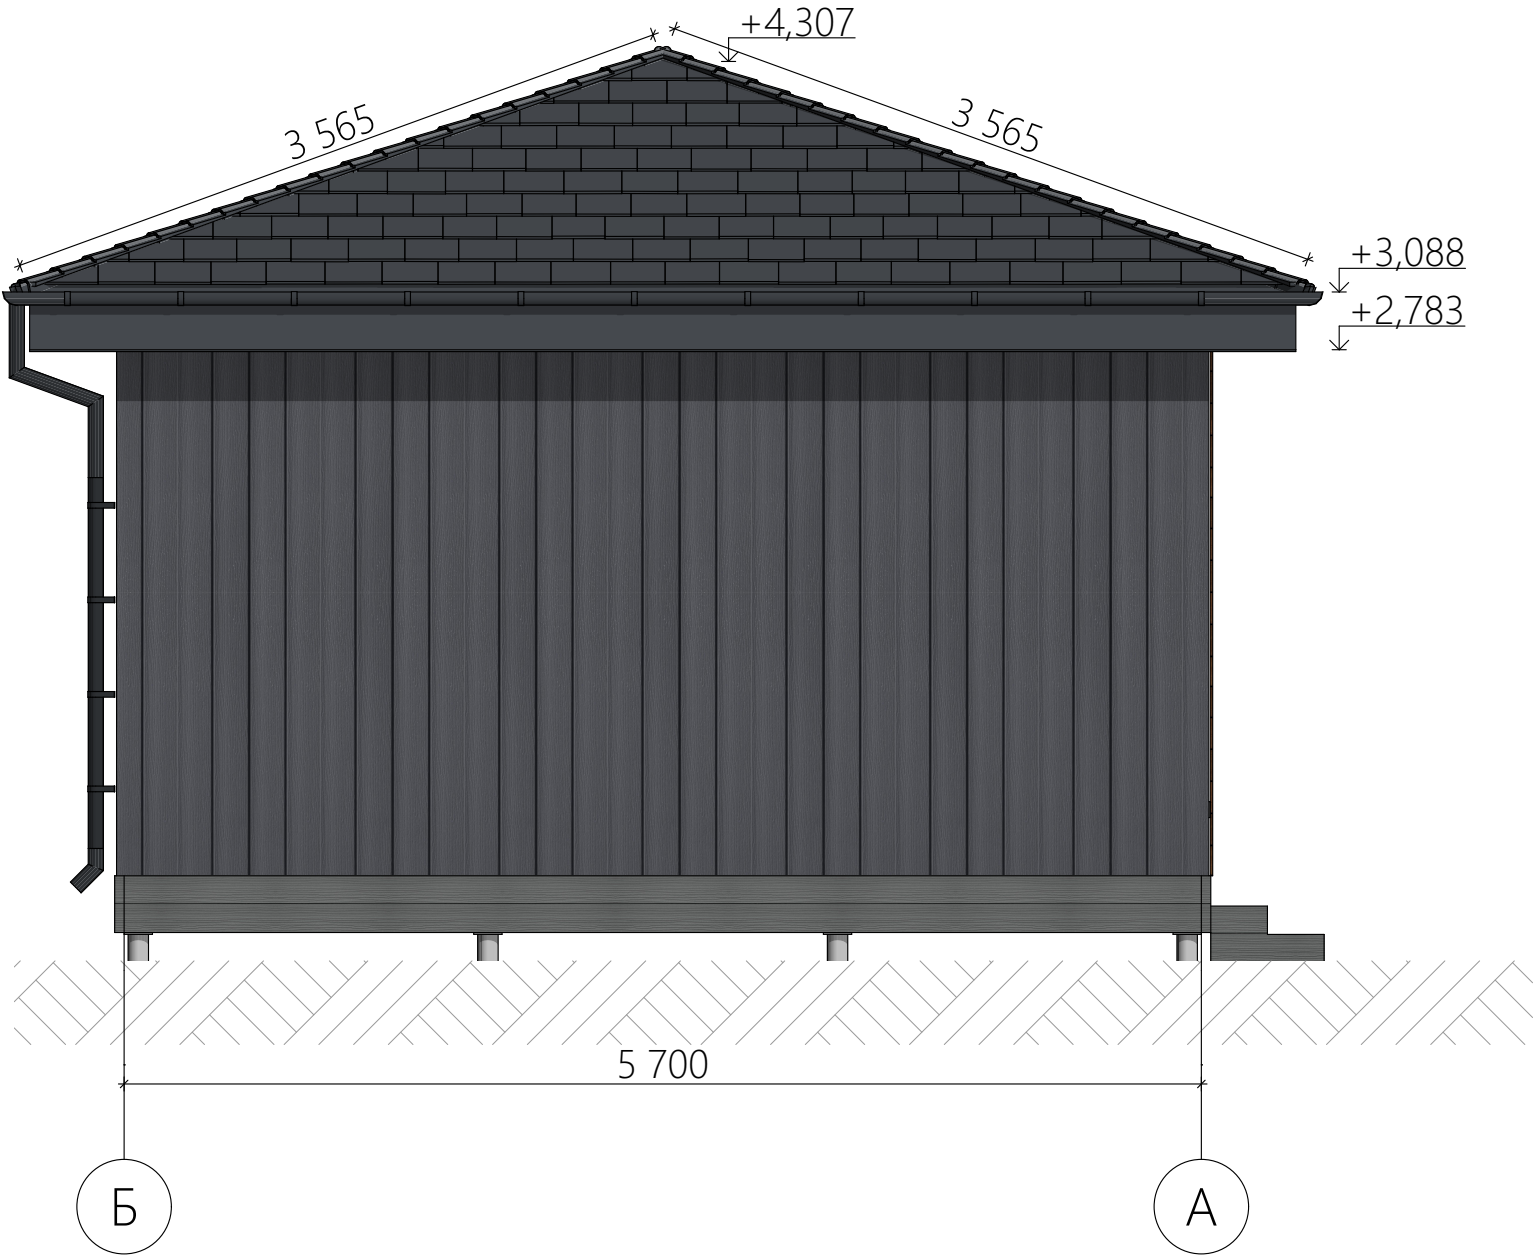

Согласовано					
Инва. № подл.	Подп. и дата	Взам. инв. №			

Лист	Изм.	№ Докум.	Подп.	Дата


МО, Мытищинский район, Новые Вешки, Зеленый бульвар 78

Фасад Б-А

#Название Организации

Фасад 3-1

1:40

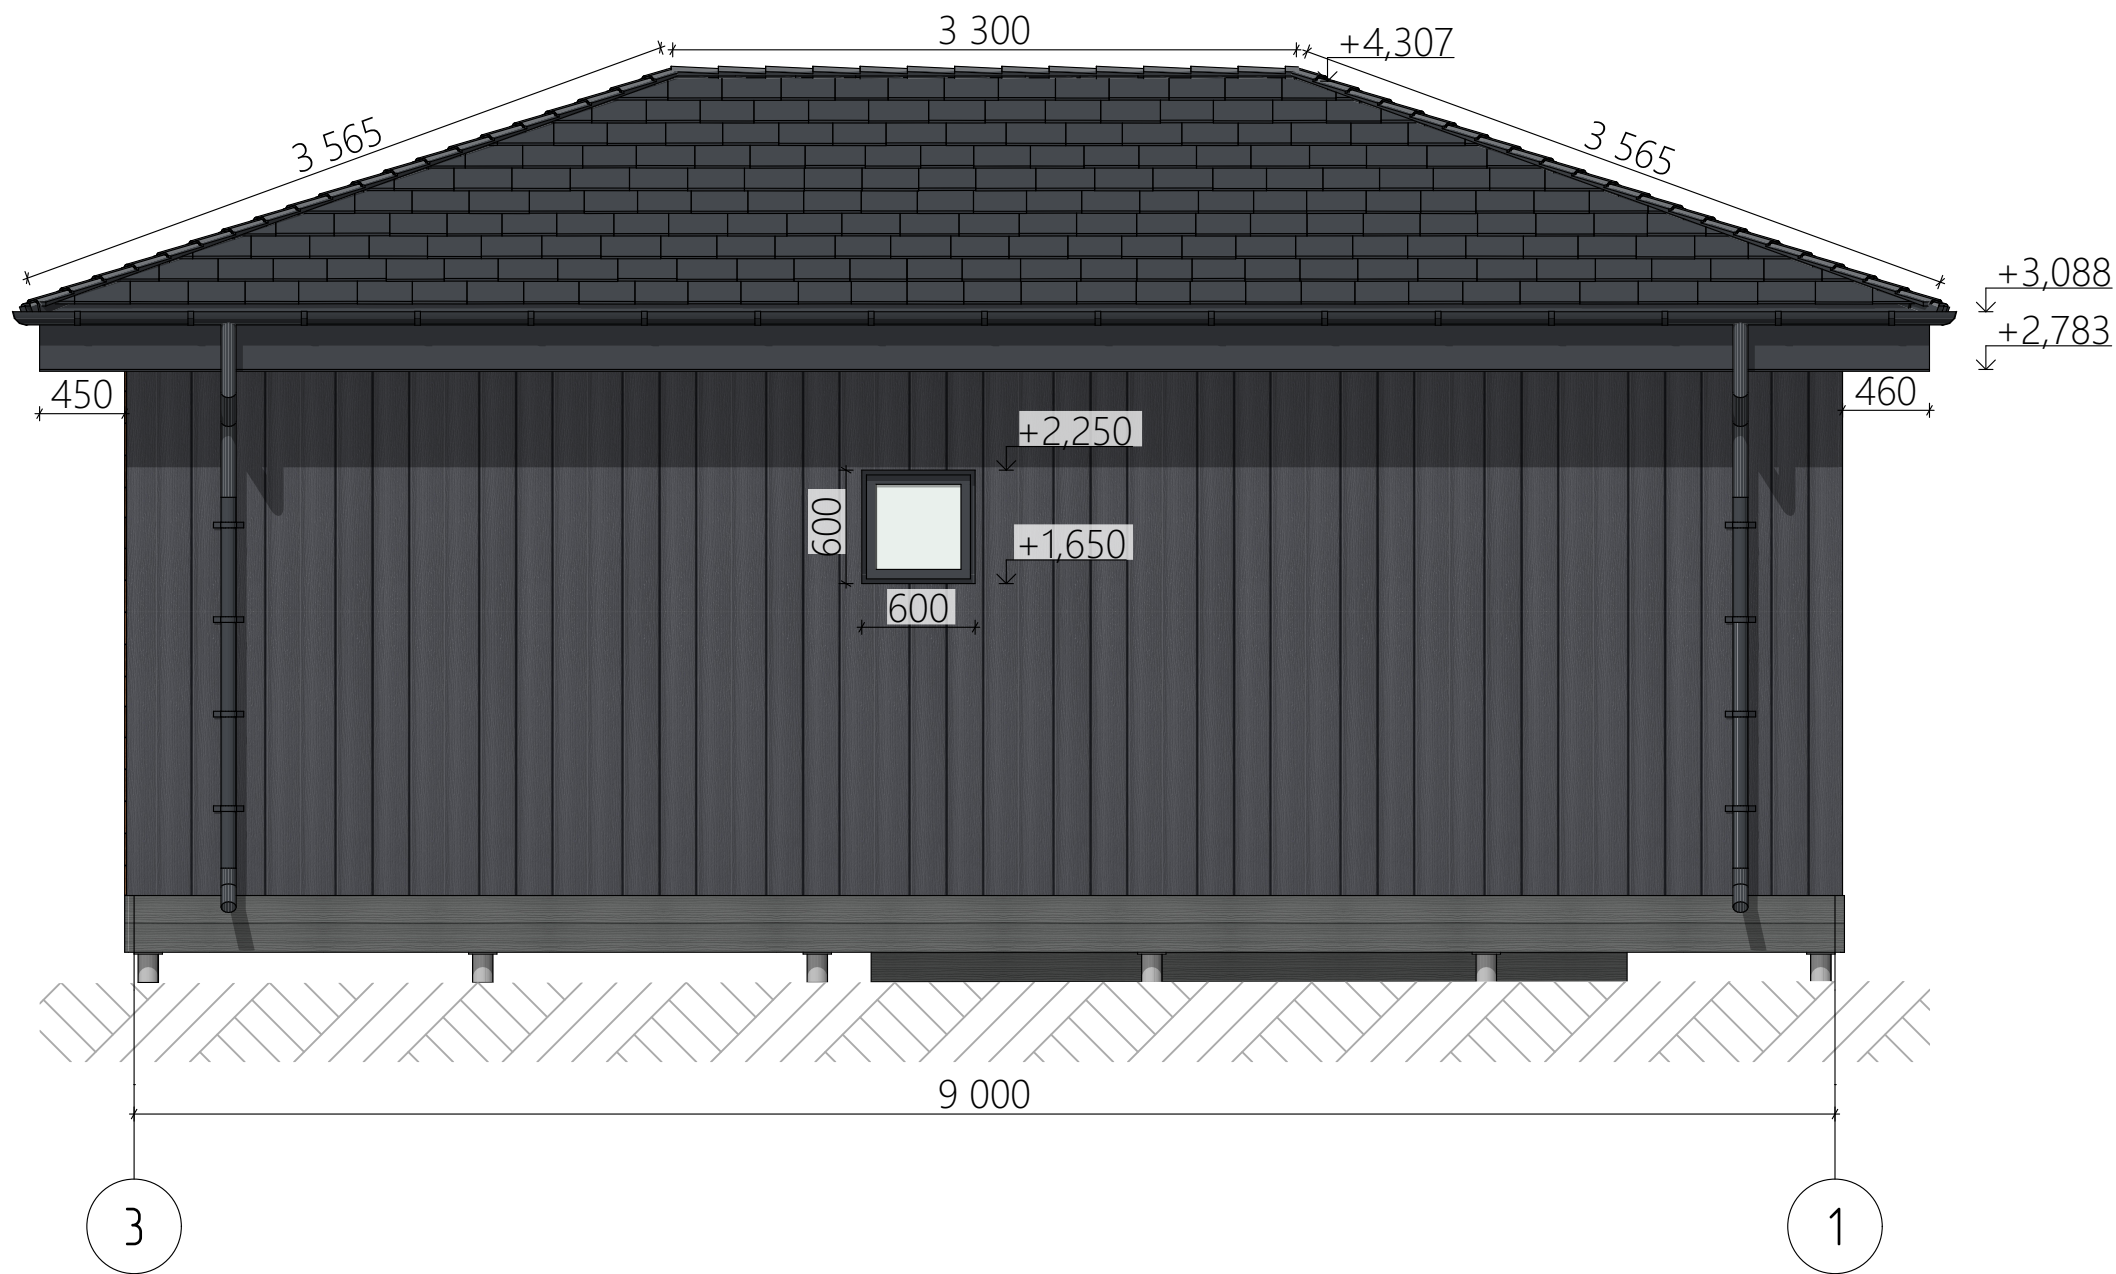

Условные обозначения:

- Фиброцементный сайдинг (RAL 7024)
- Террасная доска (Экодек кантри серый)
- Водосточная система, металлочерепица лобовая рамы, наличники (RAL 7024)
- Планкен (цвет махагон)

Согласовано

Взам. инв. №

Подп. и дата

Инв. № подл.

Лист	Изм.	№ Докум.	Подп.	Дата


МО, Мытищинский район, Новые Вешки, Зеленый бульвар 78

Фасад 3-1

#Название Организации

Согласовано			

Инва. № подл.	Подп. и дата		Взам. инв. №	

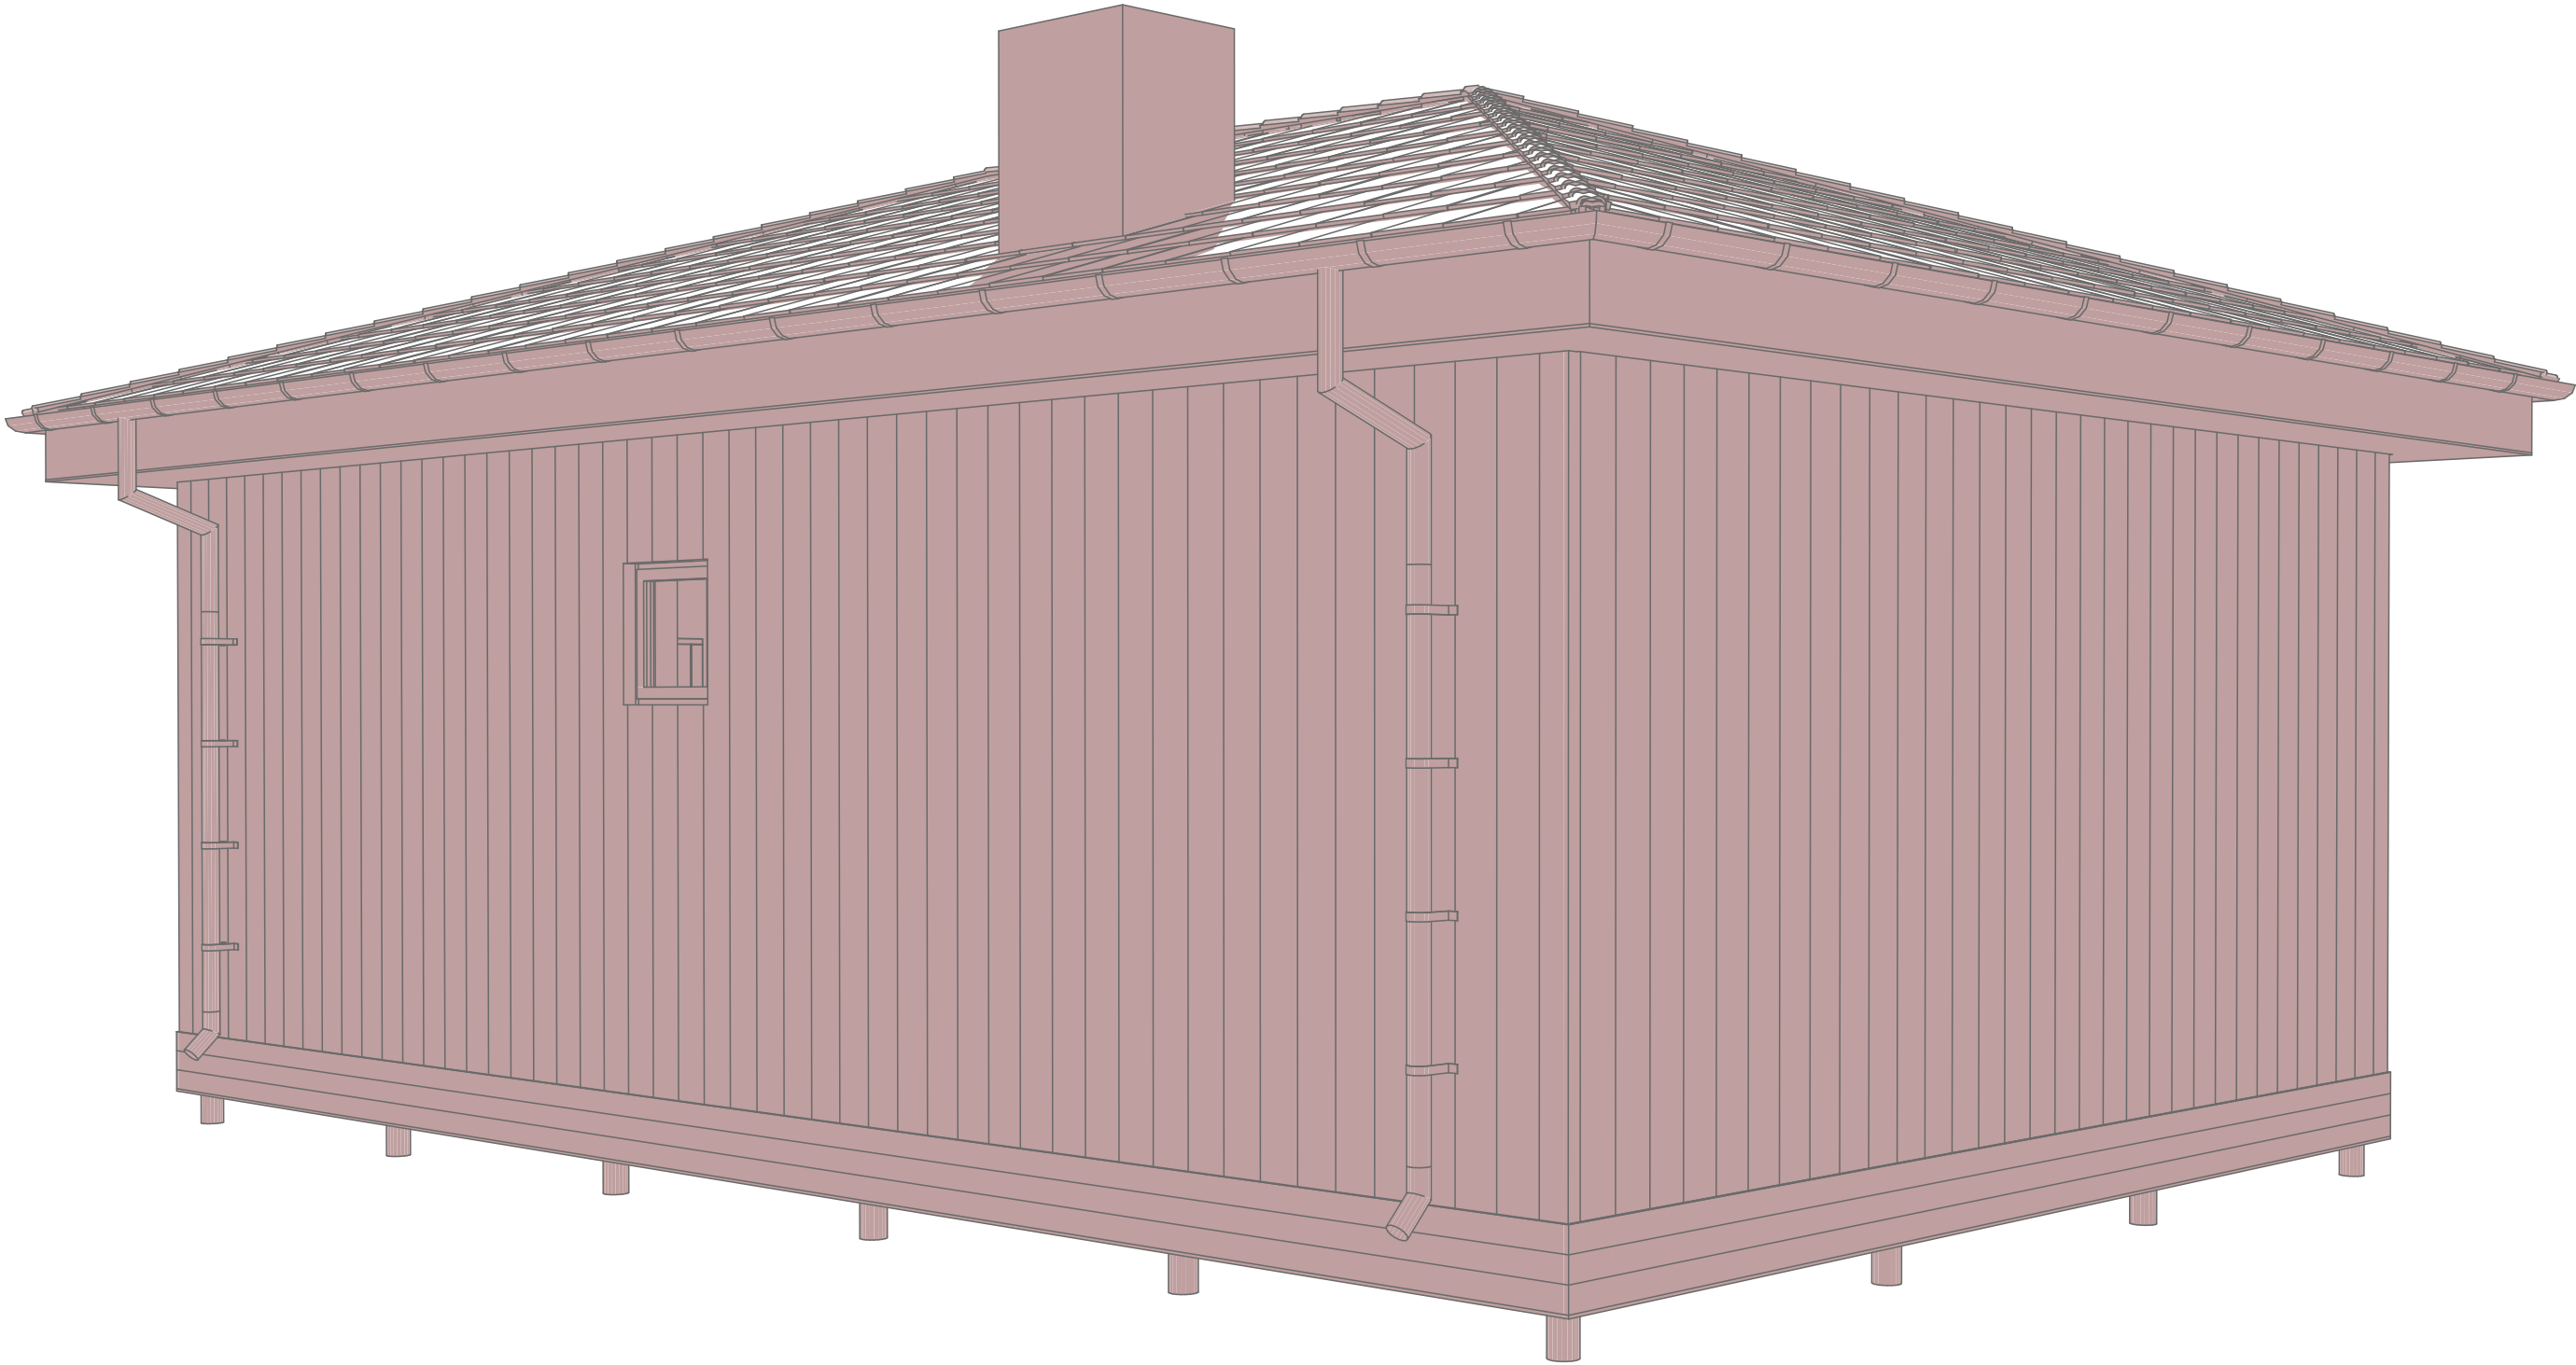

Лист	Изм.	№ Докум.	Подп.	Дата

МО, Мытищинский район, Новые Вешки, Зеленый бульвар 78

Аксонометрия №2

#Название Организации

Согласовано					
И-нв. № подл.	Подп. и дата		Взам. инв. №		



Лист	Изм.	№ Докум.	Подп.	Дата

МО, Мытищинский район, Новые Вешки, Зеленый бульвар 78

Визуализация

#Название Организации

Лист
26

Согласовано					
Инва. № подл.	Подп. и дата	Взам. инв. №			



Лист	Изм.	№ Докум.	Подп.	Дата

МО, Мытищинский район, Новые Вешки, Зеленый бульвар 78

Визуализация

#Название Организации

Лист
27

Согласовано				
И-чв. № подл.	Подп. и дата	Взам. и-чв. №		



Лист	Изм.	№ Докум.	Подп.	Дата

МО, Мытищинский район, Новые Вешки, Зеленый бульвар 78

Визуализация

#Название Организации

Лист
28

Согласовано					
Инва. № подл.	Подп. и дата	Взам. инв. №			



Лист	Изм.	№ Докум.	Подп.	Дата

МО, Мытищинский район, Новые Вешки, Зеленый бульвар 78

Визуализация

#Название Организации

Лист
29

Согласовано					
И-чв. № подл.	Подп. и дата	Взам. инв. №			



Лист	Изм.	№ Докум.	Подп.	Дата

МО, Мытищинский район, Новые Вешки, Зеленый бульвар 78

Визуализация

#Название Организации

Лист
30