


ARCHITECTURE/
CONSTRUCTION

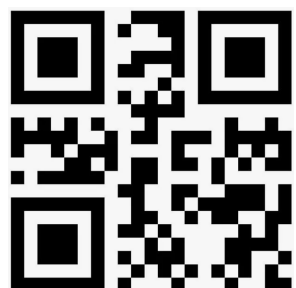

Название:
Разработал:
-
Принял:
-
г. Москва



Согласовано				
И.нв. № подл.	Подп. и дата	Взам. инв. №		

Лист	Наименование	Примечание
1	Титульный	
2	Ведомость чертежей	
3	Пояснительная записка	
4	СПОЗУ	
5	Маркировочный план	
6	Размерный план	
7	План расстановки оборудования и мебели	
8	Зд-разре	
9	План покрытия пола	
10	Пироги пола	
11	План покрытия стен	
12	Пироги стен	
13	План размещения розеток	
14	План размещения светильников и выключателей	
15	План крыши	
16	Ведомость оконных проемов	
17	Ведомость дверных проемов	
18	Разрез 1-1	
19	Разрез 2-2	
20	Разрез 3-3	
21	Фасад 1-5	
22	Фасад Д-А	
23	Фасад 5-1	
24	Фасад А-Д	
25	Визуализация	
26	Визуализация	
27	Визуализация	
28	Визуализация	
29	Визуализация	
30	Визуализация	

В основу архитектурно-планировочных решений положены требования технологических заданий и требования норм и правил строительного проектирования, действующих на территории РФ.

Основные параметры и требования разработаны на основании пожеланий и требований заказчика.

Архитектурные решения приняты в соответствии со следующими нормативными документами:

- Градостроительный кодекс российской федерации.
- Земельного Кодекса Российской Федерации.
- Федеральный закон от 22.07.2008 N 123 - ФЗ (ред. от 29.07.2017)"Технический регламент о требованиях пожарной безопасности.
- Федеральный закон № 384 - ФЗ «Технический регламент о безопасности зданий и сооружений».
- ГОСТ Р 21.1101-2013.«Основные требования к проектной и рабочей документации».
- Постановление правительства РФ от 16.02.2008 № 87 «Положение о составе разделов проектной документации и требованиях к их содержанию».
- СП 42.13330.2011 «Градостроительство. Планировка и застройка городских и сельских поселений».
- СП 131.13330.2018 «СНиП 23-01-99* Строительная климатология».
- СП 20.13330.2016 «СНиП 2.01.07-85* Нагрузки и воздействия».
- СП 22.13330.2016 «СНиП 2.02.01-83* Основания зданий и сооружений».
- СП 70.13330.2012 (с изменениями №1) «СНиП 3.03.01-87 Несущие и ограждающие конструкции».
- СП 64.13330.2017 «СНиП II-25-80 Деревянные конструкции».
- СП 17.13330.2017 «СНиП II-26-76 Кровли».
- СП 29.13330.2011 «СНиП 2.03.13-88 Полы».
- СП 28.13330.2017 «СНиП 2.03.11-85 Защита строительных конструкций от коррозии».
- СП 50.13330.2012 «СНиП 23-02-2003 Тепловая защита зданий».

Согласовано				
И-нв. № подл.	Подп. и дата	Взам. инв. №		

1. Общие данные:

1.1. Архитектурный проект разработан на основании требований и пожеланий заказчика.

Тип строения	Баня
Относительная отм. ±0.000	ур. верха лаг перекрытия
Общая площадь застройки, м2	108,00
Габаритные размеры каркаса здания	12х9м
Этажность	1 этаж
Конструктивная схема	Деревянный каркас

2. Конструктивные решения:

2.1. Рабочие чертежи разработаны на основании задания на проектирование

Полезная нагрузка на перекрытие	150 кгс/м2	-
Нормативная глубина промерзания	1,2м	СП 22.13330.2016 СП 131.13330.2020
Нормативное ветровое давление	I район (23кгс/м2)	СП 22.13330.2016
Нормативный вес снегового покрова	III район (150кгс/м2)	СП 22.13330.2016
Температура наиболее холодной пятидневки	-29°С	СП 131.13330.2020

2.2. Конструктивное строение представляет собой сооружение:

- на свайном фундаменте
- несущими стенами из деревянного каркаса
- односкатной кровлей по деревянным стропилам

2.3. Необходимо осуществлять технический надзор за производством строительных работ. Данные по проведённым работам необходимо систематически вносить в журнал работ.

По каждому из этапов работ необходимо осуществлять входной контроль материалов и вести приёмку.

Фундамент	сваи винтовые d=108мм
Несущие конструкции	деревянный каркас (140х45мм)
Стропильная система	строганая доска (190х45мм)
Тип крыши	односкатная
Покрытие кровли	фальцевые листы

2.4. Все деревянные конструкции обработать огне-биозащитными септиками в соответствии со СП 28.13330.2017 "Защита строительных конструкций от коррозии".

2.5. Кровельные работы выполнять в соответствии с требованиями фирмы производителя.


2.6. Все работы вести в строгом соответствии с требованиями СНиП 12.03.2001 "Безопасность труда в строительстве".

2.7. При выполнении всех работ строго соблюдать меры противопожарной безопасности.

2.8. Возможна замена материалов аналогами.



*Решения, принятые в проекте и отображенные в чертежах, соответствуют требованиям экологических, санитарно - гигиенических, противопожарных и других норм, действующих на территории Российской Федерации, и обеспечивают безопасную для жизни и здоровья людей эксплуатацию объекта при соблюдении предусмотренных рабочих чертежей и мероприятий.

Условные обозначения:

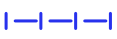-  - Граница участка
-  - Граница застройки участка
-  - Существующий индивидуальный жилой дом
-  - Банный комплекс (проектируемая постройка)

Технико-экономические показатели

Наименование	Площадь, м²
Площадь участка (по кадастровой документации)	2363,00
Общая площадь застройки (баня+ИЖД)	345,00
Площадь участка (по топографической съемке)	-
Площадь застройки (баня)	107,00
Площадь застройки (ИЖД)	237,00

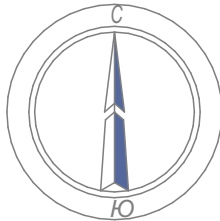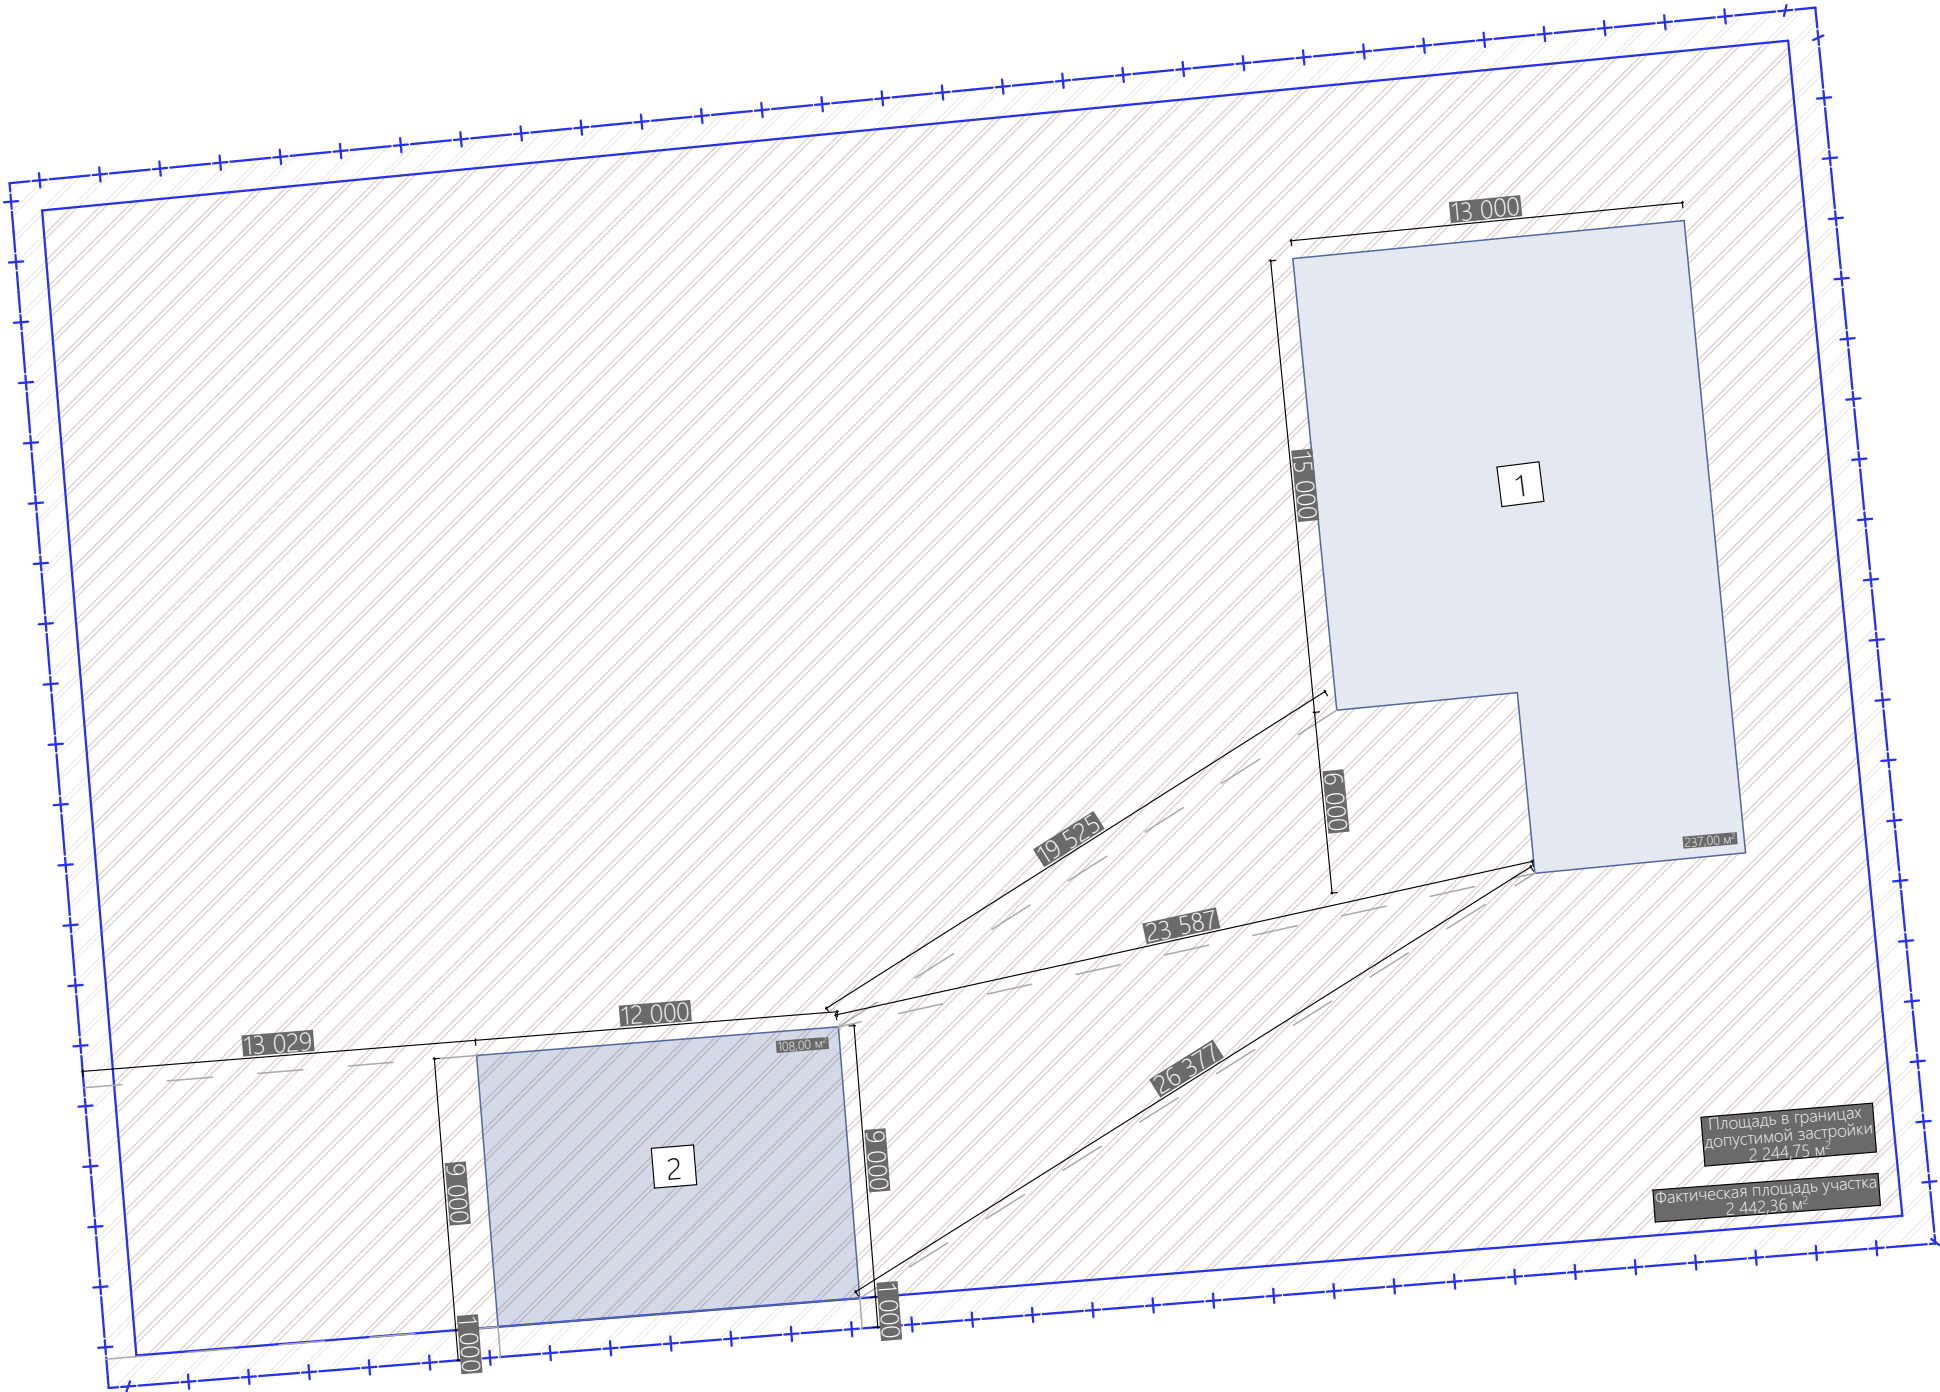

Согласовано				
И.нв. № подл.	Взам. инв. №	Подп. и дата		

Лист	Изм.	№ Докум.	Подп.	Дата

Московская область, Одинцовский городской округ, село Каринское,		50:20:0080803:1001	СПОЗУ	#Название Организации	Лист
					4

Маркировочный план

1:60



Экспликация помещений

№	Наименование	Площадь, кв.м.
1	Парная	7,94
2	Душевая	5,90
3	С/у	2,32
4	Прачечная	2,34
5	Тамбур	3,49
6	Холл	8,72
7	Спальня	10,20
8	Комната отдыха	15,97
9	Тамбур 1	11,85
10	Тамбур 2	26,78
		95,51 м²

Наименование	Площадь, кв.м.
Площадь застройки	108,00

Примечание:

1. Вся индивидуальная мебель выполняется по отдельному проекту с детальной проработкой и калькуляцией. Чертежи предоставляет фирма-изготовитель столярных изделий.
2. Данный проект отдельно согласовывается с автором проекта и непосредственно с заказчиком.
3. Цветовое решение фасада и материалов отделки показаны в проекте приблизительно.
4. Количество ступеней показано условно.

Согласовано

Взам. инв. №

Подп. и дата

Инв. № подл.

Лист	Изм.	№ Докум.	Подп.	Дата


Московская область, Одинцовский городской округ, село Каринское, 50:20:0080803:1001

Маркировочный план

#Название Организации

Размерный план

1:60

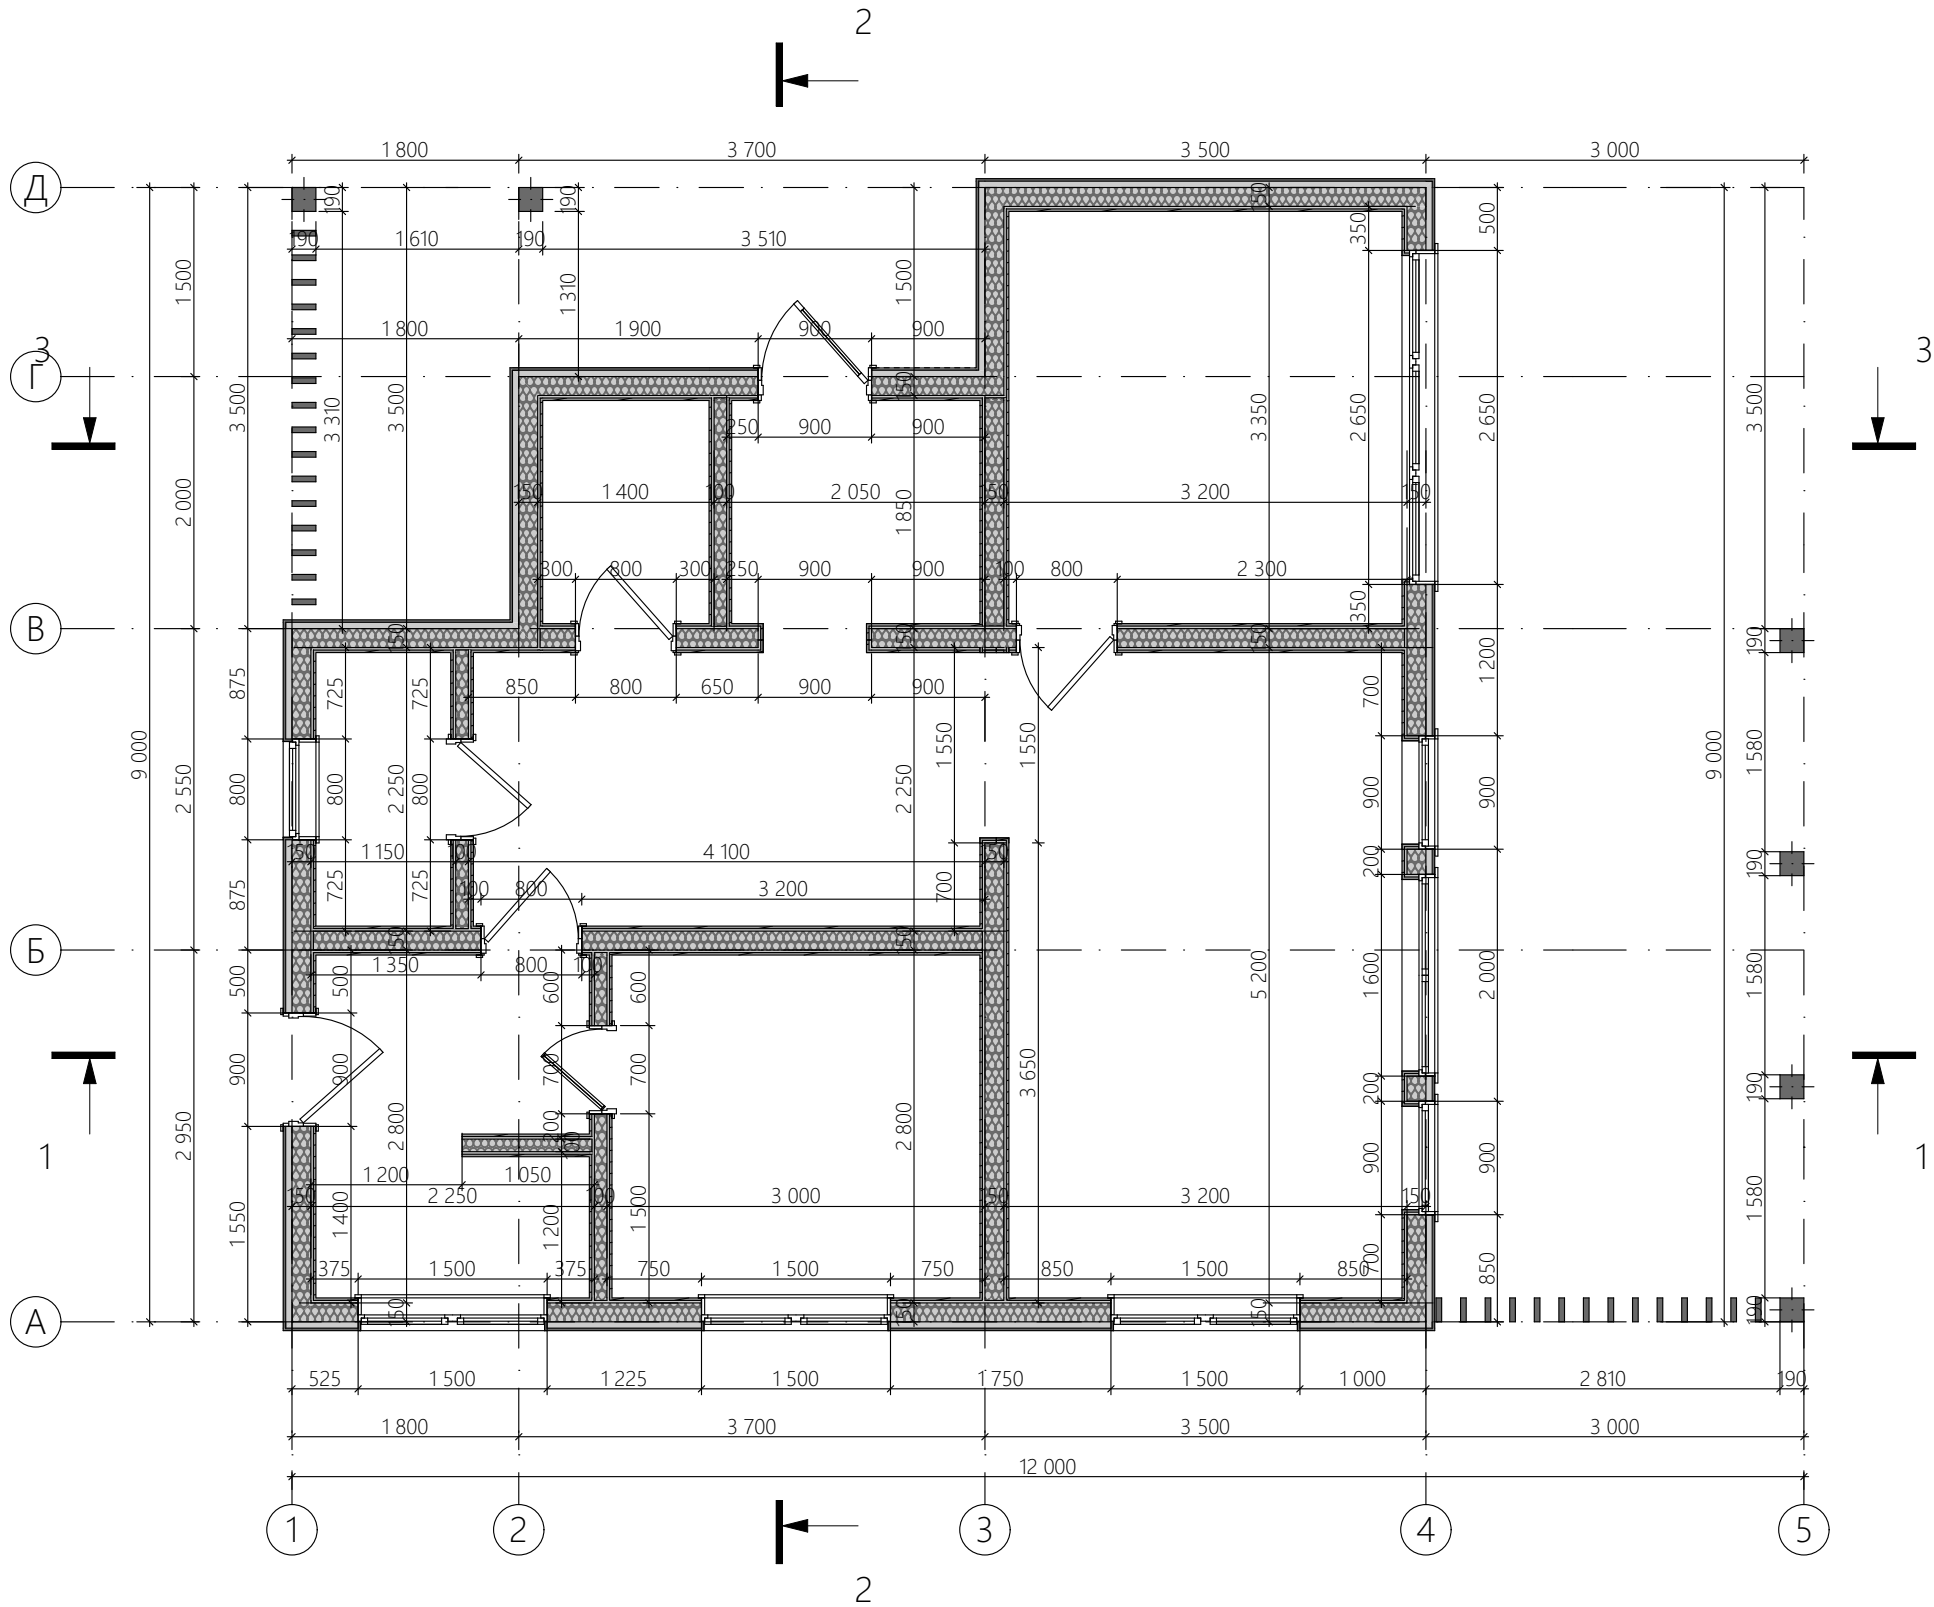

Примечание:
1. Представленные размеры указаны без учета внешней и внутренней отделки


Согласовано				
И-в. № подл.	Подп. и дата	Взам. инв. №		

Лист	Изм.	№ Докум.	Подп.	Дата

Московская область, Одинцовский городской округ, село Каринское,		50:20:0080803:1001	Размерный план	#Название Организации	Лист
					6

План расстановки мебели и оборудования

1:60

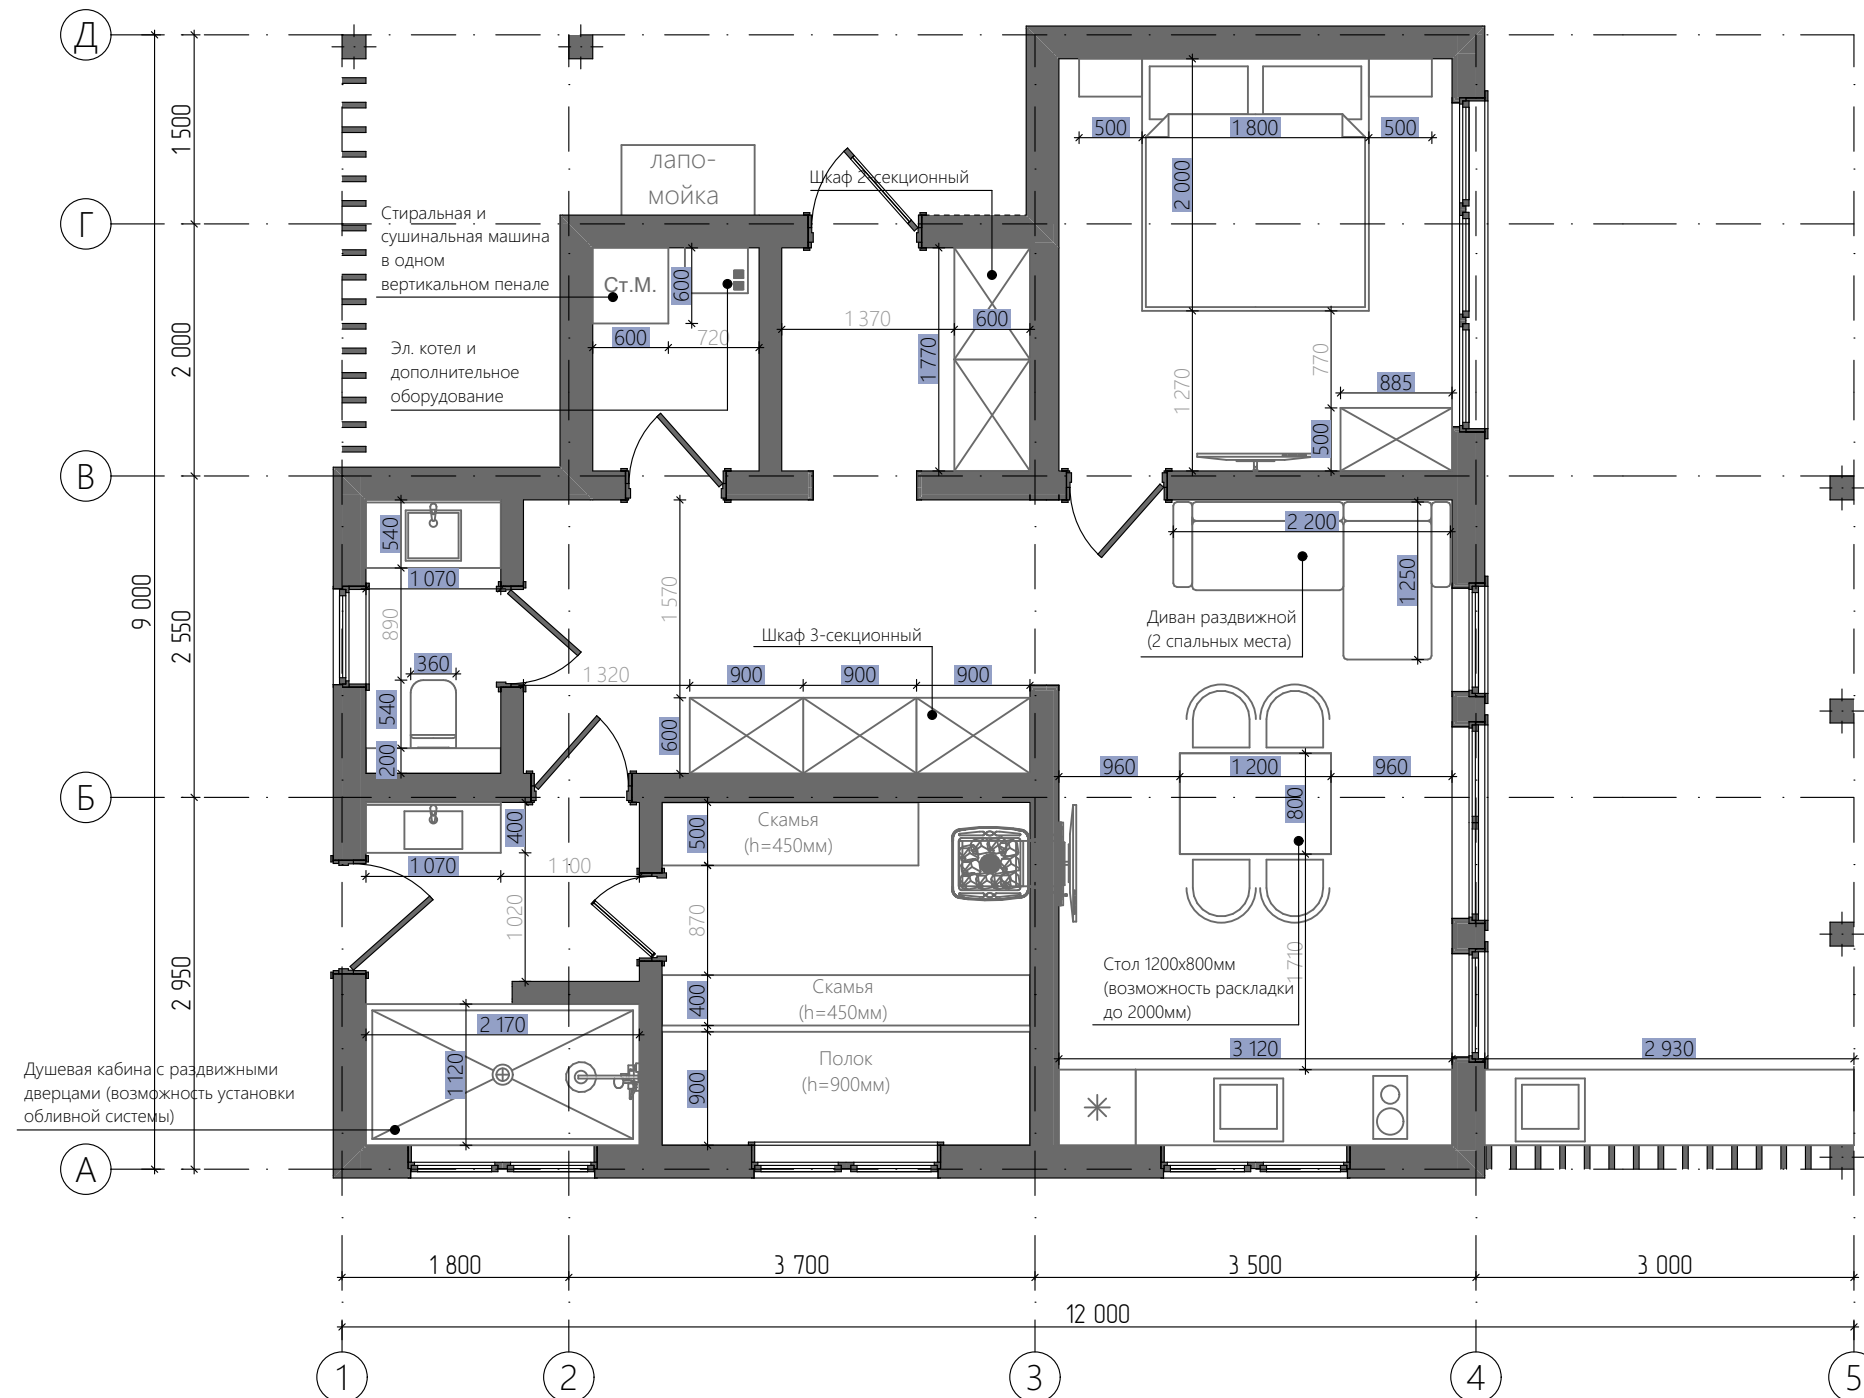

Примечание:

1. Вся индивидуальная мебель выполняется по отдельному проекту с детальной проработкой и калькуляцией. Чертежи предоставляет фирма-изготовитель столярных изделий.
2. Финальные размеры мебели и оборудования указаны ориентировочно — для точной компоновки требуется разработка дизайн-проекта.

Согласовано

Взам. инв. №

Подп. и дата

Инв. № подл.


Лист	Изм.	№ Докум.	Подп.	Дата

Московская область, Одинцовский городской округ, село Каринское,

50:20:0080803:1001

План расстановки оборудования и мебели

#Название Организации

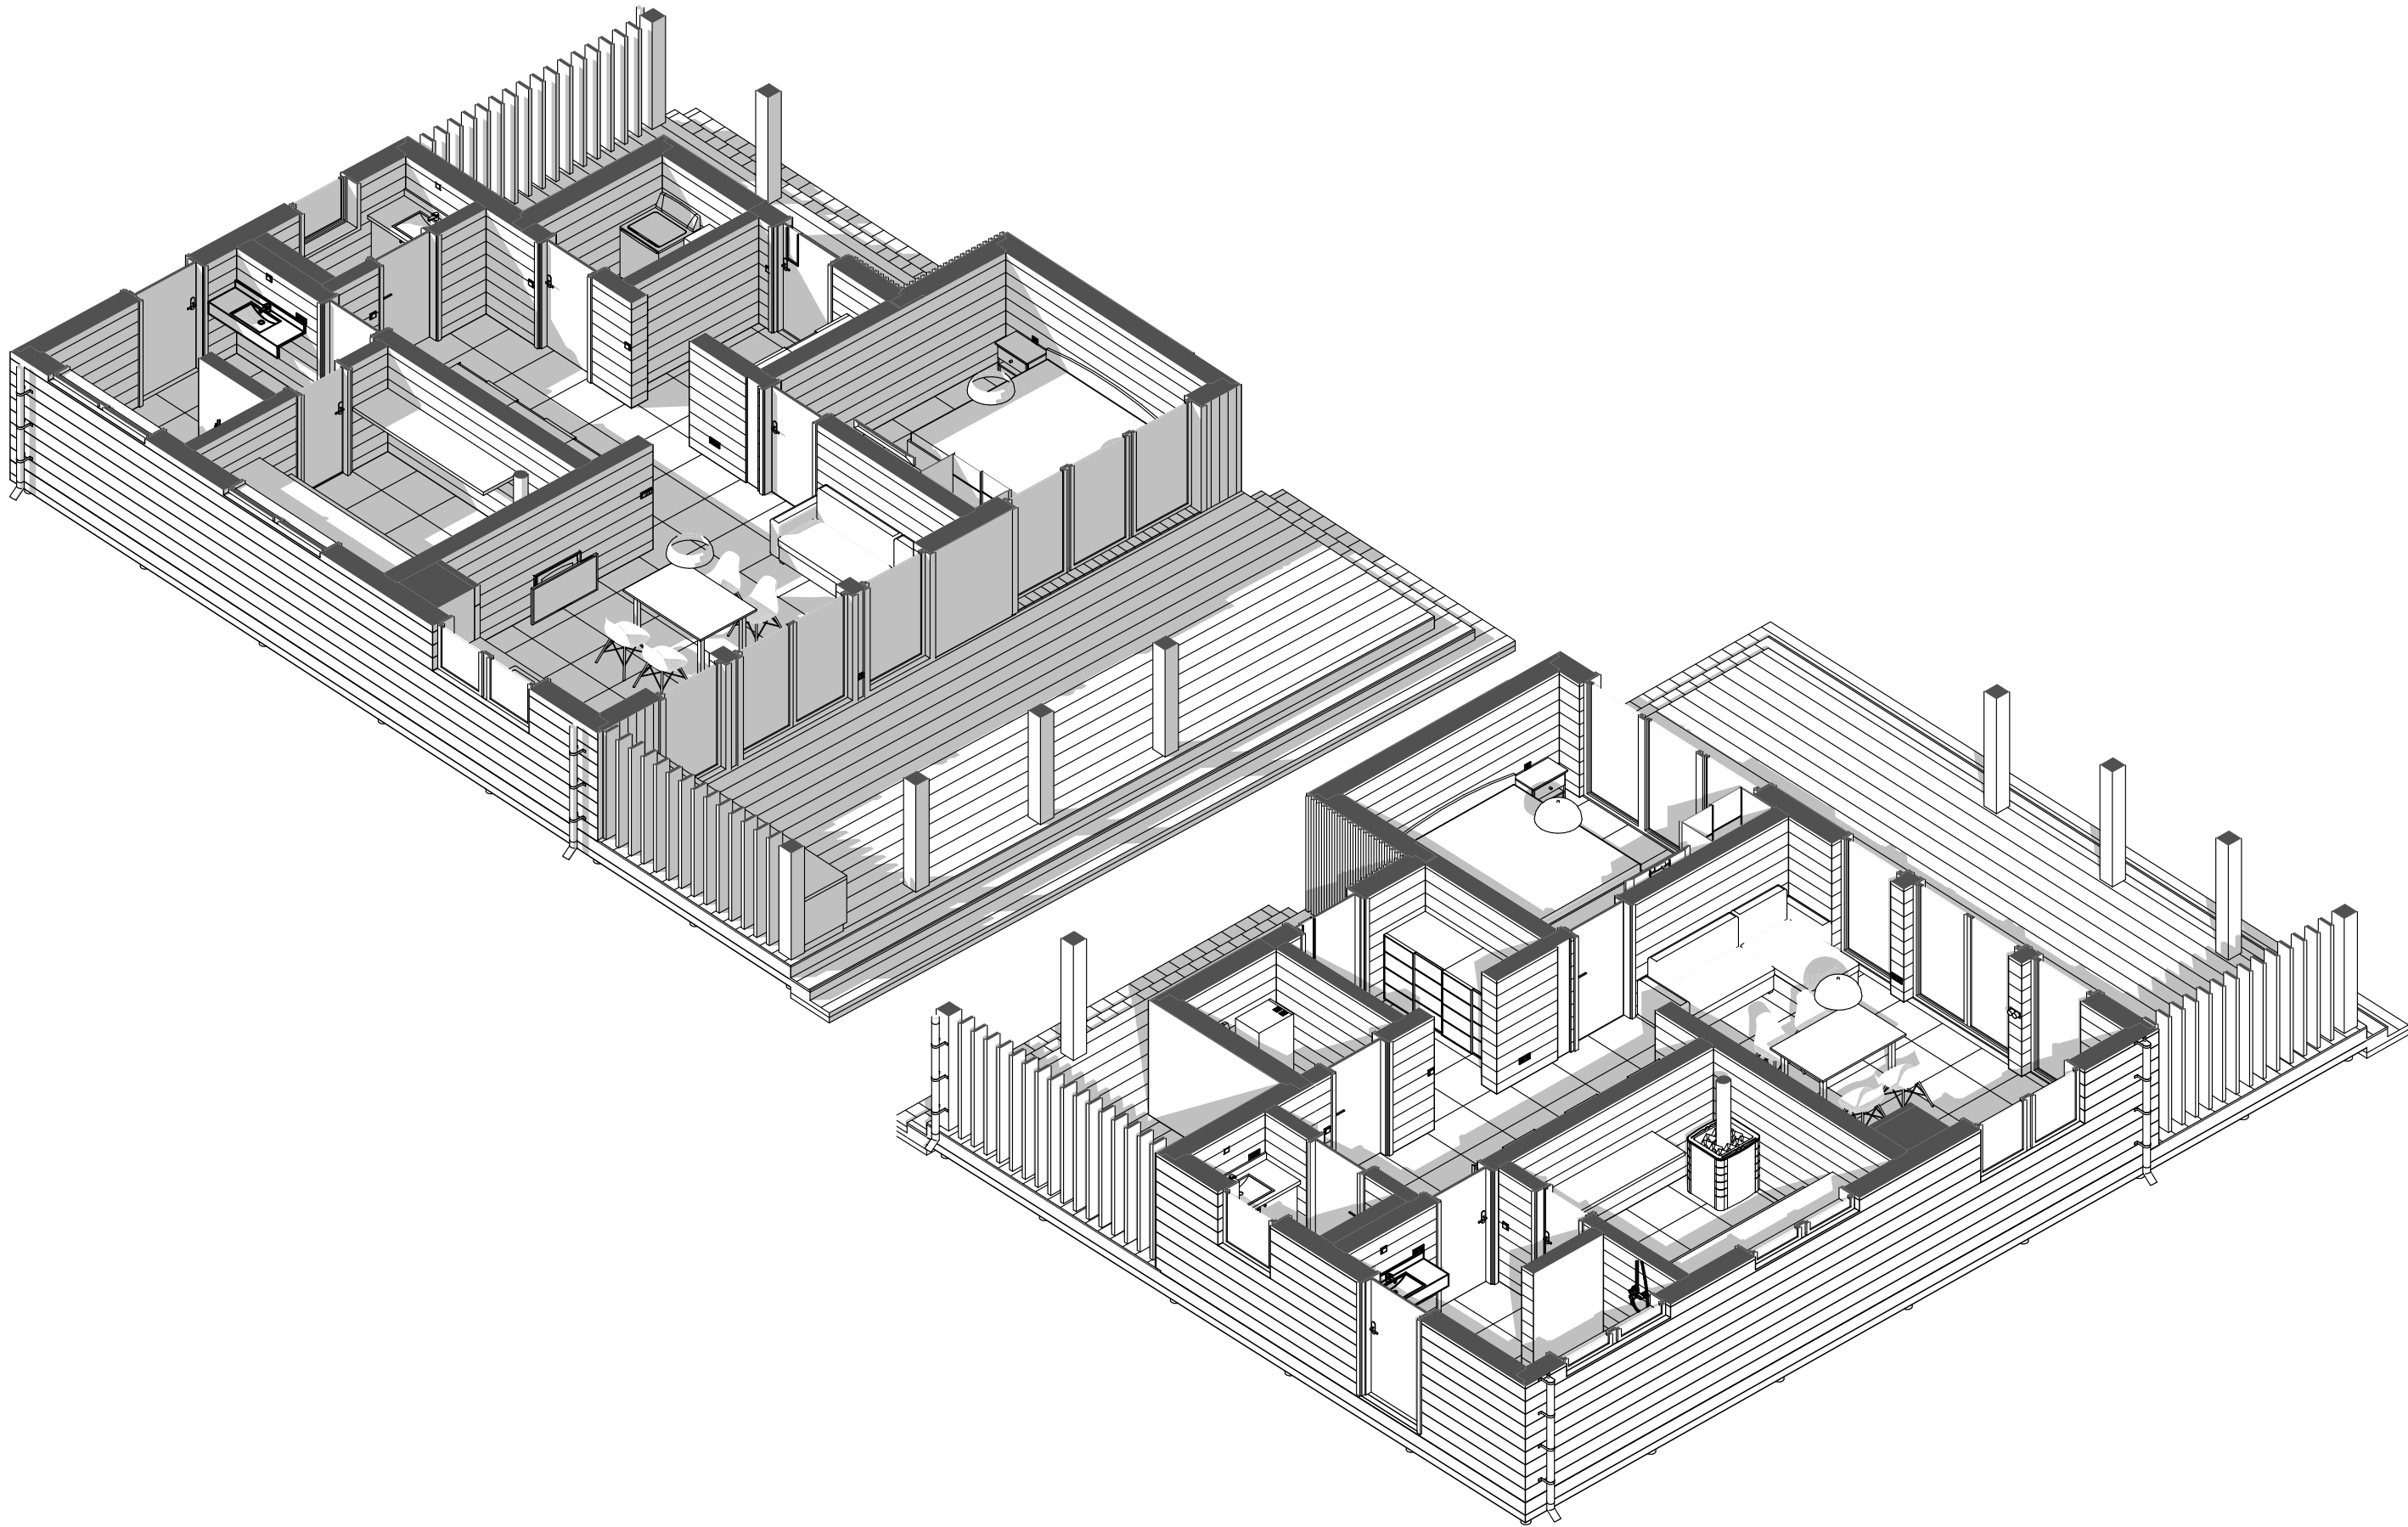

Согласовано				
Инва. № подл.	Подп. и дата	Взам. инв. №		


Лист	Изм.	№ Докум.	Подп.	Дата

Московская область, Одинцовский городской округ, село Каринское, 50:20:0080803:1001


Зд-разре

#Название Организации

Согласовано				
И-нв. № подл.	Взам. инв. №		Подп. и дата	

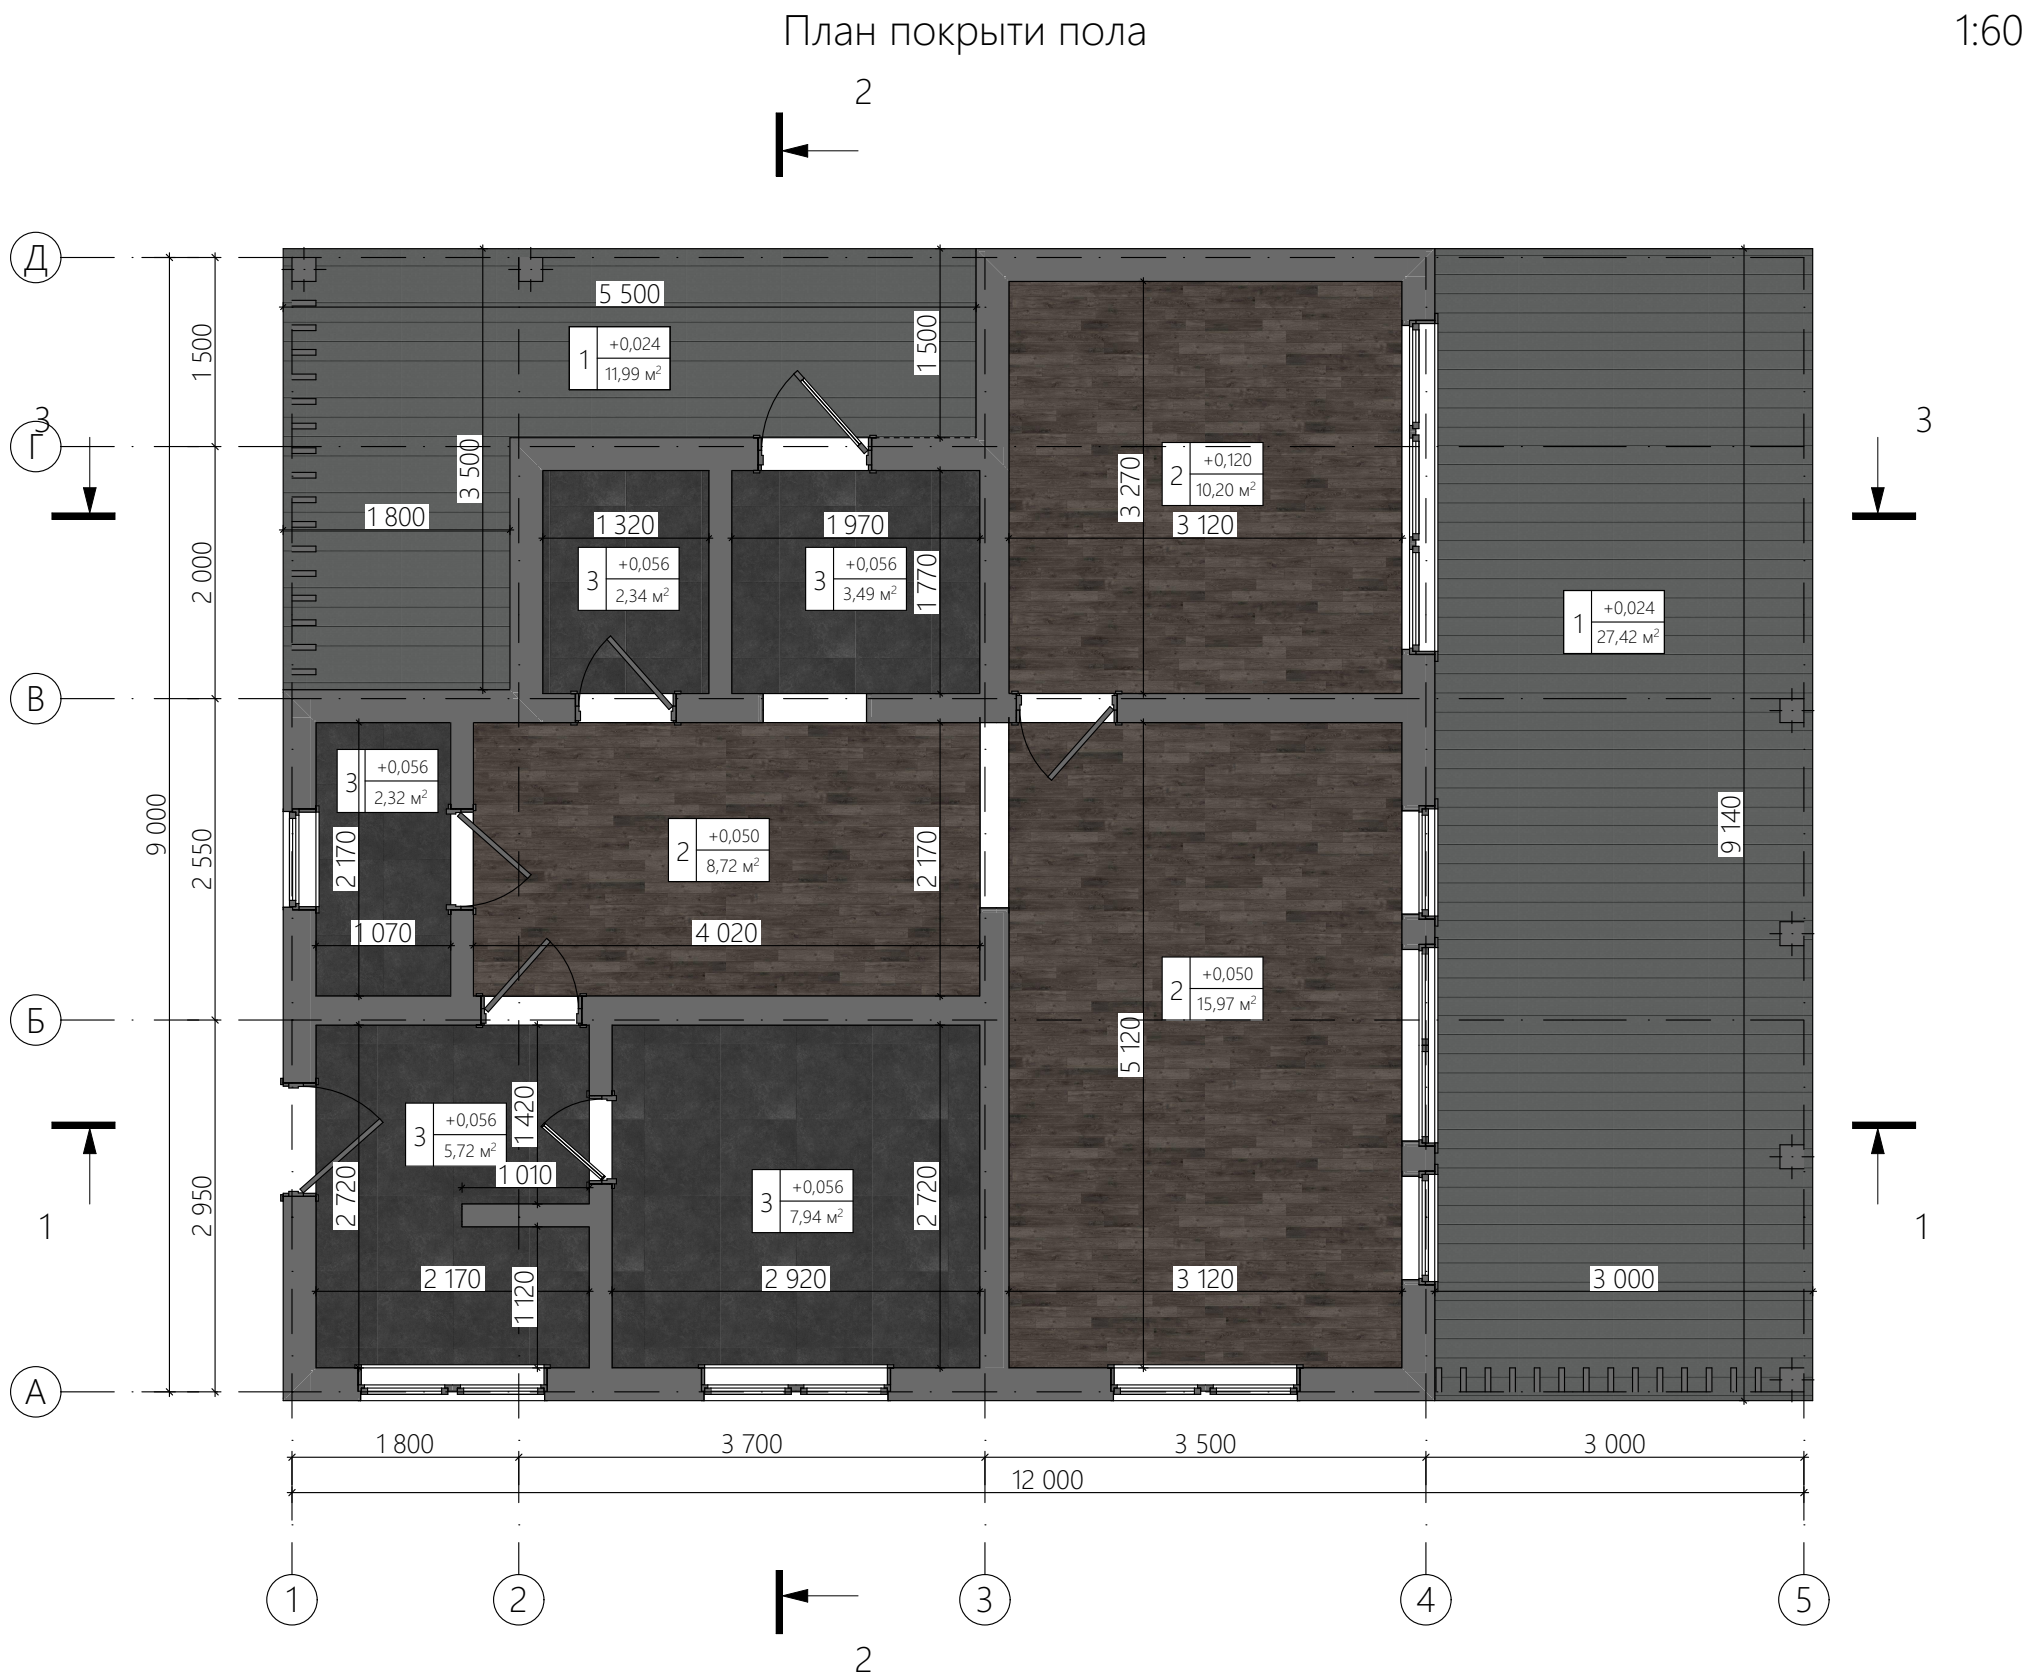

Условные обозначения

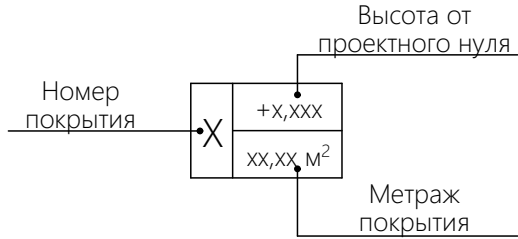

Экспликация покрытий пола

№	Наименование	Площадь, м²
1	Террасная доска	39,41
2	Ламинат	34,89
3	Керамогранит	21,81

Примечание:




1. Приведённые цветовые решения носят рекомендательный характер. Фактический подбор оттенков и материалов выполняется на этапе реализации с учётом наличия продукции у поставщиков и утверждения заказчиком.
2. Пирог покрытия смотреть на след. листе.

Лист	Изм.	№ Докум.	Подп.	Дата

Московская область, Одинцовский городской округ, село Каринское, 50:20:0080803:1001

План покрытия пола

#Название Организации

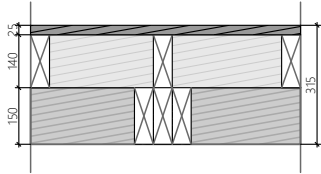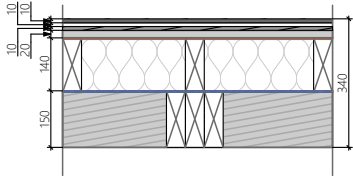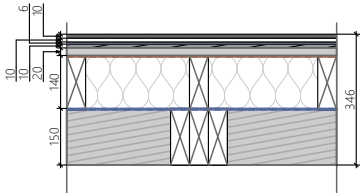Пироги пола									
№		Наименование		Разрез		Состав			
1		Террасная доска				-Террасная доска (ДПК)25мм -Лага перекрытия (шаг 400мм)140мм -Нижняя обвязка (тройная сросщенная доска)150мм			
2		Ламинат				-Ламинат10мм -Положка под ламинат10мм -ЦСП10мм -ОСБ20мм -Пароизоляционная мембрана -Лага перккрытия (шаг 600мм)140мм (с утеплителем в теле) -Гидро-ветрозащитная мембрана -Просейчка (ячейка 5х5мм) -Обрешетка (шаг 400мм) -Нижняя обвязка25мм (тройная сросщенная доска)150мм			
3		Керамогранит				-Керамогранит10мм -Клей10мм -Руспанель6мм -ЦСП10мм -ОСБ20мм -Пароизоляционная мембрана -Лага перккрытия (шаг 600мм)140мм (с утеплителем в теле) -Гидро-ветрозащитная мембрана -Просейчка (ячейка 5х5мм) -Обрешетка (шаг 400мм)25мм -Нижняя обвязка150мм (тройная сросщенная доска)			
Согласовано									
Ив. № подл.		Подп. и дата		Взам. инв. №					
Лист		Изм.		№ Докум.		Подп.		Дата	
Пироги пола						#Название Организации		Лист	
								10	

1:60



№	Наименование	Условное обозначение
---	--------------	----------------------

1	Фиброцементный сайдинг (20мм)	
2	Фиброцементные панели (20мм)	
3	Планкен (20мм)	
4	Имитация бруса (20мм)	
5	Вагонка (16мм)	
6	Керамогранит (10мм)	

Согласовано

Взам. инв. №

Подп. и дата

ИНВ. № подл.

Лист	Изм.	№ Докум.	Подп.	Дата

Московская область, Одинцовский городской округ, село Каринское,

50:20:0080803:1001

План покрытия стен

#Название Организации

ист

11


Пироги стен

№ разреза

Сечение


Состав

а-а

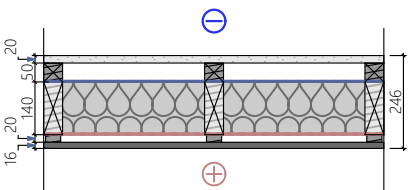


- Фиброцементный сайдинг 20мм
- Вентбрус (вертикально) 50мм
- Гидро-ветрозащитная мембрана -
- Стойка каркаса (утепленная) 140мм
- Пароизоляционная мембрана (алюм. фольга) -
- Вентбрус (вертикально) 20мм
- Вагонка 16мм

б-б

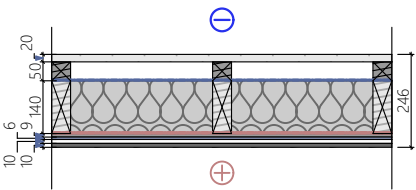


- Фиброцементный сайдинг 20мм
- Вентбрус (вертикально) 50мм
- Гидро-ветрозащитная мембрана -
- Стойка каркаса (утепленная) 140мм
- Пароизоляционная мембрана -
- ОСБ 9мм
- Рупанель 6мм
- Клей 10мм
- Керамогранит 10мм

в-в

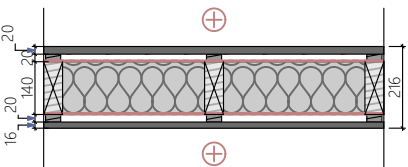


- Имитация бруса 20мм
- Вентбрус (вертикально) 20мм
- Пароизоляционная мембрана -
- Стойка каркаса (утепленная) 140мм
- Пароизоляционная мембрана (алюм. фольга) -
- Вентбрус (вертикально) 20мм
- Вагонка 16мм

г-г

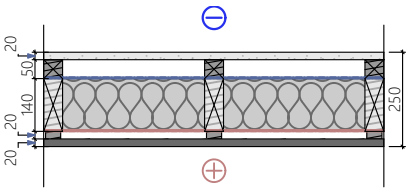

- Фиброцементные панели 20мм
- Вентбрус (вертикально) 50мм
- Гидро-ветрозащитная мембрана -
- Стойка каркаса (утепленная) 140мм
- Пароизоляционная мембрана -
- Вентбрус (вертикально) 20мм
- Имитация бруса 20мм

д-д

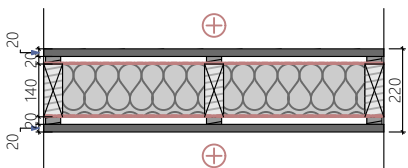

- Имитация бруса 20мм
- Вентбрус (вертикально) 20мм
- Пароизоляционная мембрана -
- Стойка каркаса (утепленная) 140мм
- Пароизоляционная мембрана -
- Вентбрус (вертикально) 20мм
- Имитация бруса 20мм

Согласовано

Взам. инв. №

Подп. и дата

Инв. № подл.

Лист	Изм.	№ Докум.	Подп.	Дата

Пироги стен


#Название Организации

Лист

12

План размещения розеток

1:60

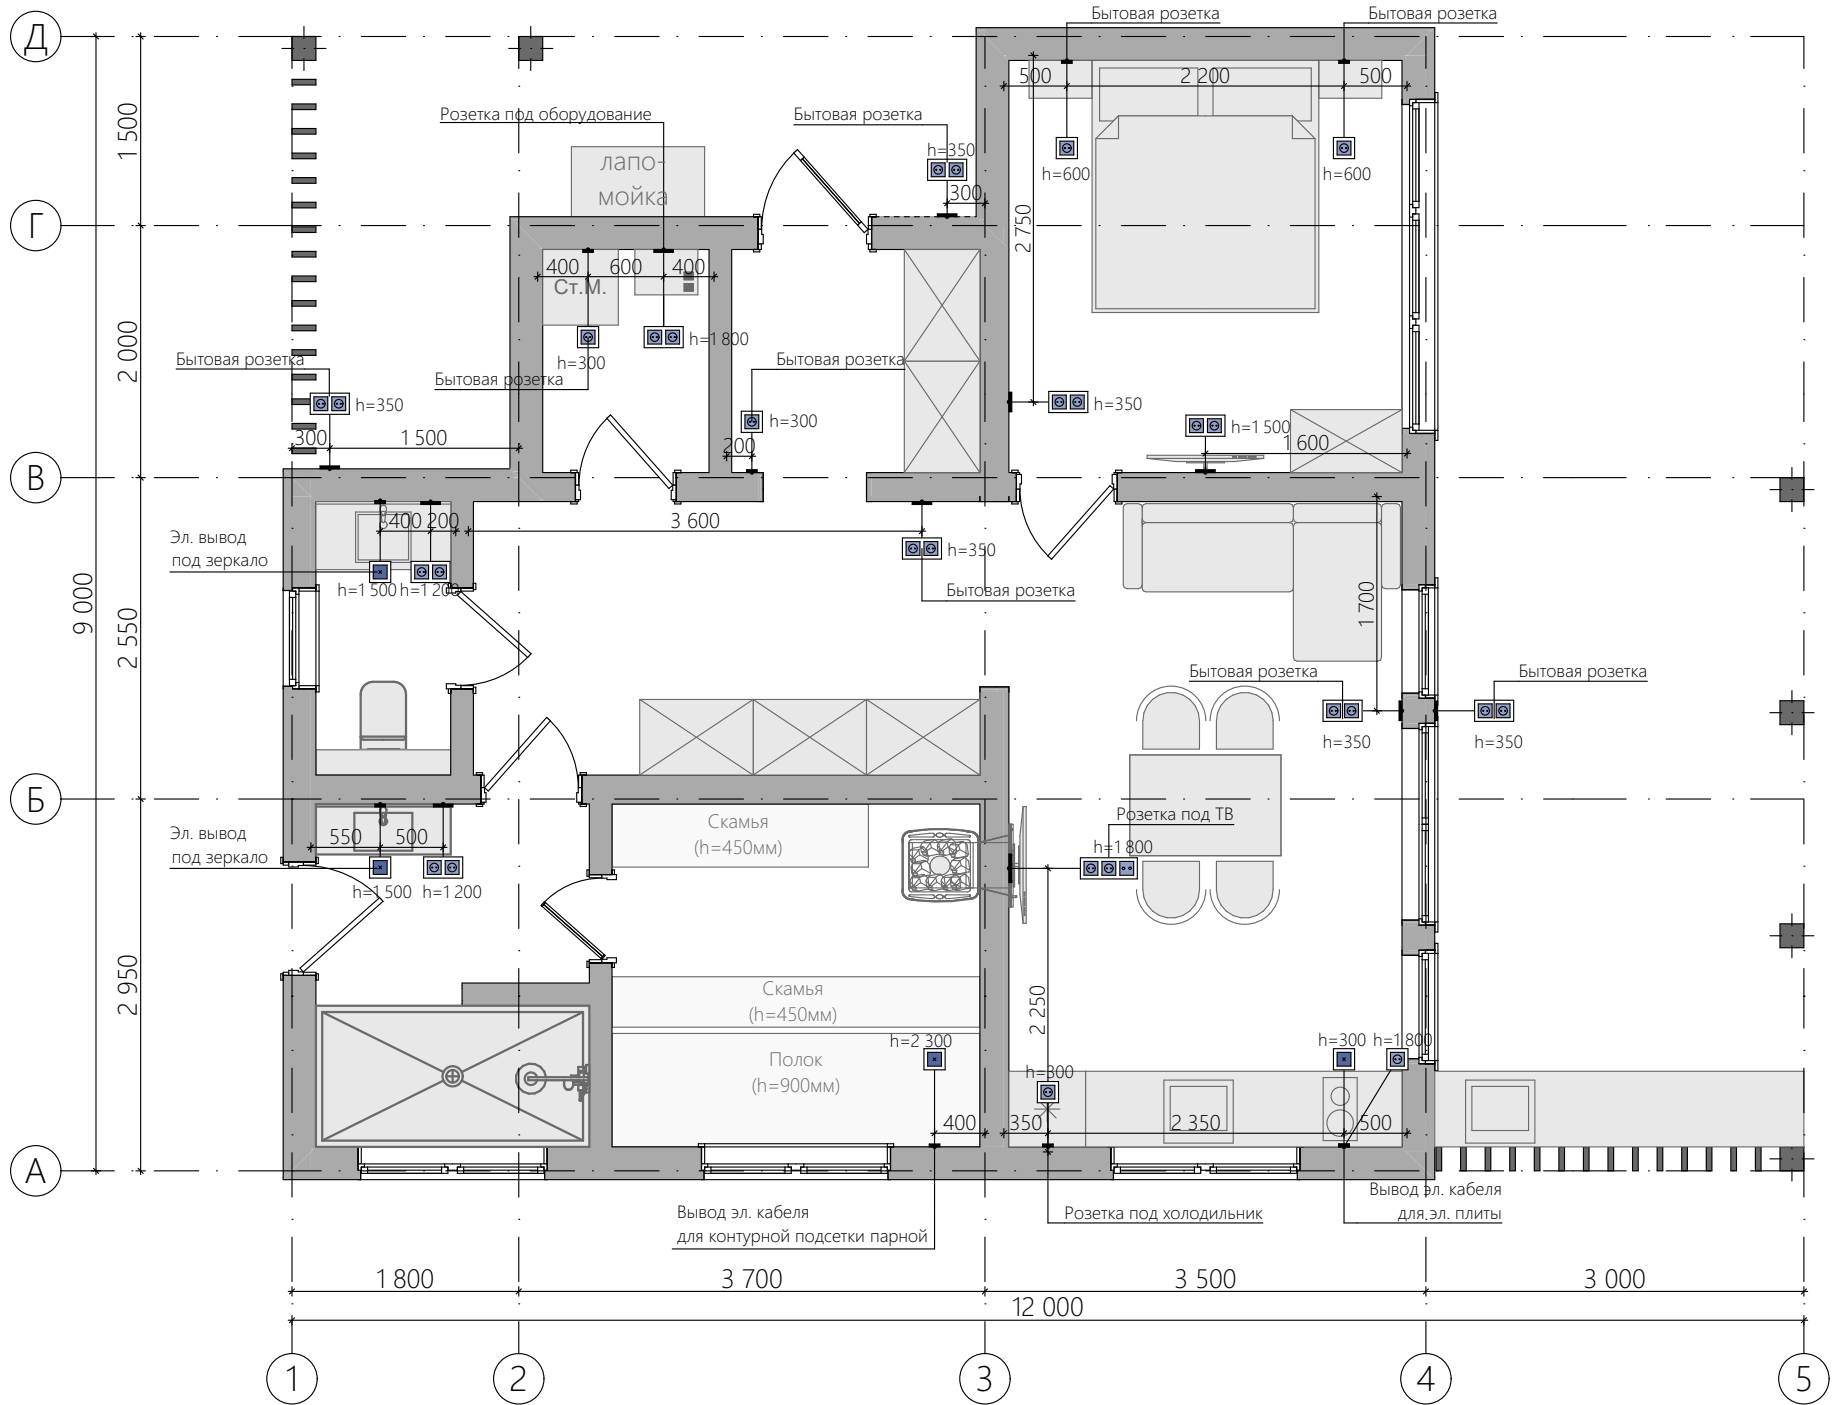

Экспликация розеток

Наименование	2д-вид	Кол-во
Розетка 220v (рамка 1 секции)		7
Розетка 220v (рамка 2 секции)		10
Розетка 220v+ТВ розетка (рамка 2 секции)		1
Эл. вывод		3
		21

Примечание:

1. Схема размещения розеток является рекомендательной и требует согласования с заказчиком по месту.
2. Все высоты даны от чистового пола.
3. Все указанные размеры даются до центра позиций.
4. Отметки розеток, выключателей, выводов и др. оборудования, являются предварительными и уточняются после выбора финишных материалов и мебели.
5. Размеры уточняются дополнительно

Согласовано

Взам. инв. №

Подп. и дата

Инв. № подл.

Лист	Изм.	№ Докум.	Подп.	Дата


Московская область, Одинцовский городской округ, село Каринское, 50:20:0080803:1001

План размещения розеток

#Название Организации

План размещения светильников и выключателей

1:60

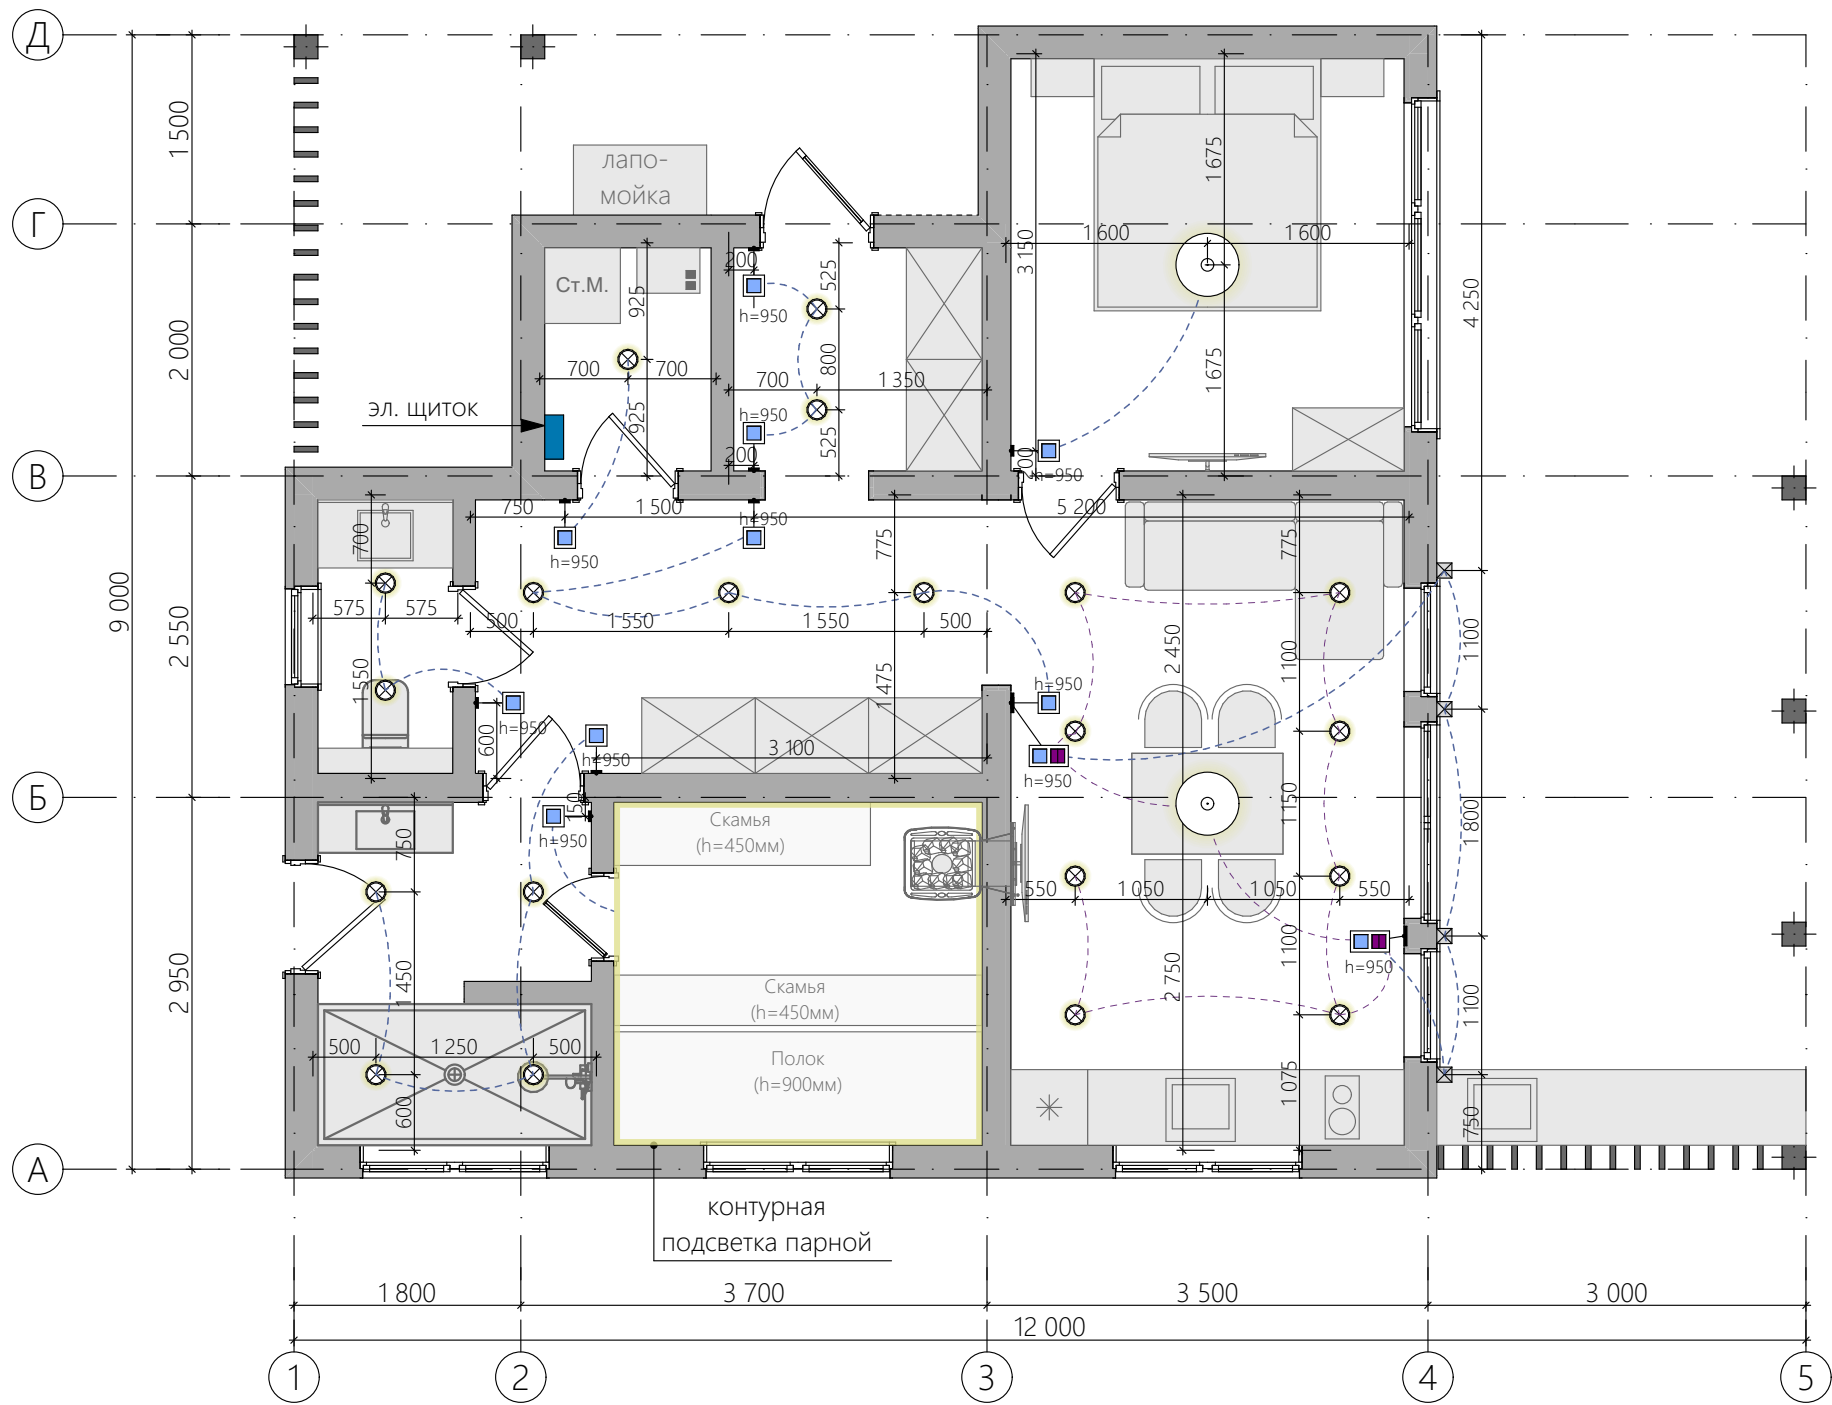

Экспликация светильников и выключателей

Наименование	2д-вид	Кол-во
Выключатель одно- и двухклавишный (рамка 2 секции)		2
Выключатель одноклавишный (рамка 1 секции)		9
Светильник подвесной		2
Светильник точечный		20
Уличный светильник		4
		37

Примечание:

1. Схема размещения розеток является рекомендательной и требует согласования с заказчиком по месту.

2. Все высоты даны от чистового пола.

3. Все указанные размеры даются до центра позиций.

4. Отметки розеток, выключателей, выводов и др. оборудования, являются предварительными и уточняются после выбора финишных материалов и мебели.

5. Размеры уточняются дополнительно

Согласовано

Взам. инв. №

Подп. и дата

Инв. № подл.

Лист	Изм.	№ Докум.	Подп.	Дата

Московская область, Одинцовский городской округ, село Каринское, 50:20:0080803:1001

План размещения светильников и выключателей

#Название Организации

Согласовано				
И-нв. № подл.	Взам. инв. №		Подп. и дата	


Лист	Изм.	№ Докум.	Подп.	Дата

Московская область, Одинцовский городской округ, село Каринское,		50:20:0080803:1001

План крыши

#Название Организации

Лист
15

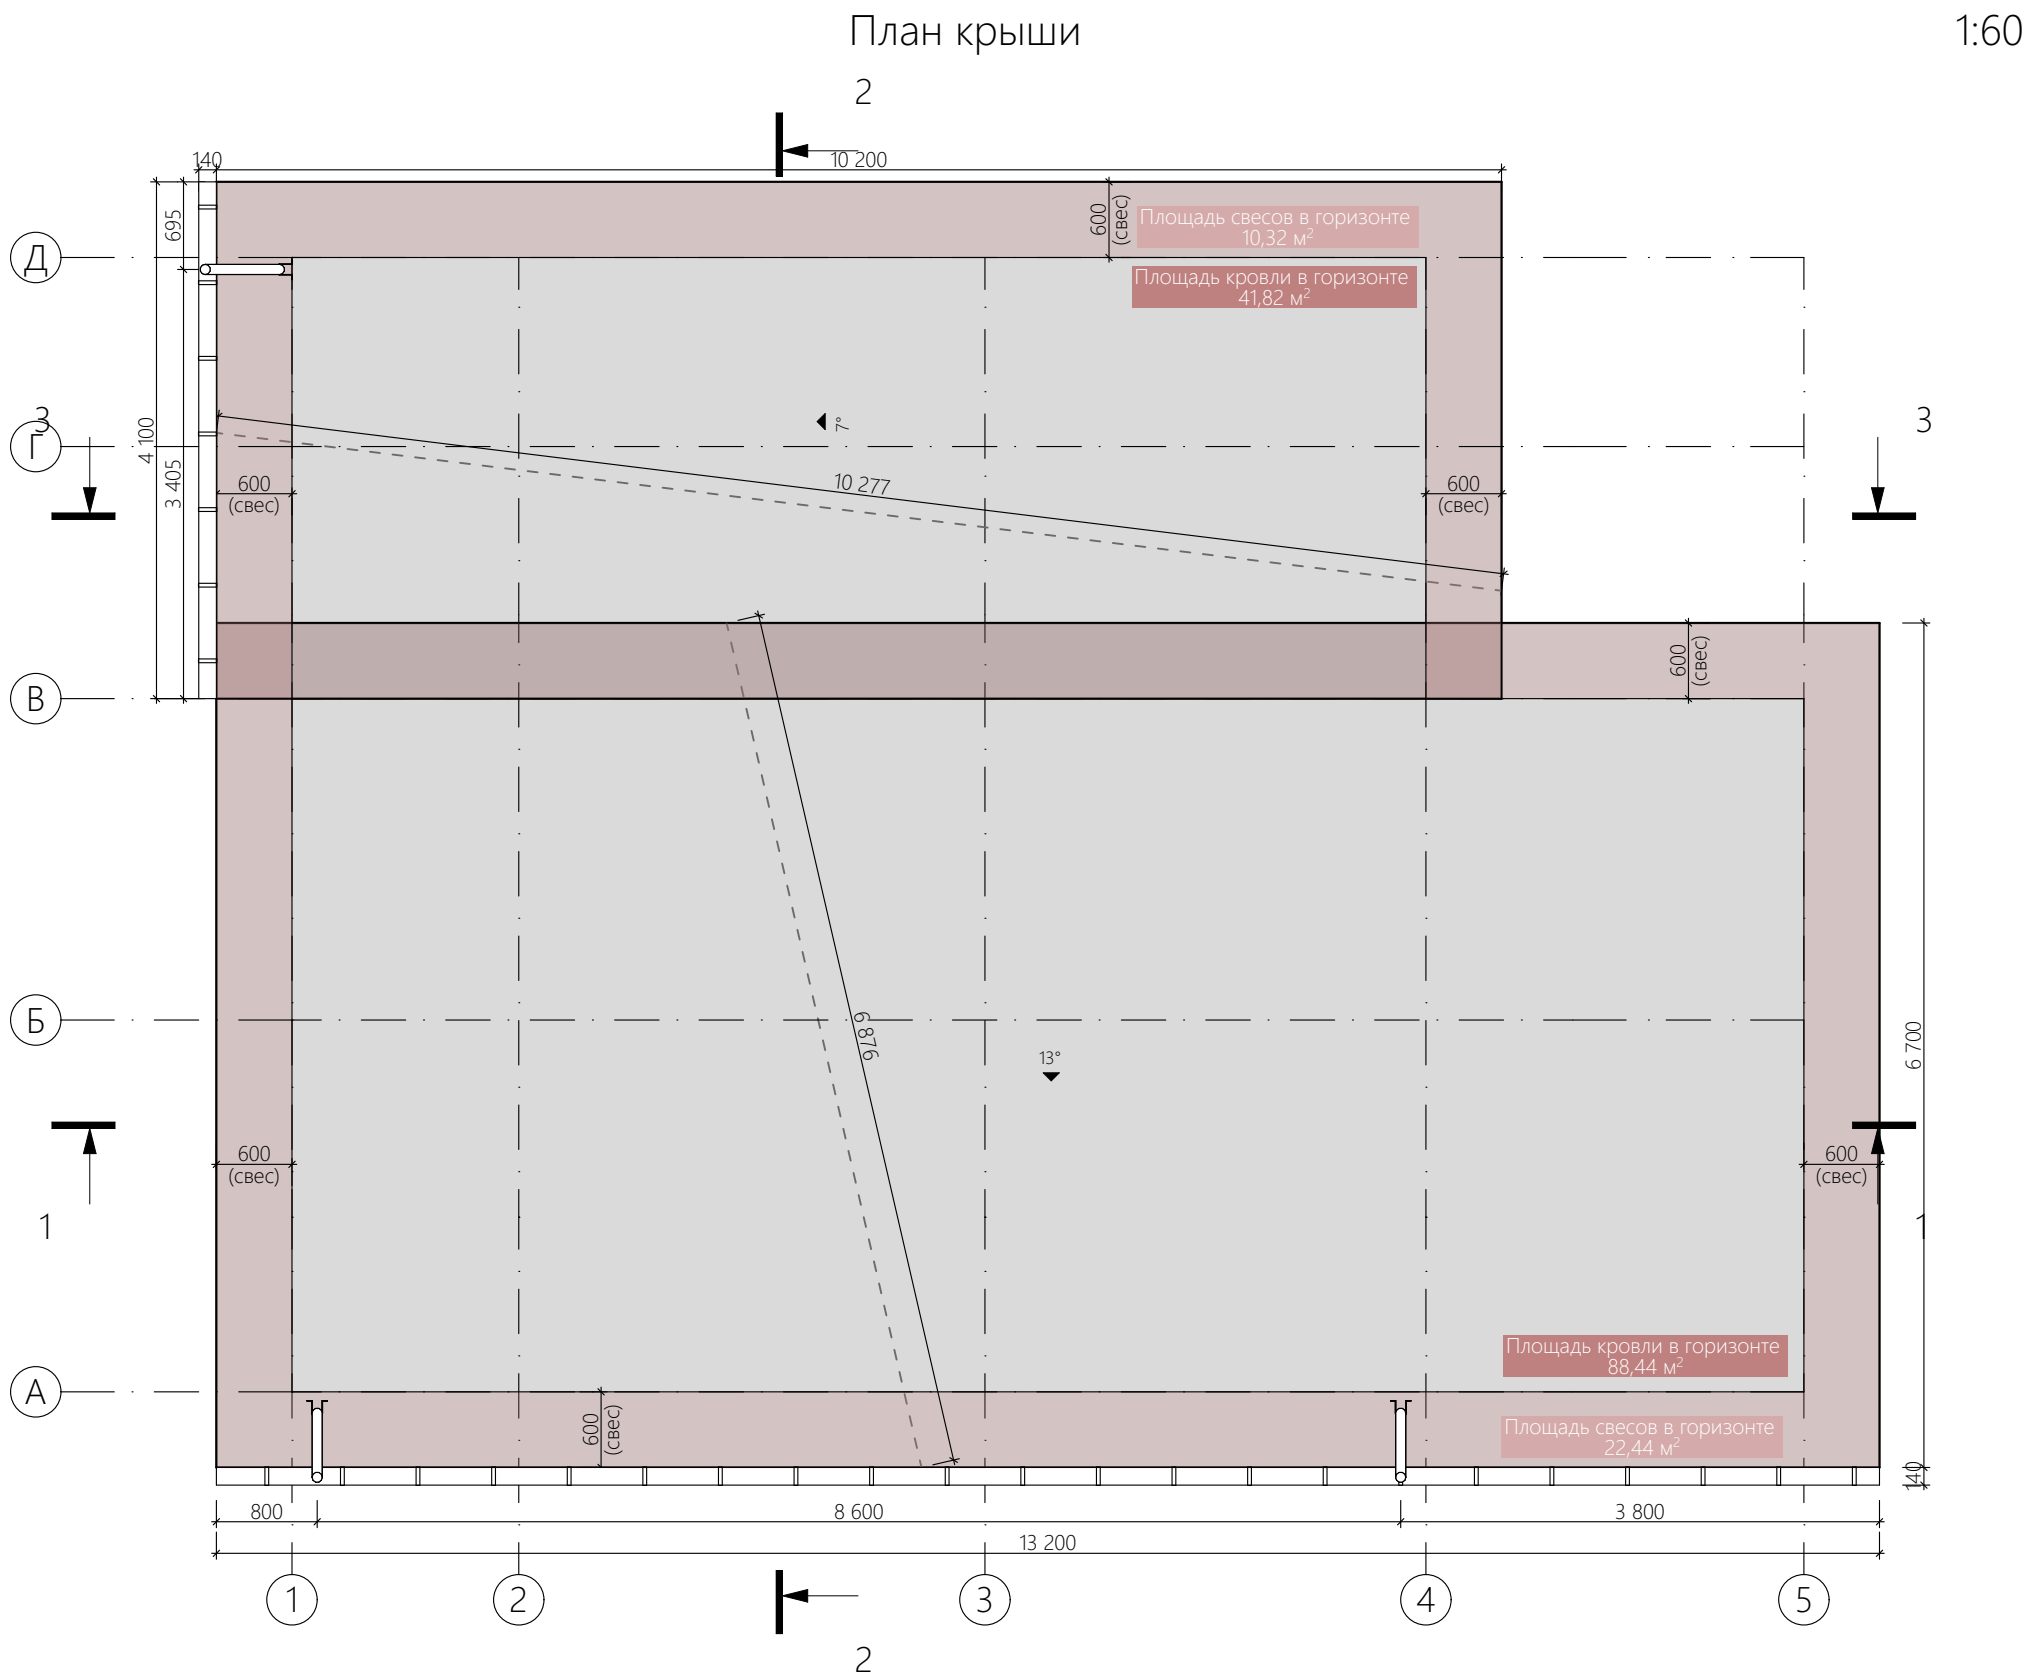

- Условные обозначения:
- Крыша бани (уклон 13/7°)
 - Подшив свесов бани

Площадь крыши бани (S, м²) = 132,90м²



Ведомость оконных проемов										1:1	
Наименование		Размеры проема Ш x В, мм		Вид		Кол- тво		Площадь, м2			
OK1		900×2 728				1		2,36			
OK2		1 600×3 143				1		4,73			
OK3		900×3 397				1		2,96			
OK4		2 650×2 900				1		7,69			
OK5		800×1 200				1		0,96			
OK6		1 500×600				2		0,90			
OK7		1 500×1 200				1		1,80			
								22,30 м²			
Примечание: 1. Изготовление окон и дверей определяется заказчиком, допускается изменение открывания окон и дверей; 2. При заказе оконных и дверных блоков необходим обмер по месту от изготовителя; 3. Оконные и дверные изделия изображены со стороны открывания.											
Инв. № подл.	Изм.	№ Докум.	Подп.	Дата	Ведомость оконных проемов			#Название Организации			Лист
											16

Согласовано				

Инв. № подл.	Подп. и дата	Взам. инв. №	


1:1

Согласовано			

Инд. №	Подл.	Подп. и дата	Взам. инв. №	<u>Примечание:</u> 1. Изготовление окон и дверей определяется заказчиком, допускается изменение открывания окон и дверей; 2. При заказе оконных и дверных блоков необходим обмер по месту от изготовителя; 3. Оконные и дверные изделия изображены со стороны открывания.			
Лист	Изм.	№ Докум.	Подп.		Дата		
					Ведомость дверных проемов	#Название Организации	Лист
							17

Разрез 1-1

1:50

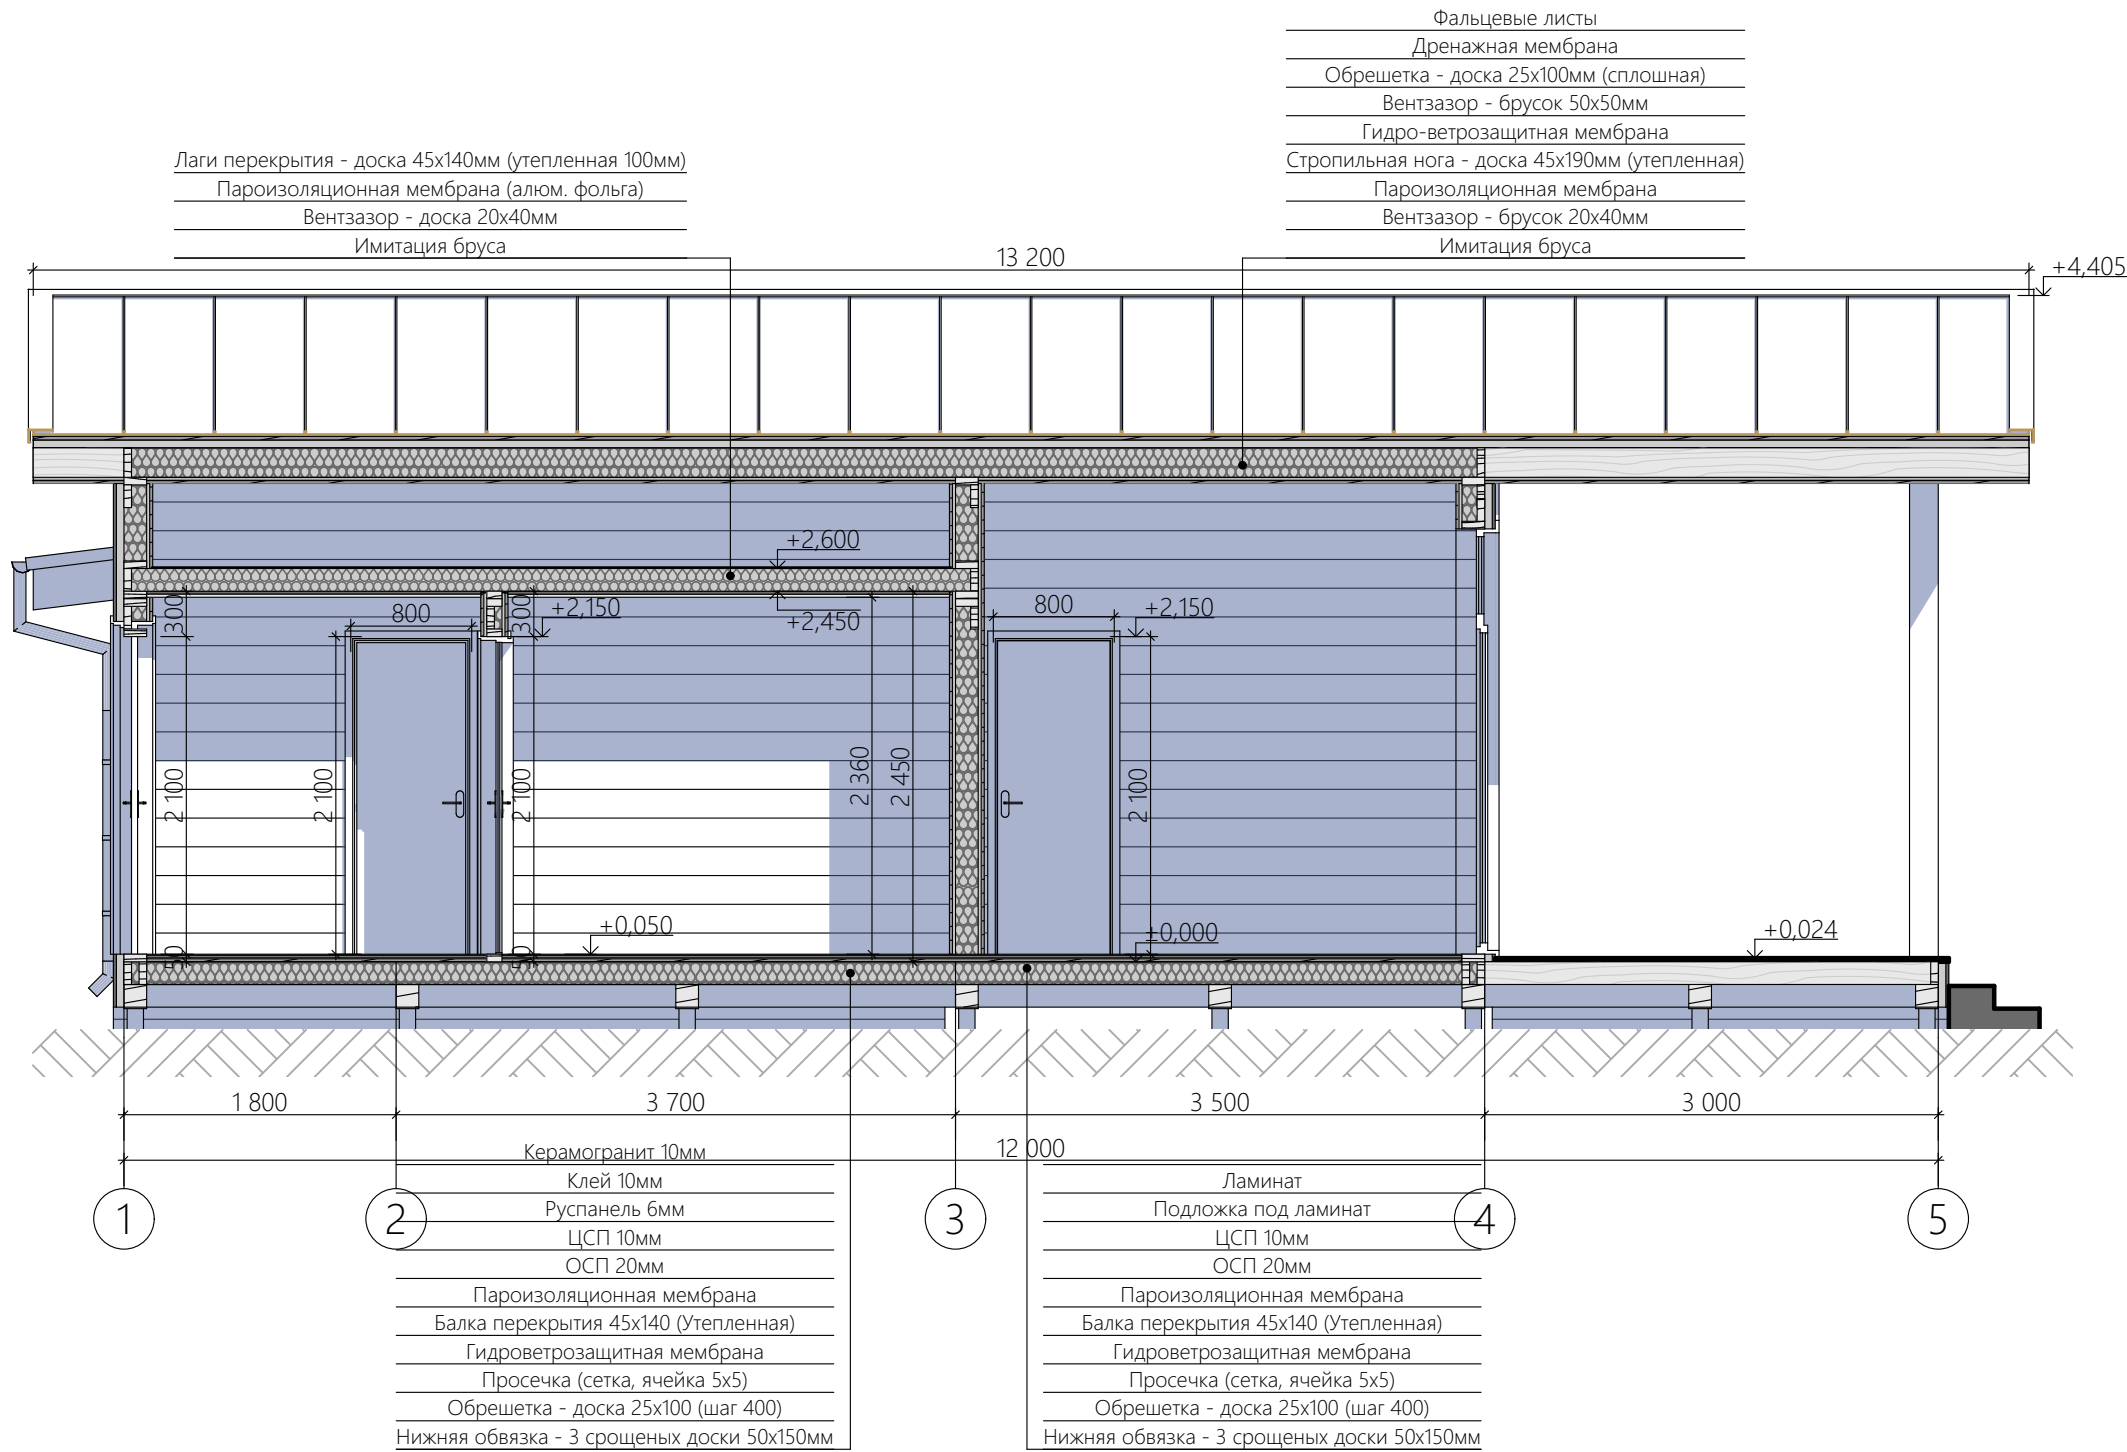

Согласовано				
И.нв. № подл.	Взам. инв. №	Подп. и дата		

Лист	Изм.	№ Докум.	Подп.	Дата

Московская область, Одинцовский городской округ, село Каринское, 50:20:0080803:1001	
---	--


Разрез 1-1

#Название Организации

Лист
18

Разрез 2-2

1:50

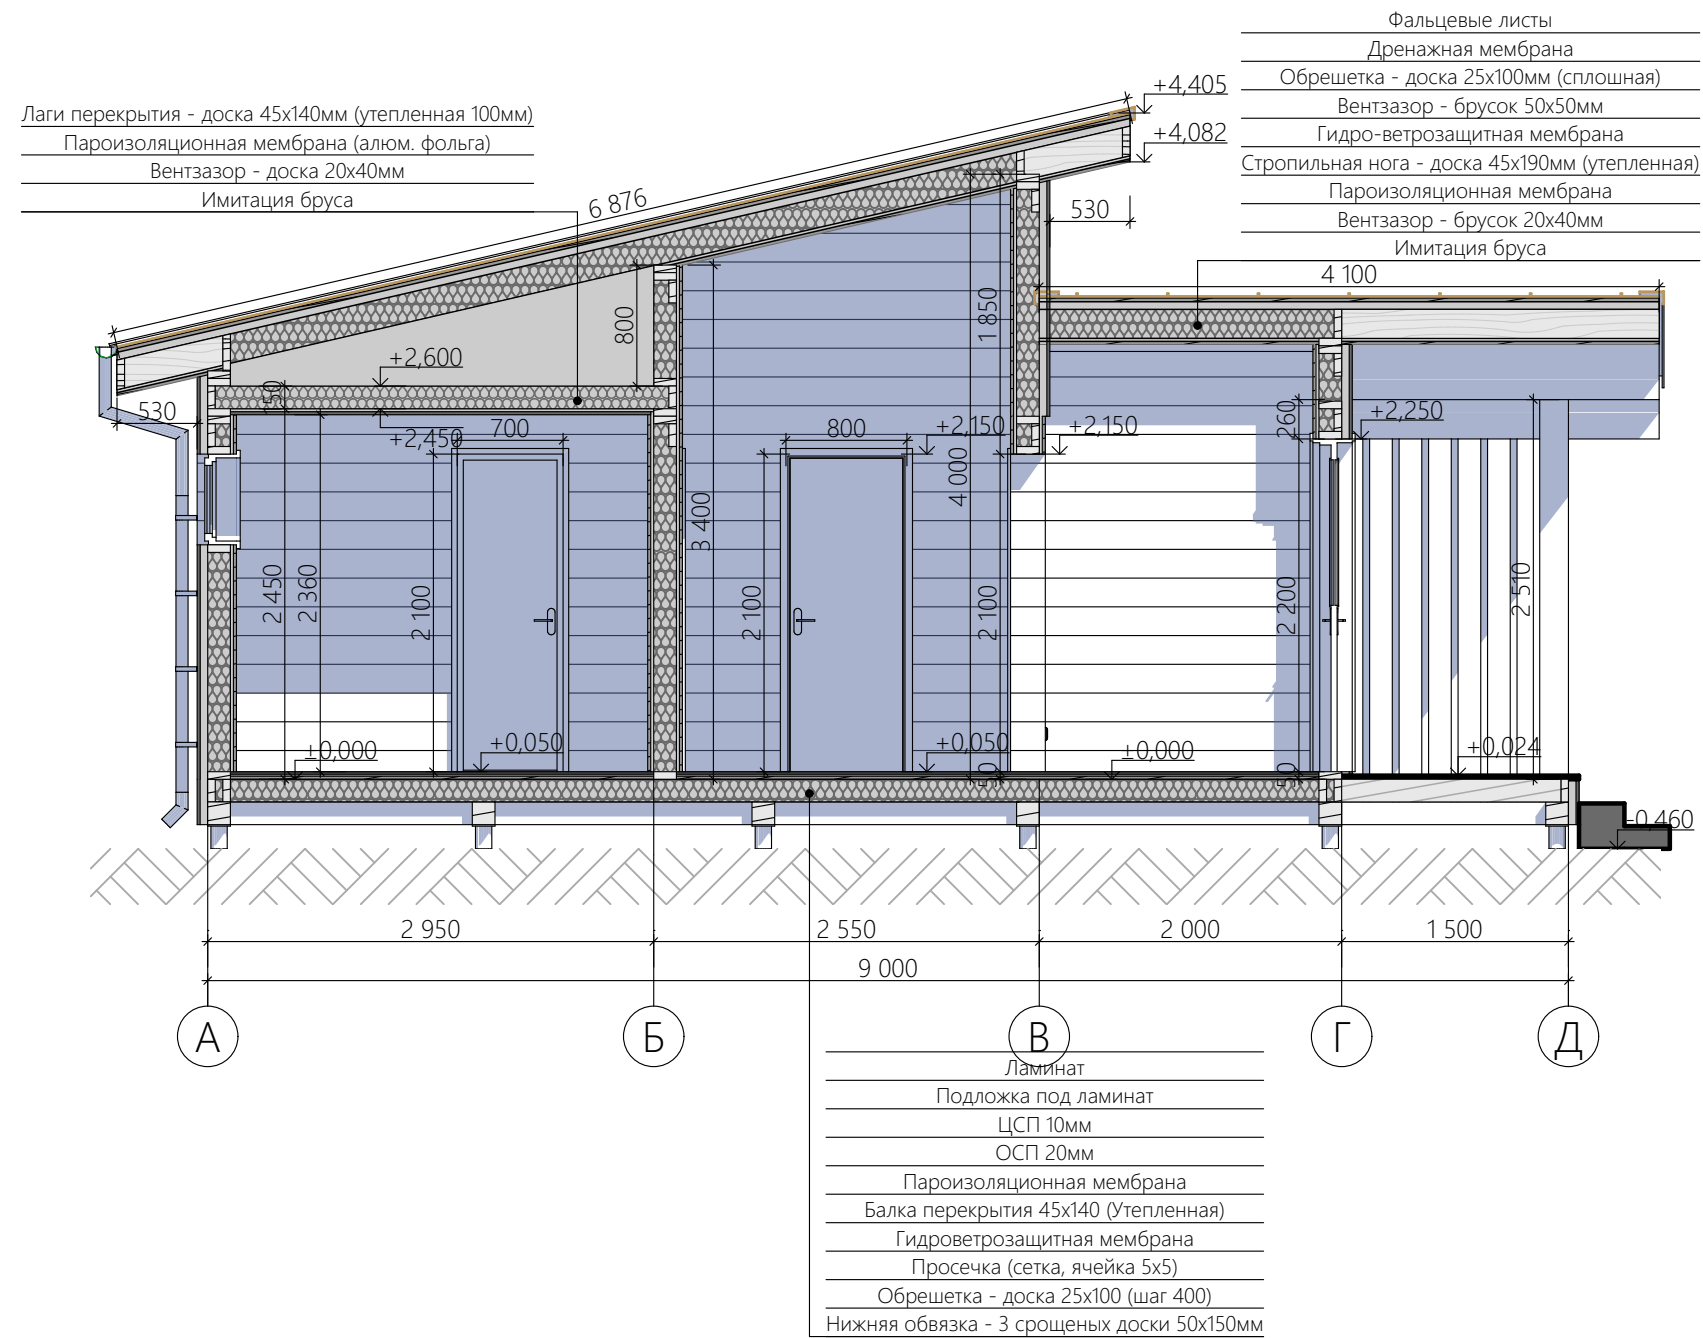

		Согласовано	

Лист	Изм.	№ Докум.	Подп.	Дата

Московская область, Одинцовский городской округ, село Каринское, 50:20:0080803:1001


Разрез 2-2

#Название Организации

19

Разрез 3-3

1:50

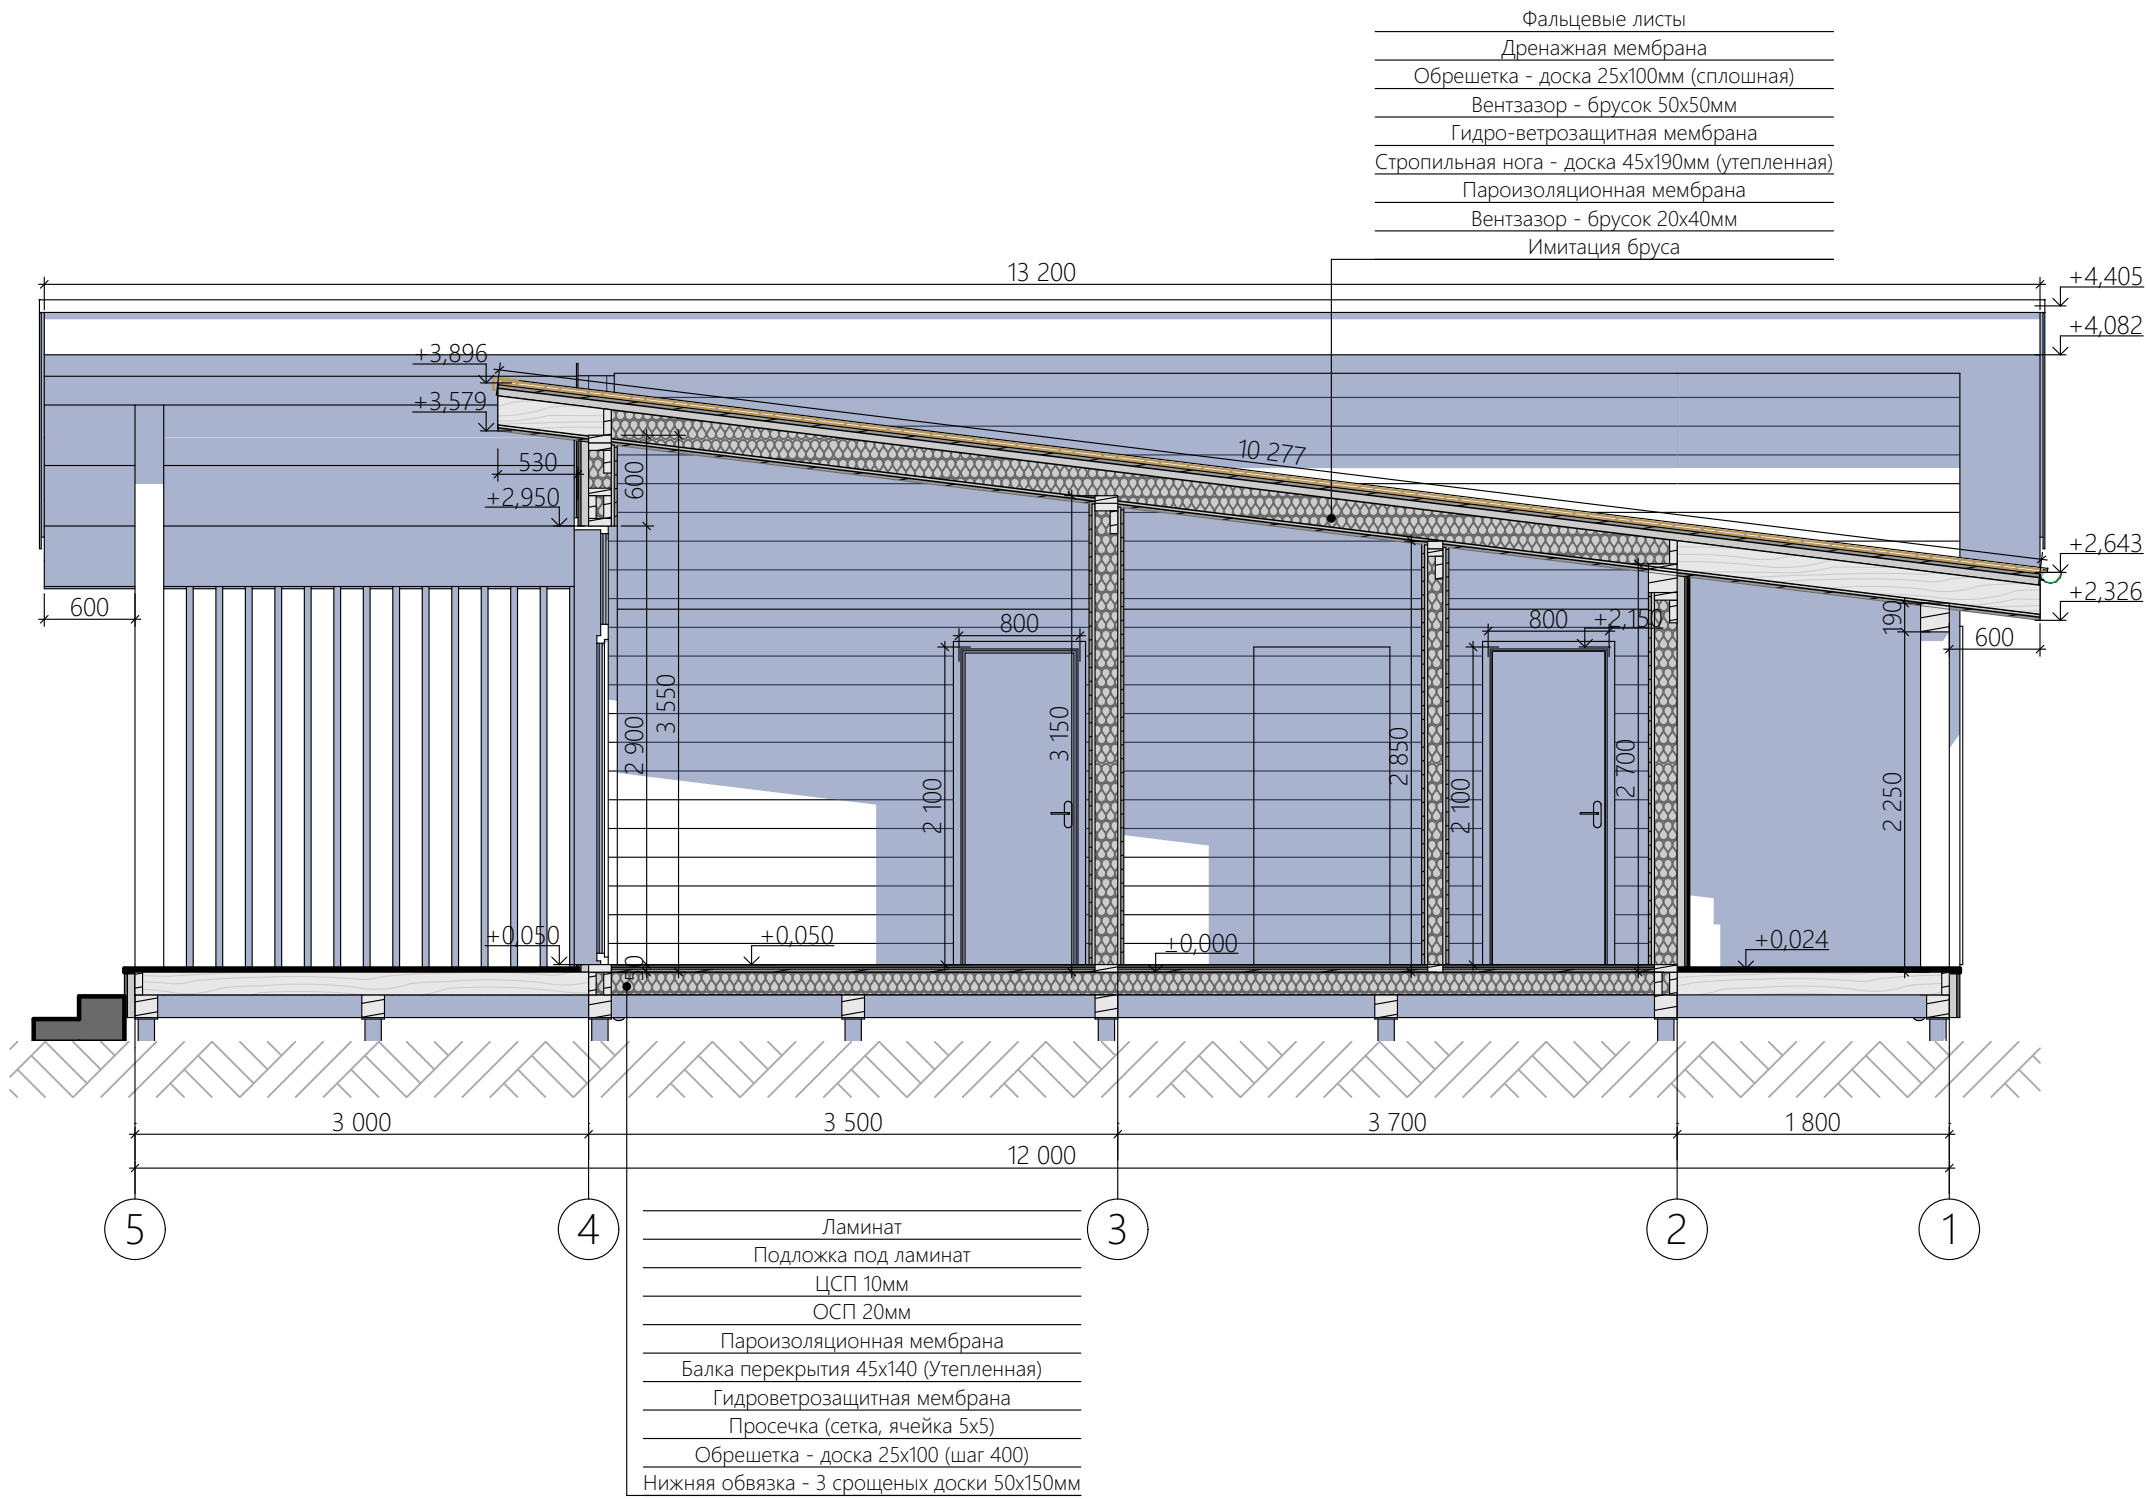

Согласовано

Взам. инв. №

Подп. и дата

Инв. № подл.

Лист	Изм.	№ Докум.	Подп.	Дата

Московская область, Одинцовский городской округ, село Каринское, 50:20:0080803:1001

Разрез 3-3

#Название Организации


Лист
20

Фасад 1-5

1:50

Условные обозначения:

- Фиброцементный сайдинг (RAL 7006)
- Террасная доска (Экодек кантри черный)
- Водосточная система, рамы, наличники, фальцевые листы (RAL 9005)
- Фальцевые листы, лобовая (RAL 7024)
- Дерево крашенное, лобовая доска, декоративные роейки
- Фиброцементные панели (RAL 9001)
- Планкен

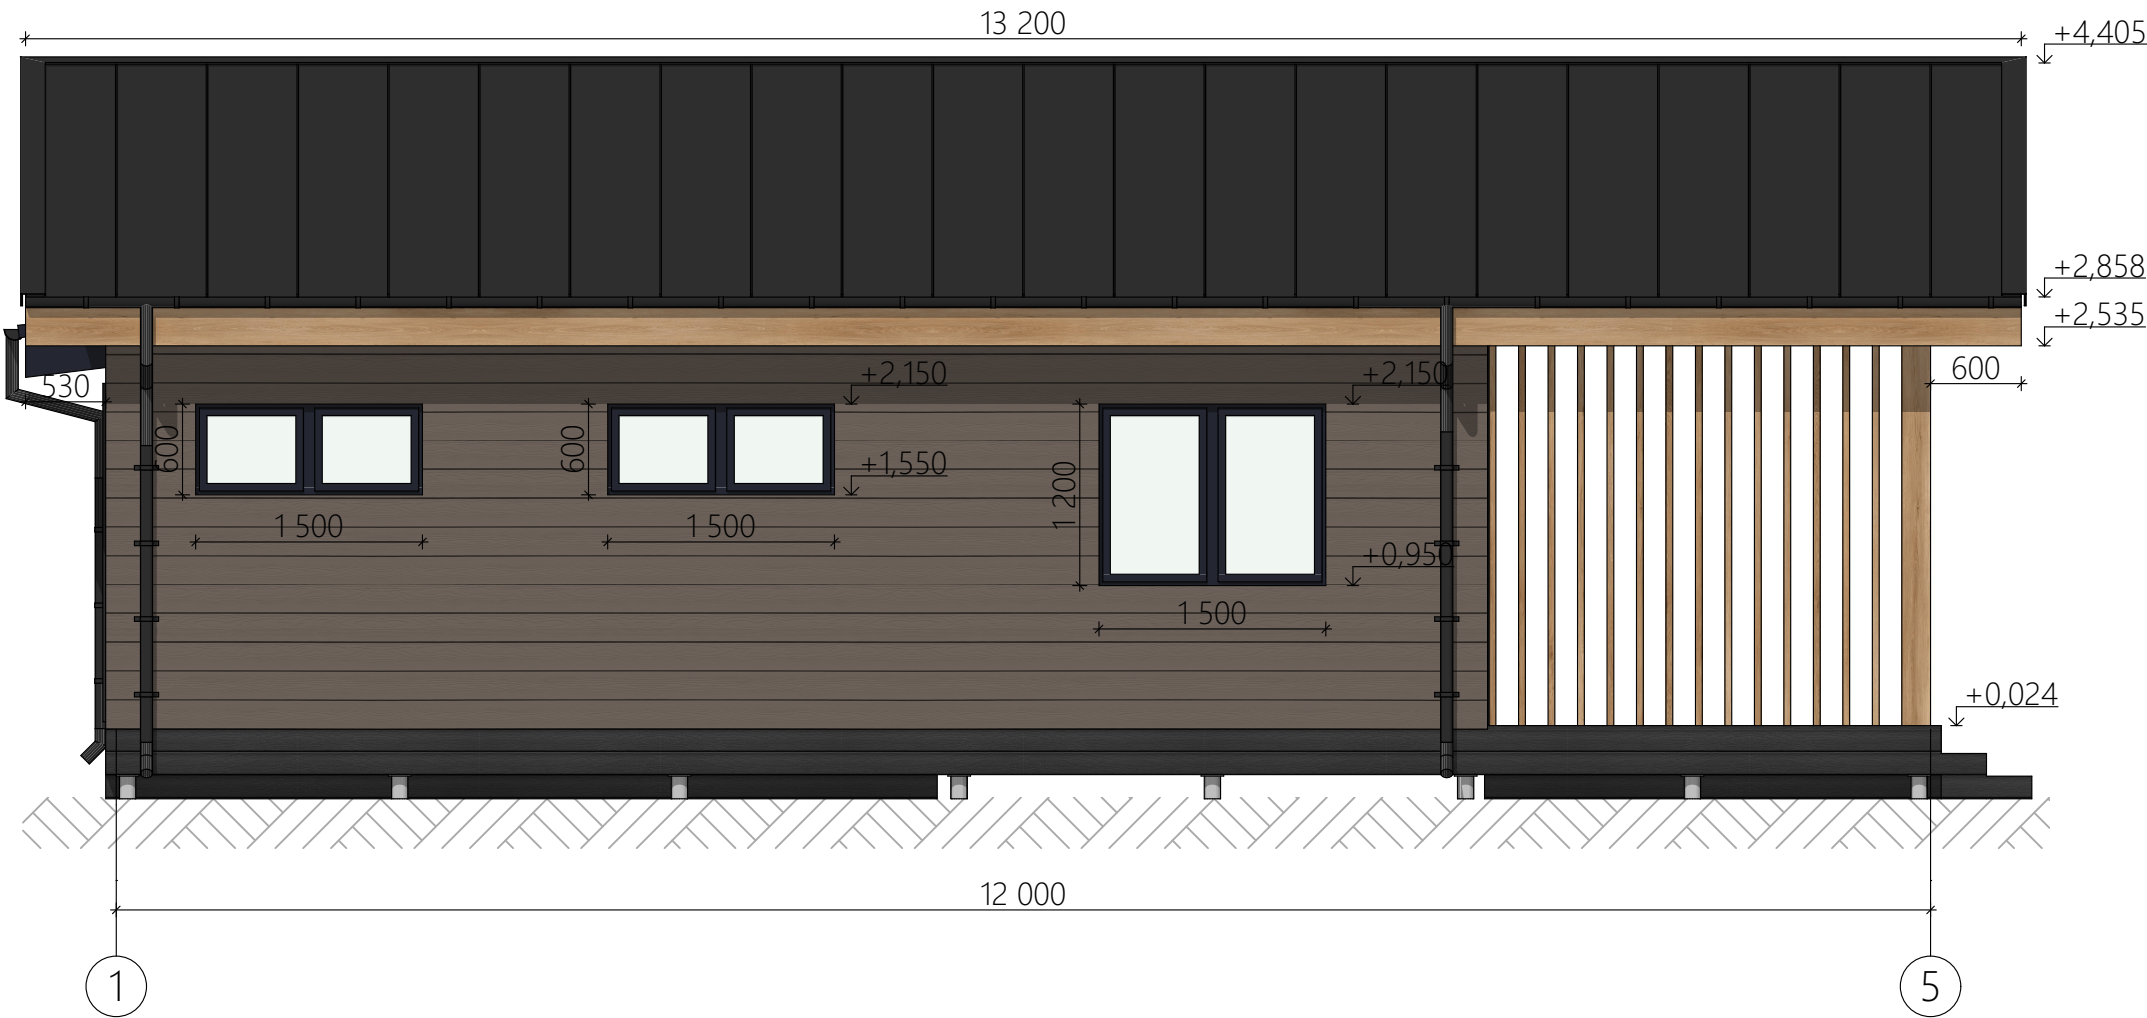

Согласовано

Взам. инв. №

Подп. и дата

Инв. № подл.

Лист	Изм.	№ Докум.	Подп.	Дата

Московская область, Одинцовский городской округ, село Каринское,

50:20:0080803:1001

Фасад 1-5

#Название Организации

Лист


21

Фасад Д-А

1:50

Условные обозначения:

- Фиброцементный сайдинг (RAL 7006)
- Террасная доска (Экодек кантри черный)
- Водосточная система, рамы, наличники, фальцевые листы (RAL 9005)
- Фальцевые листы, лобовая (RAL 7024)
- Дерево крашенное, лобовая доска, декоративные роейки
- Фиброцементные панели (RAL 9001)
- Планкен

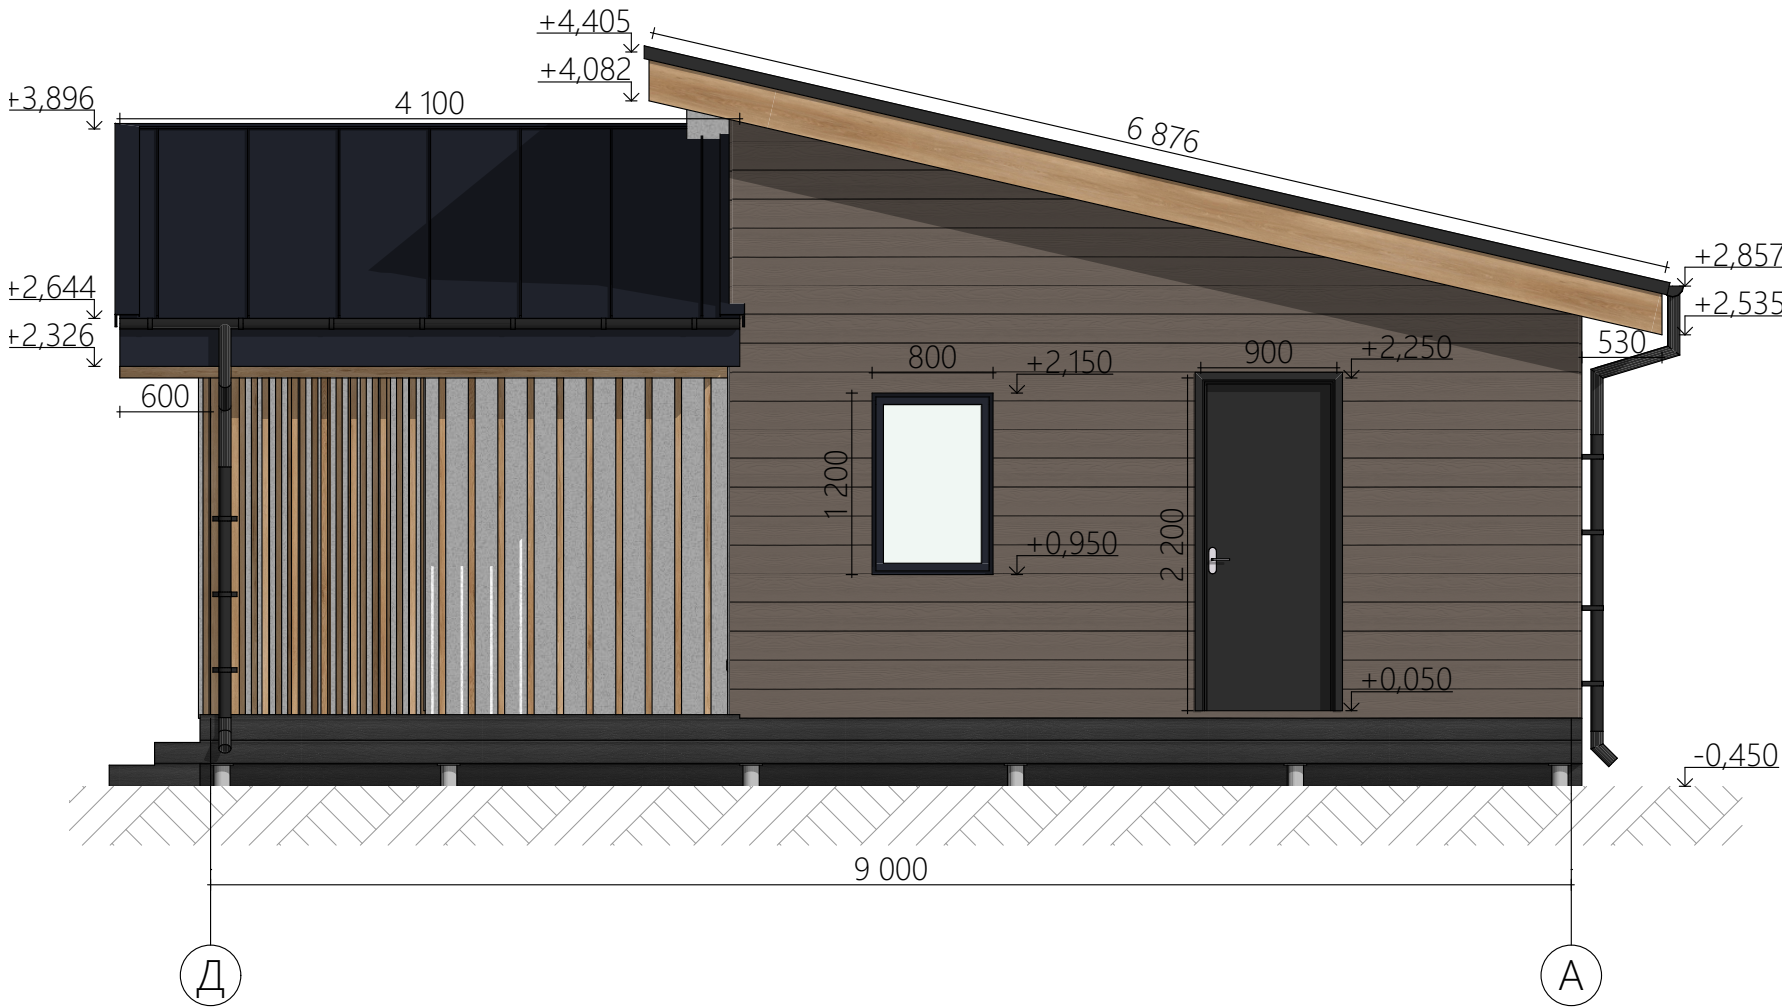

Согласовано				
Инов. № подл.	Взам. инв. №	Подп. и дата		

Лист	Изм.	№ Докум.	Подп.	Дата

Московская область, Одинцовский городской округ, село Каринское,		50:20:0080803:1001
--	--	--------------------

Фасад Д-А


#Название Организации
22

Фасад 5-1

1:50

Условные обозначения:

- Фиброцементный сайдинг (RAL 7006)
- Террасная доска (Экодек кантри черный)
- Водосточная система, рамы, наличники, фальцевые листы (RAL 9005)
- Фальцевые листы, лобовая (RAL 7024)
- Дерево крашенное, лобовая доска, декоративные роейки
- Фиброцементные панели (RAL 9001)
- Планкен

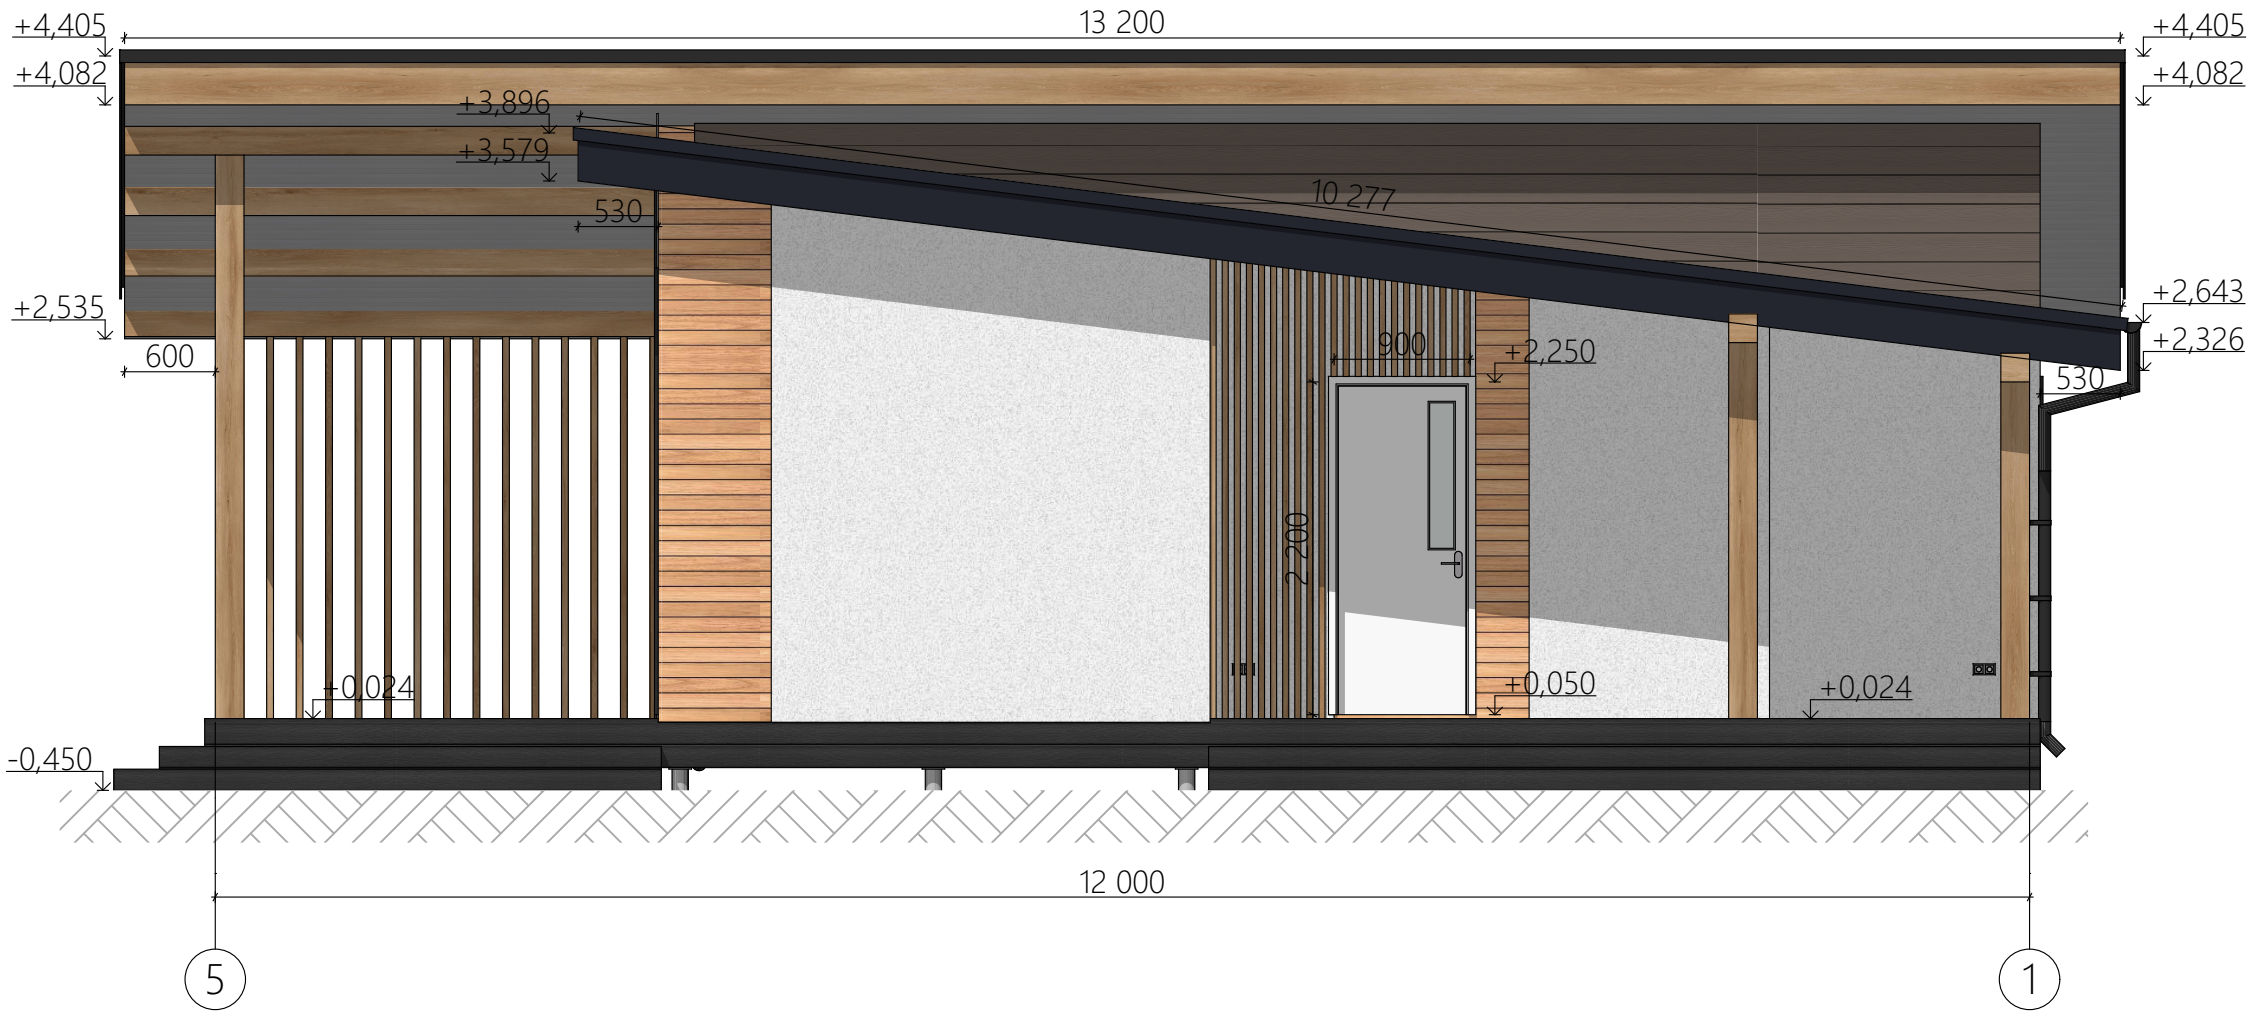

Согласовано				
Инов. № подл.	Взам. инв. №	Подп. и дата		

Лист	Изм.	№ Докум.	Подп.	Дата

Московская область, Одинцовский городской округ, село Каринское,		50:20:0080803:1001


Фасад 5-1

#Название Организации

Лист
23

Фасад А-Д

1:50

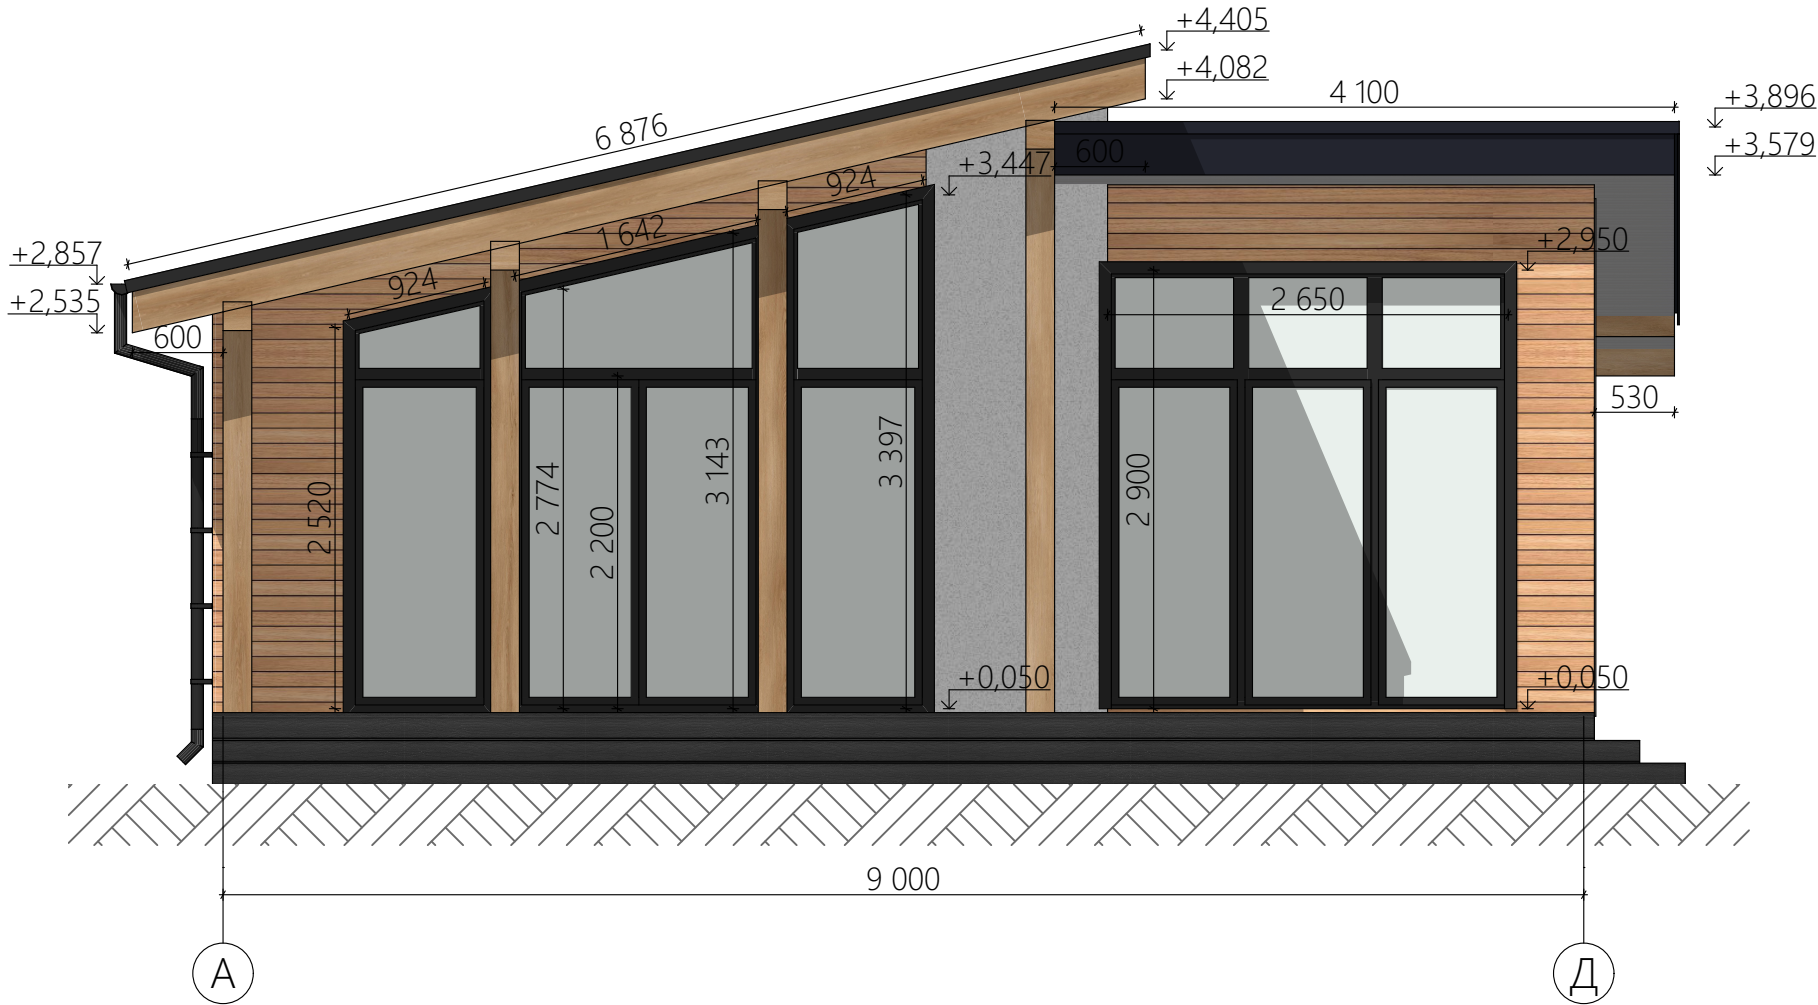

Условные обозначения:

- Фиброцементный сайдинг (RAL 7006)
- Террасная доска (Экодек кантри черный)
- Водосточная система, рамы, наличники, фальцевые листы (RAL 9005)
- Фальцевые листы, лобовая (RAL 7024)
- Дерево крашенное, лобовая доска, декоративные роейки
- Фиброцементные панели (RAL 9001)
- Планкен

Согласовано

Взам. инв. №

Подп. и дата

Инв. № подл.

Лист	Изм.	№ Докум.	Подп.	Дата

Московская область, Одинцовский городской округ, село Каринское,

50:20:0080803:1001

Фасад А-Д

#Название Организации

Лист

24

Согласовано				
Инва. № подл.	Подп. и дата	Взам. инв. №		



Лист	Изм.	№ Докум.	Подп.	Дата

Московская область, Одинцовский городской округ, село Каринское, 50:20:0080803:1001

Визуализация

#Название Организации

Согласовано

Взам. инв. №

Подп. и дата

Инв. № подл.



Лист	Изм.	№ Докум.	Подп.	Дата

Московская область, Одинцовский городской округ, село Каринское, 50:20:0080803:1001

Визуализация

#Название Организации

Согласовано

Взам. инв. №

Подп. и дата

Инв. № подл.

Лист	Изм.	№ Докум.	Подп.	Дата

Московская область, Одинцовский городской округ, село Каринское, 50:20:0080803:1001

Визуализация

#Название Организации

Согласовано					
Инва. № подл.	Подп. и дата	Взам. инв. №			



Лист	Изм.	№ Докум.	Подп.	Дата


Московская область, Одинцовский городской округ, село Каринское, 50:20:0080803:1001

Визуализация

#Название Организации

Согласовано			

Инва. № подл.	Подп. и дата	Взам. инв. №	

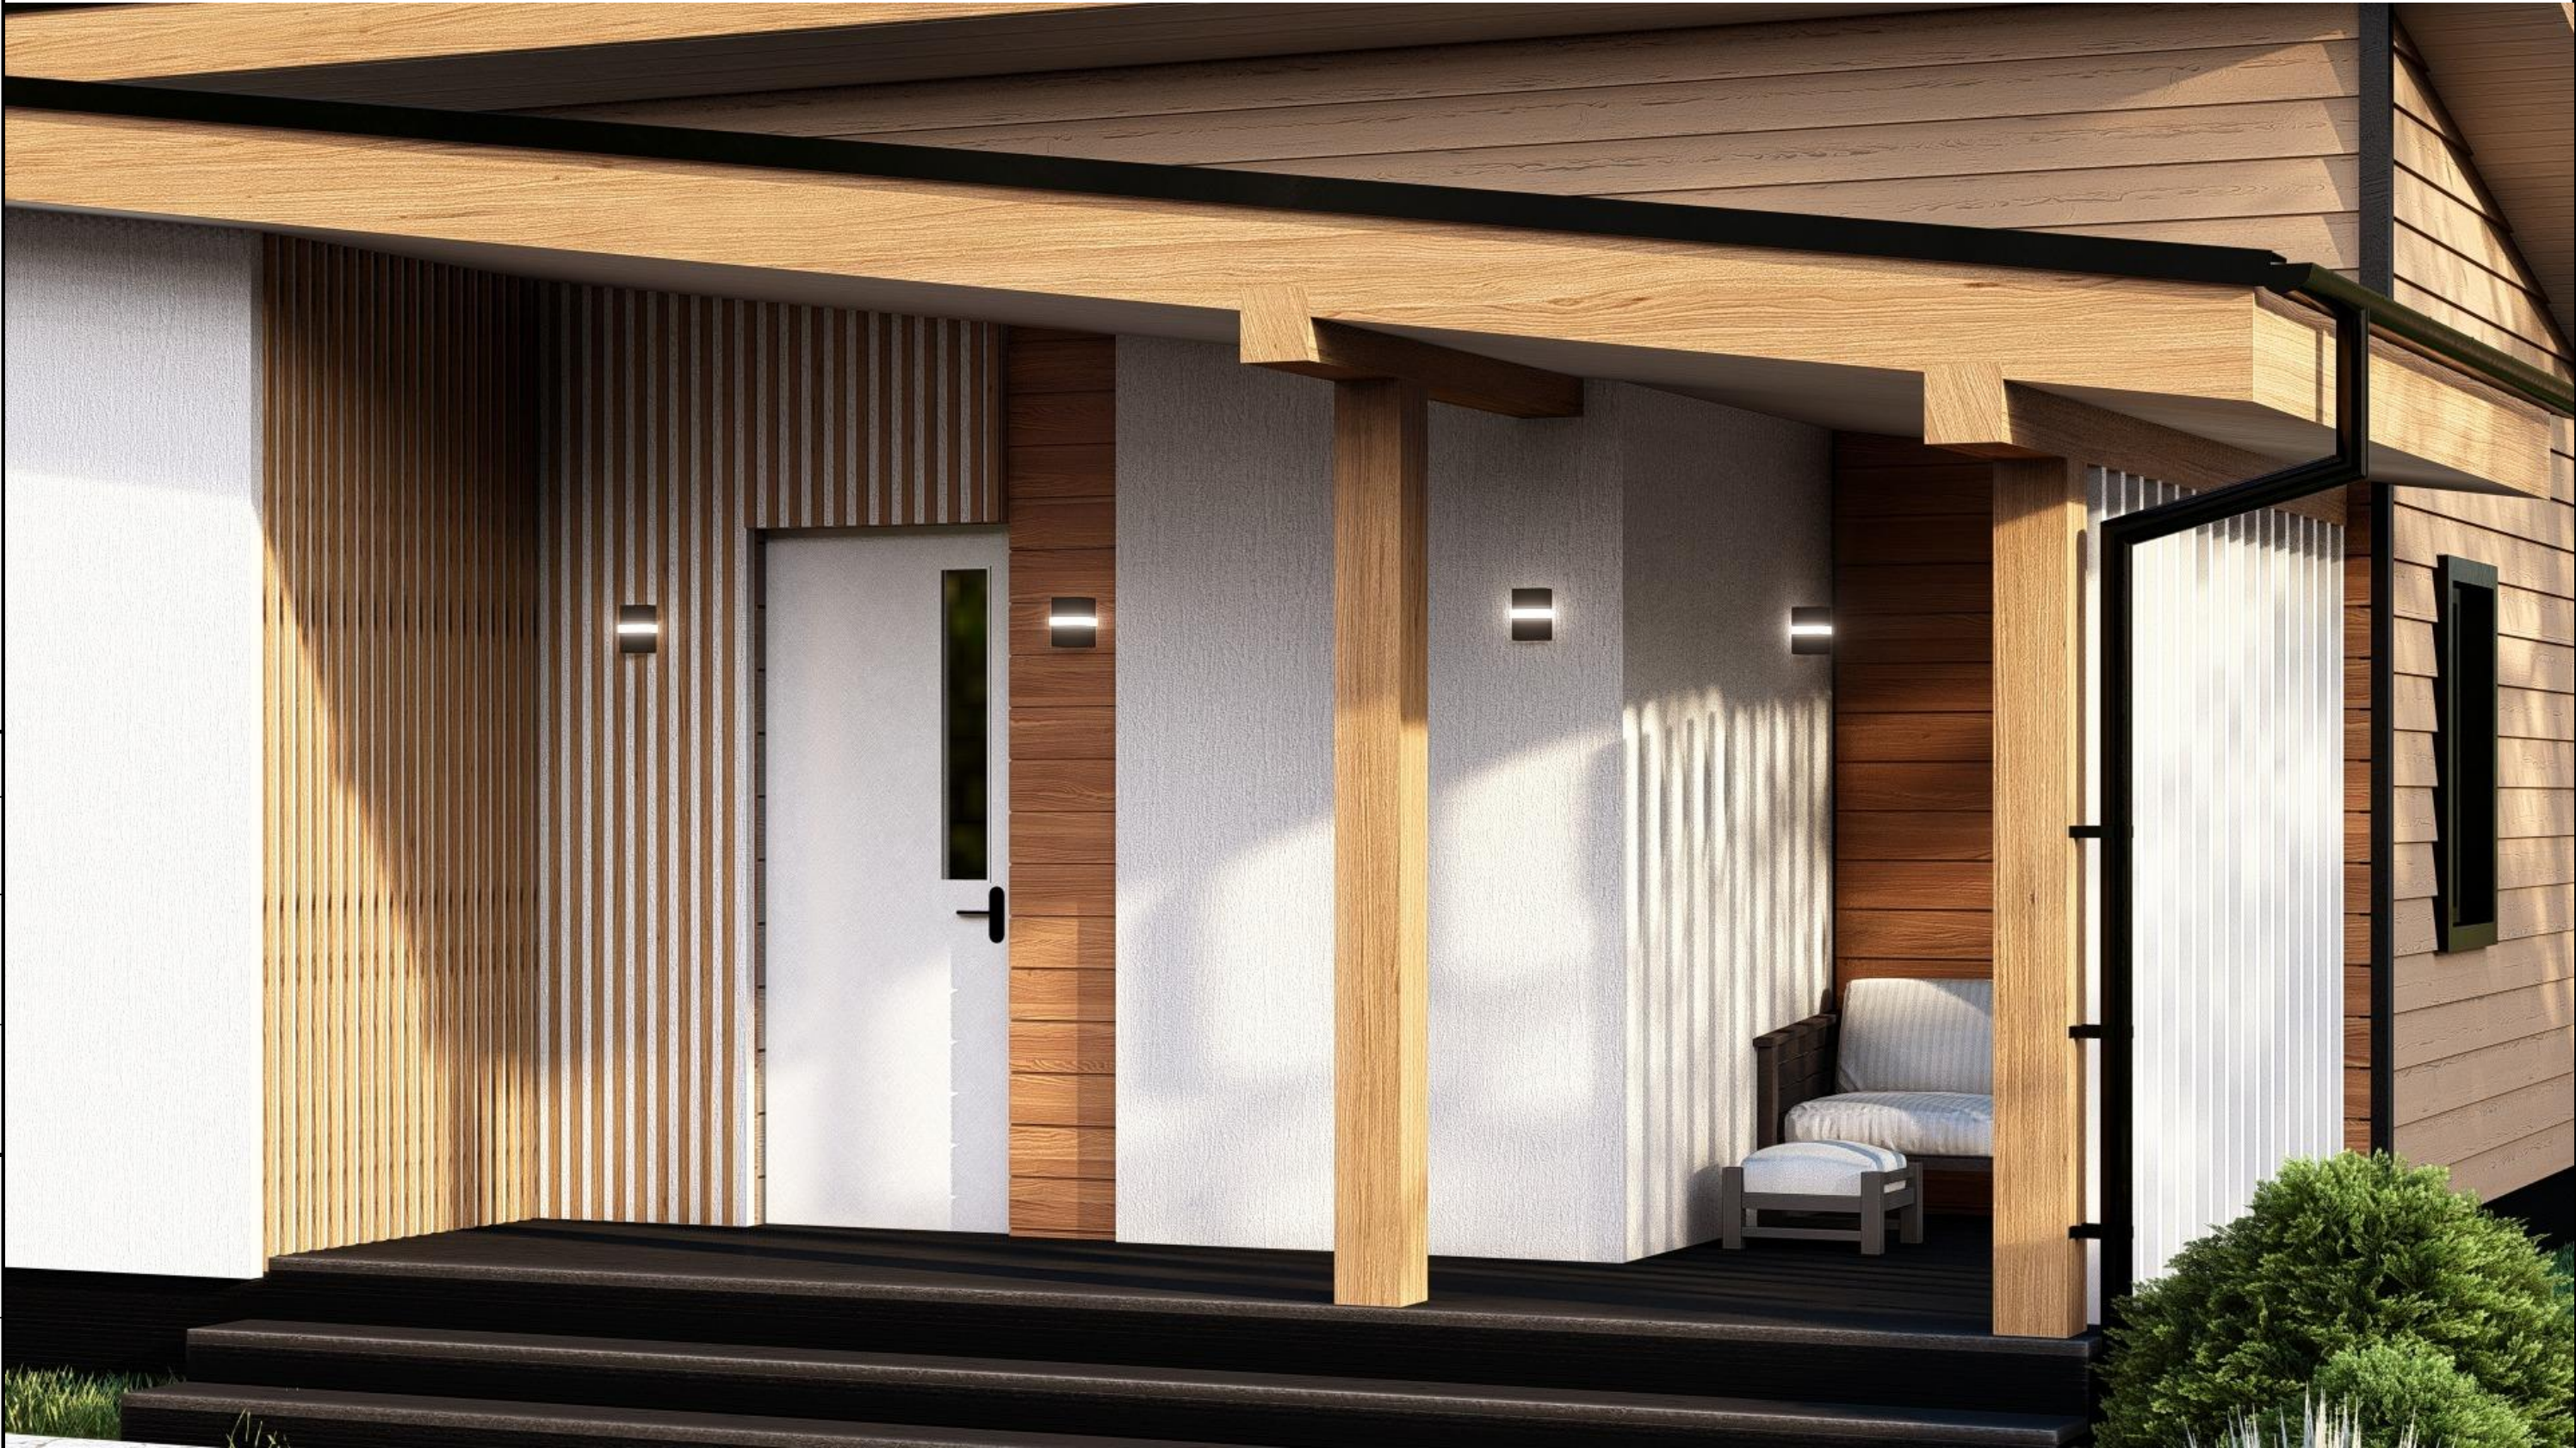

Лист	Изм.	№ Докум.	Подп.	Дата

Московская область, Одинцовский городской округ, село Каринское, 50:20:0080803:1001

Визуализация

#Название Организации

Согласовано					
Инва. № подл.	Подп. и дата	Взам. инв. №			



Лист	Изм.	№ Докум.	Подп.	Дата

Московская область, Одинцовский городской округ, село Каринское, 50:20:0080803:1001

Визуализация

#Название Организации