


План покрытия стен

1:70

Экспликация покрытий стен

№	Наименование	Условное обозначение
1	Планкен (20мм)	
2	Имитация бруса (20мм)	
3	Керамогранит (10мм)	

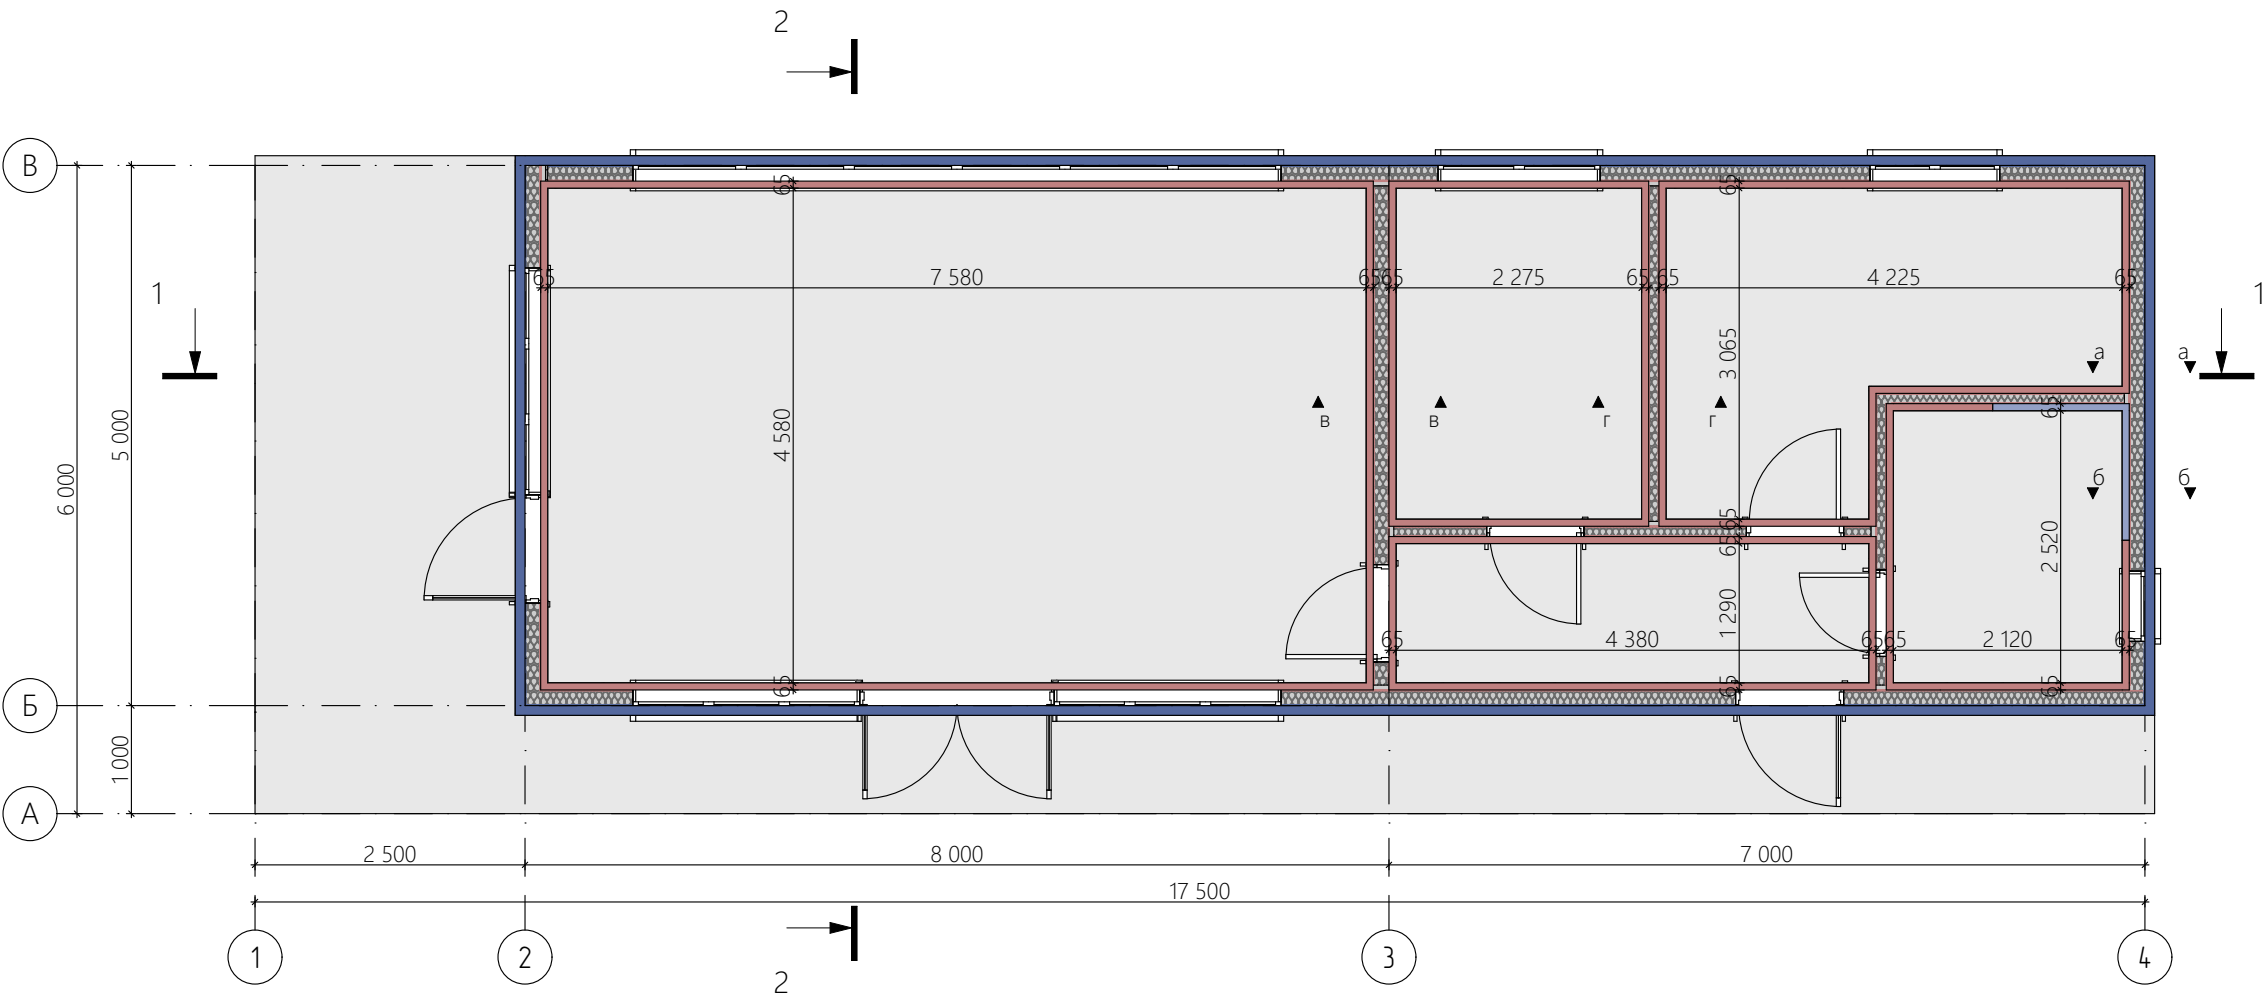

Согласовано				
Инов. № подл.	Подп. и дата	Взам. инв. №		

Лист	Изм.	№ Докум.	Подп.	Дата