


План размещения розеток

1:70

Экспликация розеток		
Наименование	2д-вид	Кол-во
Розетка 220v (рамка 1 секции)		5
Розетка 220v (рамка 2 секции)		5
Розетка 220v+ТВ розетка (рамка 2 секции)		1
Эл. вывод		3
		14
Примечание:		
1. Схема размещения розеток является рекомендательной и требует согласования с заказчиком по месту.		
2. Все высоты даны от чистового пола.		
3. Все указанные размеры даются до центра позиций.		
4. Отметки розеток, выключателей, выводов и др. оборудования, являются предварительными и уточняются после выбора финишных материалов и мебели.		
5. Размеры уточняются дополнительно		
		Лист
		12

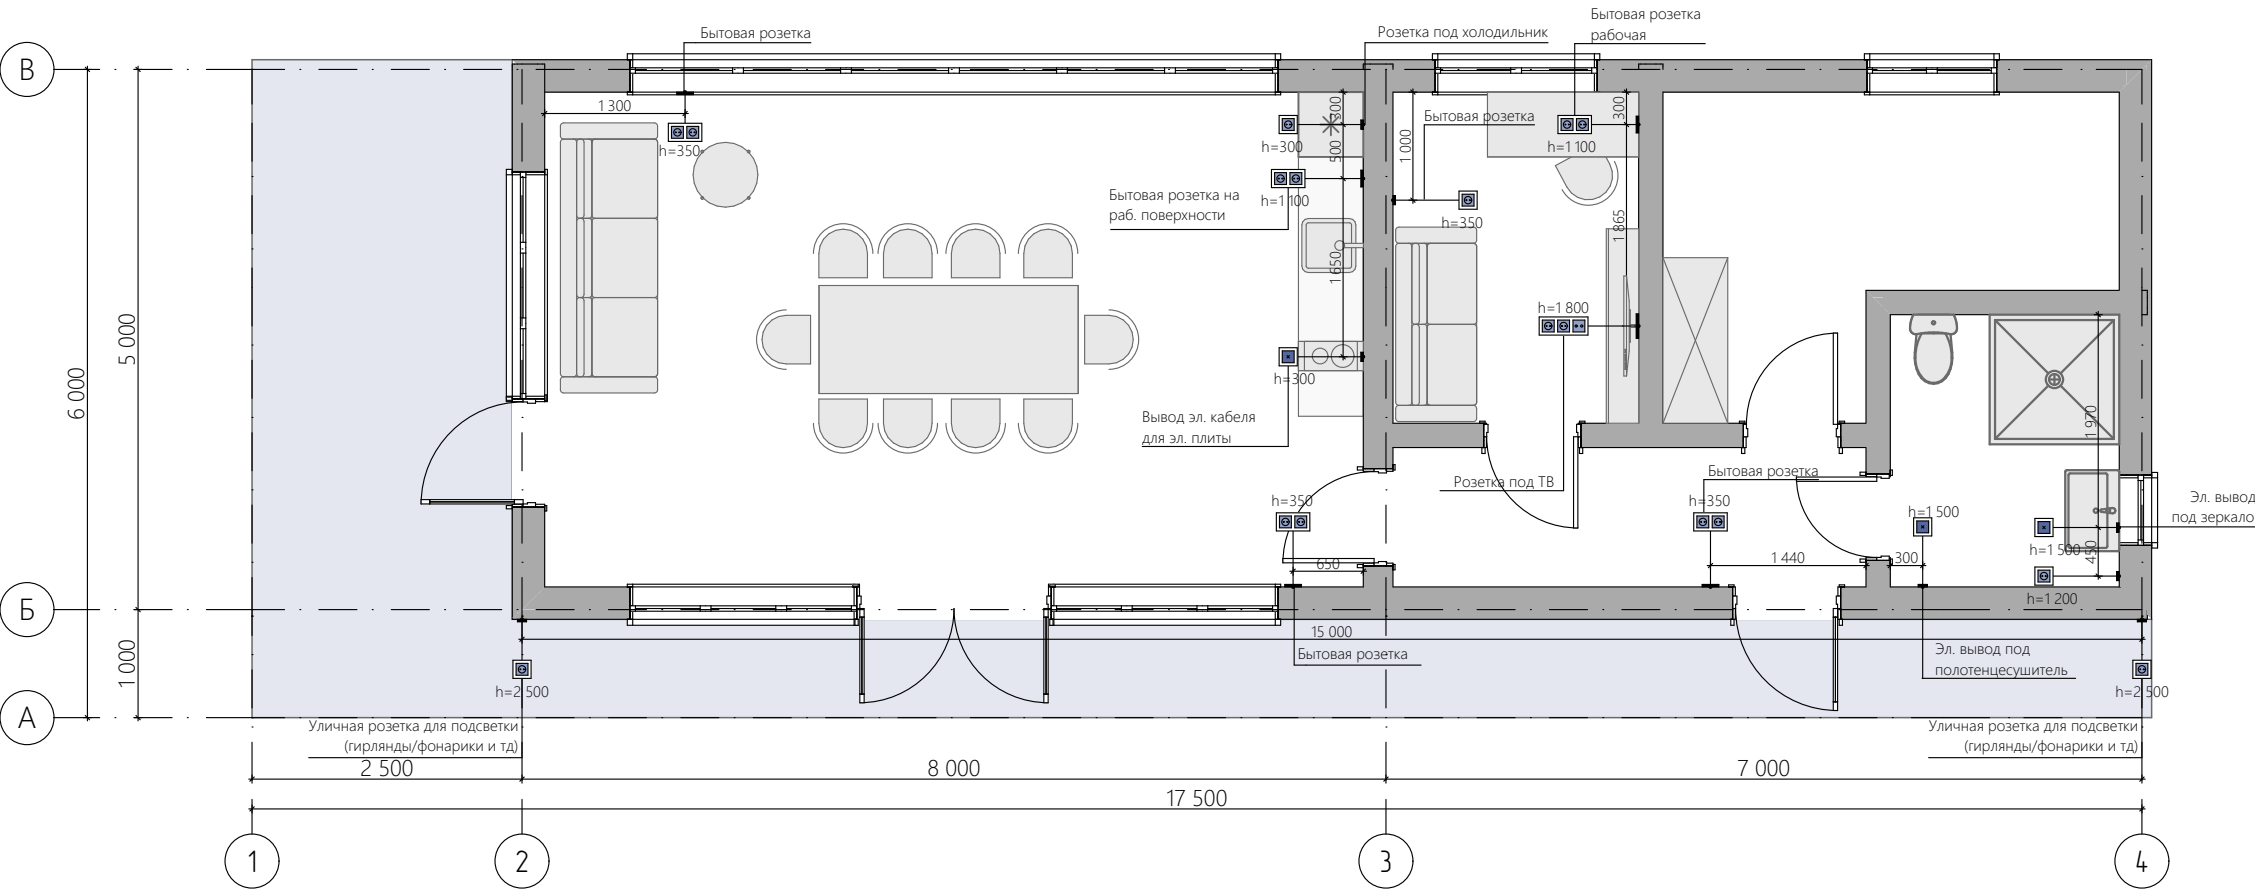

Согласовано					
И.нв. № подл.	Подп. и дата	Взам. инв. №			

Лист	Изм.	№ Докум.	Подп.	Дата

Деревня Милорадово, 161, район Коммунарка, Новомосковский административный округ, Москва

План размещения розеток