


План размещения светильников и выключателей

1:70

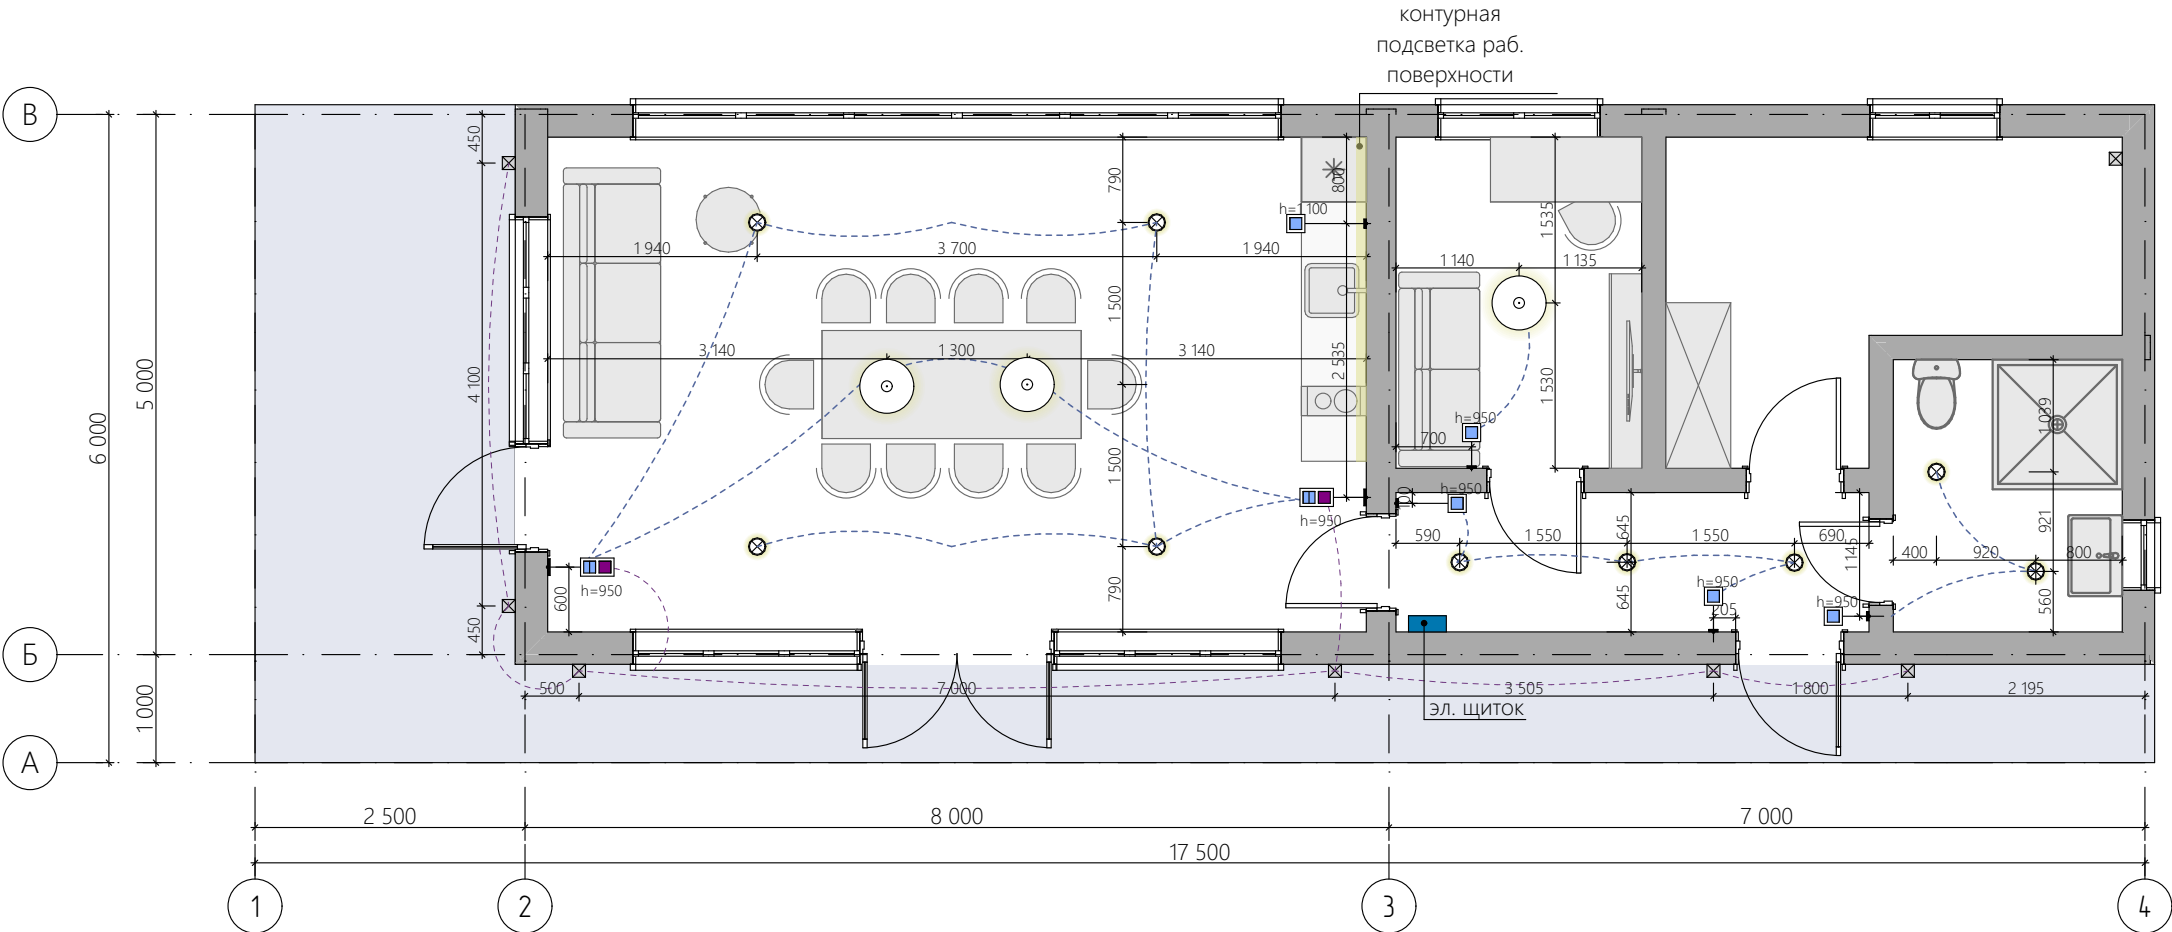

Экспликация светильников и выключателей

Наименование	2д-вид	Кол-во
Бра		1
Выключатель одно- и двухклавишный (рамка 2 секции)		2
Выключатель одноклавишный (рамка 1 секции)		5
Светильник точечный		9
Светильник подвесной		3
Уличный светильник		6
		26

Примечание:

1. Схема размещения розеток является рекомендательной и требует согласования с заказчиком по месту.

2. Все высоты даны от чистового пола.

3. Все указанные размеры даются до центра позиций.

4. Отметки розеток, выключателей, выводов и др. оборудования, являются предварительными и уточняются после выбора финишных материалов и мебели.

5. Размеры уточняются дополнительно

Согласовано				
И-нв. № подл.	Подп. и дата	Взам. инв. №		

Лист	Изм.	№ Докум.	Подп.	Дата	Деревня Милорадово, 161, район Коммунарка, Новомосковский административный округ, Москва

План размещения светильников и выключателей

		Лист
		13