


План крыши

1:70


Условные обозначения:

- Крыша беседки (уклон 25°)
- Подшив свесов беседки

Площадь крыши бани (S, м²) = 105,92м²

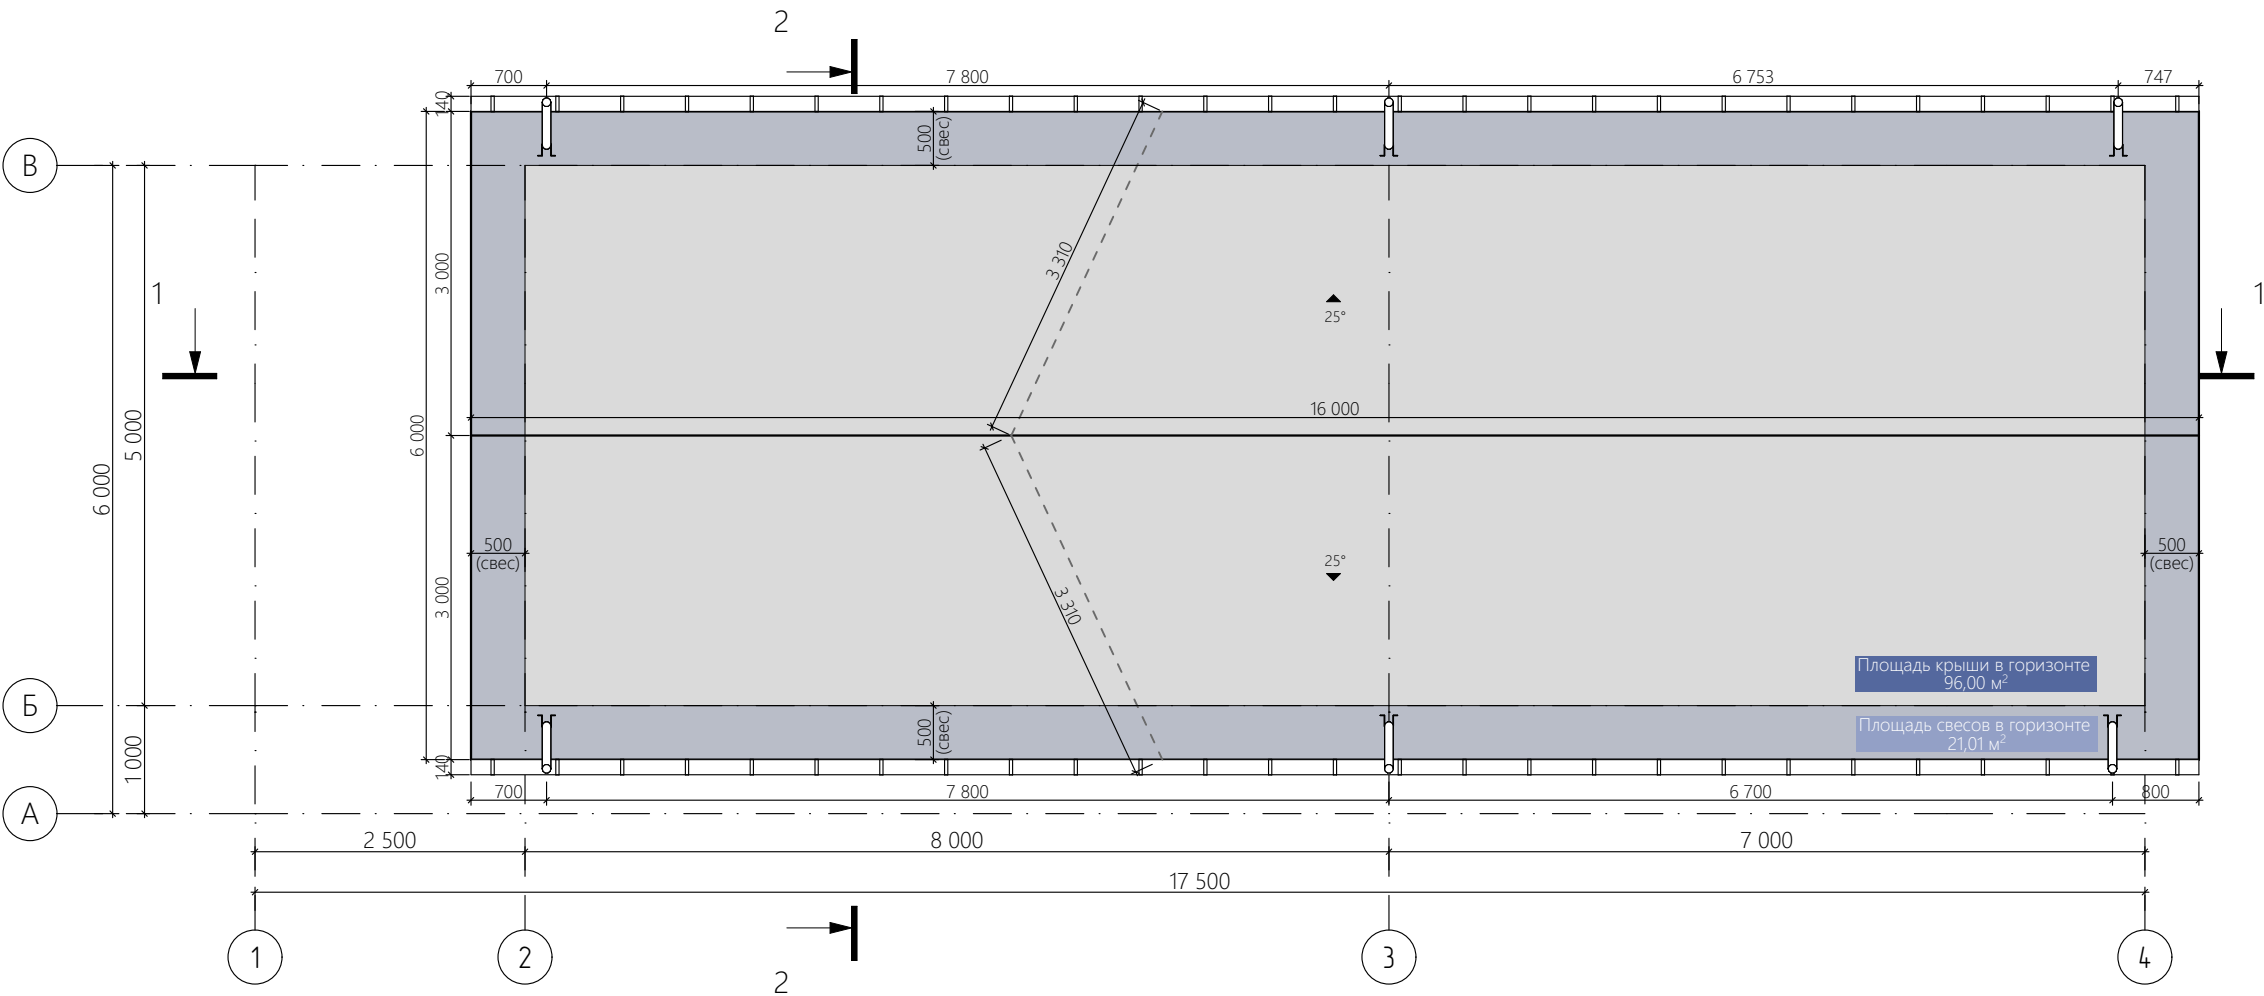

Аксонометрия крыши

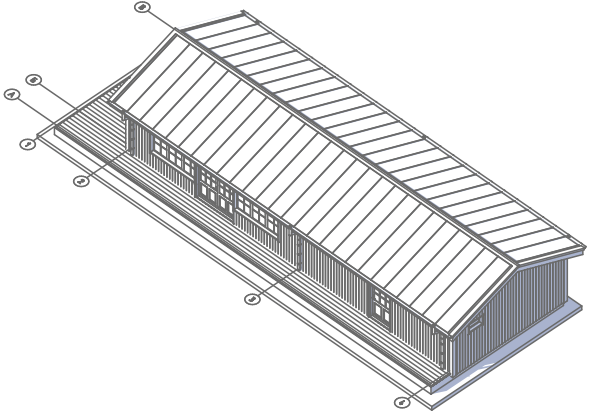

Согласовано				
И-нв. № подл.	Подп. и дата	Взам. инв. №		

Лист	Изм.	№ Докум.	Подп.	Дата

Деревня Милорадово, 161, район Коммунарка, Новомосковский административный округ, Москва

План крыши