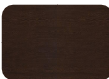



Согласовано				
Инва. № подл.	Подп. и дата	Взам. инв. №		

Фасад А-В

1:40

Условные обозначения:

-  - Планкен (темно-коричневый)
-  - Палубная доска (темно-коричневая)
-  - Водосточная система, лобовая рамы (RAL 9010)
-  - Наличники, рамы, угловые элементы (песочный)
-  - Кликфальц (темно-коричневый)

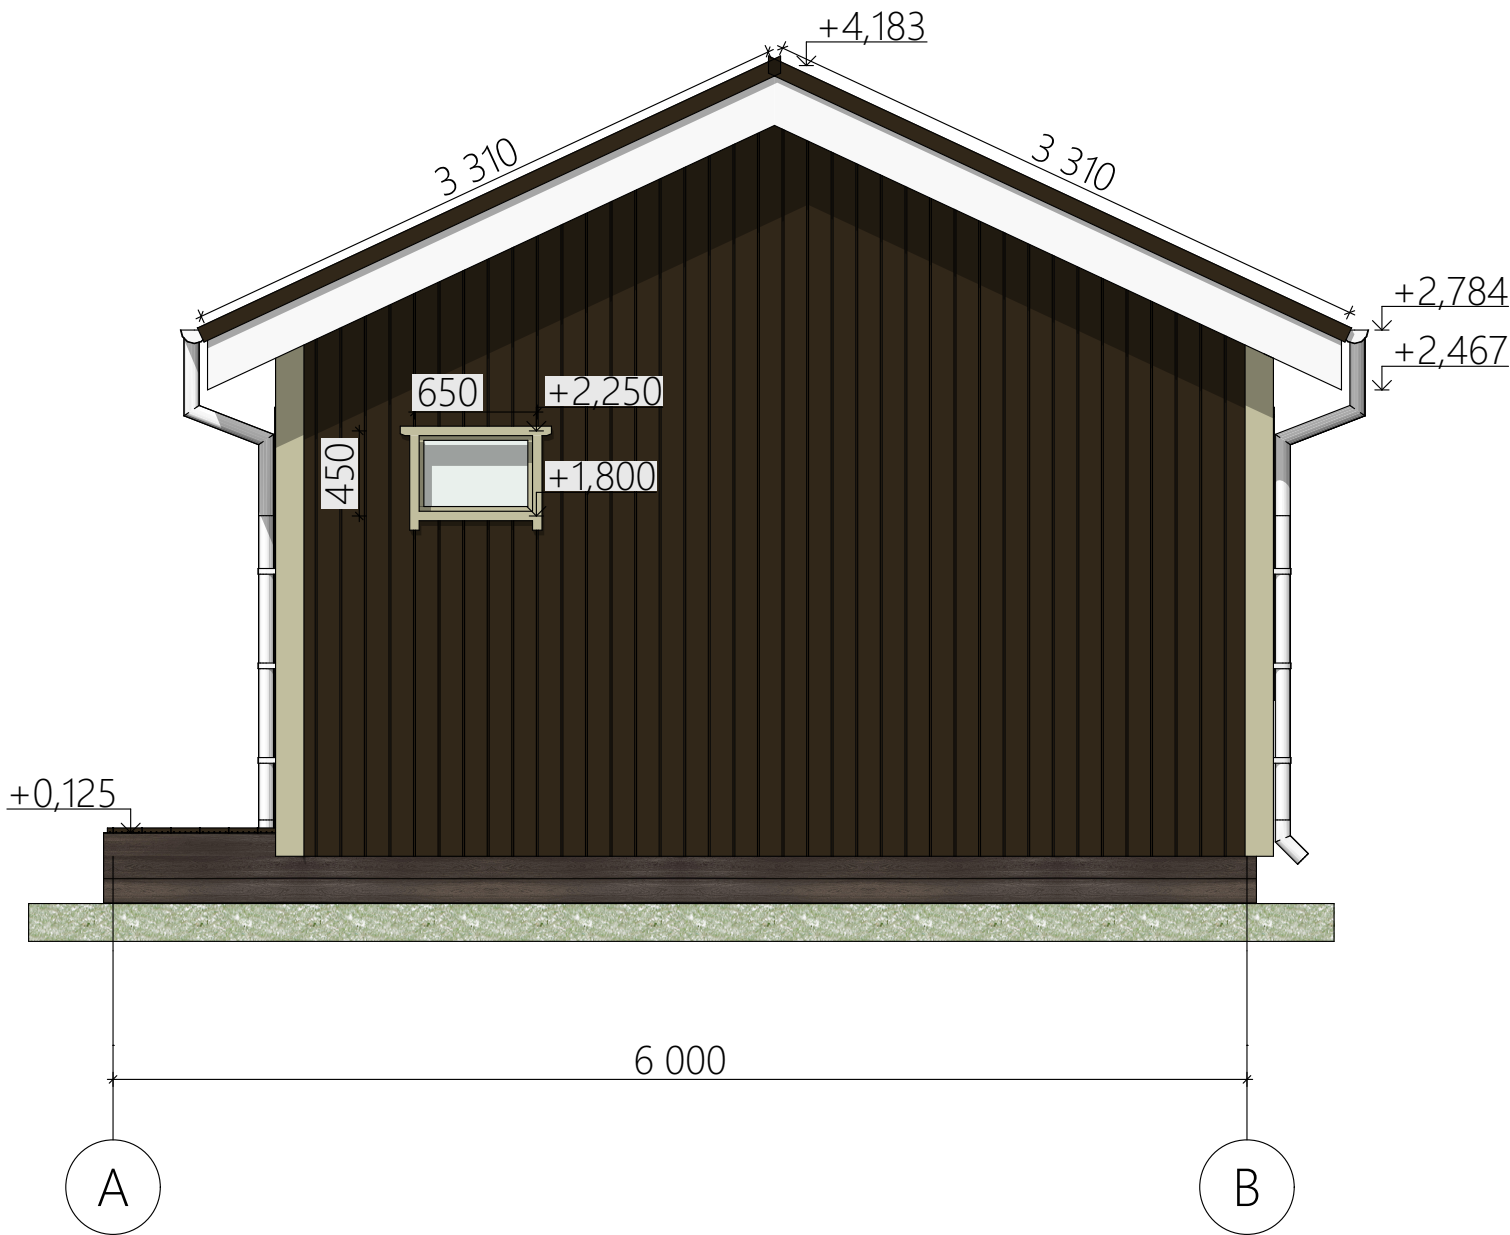

Лист	Изм.	№ Докум.	Подп.	Дата

Деревня Милорадово, 161, район Коммунарка, Новомосковский административный округ, Москва

Фасад А-В