


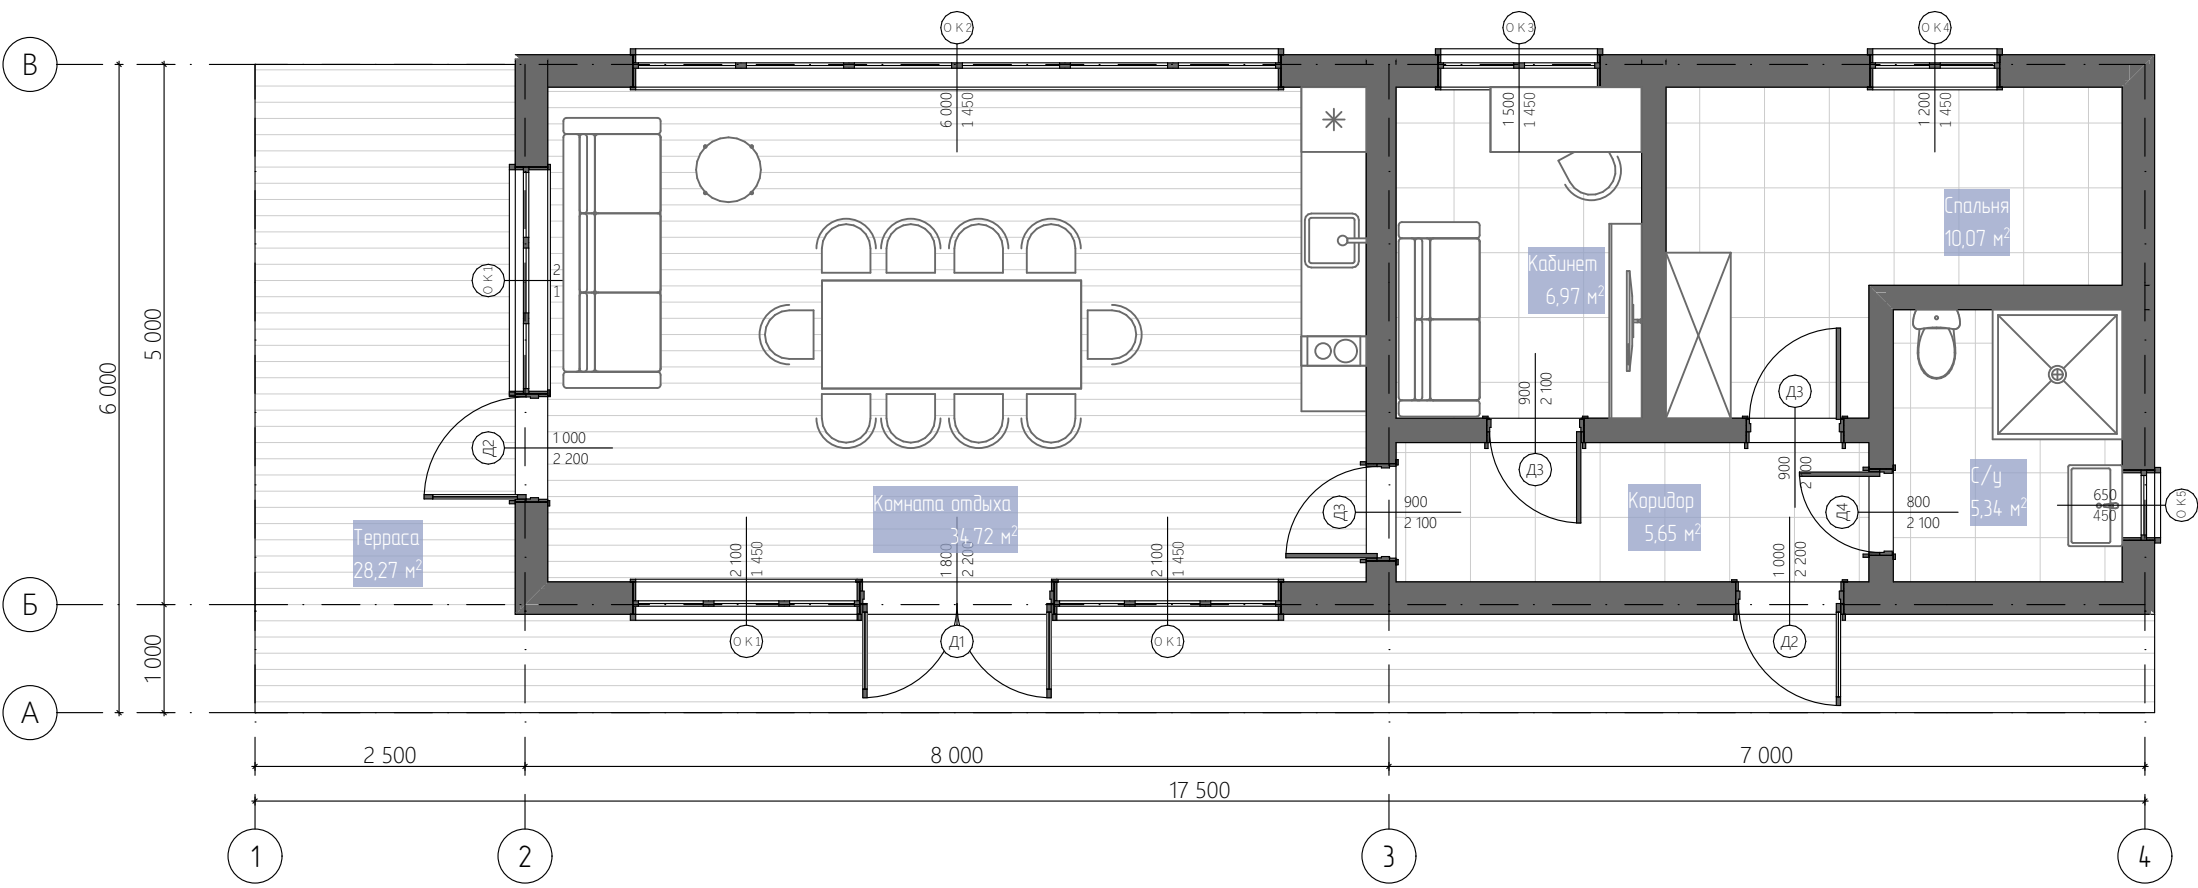

Экспликация помещений		
№	Наименование	Площадь, кв.м.
1	Комната отдыха	34,72
2	Кабинет	6,97
3	Спальня	10,07
5	Коридор	5,65
5	С/у	5,34
6	Терраса	28,27
		91,02 м²
		Площадь, кв.м.
Площадь застройки		105,00
Примечание: 1. Вся индивидуальная мебель выполняется по отдельному проекту с детальной проработкой и калькуляцией. Чертежи предоставляет фирма-изготовитель столярных изделий. 2. Данный проект отдельно согласовывается с автором проекта и непосредственно с заказчиком. 3. Цветовое решение фасада и материалов отделки показаны в проекте приблизительно. 4. Количество ступеней показано условно.		
		Лист
		4

Согласовано

Взам. инв. №

Подп. и дата

Инв. № подл.

Лист	Изм.	№ Докум.	Подп.	Дата

Деревня Милорадово, 161, район Коммунарка, Новомосковский административный округ, Москва

Маркировочный план