


Экспликация покрытий пола

№	Наименование	Площадь, м²
1	Инженерная доска	34,72
2	Керамогранит	28,14
3	Палубная доска	28,5

Примечание:

1. Приведённые цветовые решения носят рекомендательный характер. Фактический подбор оттенков и материалов выполняется на этапе реализации с учётом наличия продукции у поставщиков и утверждения заказчиком.
2. Пирог покрытия смотреть на след. листе.

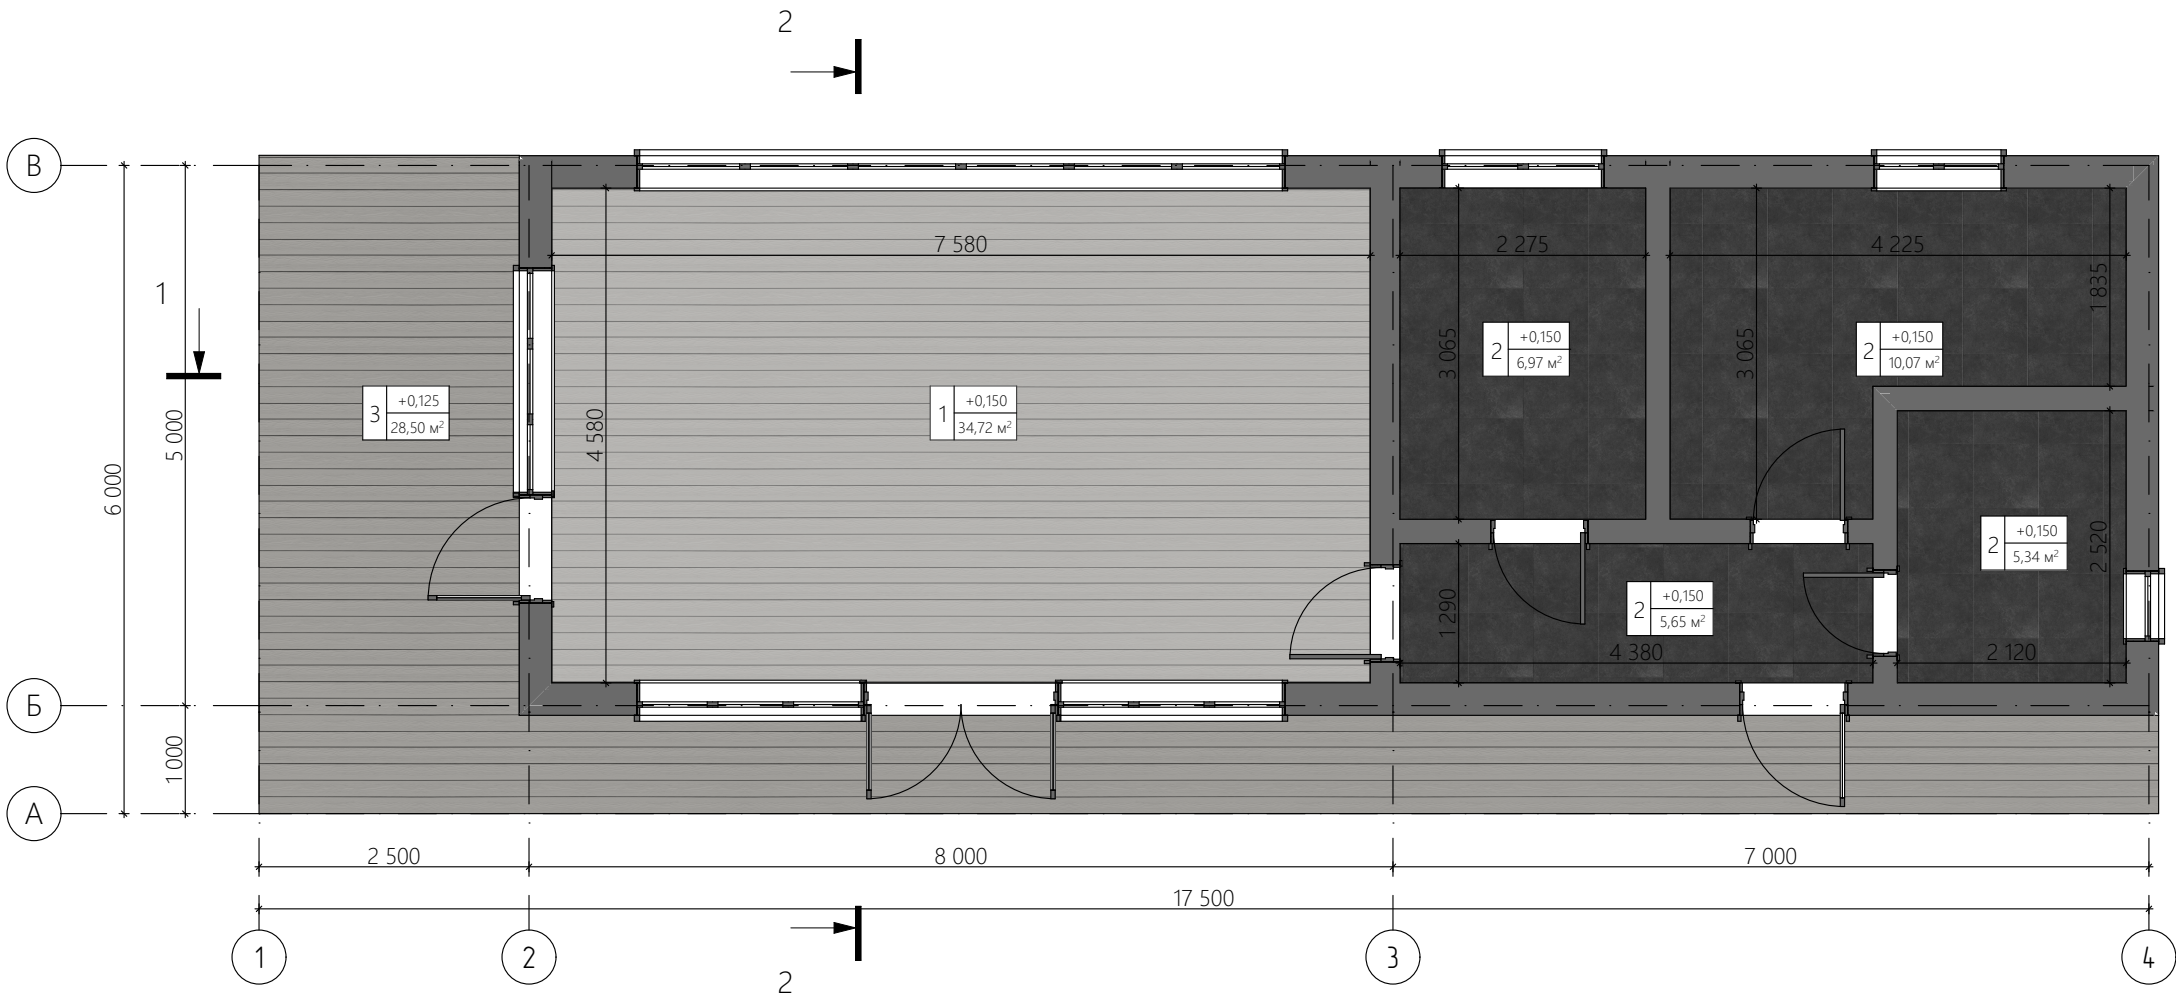

Согласовано

Взам. инв. №

Подп. и дата

Инв. № подл.

Лист	Изм.	№ Докум.	Подп.	Дата

Деревня Милорадово, 161, район Коммунарка, Новомосковский административный округ, Москва

План покрытия пола