



ARCHITECTURE/
CONSTRUCTION

Название:
Разработал:
Принял:
г. Москва



Согласовано				
Инов. № подл.	Подп. и дата	Взам. инв. №		

1. Общие данные:

1.1. Архитектурный проект разработан на основании требований и пожеланий заказчика.

Тип строения	ИЖД
Относительная отм. ±0.000	ур. верха монолитного основания
Общая площадь застройки, м2	183,10
Габаритные размеры здания, м	13,76х9,76
Этажность	1 этаж
Конструктивная схема	Керамический блок

2. Конструктивные решения:

2.1. Рабочие чертежи разработаны на основании задания на проектирование

Полезная нагрузка на перекрытие	150 кгс/м2	-
Нормативная глубина промерзания	1,2м	СП 22.13330.2016 СП 131.13330.2020
Нормативное ветровое давление	I район (23кгс/м2)	СП 22.13330.2016
Нормативный вес снегового покрова	III район (150кгс/м2)	СП 22.13330.2016
Температура наиболее холодной пятидневки	-29°С	СП 131.13330.2020

2.2. Конструктивное строение представляет собой сооружение:

- на монолитном фундаменте
- несущими стенами из керамического блока
- двускатной кровлей по деревянным стропилам

2.3. Необходимо осуществлять технический надзор за производством строительных работ. Данные по проведённым работам необходимо систематически вносить в журнал работ.

По каждому из этапов работ необходимо осуществлять входной контроль материалов и вести приёмку.

Фундамент	монолитное основание
Несущие конструкции	керамический блок (380х250х219мм)
Стропильная система	строганая доска (190х45мм)
Тип крыши	Двускатная
Покрытие кровли	Фальцевая черепица

2.4. Все деревянные конструкции обработать огне-биозащитными септиками в соответствии со СП 28.13330.2017 "Защита строительных конструкций от коррозии".

2.5. Кровельные работы выполнять в соответствии с требованиями фирмы производителя.

2.6. Все работы вести в строгом соответствии с требованиями СНиП 12.03.2001 "Безопасность труда в строительстве".

2.7. При выполнении всех работ строго соблюдать меры противопожарной безопасности.

2.8. Возможна замена материалов аналогами.

*Решения, принятые в проекте и отображенные в чертежах, соответствуют требованиям экологических, санитарно - гигиенических, противопожарных и других норм, действующих на территории Российской Федерации, и обеспечивают безопасную для жизни и здоровья людей эксплуатацию объекта при соблюдении предусмотренных рабочих чертежей и мероприятий.

Лист	Изм.	№ Докум.	Подп.	Дата

Адрес:

Пояснительная записка

#Название Организации

Согласовано				
Инв. № подл.	Подп. и дата	Взам. инв. №		

Лист	Наименование	Примечание
1	Пояснительная записка	
2	Ведомость чертежей	
3	Визуализация №1	
4	Схема планировочной организации земельного участка	
5	Маркировочный план	
6	Размерный план	
7	План расстановки мебели и оборудования	
8	Зд-разрез	
9	План кровли дома	
10	План кровли террасы	
11	Разрез 1-1	
12	Разрез 2-2	
13	Ведомость оконных проёмов (начало)	
14	Ведомость оконных проёмов (окончание)	
15	Ведомость дверных проёмов	
16	Цветовое решение; Фасад в осях В-А	
17	Цветовое решение; Фасад в осях З-1	
18	Цветовое решение; Фасад в осях А-В	
19	Цветовое решение; Фасад в осях 1-3	

В основу архитектурно-планировочных решений положены требования технологических заданий и требования норм и правил строительного проектирования, действующих на территории РФ.

Основные параметры и требования разработаны на основании пожеланий и требований заказчика.

Архитектурные решения приняты в соответствии со следующими нормативными документами:

- Градостроительный кодекс российской федерации.
- Земельного Кодекса Российской Федерации.
- Федеральный закон от 22.07.2008 N 123 - ФЗ (ред. от 29.07.2017)"Технический регламент о требованиях пожарной безопасности.
- Федеральный закон № 384 - ФЗ «Технический регламент о безопасности зданий и сооружений».
- ГОСТ Р 21.1101-2013.«Основные требования к проектной и рабочей документации».
- Постановление правительства РФ от 16.02.2008 № 87 «Положение о составе разделов проектной документации и требованиях к их содержанию».
- СП 42.13330.2011 «Градостроительство. Планировка и застройка городских и сельских поселений».
- СП 131.13330.2018 «СНиП 23-01-99* Строительная климатология».
- СП 20.13330.2016 «СНиП 2.01.07-85* Нагрузки и воздействия».
- СП 22.13330.2016 «СНиП 2.02.01-83* Основания зданий и сооружений».
- СП 70.13330.2012 (с изменениями №1) «СНиП 3.03.01-87 Несущие и ограждающие конструкции».
- СП 64.13330.2017 «СНиП II-25-80 Деревянные конструкции».
- СП 17.13330.2017 «СНиП II-26-76 Кровли».
- СП 29.13330.2011 «СНиП 2.03.13-88 Полы».
- СП 28.13330.2017 «СНиП 2.03.11-85 Защита строительных конструкций от коррозии».
- СП 50.13330.2012 «СНиП 23-02-2003 Тепловая защита зданий».

Лист	Изм.	№ Докум.	Подп.	Дата

Адрес:	Ведомость чертежей	#Название Организации	Лист
			2



Согласовано			



Инв. № подл.	Подп. и дата	Взам. инв. №	

Лист	Изм.	№ Докум.	Подп.	Дата

Адрес:

Визуализация №1

#Название Организации

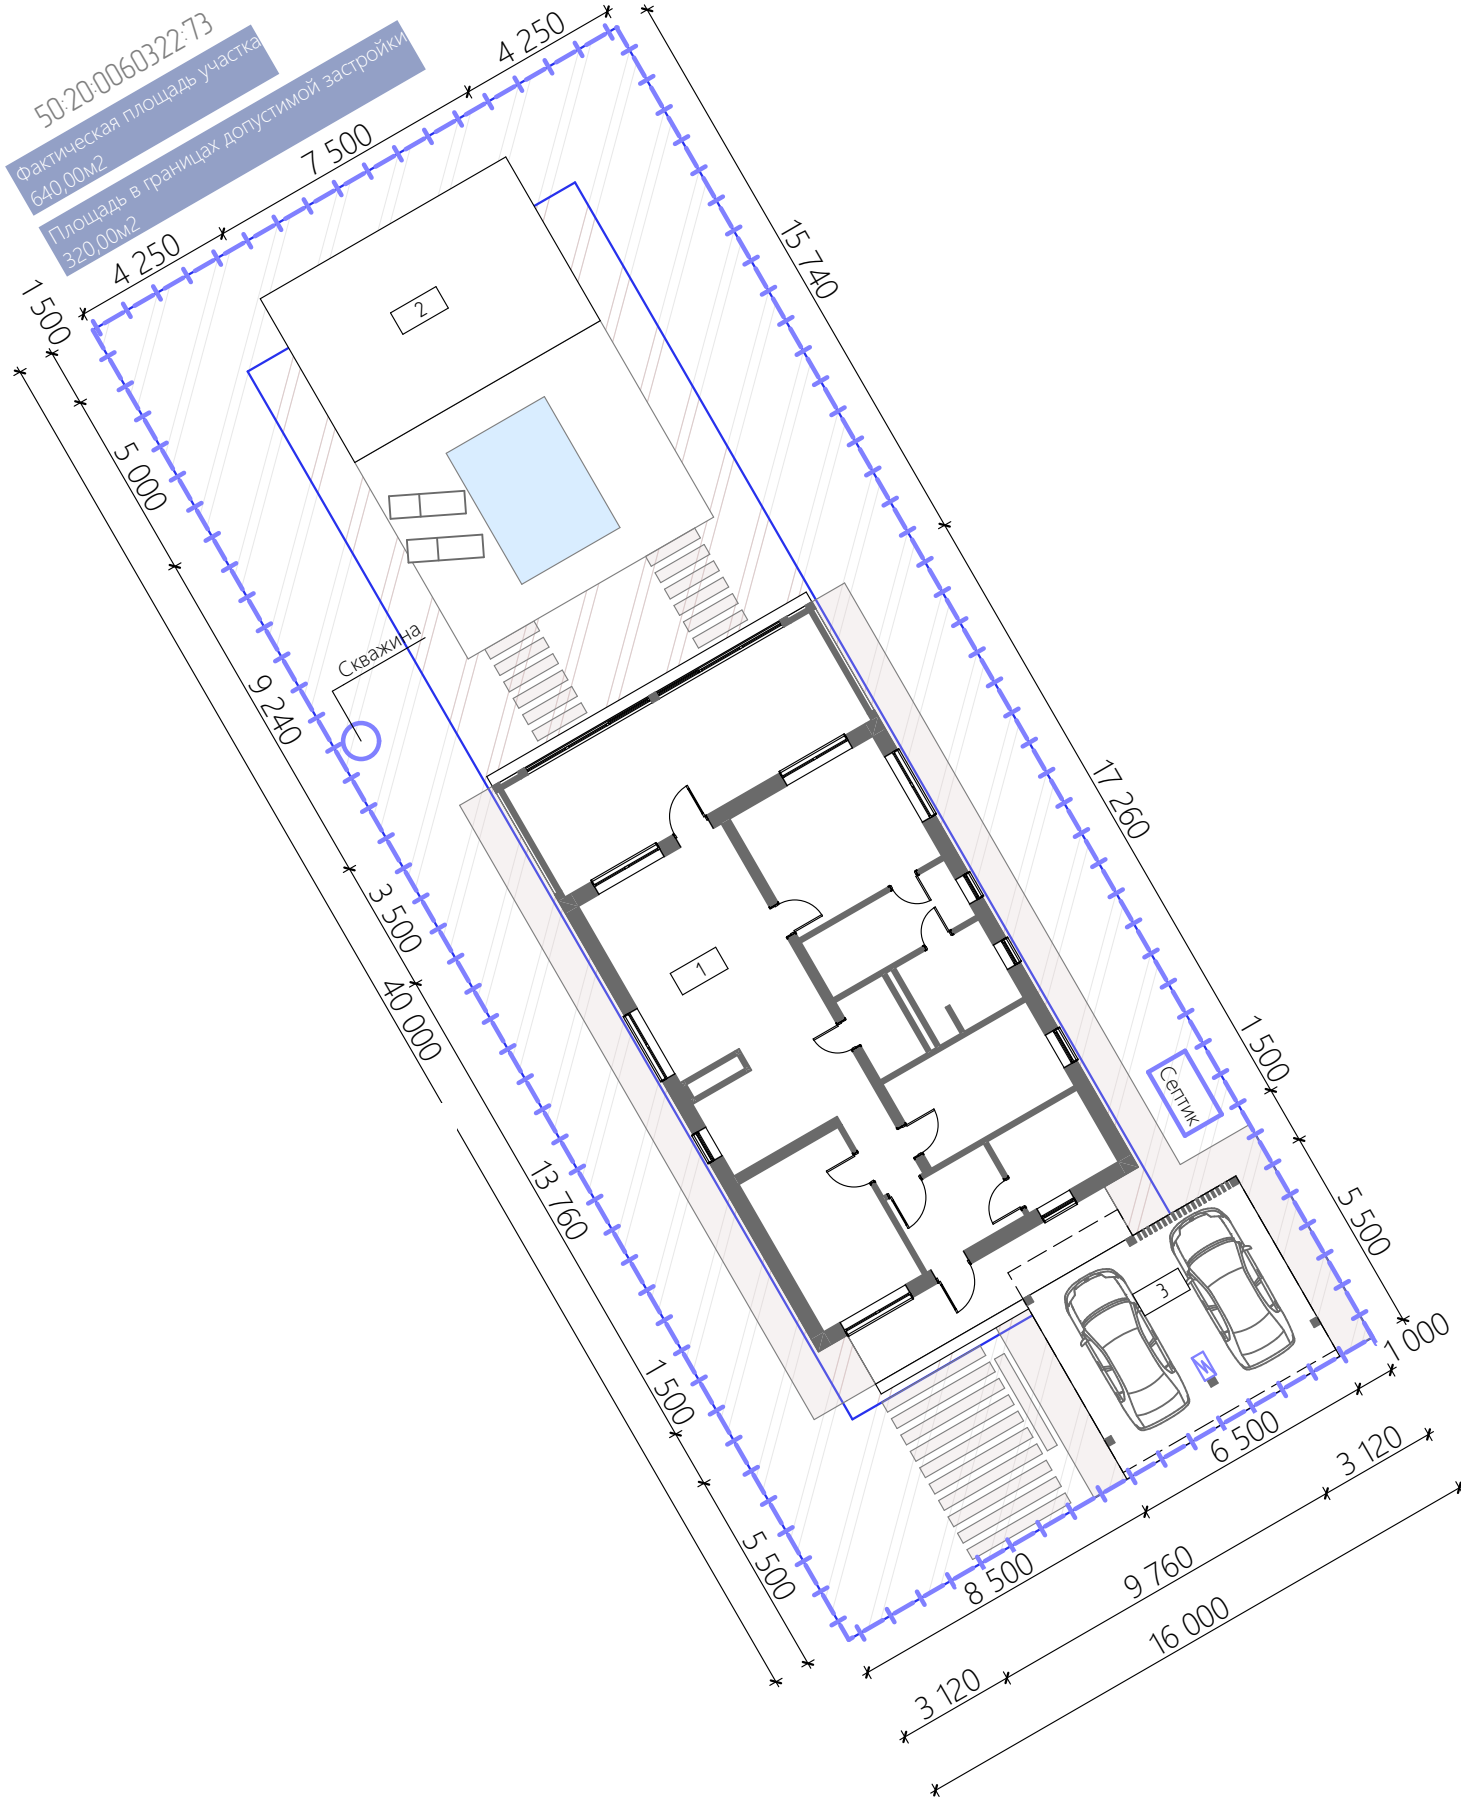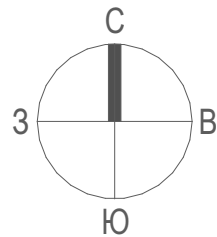

Условные обозначения:

- Граница участка
- Граница застройки участка
- 1 - Индивидуальный жилой дом
- 2 - Банный комплекс
- 3 - Навес под 2 м/м

Технико-экономические показатели

Наименование	Площадь, м²
Общая площадь застройки (ИЖД+баня)	
Площадь участка	640,00
Площадь застройки (ИЖД)	183,1

Согласовано				

И-нв. № подл.	Подп. и дата	Взам. инв. №

Лист	Изм.	№ Докум.	Подп.	Дата


Адрес:

Схема планировочной организации земельного участка

#Название Организации

Размерный план

1:90

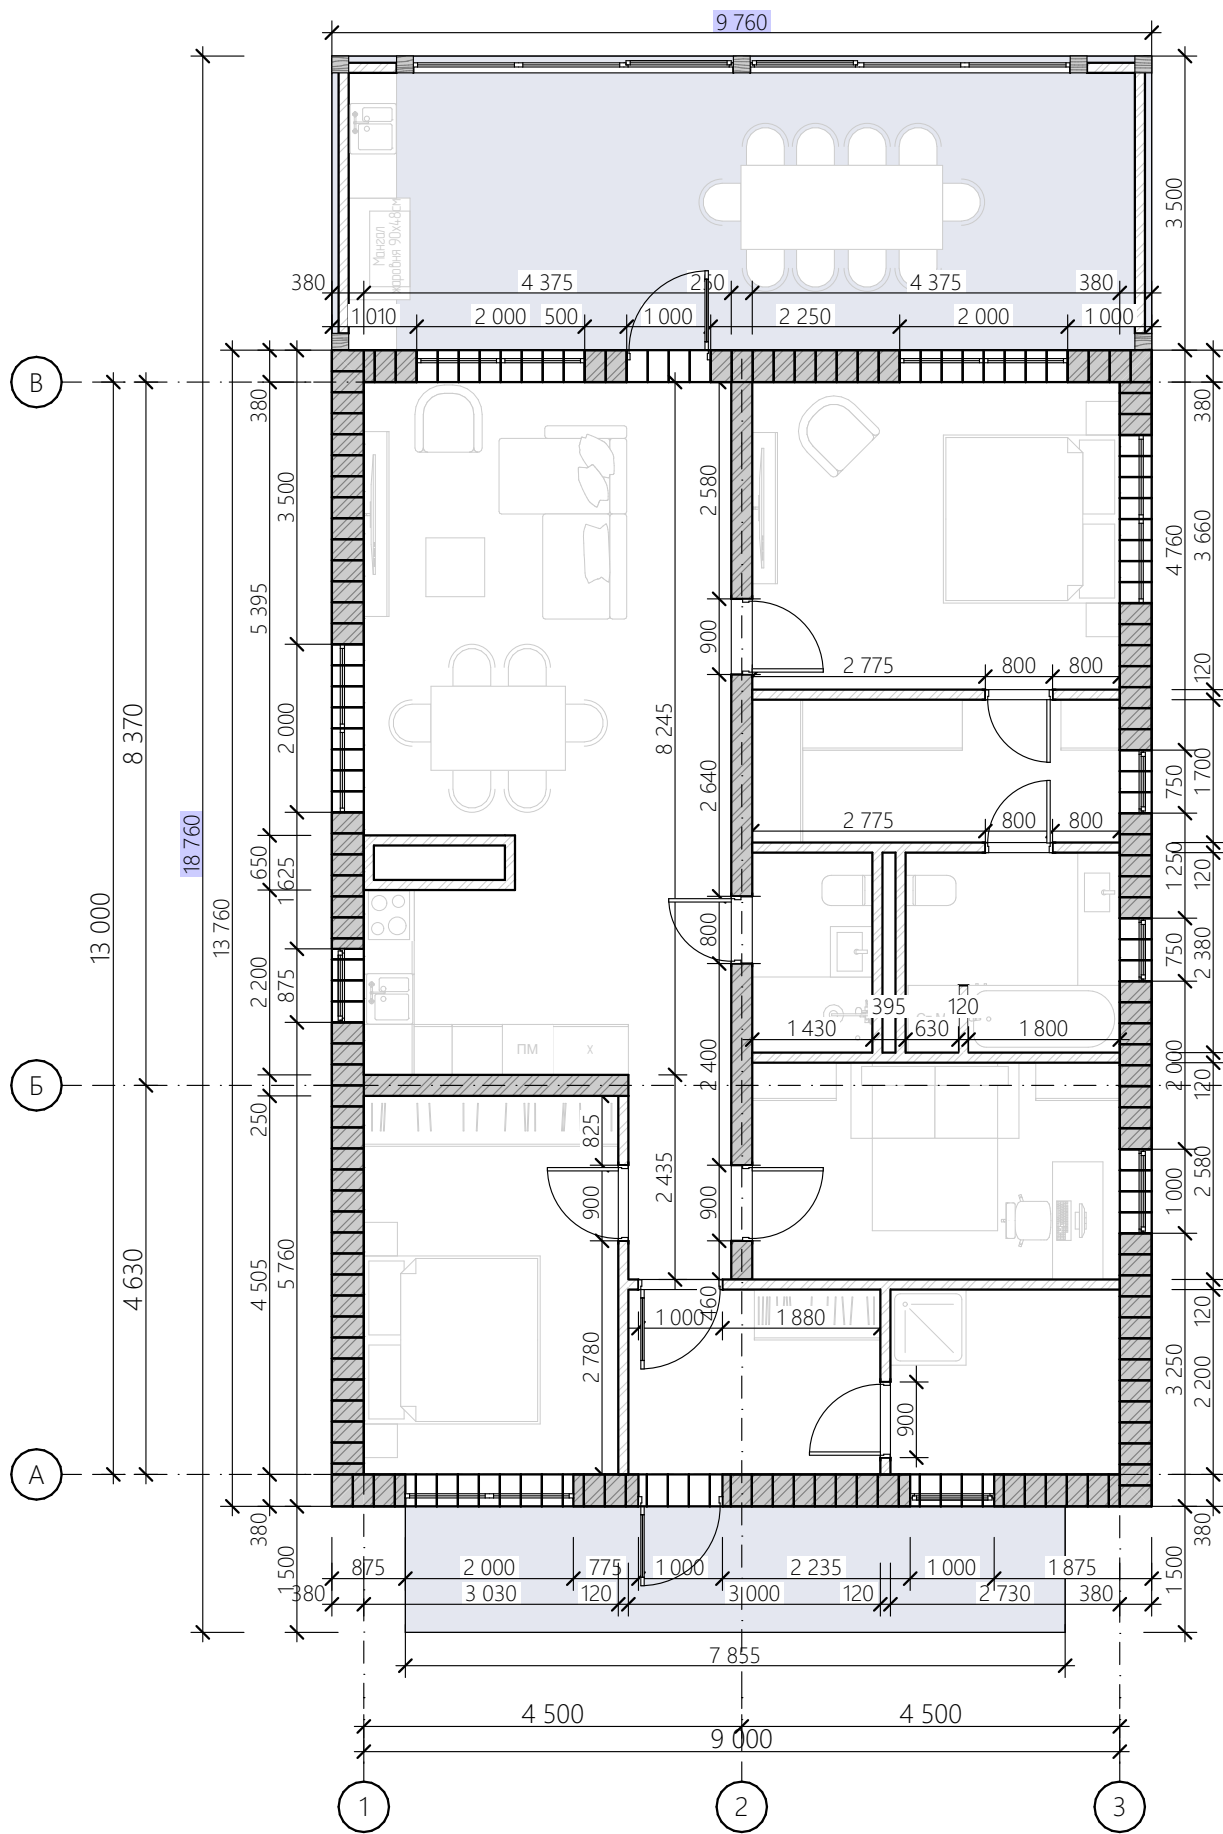

Примечание:

1. Представленные размеры
указаны без учета внешней и
внутренней отделки


Согласовано				
Инов. № подл.	Подп. и дата	Взам. инв. №		

Лист	Изм.	№ Докум.	Подп.	Дата

Адрес:

Размерный план

#Название Организации

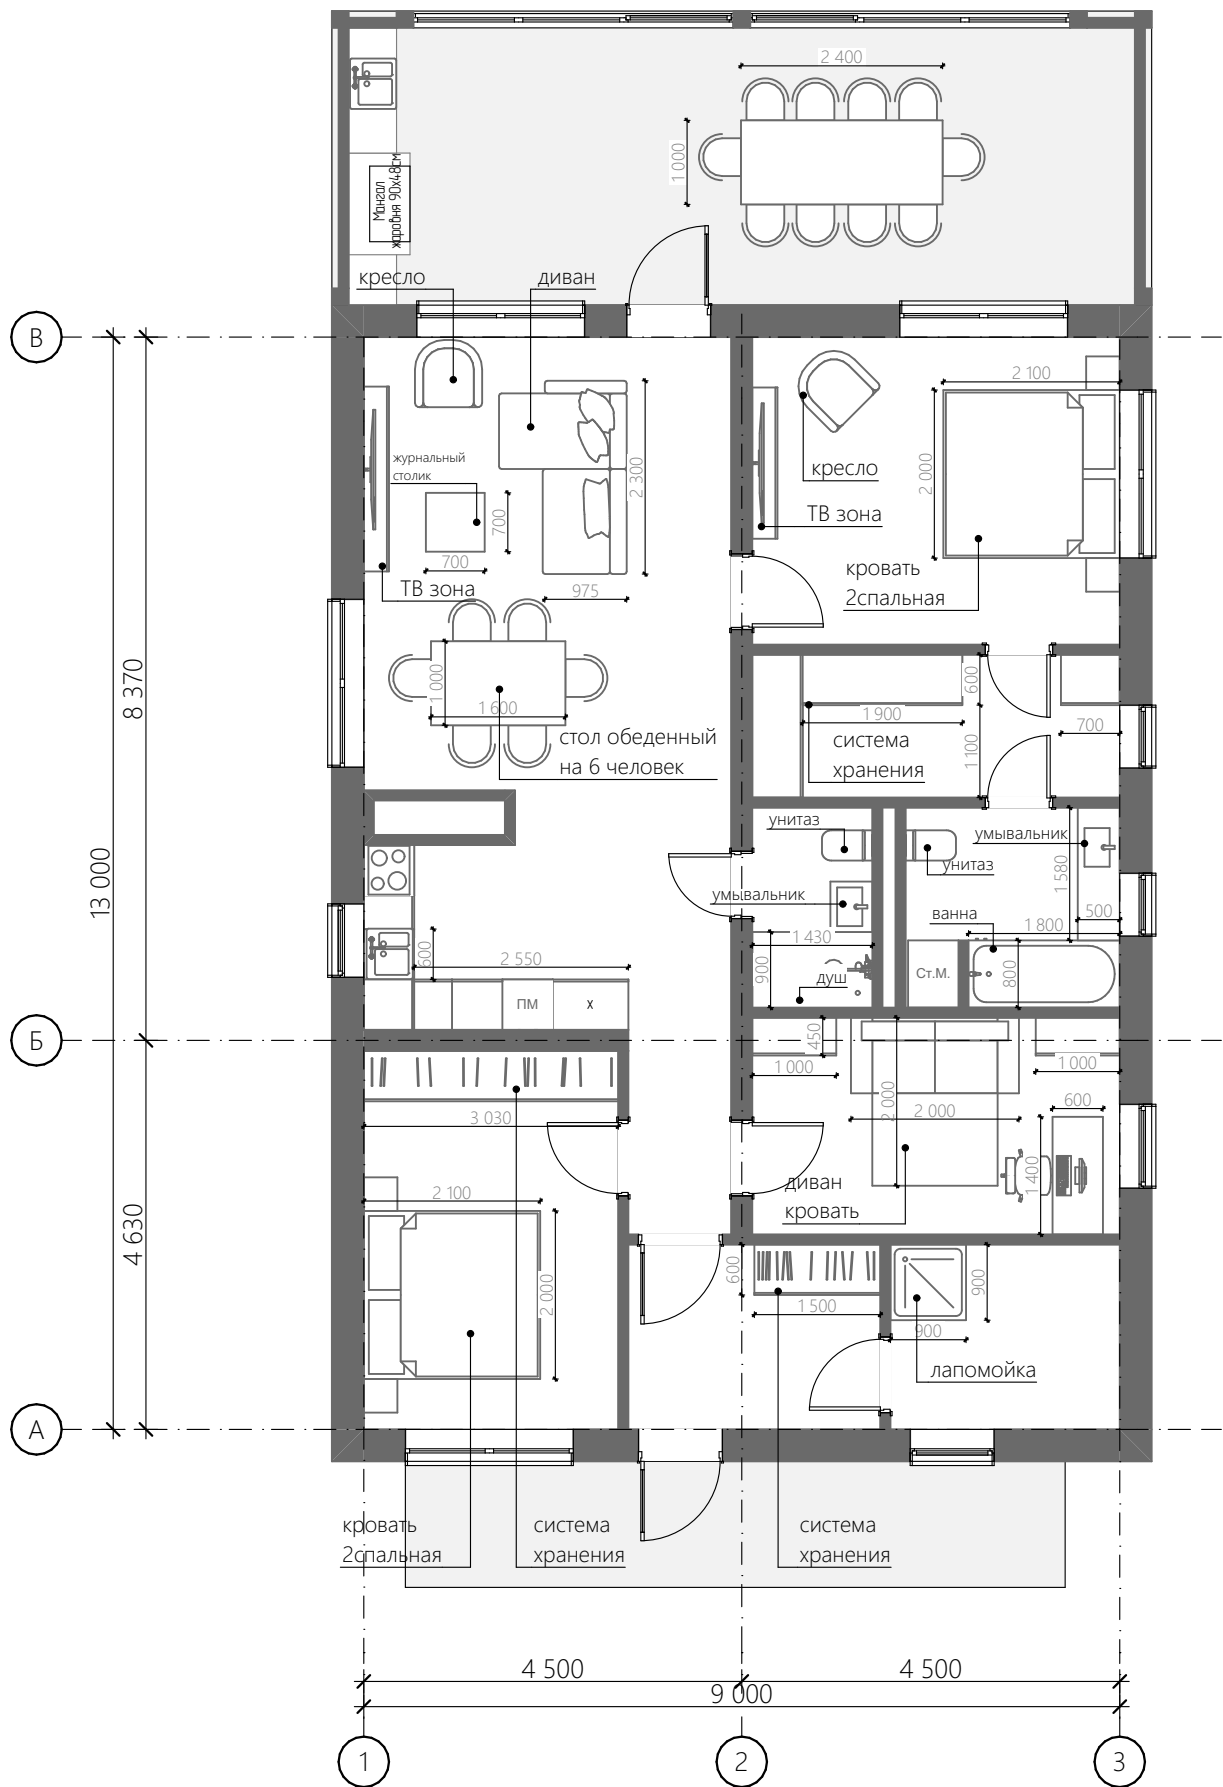

Примечание:

1. Вся индивидуальная мебель выполняется по отдельному проекту с детальной проработкой и калькуляцией. Чертежи предоставляет фирма-изготовитель столярных изделий.

2. Финальные размеры мебели и оборудования указаны ориентировочно — для точной компоновки требуется разработка дизайн-проекта.

Согласовано				
Инов. № подл.	Подп. и дата	Взам. инв. №		

Лист	Изм.	№ Докум.	Подп.	Дата

Адрес:

План расстановки мебели и оборудования

#Название Организации


7

Согласовано

Инва. № подл. Подп. и дата Взам. инв. №

Лист	Изм.	№ Докум.	Подп.	Дата

Адрес:

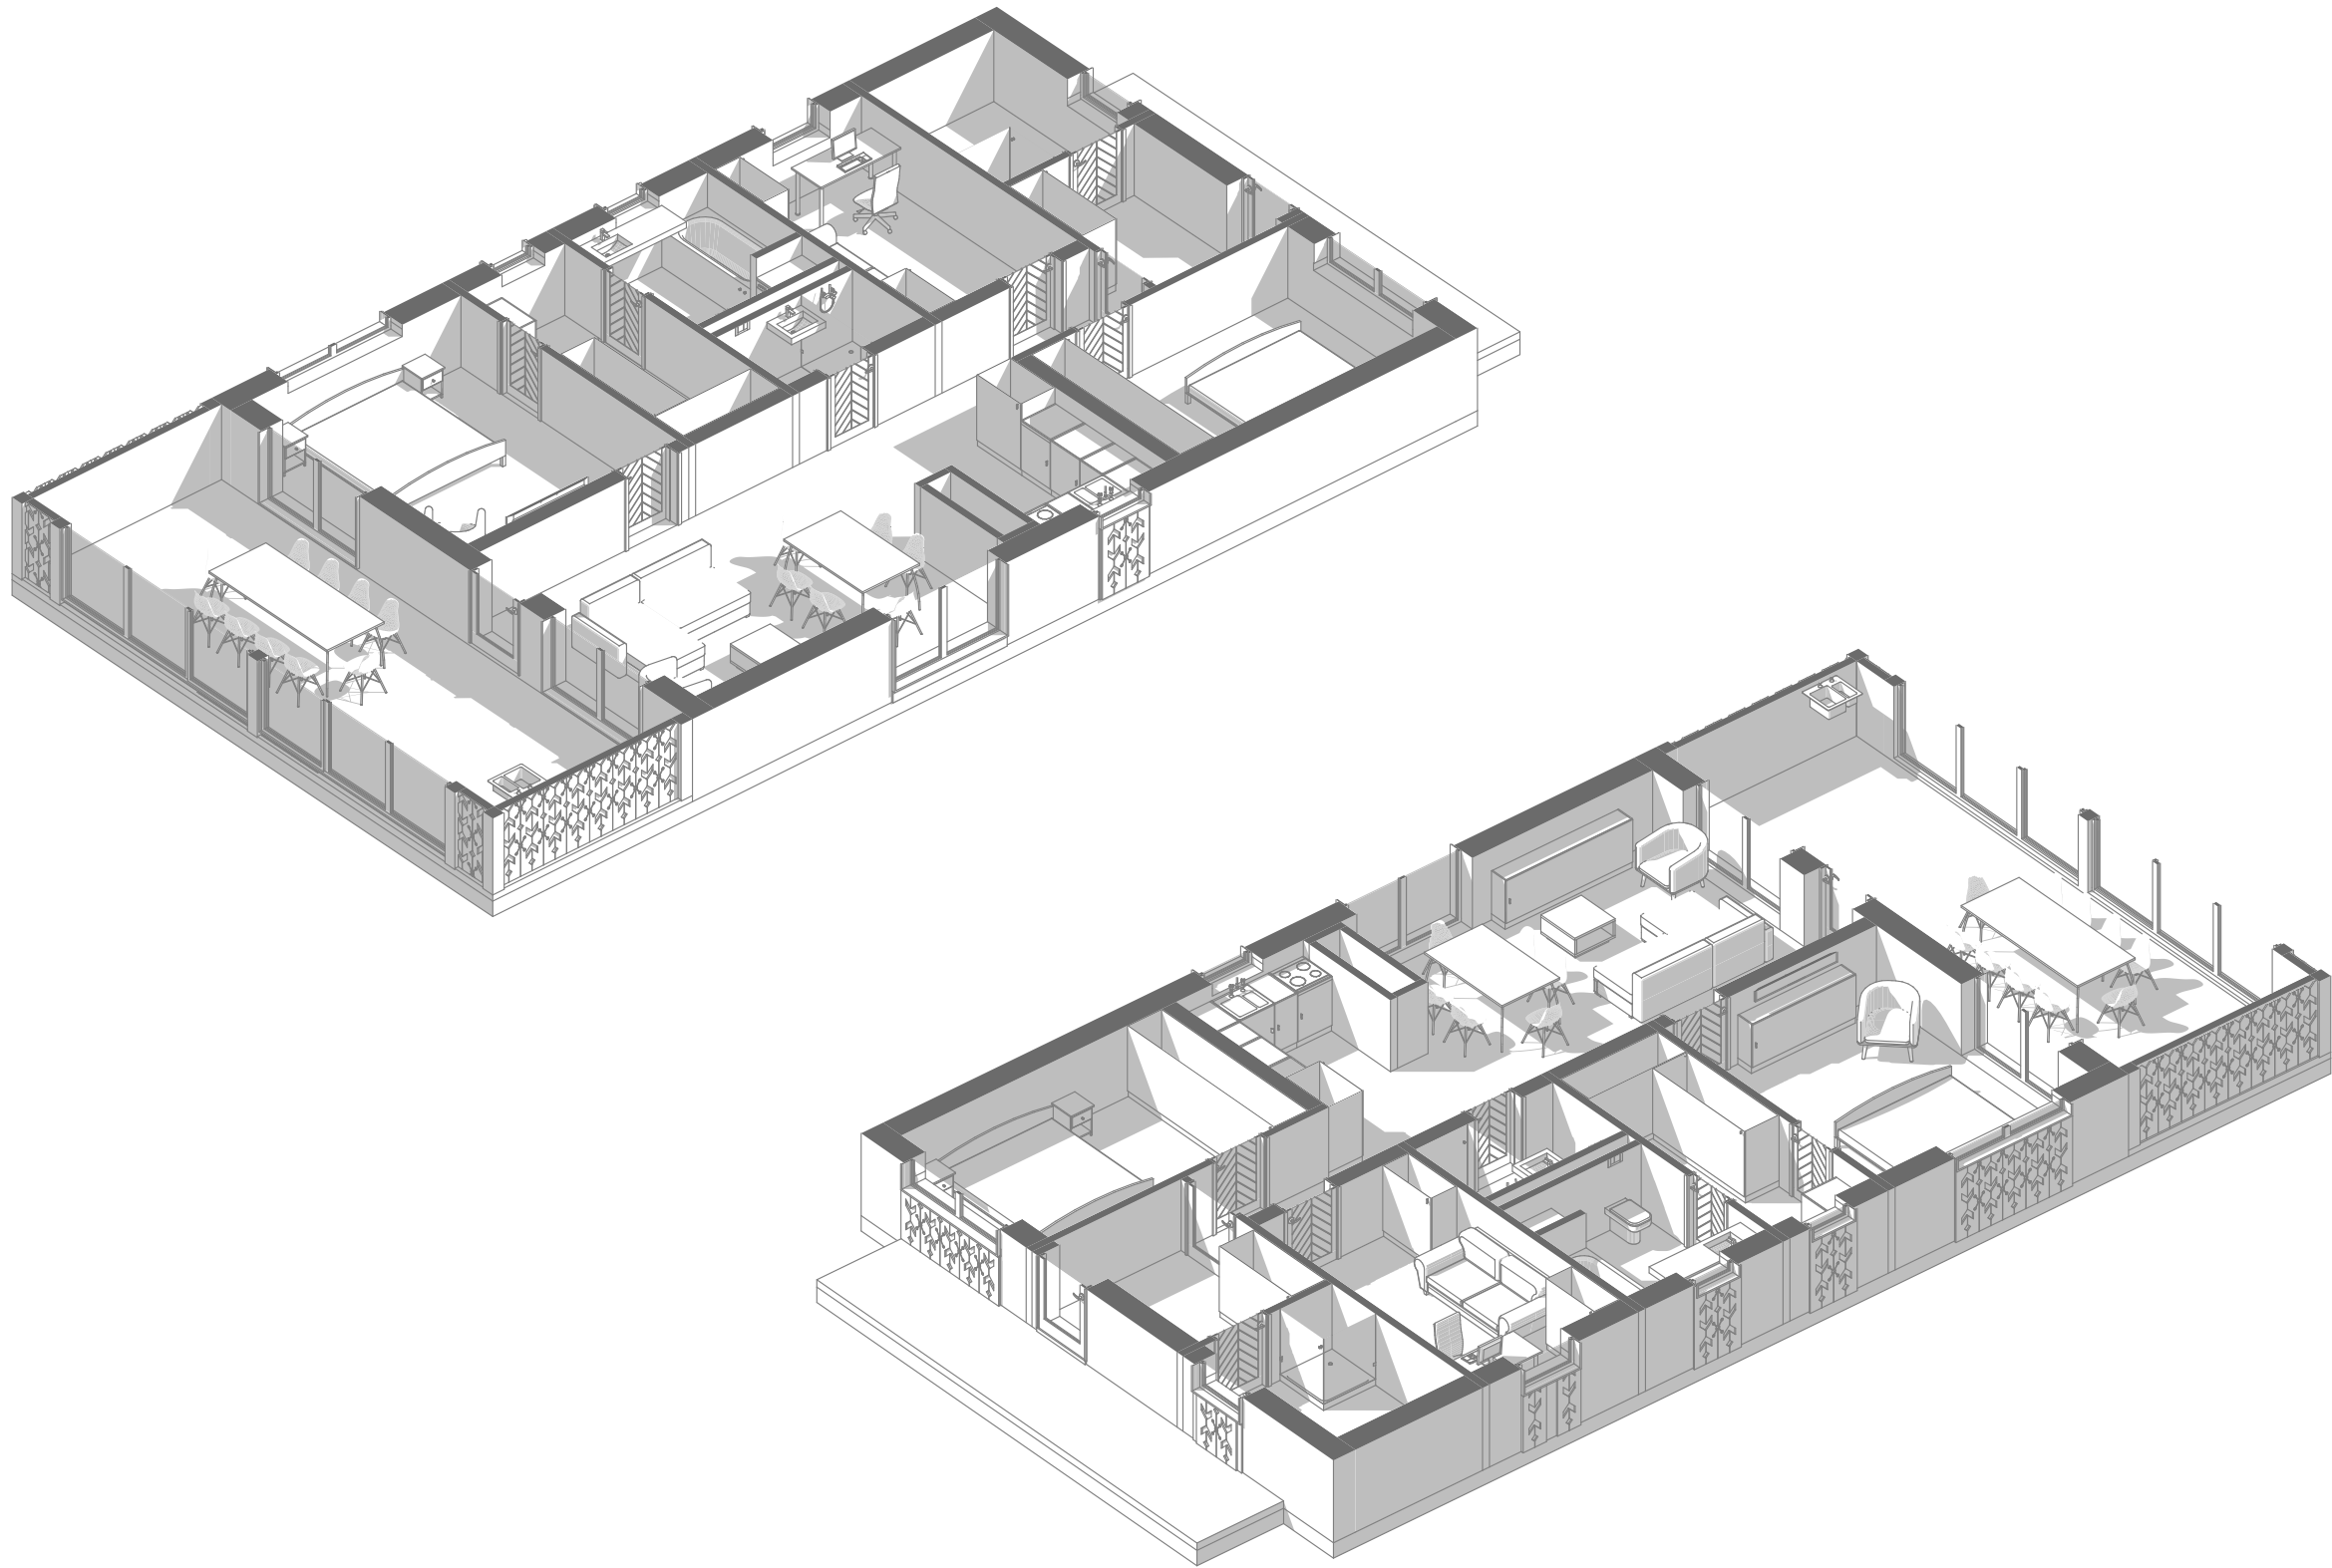

Зд-разрез


#Название Организации

План кровли дома

1:90

Условные обозначения:

- Кровля дома
- Подшив свесов

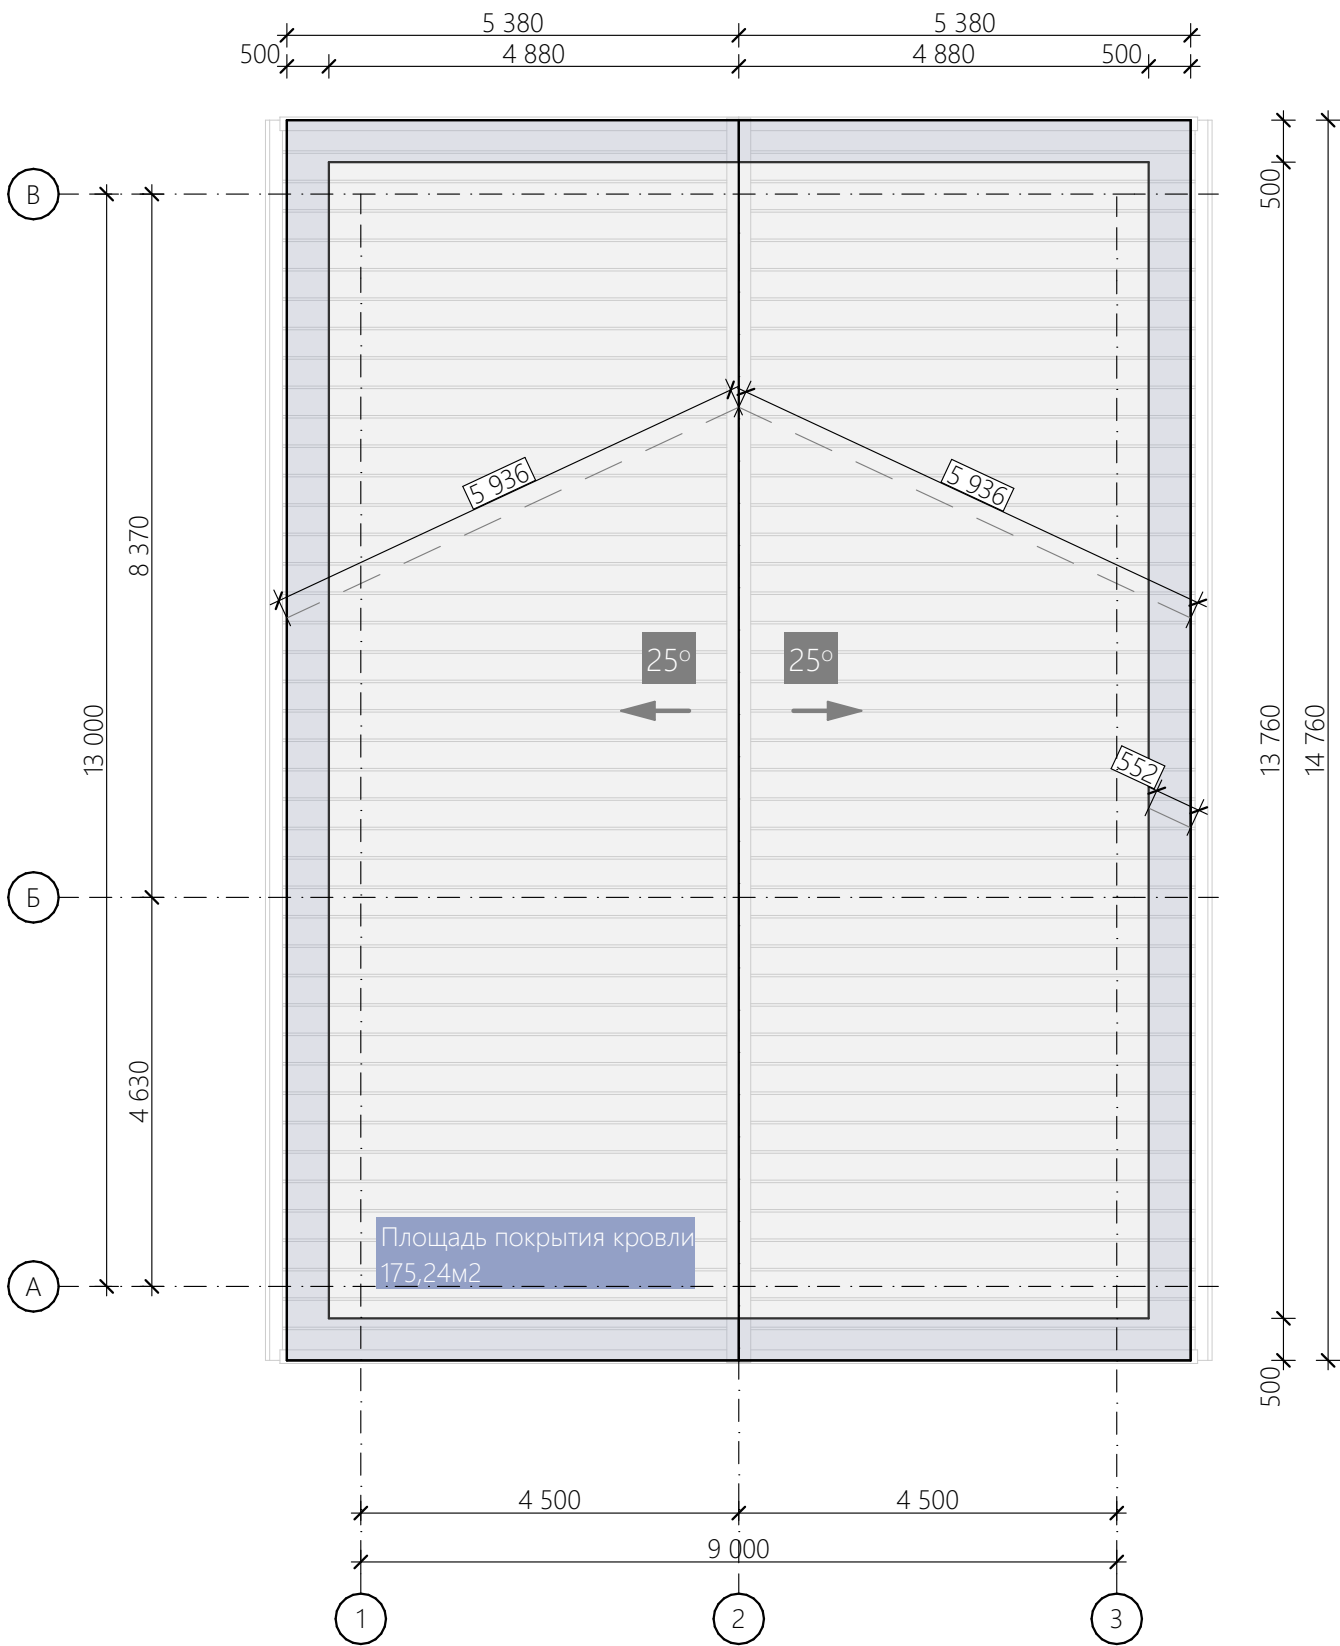

Согласовано				
Инв. № подл.	Подп. и дата	Взам. инв. №		



Лист	Изм.	№ Докум.	Подп.	Дата

Адрес:

План кровли дома

1:90

Условные обозначения:

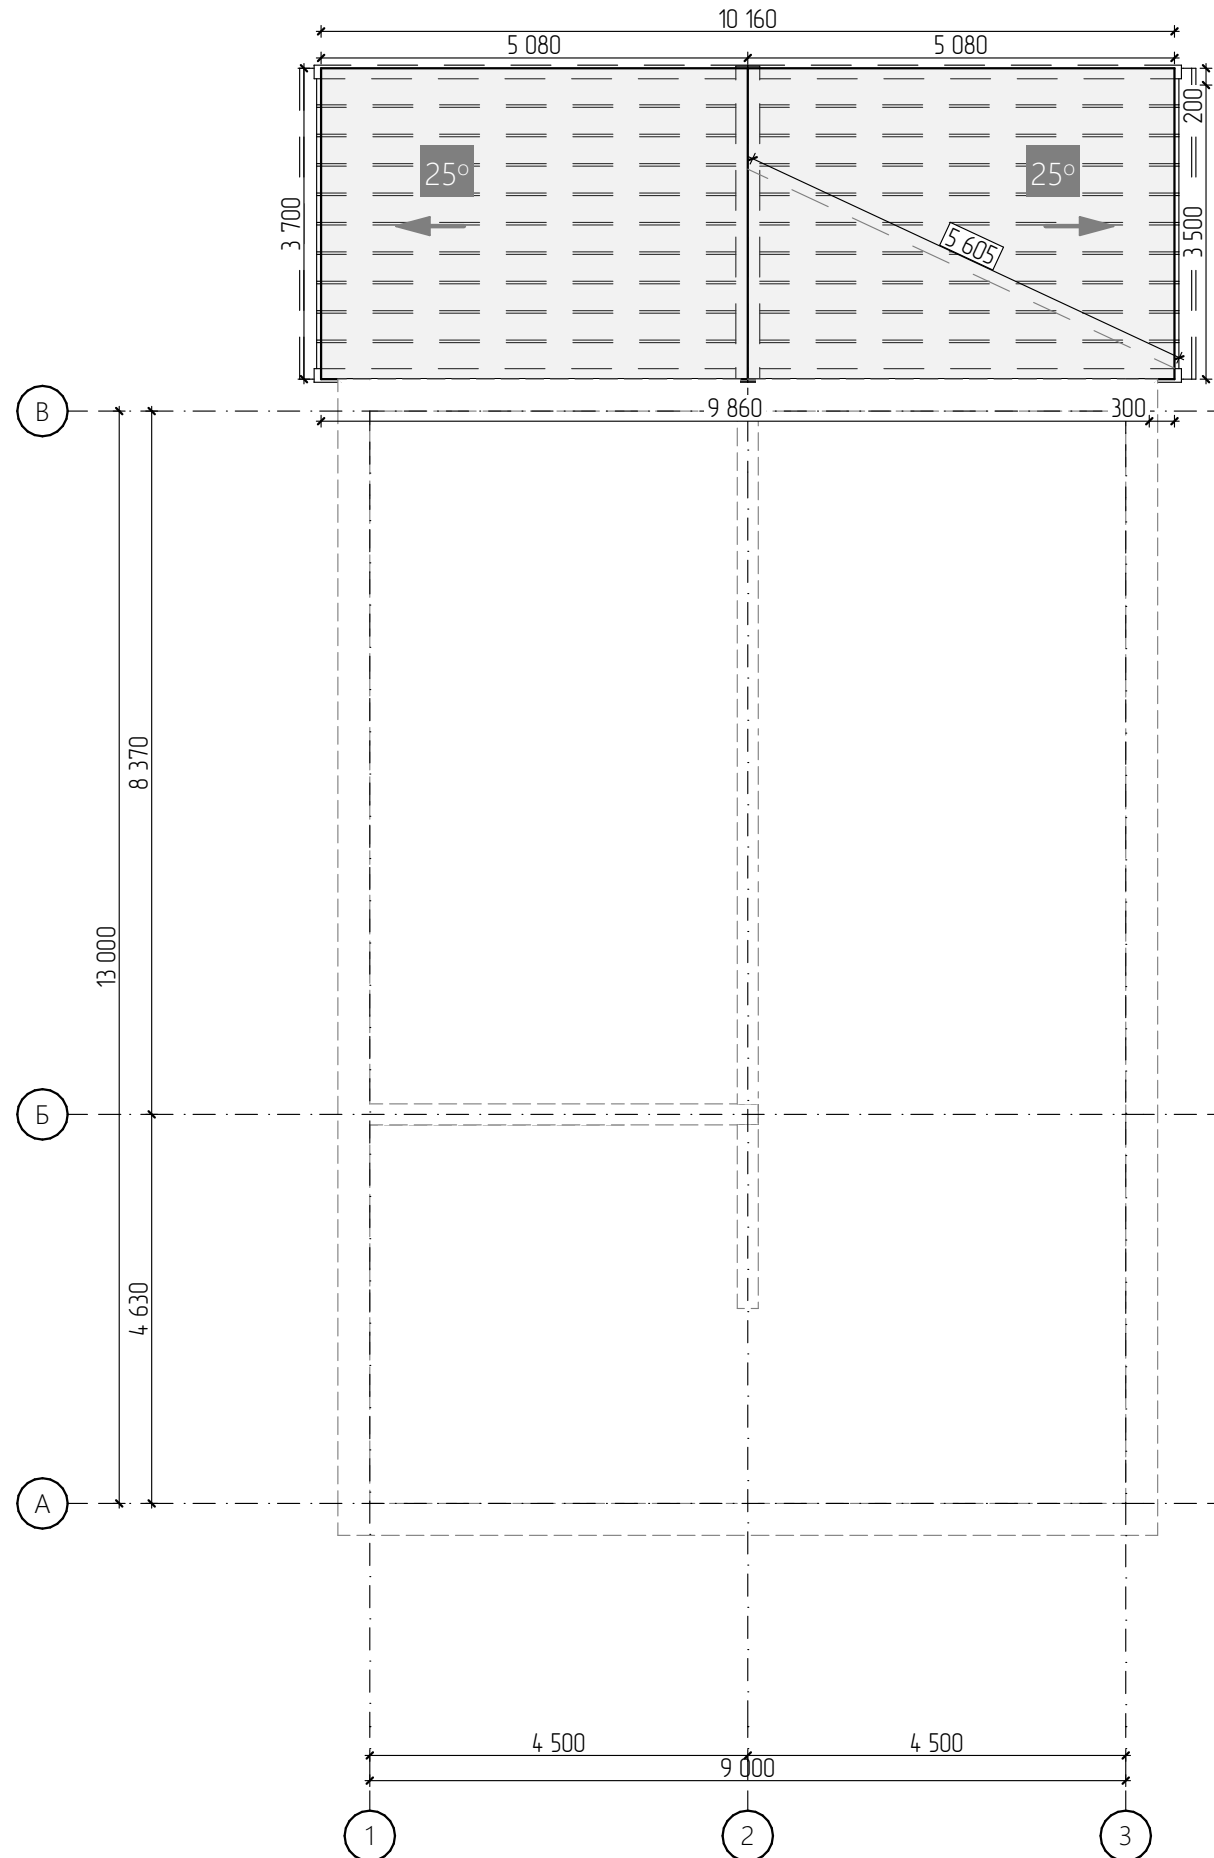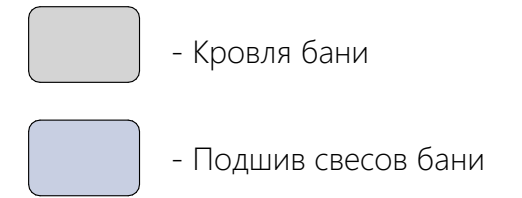

		Согласовано	

Лист	Изм.	№ Докум.	Подп.	Дата

Адрес:


План кровли террасы

#Название Организации

10

Разрез 1-1

1:75

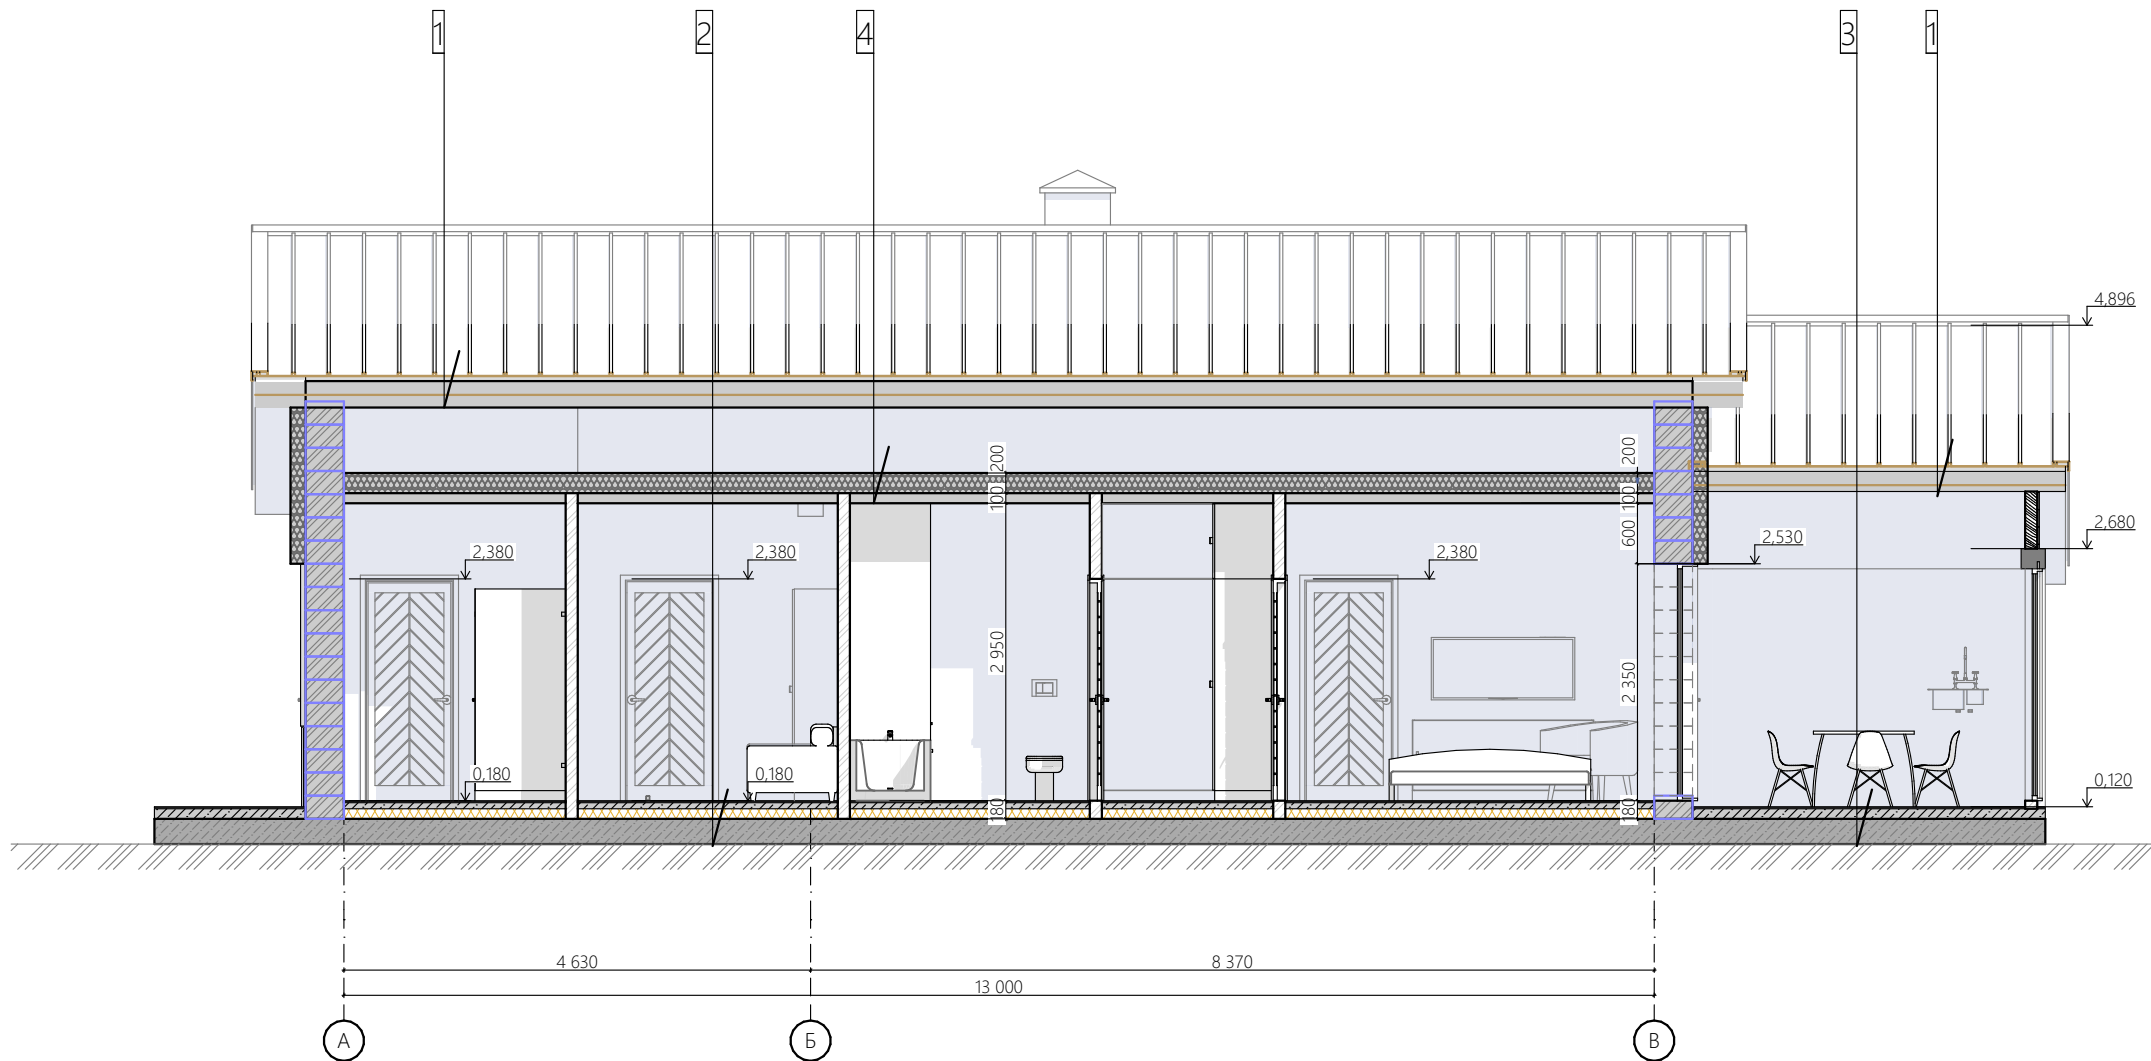

- 1
- Фальц клик
 - Обрешётка 25x100мм
 - Контробрешётка 50x50мм
 - Гидроветрозащитная мембрана
 - Стропильная система 190x45мм

- 2
- Ламинат 10мм
 - Подложка под ламинат 10мм
 - Цементно-песчаная стяжка 60мм
 - Утеплитель 100мм
 - Монолитное основание 250мм

- 3
- Керамогранит 10мм
 - Клей 10мм
 - Цементно-песчаная стяжка 80мм
 - Монолитное основание 250мм

- 4
- Лаги перекрытия (утеплённые 200мм) 190x45мм
 - Пароизоляционная мембрана
 - Отделка потолка 100мм

- 5
- Фальц клик
 - Обрешётка 25x100мм
 - Контробрешётка 50x50мм
 - Гидроветрозащитная мембрана
 - Стропильная система 190x45мм
 - утепленная
 - Пароизоляционная мембрана
 - Отделка потолка 100мм

Согласовано

Взам. инв. №

Подп. и дата

Инв. № подл.

Лист	Изм.	№ Докум.	Подп.	Дата

Адрес:

Разрез 1-1

#Название Организации

Согласовано

Взам. инв. №

Подп. и дата


Инв. № подл.

Лист	Изм.	№ Докум.	Подп.	Дата

Адрес:

Разрез 2-2

1:50

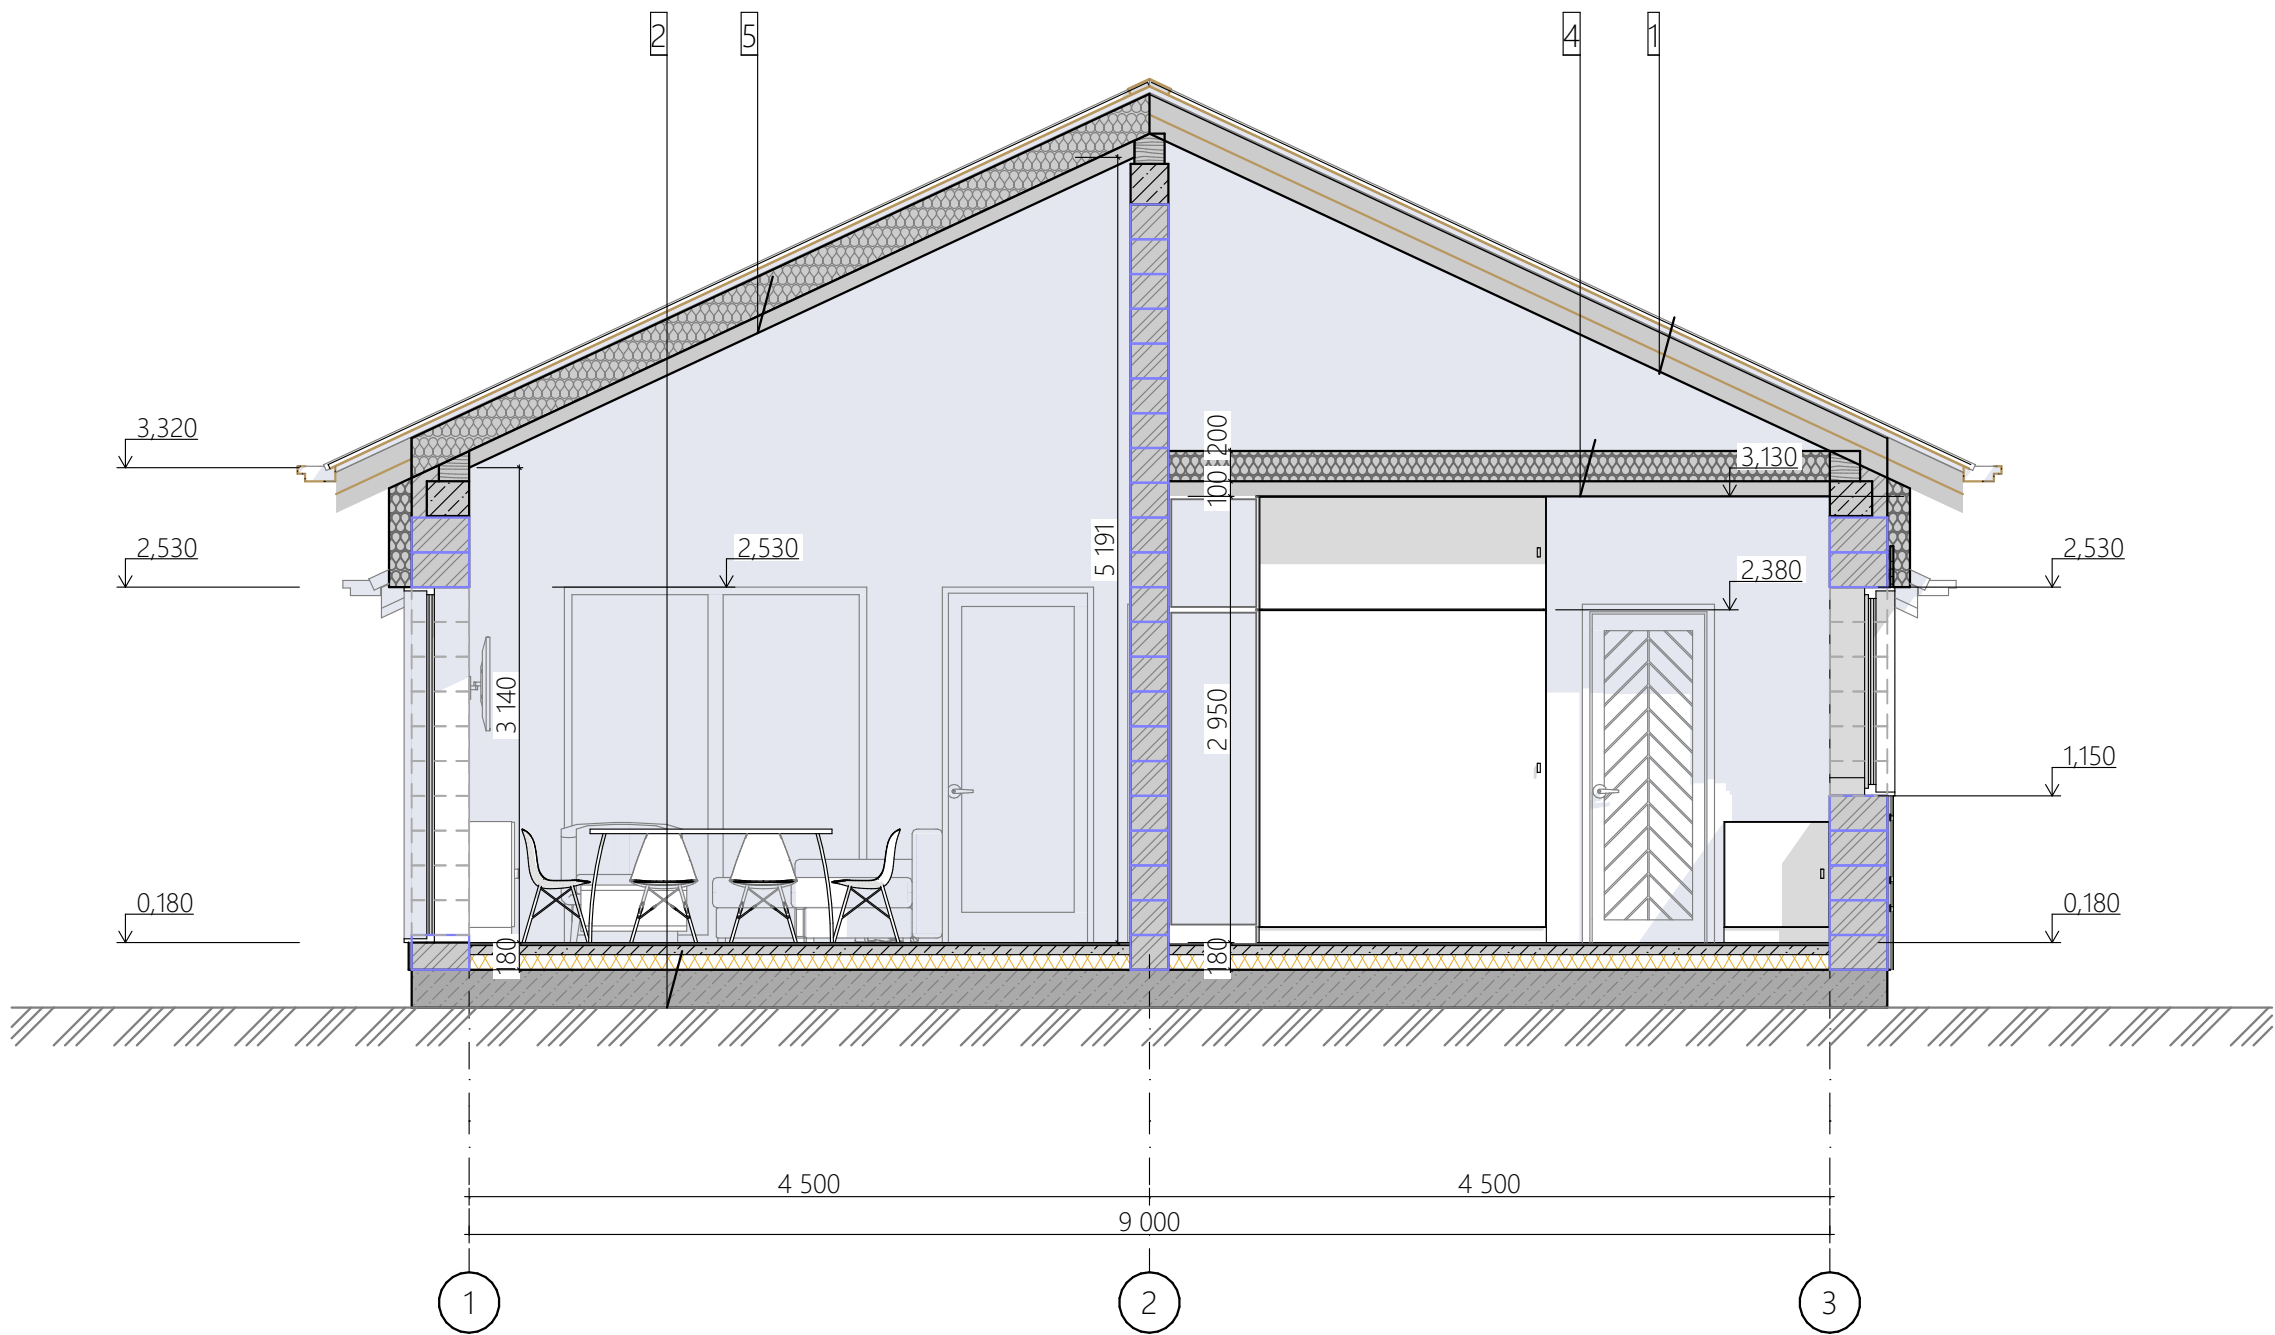

- | | | |
|---|------------------------------|----------|
| 1 | -Фальц | клик |
| | -Обрешётка | 25x100мм |
| | -Контробрешётка | 50x50мм |
| | -Гидроветрозащитная мембрана | |
| | -Стропильная система | 190x45мм |

- | | | |
|---|-----------------------|-------|
| 2 | -Ламинат | 10мм |
| | -Подложка под ламинат | 10мм |
| | -Цементно-песчаная | |
| | стяжка | 60мм |
| | -Утеплитель | 100мм |
| | -Монолитное основание | 250мм |

- | | | |
|---|-----------------------|-------|
| 3 | -Керамогранит | 10мм |
| | -Клей | 10мм |
| | -Цементно-песчаная | |
| | стяжка | 80мм |
| | -Монолитное основание | 250мм |

- | | | |
|---|----------------------------|----------|
| 4 | -Лаги перекрытия | 190x45мм |
| | (утеплённые 200мм) | |
| | -Пароизоляционная мембрана | |
| | -Отделка потолка | 100мм |

- | | | |
|---|------------------------------|----------|
| 5 | -Фальц | клик |
| | -Обрешётка | 25x100мм |
| | -Контробрешётка | 50x50мм |
| | -Гидроветрозащитная мембрана | |
| | -Стропильная система | 190x45мм |
| | утепленная | |
| | -Пароизоляционная мембрана | |
| | -Отделка потолка | 100мм |

Разрез 2-2

#Название Организации

Лист

12

Согласовано

Изм.

Изм.

Изм.

Изм.

Взам. инв. №

Подп. и дата

Инд. № подл.

Лист

Изм.

№ Докум.

Подп.

Дата

Адрес:

Ведомость оконных проёмов



(начало)

#Название Организации

Лист

13

Ведомость оконных проемов

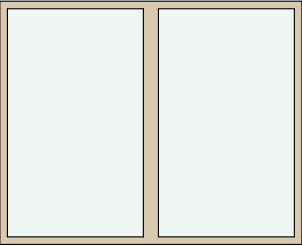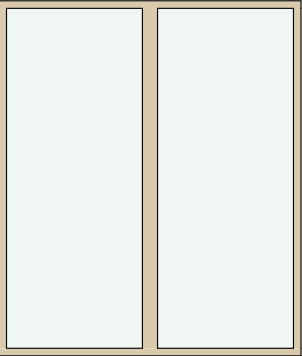Наименование	шт	Размеры проема	Ш х В, мм	Вид	Площадь, м2	Наименование	шт	Размеры проема	Ш х В, мм	Вид	Площадь, м2
ОК-01	1	2 000×1 610			3,22	ОК-04	1	750×1 380			1,04
ОК-02	1	1 000×1 610			1,61	ОК-05	1	750×1 380			1,04
ОК-03	1	1 000×1 610			1,61	ОК-06	1	2 000×2 350			4,70

Примечание:
1. Изготовление окон и дверей определяется заказчиком, допускается изменение открывания окон и дверей;
2. При заказе оконных и дверных блоков необходим обмер по месту от изготовителя;
3. Оконные и дверные изделия изображены со стороны открывания.

Согласовано

Изнач. № подл.


Подп. и дата


Взам. инв. №


Ведомость оконных проемов


Наименование	шт	Размеры проема	Ш х В, мм	Вид	Площадь, м2
--------------	----	----------------	-----------	-----	-------------


Наименование	шт	Размеры проема	Ш х В, мм	Вид	Площадь, м2
--------------	----	----------------	-----------	-----	-------------

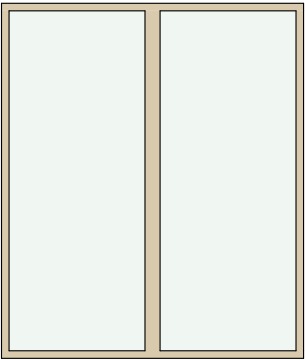
OK-07	1	2 000×2 350		4,70
-------	---	-------------	--	------

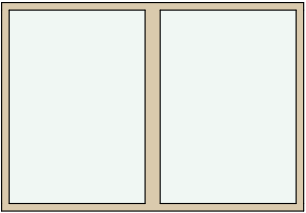OK-10	1	2 000×1 380		2,76
-------	---	-------------	---	------




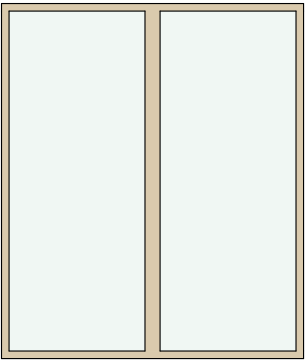
OK-08	1	2 000×2 350		4,70
-------	---	-------------	--	------

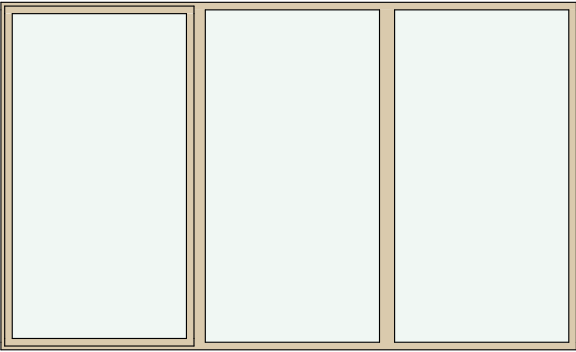OK-11	1	3 810×2 300		8,76
-------	---	-------------	---	------

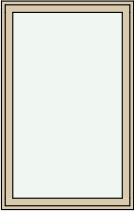OK-09	1	875×1 380		1,21
-------	---	-----------	---	------

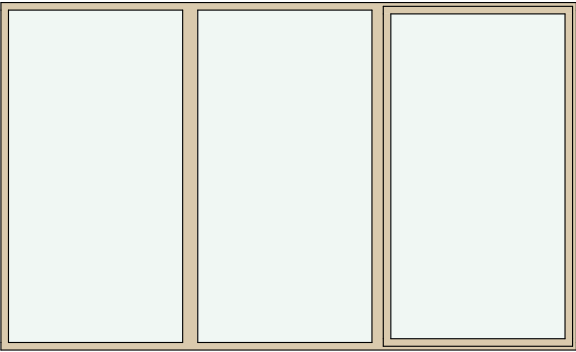OK-12	1	3 810×2 300		8,76
-------	---	-------------	---	------

44,11 м²

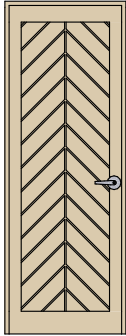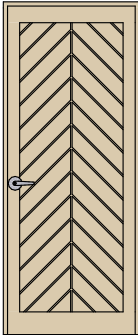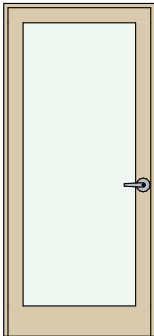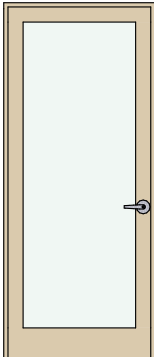Ведомость дверных проемов												
Наименование		шт.	Размеры проема		Ш х В, мм		Вид			Площадь, м2		
ДВ-01		3	800×2 200					1,76				
ДВ-02		4	900×2 200					1,98				
ДВ-03		1	1 000×2 200					2,20				
ДН-01		2	1 000×2 350					2,35				
										20,10 м²		
Инв. № подл.	Подп. и дата	Взам. инв. №	Лист	Изм.	№ Докум.	Подп.	Дата	Ведомость дверных проёмов		#Название Организации		Лист
												15

Согласовано

Согласовано

Взам. инв. №

Подп. и дата

Инв. № подл.

Ф-1

1:75

Условные обозначения:



Лист	Изм.	№ Докум.	Подп.	Дата

Адрес:

Цветовое решение; Фасад в
осях В-А

#Название Организации


Лист

16

Условные обозначения:

Ф-2

1:50

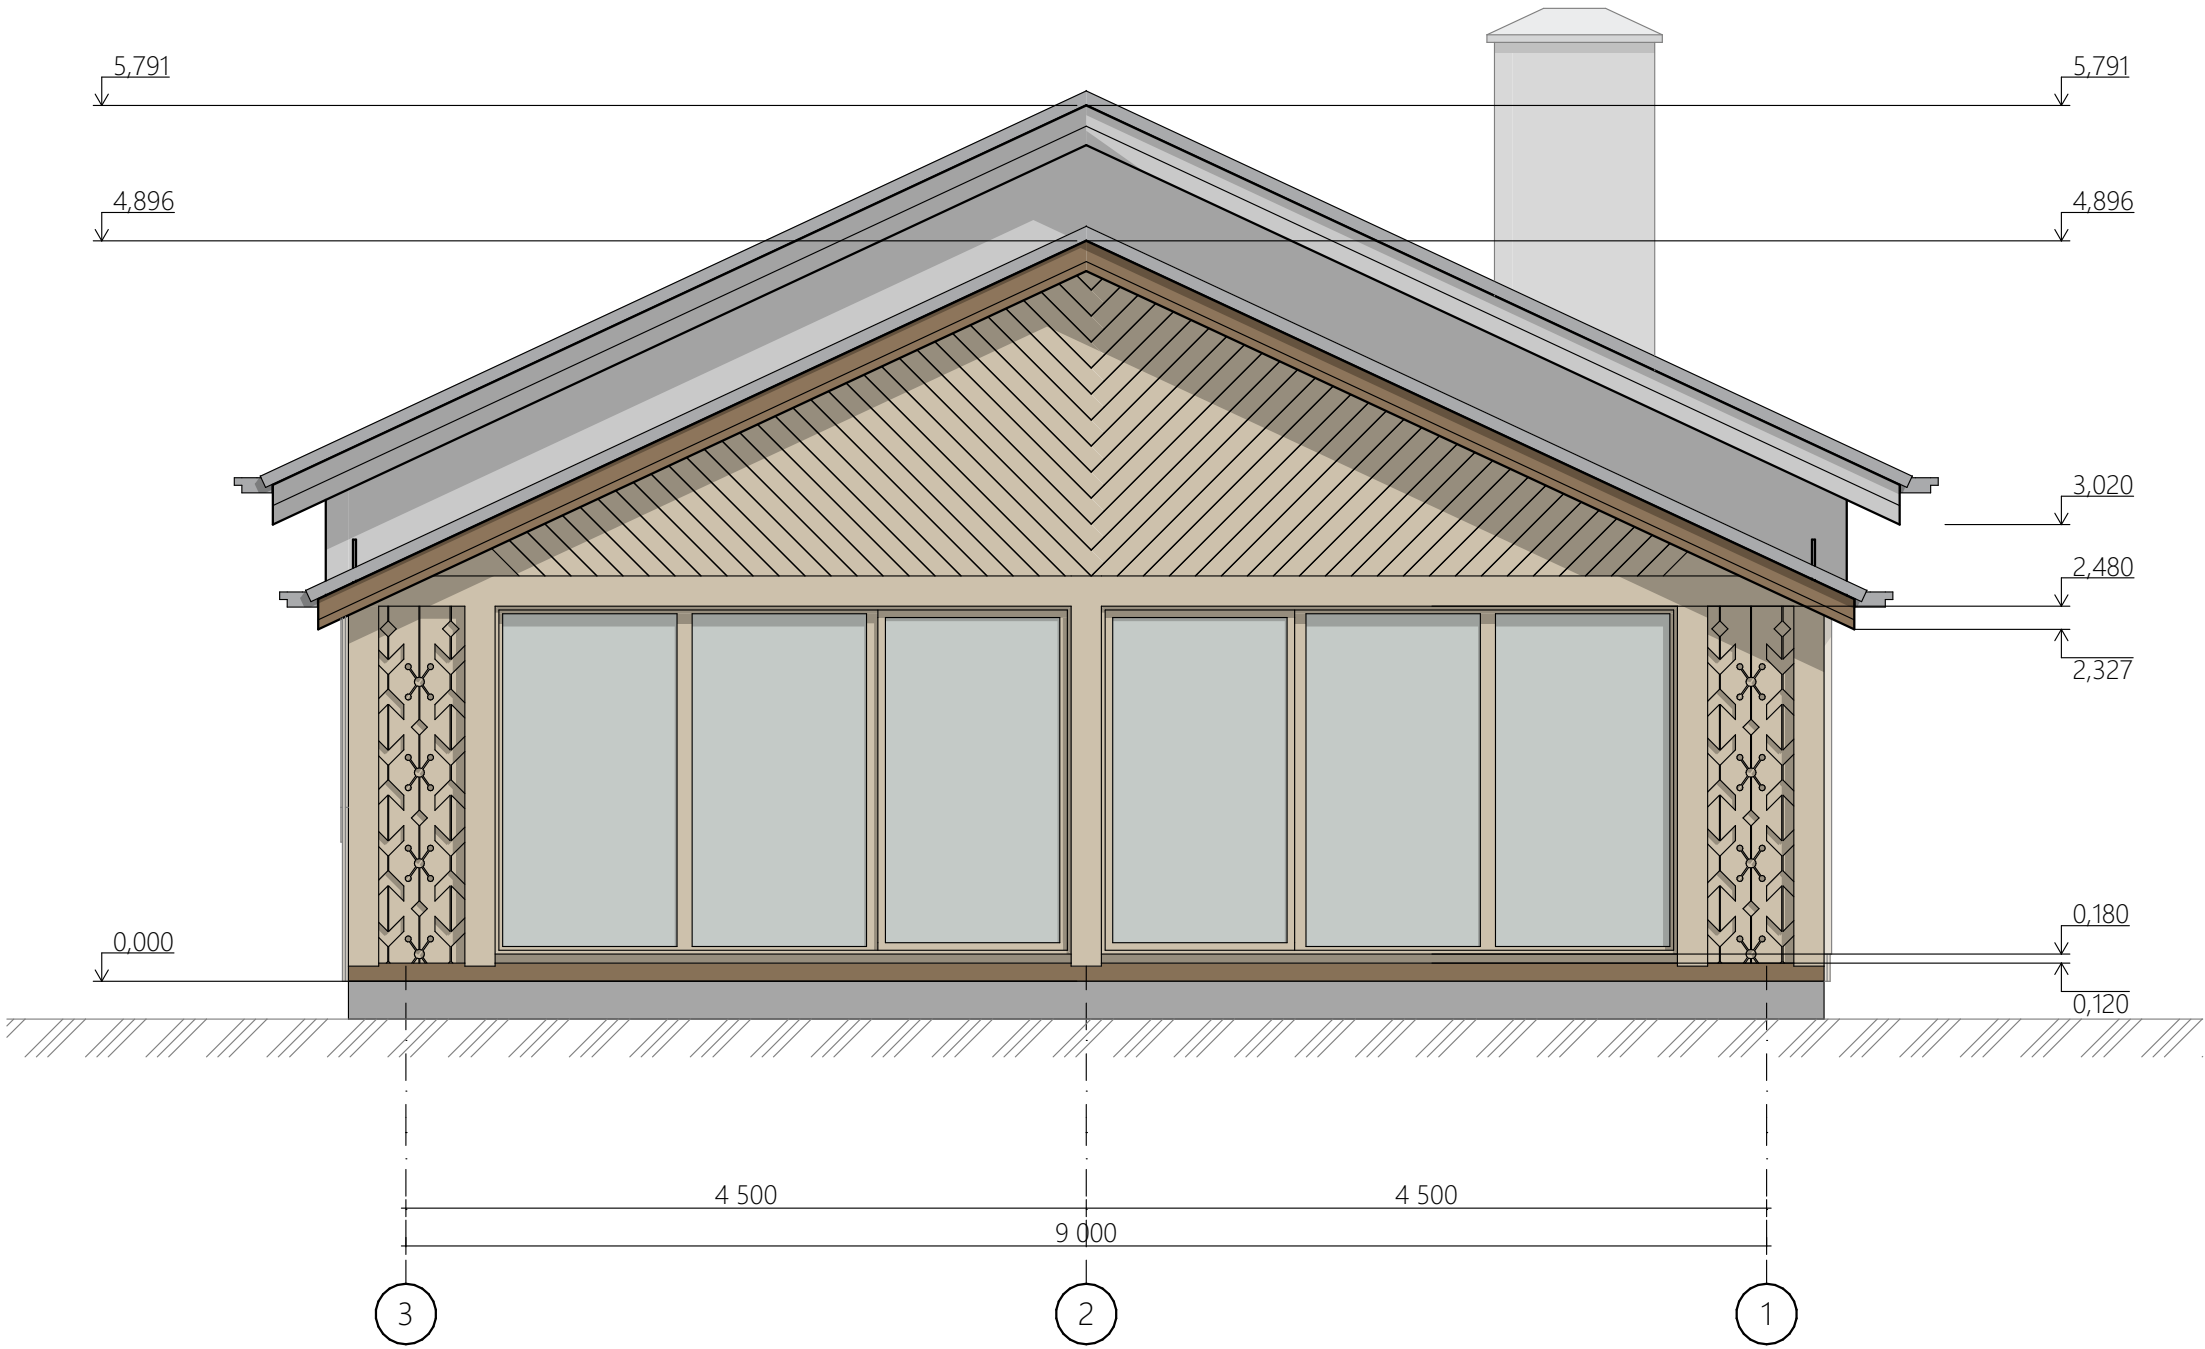

Согласовано

Взам. инв. №

Подп. и дата

Инв. № подл.

Лист	Изм.	№ Докум.	Подп.	Дата

Адрес:


Цветовое решение; Фасад в осях 3-1

#Название Организации

Лист

17

Согласовано				
Инв. № подл.	Подп. и дата	Взам. инв. №		

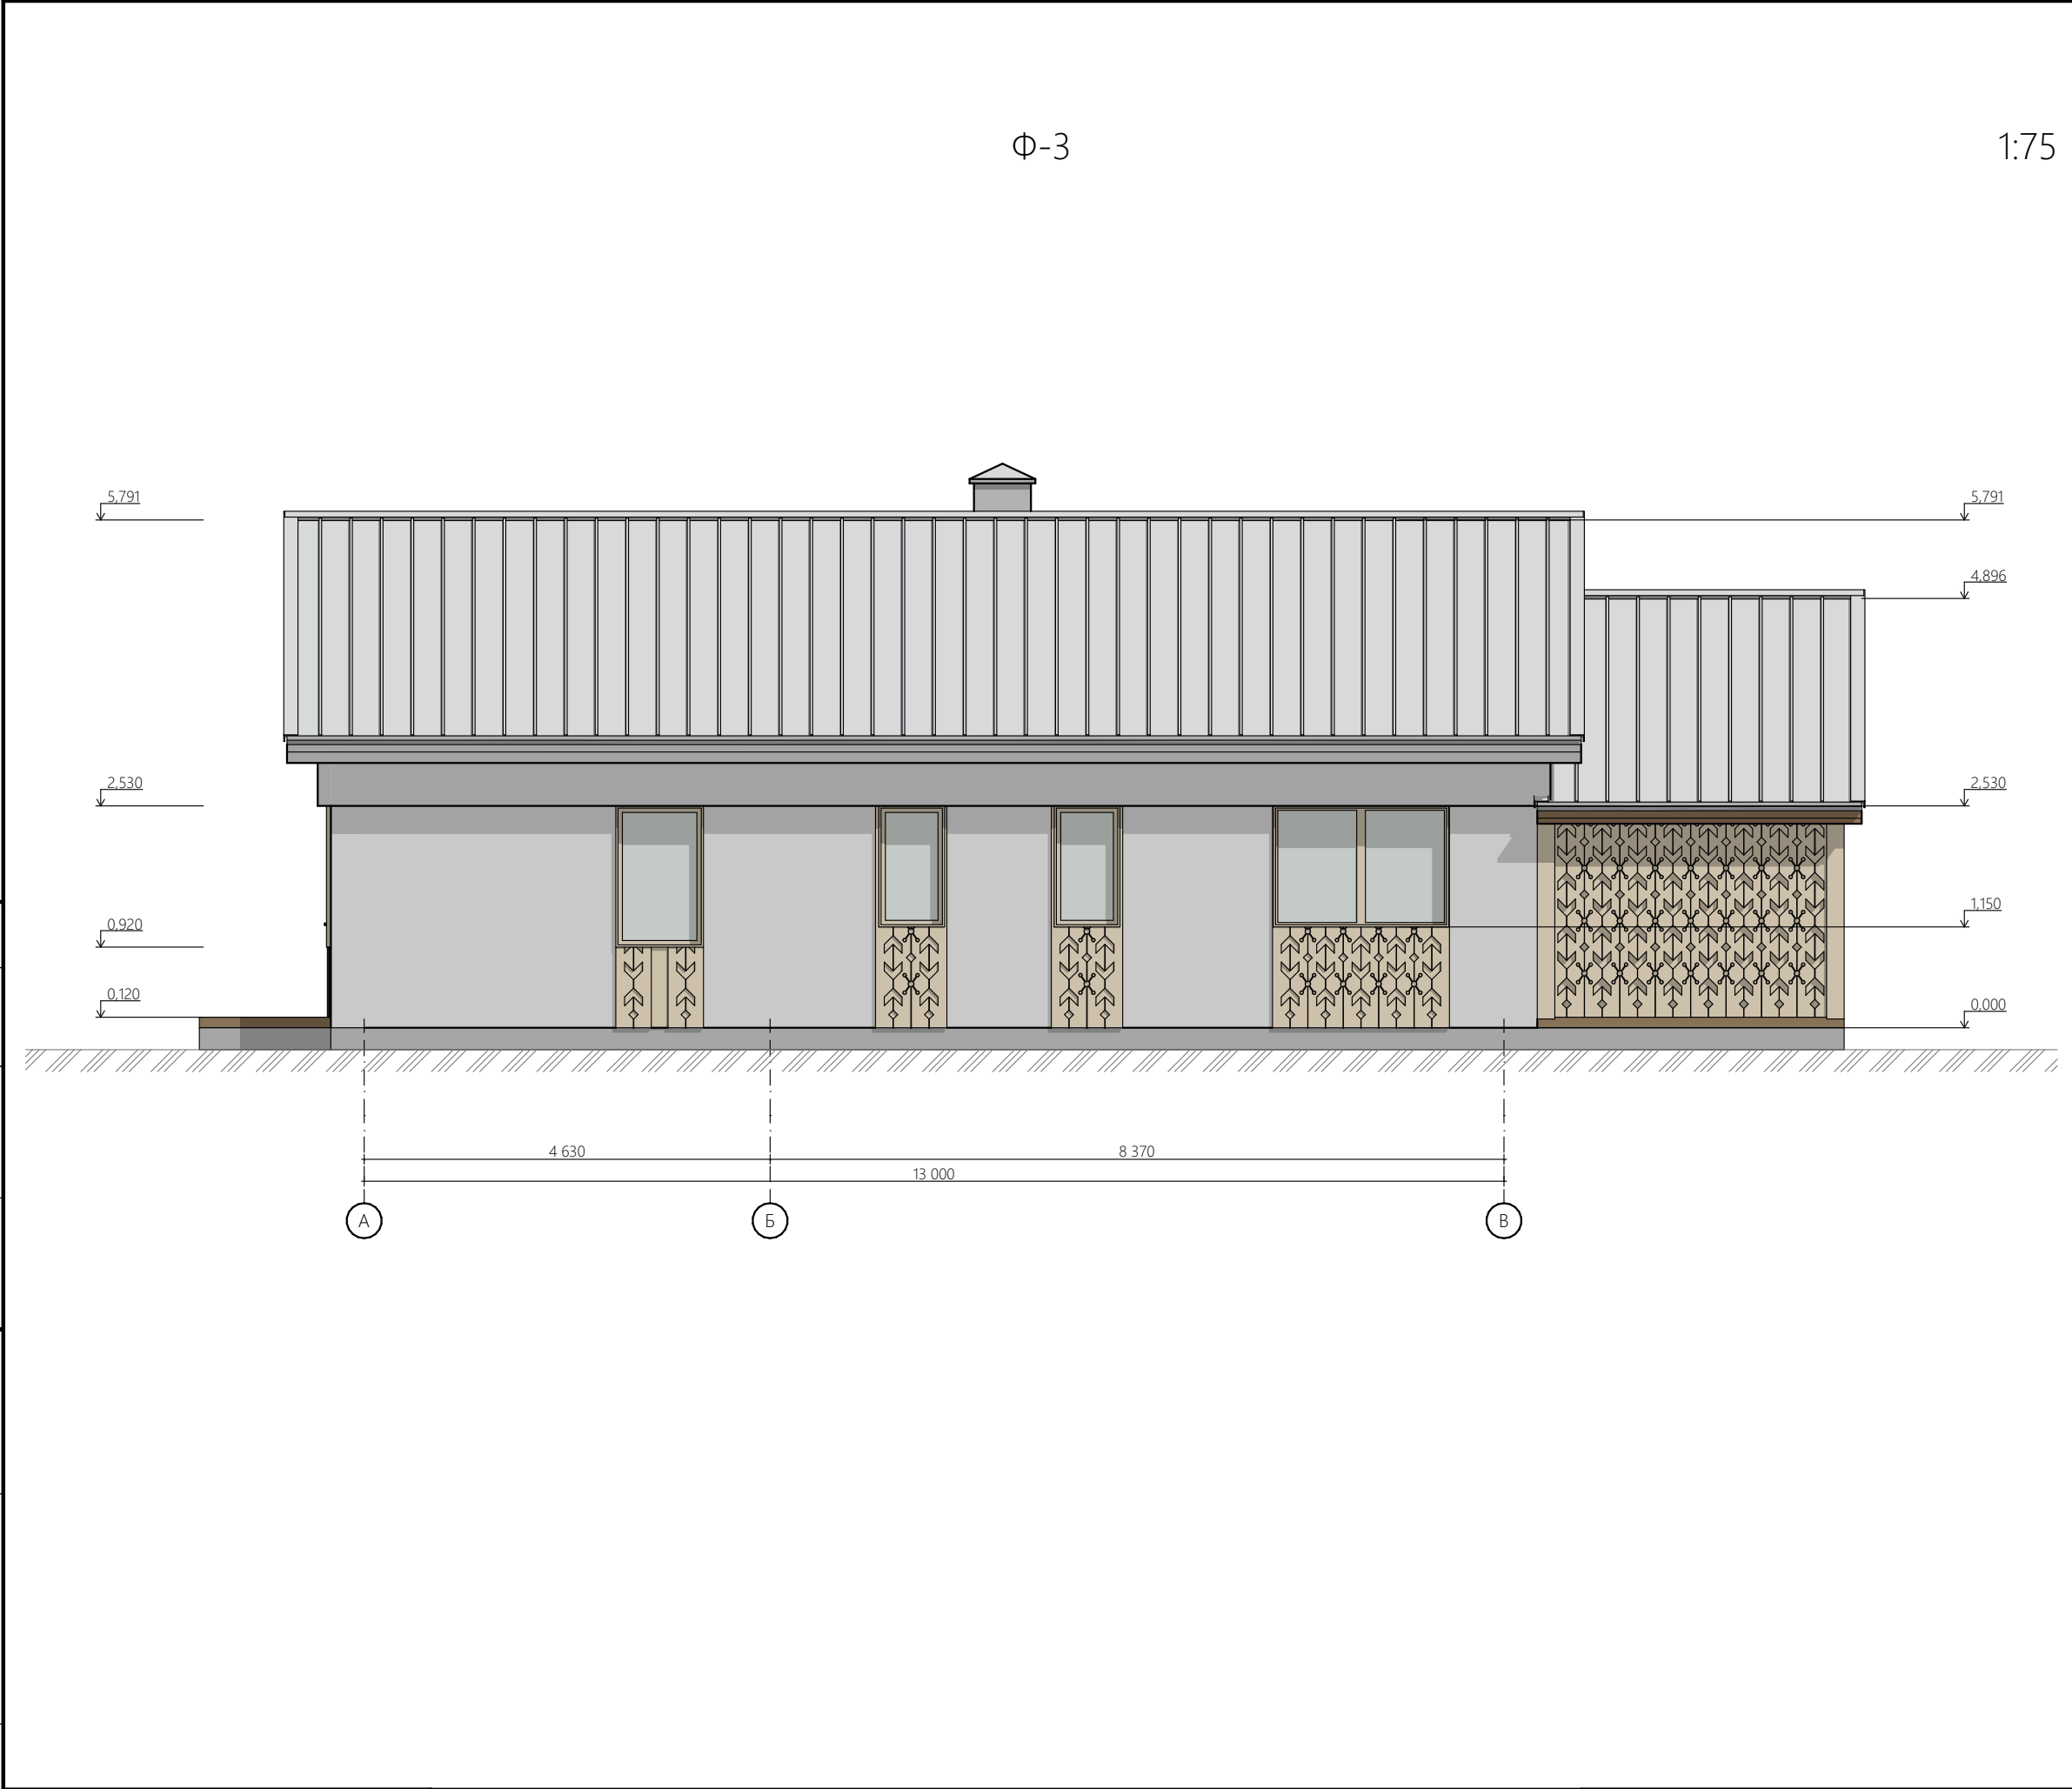

Условные обозначения:

Лист	Изм.	№ Докум.	Подп.	Дата


Адрес:

Цветовое решение; Фасад в
осях А-В

#Название Организации

Patient Information	
First Name	
Last Name	
Address	
City	
State	
Zip	
Phone	
Age	
Gender	
Marital Status	
Occupation	
Insurance	
Referral	
History of Present Illness	
Past Medical History	
Past Surgical History	
Family History	
Social History	
Review of Systems	
Physical Examination	
Vital Signs	
Laboratory Tests	
Imaging Studies	
Diagnosis	
Treatment Plan	
Follow-up	

1:50

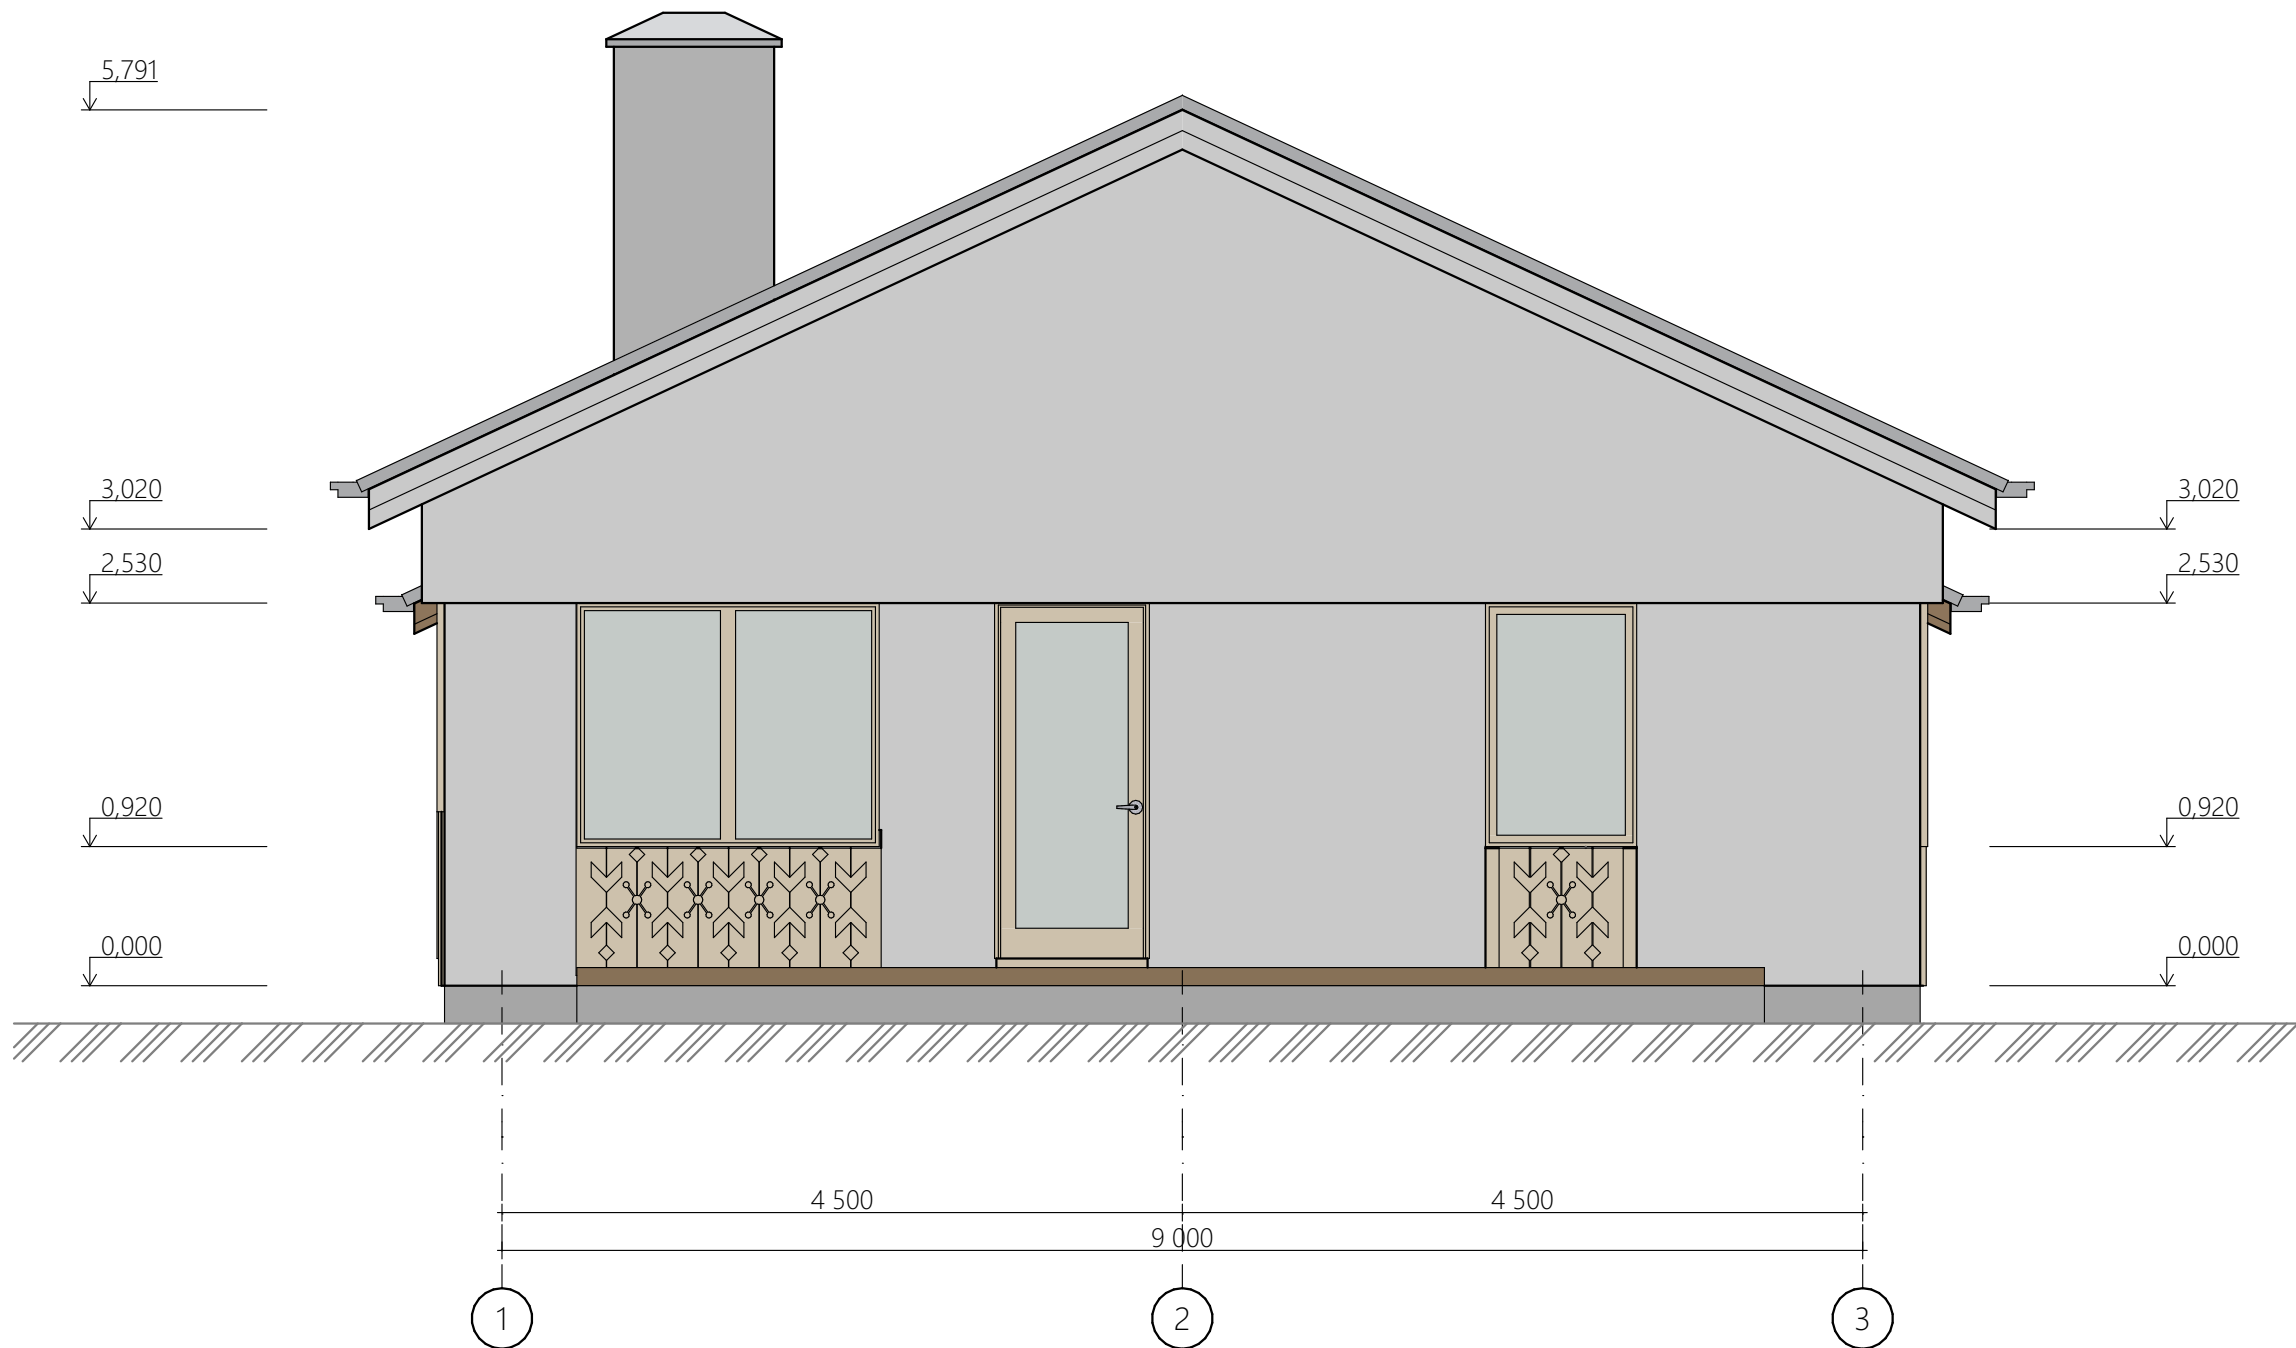

		Согласовано	

Лист	Изм.	№ Докум.	Подп.	Дата

Адрес:

Цветовое решение; Фасад в осях 1-3

#Название Организации

19