



Архитектор

Заказчик

Архитектурные решения
(раздел АР)

Одноэтажное здание
(баня)

Основной комплект чертежей
(планы, разрезы, фасады)

Мясникова В.А.

Согласовано				
И-нв. № подл.	Подп. и дата	Взам. инв. №		

Лист	Наименование	Примечание
1	Титульный	
2	Ведомость чертежей	
3	Пояснительная записка	
4	Маркировочный план 1 этажа	
5	Маркировочный план 2 этажа	
6	Размерный план 1 этажа	
7	Размерный план 2 этажа	
8	План расстановки мебели и оборудования 1 этажа	
9	Зд-разрез	
10	План покрытия пола	
11	Пироги пола	
12	План покрытия стен	
13	Пироги стен	
14	План размещения розеток 1 этажа	
15	План размещения розеток 2 этажа	
16	План размещения светильников и выключателей 1 этажа	
17	План размещения светильников и выключателей 2 этажа	
18	План крыши	
19	Ведомость оконных проемов	
20	Ведомость дверных проемов	
21	Разрез 1-1	
22	Разрез 2-2	
23	Разрез 3-3	
24	Фасад 1-4	
25	Фасад А-Г	
26	Аксонометрия №1	
27	Фасад Г-А	
28	Фасад 4-1	
29	Аксонометрия №2	
30	Визуализация	
31	Визуализация	
32	Визуализация	
33	Визуализация	
34	Визуализация	
35	Визуализация	
36	Визуализация	
37	Визуализация	

Лист	Изм.	№ Докум.	Подп.	Дата

обл. Московская, р-н Дмитровский, с/пос. Яотское, д. Новое Сельцо, дом 43	Ведомость чертежей		Лист
			2

В основу архитектурно-планировочных решений положены требования технологических заданий и требования норм и правил строительного проектирования, действующих на территории РФ.

Основные параметры и требования разработаны на основании пожеланий и требований заказчика.

Архитектурные решения приняты в соответствии со следующими нормативными документами:

- Градостроительный кодекс российской федерации.
- Земельного Кодекса Российской Федерации.
- Федеральный закон от 22.07.2008 N 123 - ФЗ (ред. от 29.07.2017)"Технический регламент о требованиях пожарной безопасности.
- Федеральный закон № 384 - ФЗ «Технический регламент о безопасности зданий и сооружений».
- ГОСТ Р 21.1101-2013.«Основные требования к проектной и рабочей документации».
- Постановление правительства РФ от 16.02.2008 № 87 «Положение о составе разделов проектной документации и требованиях к их содержанию».
- СП 42.13330.2011 «Градостроительство. Планировка и застройка городских и сельских поселений».
- СП 131.13330.2018 «СНиП 23-01-99* Строительная климатология».
- СП 20.13330.2016 «СНиП 2.01.07-85* Нагрузки и воздействия».
- СП 22.13330.2016 «СНиП 2.02.01-83* Основания зданий и сооружений».
- СП 70.13330.2012 (с изменениями №1) «СНиП 3.03.01-87 Несущие и ограждающие конструкции».
- СП 64.13330.2017 «СНиП II-25-80 Деревянные конструкции».
- СП 17.13330.2017 «СНиП II-26-76 Кровли».
- СП 29.13330.2011 «СНиП 2.03.13-88 Полы».
- СП 28.13330.2017 «СНиП 2.03.11-85 Защита строительных конструкций от коррозии».
- СП 50.13330.2012 «СНиП 23-02-2003 Тепловая защита зданий».

Согласовано				
И-нв. № подл.	Подп. и дата	Взам. инв. №		

1. Общие данные:

1.1. Архитектурный проект разработан на основании требований и пожеланий заказчика.

Тип строения	Баня
Относительная отм. ±0.000	ур. верха лаг перекрытия
Общая площадь застройки, м2	88,20
Габаритные размеры каркаса здания	10,00х9,80м
Этажность	1 этаж
Конструктивная схема	Деревянный каркас

2. Конструктивные решения:

2.1. Рабочие чертежи разработаны на основании задания на проектирование

Полезная нагрузка на перекрытие	150 кгс/м2	-
Нормативная глубина промерзания	1,2м	СП 22.13330.2016 СП 131.13330.2020
Нормативное ветровое давление	I район (23кгс/м2)	СП 22.13330.2016
Нормативный вес снегового покрова	III район (150кгс/м2)	СП 22.13330.2016
Температура наиболее холодной пятидневки	-29°С	СП 131.13330.2020

2.2. Конструктивное строение представляет собой сооружение:

- на свайном фундаменте
- несущими стенами из деревянного каркаса
- двускатной кровлей по деревянным стропилам

2.3. Необходимо осуществлять технический надзор за производством строительных работ. Данные по проведённым работам необходимо систематически вносить в журнал работ.

По каждому из этапов работ необходимо осуществлять входной контроль материалов и вести приёмку.

Фундамент	сваи винтовые d=108мм
Несущие конструкции	деревянный каркас (145х45мм)
Стропильная система	строганая доска (145х45мм)
Тип крыши	двускатная
Покрытие кровли	металлочерепица

2.4. Все деревянные конструкции обработать огне-биозащитными септиками в соответствии со СП 28.13330.2017 "Защита строительных конструкций от коррозии".

2.5. Кровельные работы выполнять в соответствии с требованиями фирмы производителя.

2.6. Все работы вести в строгом соответствии с требованиями СНиП 12.03.2001 "Безопасность труда в строительстве".

2.7. При выполнении всех работ строго соблюдать меры противопожарной безопасности.


2.8. Возможна замена материалов аналогами.

*Решения, принятые в проекте и отображенные в чертежах, соответствуют требованиям экологических, санитарно - гигиенических, противопожарных и других норм, действующих на территории Российской Федерации, и обеспечивают безопасную для жизни и здоровья людей эксплуатацию объекта при соблюдении предусмотренных рабочих чертежей и мероприятий.

Лист	Изм.	№ Докум.	Подп.	Дата

Маркировочный план 1 этажа

1:55

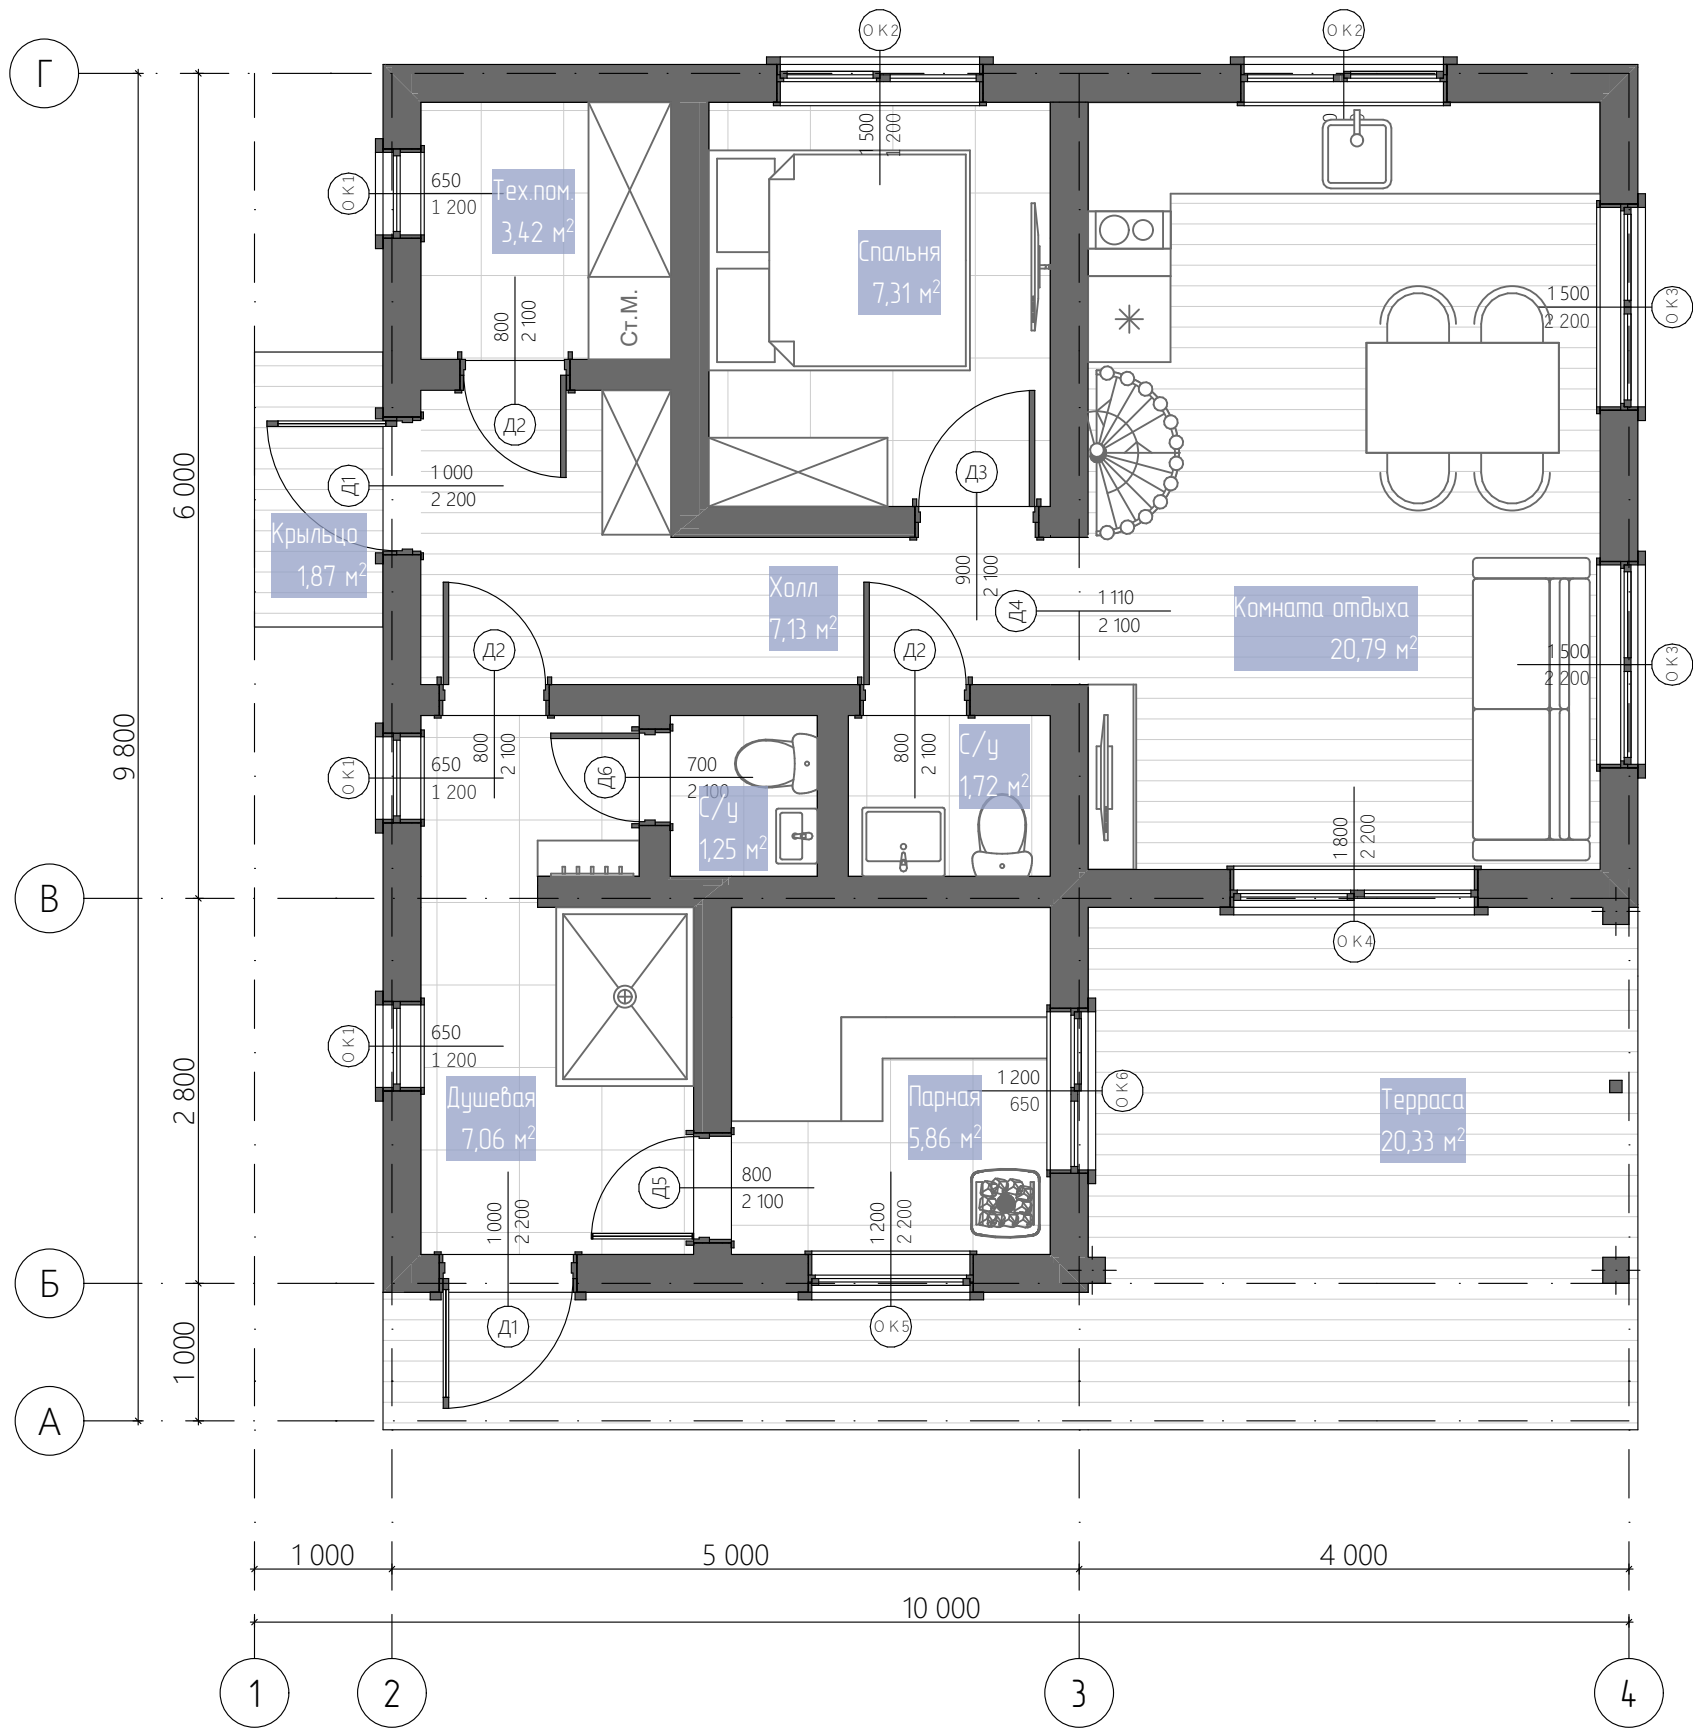

Экспликация помещений

№	Наименование	Площадь, кв.м.
1	Холл	7,13
2	Тех.пом.	3,42
3	Спальня	7,31
4	Душевая	7,06
5	С/у	1,25
6	С/у	1,72
7	Парная	5,86
8	Комната отдыха	20,79
9	Терраса	20,33
10	Крыльцо	1,87
11	Зона мансарды	39,55
		116,29 м²

Наименование	Площадь, кв.м.
Площадь застройки	88,20

Примечание:

1. Вся индивидуальная мебель выполняется по отдельному проекту с детальной проработкой и калькуляцией. Чертежи предоставляет фирма-изготовитель столярных изделий.
2. Данный проект отдельно согласовывается с автором проекта и непосредственно с заказчиком.
3. Цветовое решение фасада и материалов отделки показаны в проекте приблизительно.
4. Количество ступеней показано условно.

Согласовано

Взам. инв. №


Подп. и дата

Инв. № подл.

Лист	Изм.	№ Докум.	Подп.	Дата


обл. Московская, р-н Дмитровский, с/пос. Якотское, д. Новое Сельцо, дом 43

Маркировочный план 1 этажа

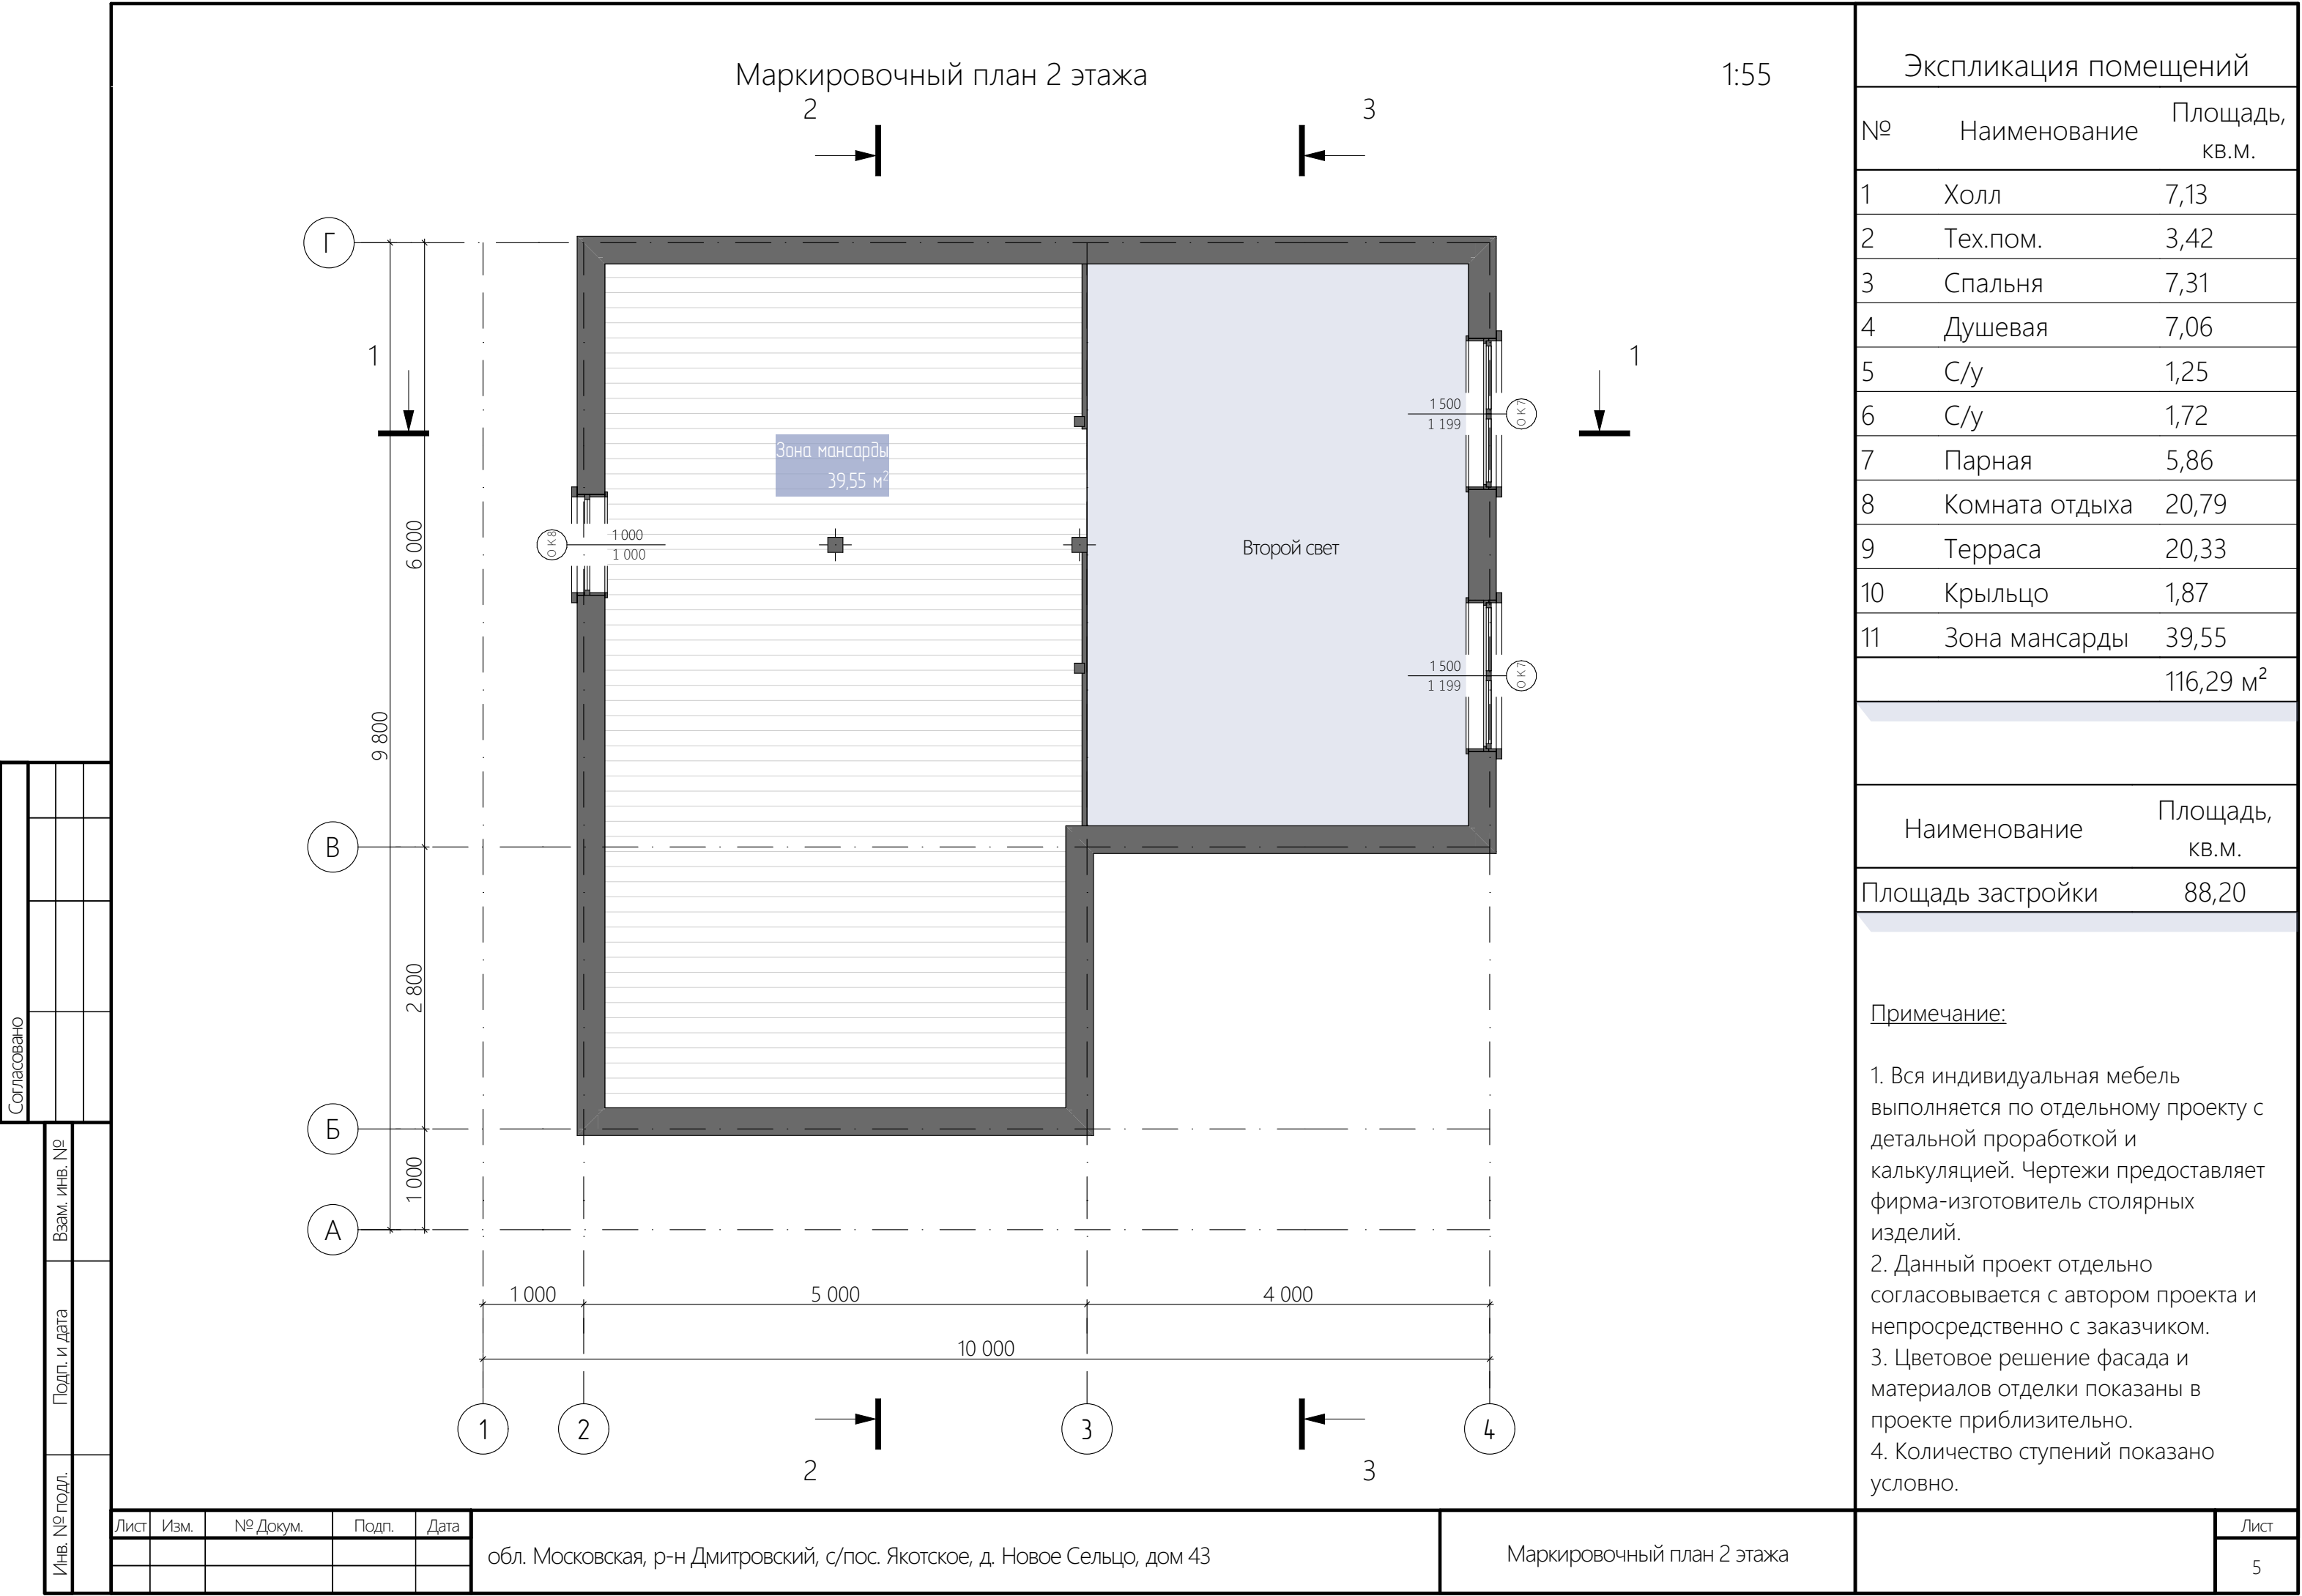

Размерный план 1 этажа

1:55

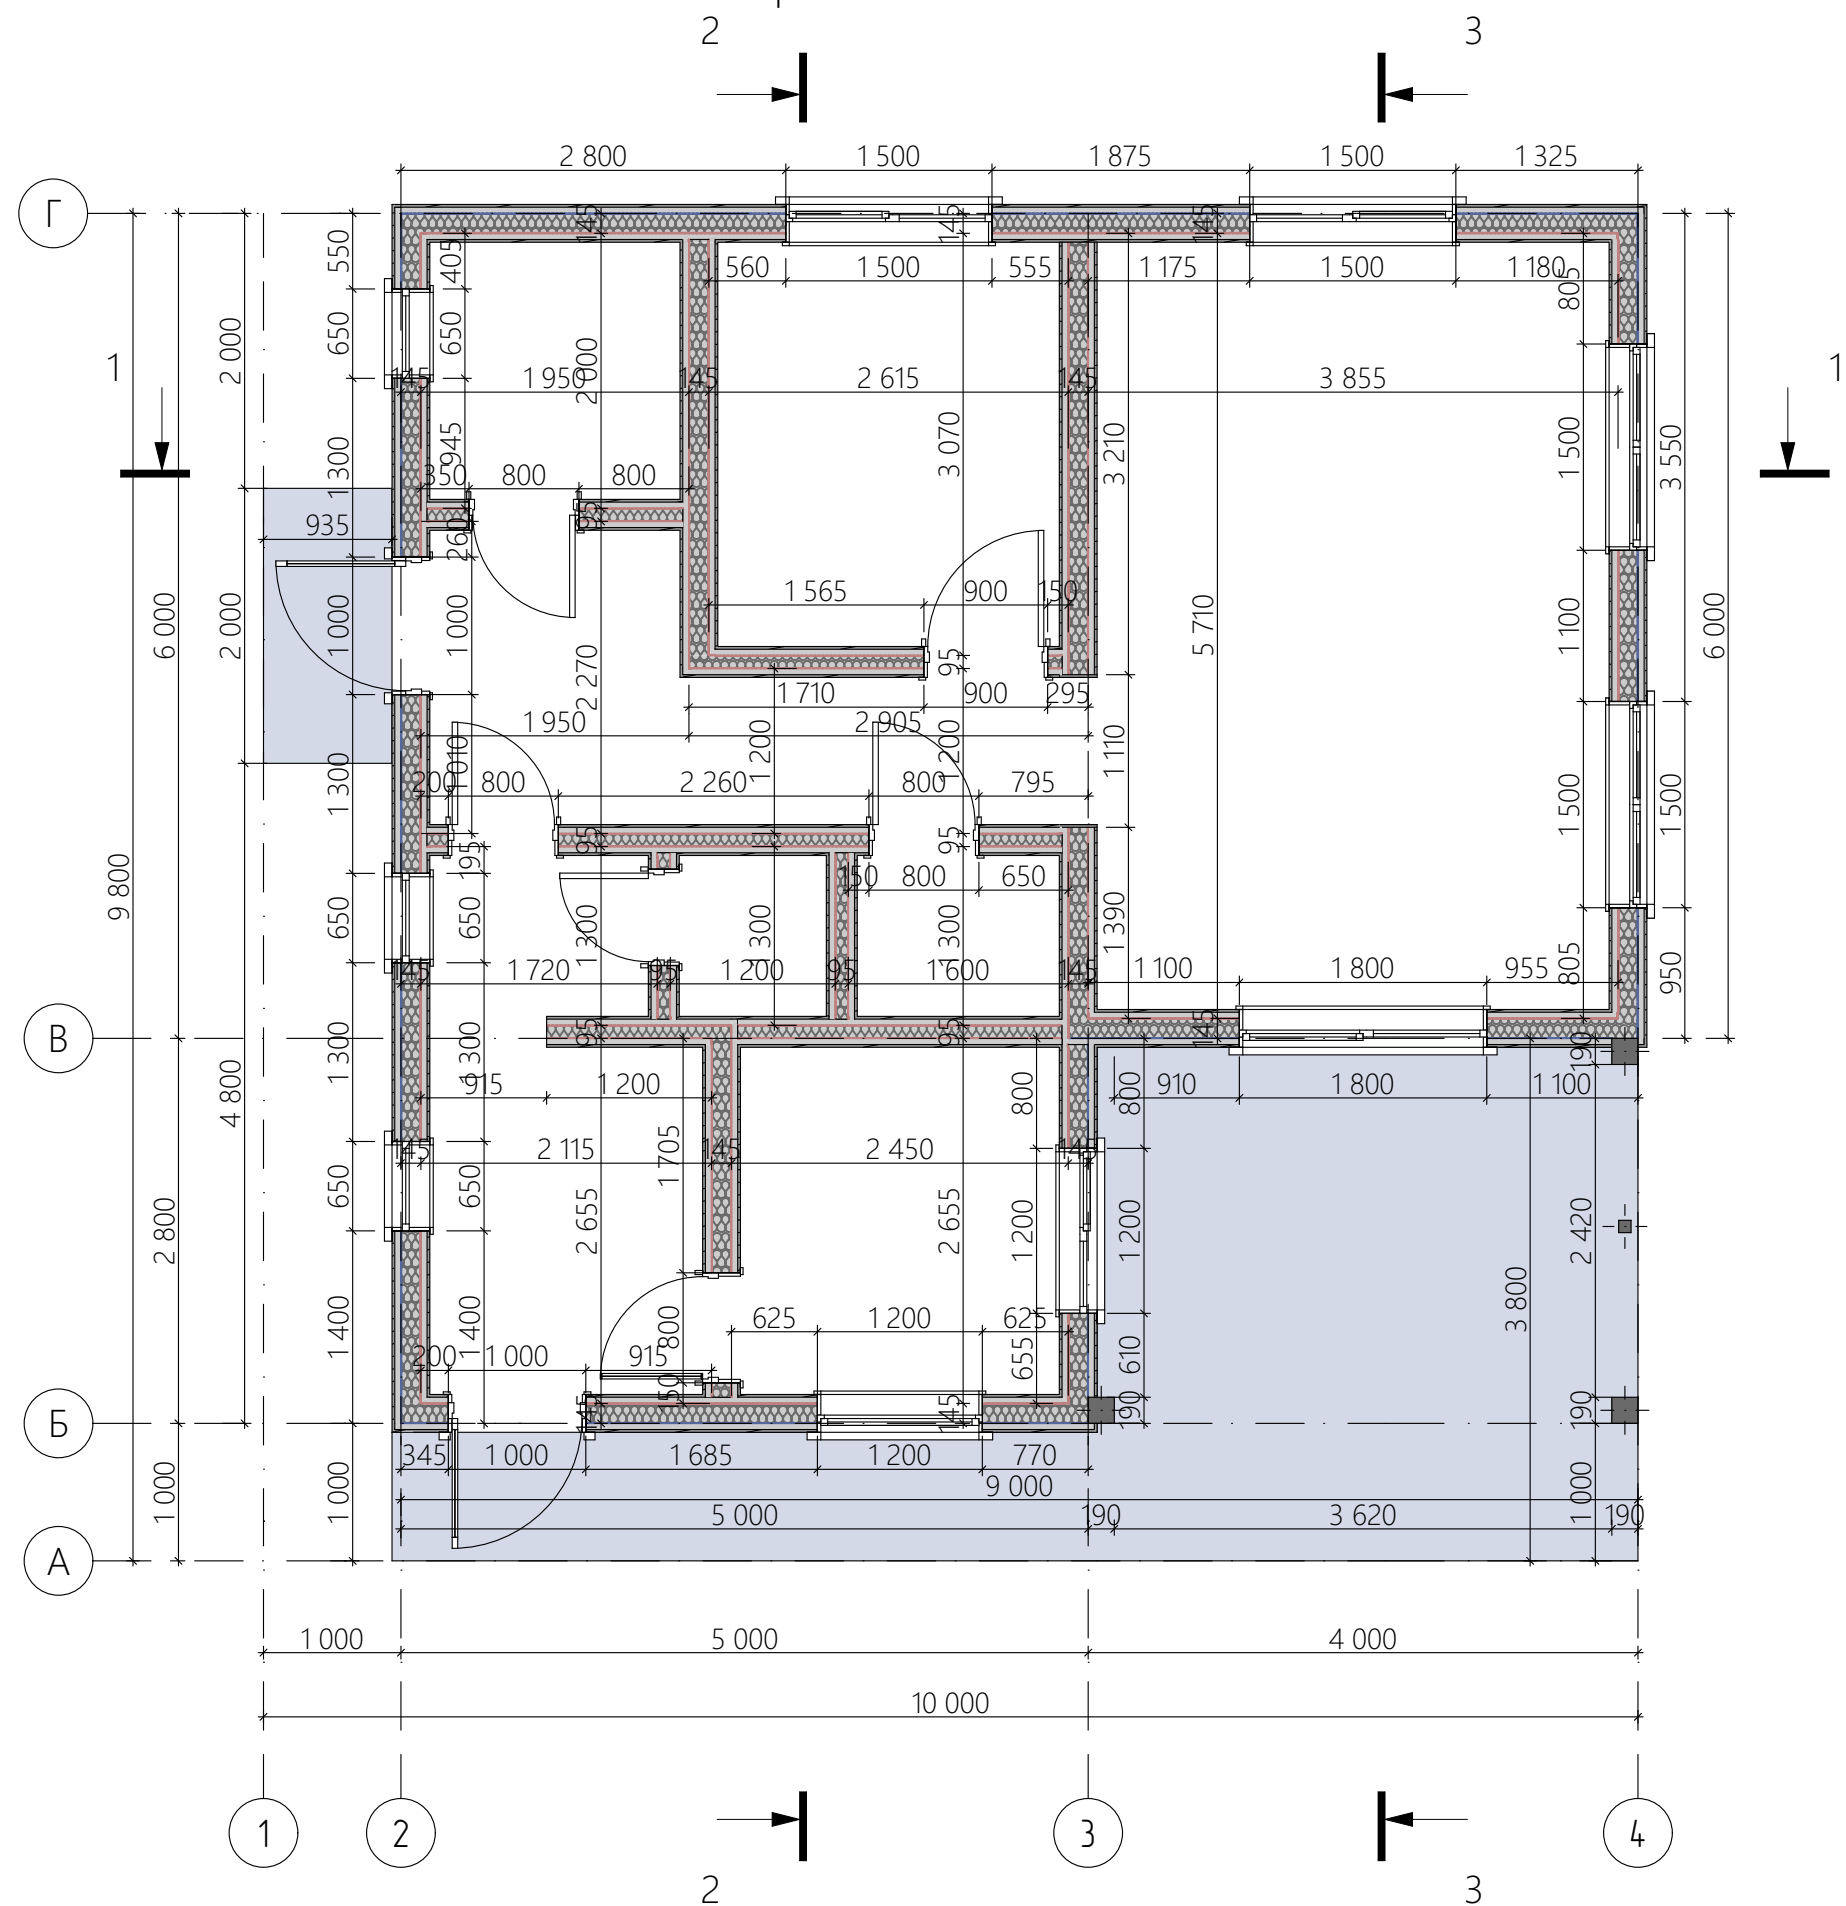

Примечание:

1. Представленные размеры указаны без учета внешней и внутренней отделки

Согласовано				
И/в. № подл.	Подп. и дата	Взам. инв. №		

Лист	Изм.	№ Докум.	Подп.	Дата

обл. Московская, р-н Дмитровский, с/пос. Яотское, д. Новое Сельцо, дом 43


Размерный план 1 этажа

Лист
6

Согласовано					Взам. инв. №		Подп. и дата		Инв. № подл.	

Размерный план 2 этажа

1:55

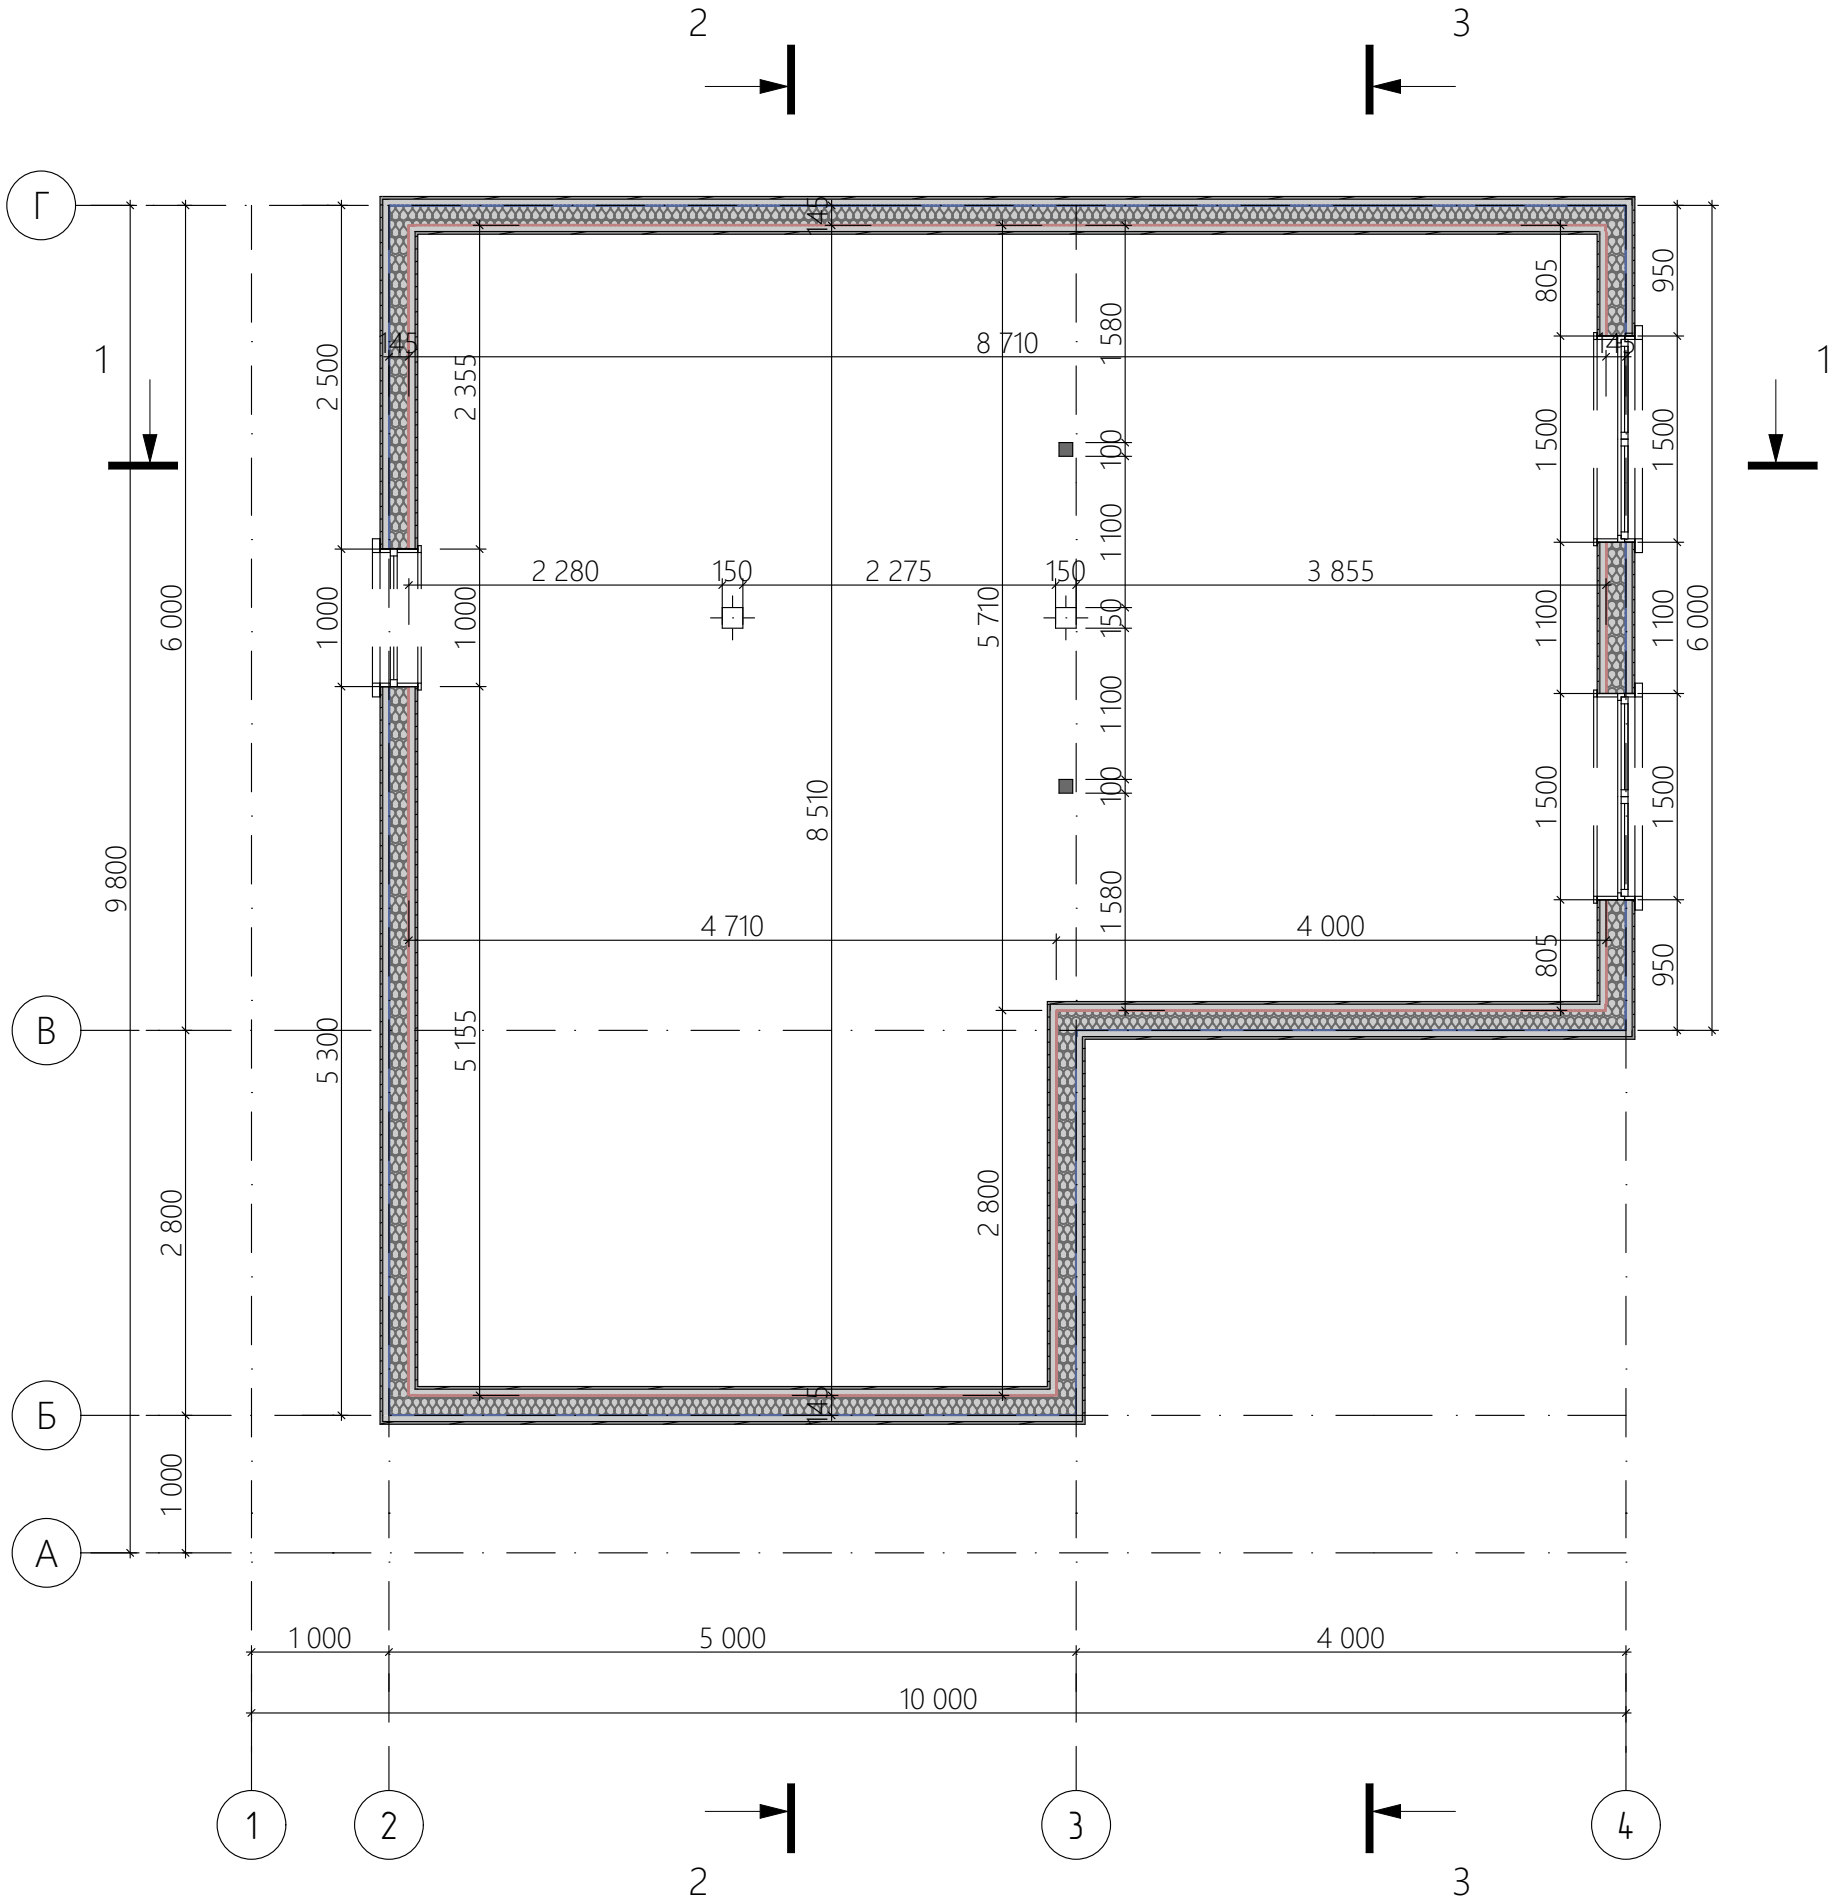

Примечание:

1. Представленные размеры указаны без учета внешней и внутренней отделки


Лист	Изм.	№ Докум.	Подп.	Дата

обл. Московская, р-н Дмитровский, с/пос. Якотское, д. Новое Сельцо, дом 43

Размерный план 2 этажа

Лист
7

1:55

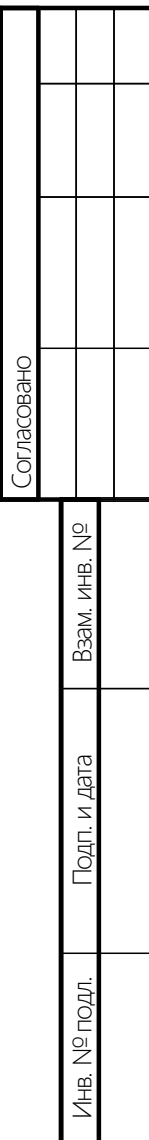

1. Вся индивидуальная мебель выполняется по отдельному проекту с детальной проработкой и калькуляцией. Чертежи предоставляет фирма-изготовитель столярных изделий.
2. Финальные размеры мебели и оборудования указаны ориентировочно — для точной компоновки требуется разработка дизайн-проекта.

Лист	Изм.	№ Докум.	Подп.	Дата

обл. Московская, р-н Дмитровский, с/пос. Якотское, д. Новое Сельцо, дом 43

План расстановки мебели и оборудования 1 этажа


Лист
8

Согласовано

Взам. инв. №

Подп. и дата


Инв. № подл.

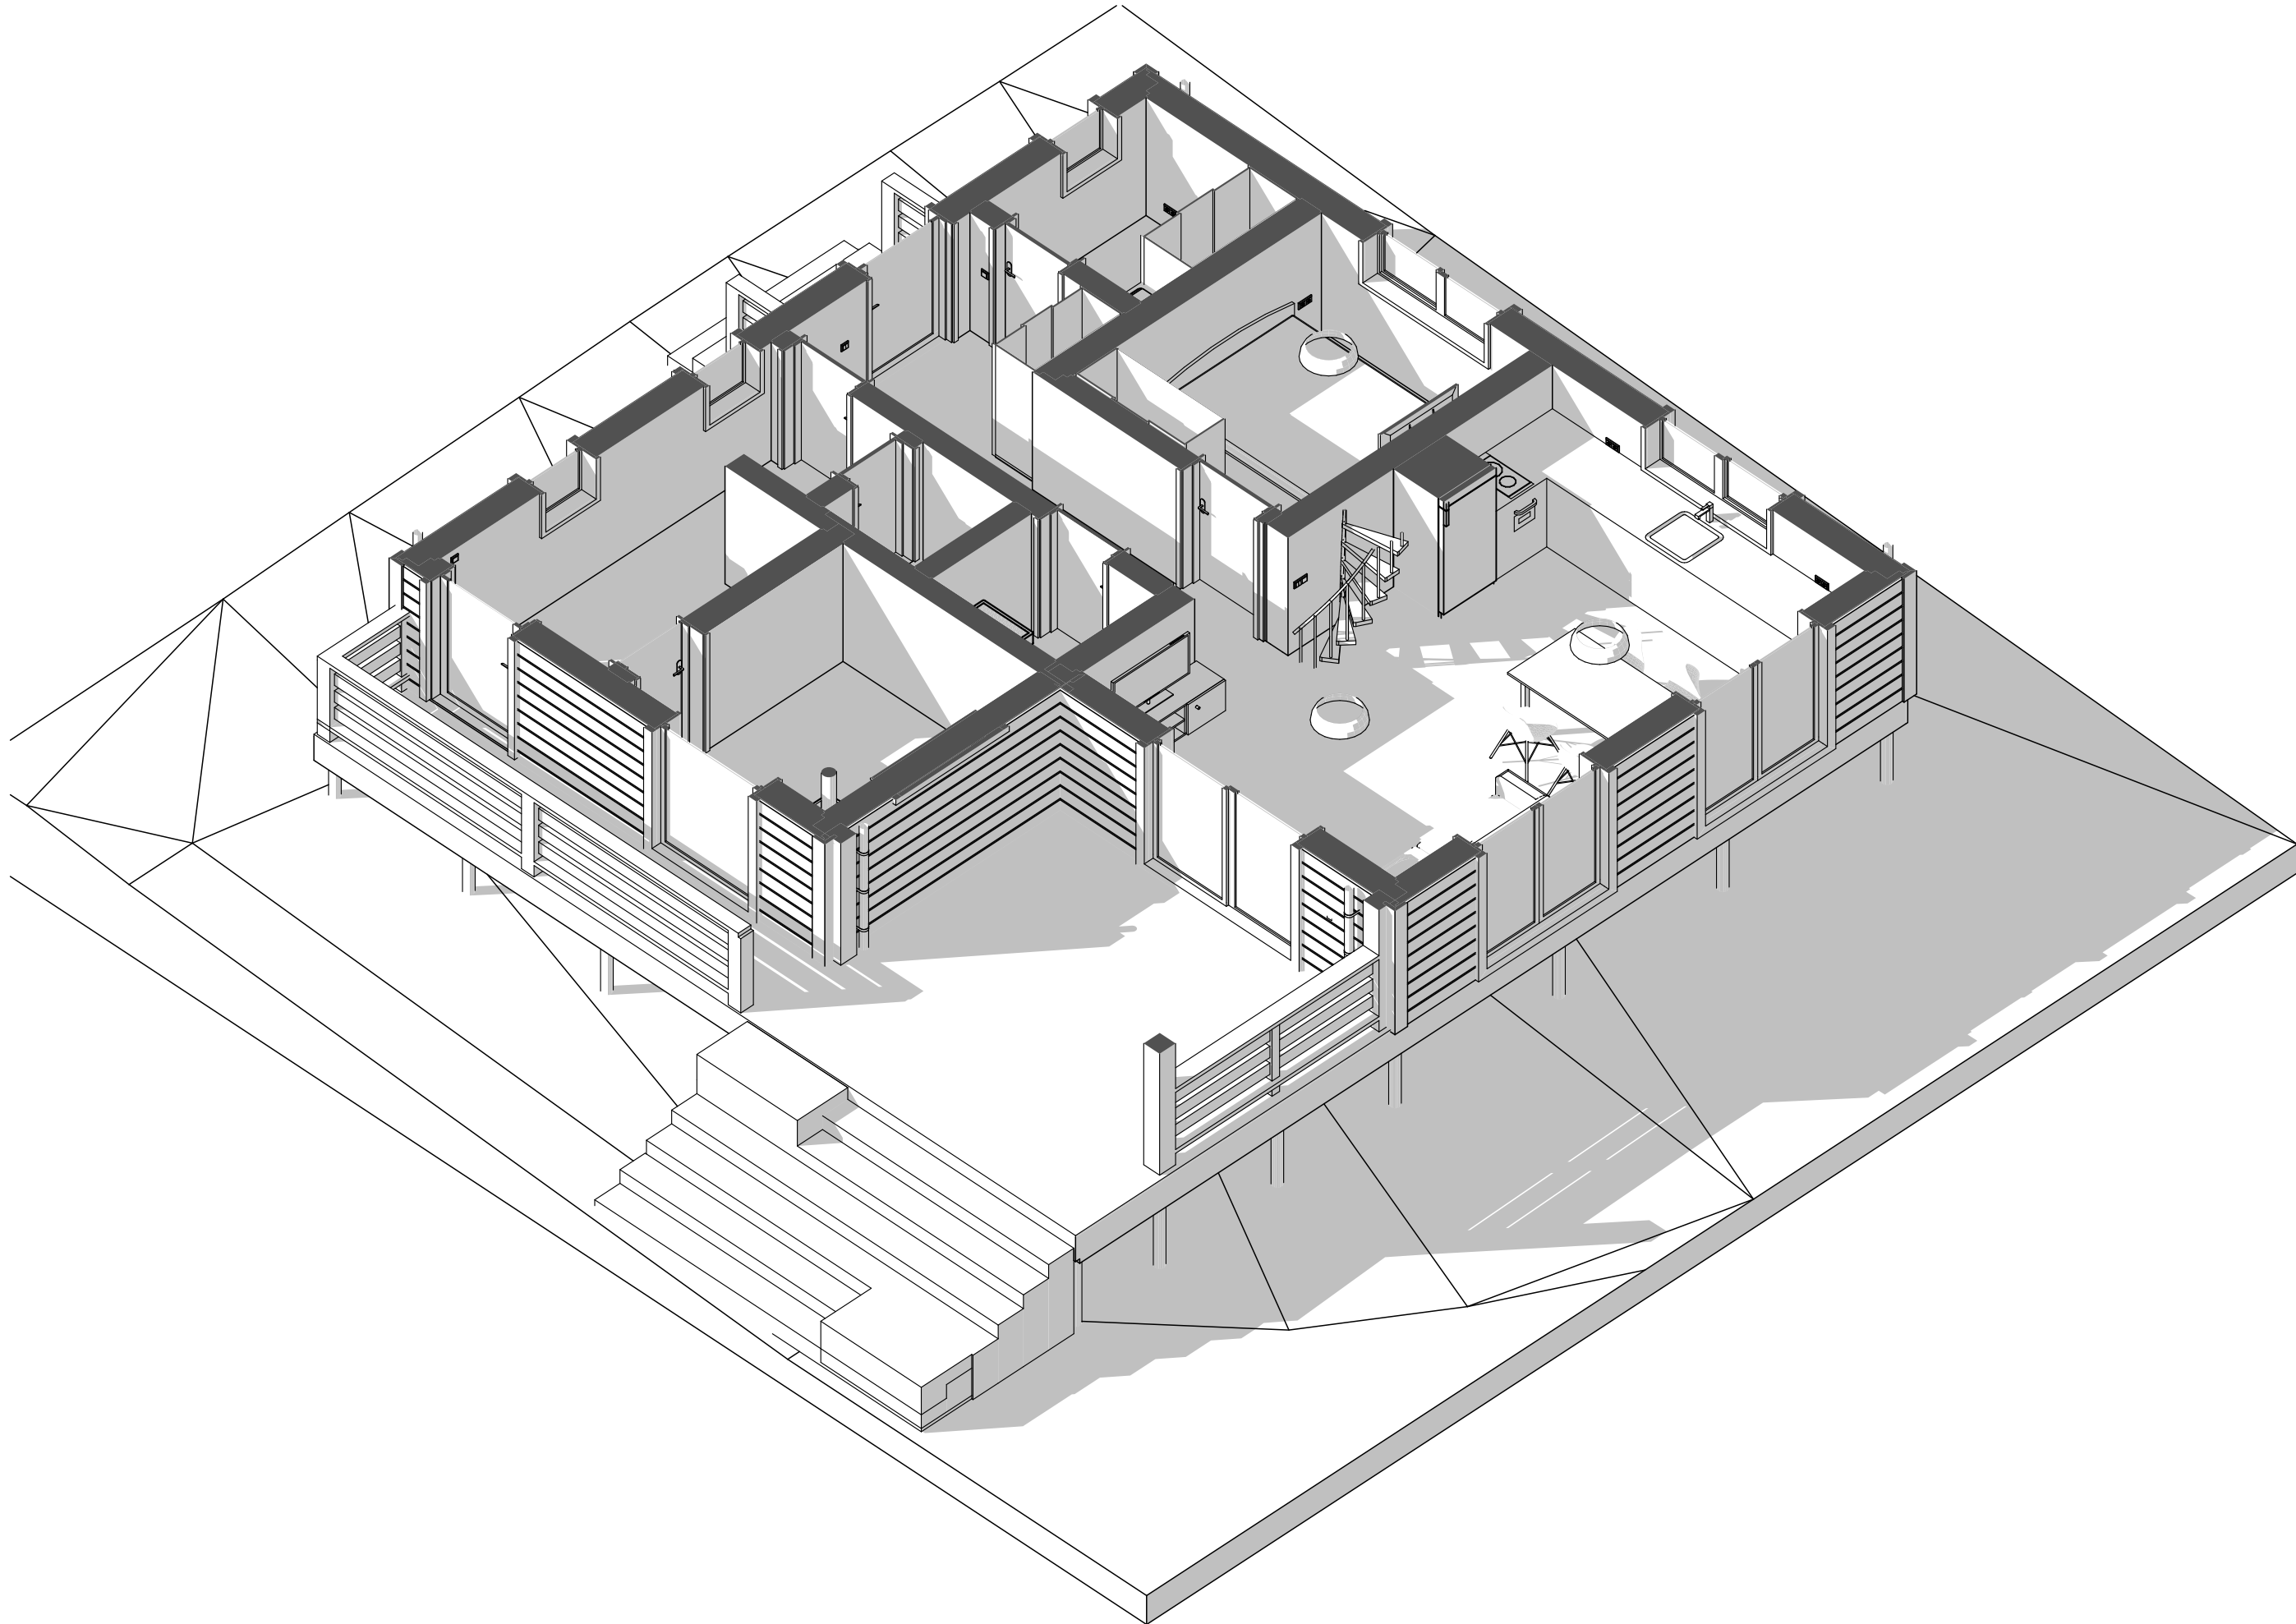





Лист	Изм.	№ Докум.	Подп.	Дата

обл. Московская, р-н Дмитровский, с/пос. Яотское, д. Новое Сельцо, дом 43

Зд-разрез

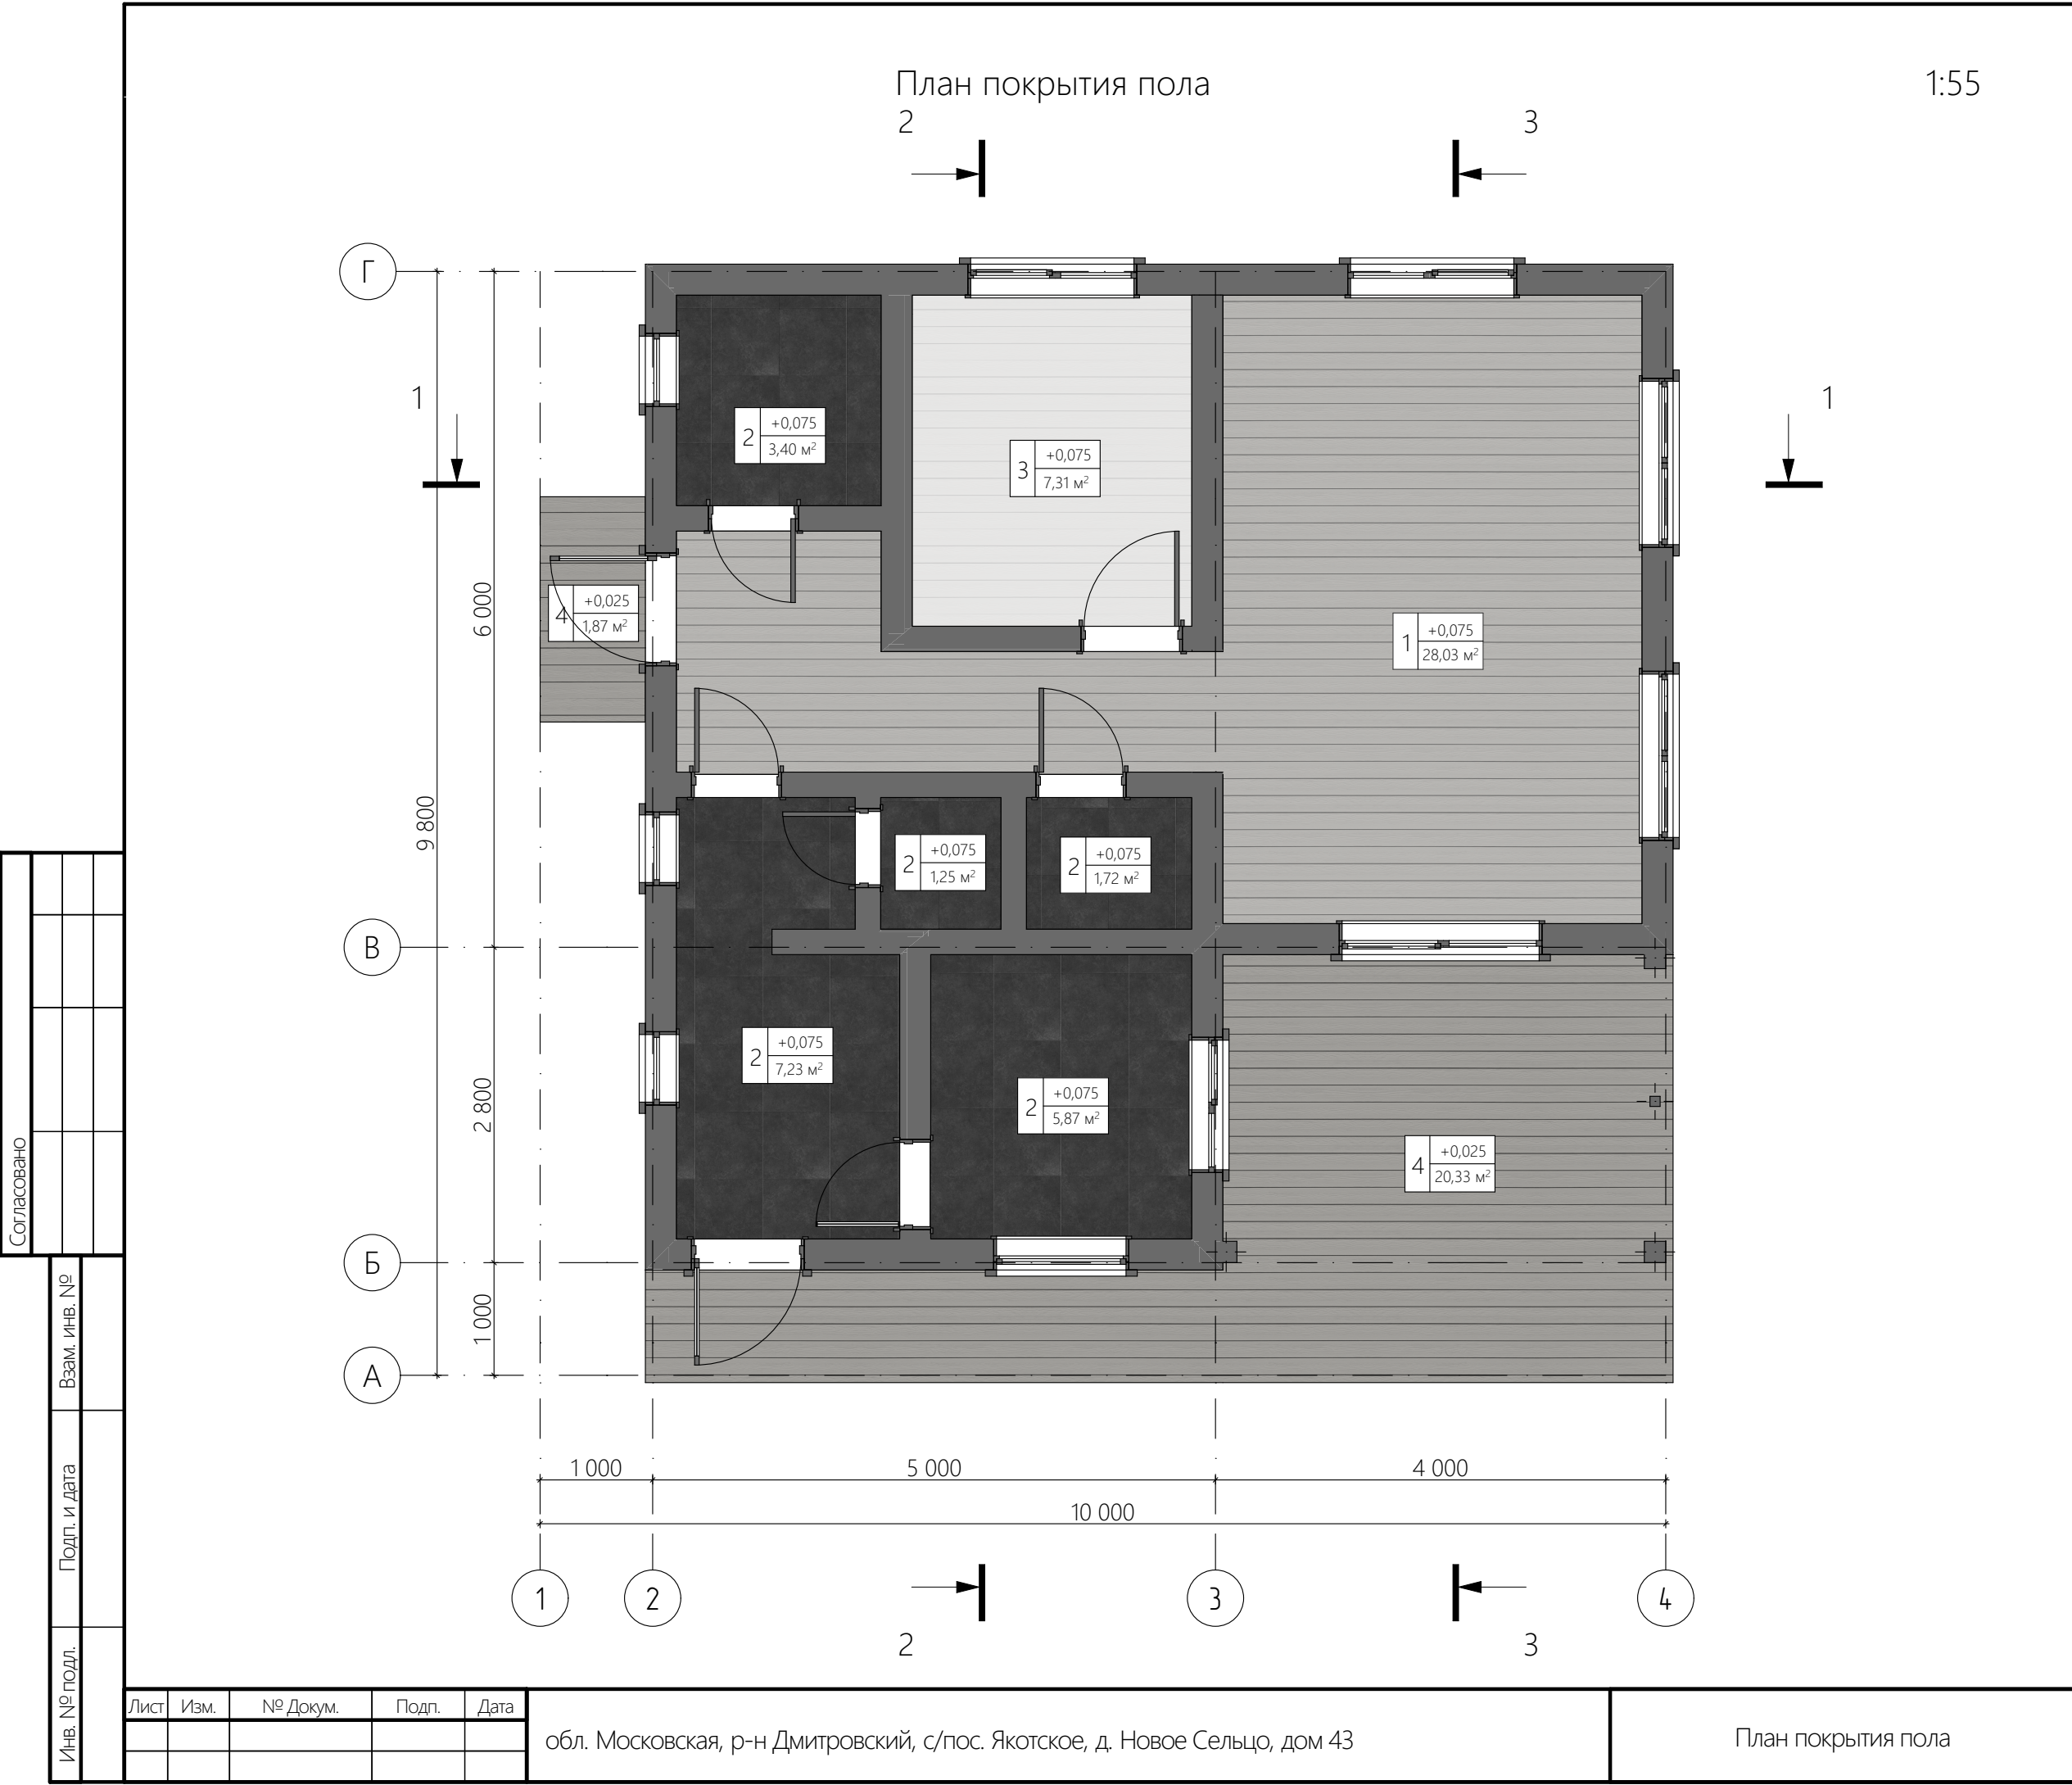


Согласовано				
И-нв. № подл.	Подп. и дата	Взам. инв. №		

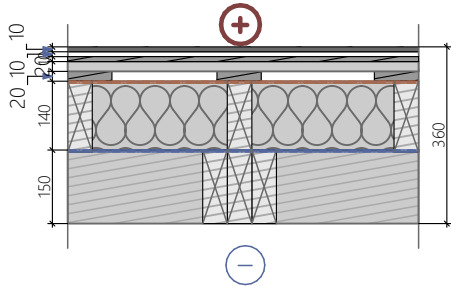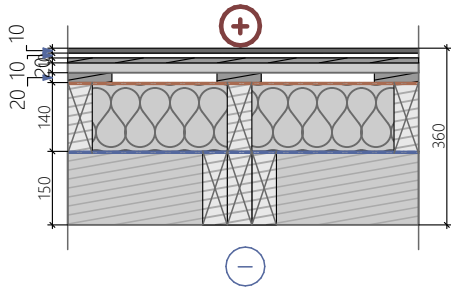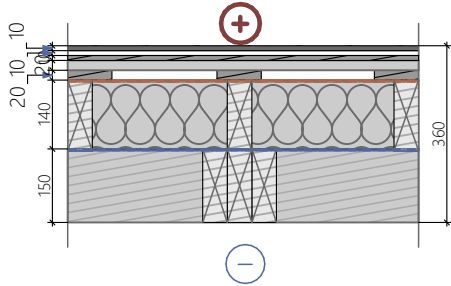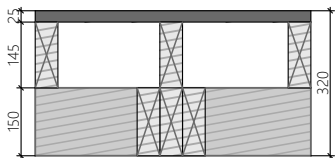Пироги пола																															
№		Наименование			Разрез		Состав																								
		1		Кварцвинил			<table><tr><td>Кварцвинил</td><td>10мм</td></tr><tr><td>Подложка под кварцвинил</td><td>10мм</td></tr><tr><td>ЦСП</td><td>10мм</td></tr><tr><td>Фанера</td><td>20мм</td></tr><tr><td>Вентбрусok (шаг 200мм)</td><td>20мм</td></tr><tr><td>Пароизоляционная мембрана</td><td>-</td></tr><tr><td>Лага перекрытия (утепленная 150мм)</td><td>145мм</td></tr><tr><td>Гидроветрозащитная мембрана</td><td>-</td></tr><tr><td>Просечка (сетка, ячейка 5х5мм)</td><td>-</td></tr><tr><td>Обрешетка (шаг 400мм)</td><td>25мм</td></tr><tr><td>Нижняя обвязка - 3 сросшенная доска</td><td>150мм</td></tr></table>			Кварцвинил	10мм	Подложка под кварцвинил	10мм	ЦСП	10мм	Фанера	20мм	Вентбрусok (шаг 200мм)	20мм	Пароизоляционная мембрана	-	Лага перекрытия (утепленная 150мм)	145мм	Гидроветрозащитная мембрана	-	Просечка (сетка, ячейка 5х5мм)	-	Обрешетка (шаг 400мм)	25мм	Нижняя обвязка - 3 сросшенная доска	150мм
							Кварцвинил	10мм																							
							Подложка под кварцвинил	10мм																							
							ЦСП	10мм																							
Фанера	20мм																														
Вентбрусok (шаг 200мм)	20мм																														
Пароизоляционная мембрана	-																														
Лага перекрытия (утепленная 150мм)	145мм																														
Гидроветрозащитная мембрана	-																														
Просечка (сетка, ячейка 5х5мм)	-																														
Обрешетка (шаг 400мм)	25мм																														
Нижняя обвязка - 3 сросшенная доска	150мм																														
		2		Керамогранит			<table><tr><td>Керамогранит</td><td>10мм</td></tr><tr><td>Клей</td><td>10мм</td></tr><tr><td>ЦСП</td><td>10мм</td></tr><tr><td>Фанера</td><td>20мм</td></tr><tr><td>Вентбрусok (шаг 200мм)</td><td>20мм</td></tr><tr><td>Пароизоляционная мембрана</td><td>-</td></tr><tr><td>Лага перекрытия (утепленная 150мм)</td><td>145мм</td></tr><tr><td>Гидроветрозащитная мембрана</td><td>-</td></tr><tr><td>Просечка (сетка, ячейка 5х5мм)</td><td>-</td></tr><tr><td>Обрешетка (шаг 400мм)</td><td>25мм</td></tr><tr><td>Нижняя обвязка - 3 сросшенная доска</td><td>150мм</td></tr></table>			Керамогранит	10мм	Клей	10мм	ЦСП	10мм	Фанера	20мм	Вентбрусok (шаг 200мм)	20мм	Пароизоляционная мембрана	-	Лага перекрытия (утепленная 150мм)	145мм	Гидроветрозащитная мембрана	-	Просечка (сетка, ячейка 5х5мм)	-	Обрешетка (шаг 400мм)	25мм	Нижняя обвязка - 3 сросшенная доска	150мм
							Керамогранит	10мм																							
							Клей	10мм																							
							ЦСП	10мм																							
Фанера	20мм																														
Вентбрусok (шаг 200мм)	20мм																														
Пароизоляционная мембрана	-																														
Лага перекрытия (утепленная 150мм)	145мм																														
Гидроветрозащитная мембрана	-																														
Просечка (сетка, ячейка 5х5мм)	-																														
Обрешетка (шаг 400мм)	25мм																														
Нижняя обвязка - 3 сросшенная доска	150мм																														
		3		Ламинат			<table><tr><td>Ламинат</td><td>10мм</td></tr><tr><td>Подложка под ламинат</td><td>10мм</td></tr><tr><td>ЦСП</td><td>10мм</td></tr><tr><td>Фанера</td><td>20мм</td></tr><tr><td>Вентбрусok (шаг 200мм)</td><td>20мм</td></tr><tr><td>Пароизоляционная мембрана</td><td>-</td></tr><tr><td>Лага перекрытия (утепленная 150мм)</td><td>145мм</td></tr><tr><td>Гидроветрозащитная мембрана</td><td>-</td></tr><tr><td>Просечка (сетка, ячейка 5х5мм)</td><td>-</td></tr><tr><td>Обрешетка (шаг 400мм)</td><td>25мм</td></tr><tr><td>Нижняя обвязка - 3 сросшенная доска</td><td>150мм</td></tr></table>			Ламинат	10мм	Подложка под ламинат	10мм	ЦСП	10мм	Фанера	20мм	Вентбрусok (шаг 200мм)	20мм	Пароизоляционная мембрана	-	Лага перекрытия (утепленная 150мм)	145мм	Гидроветрозащитная мембрана	-	Просечка (сетка, ячейка 5х5мм)	-	Обрешетка (шаг 400мм)	25мм	Нижняя обвязка - 3 сросшенная доска	150мм
							Ламинат	10мм																							
							Подложка под ламинат	10мм																							
							ЦСП	10мм																							
Фанера	20мм																														
Вентбрусok (шаг 200мм)	20мм																														
Пароизоляционная мембрана	-																														
Лага перекрытия (утепленная 150мм)	145мм																														
Гидроветрозащитная мембрана	-																														
Просечка (сетка, ячейка 5х5мм)	-																														
Обрешетка (шаг 400мм)	25мм																														
Нижняя обвязка - 3 сросшенная доска	150мм																														
		4		ДПК			<table><tr><td>-ДПК</td><td>25мм</td></tr><tr><td>-Лага перкрытия (шаг 400мм)</td><td>145мм</td></tr><tr><td>-Нижняя обвязка (тройная сросшенная доска)</td><td>150мм</td></tr></table>			-ДПК	25мм	-Лага перкрытия (шаг 400мм)	145мм	-Нижняя обвязка (тройная сросшенная доска)	150мм																
							-ДПК	25мм																							
							-Лага перкрытия (шаг 400мм)	145мм																							
							-Нижняя обвязка (тройная сросшенная доска)	150мм																							
Лист		Изм.	№ Докум.	Подп.	Дата	Пироги пола		Лист																							
								11																							

План покрытия стен

1:55

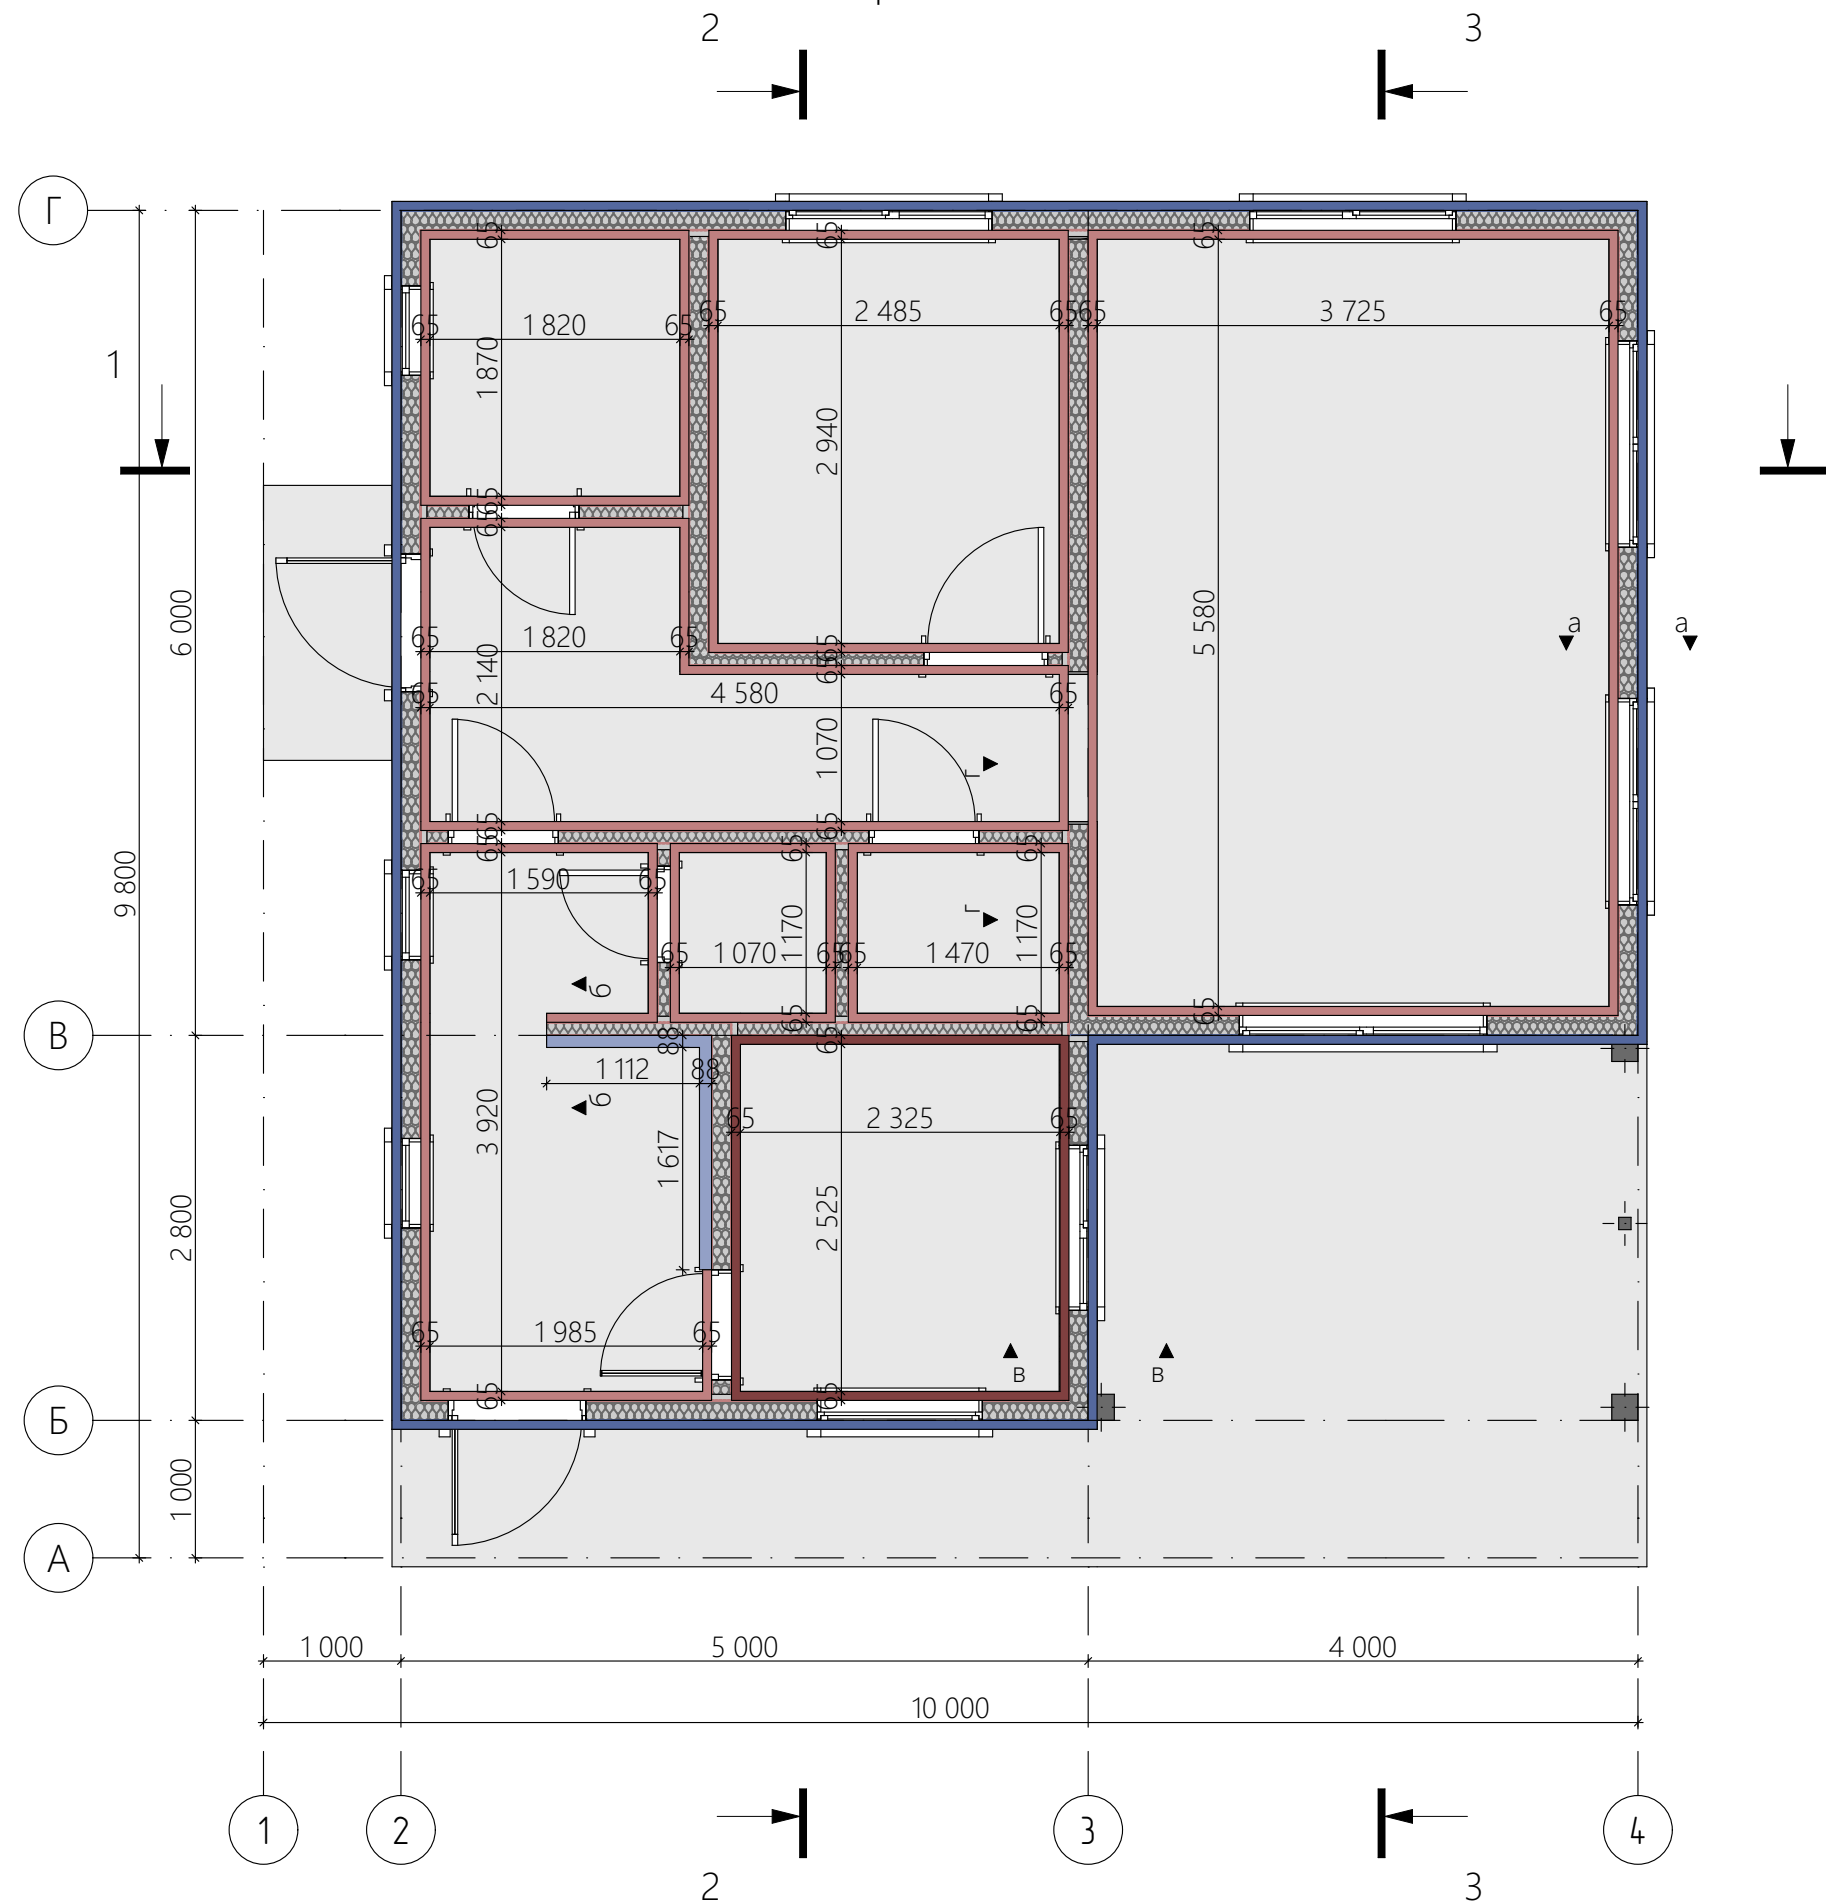

Экспликация покрытий стен

№	Наименование	Условное обозначение
1	Фиброцементный сайдинг (20мм)	
2	Имитация бруса (20мм)	
3	Керамогранит (10мм)	
5	Вагонка (20мм)	

Инва. № подл.	Подп. и дата	Взам. инв. №	Согласовано

Лист	Изм.	№ Докум.	Подп.	Дата

обл. Московская, р-н Дмитровский, с/пос. Якотское, д. Новое Сельцо, дом 43

План покрытия стен


Пироги стен

№ разреза

Сечение


Состав

а-а

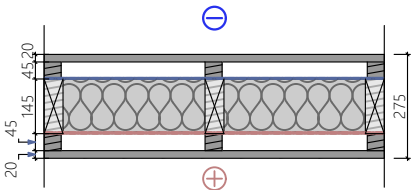


- Фиброцементный сайдинг 20мм
- Вентбрусок (вертикально) 45мм
- Гидро-ветрозащитная мембрана -
- Стойка каркаса (утепленная) 145мм
- Пароизоляционная мембрана -
- Вентбрусок (вертикально) 45мм
- Имитация бруса 20мм

б-б

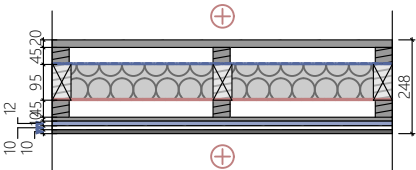


- Имитация бруса 20мм
- Вентбрусок (вертикально) 45мм
- Пароизоляционная мембрана -
- Стойка каркаса (утепленная) 145мм
- Пароизоляционная мембрана -
- Вентбрусок (вертикально) 45мм
- ОСБ 10мм
- ЦСП 12мм
- Клей 10мм
- Керамогранит 10мм

в-в

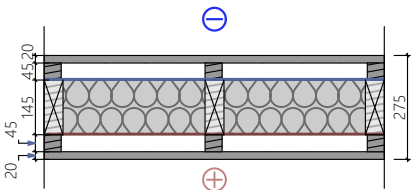

- Фиброцементный сайдинг 20мм
- Вентбрусок (вертикально) 45мм
- Гидро-ветрозащитная мембрана -
- Стойка каркаса (утепленная) 145мм
- Пароизоляционная мембрана (алюм. фольга) -
- Вентбрусок (вертикально) 45мм
- Вагонка 20мм

г-г

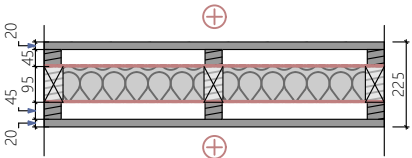

- Имитация бруса 20мм
- Вентбрусок (вертикально) 45мм
- Пароизоляционная мембрана -
- Стойка каркаса (утепленная) 95мм
- Пароизоляционная мембрана -
- Вентбрусок (вертикально) 45мм
- Имитация бруса 20мм

Согласовано

Взам. инв. №

Подп. и дата

Инв. № подл.

Лист	Изм.	№ Докум.	Подп.	Дата

Пироги стен


Лист

13

Согласовано				
И.нв. № подл.	Подп. и дата	Взам. инв. №		

План размещения розеток 1 этажа

1:55

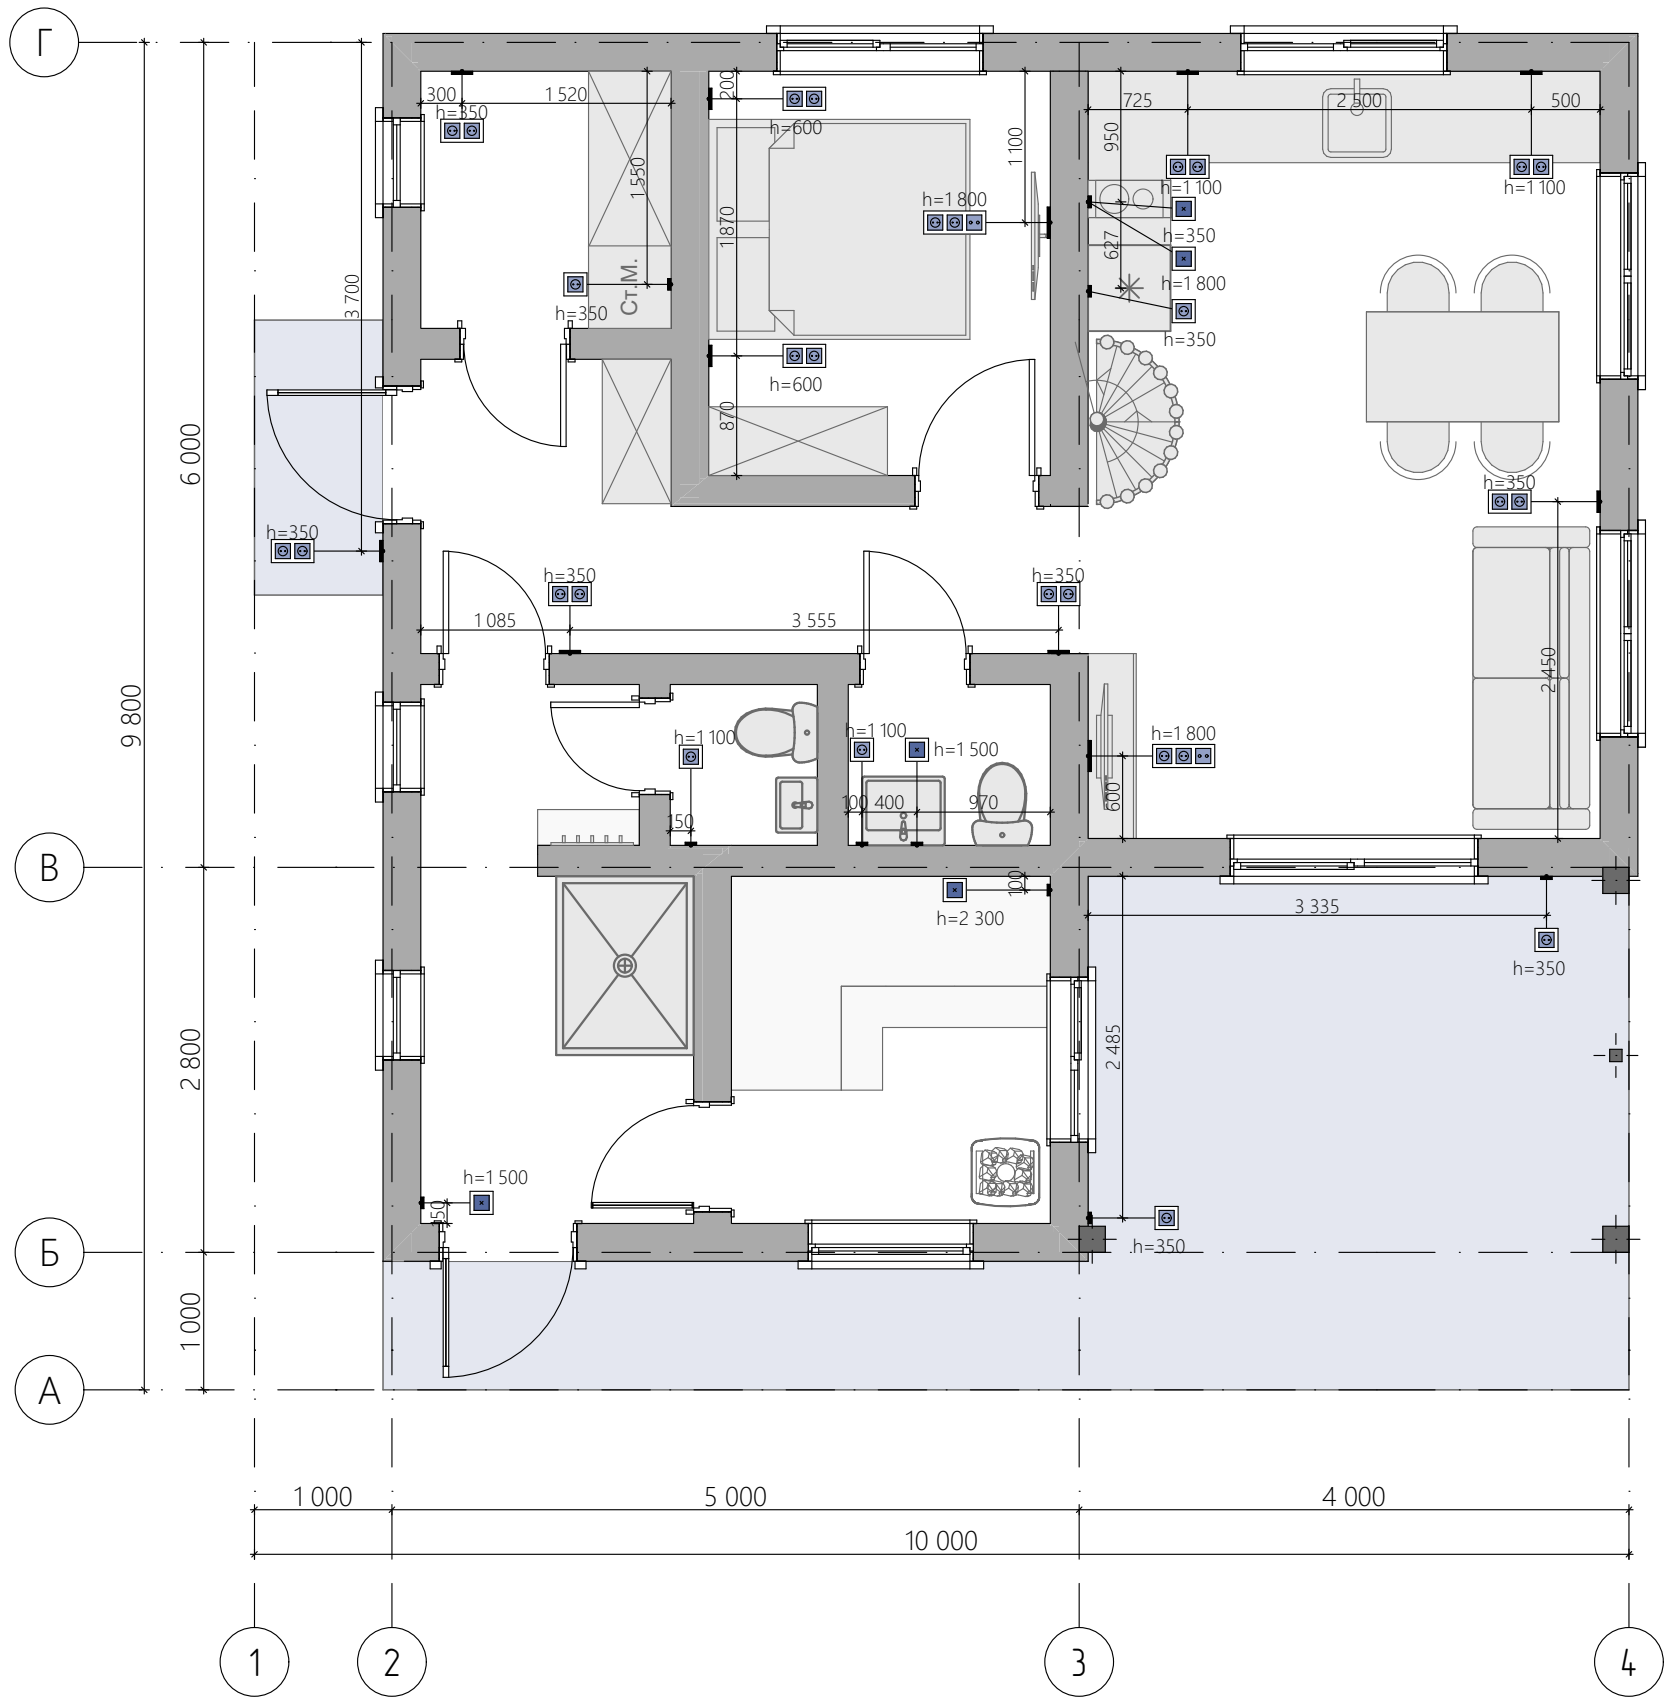

Экспликация розеток

Наименование	2д-вид	Кол-во
Розетка 220v (рамка 1 секции)		9
Розетка 220v (рамка 2 секции)		9
Розетка 220v+ТВ розетка (рамка 2 секции)		2
Эл. вывод		5
		25

Примечание:

1. Схема размещения розеток является рекомендательной и требует согласования с заказчиком по месту.

2. Все высоты даны от чистового пола.


3. Все указанные размеры даются до центра позиций.

4. Отметки розеток, выключателей, выводов и др. оборудования, являются предварительными и уточняются после выбора финишных материалов и мебели.

5. Размеры уточняются дополнительно

Лист	Изм.	№ Докум.	Подп.	Дата


Согласовано				
И-нв. № подл.	Подп. и дата	Взам. инв. №		

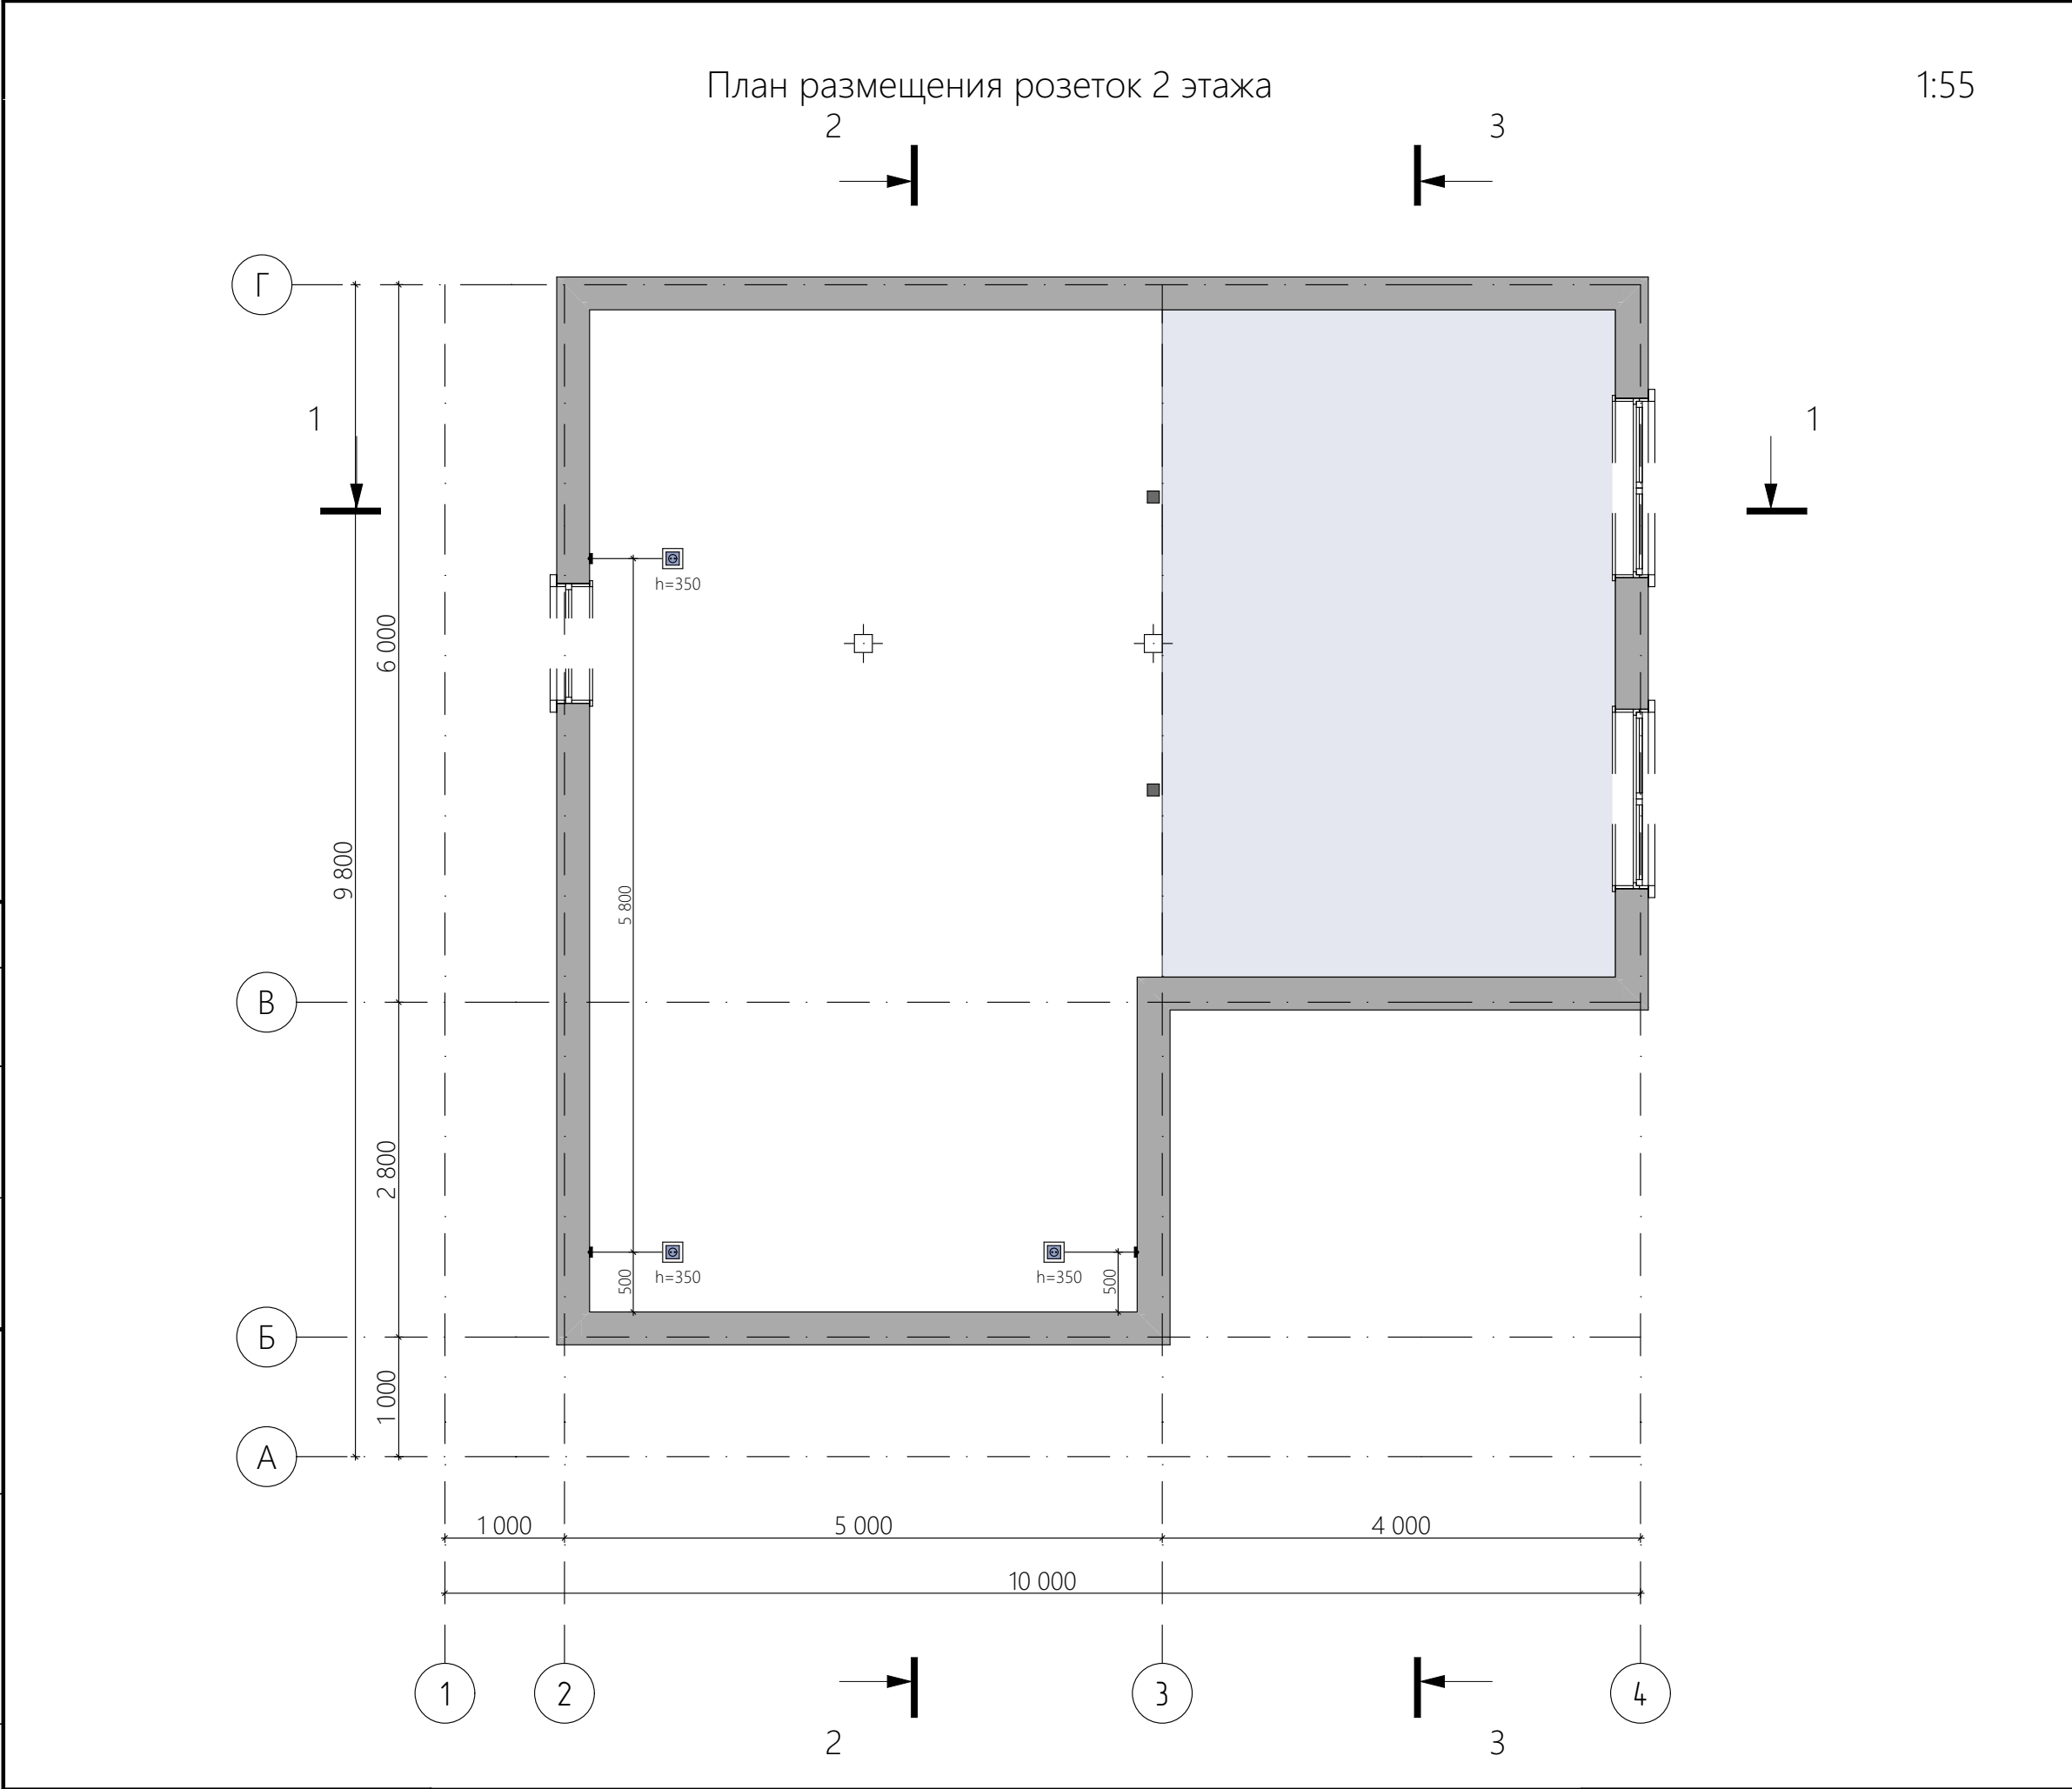

Экспликация розеток		
Наименование	2д-вид	Кол-во
Розетка 220v (рамка 1 секции)		9
Розетка 220v (рамка 2 секции)		9
Розетка 220v+ТВ розетка (рамка 2 секции)		2
Эл. вывод		5
		25
Примечание:		
1. Схема размещения розеток является рекомендательной и требует согласования с заказчиком по месту. 2. Все высоты даны от чистового пола. 3. Все указанные размеры даются до центра позиций. 4. Отметки розеток, выключателей, выводов и др. оборудования, являются предварительными и уточняются после выбора финишных материалов и мебели. 5. Размеры уточняются дополнительно		
		Лист
		15

План размещения светильников и выключателей

1:55

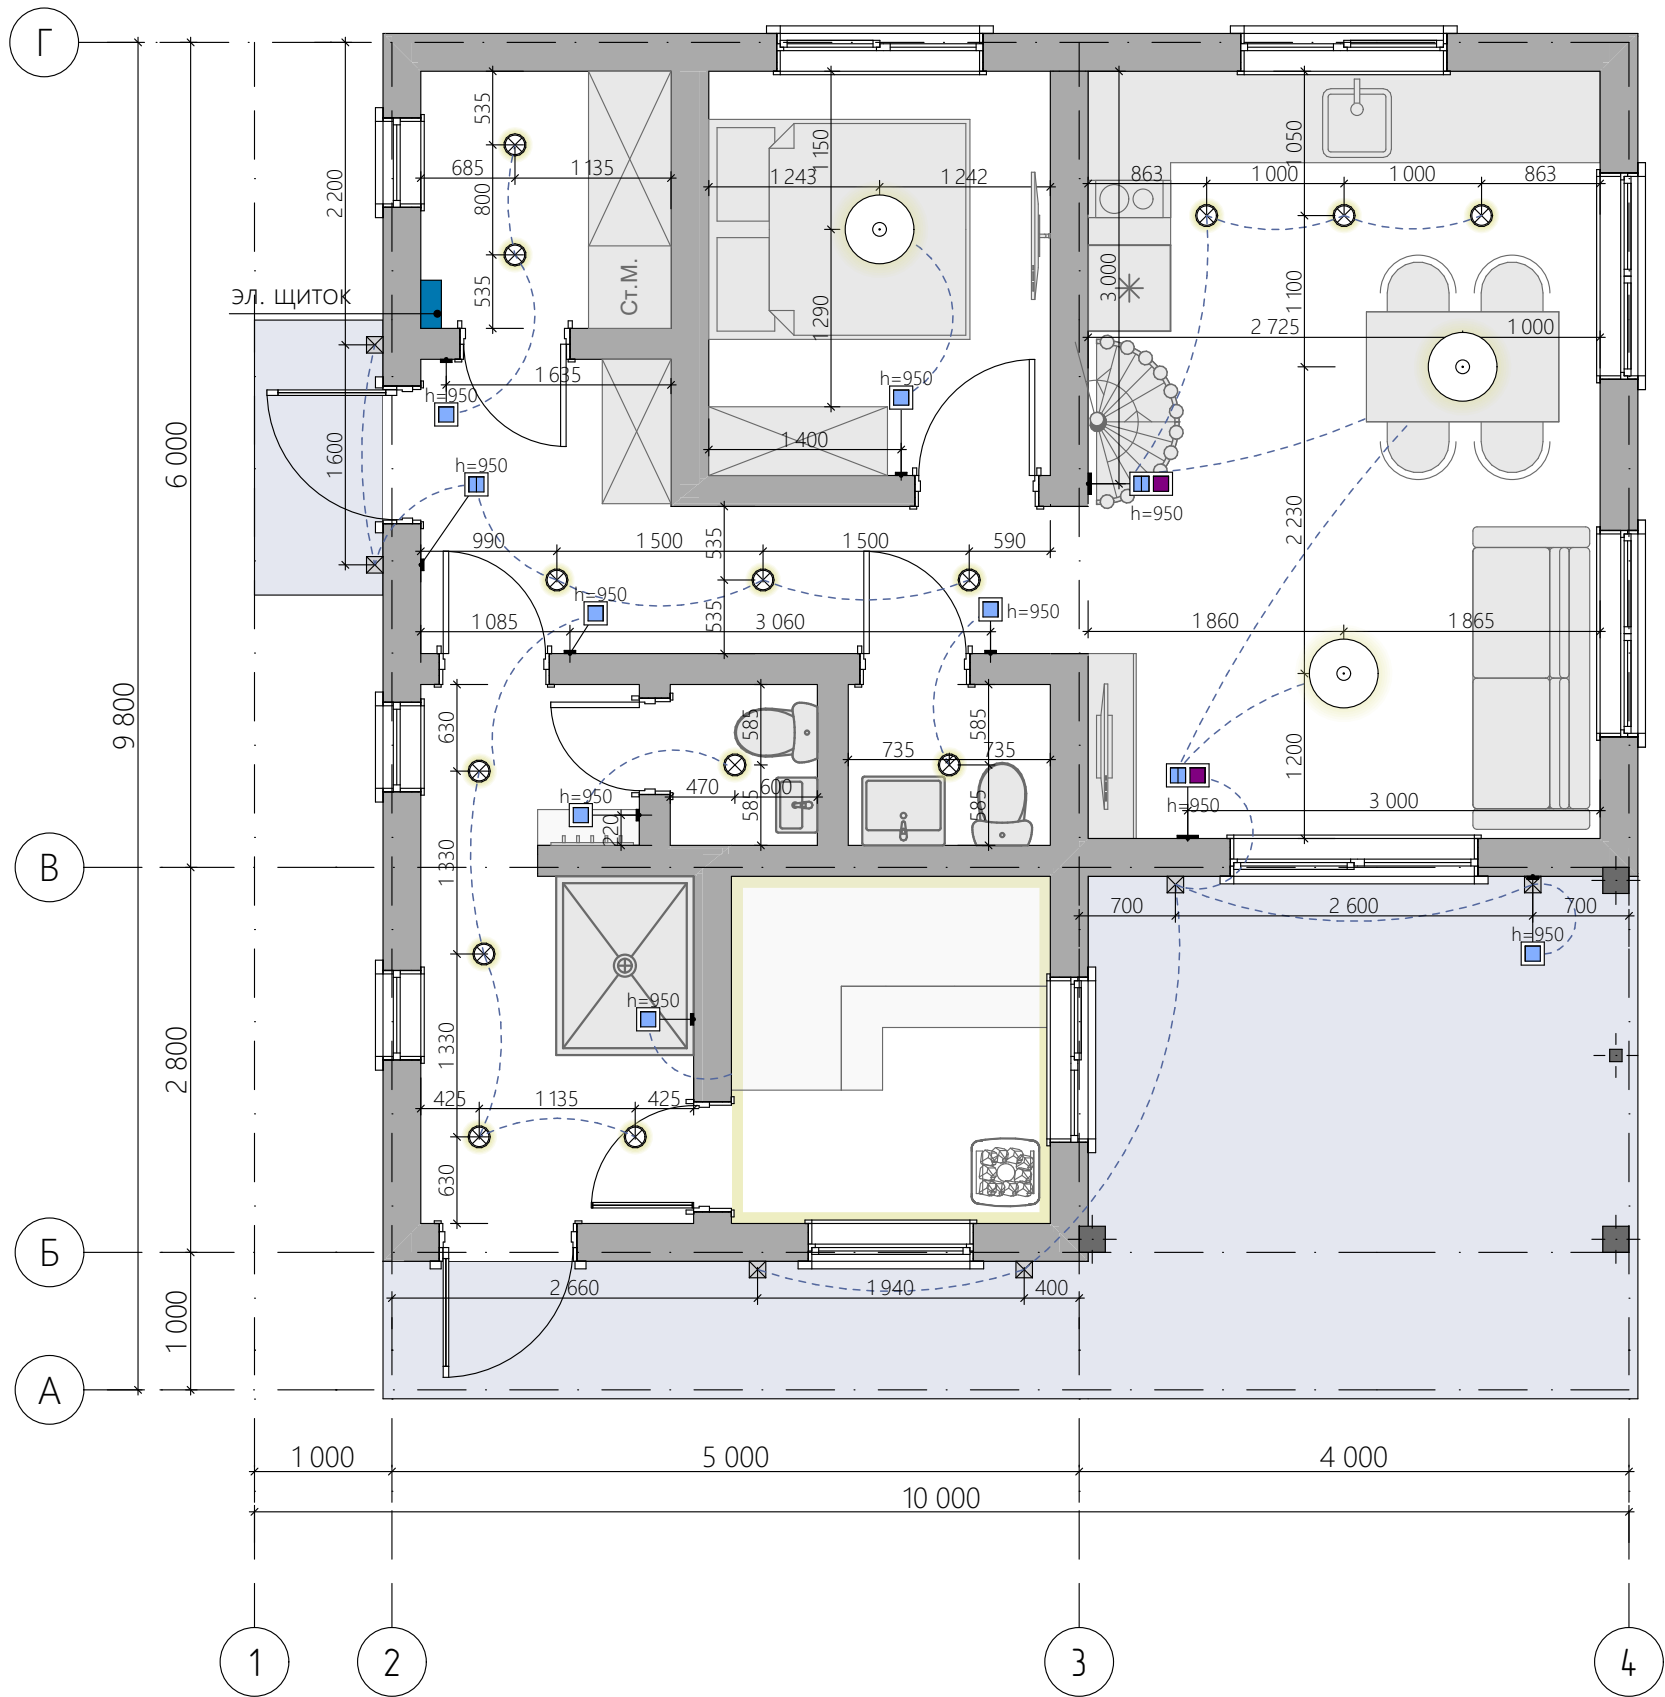

Экспликация светильников и выключателей

Наименование	2д-вид	Кол-во
Выключатель двухклавишный (рамка 1 секции)		1
Выключатель одно- и двухклавишный (рамка 2 секции)		3
Выключатель одноклавишный (рамка 1 секции)		7
Светильник точечный		18
Светильник подвесной		3
Уличный светильник		6
		38

Примечание:

1. Схема размещения розеток является рекомендательной и требует согласования с заказчиком по месту.
2. Все высоты даны от чистового пола.
3. Все указанные размеры даются до центра позиций.
4. Отметки розеток, выключателей, выводов и др. оборудования, являются предварительными и уточняются после выбора финишных материалов и мебели.
5. Размеры уточняются дополнительно

Согласовано

Взам. инв. №

Подп. и дата

Инв. № подл.


Лист	Изм.	№ Докум.	Подп.	Дата

обл. Московская, р-н Дмитровский, с/пос. Яотское, д. Новое Сельцо, дом 43

План размещения светильников и выключателей 1 этажа

План размещения светильников и выключателей 2 этажа

1:55

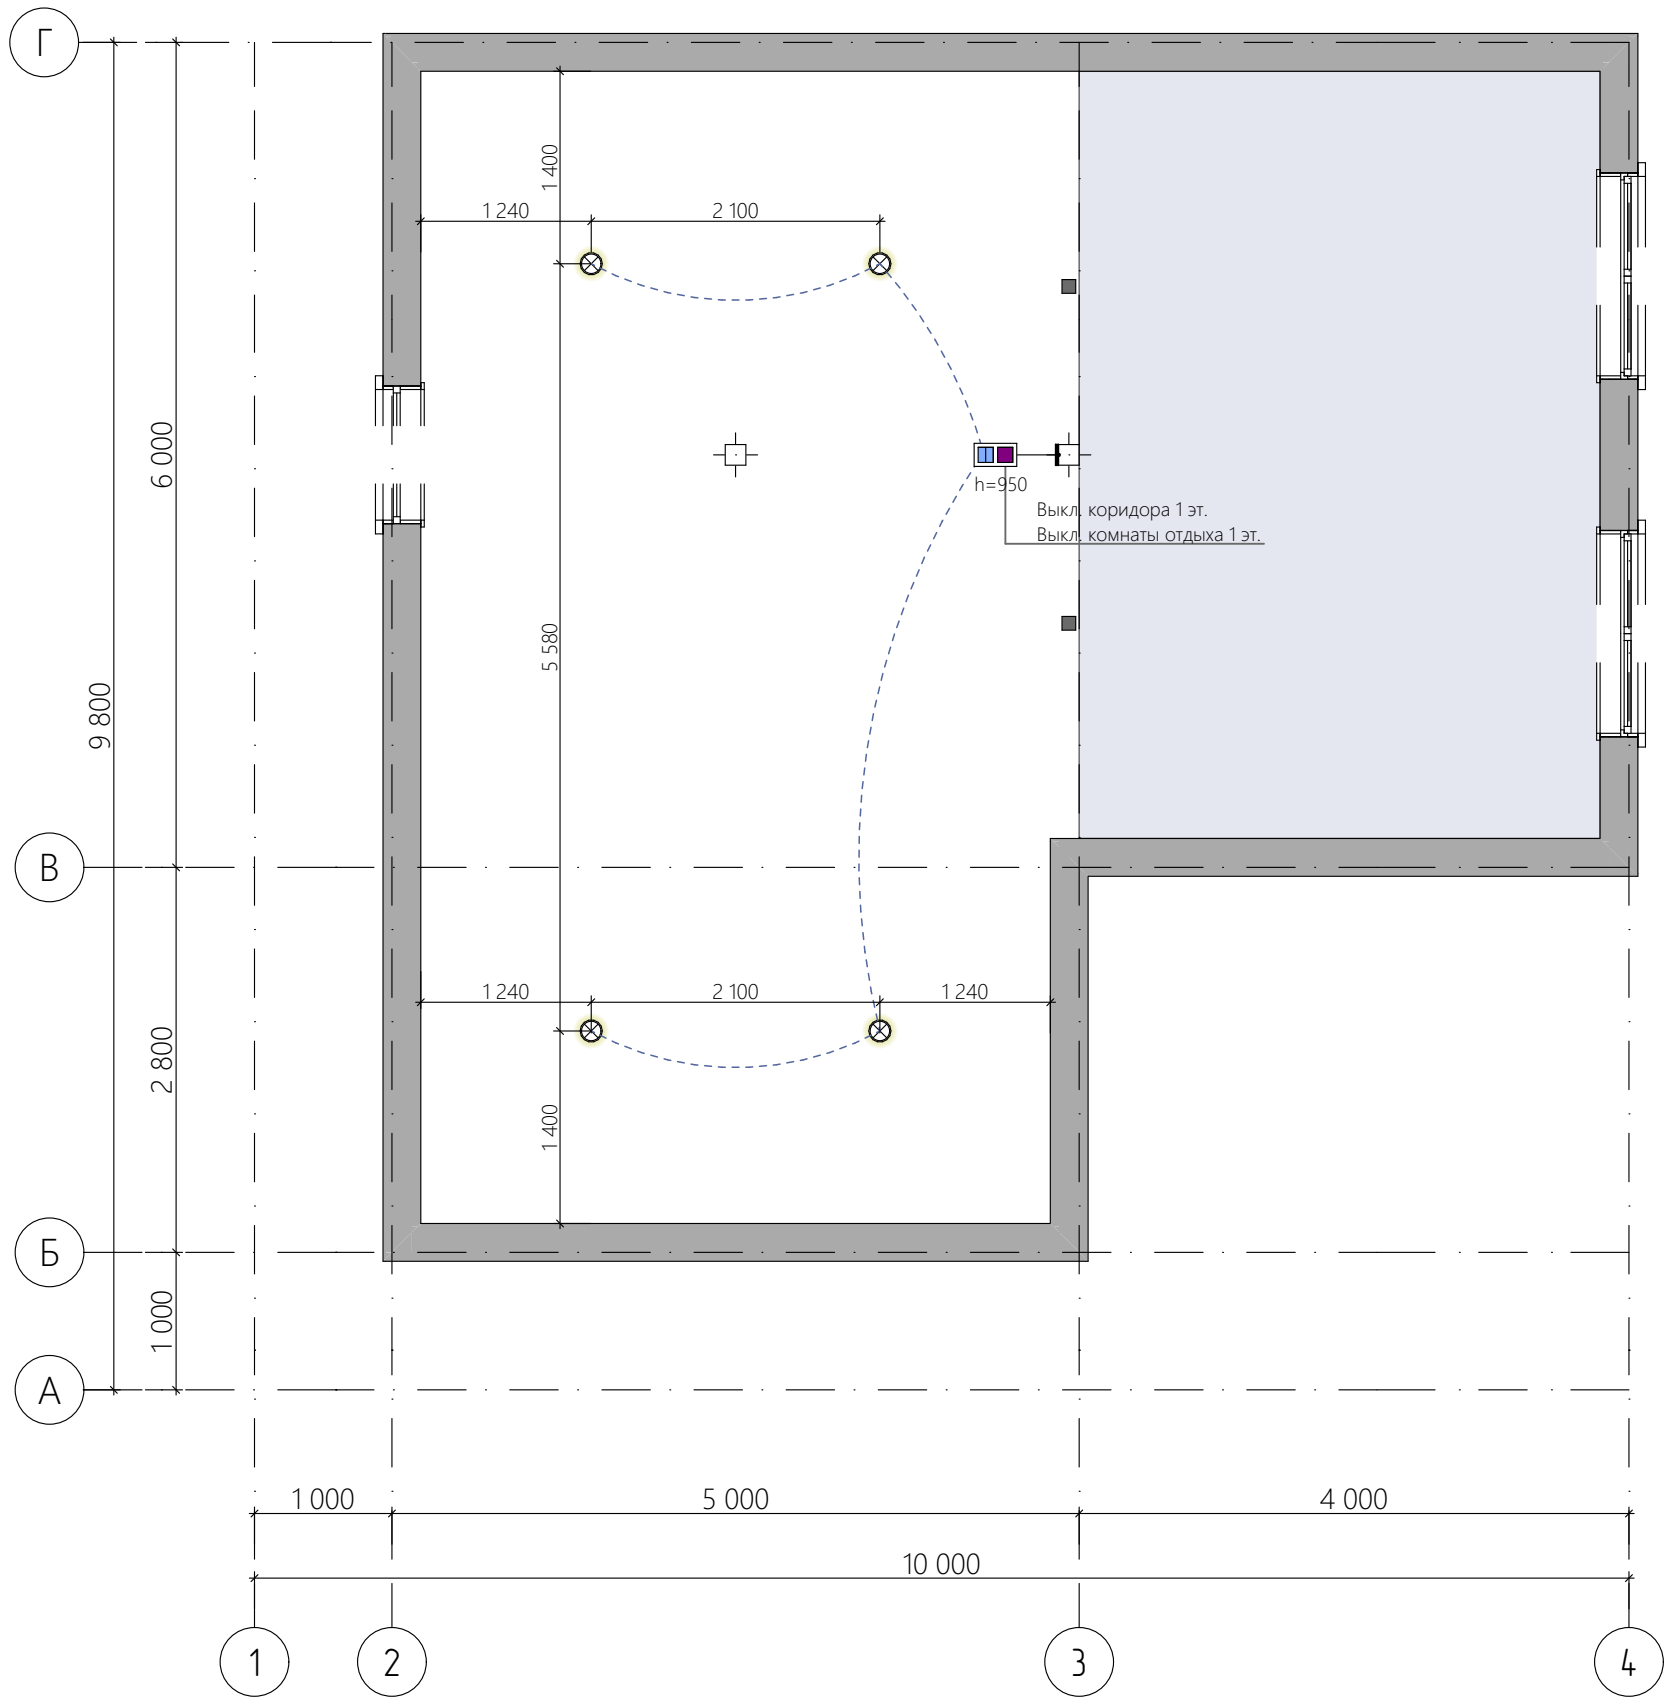

Экспликация светильников и выключателей

Наименование	2д-вид	Кол-во
Выключатель двухклавишный (рамка 1 секции)		1
Выключатель одно- и двухклавишный (рамка 2 секции)		3
Выключатель одноклавишный (рамка 1 секции)		7
Светильник точечный		18
Светильник подвесной		3
Уличный светильник		6

38

Примечание:

1. Схема размещения розеток является рекомендательной и требует согласования с заказчиком по месту.
2. Все высоты даны от чистового пола.
3. Все указанные размеры даются до центра позиций.
4. Отметки розеток, выключателей, выводов и др. оборудования, являются предварительными и уточняются после выбора финишных материалов и мебели.
5. Размеры уточняются дополнительно

Согласовано

Взам. инв. №

Подп. и дата

Инв. № подл.

Лист	Изм.	№ Докум.	Подп.	Дата


обл. Московская, р-н Дмитровский, с/пос. Яотское, д. Новое Сельцо, дом 43

План размещения светильников и выключателей 2 этажа

Лист

17

Согласовано				
И-нв. № подл.	Подп. и дата	Взам. инв. №		

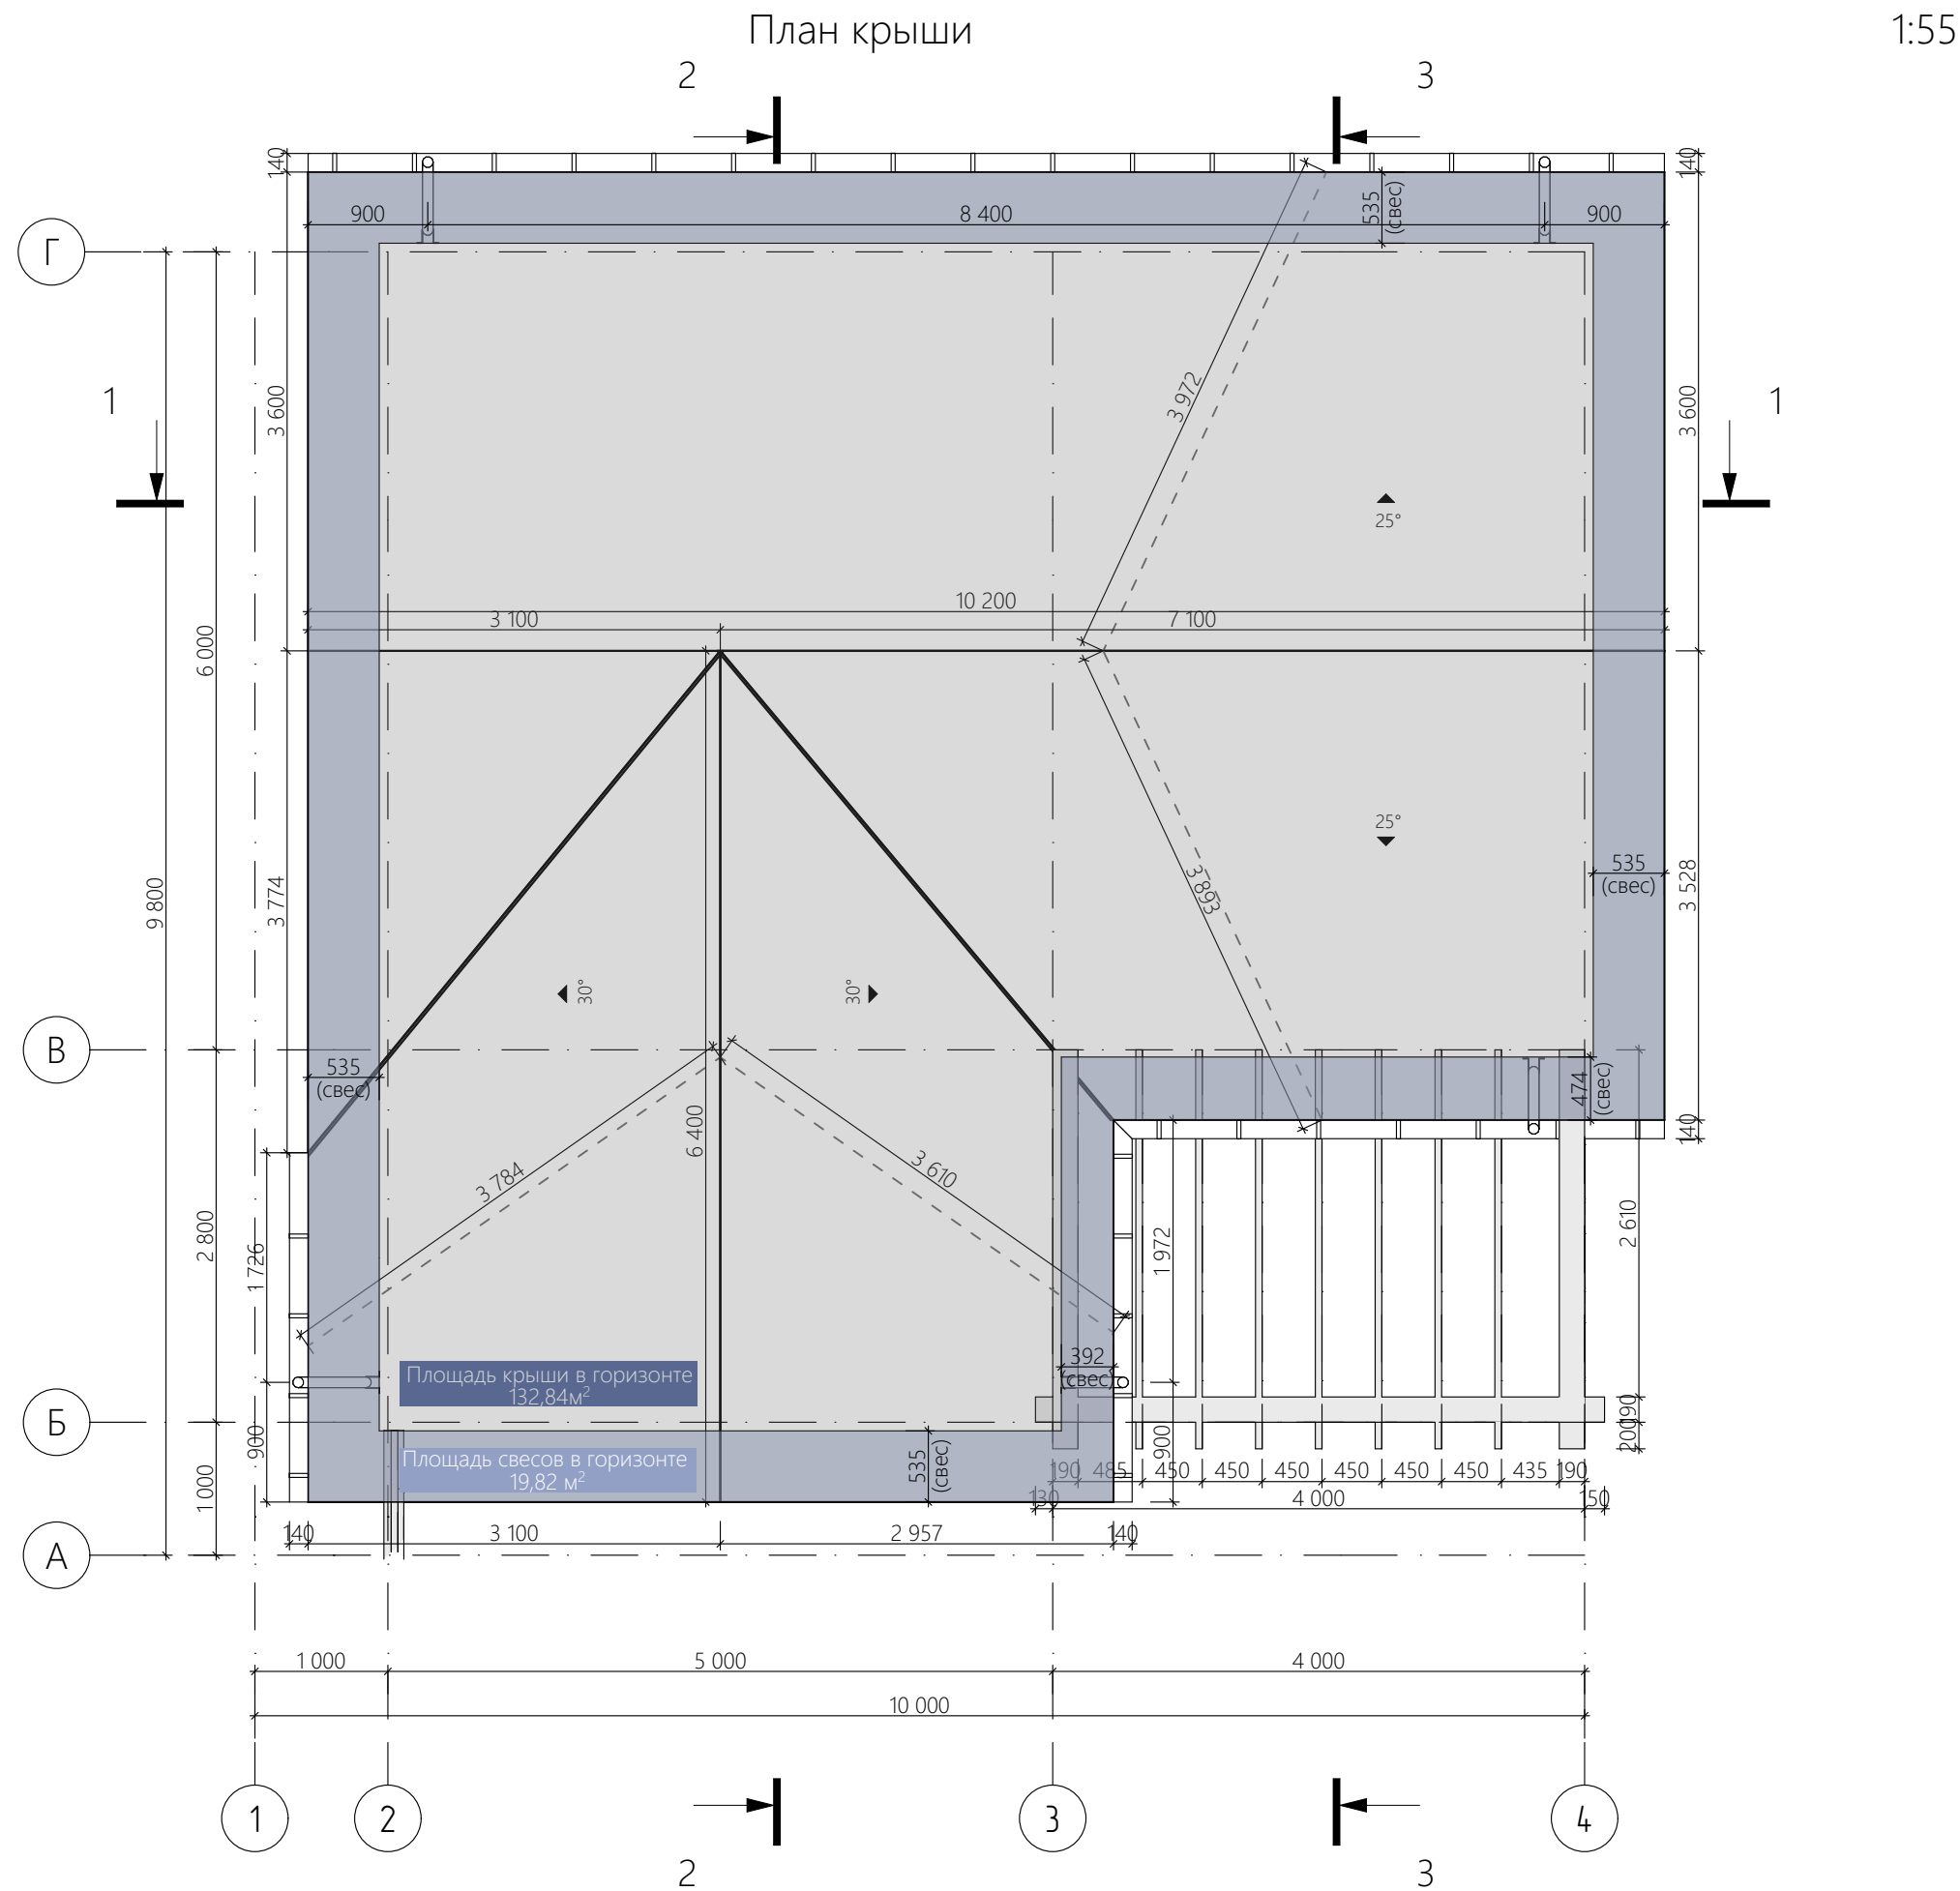


Условные обозначения:

- Крыша (уклон 25/30°)
- Подшив свесов

Площадь крыши бани (S, м²) = 100,70м²

Аксонометрия крыши

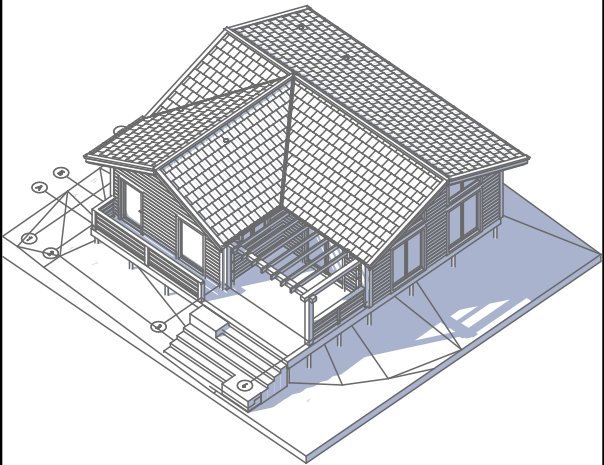

Лист	Изм.	№ Докум.	Подп.	Дата

обл. Московская, р-н Дмитровский, с/пос. Якотское, д. Новое Сельцо, дом 43



План крыши

1:1

Инв. № подл.	Подп. и дата	Взам. инв. №

1. Изготовление окон и дверей определяется заказчиком, допускается изменение открывания окон и дверей;
2. При заказе оконных и дверных блоков необходим обмер по месту от изготовителя;
3. Оконные и дверные изделия изображены со стороны открывания.

Лист	Изм.	№ Докум.	Подп.	Дата	Ведомость оконных проемов		Лист
							19

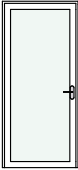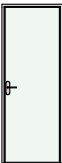Ведомость дверных проемов										1:1			
Наименование		Размеры проема Ш x В, мм			Вид		Кол-во		Площадь, м2				
Д1		1 000×2 200					2		2,20				
Д2		800×2 100					3		1,68				
Д3		900×2 100					1		1,89				
Д4		1 110×2 100					1		2,33				
Д5		800×2 100					1		1,68				
Д6		700×2 100					1		1,47				
									16,81 м²				
Примечание:													
1. Изготовление окон и дверей определяется заказчиком, допускается изменение открывания окон и дверей;													
2. При заказе оконных и дверных блоков необходим обмер по месту от изготовителя;													
3. Оконные и дверные изделия изображены со стороны открывания.													
Лист		Изм.		№ Докум.		Подп.		Дата		Ведомость дверных проемов		Лист	
												20	

Согласовано


Ив. № подл.

Подп. и дата

Взам. инв. №

Разрез 1-1

1:40

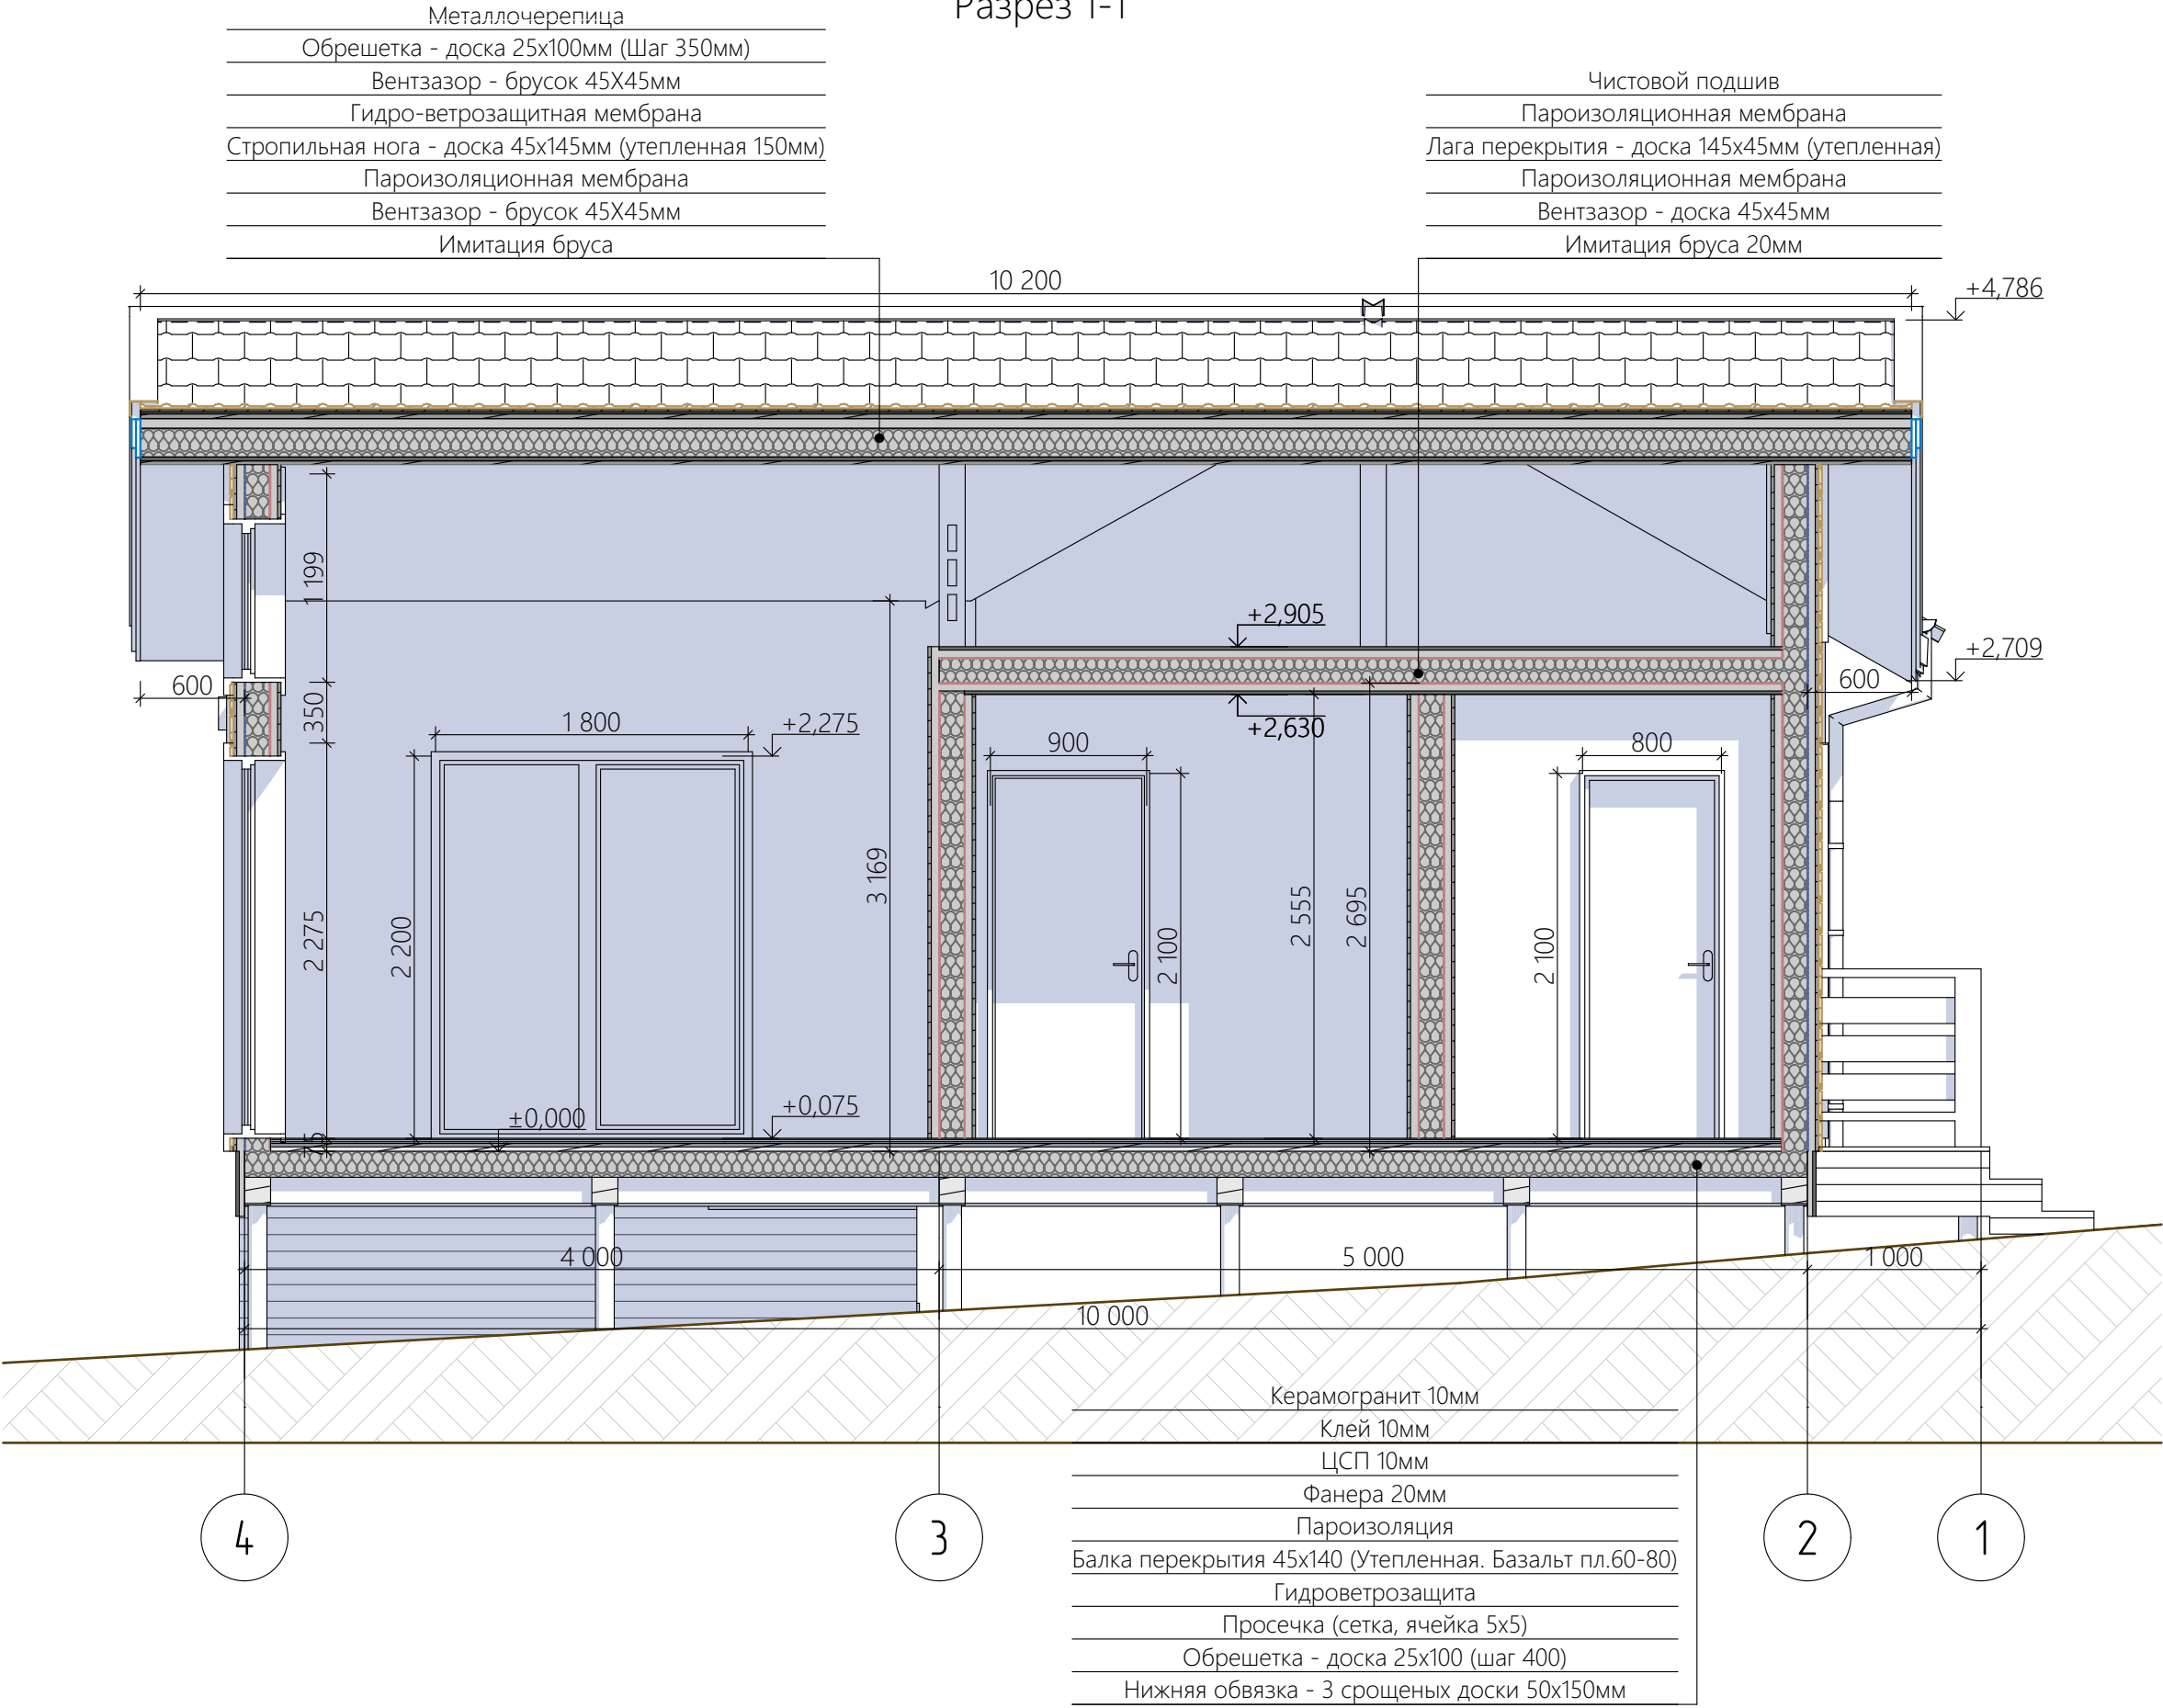

Согласовано				
Взам. инв. №				
Подп. и дата				
Инв. № подл.				

Лист	Изм.	№ Докум.	Подп.	Дата


обл. Московская, р-н Дмитровский, с/пос. Яотское, д. Новое Сельцо, дом 43

Разрез 1-1

Лист
21

Разрез 2-2

1:40

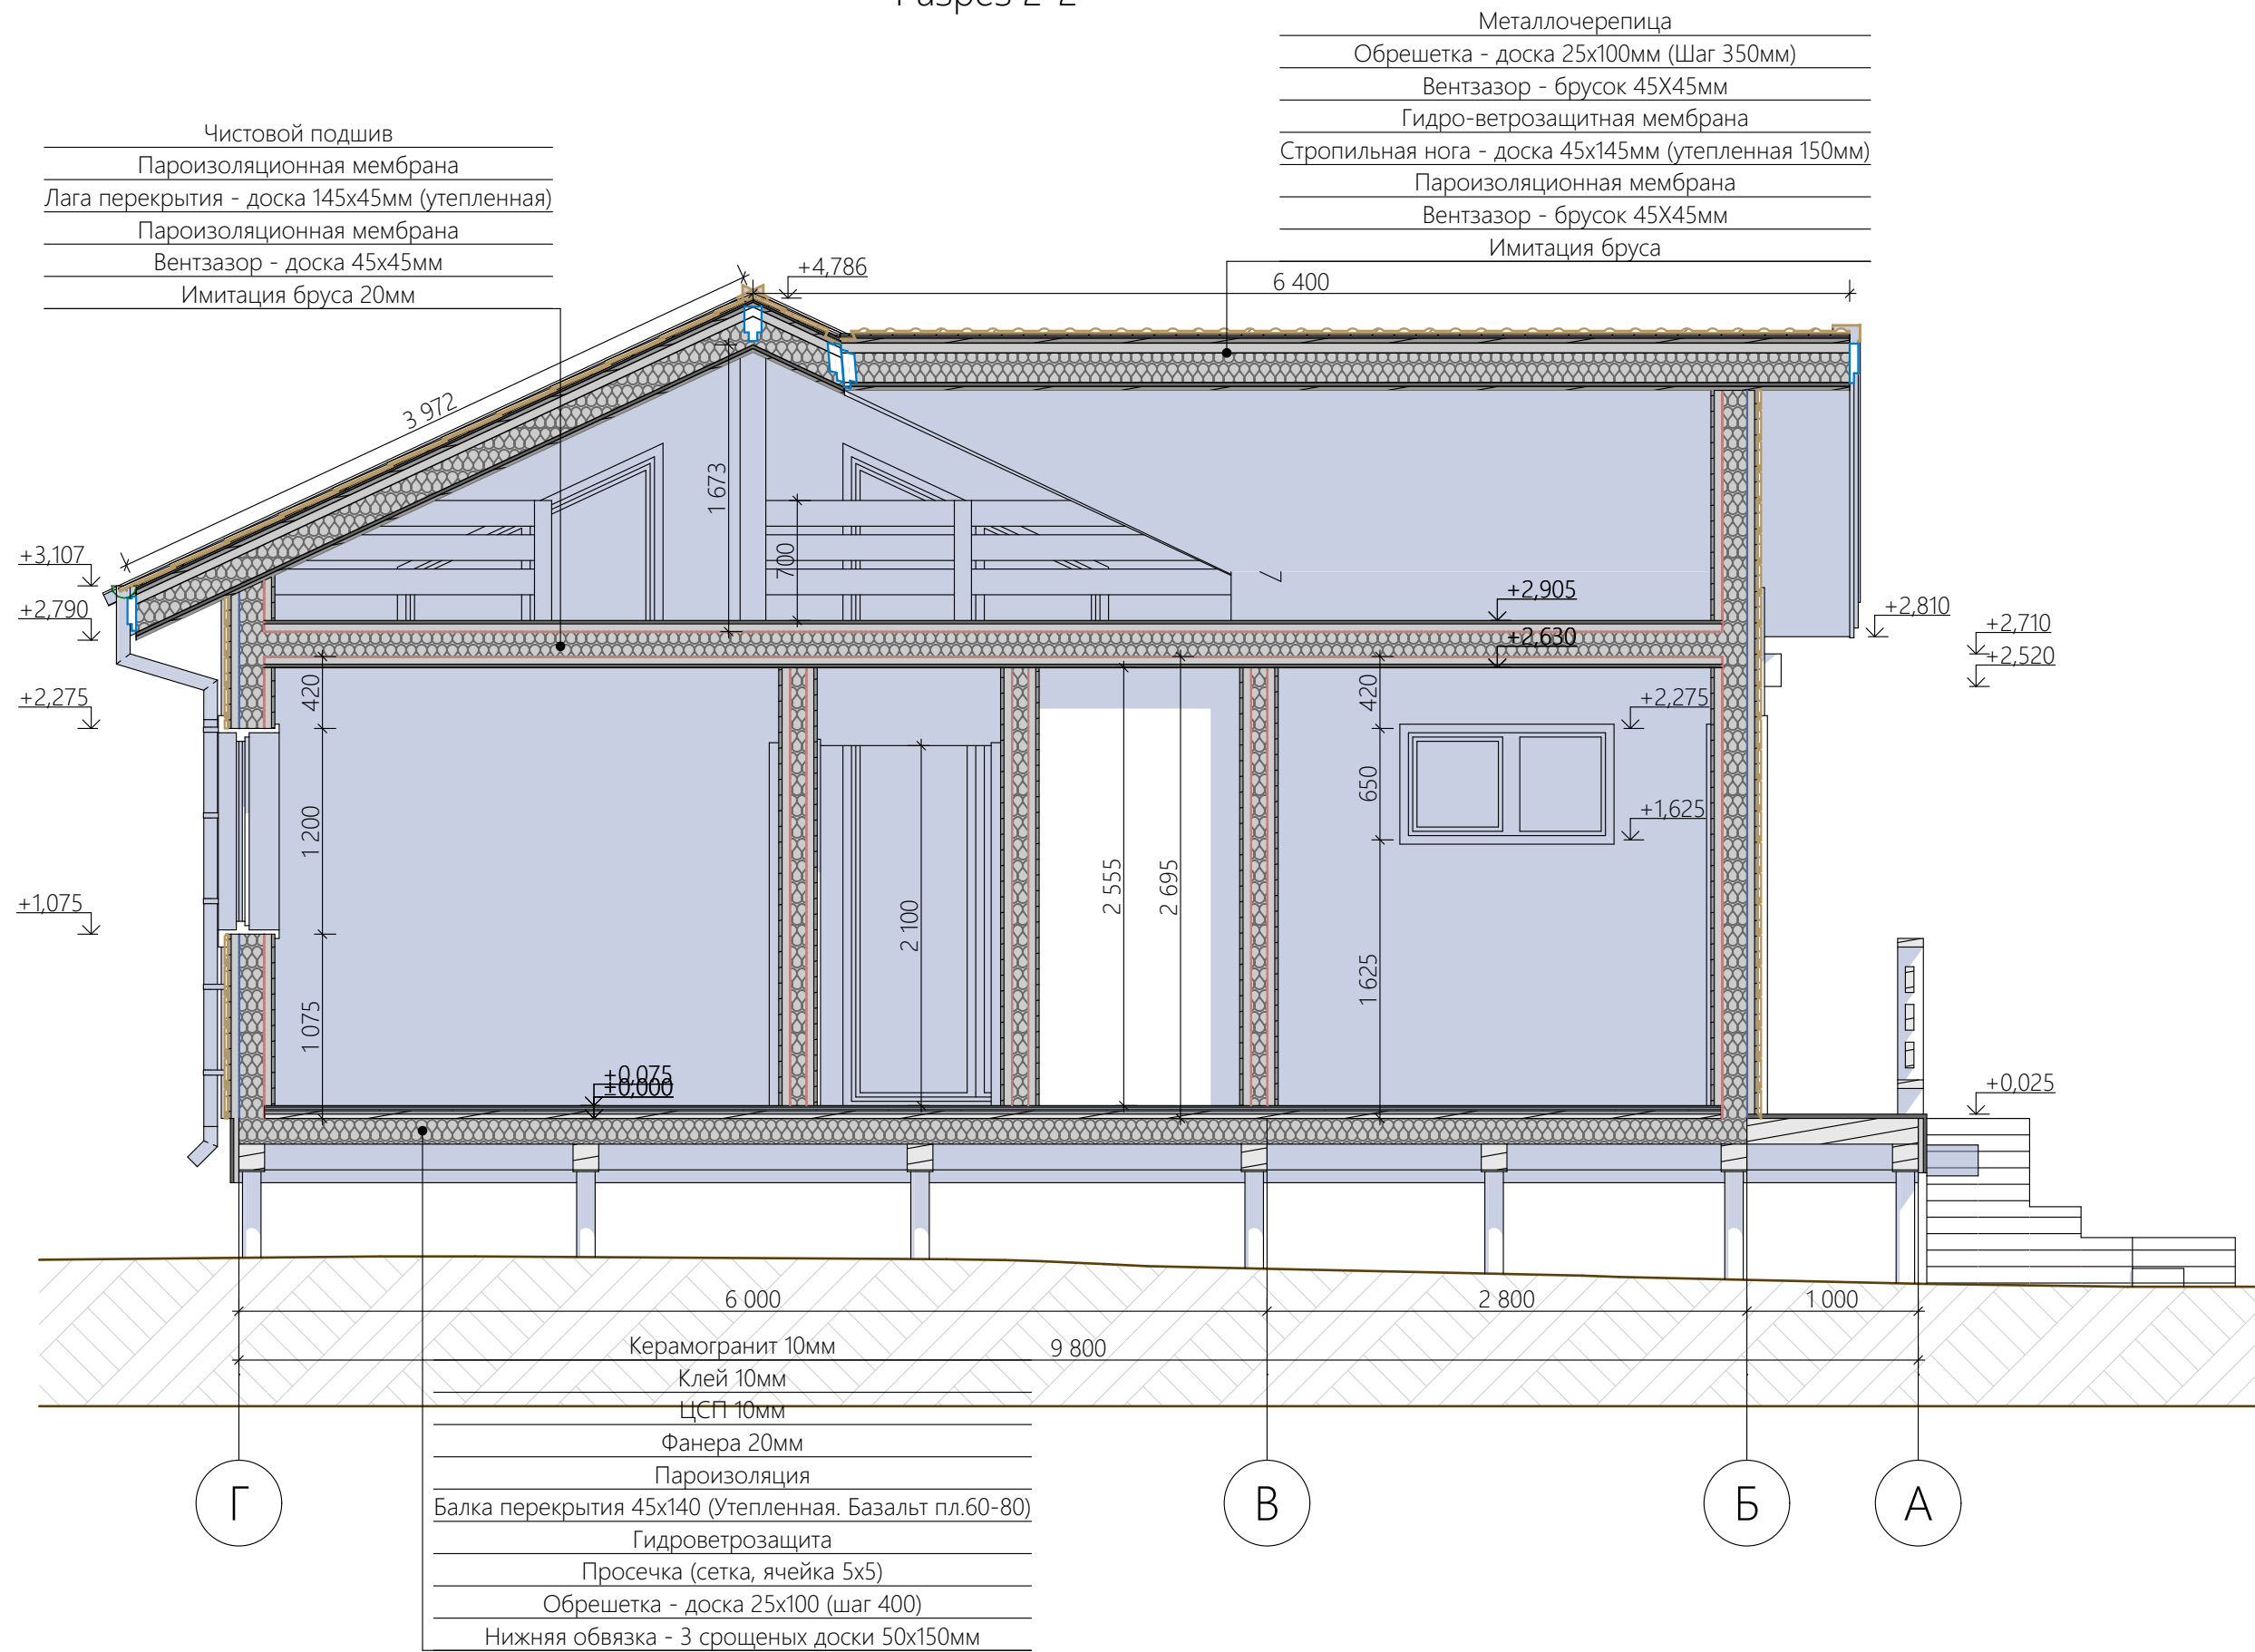

Согласовано				
Взам. инв. №				
Подп. и дата				
Инв. № подл.				


Лист	Изм.	№ Докум.	Подп.	Дата

обл. Московская, р-н Дмитровский, с/пос. Яотское, д. Новое Сельцо, дом 43

Разрез 2-2

Лист
22

Разрез 3-3

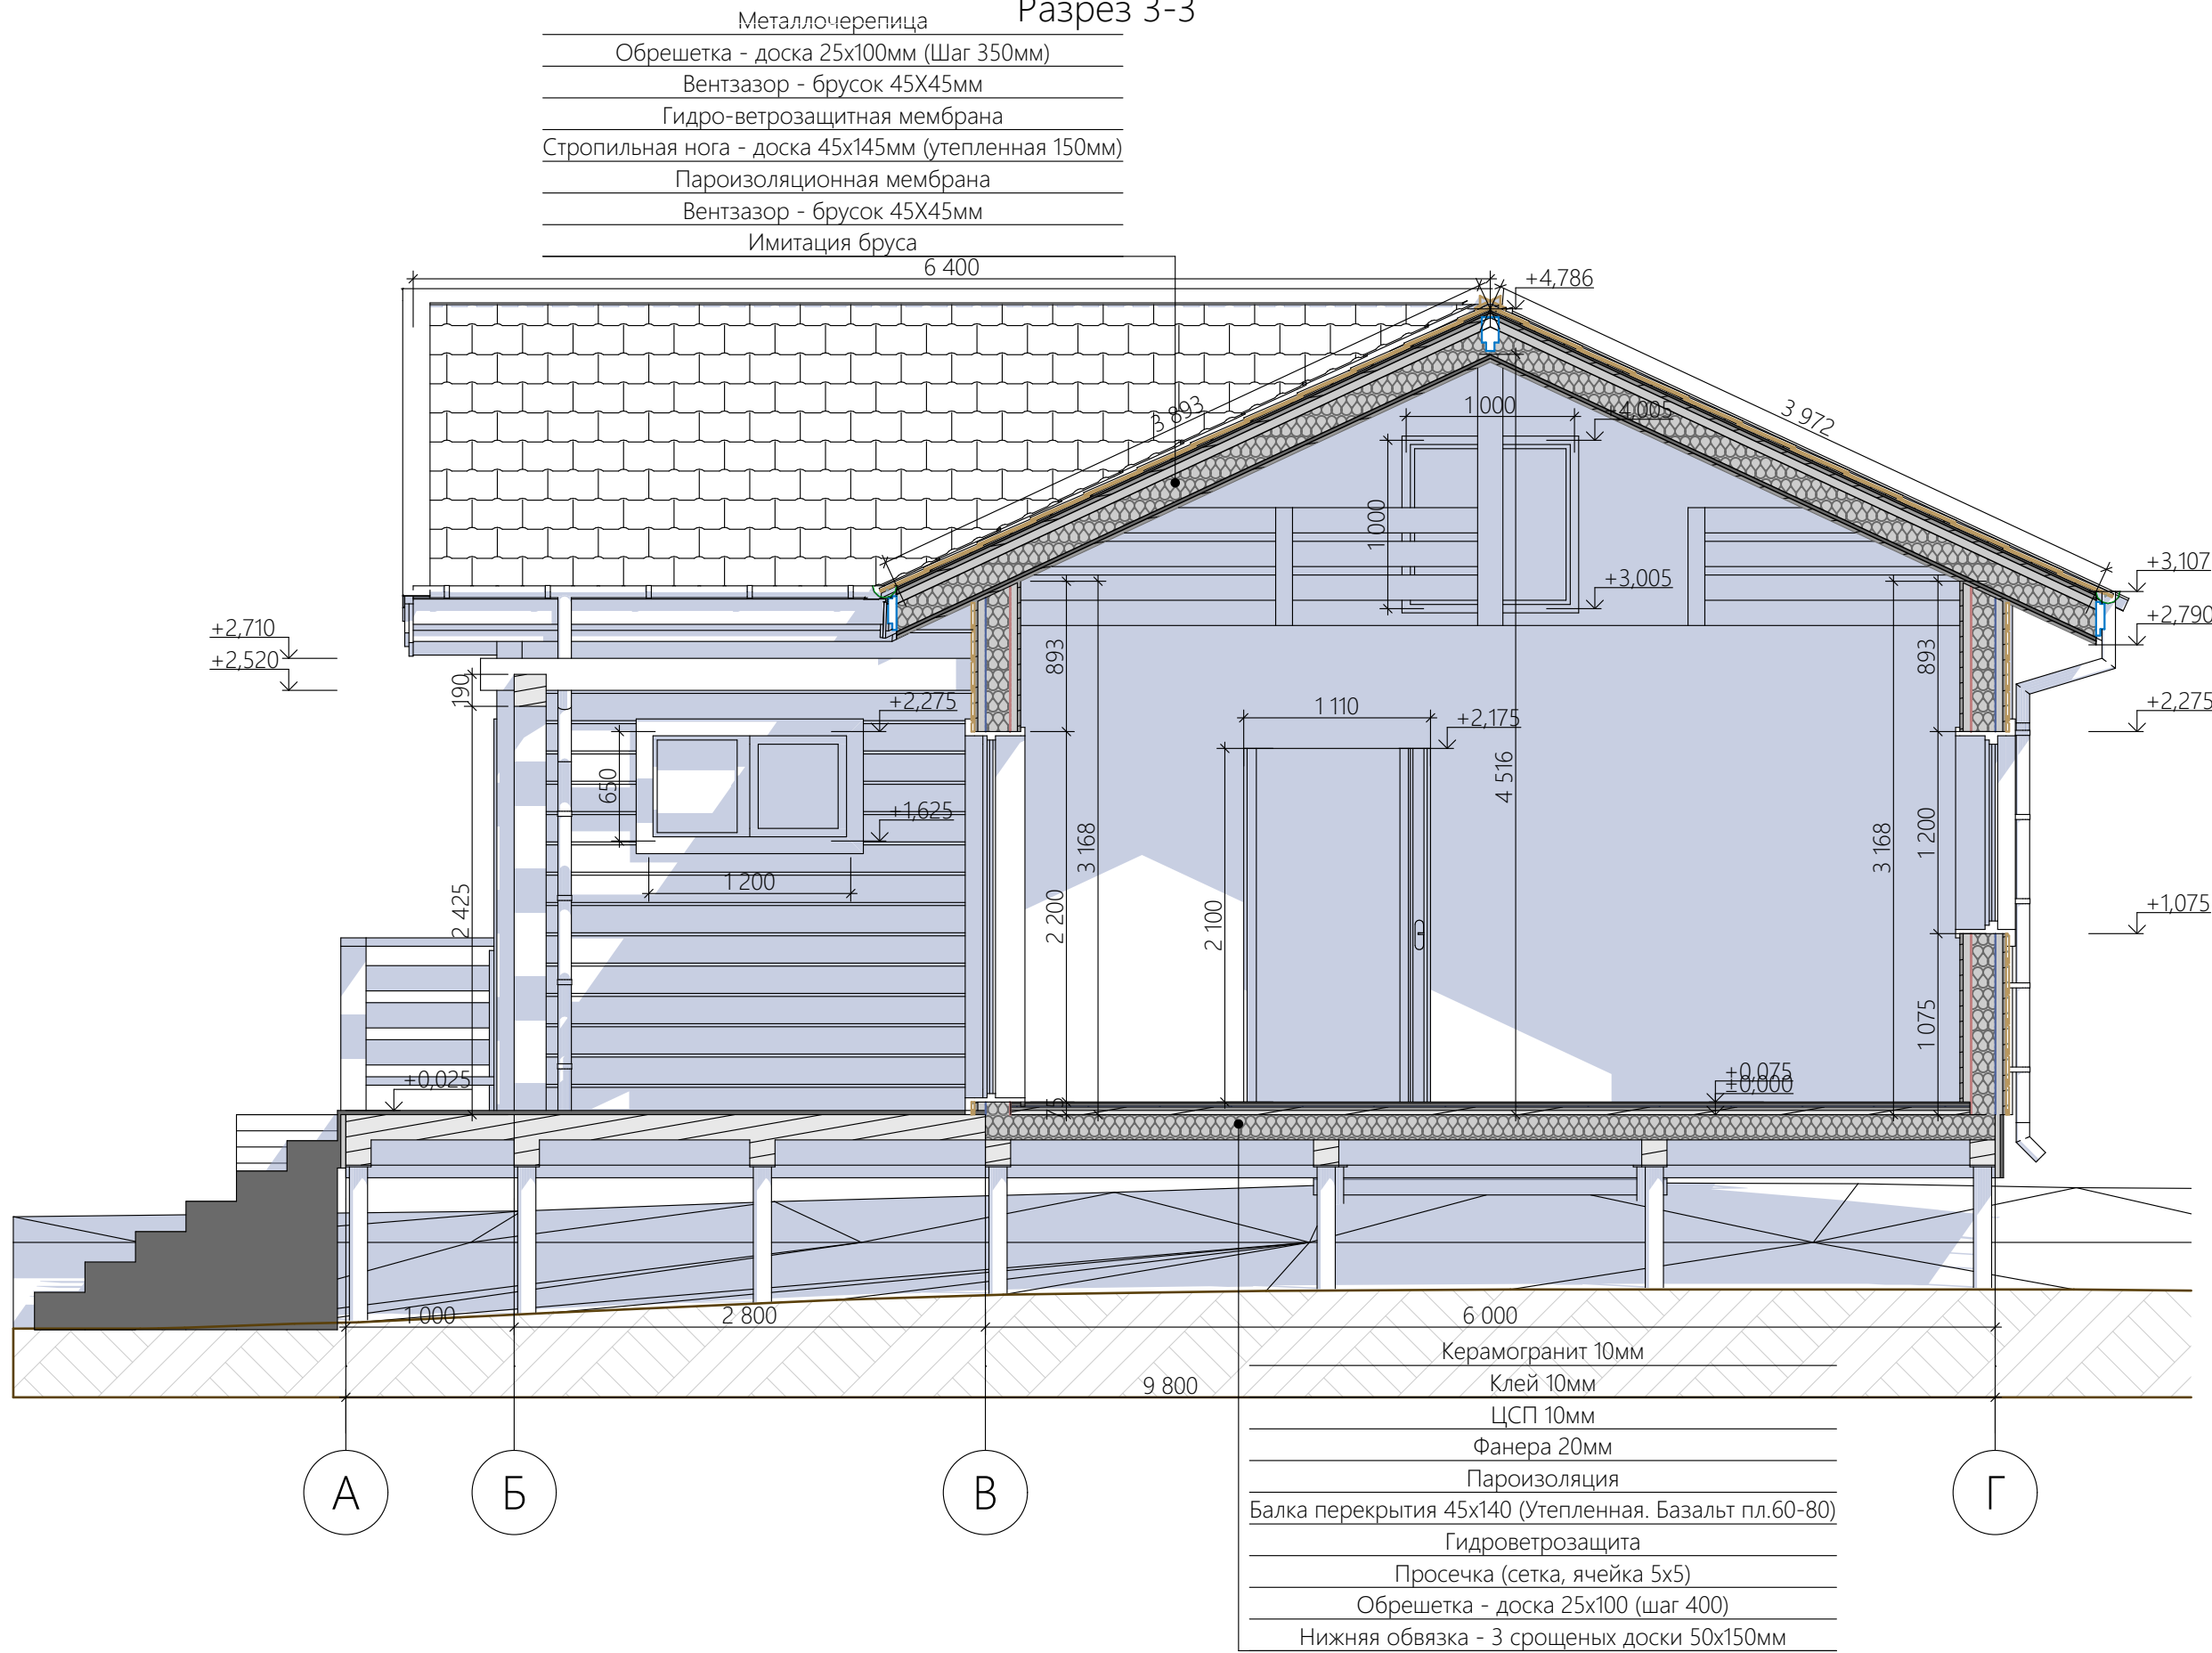

Согласовано				
Взам. инв. №				
Подп. и дата				
Инв. № подл.				


Лист	Изм.	№ Докум.	Подп.	Дата

Фасад 1-4

1:50

Условные обозначения:

- Фиброцементный сайдинг (светло-серый)
- ДПК (темно-серый)
- Водосточная система, лобовая рамы (RAL 9010)
- Наличники, рамы, угловые элементы (RAL 9010)
- Металлочерепица (RAL 7024)

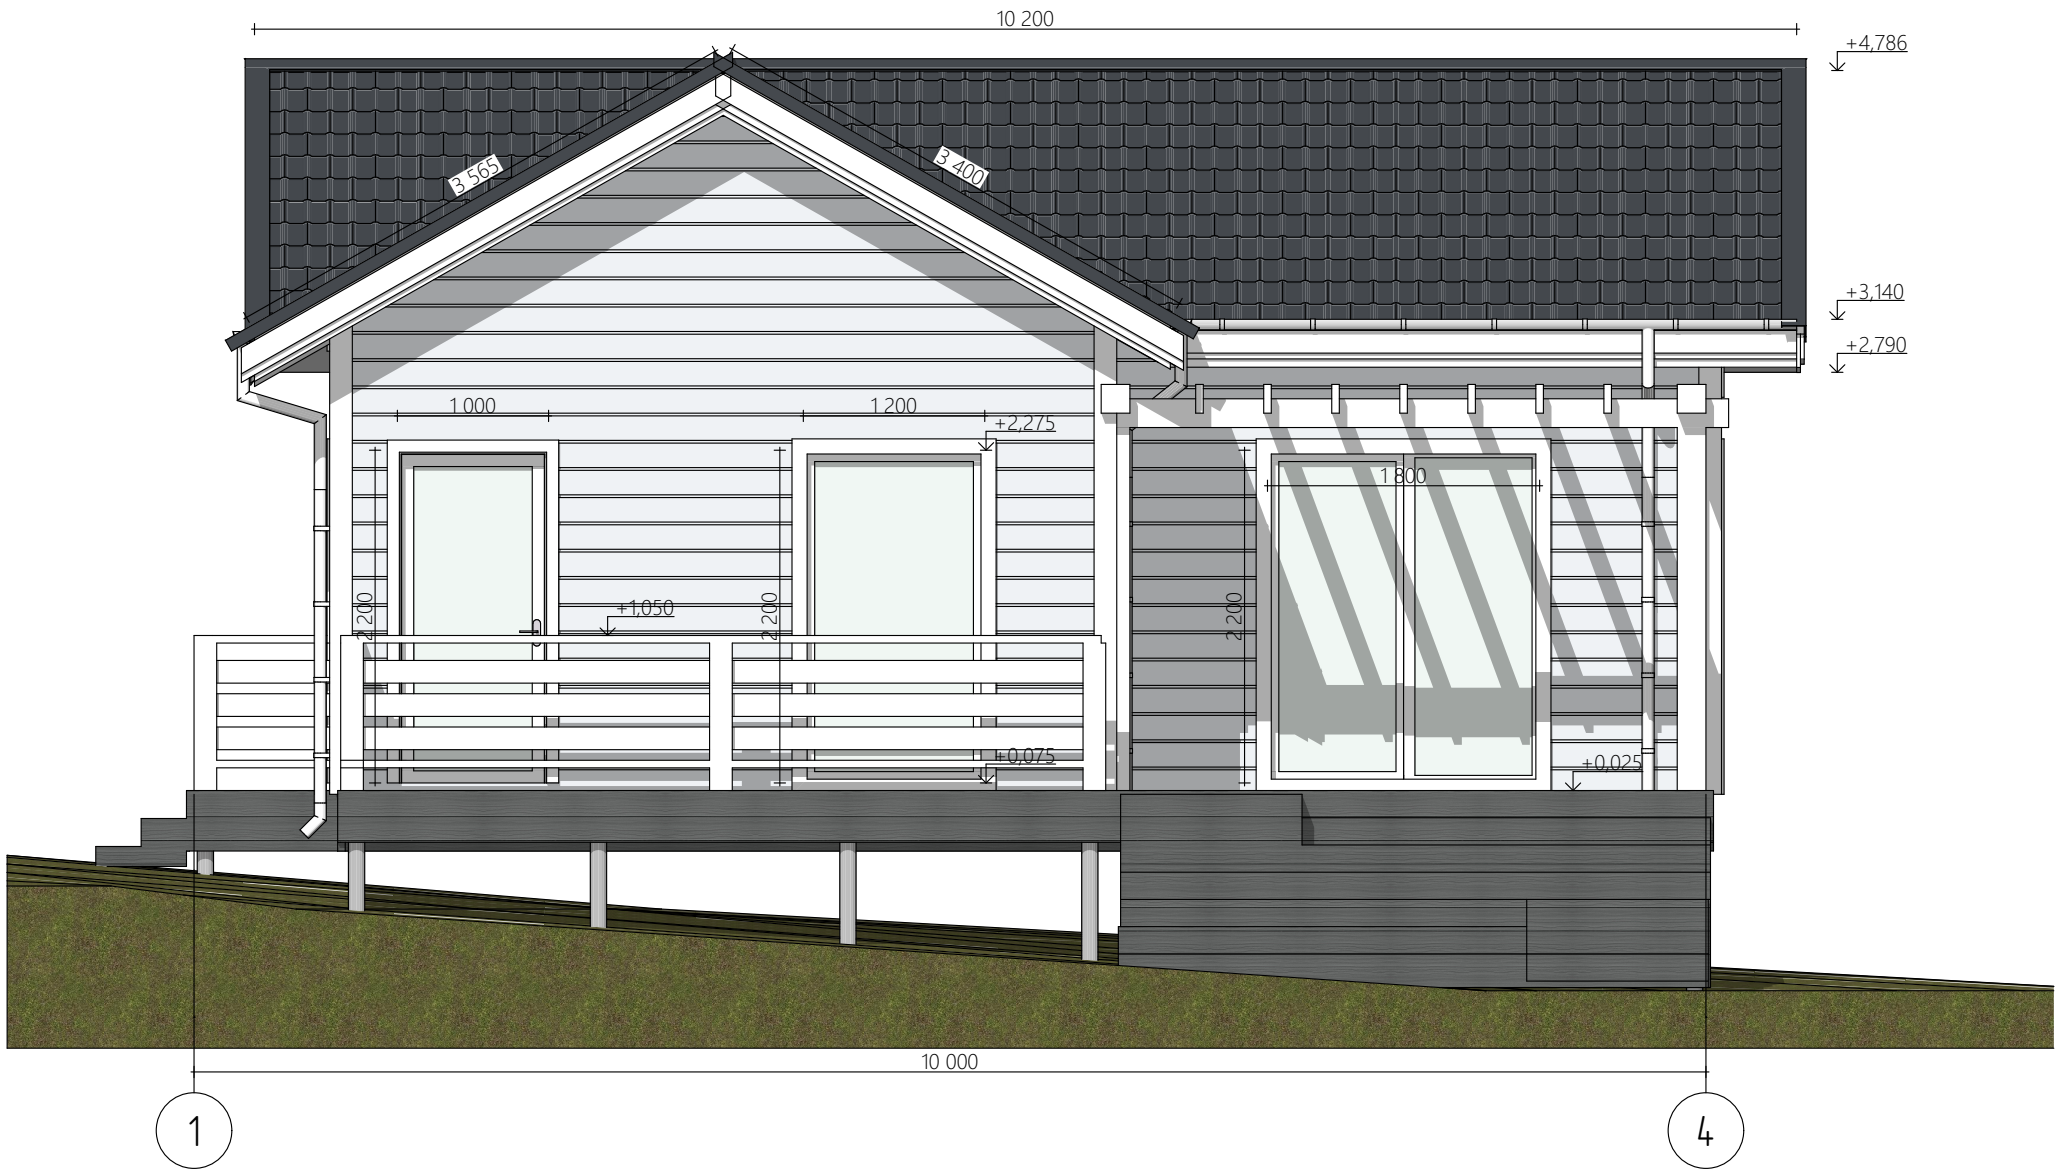

Согласовано

Взам. инв. №

Подп. и дата

Инв. № подл.

Лист	Изм.	№ Докум.	Подп.	Дата

обл. Московская, р-н Дмитровский, с/пос. Якотское, д. Новое Сельцо, дом 43

Фасад 1-4

Лист


24

Фасад А-Г

1:50

Условные обозначения:

- Фиброцементный сайдинг (светло-серый)
- ДПК (темно-серый)
- Водосточная система, лобовая рамы (RAL 9010)
- Наличники, рамы, угловые элементы (RAL 9010)
- Металлочерепица (RAL 7024)

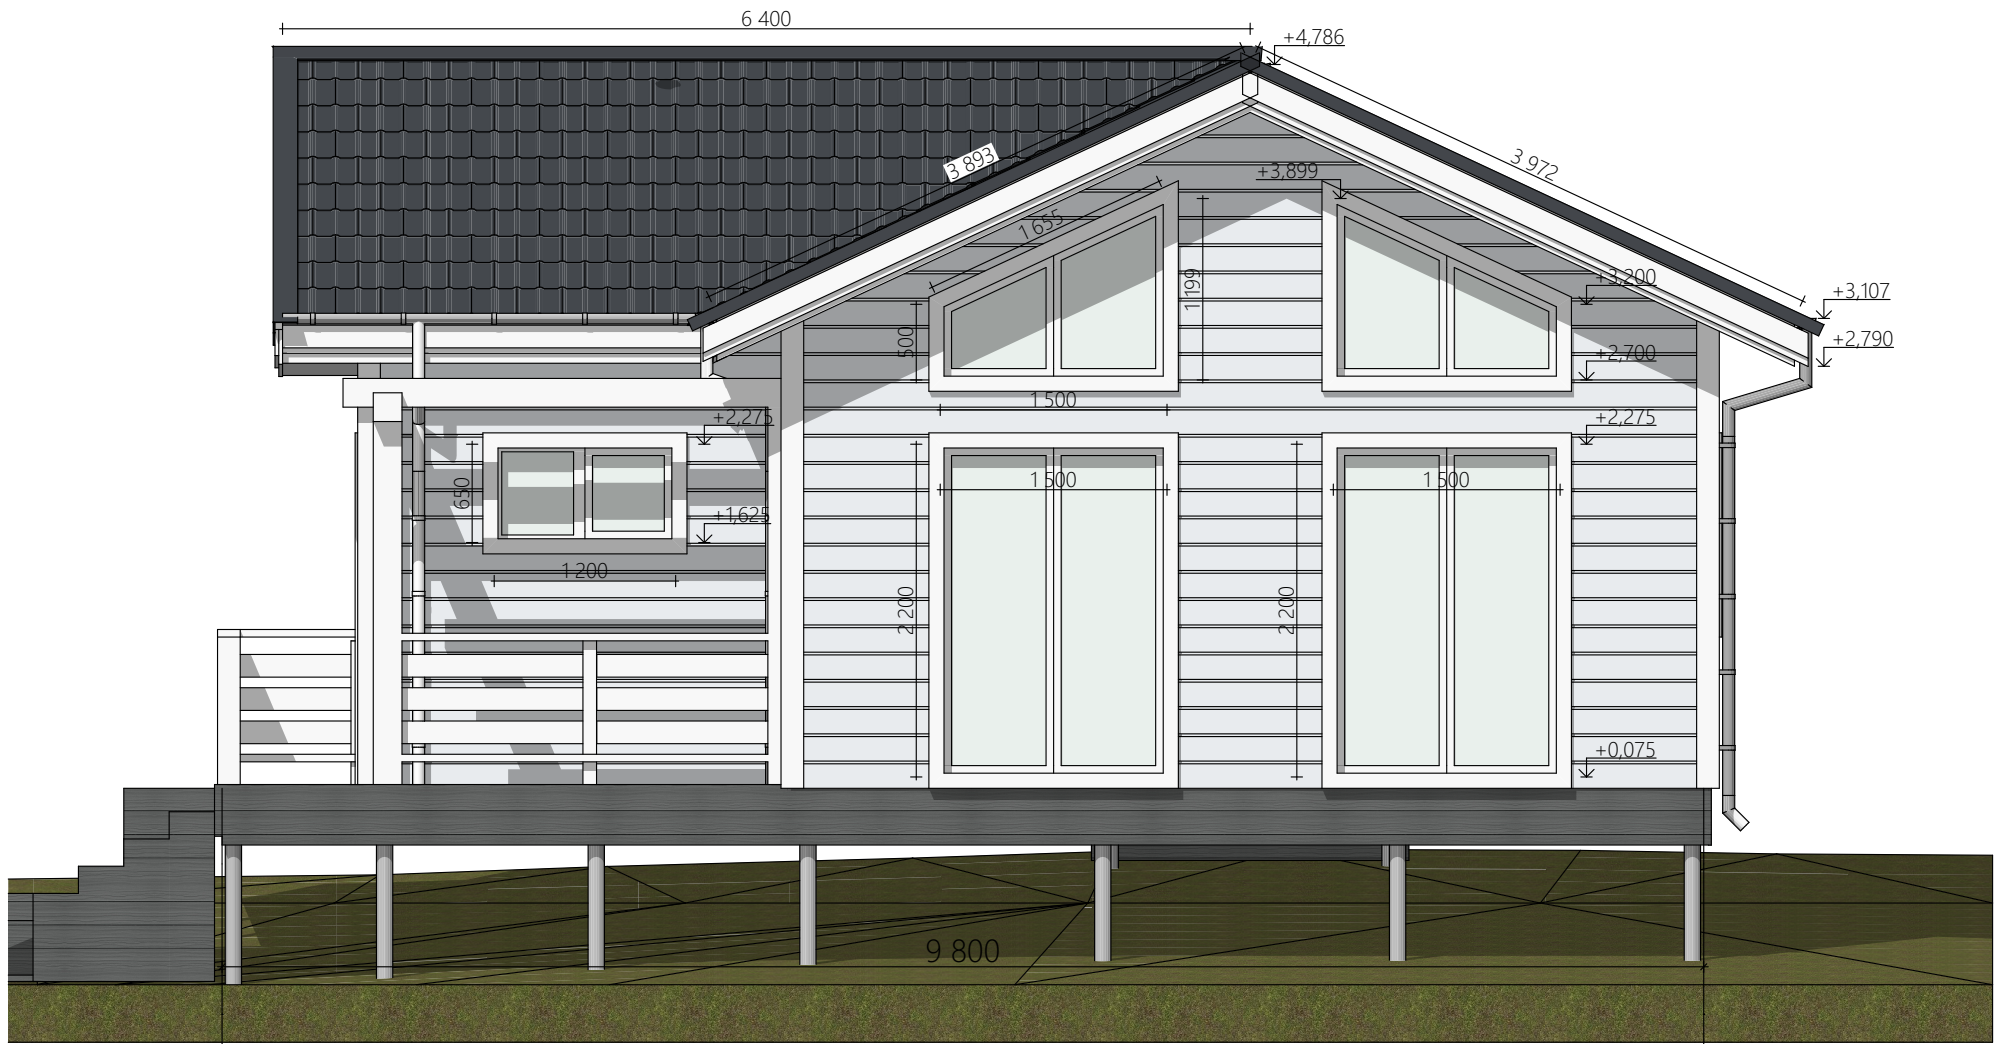

Согласовано

Взам. инв. №

Подп. и дата

Инв. № подл.

Лист	Изм.	№ Докум.	Подп.	Дата

обл. Московская, р-н Дмитровский, с/пос. Якотское, д. Новое Сельцо, дом 43

Фасад А-Г

Лист


25

Согласовано

Взам. инв. №

Подп. и дата

Инв. № подл.

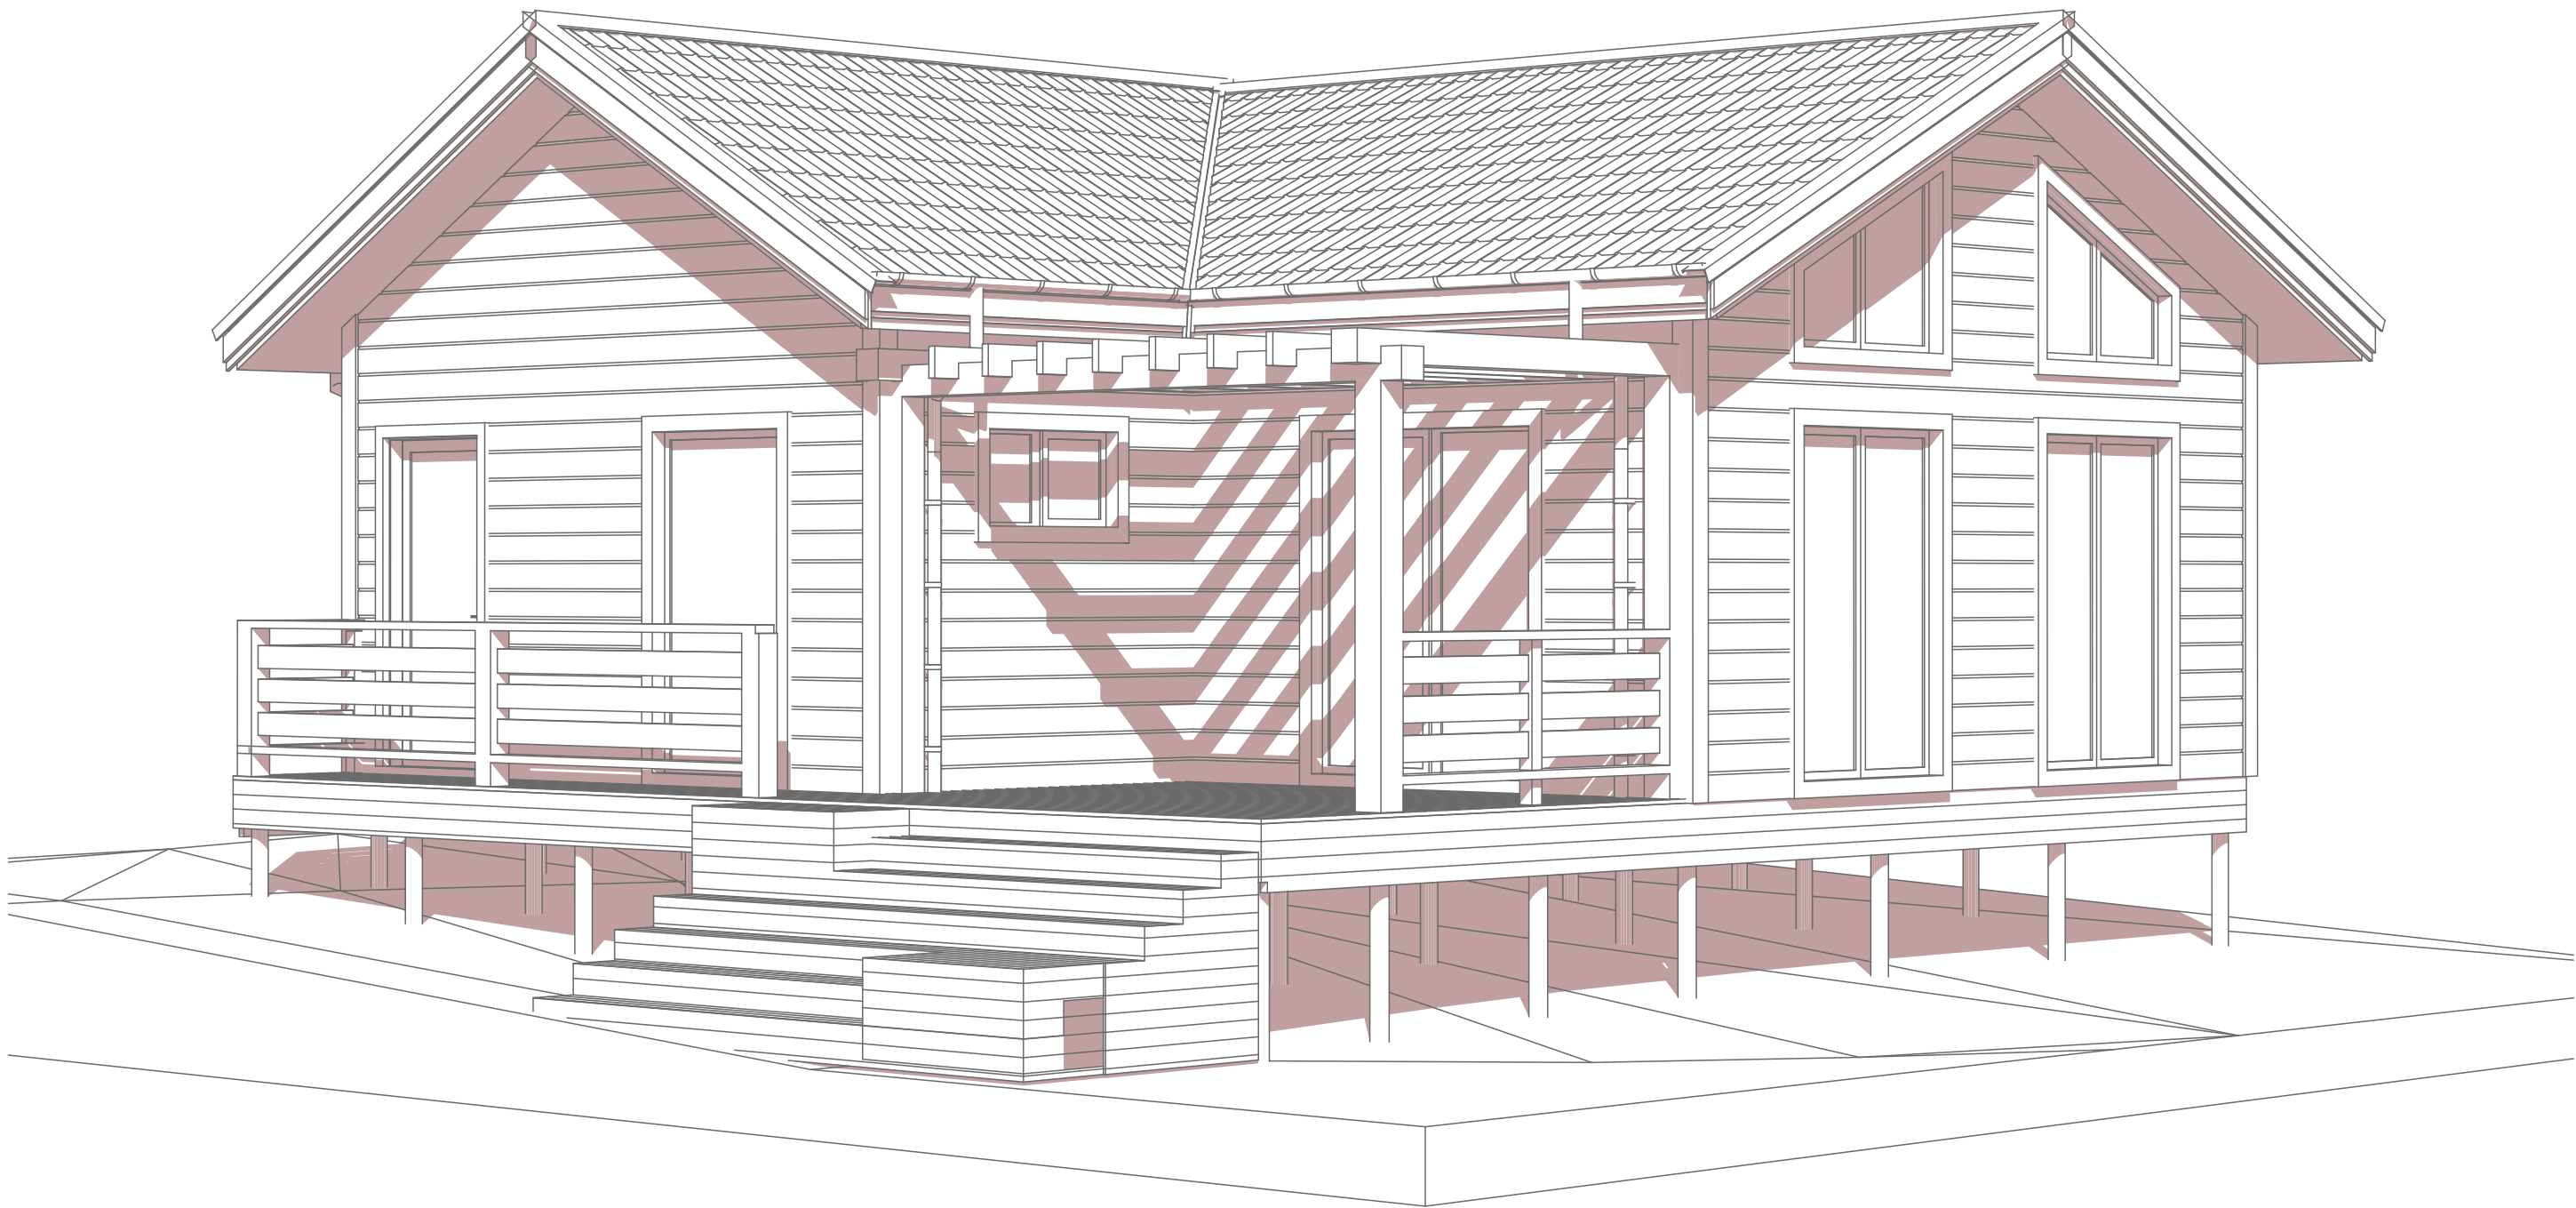

Лист	Изм.	№ Докум.	Подп.	Дата

обл. Московская, р-н Дмитровский, с/пос. Яотское, д. Новое Сельцо, дом 43


Аксометрия №1

Фасад Г-А

1:50

Условные обозначения:

- Фиброцементный сайдинг (светло-серый)
- ДПК (темно-серый)
- Водосточная система, лобовая рамы (RAL 9010)
- Наличники, рамы, угловые элементы (RAL 9010)
- Металлочерепица (RAL 7024)

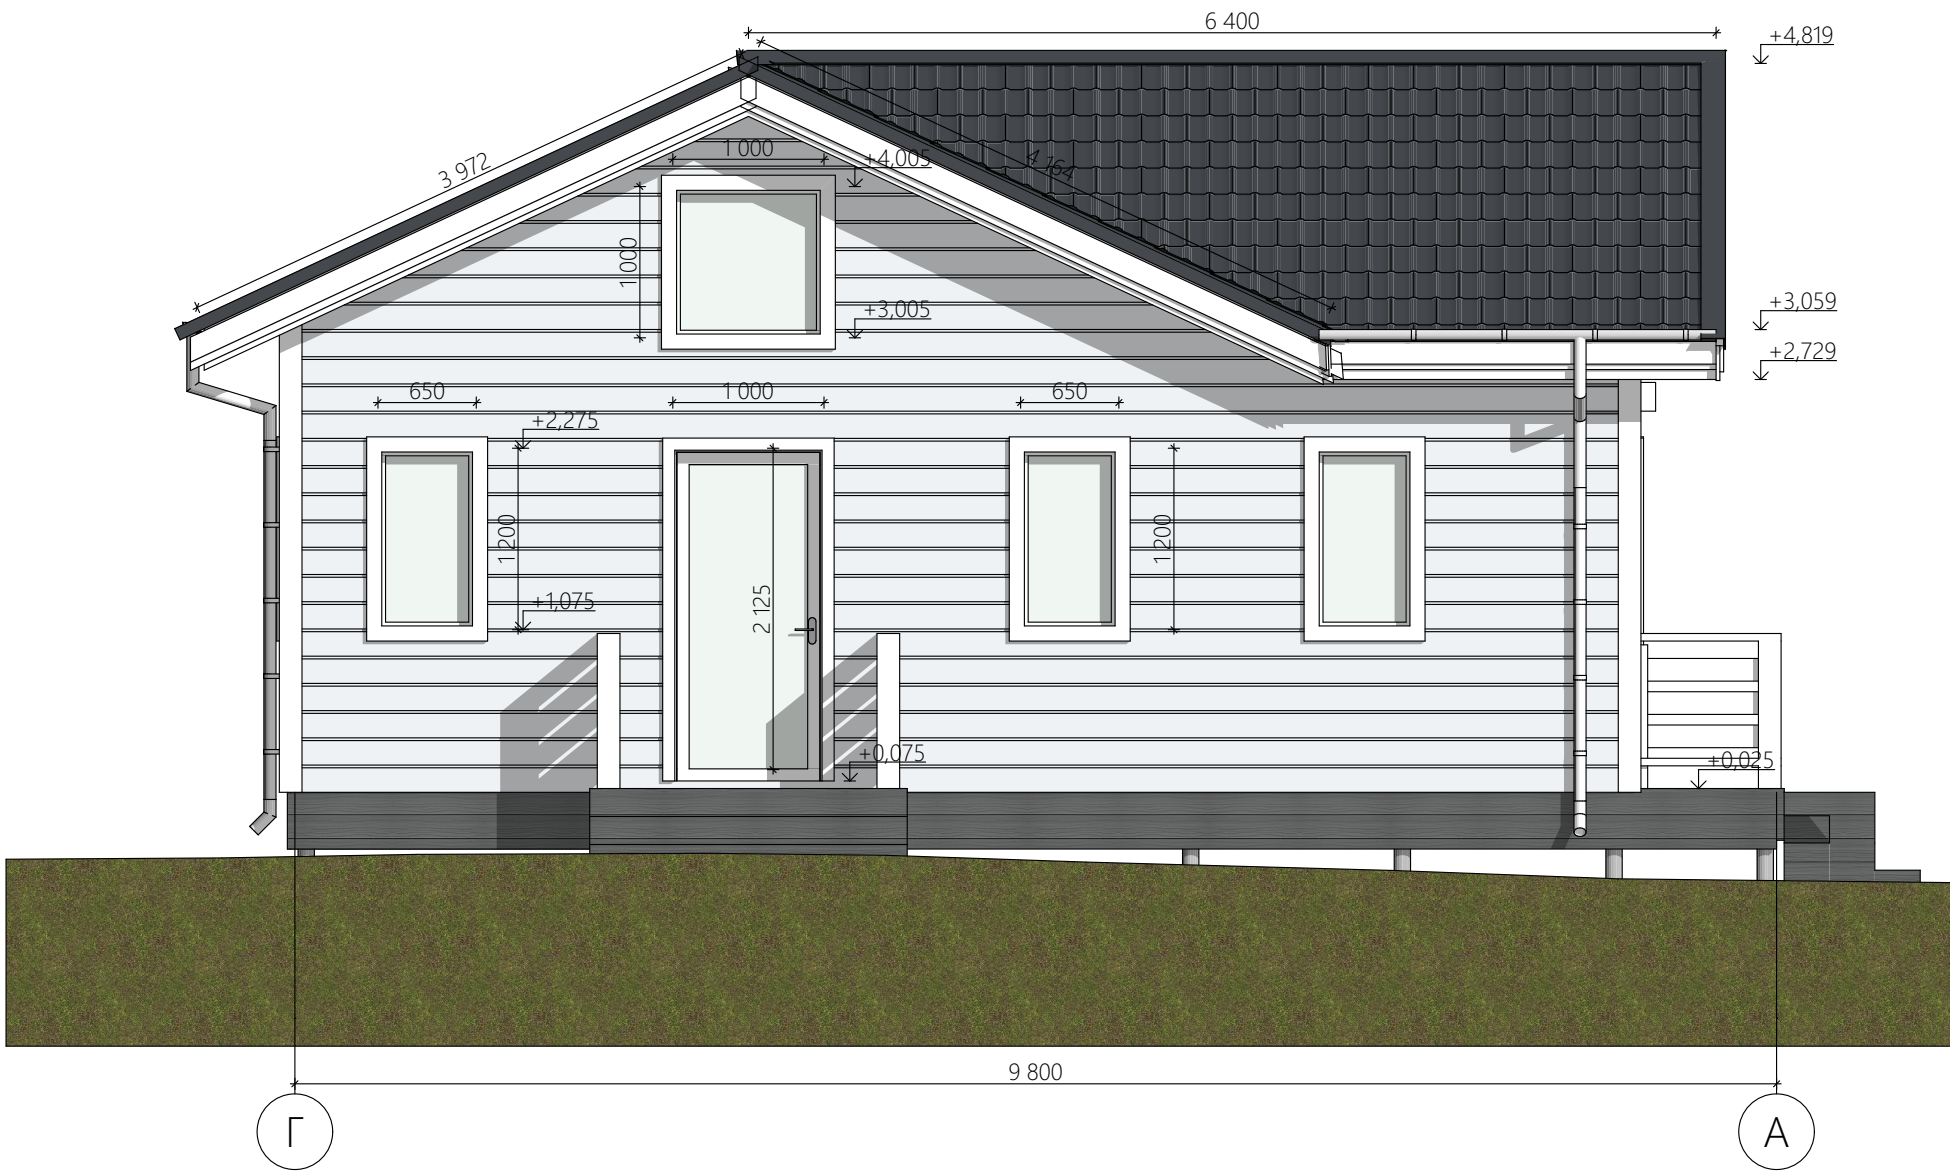

Согласовано				
Инва. № подл.	Подп. и дата	Взам. инв. №		

Лист	Изм.	№ Докум.	Подп.	Дата

обл. Московская, р-н Дмитровский, с/пос. Якотское, д. Новое Сельцо, дом 43

Фасад Г-А

Фасад 4-1

1:50

Условные обозначения:

- Фиброцементный сайдинг (светло-серый)
- ДПК (темно-серый)
- Водосточная система, лобовая рамы (RAL 9010)
- Наличники, рамы, угловые элементы (RAL 9010)
- Металлочерепица (RAL 7024)



Согласовано				
Инов. № подл.	Подп. и дата	Взам. инв. №		

Лист	Изм.	№ Докум.	Подп.	Дата

обл. Московская, р-н Дмитровский, с/пос. Якотское, д. Новое Сельцо, дом 43


Фасад 4-1

Согласовано

Взам. инв. №

Подп. и дата

Инв. № подл.

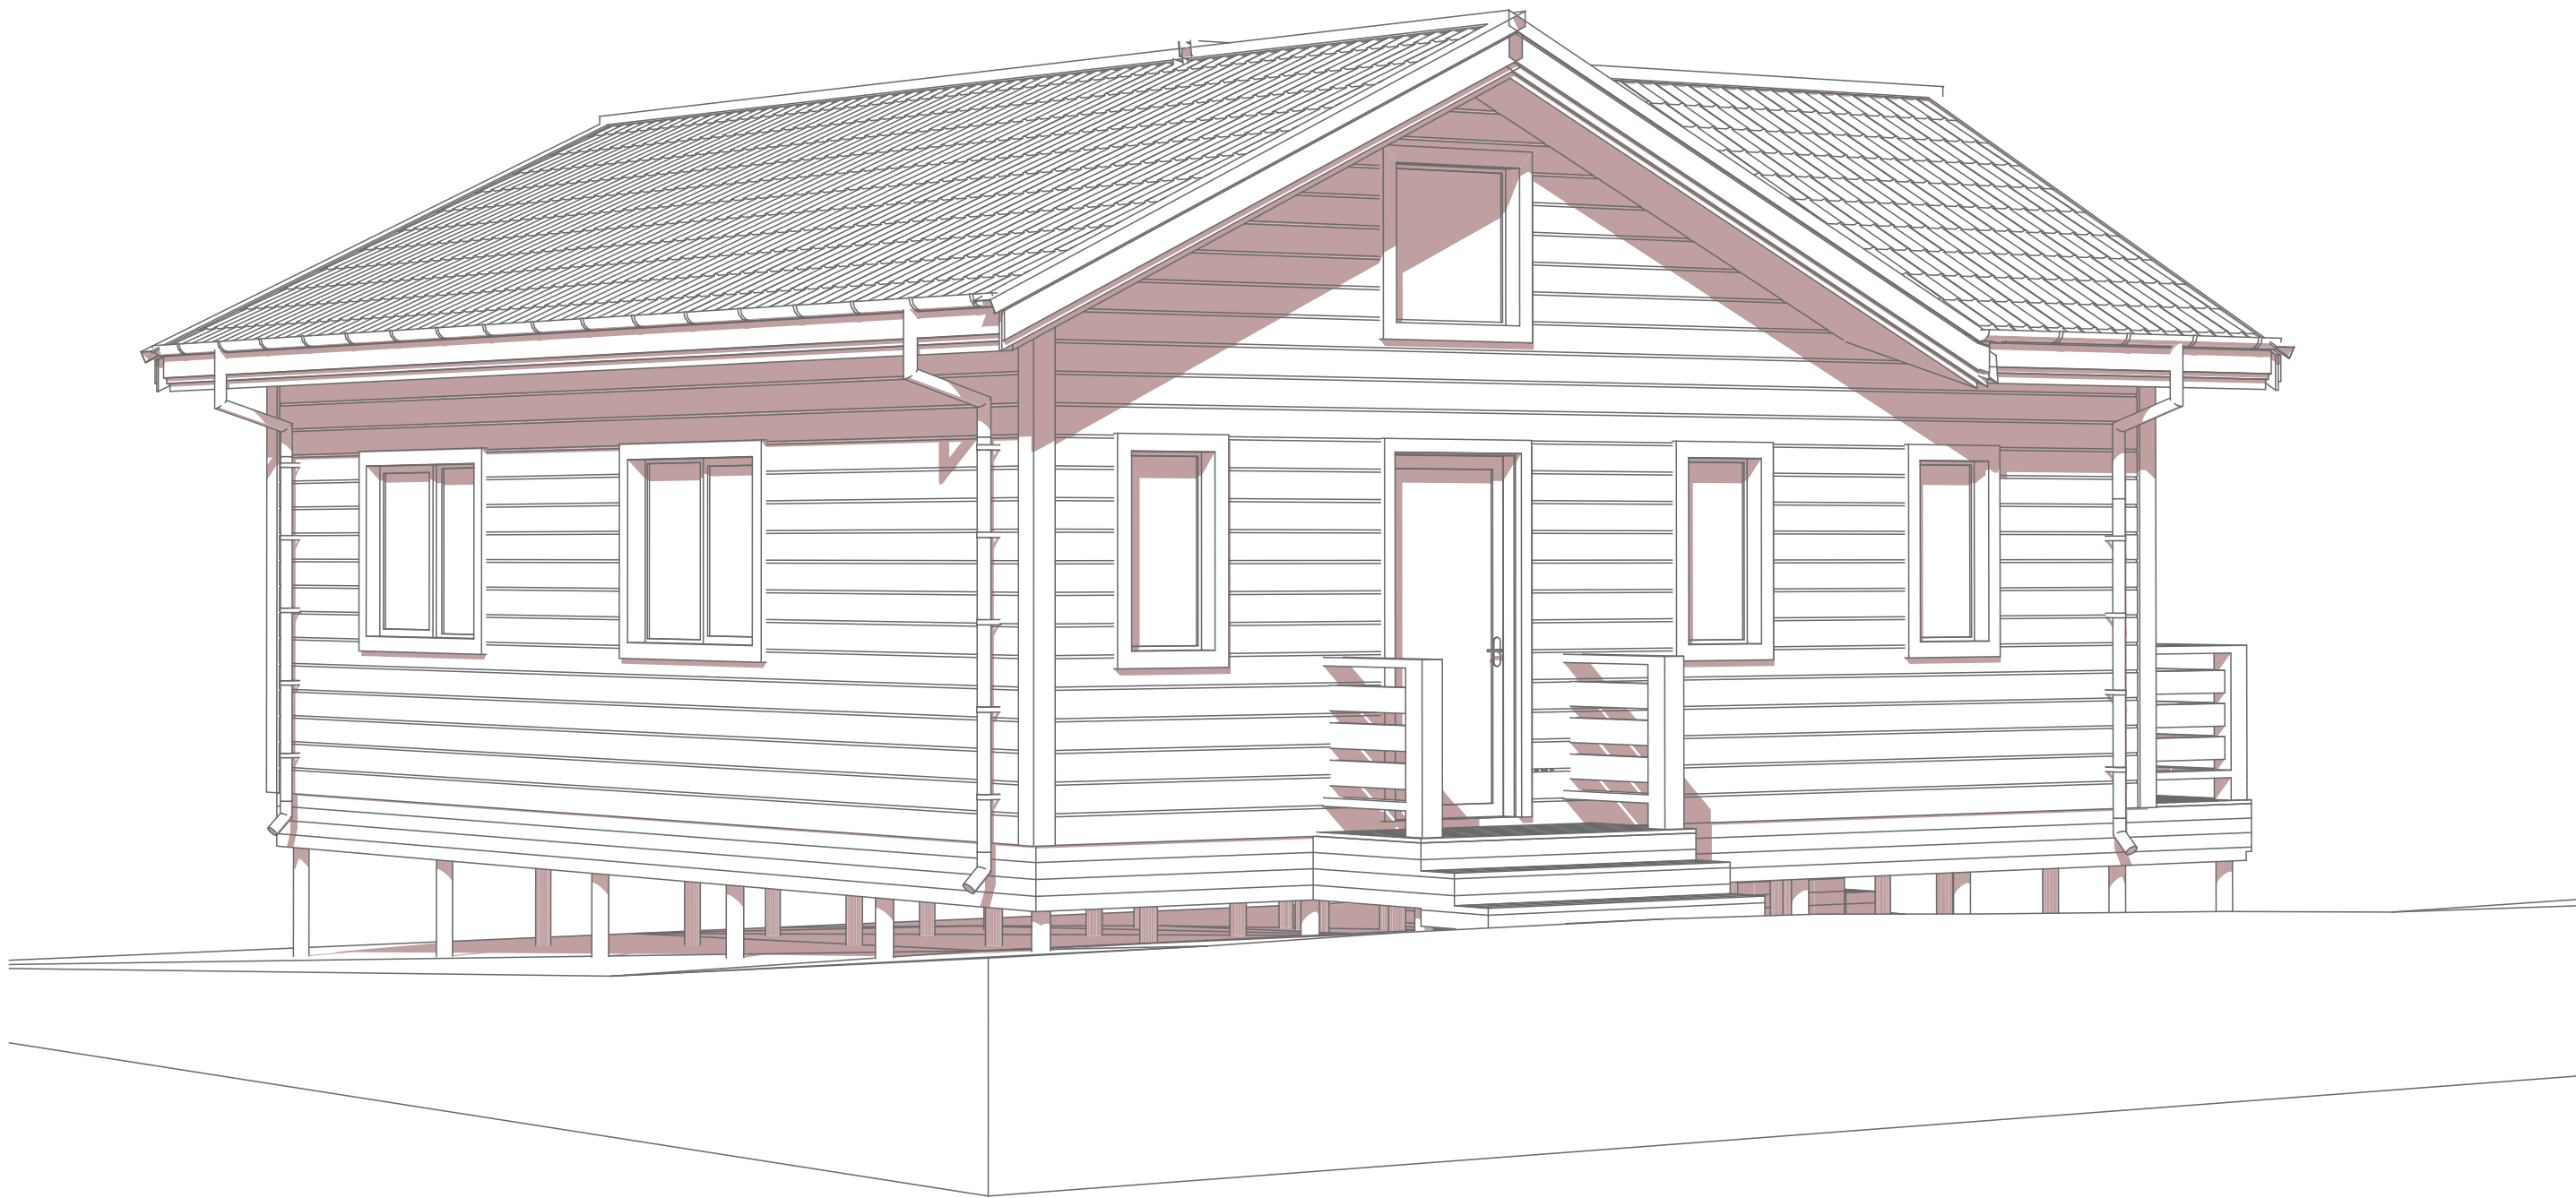

Лист	Изм.	№ Докум.	Подп.	Дата

обл. Московская, р-н Дмитровский, с/пос. Яотское, д. Новое Сельцо, дом 43

Аксометрия №2

Согласовано

Взам. инв. №

Подп. и дата

Инв. № подл.



Лист	Изм.	№ Докум.	Подп.	Дата

обл. Московская, р-н Дмитровский, с/пос. Якотское, д. Новое Сельцо, дом 43

Визуализация

Согласовано					
Инов. № подл.	Подп. и дата	Взам. инв. №			



Лист	Изм.	№ Докум.	Подп.	Дата

обл. Московская, р-н Дмитровский, с/пос. Якотское, д. Новое Сельцо, дом 43

Визуализация

Лист
31

Согласовано					
Изм. № подл.	Подп. и дата	Взам. инв. №			



Лист	Изм.	№ Докум.	Подп.	Дата

обл. Московская, р-н Дмитровский, с/пос. Яотское, д. Новое Сельцо, дом 43

Визуализация

Согласовано

Взам. инв. №

Подп. и дата

Инв. № подл.

Лист	Изм.	№ Докум.	Подп.	Дата

обл. Московская, р-н Дмитровский, с/пос. Яотское, д. Новое Сельцо, дом 43

Визуализация

Согласовано

Взам. инв. №

Подп. и дата

Инв. № подл.



Лист	Изм.	№ Докум.	Подп.	Дата

обл. Московская, р-н Дмитровский, с/пос. Якотское, д. Новое Сельцо, дом 43

Визуализация

Согласовано

Взам. инв. №

Подп. и дата

Инв. № подл.

Лист	Изм.	№ Докум.	Подп.	Дата

обл. Московская, р-н Дмитровский, с/пос. Якотское, д. Новое Сельцо, дом 43

Визуализация

Согласовано

Взам. инв. №

Подп. и дата

Инв. № подл.



Лист	Изм.	№ Докум.	Подп.	Дата

обл. Московская, р-н Дмитровский, с/пос. Яотское, д. Новое Сельцо, дом 43

Визуализация

Согласовано

Взам. инв. №

Подп. и дата

Инв. № подл.



Лист	Изм.	№ Докум.	Подп.	Дата

обл. Московская, р-н Дмитровский, с/пос. Яотское, д. Новое Сельцо, дом 43

Визуализация