


План размещения розеток

1:80

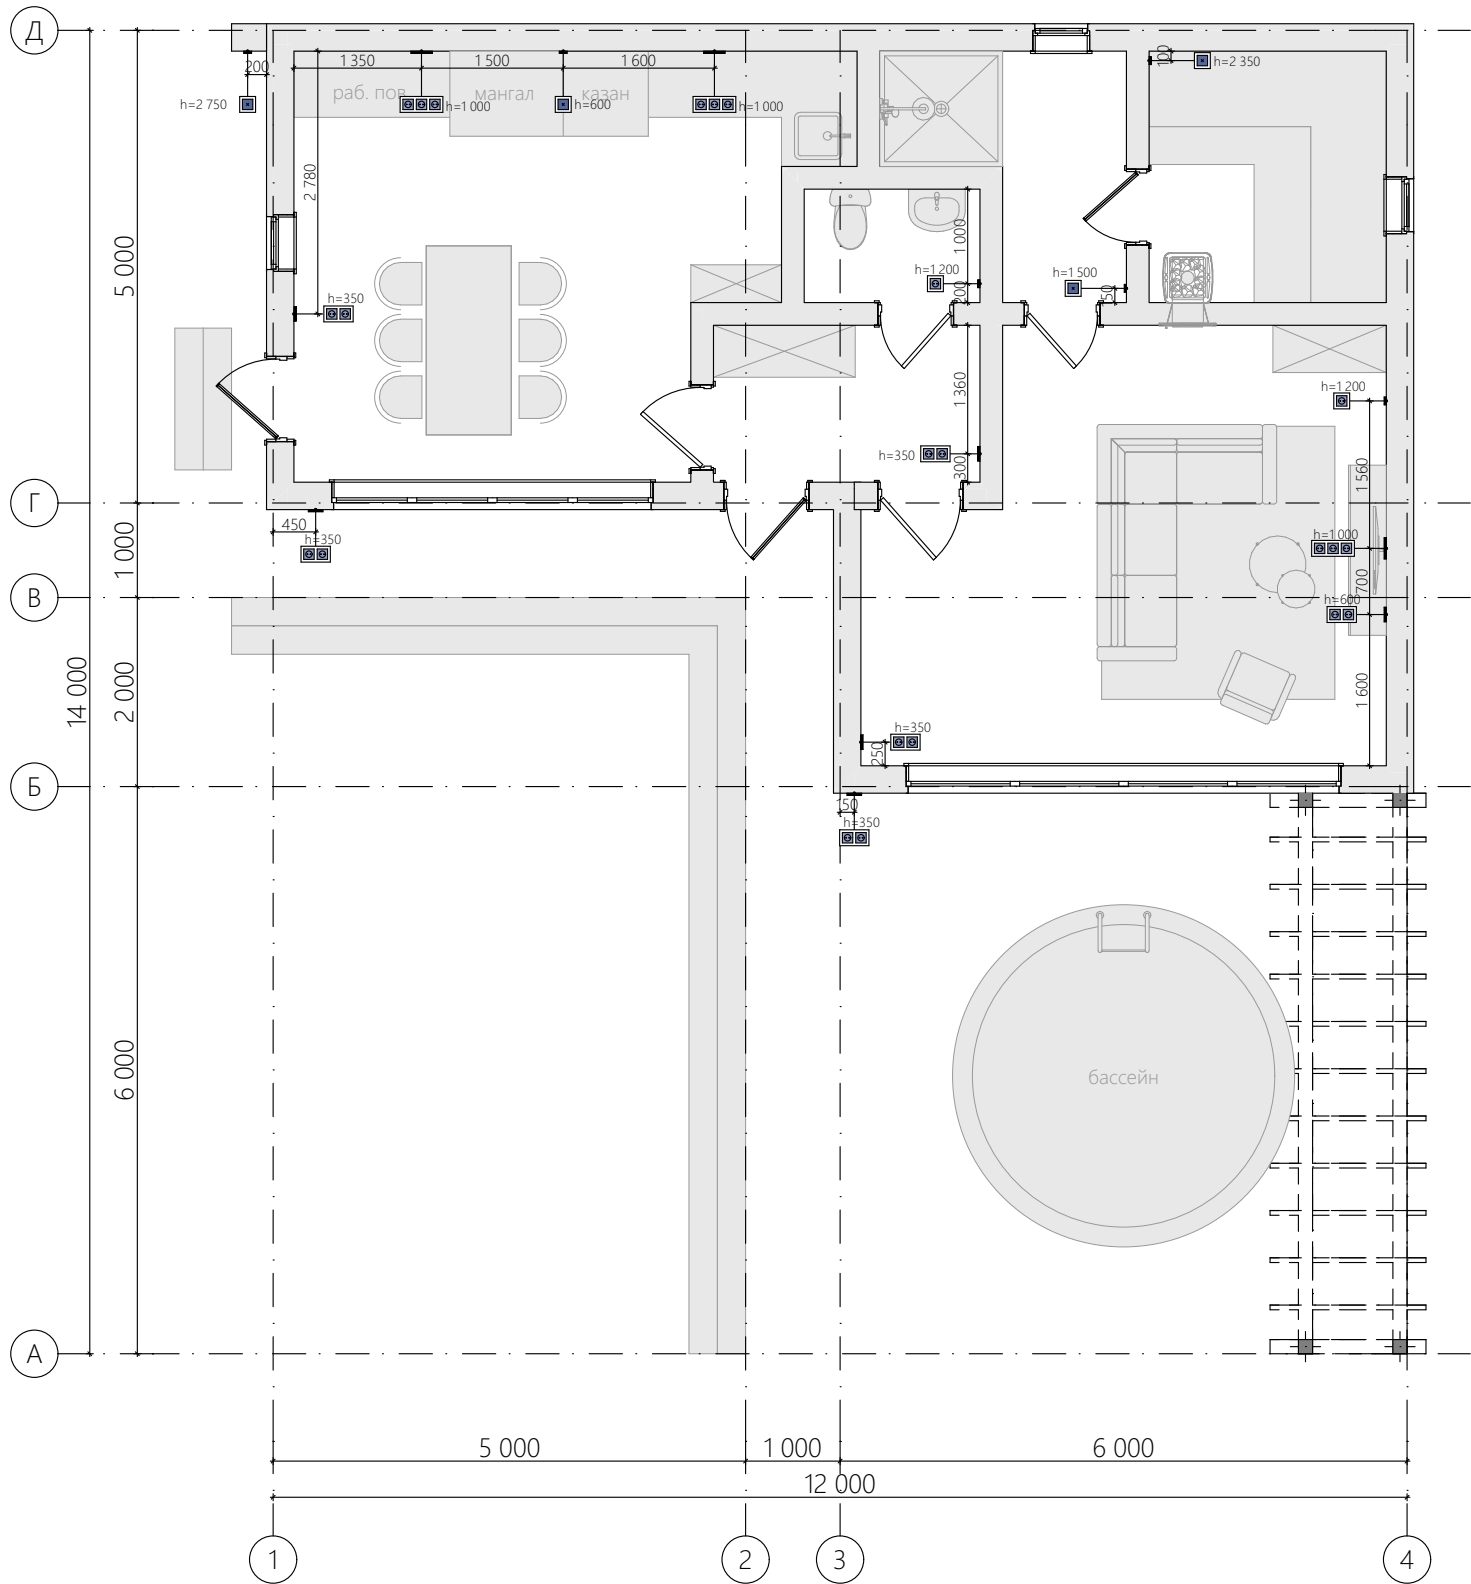

Экспликация розеток

Наименование	2д-вид	Кол-во
Розетка 220v (1 секции)		2
Розетка 220v (2 секции)		6
Розетка 220v (3 секции)		3
Эл. вывод (влагозащитная)		4
		15

Примечание:

1. Схема размещения розеток является рекомендательной и требует согласования с заказчиком по месту.
2. Все высоты даны от чистового пола.
3. Все указанные размеры даются до центра позиций.
4. Отметки розеток, выключателей, выводов и др. оборудования, являются предварительными и уточняются после выбора финишных материалов и мебели.
5. Размеры уточняются дополнительно

Согласовано				
Взам. инв. №				
Подп. и дата				
Инв. № подл.				

Лист	Изм.	№ Докум.	Подп.	Дата