


План размещения светильников и выключателей

1:80

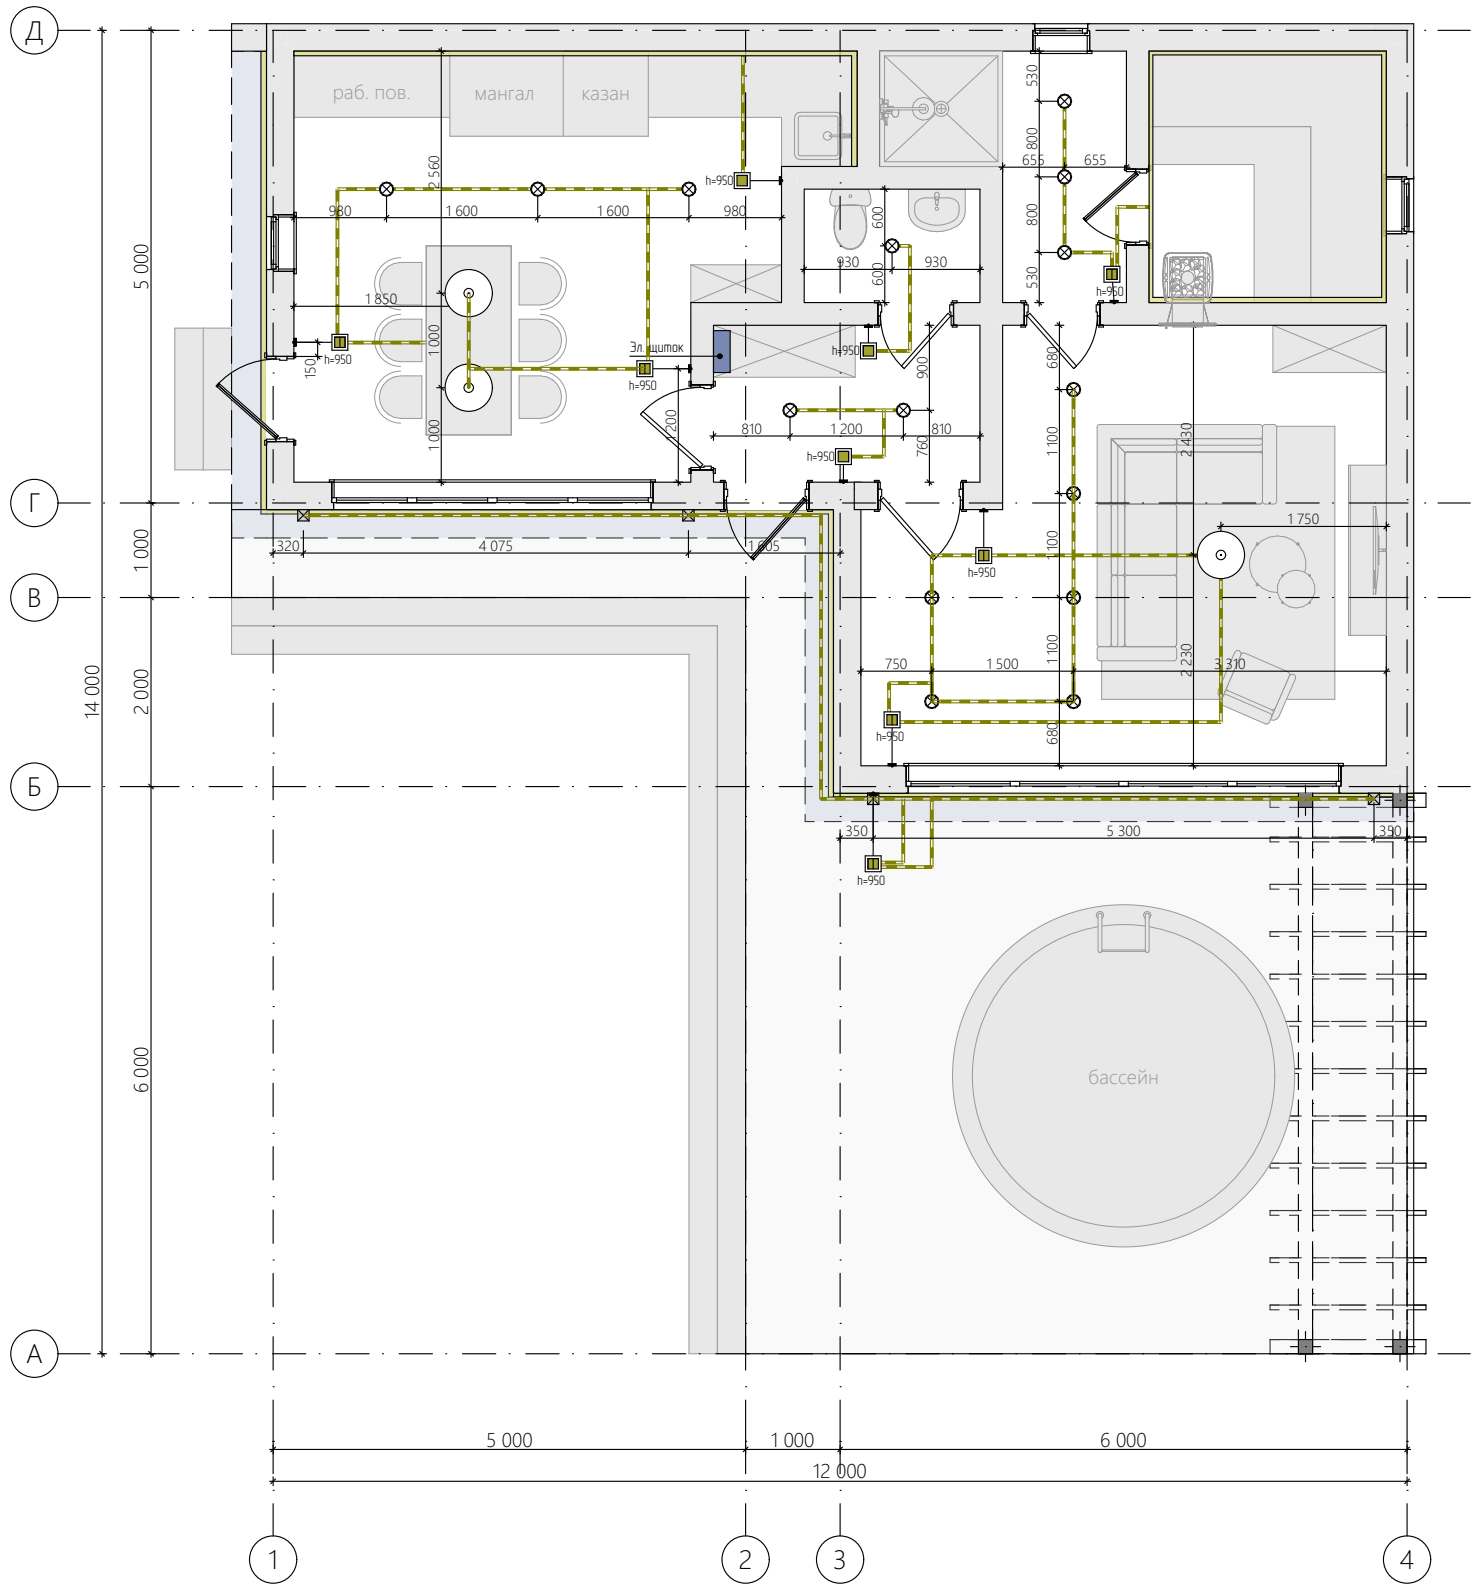

Экспликация светильников и выключателей

Наименование	2д-вид	Кол-во
Выключатель одноклавишный (1 секция)		3
Выключатель одноклавишный (2 секции)		6
Светильник подвесной		3
Точечный светильник		15
Уличный светильник		4
		31

Примечание:

1. Схема размещения розеток является рекомендательной и требует согласования с заказчиком по месту.
2. Все высоты даны от чистового пола.
3. Все указанные размеры даются до центра позиций.
4. Отметки розеток, выключателей, выводов и др. оборудования, являются предварительными и уточняются после выбора финишных материалов и мебели.
5. Размеры уточняются дополнительно

Согласовано

Взам. инв. №

Подп. и дата

Инв. № подл.

Лист	Изм.	№ Докум.	Подп.	Дата

План размещения светильников и выключателей

#Название Организации