


Маркировочный план

1:80

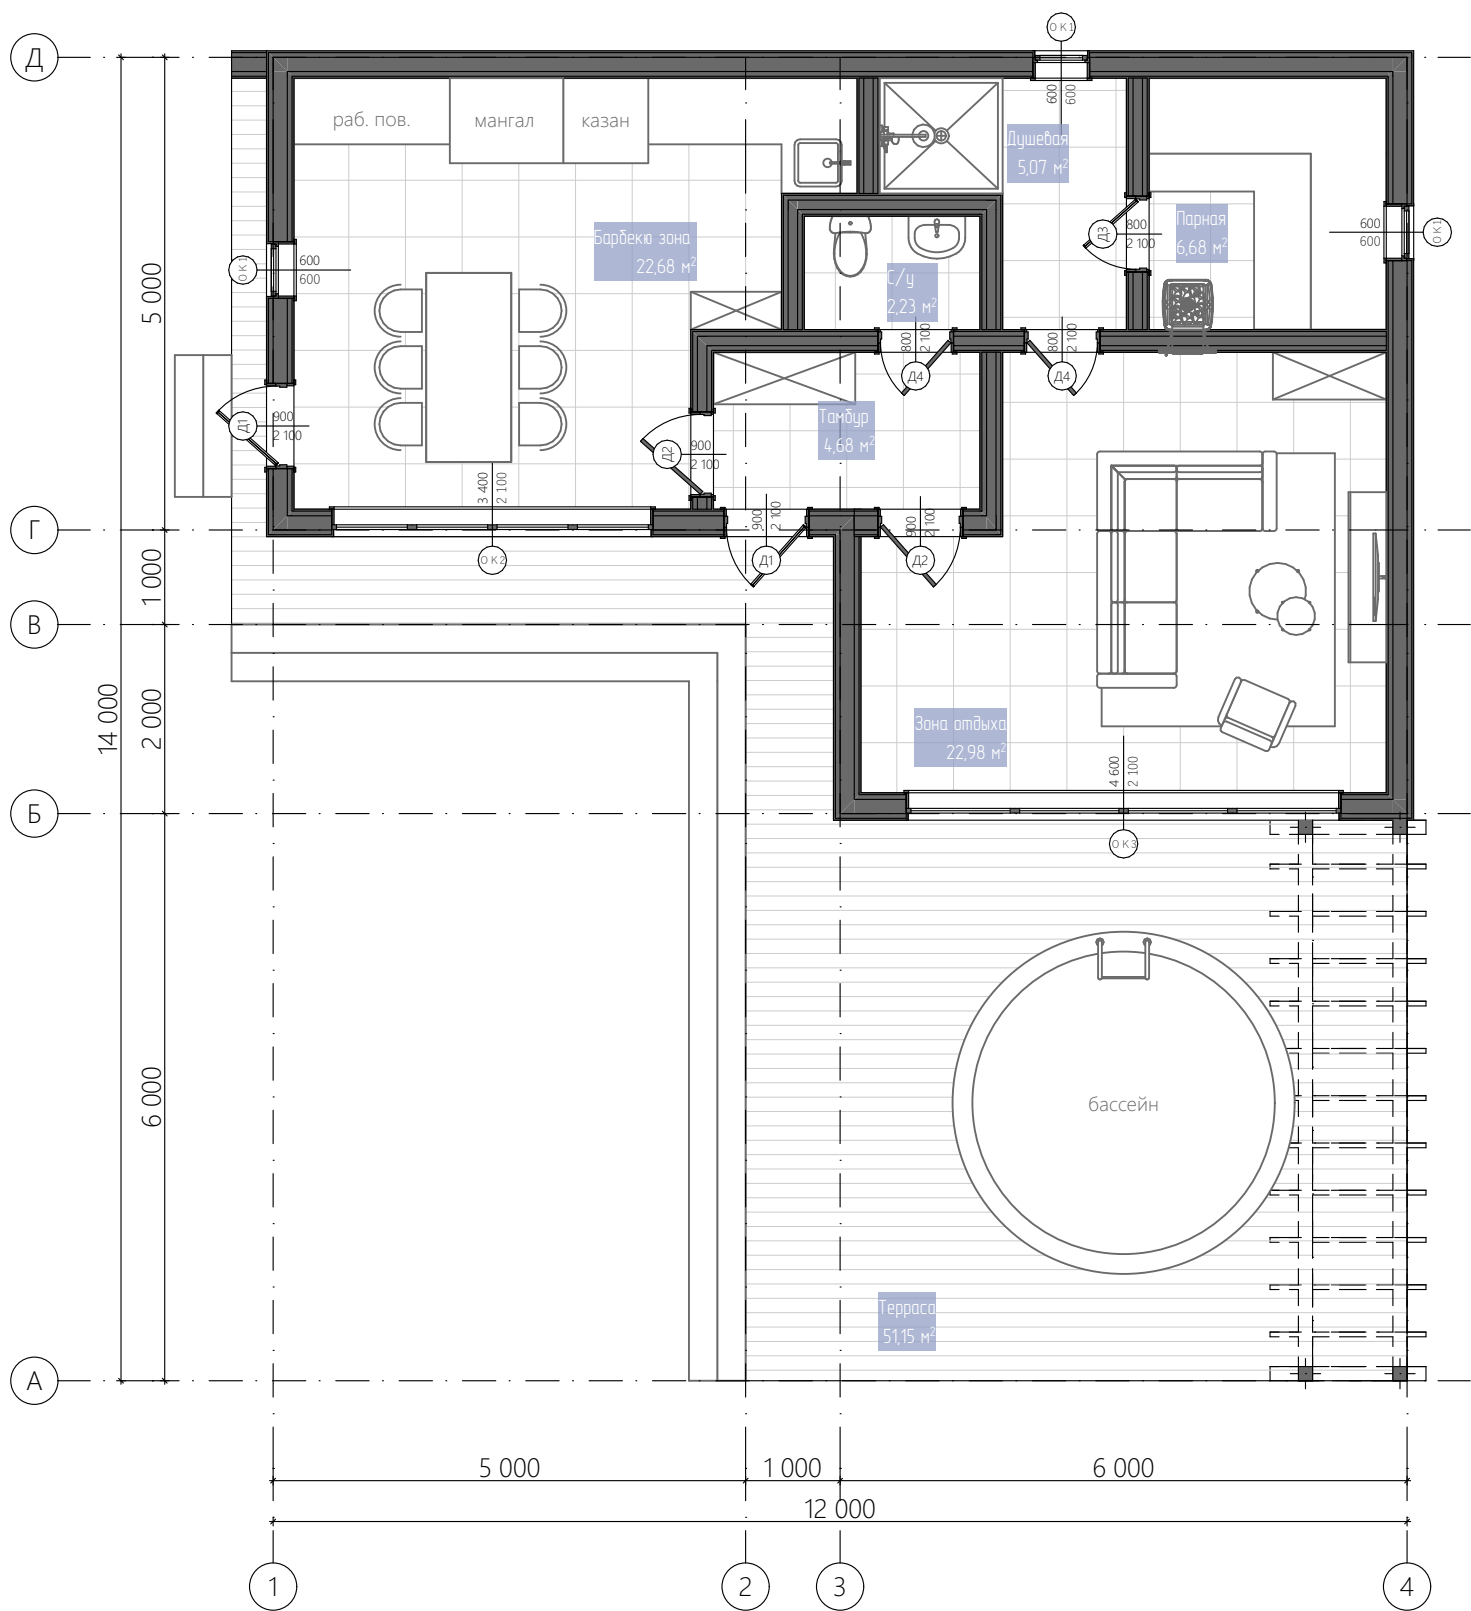

Экспликация помещений

№	Название	Площадь, м2
1	Терраса	51,15
2	Барбекю зона	22,68
3	Тамбур	4,68
4	С/у	2,23
5	Душевая	5,07
6	Парная	6,68
7	Зона отдыха	22,98
		115,47 м²

Название	Площадь, м2
Площадь застройки	128,00

Примечание:

1. Вся индивидуальная мебель выполняется по отдельному проекту с детальной проработкой и калькуляцией. Чертежи предоставляет фирма-изготовитель столярных изделий.
2. Данный проект отдельно согласовывается с автором проекта и непосредственно с заказчиком.
3. Цветовое решение фасада и материалов отделки показаны в проекте приблизительно.
4. Количество ступеней показано условно.

Согласовано

Взам. инв. №

Подп. и дата

Инв. № подл.

Лист	Изм.	№ Докум.	Подп.	Дата

Маркировочный план

#Название Организации