



План покрытия пола

1:80

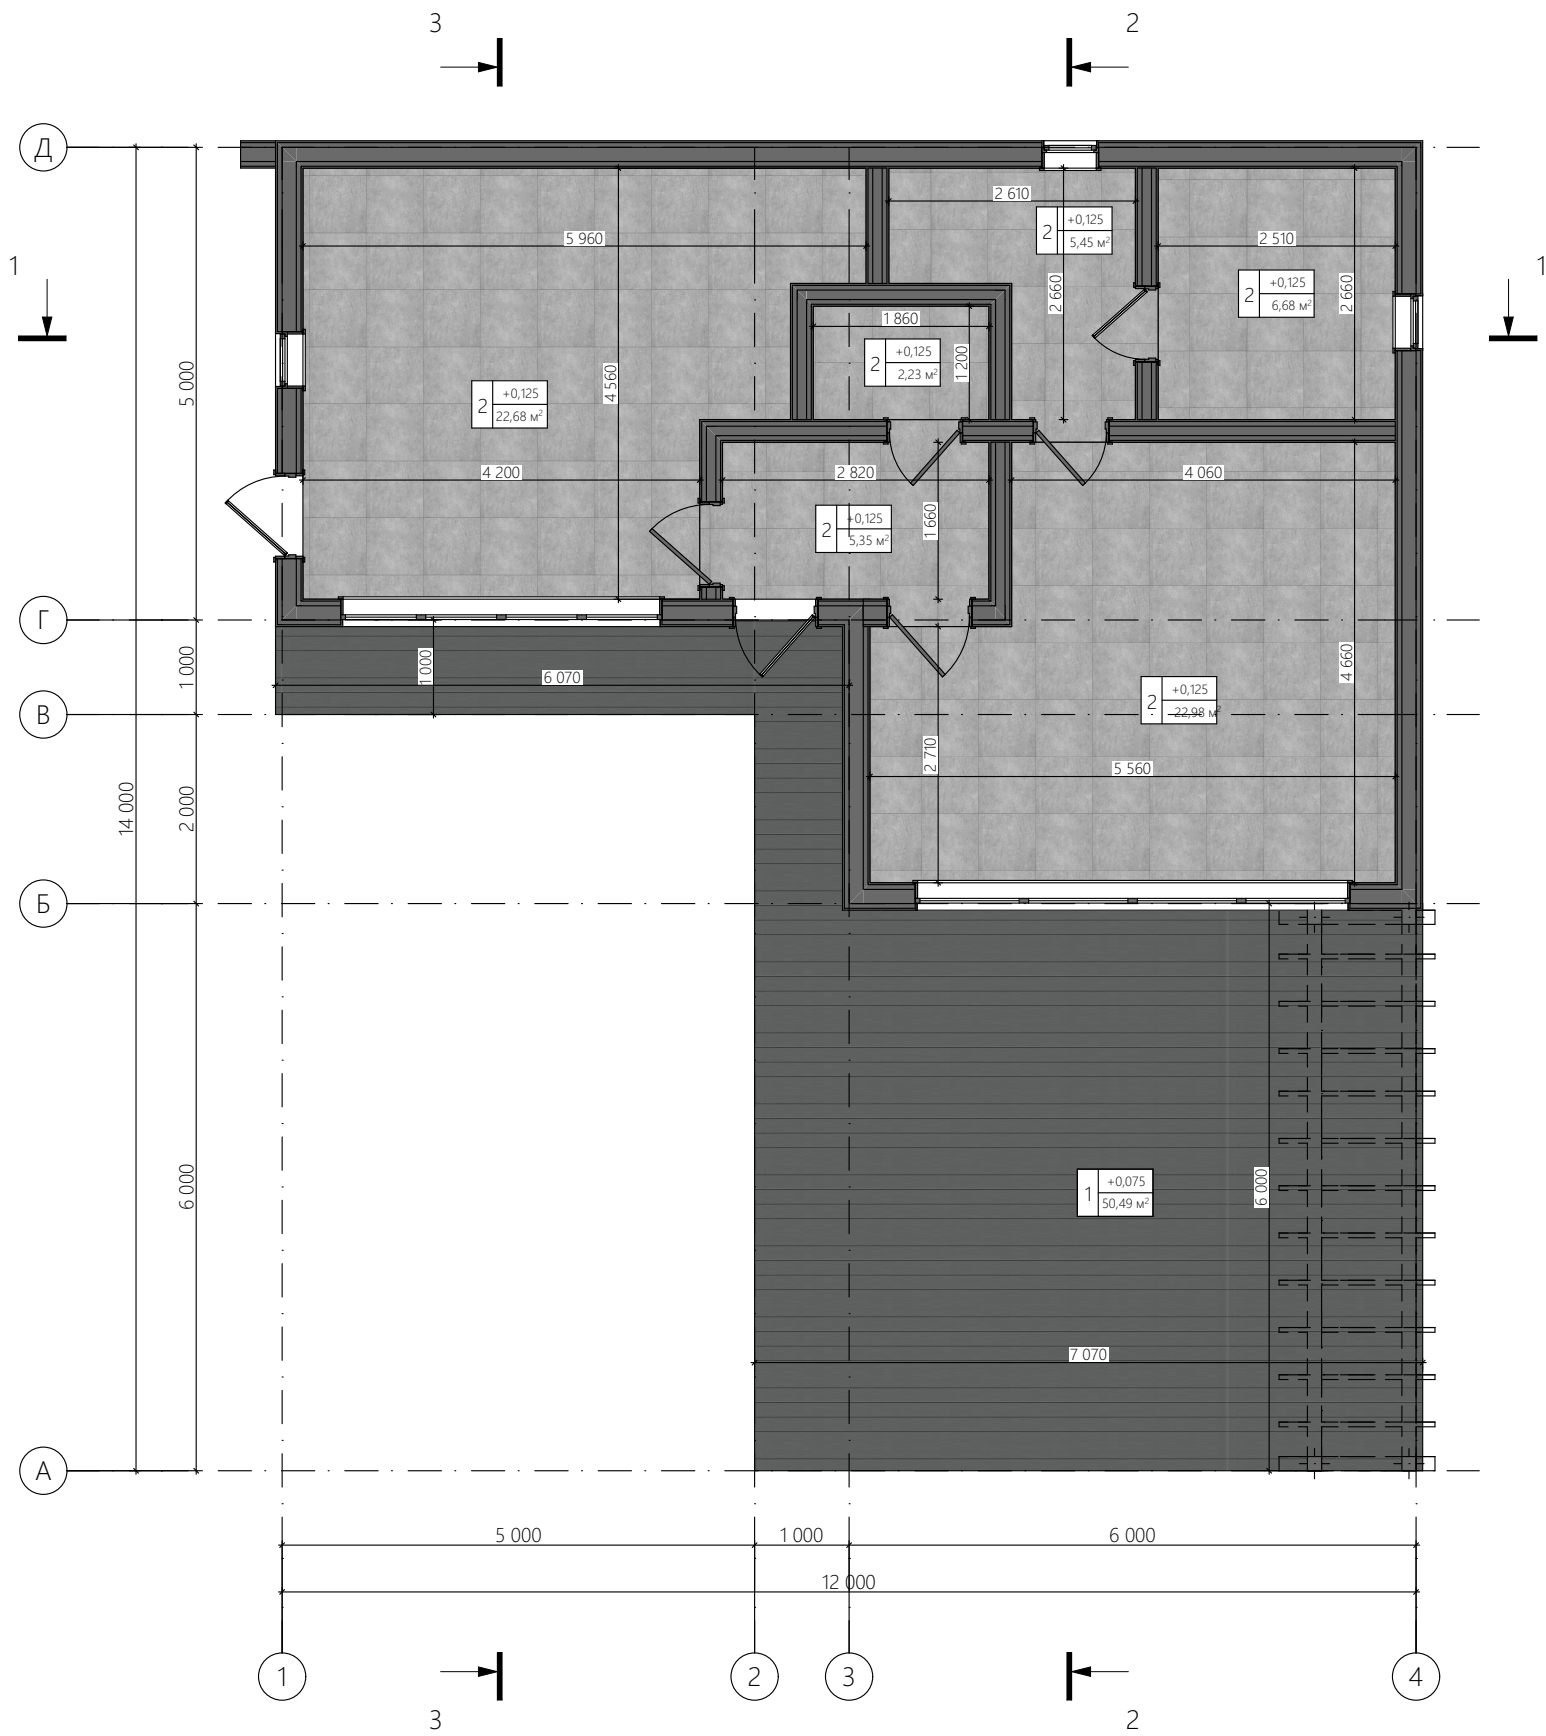

Условные обозначения

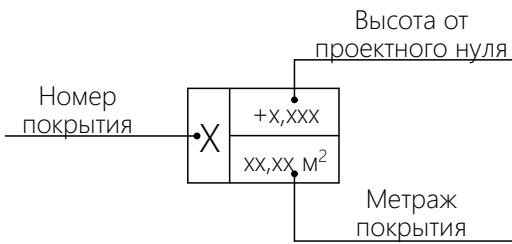

Экспликация покрытий пола

№	Наименование	Площадь, м²
1	Террасная доска	50,49
2	Керамогранит	65,37

Примечание:

1. Приведённые цветовые решения носят рекомендательный характер. Фактический подбор оттенков и материалов выполняется на этапе реализации с учётом наличия продукции у поставщиков и утверждения заказчиком.
2. Пирог покрытия смотреть на след. листе.

Согласовано

Взам. инв. №

Подп. и дата

Инв. № подл.

Лист	Изм.	№ Докум.	Подп.	Дата

План покрытия пола

#Название Организации