

РАБОЧИЙ ПРОЕКТ



Архитектор

Мясникова В.А.

Заказчик

г. Москва 2026

Инов. № подл.	Подп. и дата	Взам. инв. №	Согласовано	

Лист	Наименование	Примечание
1	Титульный	
2	Ведомость чертежей	
3	Пояснительная записка	
4	Маркировочный план	
5	Размерный план	
6	План расстановки мебели и оборудования	
7	План покрытия пола	
8	Пироги пола	
9	План покрытия стен	
10	Пироги стены	
11	План размещения розеток	
12	План размещения светильников и выключателей	
13	План теплого пола	
14	План крыши	
15	Ведомость заполнения оконных проемов	
16	Ведомость заполнения дверных проемов	
17	Разрез 1-1	
18	Разрез 2-2	
19	Разрез 3-3	
20	Фасад 1-4	
21	Фасад А-Д	
22	Фасад Д-А	
23	Фасад 4-1	
24	Аксонометрия №1	
25	Аксонометрия №2	
26	Визуализация	
27	Визуализация	
28	Визуализация	
29	Визуализация	

Лист	Изм.	№ Докум.	Подп.	Дата

--

Ведомость чертежей

#Название Организации

В основу архитектурно-планировочных решений положены требования технологических заданий и требования норм и правил строительного проектирования, действующих на территории РФ.

Основные параметры и требования разработаны на основании пожеланий и требований заказчика.

Архитектурные решения приняты в соответствии со следующими нормативными документами:

- Градостроительный кодекс российской федерации.
- Земельного Кодекса Российской Федерации.
- Федеральный закон от 22.07.2008 N 123 - ФЗ (ред. от 29.07.2017)"Технический регламент о требованиях

пожарной безопасности.

- Федеральный закон № 384 - ФЗ «Технический регламент о безопасности зданий и сооружений».
- ГОСТ Р 21.1101-2013.«Основные требования к проектной и рабочей документации».
- Постановление правительства РФ от 16.02.2008 № 87 «Положение о составе разделов проектной документации и требованиях к их содержанию».

- СП 42.13330.2011 «Градостроительство. Планировка и застройка городских и сельских поселений».
- СП 131.13330.2018 «СНиП 23-01-99* Строительная климатология».
- СП 20.13330.2016 «СНиП 2.01.07-85* Нагрузки и воздействия».
- СП 22.13330.2016 «СНиП 2.02.01-83* Основания зданий и сооружений».
- СП 70.13330.2012 (с изменениями №1) «СНиП 3.03.01-87 Несущие и ограждающие конструкции».
- СП 64.13330.2017 «СНиП II-25-80 Деревянные конструкции».
- СП 17.13330.2017 «СНиП II-26-76 Кровли».
- СП 29.13330.2011 «СНиП 2.03.13-88 Полы».
- СП 28.13330.2017 «СНиП 2.03.11-85 Защита строительных конструкций от коррозии».
- СП 50.13330.2012 «СНиП 23-02-2003 Тепловая защита зданий».

Согласовано				
И-нв. № подл.	Подп. и дата	Взам. инв. №		

1. Общие данные:

1.1. Архитектурный проект разработан на основании требований и пожеланий заказчика.

Тип строения	беседка
Относительная отм. ±0.000	ур. верха лаг перекрытия
Общая площадь застройки, м2	128,00м2
Габаритные размеры каркаса здания, м	14,00х12,00
Этажность	1 этаж
Конструктивная схема	деревянный каркас

2. Конструктивные решения:

2.1. Рабочие чертежи разработаны на основании задания на проектирование

Полезная нагрузка на перекрытие	150 кгс/м2	-
Нормативная глубина промерзания	1,2м	СП 22.13330.2016 СП 131.13330.2020
Нормативное ветровое давление	I район (23кгс/м2)	СП 22.13330.2016
Нормативный вес снегового покрова	III район (150кгс/м2)	СП 22.13330.2016
Температура наиболее холодной пятидневки	-29°С	СП 131.13330.2020

2.2. Конструктивное строение представляет собой сооружение:

- на свайном фундаменте
- несущими стенами из деревянного каркаса
- плоской кровлей по деревянным стропилам

2.3. Необходимо осуществлять технический надзор за производством строительных работ. Данные по проведённым работам необходимо систематически вносить в журнал работ.

По каждому из этапов работ необходимо осуществлять входной контроль материалов и вести приёмку.

Фундамент	винтовые сваи (d=108мм)
Несущие конструкции	деревянный каркас (145х45мм)
Стропильная система	строганая доска (195х45мм)
Тип крыши	плоская
Покрытие кровли	наплавляемая

2.4. Все деревянные конструкции обработать огне-биозащитными септиками в соответствии со СП 28.13330.2017 "Защита строительных конструкций от коррозии".

2.5. Кровельные работы выполнять в соответствии с требованиями фирмы производителя.

2.6. Все работы вести в строгом соответствии с требованиями СНиП 12.03.2001 "Безопасность труда в строительстве".

2.7. При выполнении всех работ строго соблюдать меры противопожарной безопасности.

2.8. Возможна замена материалов аналогами.

*Решения, принятые в проекте и отображенные в чертежах, соответствуют требованиям экологических, санитарно - гигиенических, противопожарных и других норм, действующих на территории Российской Федерации, и обеспечивают безопасную для жизни и здоровья людей эксплуатацию объекта при соблюдении предусмотренных рабочих чертежей и мероприятий.


Лист	Изм.	№ Докум.	Подп.	Дата

Пояснительная записка

#Название Организации

Маркировочный план

1:80

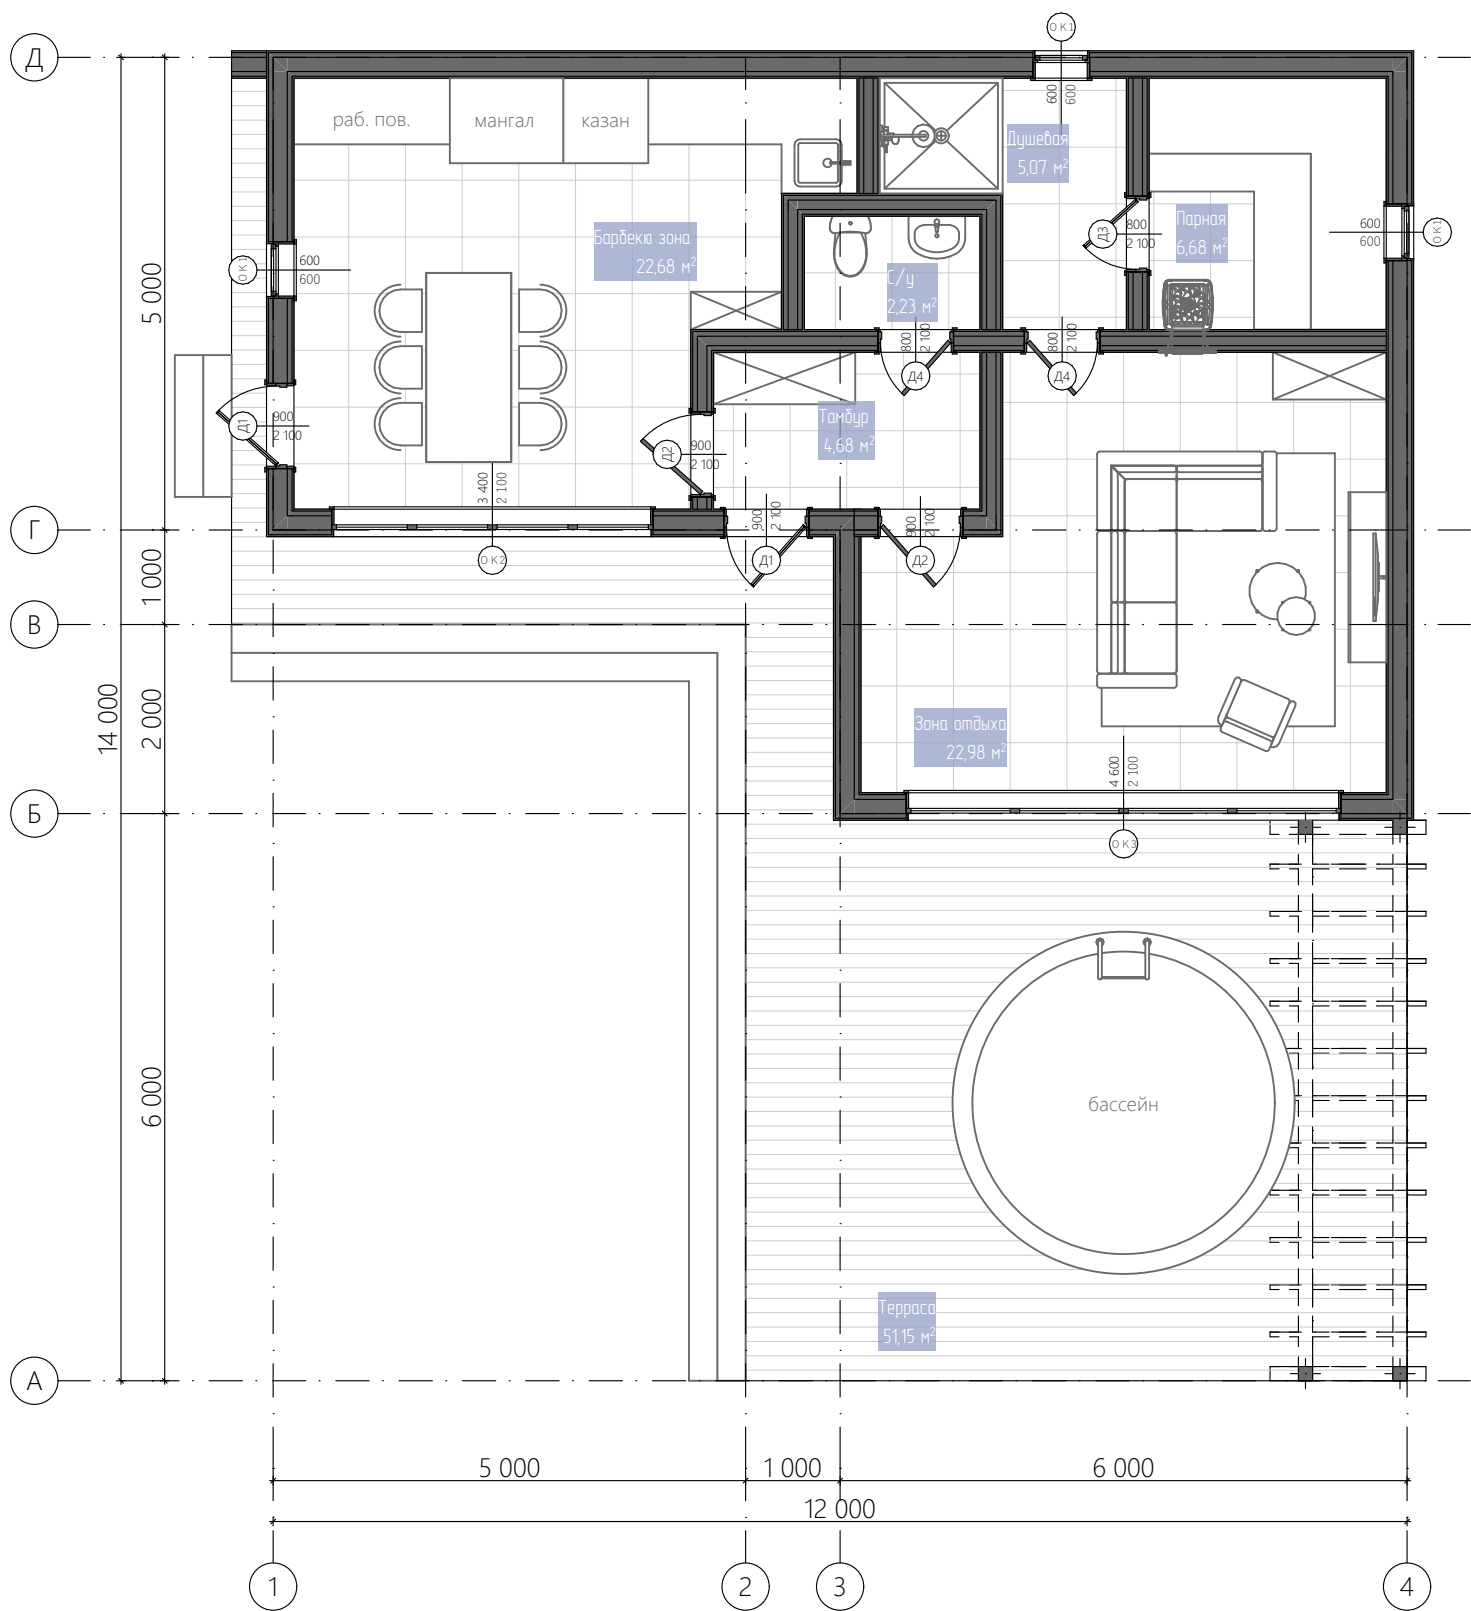

Экспликация помещений

№	Название	Площадь, м2
1	Терраса	51,15
2	Барбекю зона	22,68
3	Тамбур	4,68
4	С/у	2,23
5	Душевая	5,07
6	Парная	6,68
7	Зона отдыха	22,98
		115,47 м²

Название	Площадь, м2
Площадь застройки	128,00

Примечание:

1. Вся индивидуальная мебель выполняется по отдельному проекту с детальной проработкой и калькуляцией. Чертежи предоставляет фирма-изготовитель столярных изделий.
2. Данный проект отдельно согласовывается с автором проекта и непосредственно с заказчиком.
3. Цветовое решение фасада и материалов отделки показаны в проекте приблизительно.
4. Количество ступеней показано условно.

Согласовано

Взам. инв. №

Подп. и дата

Инв. № подл.


Лист	Изм.	№ Докум.	Подп.	Дата

Маркировочный план

#Название Организации

Размерный план

1:80

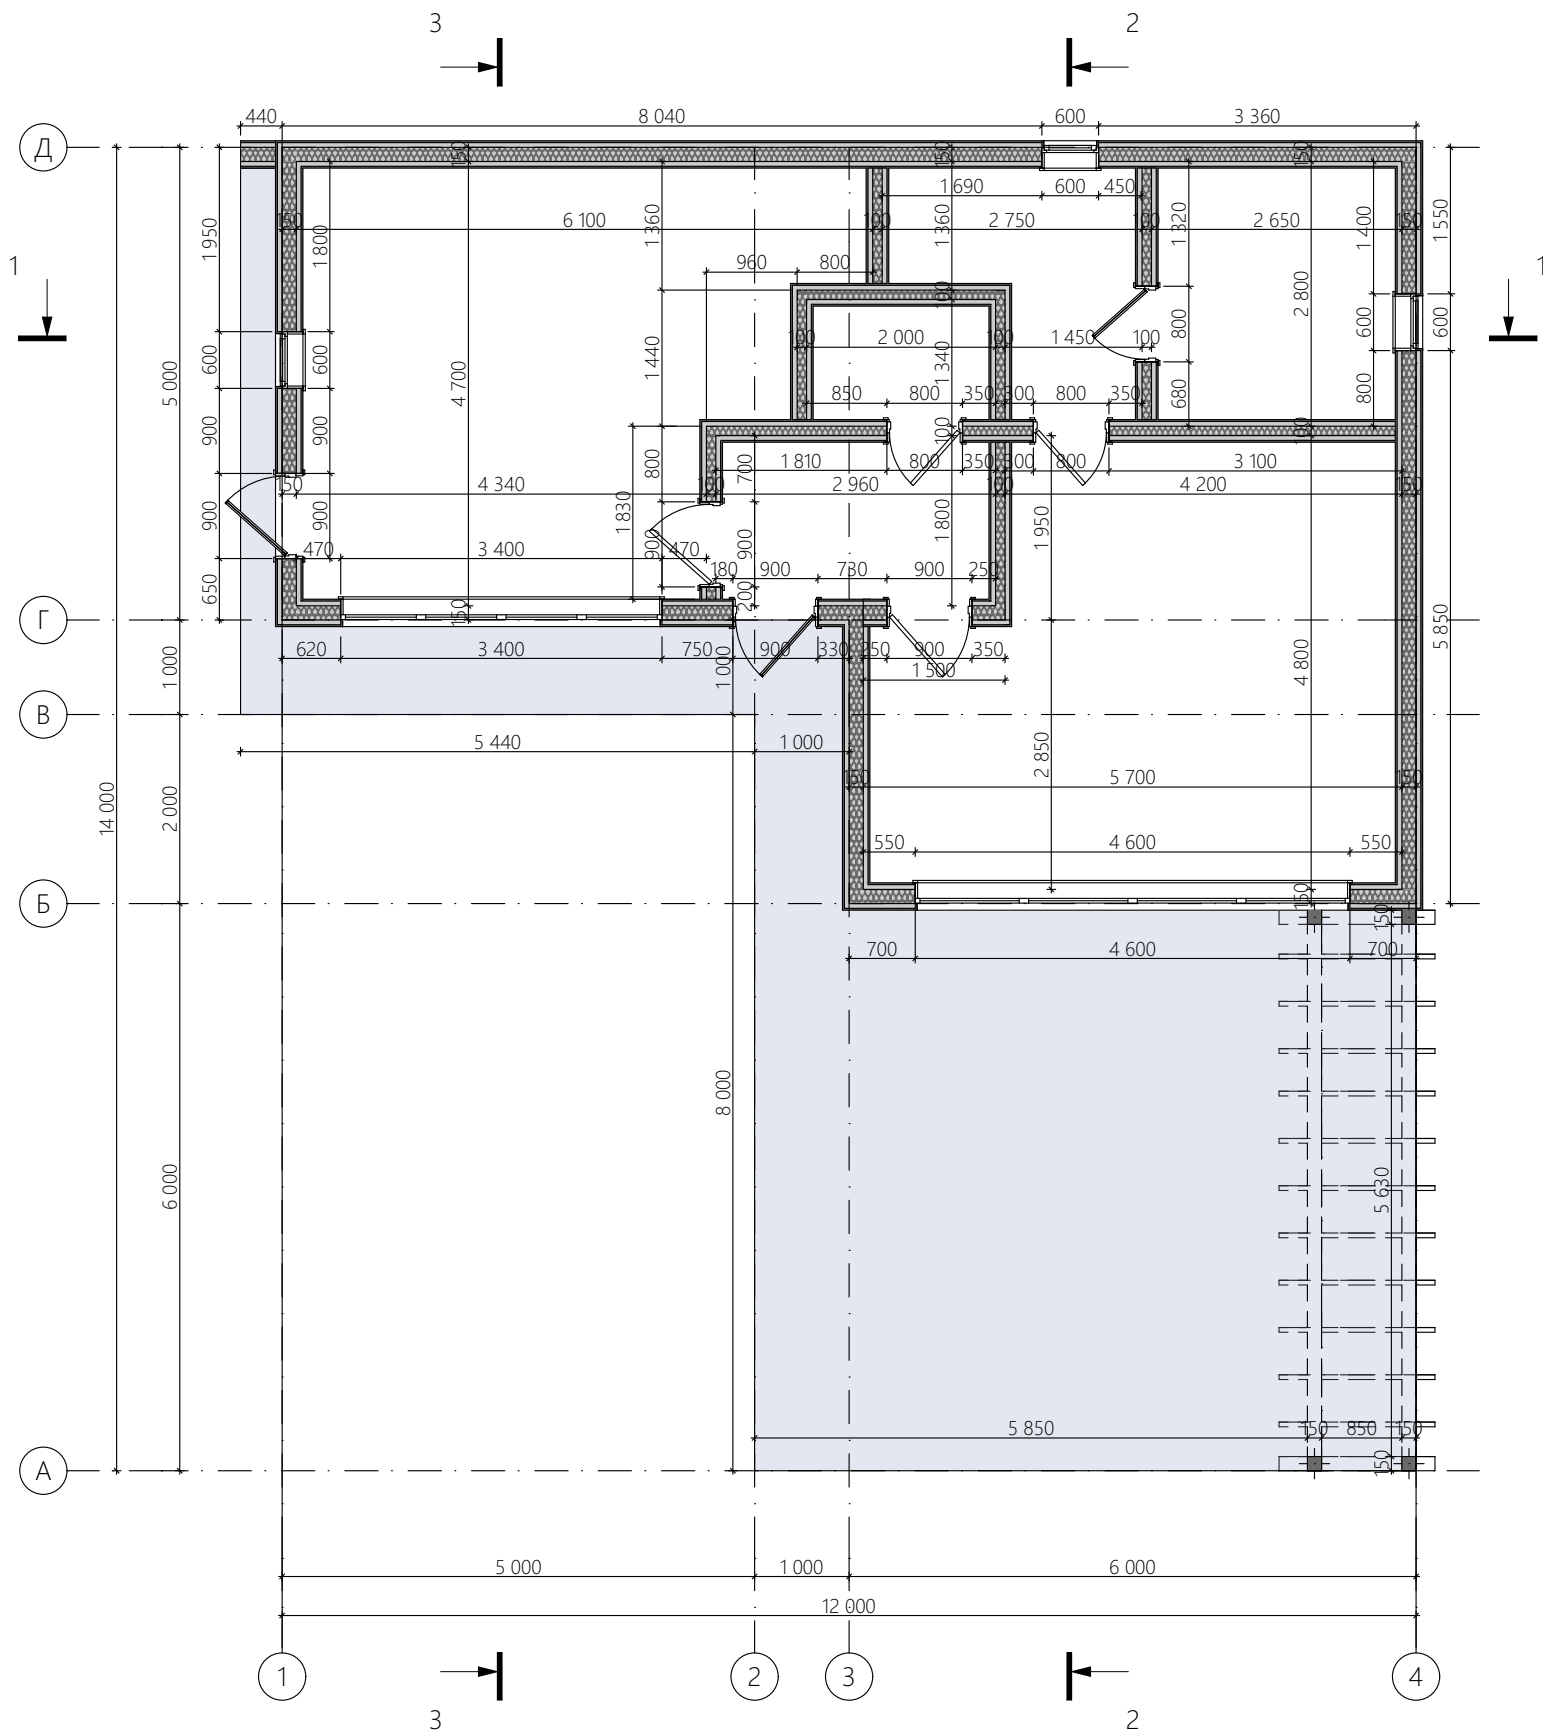


Примечание:
1. Представленные размеры указаны без учета внешней и внутренней отделки

Согласовано				
И-нв. № подл.	Подп. и дата	Взам. инв. №		

Лист	Изм.	№ Докум.	Подп.	Дата

Размерный план

#Название Организации
5

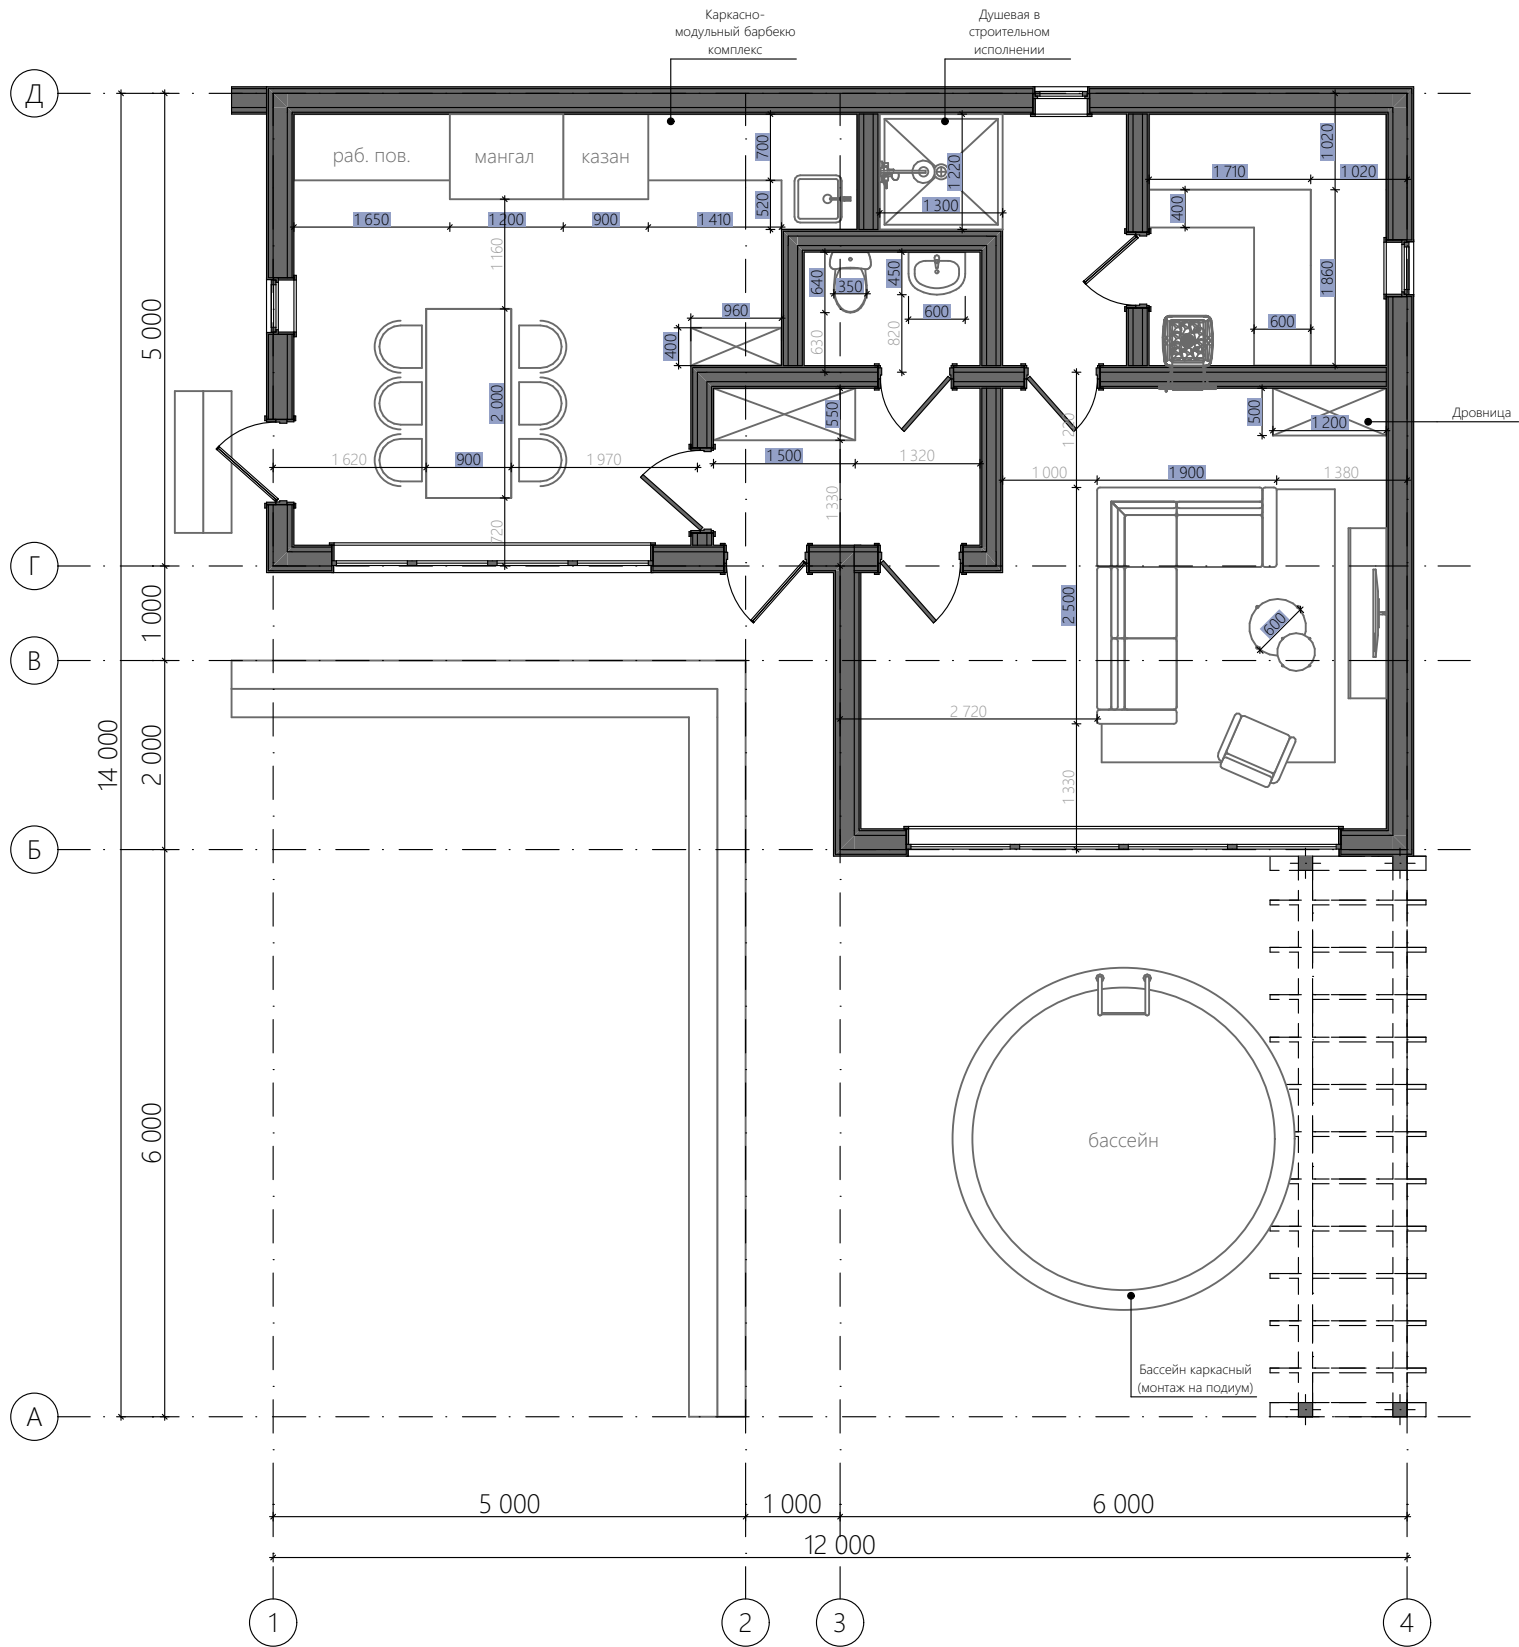

Примечание:

1. Вся индивидуальная мебель выполняется по отдельному проекту с детальной проработкой и калькуляцией. Чертежи предоставляет фирма-изготовитель столярных изделий.


2. Финальные размеры мебели и оборудования указаны ориентировочно — для точной компоновки требуется разработка дизайн-проекта.

Согласовано					
И-нв. № подл.	Подп. и дата	Взам. инв. №			

Лист	Изм.	№ Докум.	Подп.	Дата


Согласовано				
И-нв. № подл.	Подп. и дата	Взам. инв. №		

Лист	Изм.	№ Докум.	Подп.	Дата

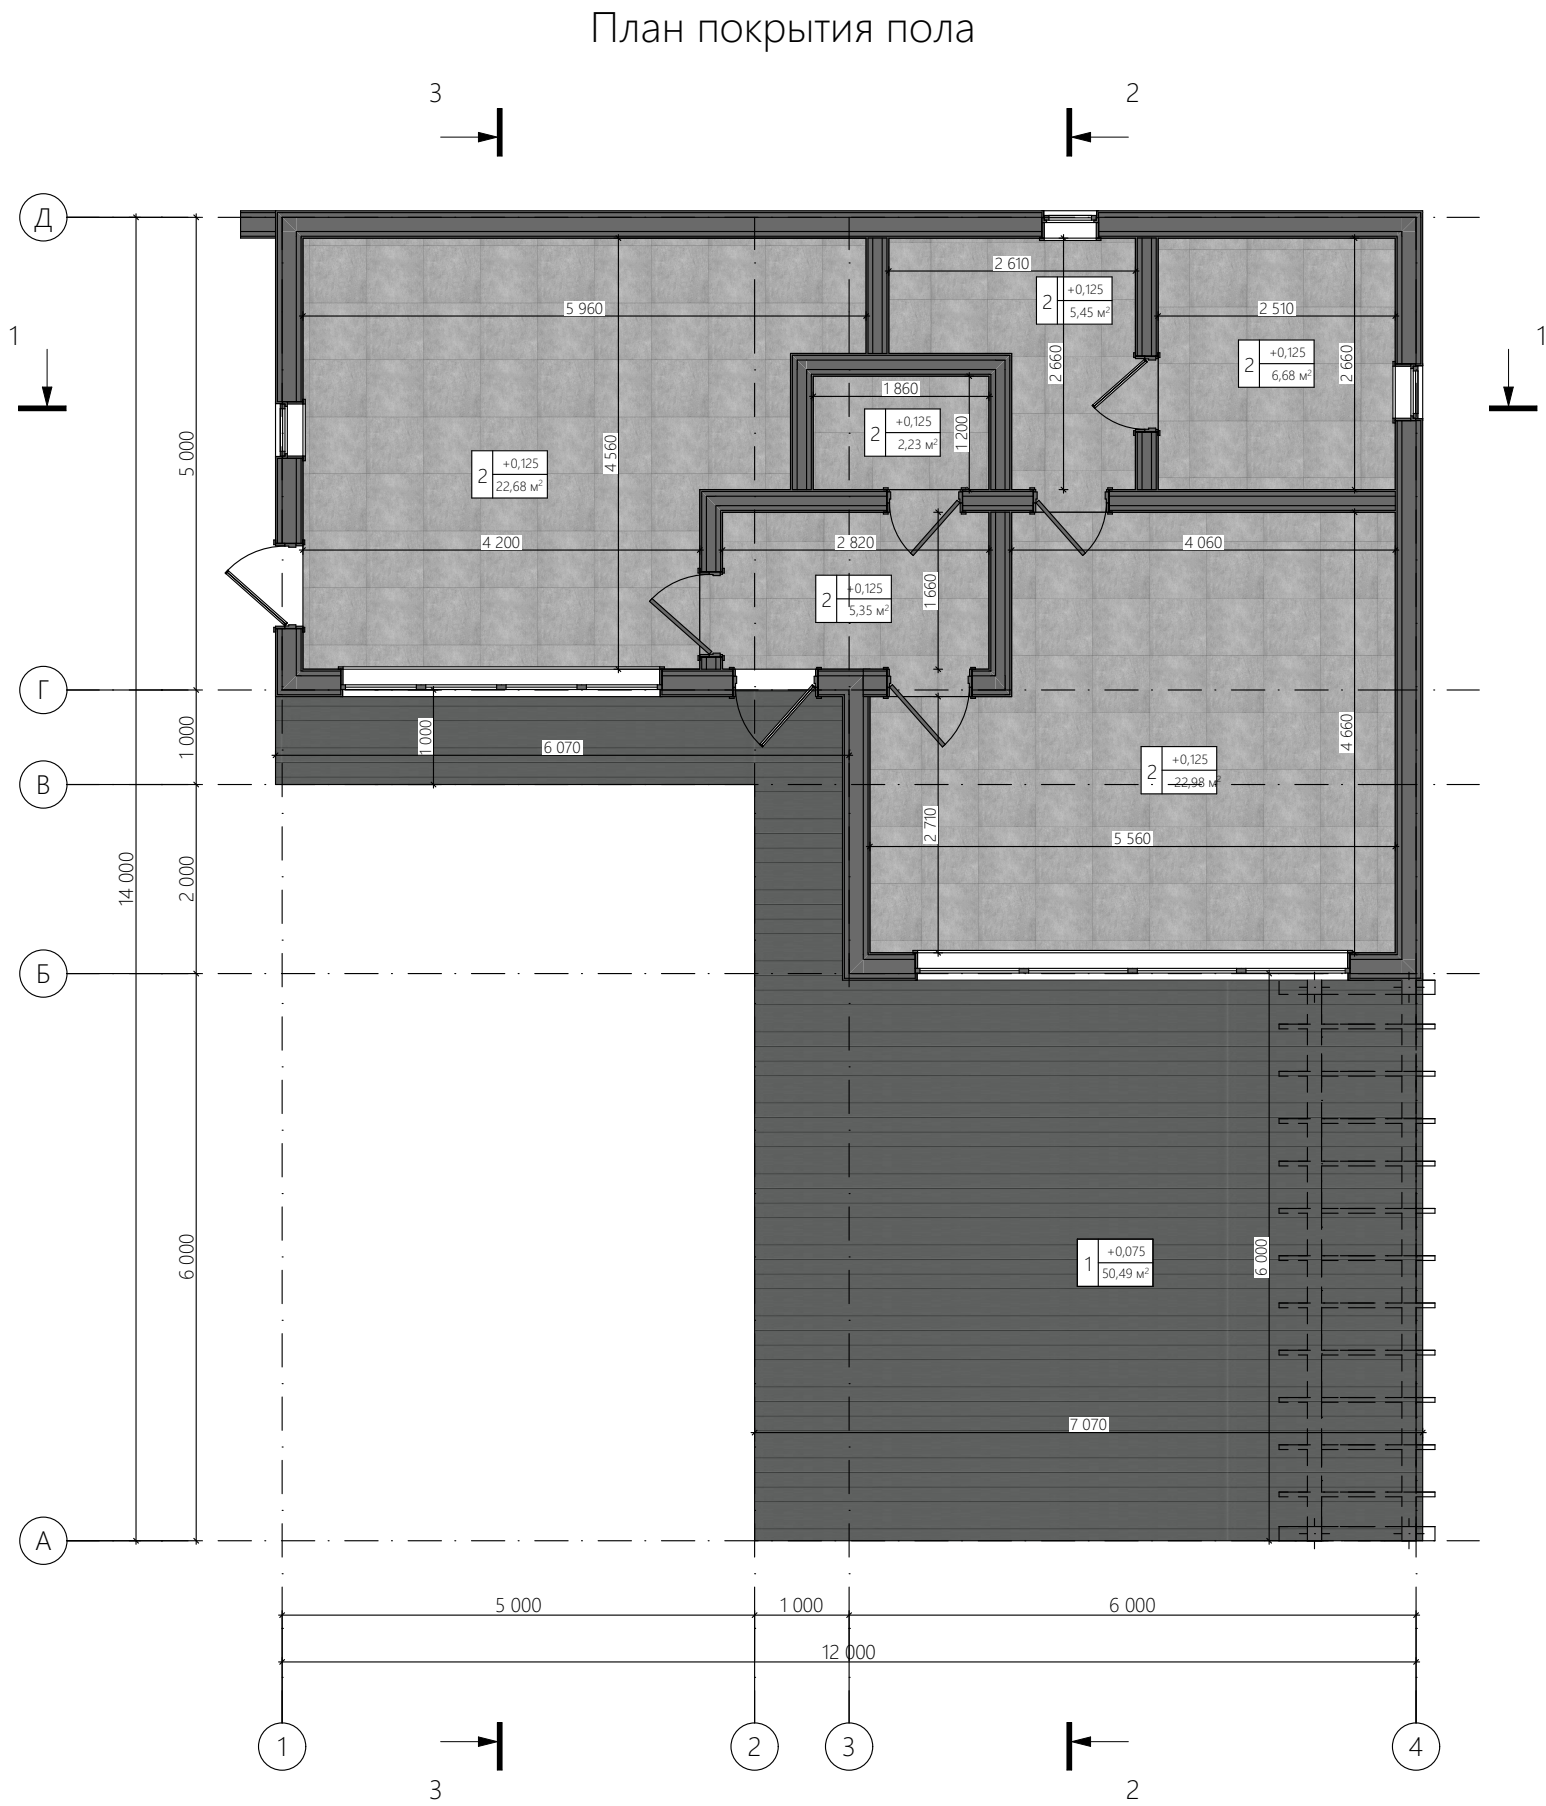

1:80

Условные обозначения

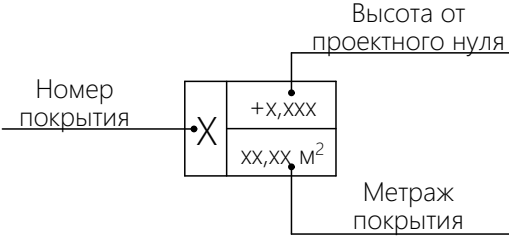

Экспликация покрытий пола

№	Наименование	Площадь, м²
1	Террасная доска	50,49
2	Керамогранит	65,37

Примечание:


1. Приведённые цветовые решения носят рекомендательный характер. Фактический подбор оттенков и материалов выполняется на этапе реализации с учётом наличия продукции у поставщиков и утверждения заказчиком.

2. Пирог покрытия смотреть на след. листе.

Пироги пола


№ Наименование Разрез Состав

1 Террасная доска

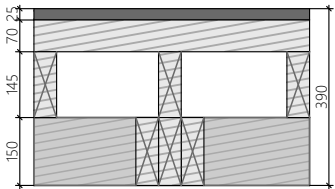

- ДПК 25мм
- Брусок добавочный 70мм
- Лага перекрытия (шаг 400мм) 145мм
- Нижняя обвязка (тройная сращенная доска) 150мм

2 Керамогранит

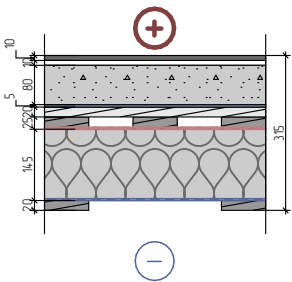

- Керамогранит 10мм
- Клей 10мм
- Цементно-песчаная стяжка 80мм (*с устройством водяного теплого пола - по ар. сетке ячейкой 150х150мм)
- Пенофол фольгированный 5мм
- Фанера 18мм
- Вентбрусок (шаг 200мм) 25мм
- Пароизоляционная мембрана -
- Лага перекрытия (утепленная 150мм) 145мм
- Гидроветрозащитная мембрана -
- Просечка (сетка, ячейка 5х5мм) -
- Обрешетка (шаг 400мм) 25мм
- Нижняя обвязка - 3 сращенная доска 150мм

Согласовано				
Инв. № подл.	Подп. и дата	Взам. инв. №		

Лист	Изм.	№ Докум.	Подп.	Дата	Пироги пола	#Название Организации	Лист
							8


1:80



Пироги пола																													
№ разреза		Сечение		Состав																									
а-а				<table><tr><td>-Фиброцементный сайдинг</td><td>20мм</td></tr><tr><td>-Вентбрусок (вертикально)</td><td>50мм</td></tr><tr><td>-Гидро-ветрозащитная мембрана</td><td>-</td></tr><tr><td>-Стойка каркаса (утепленная)</td><td>145мм</td></tr><tr><td>-Пароизоляционная мембрана (алюм. фольга)</td><td>-</td></tr><tr><td>-Вентбрусок (вертикально)</td><td>50мм</td></tr><tr><td>-Вагонка</td><td>20мм</td></tr></table>						-Фиброцементный сайдинг	20мм	-Вентбрусок (вертикально)	50мм	-Гидро-ветрозащитная мембрана	-	-Стойка каркаса (утепленная)	145мм	-Пароизоляционная мембрана (алюм. фольга)	-	-Вентбрусок (вертикально)	50мм	-Вагонка	20мм						
-Фиброцементный сайдинг	20мм																												
-Вентбрусок (вертикально)	50мм																												
-Гидро-ветрозащитная мембрана	-																												
-Стойка каркаса (утепленная)	145мм																												
-Пароизоляционная мембрана (алюм. фольга)	-																												
-Вентбрусок (вертикально)	50мм																												
-Вагонка	20мм																												
б-б				<table><tr><td>-Фиброцементный сайдинг</td><td>20мм</td></tr><tr><td>-Вентбрусок (вертикально)</td><td>50мм</td></tr><tr><td>-Гидро-ветрозащитная мембрана</td><td>-</td></tr><tr><td>-Стойка каркаса (утепленная)</td><td>145мм</td></tr><tr><td>-Пароизоляционная мембрана</td><td>-</td></tr><tr><td>-Вентбрусок (вертикально)</td><td>50мм</td></tr><tr><td>-ОСБ</td><td>9мм</td></tr><tr><td>-Руспанель</td><td>6мм</td></tr><tr><td>-Клей</td><td>10мм</td></tr><tr><td>-Керамогранит</td><td>10мм</td></tr></table>						-Фиброцементный сайдинг	20мм	-Вентбрусок (вертикально)	50мм	-Гидро-ветрозащитная мембрана	-	-Стойка каркаса (утепленная)	145мм	-Пароизоляционная мембрана	-	-Вентбрусок (вертикально)	50мм	-ОСБ	9мм	-Руспанель	6мм	-Клей	10мм	-Керамогранит	10мм
-Фиброцементный сайдинг	20мм																												
-Вентбрусок (вертикально)	50мм																												
-Гидро-ветрозащитная мембрана	-																												
-Стойка каркаса (утепленная)	145мм																												
-Пароизоляционная мембрана	-																												
-Вентбрусок (вертикально)	50мм																												
-ОСБ	9мм																												
-Руспанель	6мм																												
-Клей	10мм																												
-Керамогранит	10мм																												
в-в				<table><tr><td>-Вагонка</td><td>20мм</td></tr><tr><td>-Вентбрусок (вертикально)</td><td>50мм</td></tr><tr><td>-Пароизоляционная мембрана (алюм. фольга)</td><td>-</td></tr><tr><td>-Стойка каркаса (утепленная)</td><td>145мм</td></tr><tr><td>-Пароизоляционная мембрана</td><td>-</td></tr><tr><td>-Вентбрусок (вертикально)</td><td>50мм</td></tr><tr><td>-Имитация бруса</td><td>20мм</td></tr></table>						-Вагонка	20мм	-Вентбрусок (вертикально)	50мм	-Пароизоляционная мембрана (алюм. фольга)	-	-Стойка каркаса (утепленная)	145мм	-Пароизоляционная мембрана	-	-Вентбрусок (вертикально)	50мм	-Имитация бруса	20мм						
-Вагонка	20мм																												
-Вентбрусок (вертикально)	50мм																												
-Пароизоляционная мембрана (алюм. фольга)	-																												
-Стойка каркаса (утепленная)	145мм																												
-Пароизоляционная мембрана	-																												
-Вентбрусок (вертикально)	50мм																												
-Имитация бруса	20мм																												
г-г				<table><tr><td>-Планкен</td><td>20мм</td></tr><tr><td>-Вентбрусок (горизонтально)</td><td>50мм</td></tr><tr><td>-Гидро-ветрозащитная мембрана</td><td>-</td></tr><tr><td>-Стойка каркаса (утепленная)</td><td>145мм</td></tr><tr><td>-Пароизоляционная мембрана</td><td>-</td></tr><tr><td>-Вентбрусок (вертикально)</td><td>50мм</td></tr><tr><td>-Имитация бруса</td><td>20мм</td></tr></table>						-Планкен	20мм	-Вентбрусок (горизонтально)	50мм	-Гидро-ветрозащитная мембрана	-	-Стойка каркаса (утепленная)	145мм	-Пароизоляционная мембрана	-	-Вентбрусок (вертикально)	50мм	-Имитация бруса	20мм						
-Планкен	20мм																												
-Вентбрусок (горизонтально)	50мм																												
-Гидро-ветрозащитная мембрана	-																												
-Стойка каркаса (утепленная)	145мм																												
-Пароизоляционная мембрана	-																												
-Вентбрусок (вертикально)	50мм																												
-Имитация бруса	20мм																												
Согласовано																													
Ив. № подл.		Подп. и дата		Взам. инв. №																									
Лист		Изм.		№ Докум.		Подп.		Дата		Пироги стены		#Название Организации		Лист															
														10															

План размещения розеток

1:80

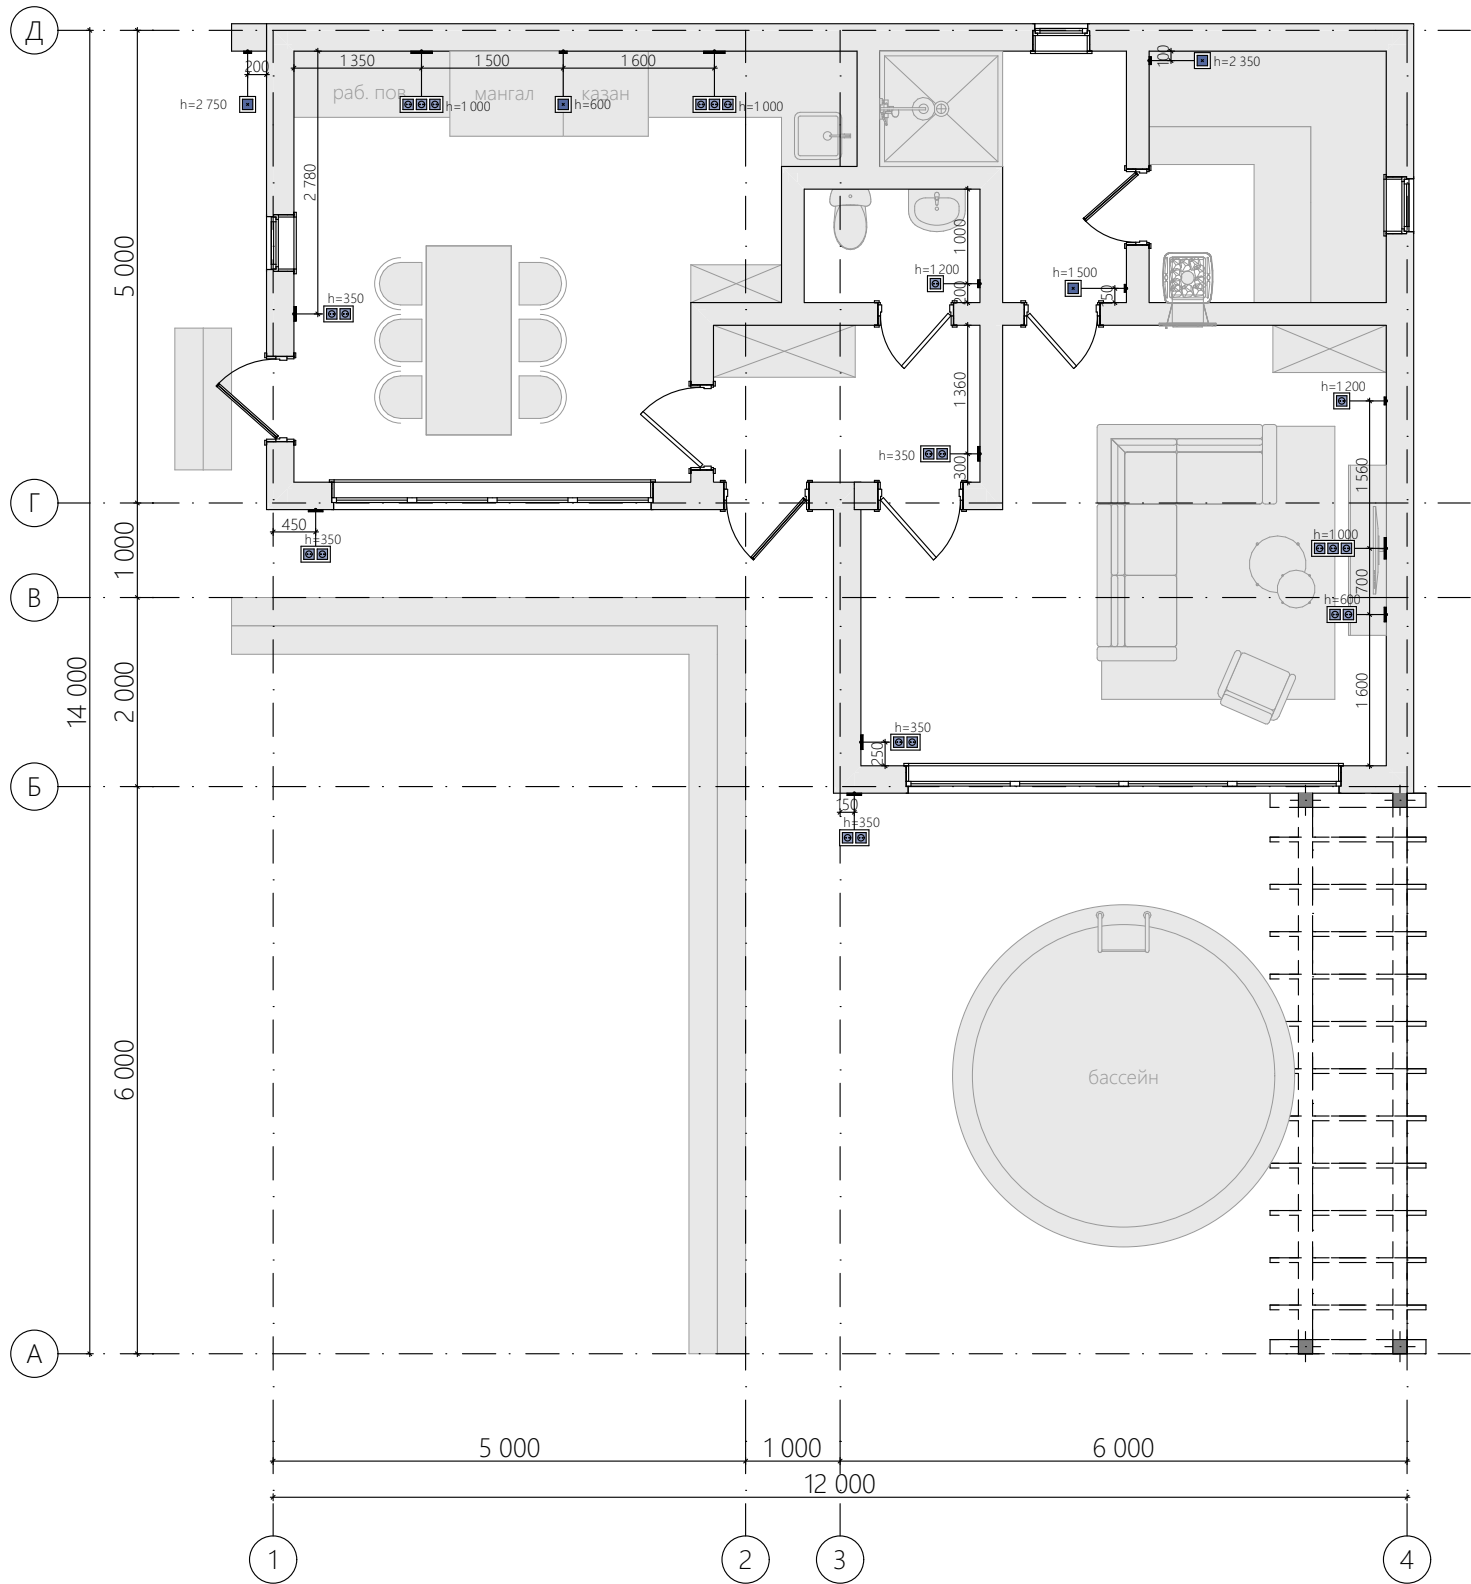

Экспликация розеток

Наименование	2д-вид	Кол-во
Розетка 220v (1 секции)		2
Розетка 220v (2 секции)		6
Розетка 220v (3 секции)		3
Эл. вывод (влагозащитная)		4
		15

Примечание:


1. Схема размещения розеток является рекомендательной и требует согласования с заказчиком по месту.
2. Все высоты даны от чистового пола.
3. Все указанные размеры даются до центра позиций.
4. Отметки розеток, выключателей, выводов и др. оборудования, являются предварительными и уточняются после выбора финишных материалов и мебели.
5. Размеры уточняются дополнительно

Согласовано				
Взам. инв. №				
Подп. и дата				
Инв. № подл.				

Лист	Изм.	№ Докум.	Подп.	Дата

План размещения светильников и выключателей

1:80

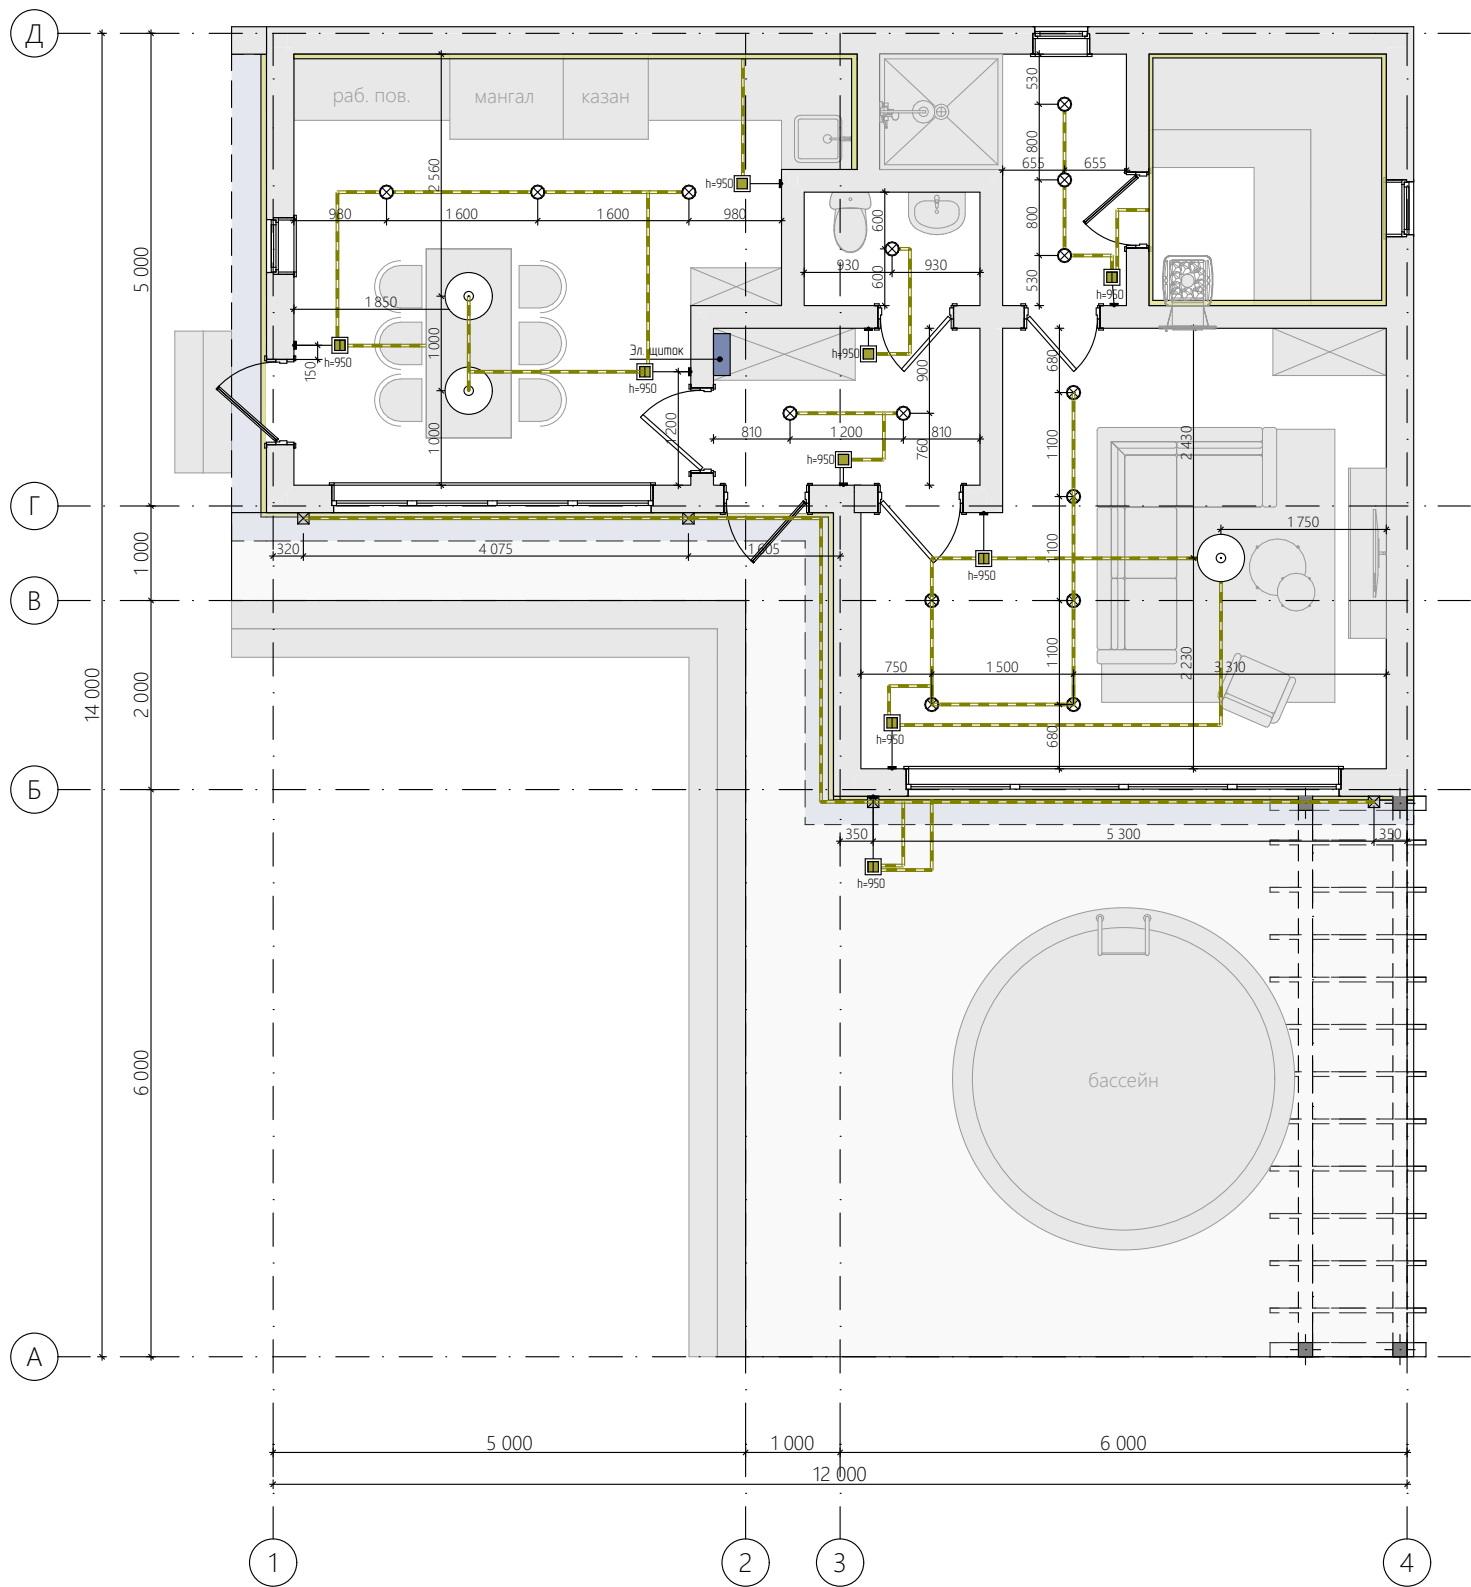

Экспликация светильников и выключателей

Наименование	2д-вид	Кол-во
Выключатель одноклавишный (1 секция)		3
Выключатель одноклавишный (2 секции)		6
Светильник подвесной		3
Точечный светильник		15
Уличный светильник		4
		31

Примечание:

1. Схема размещения розеток является рекомендательной и требует согласования с заказчиком по месту.
2. Все высоты даны от чистового пола.
3. Все указанные размеры даются до центра позиций.
4. Отметки розеток, выключателей, выводов и др. оборудования, являются предварительными и уточняются после выбора финишных материалов и мебели.
5. Размеры уточняются дополнительно

Согласовано

Взам. инв. №

Подп. и дата

Инв. № подл.

Лист	Изм.	№ Докум.	Подп.	Дата

План размещения светильников и выключателей

#Название Организации


План стоек каркаса

1:80

Условные обозначения:

 -Контур теплого пола

Площадь теплого пола (S, м²) = 38,32м²

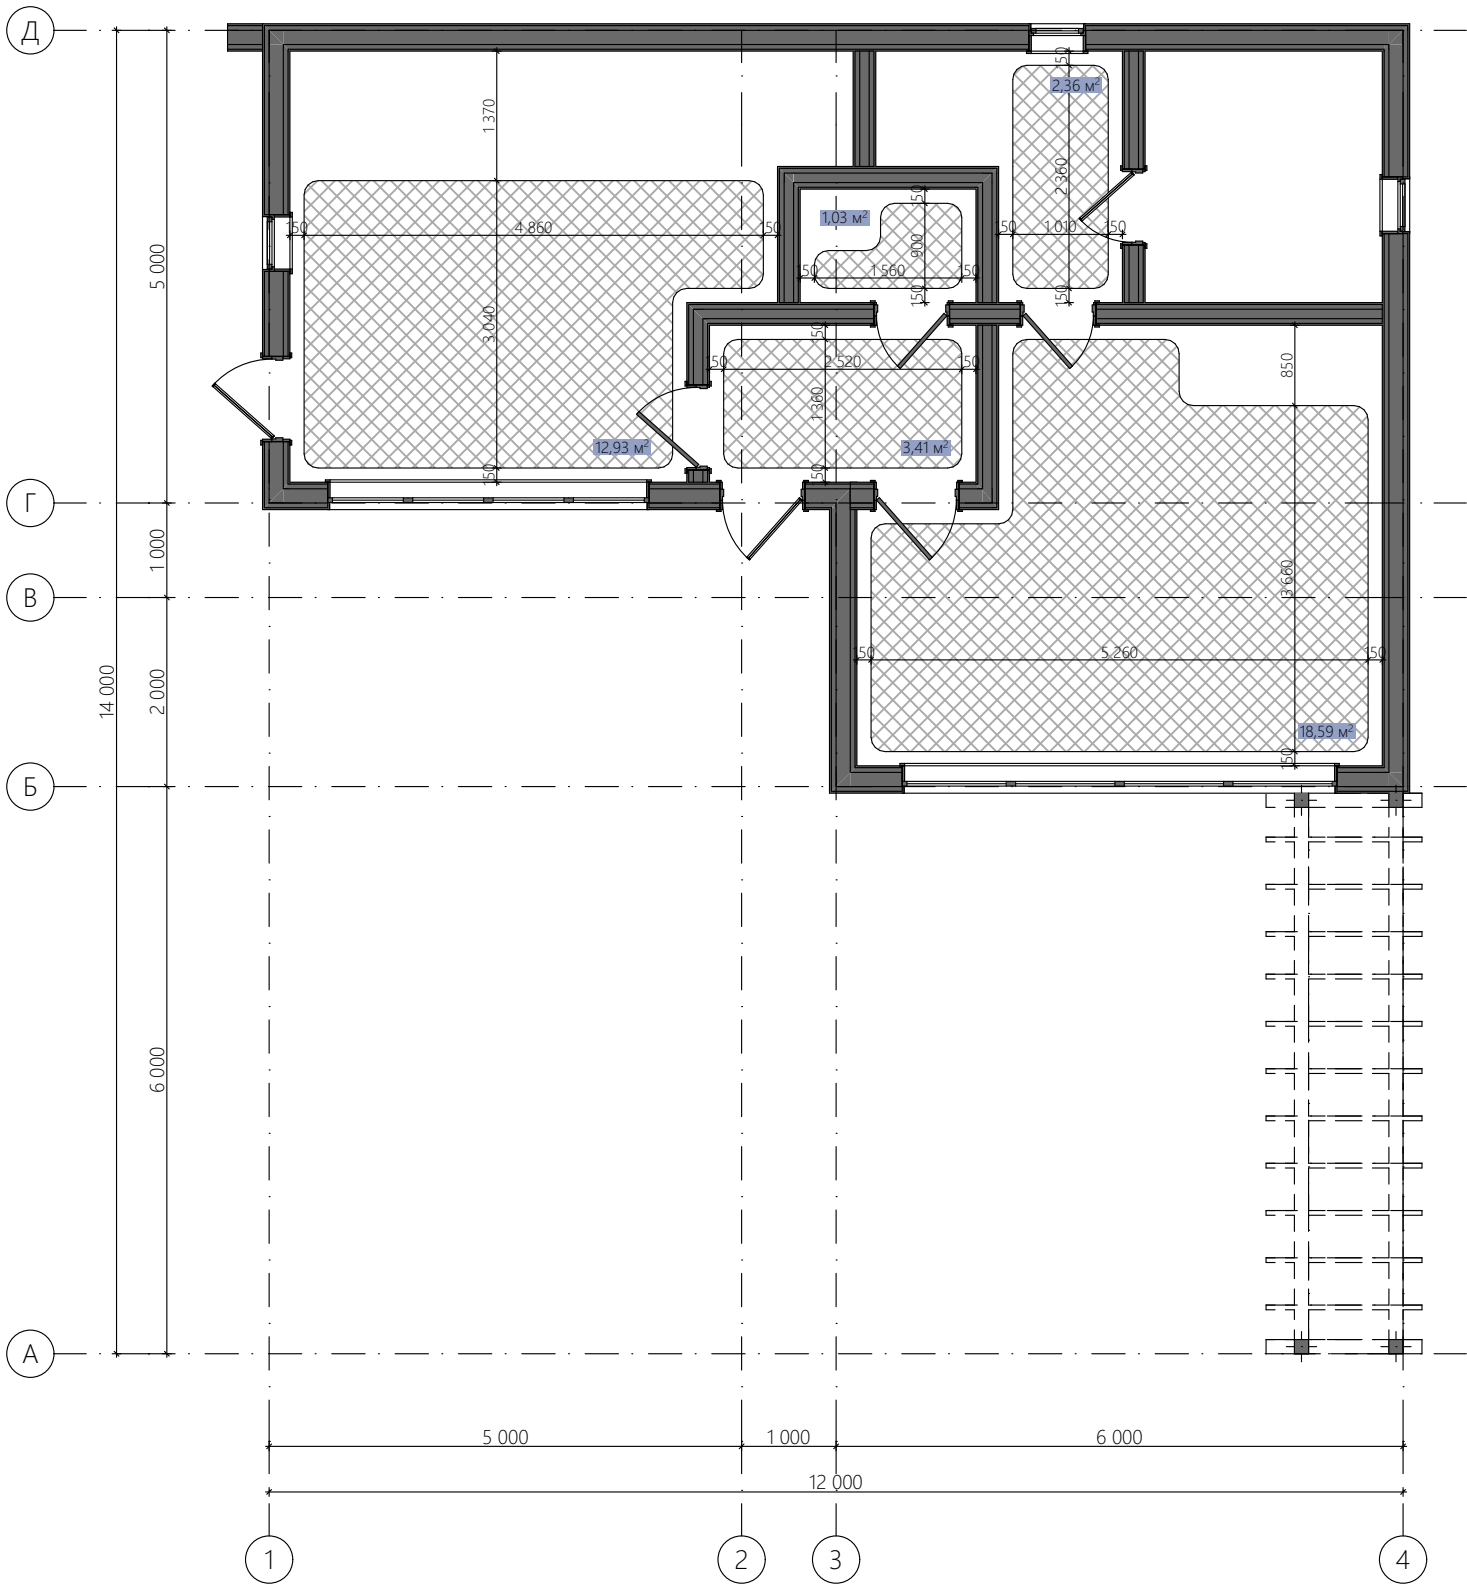

Согласовано				
И-нв. № подл.	Подп. и дата	Взам. инв. №		

Лист	Изм.	№ Докум.	Подп.	Дата

План теплого пола

#Название Организации


План крыши

1:80


Условные обозначения:

- Крыша (уклон 3°)
- Подшив свесов

Площадь крыши (S, м²) = 90,93м²

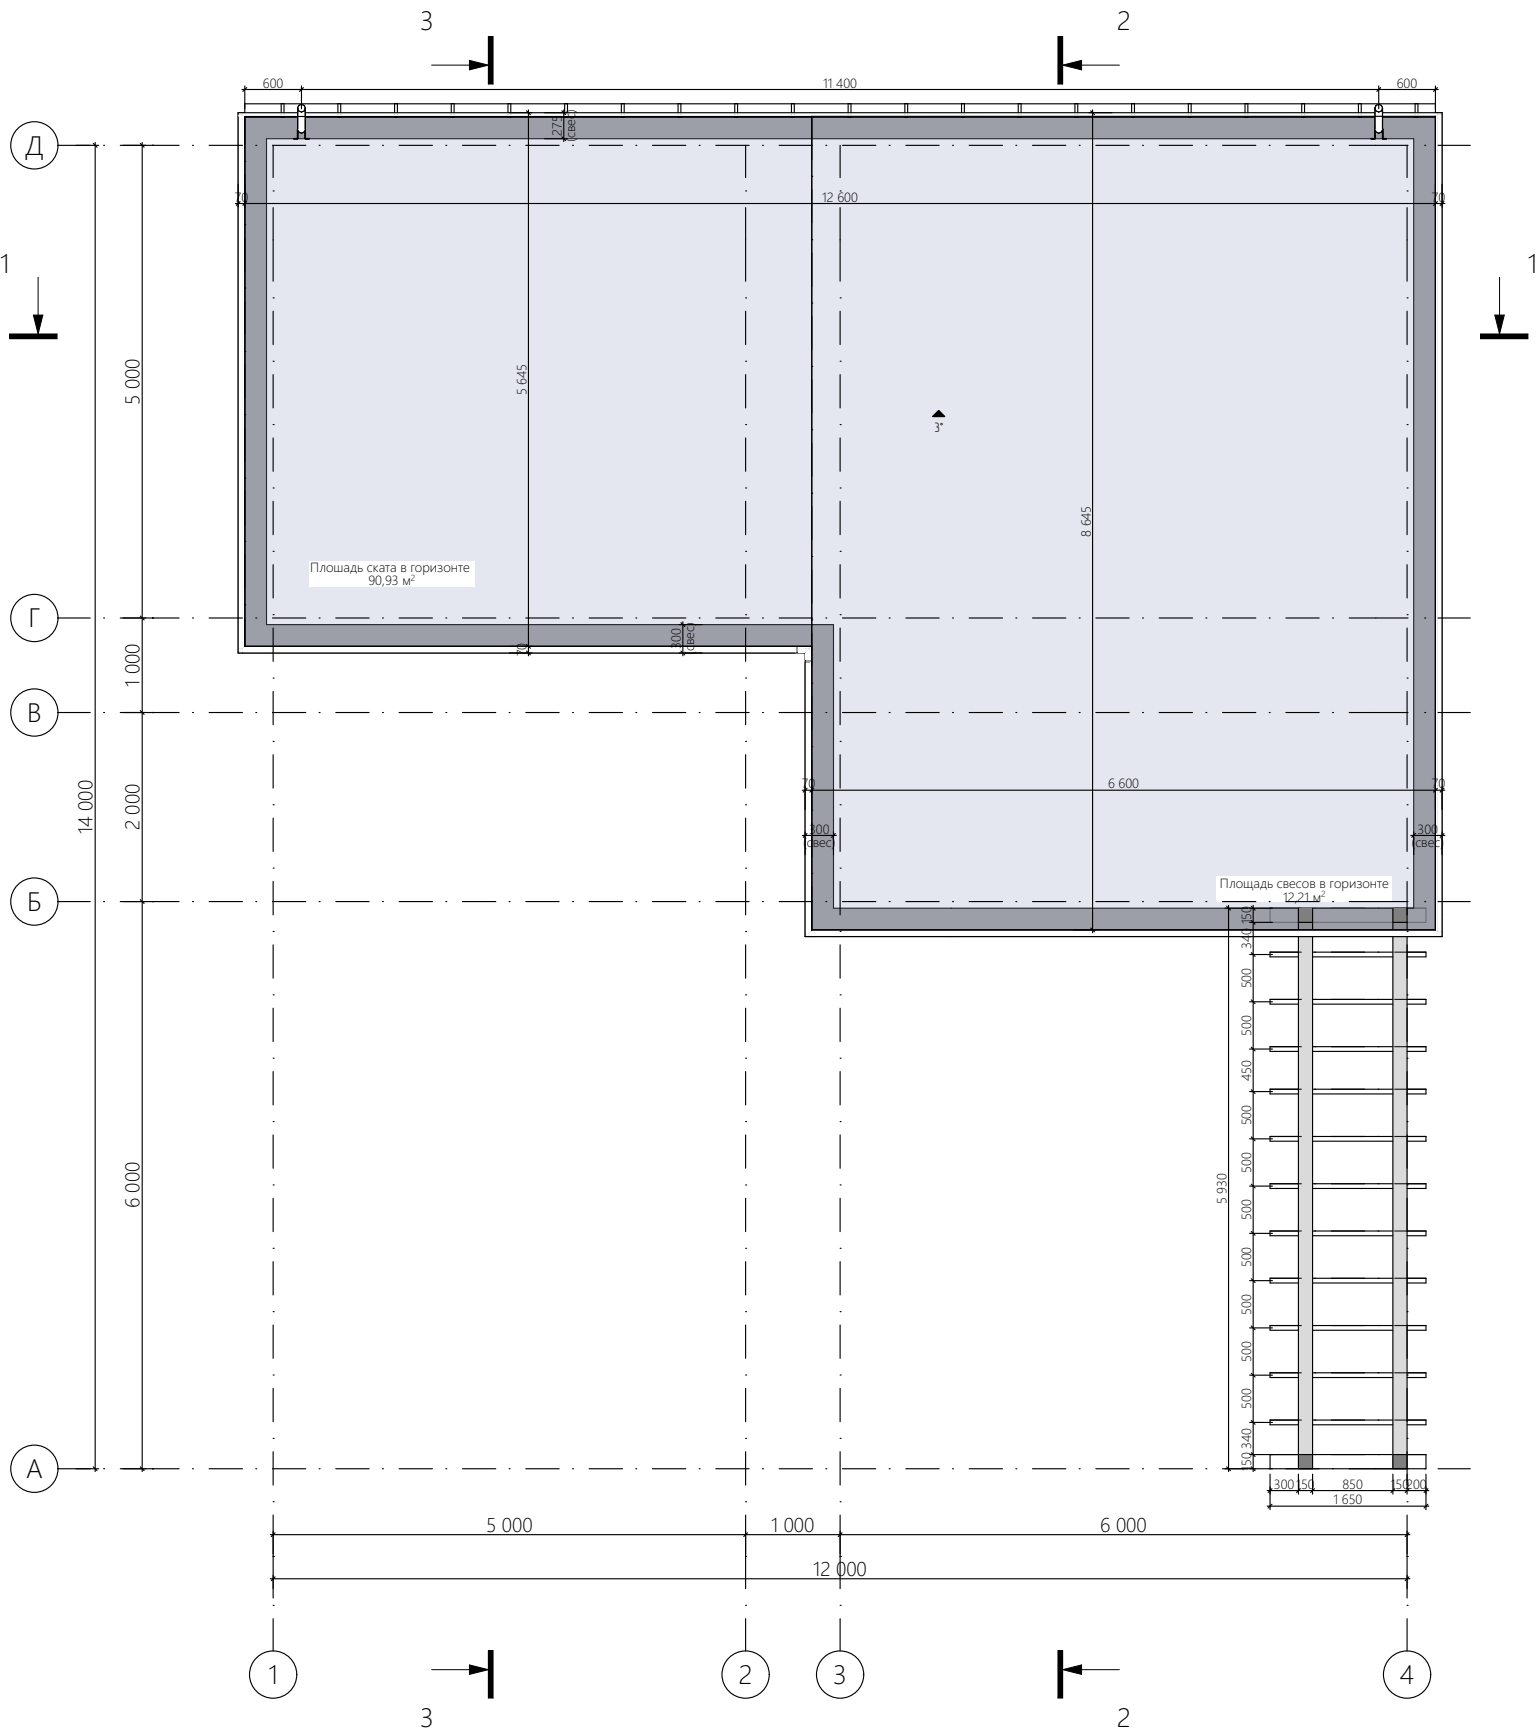

Аксонометрия крыши

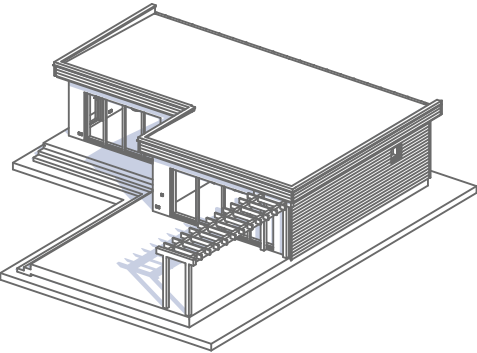

Согласовано				
И-нв. № подл.	Подп. и дата	Взам. инв. №		



Лист	Изм.	№ Докум.	Подп.	Дата

План крыши

#Название Организации

Ведомость оконных проемов

1:1

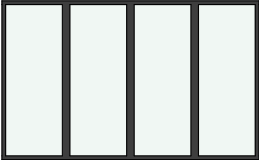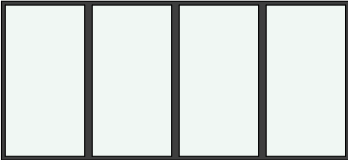Наименование	Размеры проема Ш х В, мм	Кол-во	Вид	Площадь, м2
ОК1	600×600	3		0,36
ОК2	3 400×2 100	1		7,14
ОК3	4 600×2 100	1		9,66

17,88 м²

Согласовано				





Инв. № подл.	Подп. и дата	Взам. инв. №	

Примечание:

- 1. Изготовление окон и дверей определяется заказчиком, допускается изменение открывания окон и дверей;
- 2. При заказе оконных и дверных блоков необходим обмер по месту от изготовителя;
- 3. Оконные и дверные изделия изображены со стороны открывания.

Лист	Изм.	№ Докум.	Подп.	Дата	Ведомость заполнения оконных проемов	#Название Организации


1:1

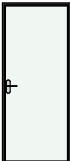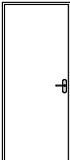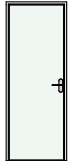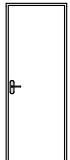Д1	900×2 100	2		1,89
Д2	900×2 100	2		1,89
Д3	800×2 100	1		1,68
Д4	800×2 100	2		1,68

12,60 m²

1. Изготовление окон и дверей определяется заказчиком, допускается изменение открывания окон и дверей;
2. При заказе оконных и дверных блоков необходим обмер по месту от изготовителя;
3. Оконные и дверные изделия изображены со стороны открывания.

Лист	Изм.	№ Докум.	Подп.	Дата	Ведомость заполнения дверных проемов	#Название Организации	Лист
							16

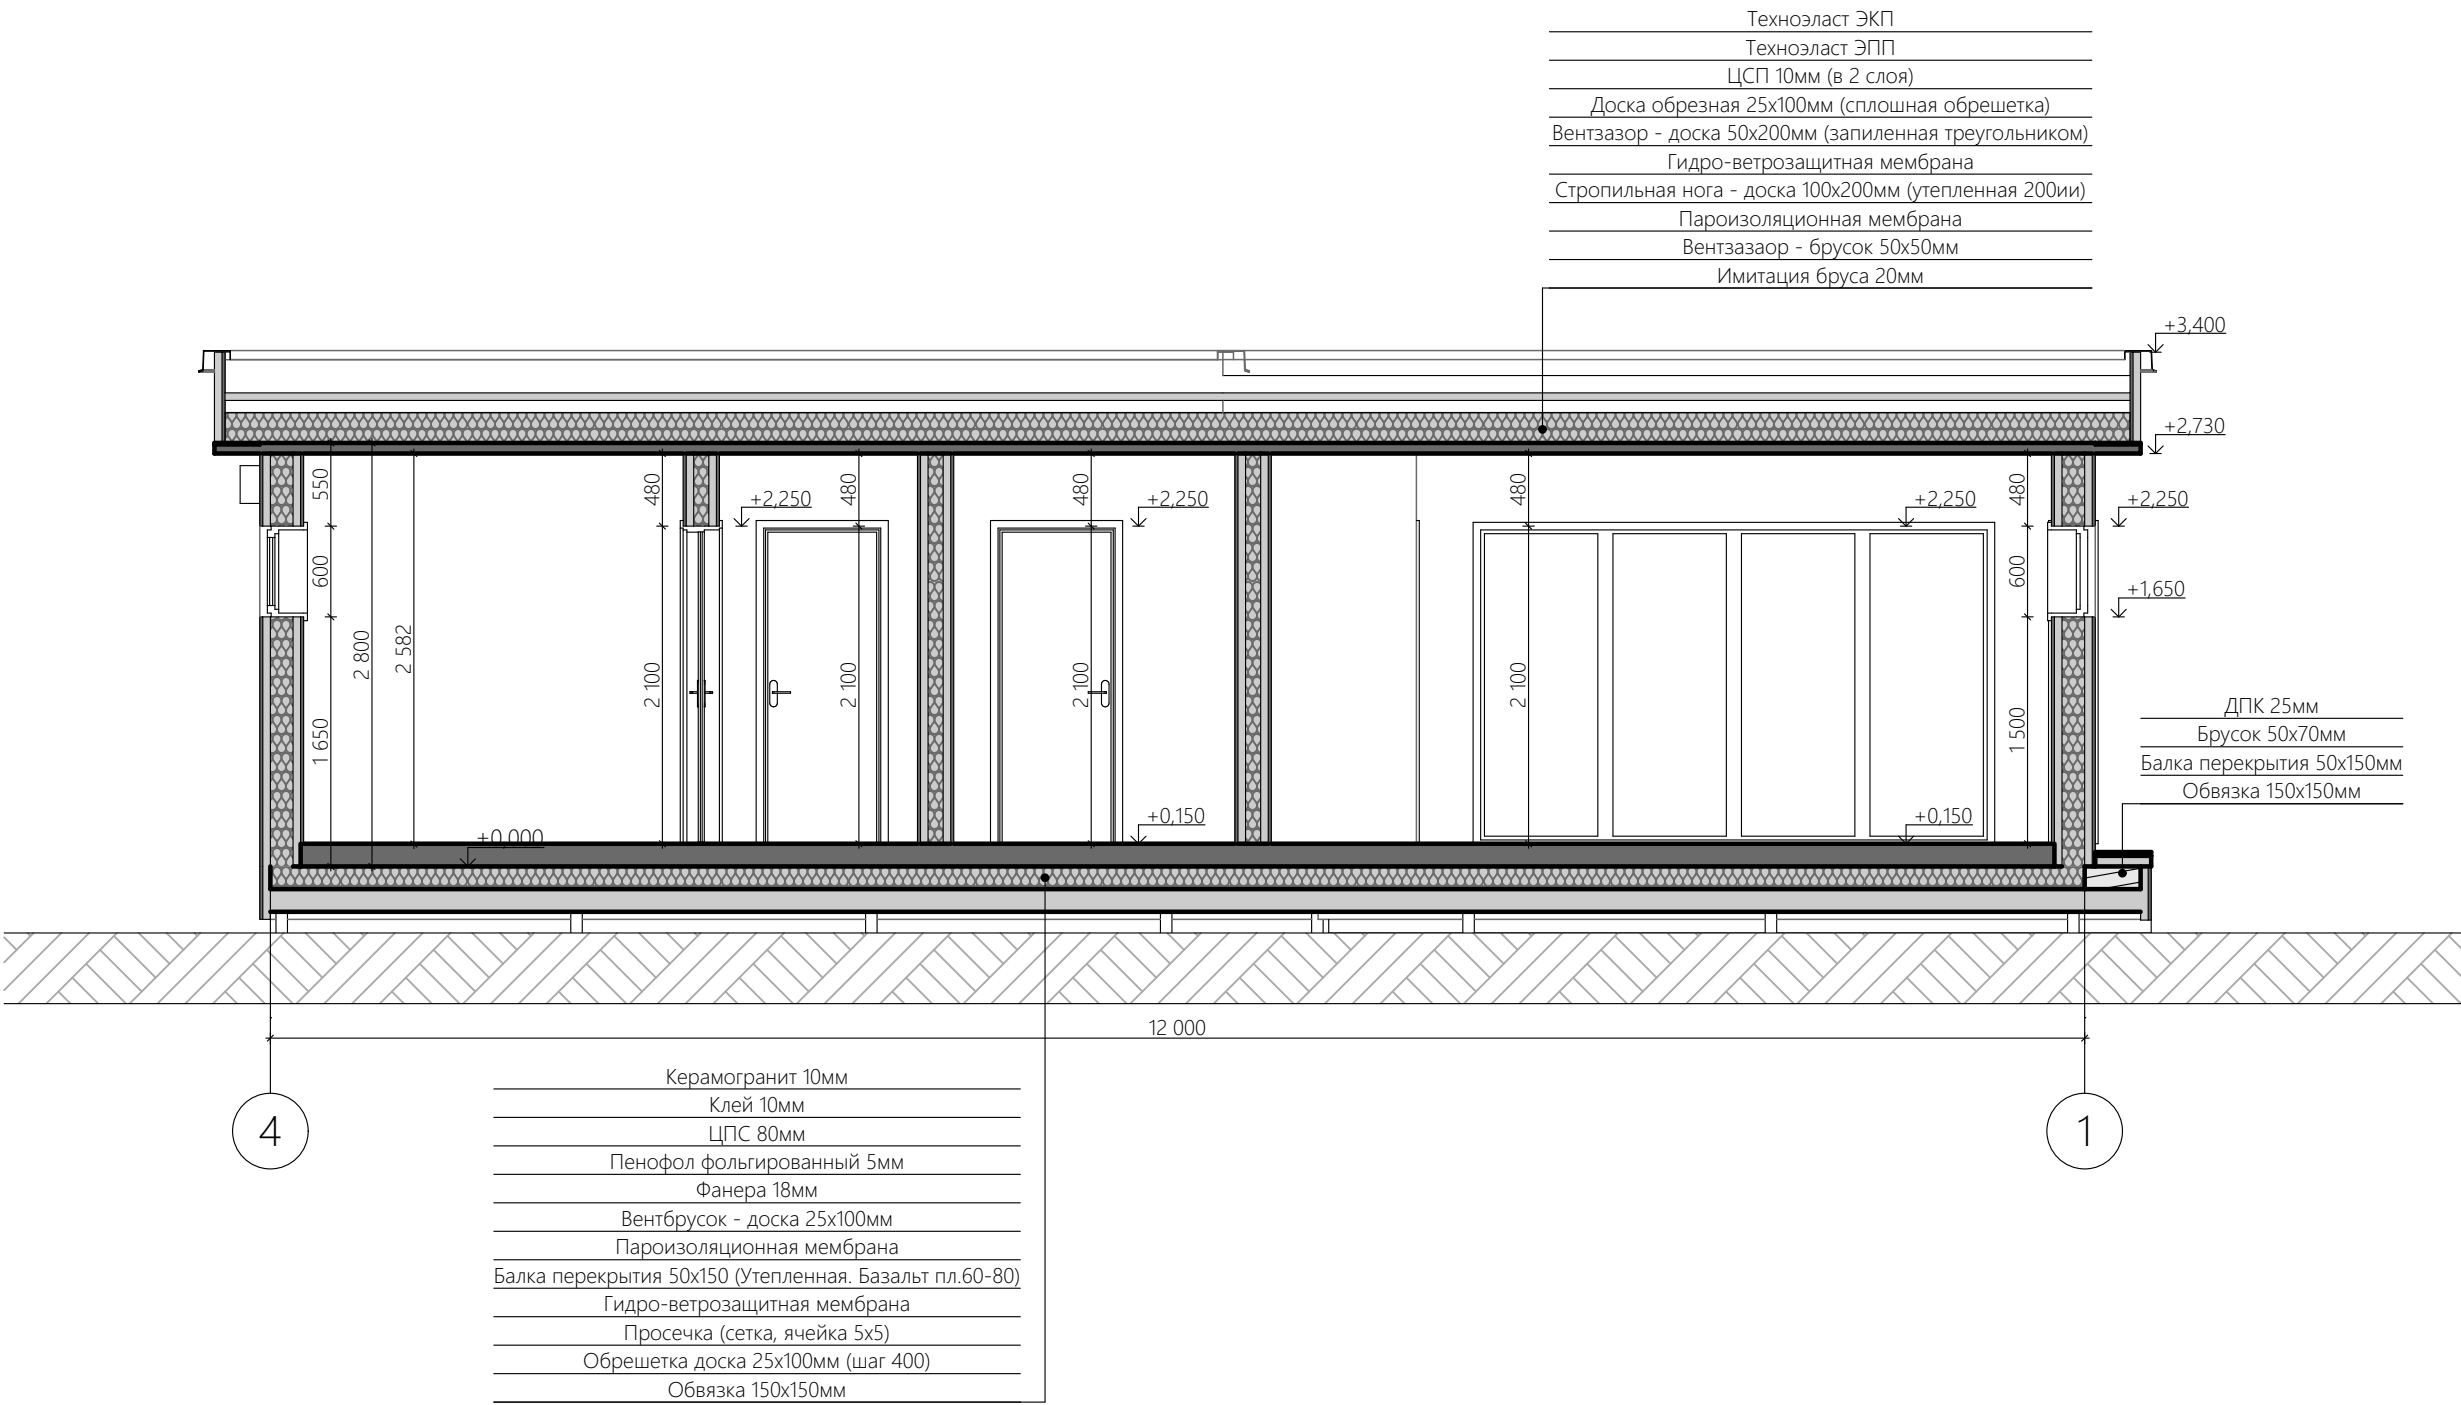

Согласовано				
И/в. № подл.	Взам. инв. №	Подп. и дата		

Лист	Изм.	№ Докум.	Подп.	Дата


Разрез 1-1	

#Название Организации

Лист
17

Разрез 2-2

1:50

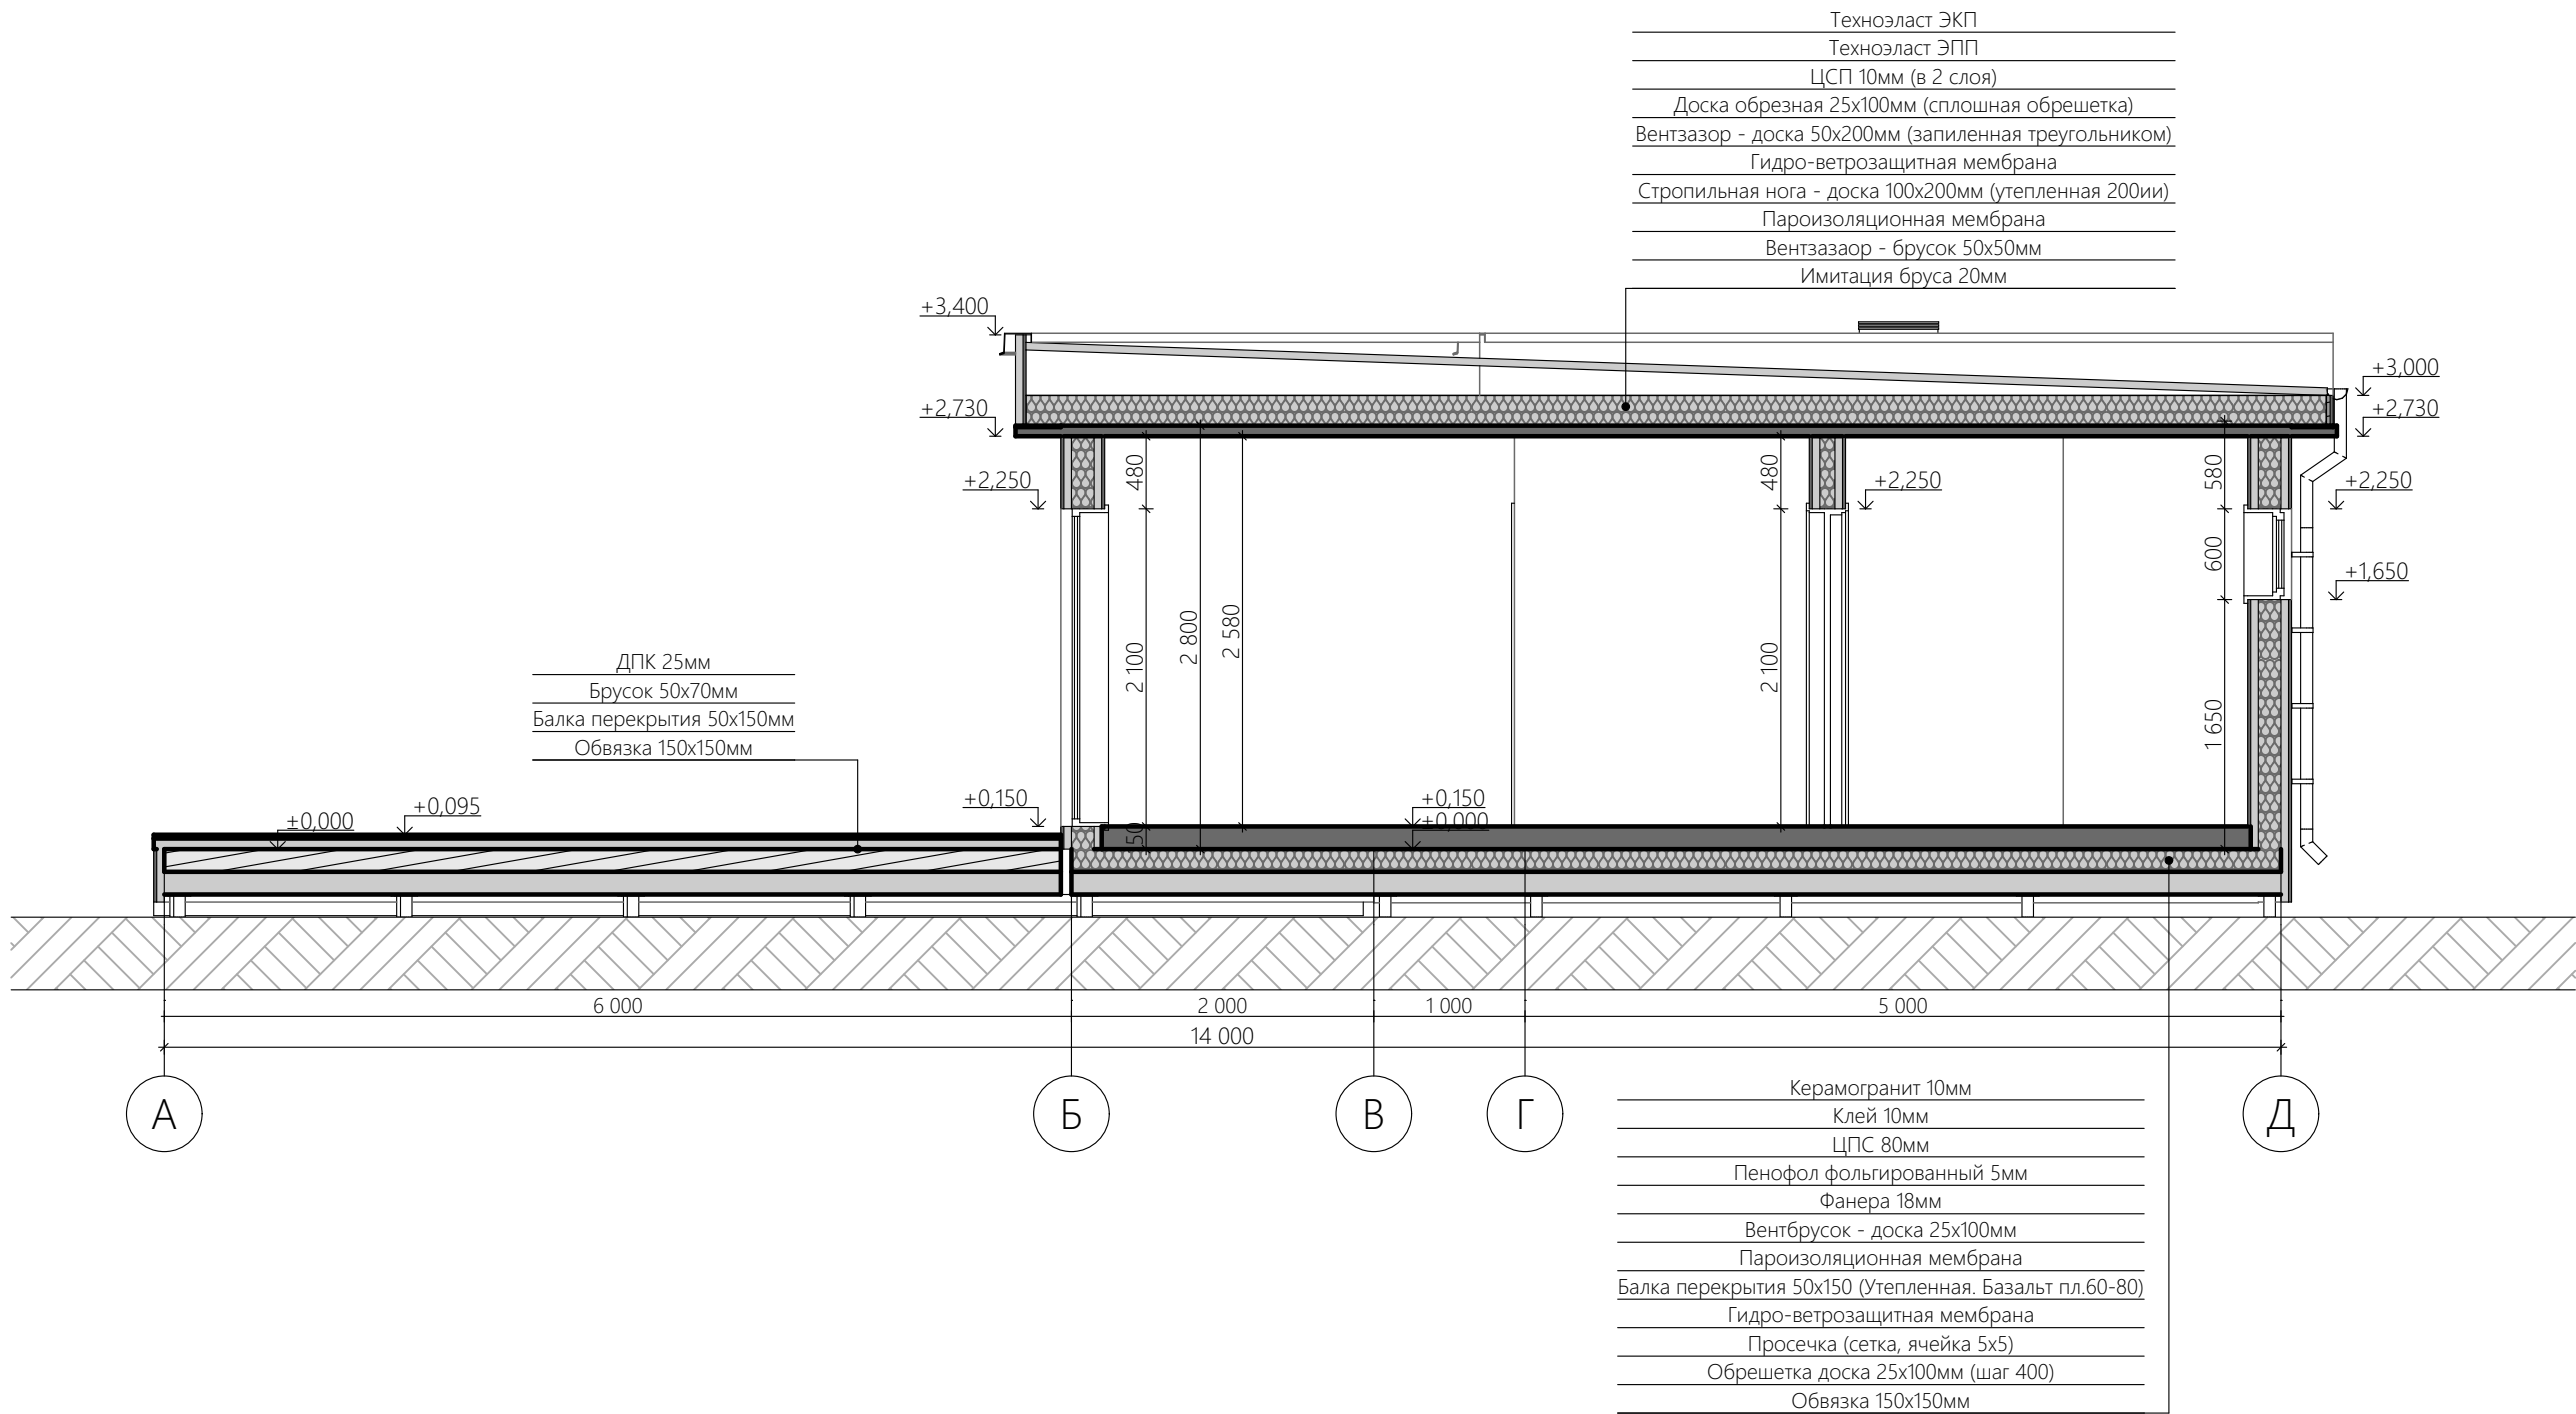

Согласовано

Взам. инв. №

Подп. и дата

Инв. № подл.


Лист	Изм.	№ Докум.	Подп.	Дата

Разрез 2-2

#Название Организации

Разрез 3-3

1:50

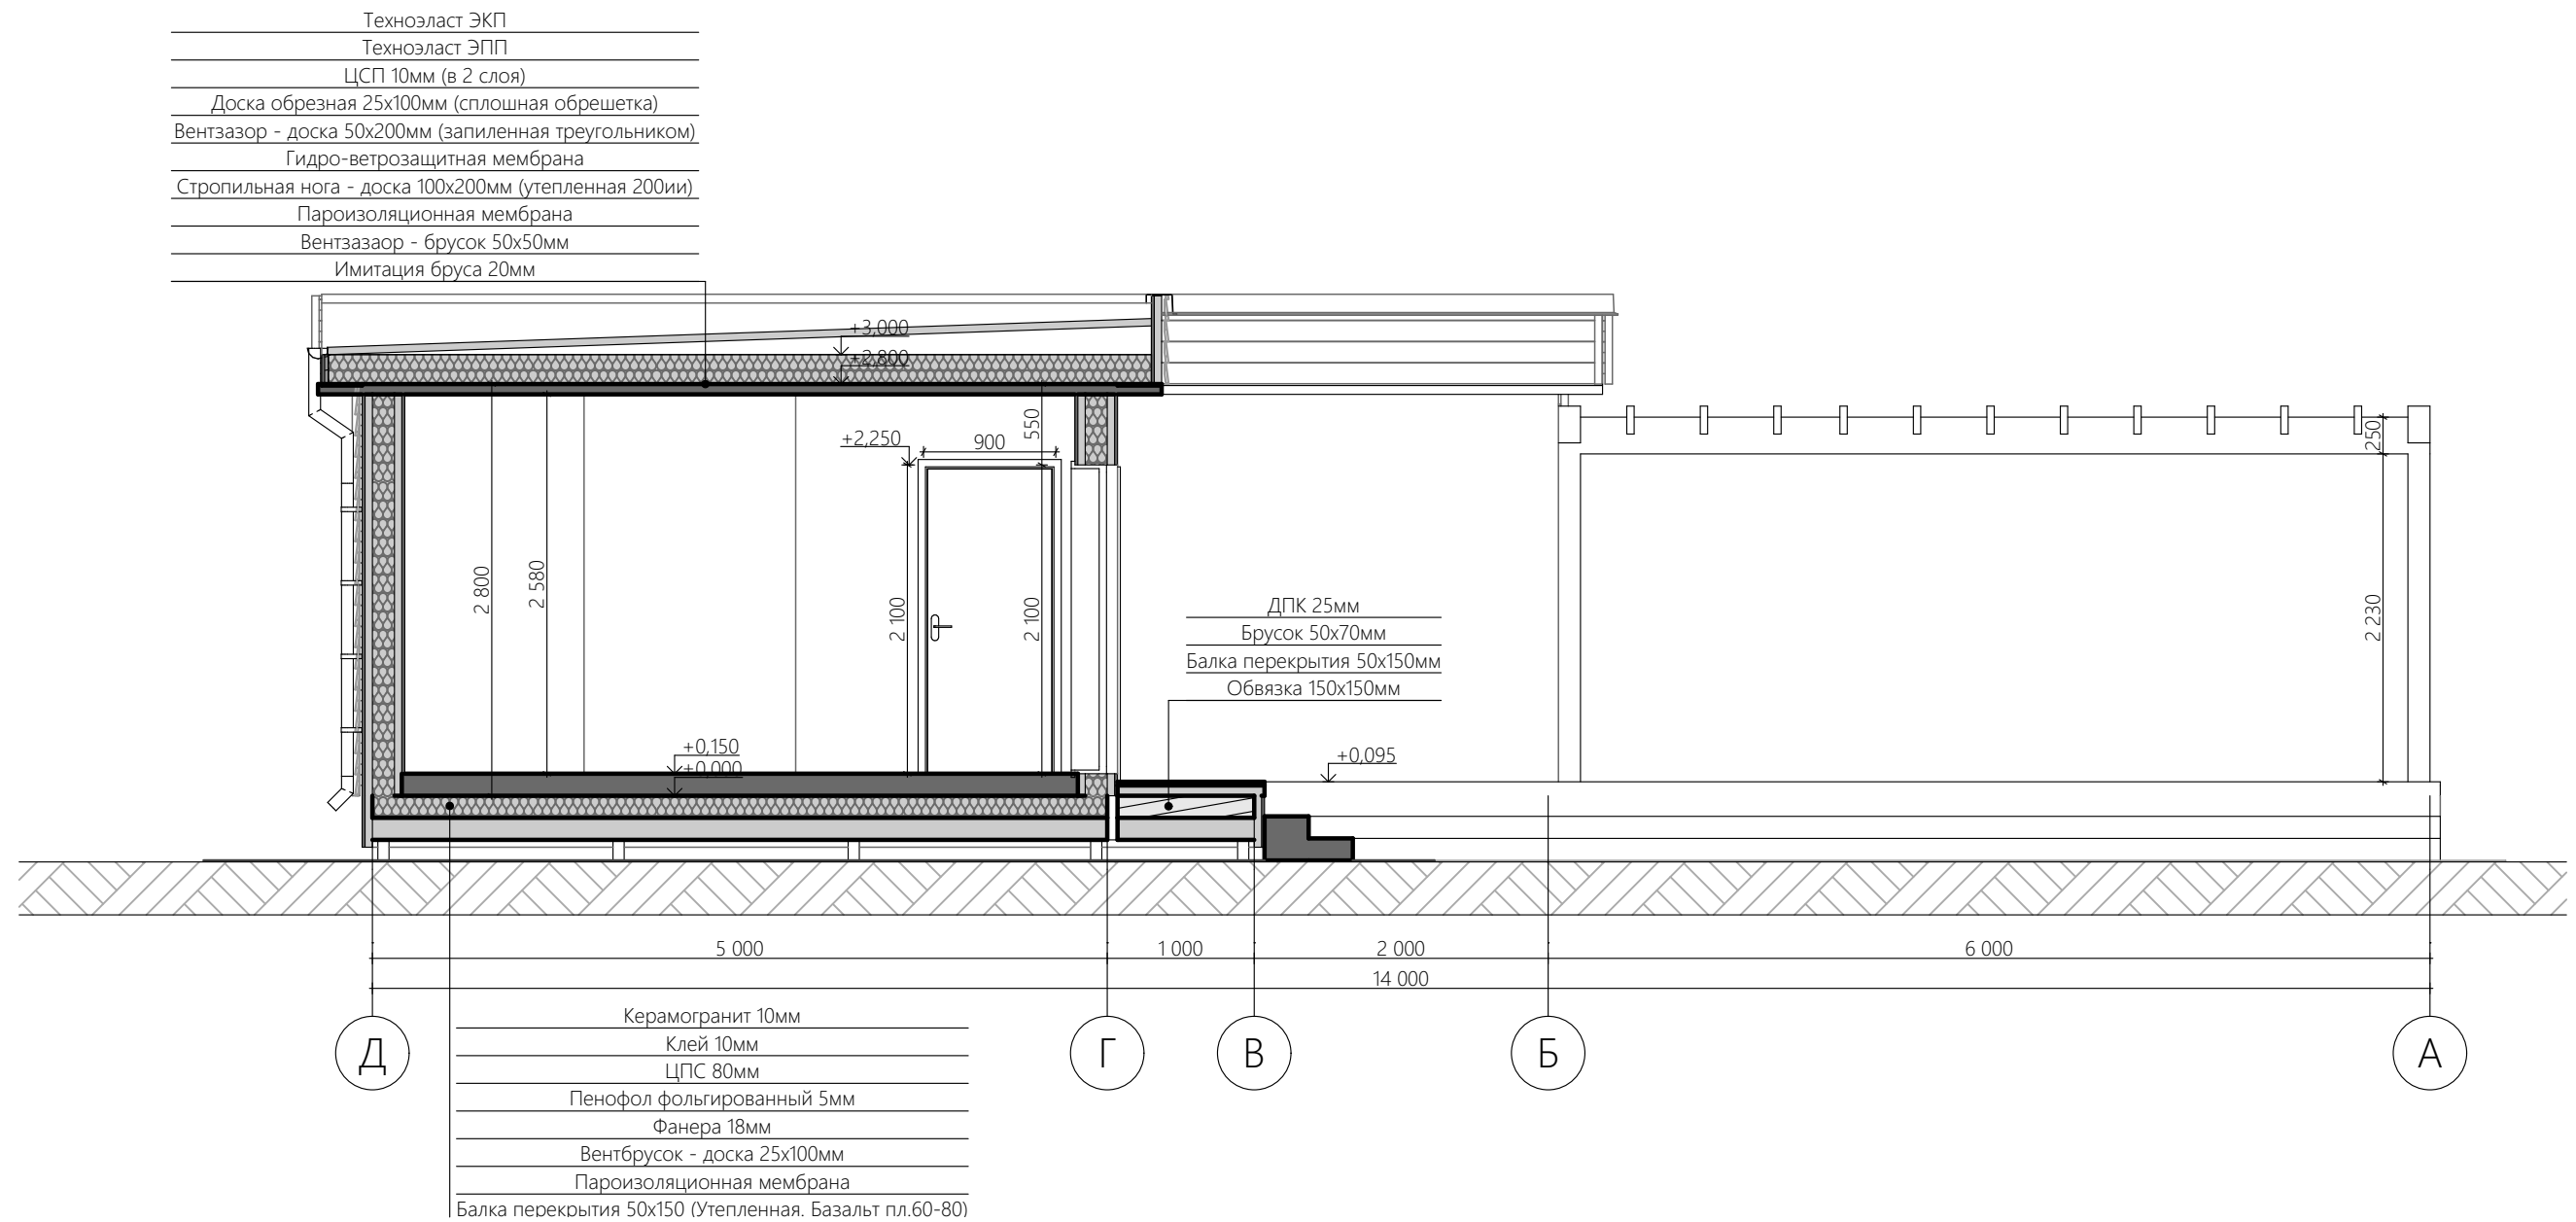

Согласовано

Взам. инв. №

Подп. и дата

ИНВ. № подл.

Лист	Изм.	№ Докум.	Подп.	Дата

Разрез 3-3

#Название Организации

Лист

19

-  -Плакен
-  -Террасная доска (ДПК. ВЕЛЬВЕТ. БРАЙТ. ШАЛЕ СЕРЫЙ)
-  -Водосточная система, наличники, оконные рамы (RAL 7024)
-  -Дерево крашенное
-  -Фиброцементный сайдинг (RAL 7024)



Согласовано				


Инов. № подл.	Взам. инв. №		Подп. и дата	


Лист	Изм.	№ Докум.	Подп.	Дата

Фасад А-Д

1:60

Условные обозначения:

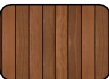-  -Плакен
-  -Террасная доска (ДПК. ВЕЛЬВЕТ. БРАЙТ. ШАЛЕ СЕРЫЙ)
-  -Водосточная система, наличники, оконные рамы (RAL 7024)
-  -Дерево крашенное
-  -Фиброцементный сайдинг (RAL 7024)

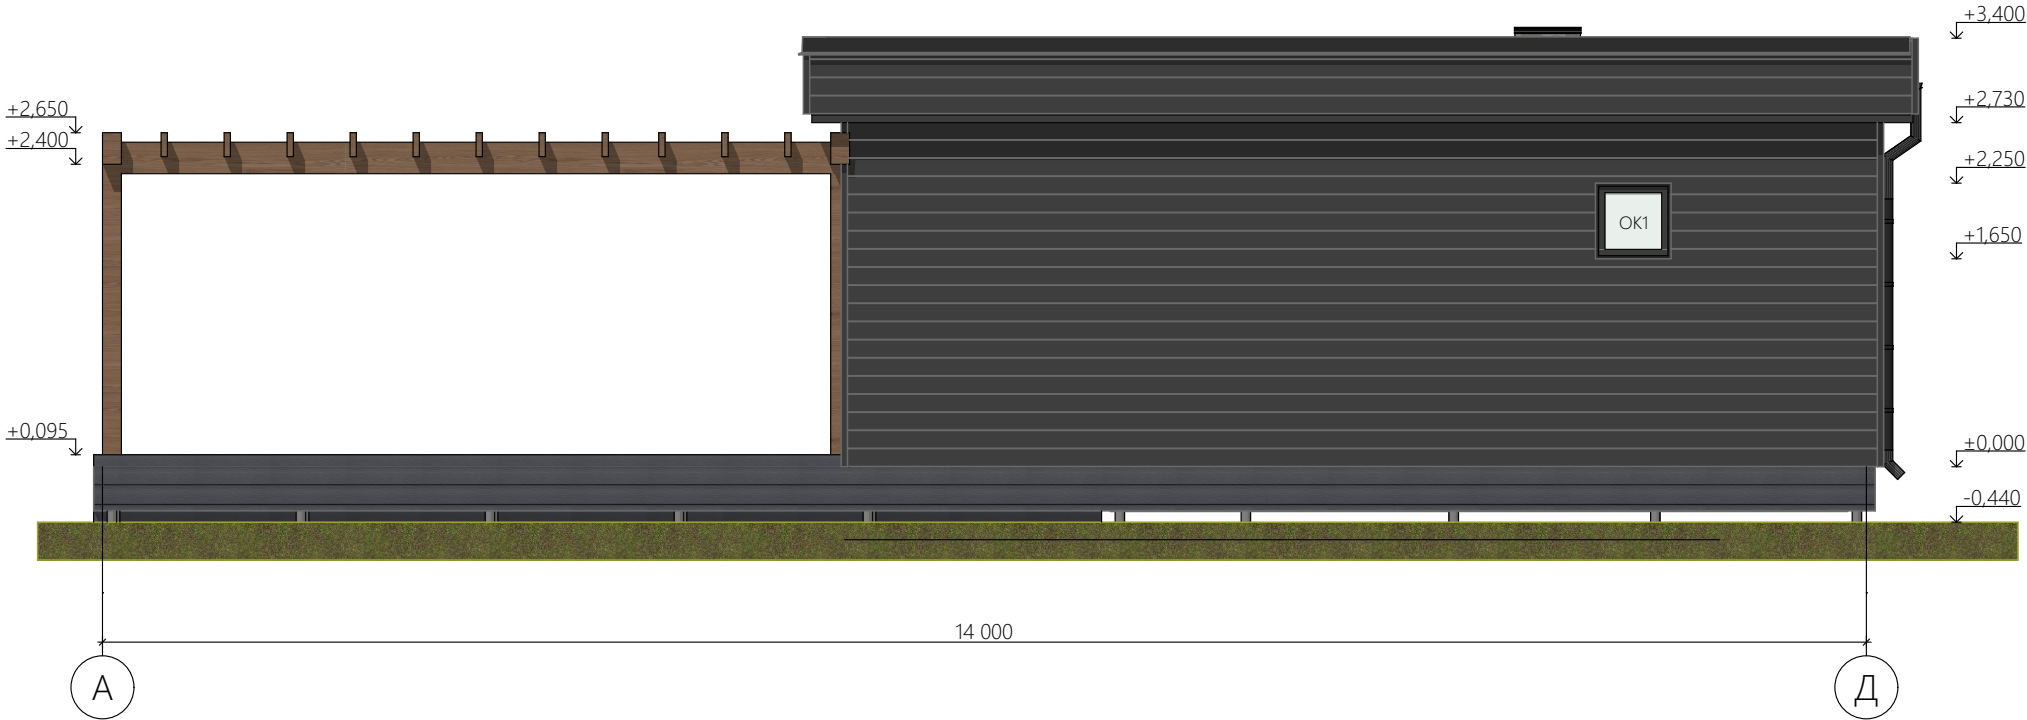

Согласовано				
Инов. № подл.	Подп. и дата	Взам. инв. №		

Лист	Изм.	№ Докум.	Подп.	Дата


--	--	--	--	--

Фасад А-Д

#Название Организации

Лист
21

-  -Плакен
-  -Террасная доска (ДПК. ВЕЛЬВЕТ. БРАЙТ. ШАЛЕ СЕРЫЙ)
-  -Водосточная система, наличники, оконные рамы (RAL 7024)
-  -Дерево крашенное
-  -Фиброцементный сайдинг (RAL 7024)

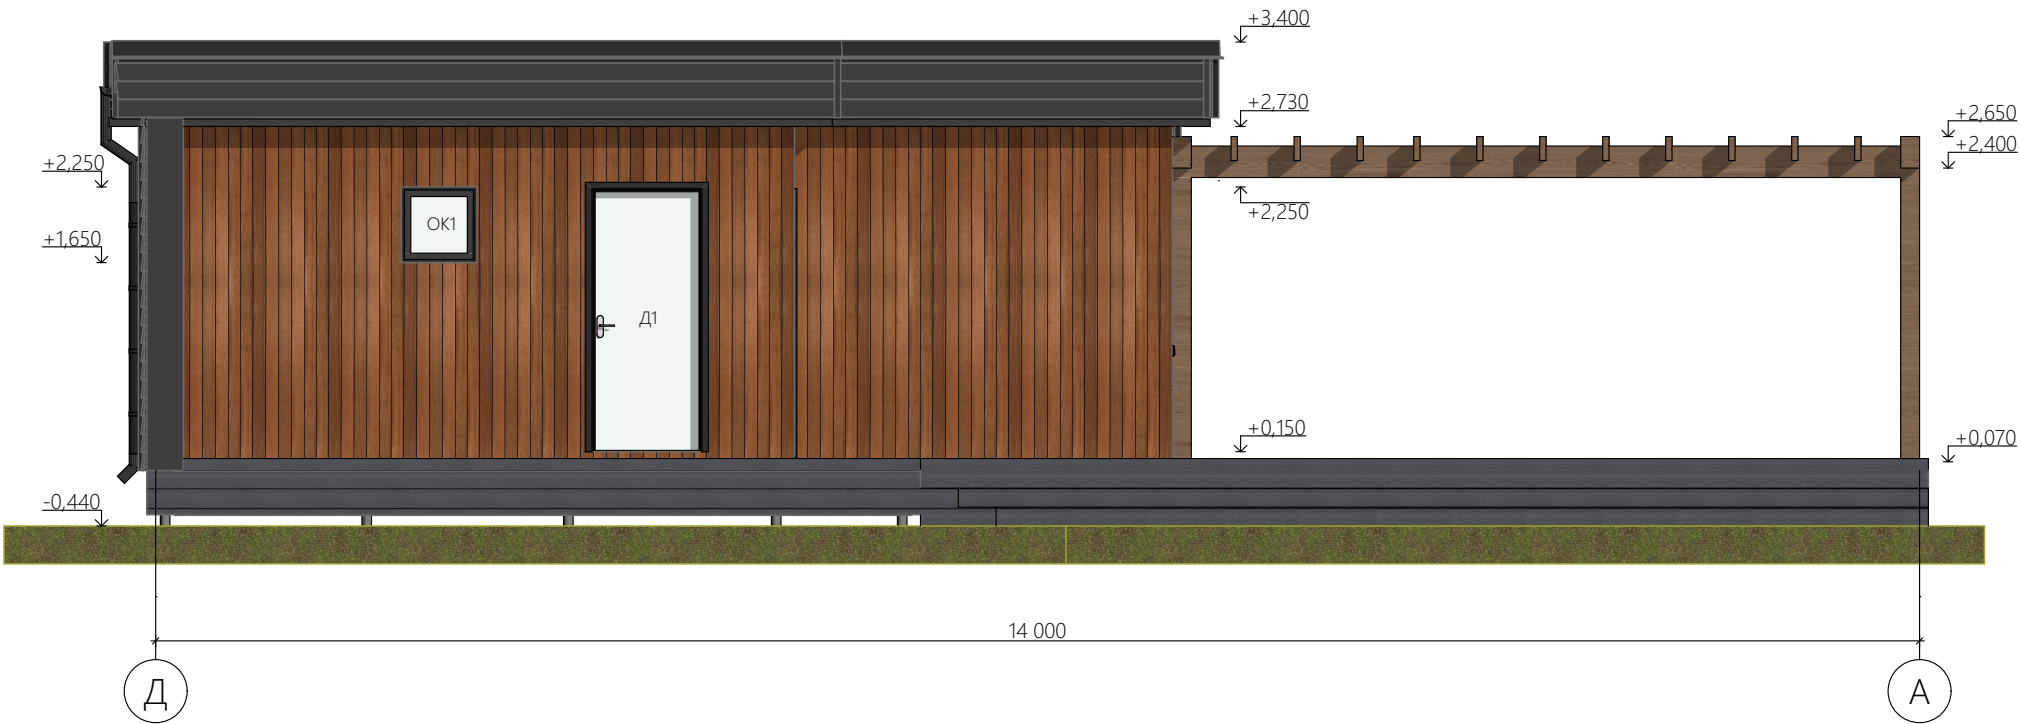

Согласовано			


И-в. № подл.	Подп. и дата	Взам. инв. №	

Лист	Изм.	№ Докум.	Подп.	Дата

Фасад 4-1

1:60

Условные обозначения:

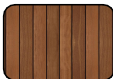-  -Плакен
-  -Террасная доска (ДПК. ВЕЛЬВЕТ. БРАЙТ. ШАЛЕ СЕРЫЙ)
-  -Водосточная система, наличники, оконные рамы (RAL 7024)
-  -Дерево крашенное
-  -Фиброцементный сайдинг (RAL 7024)



Согласовано			

Инов. № подл.	Подп. и дата	Взам. инв. №	


Лист	Изм.	№ Докум.	Подп.	Дата

Фасад 4-1

#Название Организации

Согласовано

Инов. № подл.	Подп. и дата	Взам. инв. №

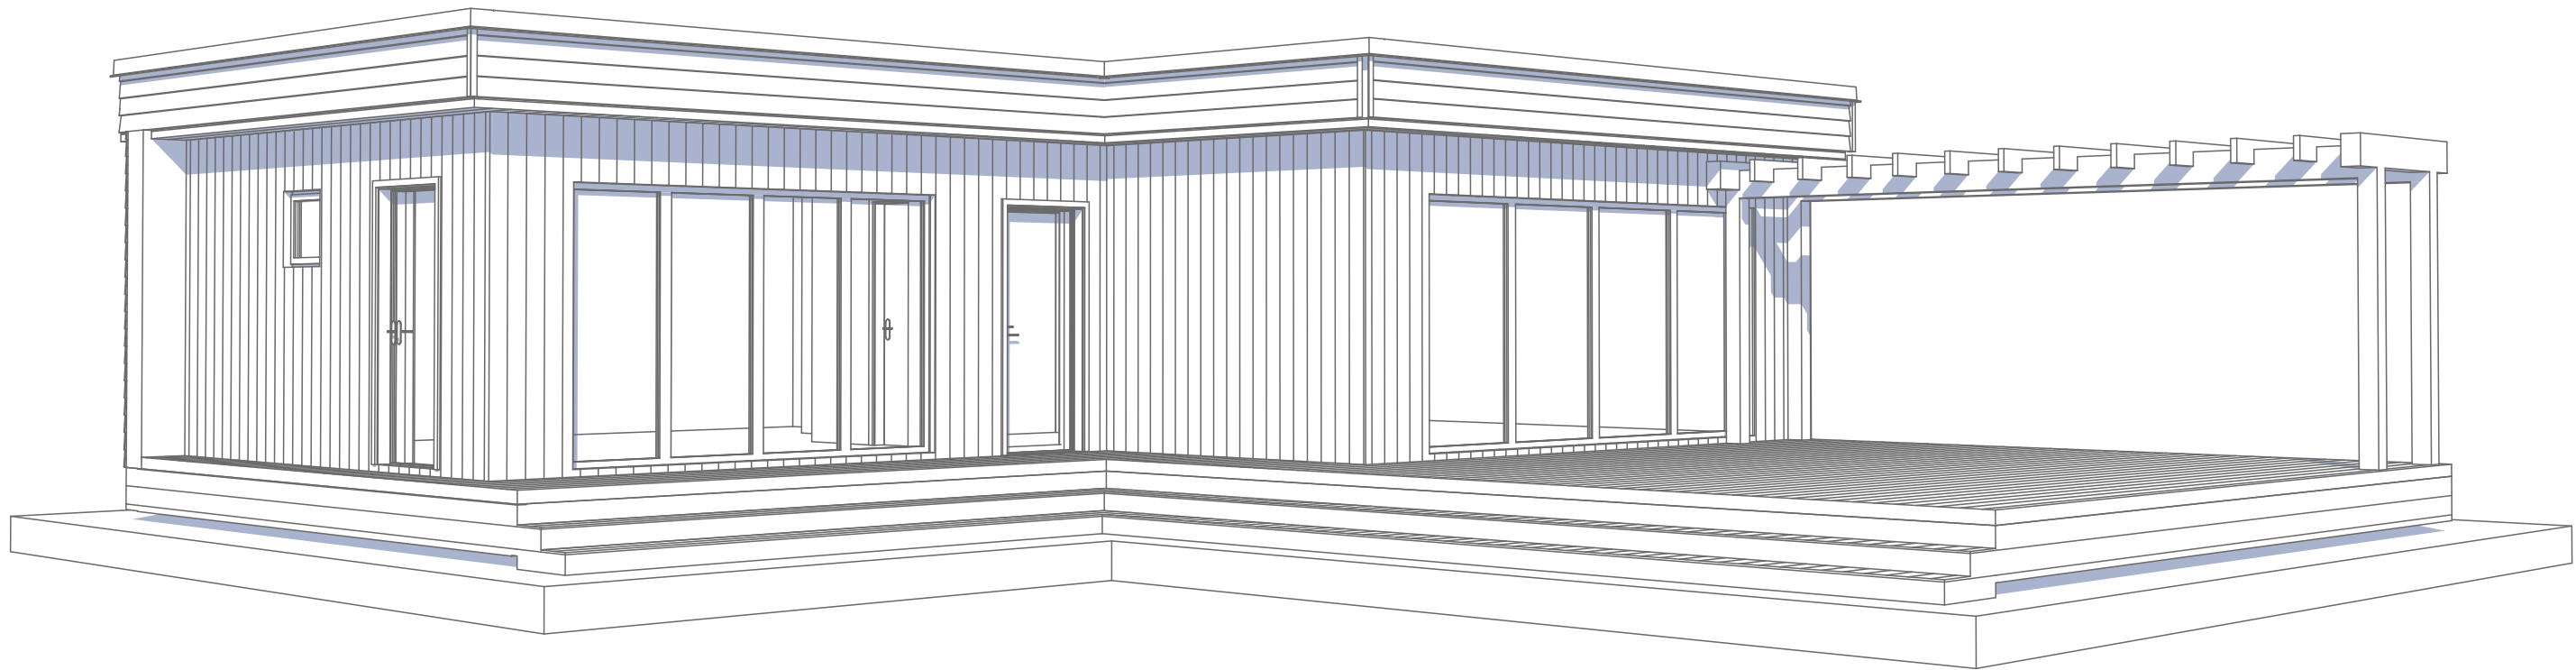

Лист	Изм.	№ Докум.	Подп.	Дата

--

Аксонометрия №1


#Название Организации

Лист
24

Согласовано			

Инва. № подл.	Подп. и дата	Взам. инв. №	

Лист	Изм.	№ Докум.	Подп.	Дата

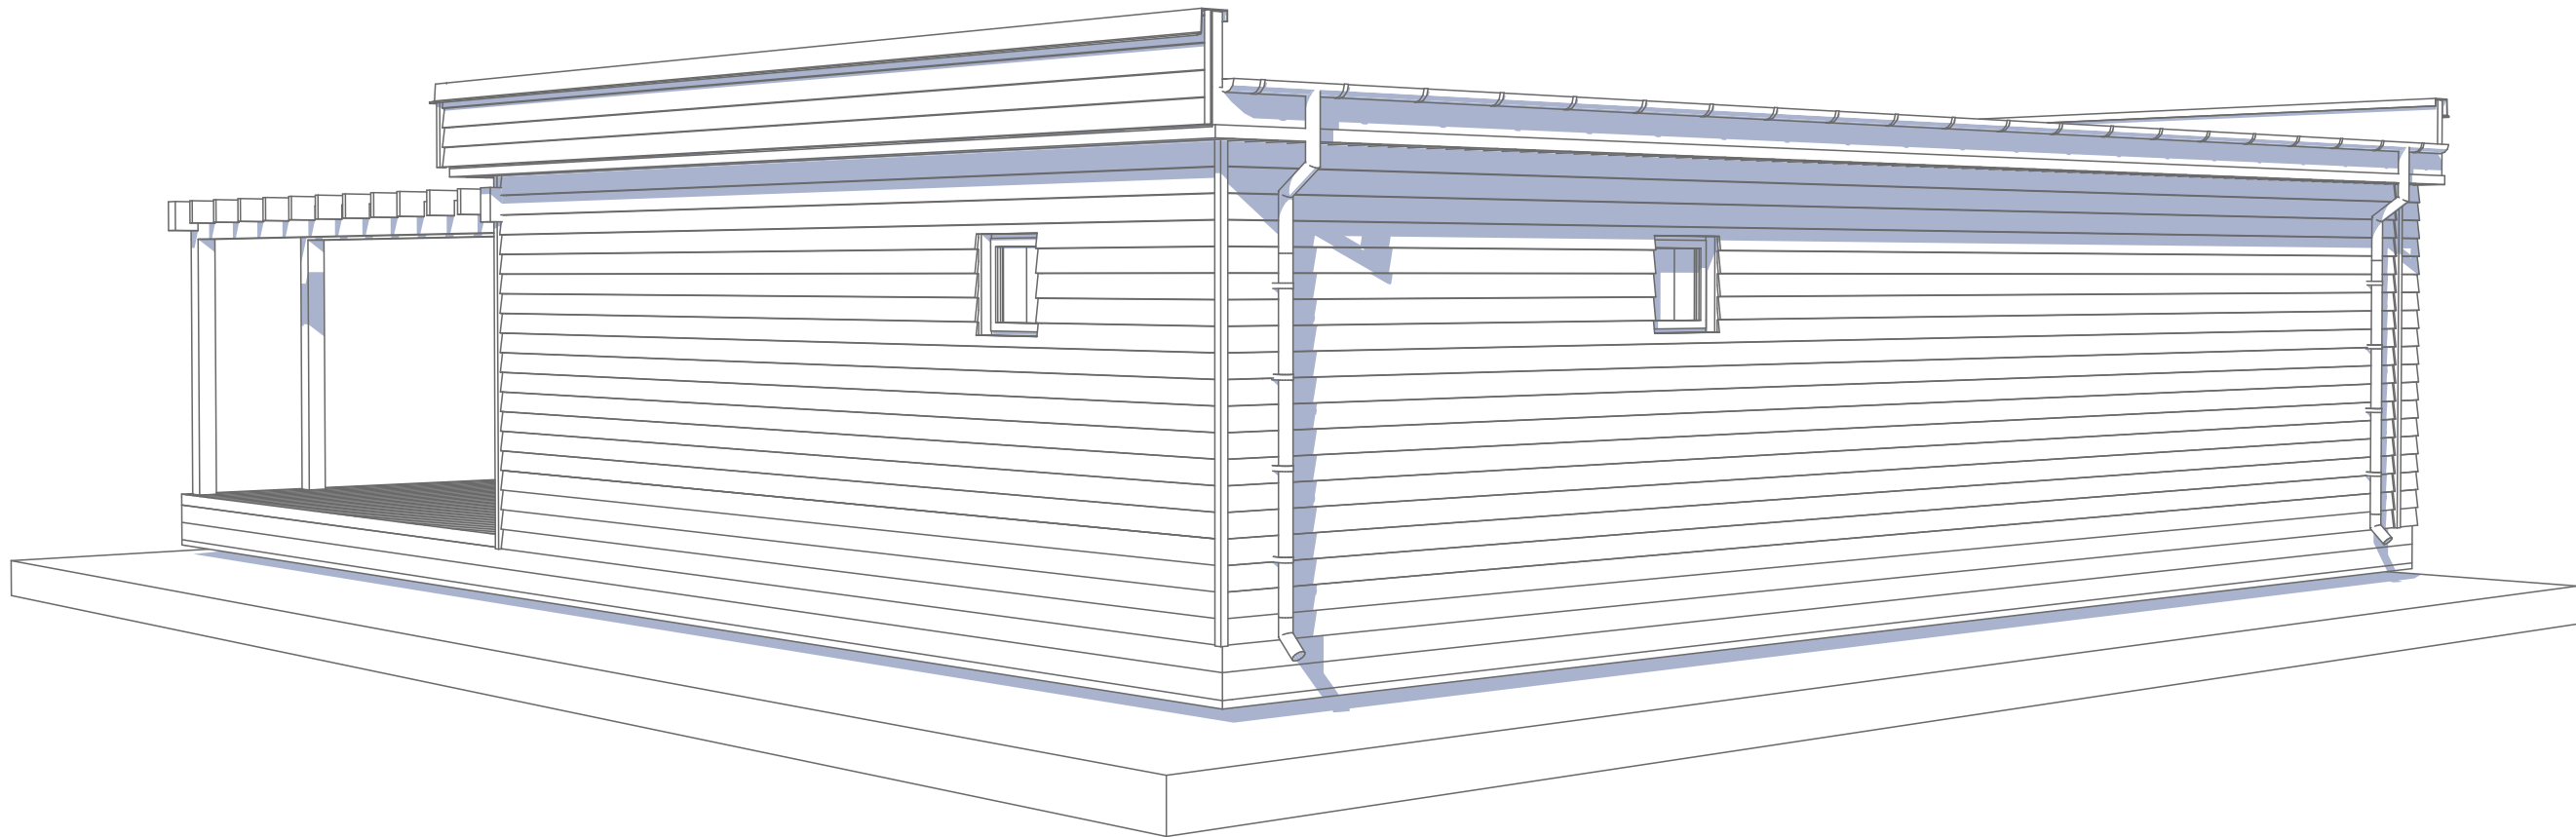

Согласовано				

Инв. № подл.	Подп. и дата	Взам. инв. №



Лист	Изм.	№ Докум.	Подп.	Дата

Визуализация

#Название Организации

ЛИСТ

26

Согласовано			

Инва. № подл.	Подп. и дата	Взам. инв. №	



Лист	Изм.	№ Докум.	Подп.	Дата

--

Визуализация

#Название Организации

Лист
27

Согласовано			



Инва. № подл.	Подп. и дата		Взам. инв. №	

Лист	Изм.	№ Докум.	Подп.	Дата

--

Визуализация

#Название Организации

Лист
28

Согласовано				



Инва. № подл.	Подп. и дата		Взам. инв. №	

Лист	Изм.	№ Докум.	Подп.	Дата

--

Визуализация

#Название Организации

Лист
29