



Архитектор

Заказчик

Архитектурные решения
(раздел АР)
Одноэтажное здание
(беседка)
Основной комплект чертежей
(планы, разрезы, фасады)

Мясникова В.А.

Согласовано				
И-нв. № подл.	Подп. и дата	Взам. инв. №		

Лист	Наименование	Примечание
1	Титульный	
2	Ведомость чертежей	
3	Пояснительная записка	
4	Маркировочный план 1 этажа	
5	Размерный план 1 этажа	
6	План расстановки мебели и оборудования 1 этажа	
7	Зд-разрез	
8	План покрытия пола	
9	Пироги пола	
10	План покрытия стен	
11	Пироги стен	
12	План размещения розеток 1 этажа	
13	План размещения светильников и выключателей 1 этажа	
14	План теплого пола	
15	План крыши	
16	Ведомость оконных проемов	
17	Разрез 1-1	
18	Разрез 2-2	
19	Фасад 1-2	
20	Фасад А-Б	
21	Аксонометрия №1	
22	Фасад Б-А	
23	Фасад 2-1	
24	Аксонометрия №2	
25	Визуализация	
26	Визуализация	
27	Визуализация	
28	Визуализация	
29	Визуализация	

В основу архитектурно-планировочных решений положены требования технологических заданий и требования норм и правил строительного проектирования, действующих на территории РФ.

Основные параметры и требования разработаны на основании пожеланий и требований заказчика.

Архитектурные решения приняты в соответствии со следующими нормативными документами:

- Градостроительный кодекс российской федерации.
- Земельного Кодекса Российской Федерации.
- Федеральный закон от 22.07.2008 N 123 - ФЗ (ред. от 29.07.2017)"Технический регламент о требованиях

пожарной безопасности.

- Федеральный закон № 384 - ФЗ «Технический регламент о безопасности зданий и сооружений».

- ГОСТ Р 21.1101-2013.«Основные требования к проектной и рабочей документации».

· Постановление правительства РФ от 16.02.2008 № 87 «Положение о составе разделов проектной документации и требованиях к их содержанию».

- СП 42.13330.2011 «Градостроительство. Планировка и застройка городских и сельских поселений».

- СП 131.13330.2018 «СНиП 23-01-99* Строительная климатология».

- СП 20.13330.2016 «СНиП 2.01.07-85* Нагрузки и воздействия».

- СП 22.13330.2016 «СНиП 2.02.01-83* Основания зданий и сооружений».

- СП 70.13330.2012 (с изменениями №1) «СНиП 3.03.01-87 Несущие и ограждающие конструкции».

- СП 64.13330.2017 «СНиП II-25-80 Деревянные конструкции».

- СП 17.13330.2017 «СНиП II-26-76 Кровли».

- СП 29.13330.2011 «СНиП 2.03.13-88 Полы».

- СП 28.13330.2017 «СНиП 2.03.11-85 Защита строительных конструкций от коррозии».

- СП 50.13330.2012 «СНиП 23-02-2003 Тепловая защита зданий».

Лист	Изм.	№ Докум.	Подп.	Дата

Обл. Московская, г.о. Мытищи, дер. Чиверёво, ул. Парусная,
дом 12

Ведомость чертежей

Лист
2

Согласовано				
И-нв. № подл.	Подп. и дата	Взам. инв. №		

1. Общие данные:

1.1. Архитектурный проект разработан на основании требований и пожеланий заказчика.

Тип строения	Беседка
Относительная отм. ±0.000	ур. верха лаг перекрытия
Общая площадь застройки, м2	40,00
Габаритные размеры каркаса здания	8,00х5,00м
Этажность	1 этаж
Конструктивная схема	Деревянный каркас

2. Конструктивные решения:

2.1. Рабочие чертежи разработаны на основании задания на проектирование

Полезная нагрузка на перекрытие	150 кгс/м2	-
Нормативная глубина промерзания	1,2м	СП 22.13330.2016 СП 131.13330.2020
Нормативное ветровое давление	I район (23кгс/м2)	СП 22.13330.2016
Нормативный вес снегового покрова	III район (150кгс/м2)	СП 22.13330.2016
Температура наиболее холодной пятидневки	-29°С	СП 131.13330.2020

2.2. Конструктивное строение представляет собой сооружение:

- на свайном фундаменте
- несущими стенами из деревянного каркаса
- плоской кровлей по деревянным стропилам

2.3. Необходимо осуществлять технический надзор за производством строительных работ. Данные по проведённым работам необходимо систематически вносить в журнал работ.

По каждому из этапов работ необходимо осуществлять входной контроль материалов и вести приёмку.

Фундамент	сваи винтовые d=108мм
Несущие конструкции	деревянный каркас (145х45мм)
Стропильная система	строганая доска (145/195х45мм)
Тип крыши	плоская
Покрытие кровли	наплавляемая

2.4. Все деревянные конструкции обработать огне-биозащитными септиками в соответствии со СП 28.13330.2017 "Защита строительных конструкций от коррозии".

2.5. Кровельные работы выполнять в соответствии с требованиями фирмы производителя.


2.6. Все работы вести в строгом соответствии с требованиями СНиП 12.03.2001 "Безопасность труда в строительстве".

2.7. При выполнении всех работ строго соблюдать меры противопожарной безопасности.

2.8. Возможна замена материалов аналогами.

*Решения, принятые в проекте и отображенные в чертежах, соответствуют требованиям экологических, санитарно - гигиенических, противопожарных и других норм, действующих на территории Российской Федерации, и обеспечивают безопасную для жизни и здоровья людей эксплуатацию объекта при соблюдении предусмотренных рабочих чертежей и мероприятий.

Экспликация помещений		
№	Наименование	Площадь, кв.м.
3	Зона отдыха	34,18
		34,18 м²
Наименование		Площадь, кв.м.
Площадь застройки		40,00
Примечание: 1. Вся индивидуальная мебель выполняется по отдельному проекту с детальной проработкой и калькуляцией. Чертежи предоставляет фирма-изготовитель столярных изделий. 2. Данный проект отдельно согласовывается с автором проекта и непосредственно с заказчиком. 3. Цветовое решение фасада и материалов отделки показаны в проекте приблизительно. 4. Количество ступеней показано условно.		
		Лист
		4

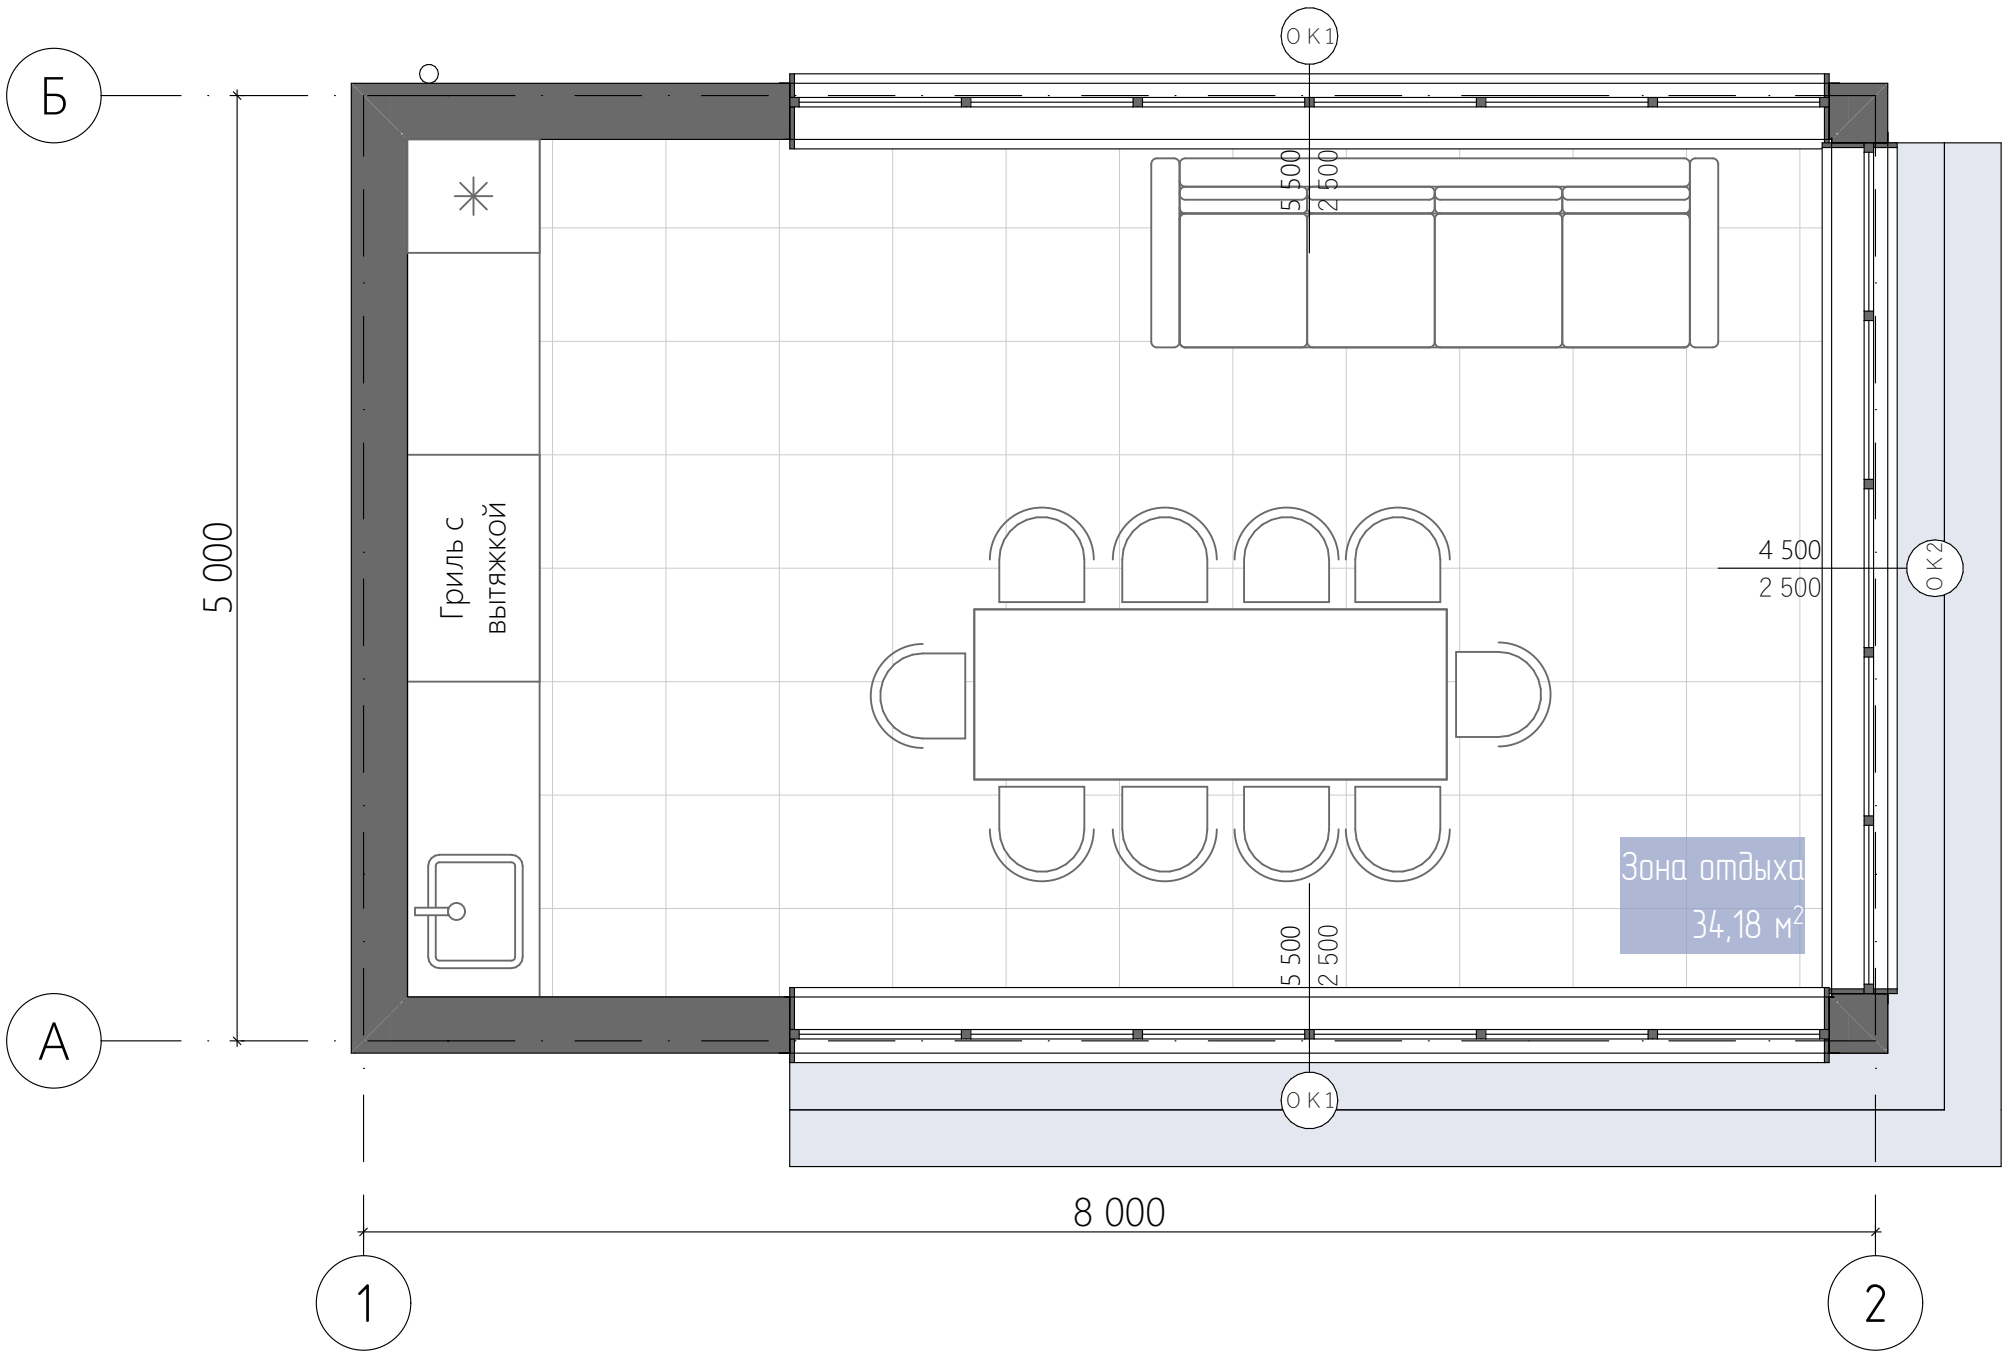


Согласовано				
Инва. № подл.	Подп. и дата	Взам. инв. №		

Лист	Изм.	№ Докум.	Подп.	Дата

Обл. Московская, г.о. Мытищи, дер. Чиверево, ул. Парусная, дом 12


Маркировочный план 1 этажа

Согласовано					Взам. инв. №		Подп. и дата		Инв. № подл.		

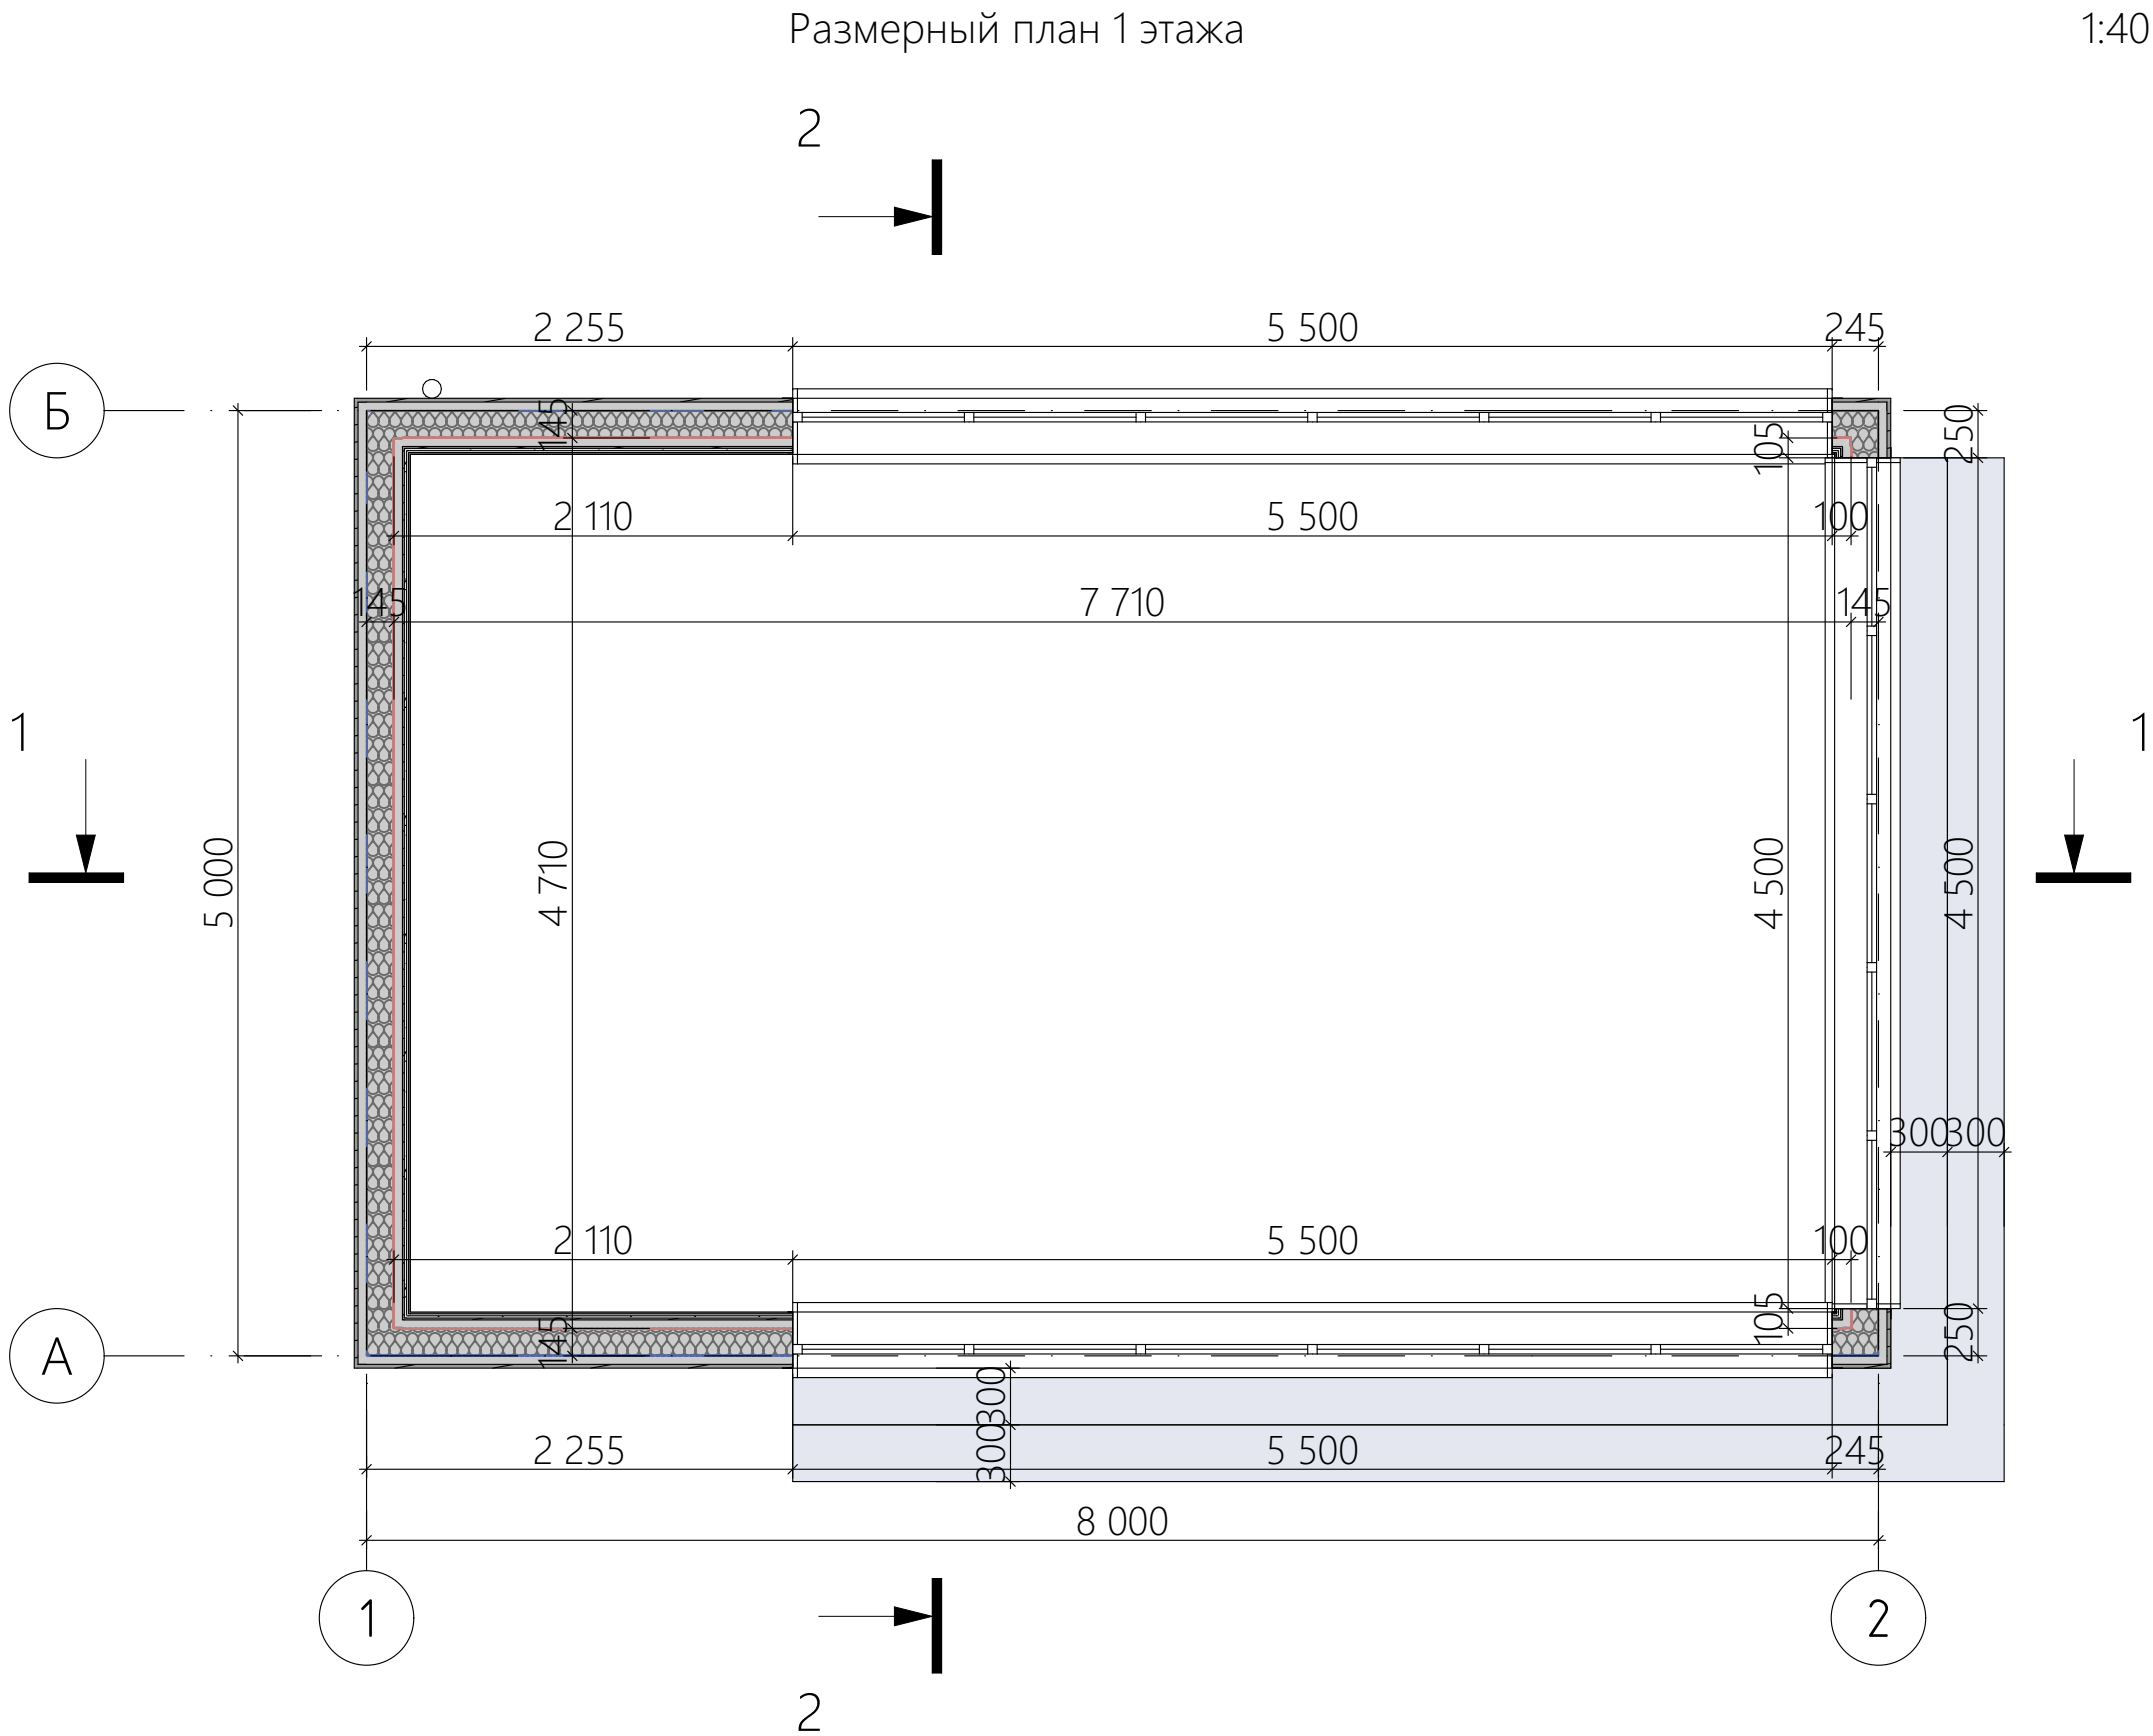

Примечание:

1. Представленные размеры указаны без учета внешней и внутренней отделки

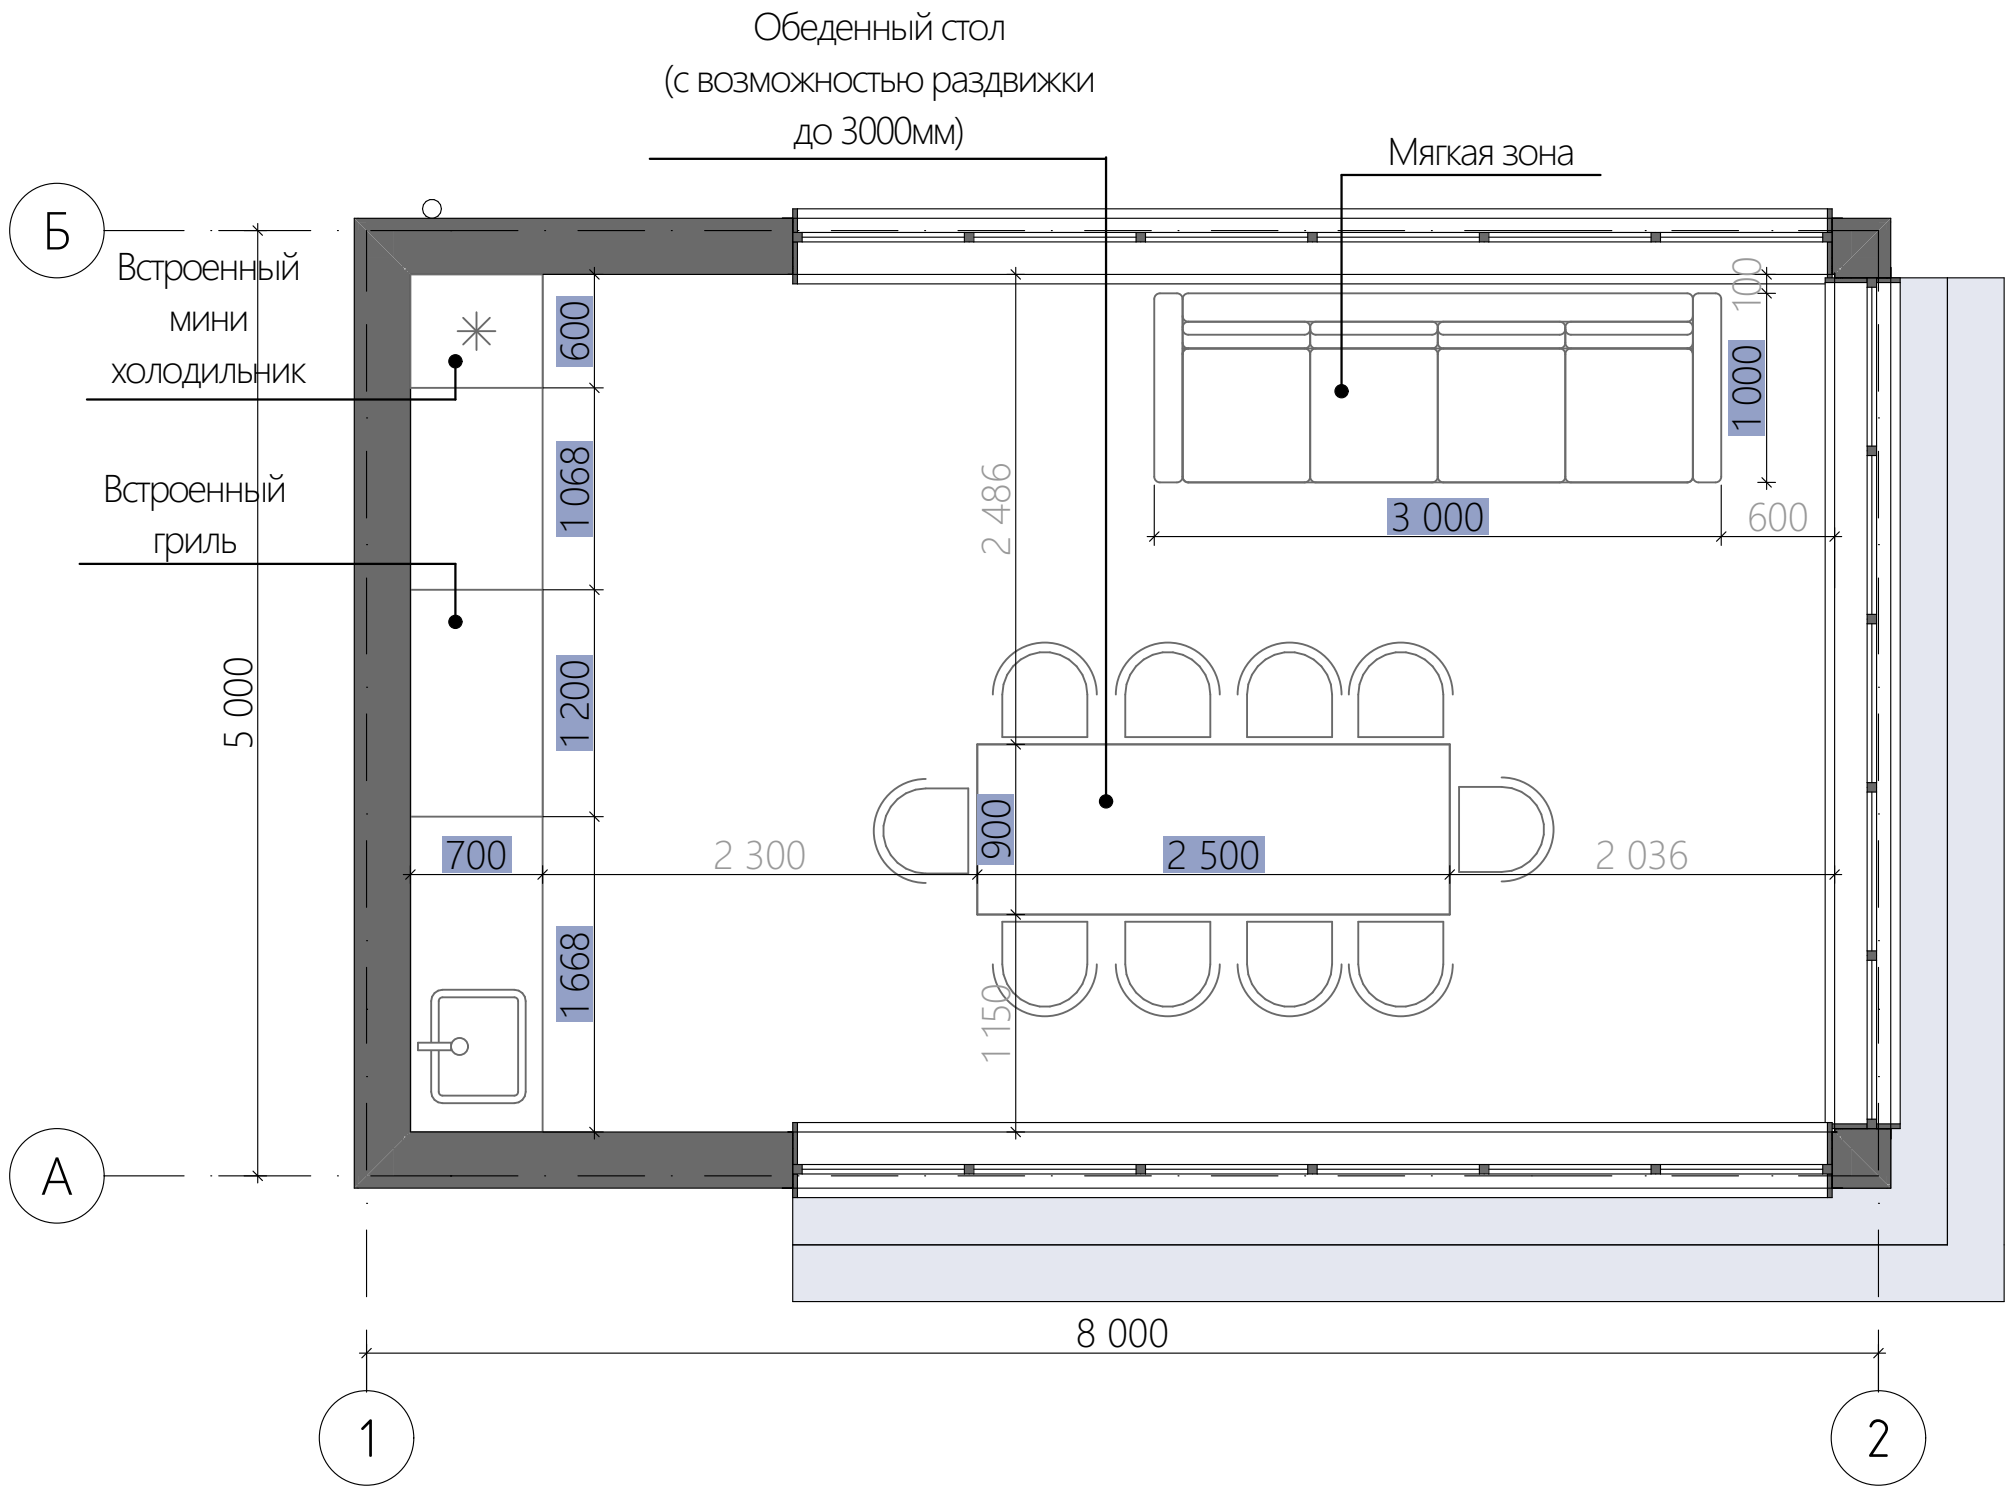

Примечание:

1. Вся индивидуальная мебель выполняется по отдельному проекту с детальной проработкой и калькуляцией. Чертежи предоставляет фирма-изготовитель столярных изделий.

2. Финальные размеры мебели и оборудования указаны ориентировочно — для точной компоновки требуется разработка дизайн-проекта.

Согласовано					
И-нв. № подл.	Подп. и дата	Взам. инв. №			
Лист	Изм.	№ Докум.	Подп.	Дата	


Согласовано

И-нв. № подл. Подп. и дата Взам. инв. №

Лист	Изм.	№ Докум.	Подп.	Дата

Обл. Московская, г.о. Мытищи, дер. Чиверёво, ул. Парусная,
дом 12

Зд-разрез

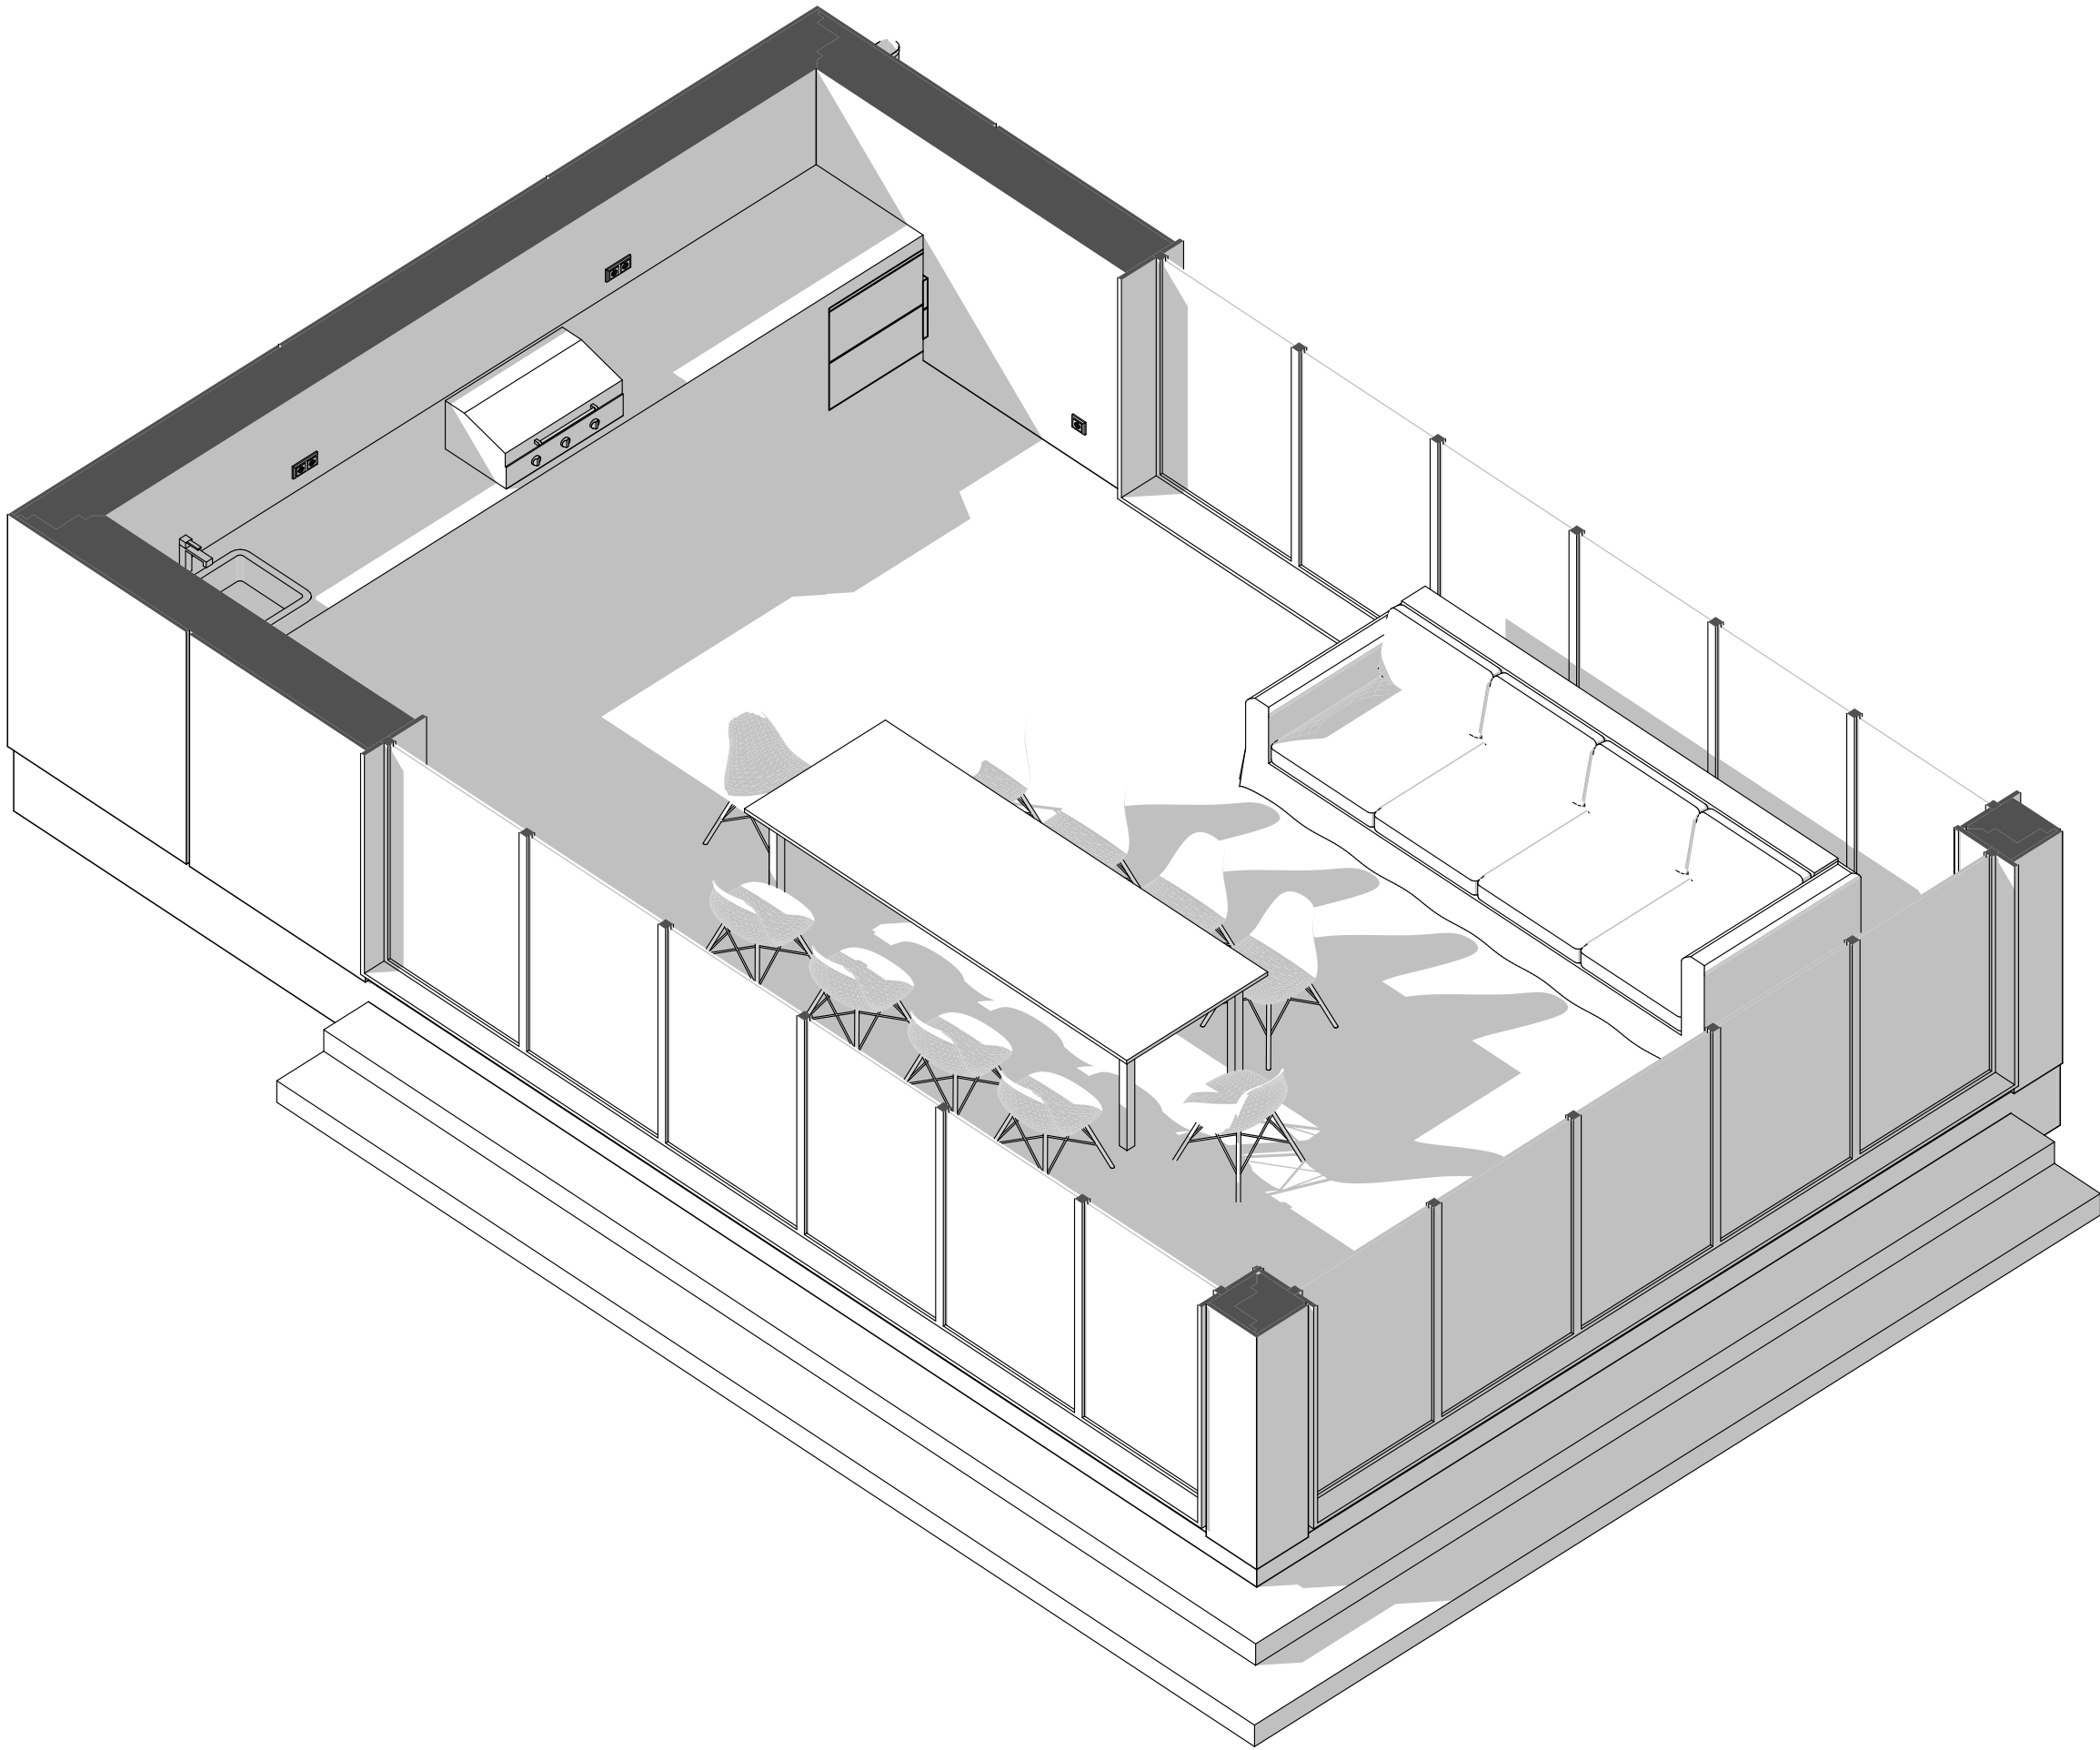

Согласовано				
Инв. № подл.	Подп. и дата	Взам. инв. №		

Лист	Изм.	№ Докум.	Подп.	Дата


Обл. Московская, г.о. Мытищи, дер. Чиверёво, ул. Парусная,
дом 12

План покрытия пола

Условные обозначения		
Номер покрытия	X +x,xxx xx,xx м²	Высота от проектного нуля Метраж покрытия
Экспликация покрытий пола		
№	Наименование	Площадь, м²
1	Керамогранит	34,18
Примечание: 1. Приведённые цветовые решения носят рекомендательный характер. Фактический подбор оттенков и материалов выполняется на этапе реализации с учётом наличия продукции у поставщиков и утверждения заказчиком. 2. Пирог покрытия смотреть на след. листе.		
		Лист
		8

План покрытия пола


1:40

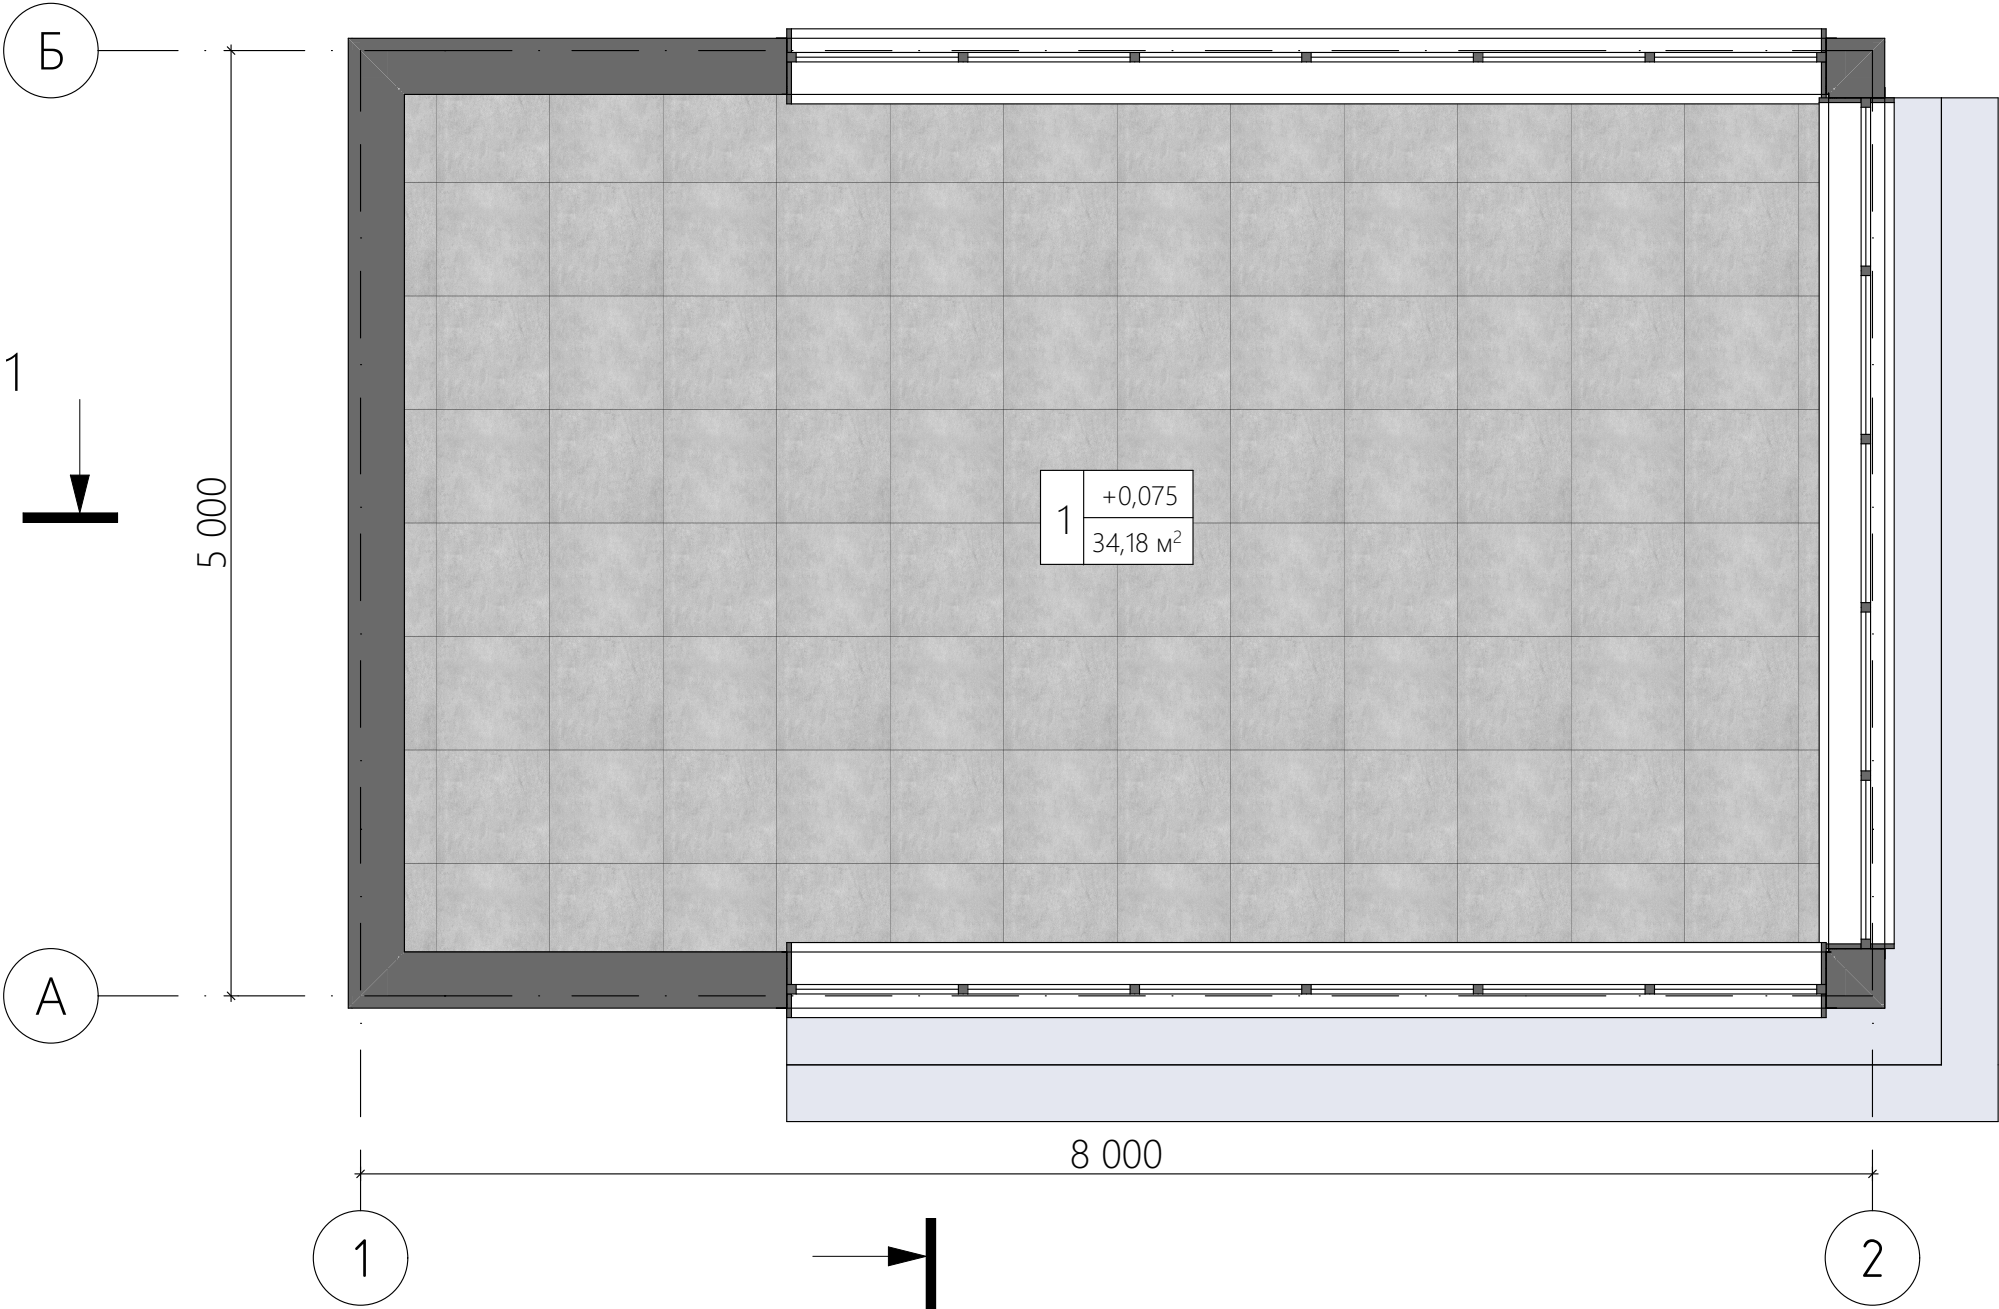

Пироги пола

№ Наименование Разрез Состав

1 Керамогранит

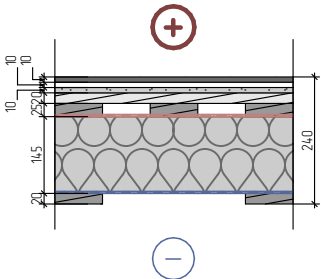


Керамогранит	10мм
Клей	10мм
(*с устройством эл. теплого пола)	-
ЦСП	10мм
Фанера	20мм
Вентбрусок (шаг 200мм)	25мм
Пароизоляционная мембрана	-
Лага перекрытия (утепленная 150мм)	145мм
Гидроветрозащитная мембрана	-
Просечка (сетка, ячейка 5х5мм)	-
Обрешетка (шаг 400мм)	25мм
Нижняя обвязка - 3 сросшаяся доска	150мм

Согласовано				Взам. инв. №	
				Подп. и дата	
				Ив. № подл.	

Лист	Изм.	№ Докум.	Подп.	Дата	Пироги пола		Лист
							9

Согласовано		Взам. инв. №		Подп. и дата	Инв. № подл.

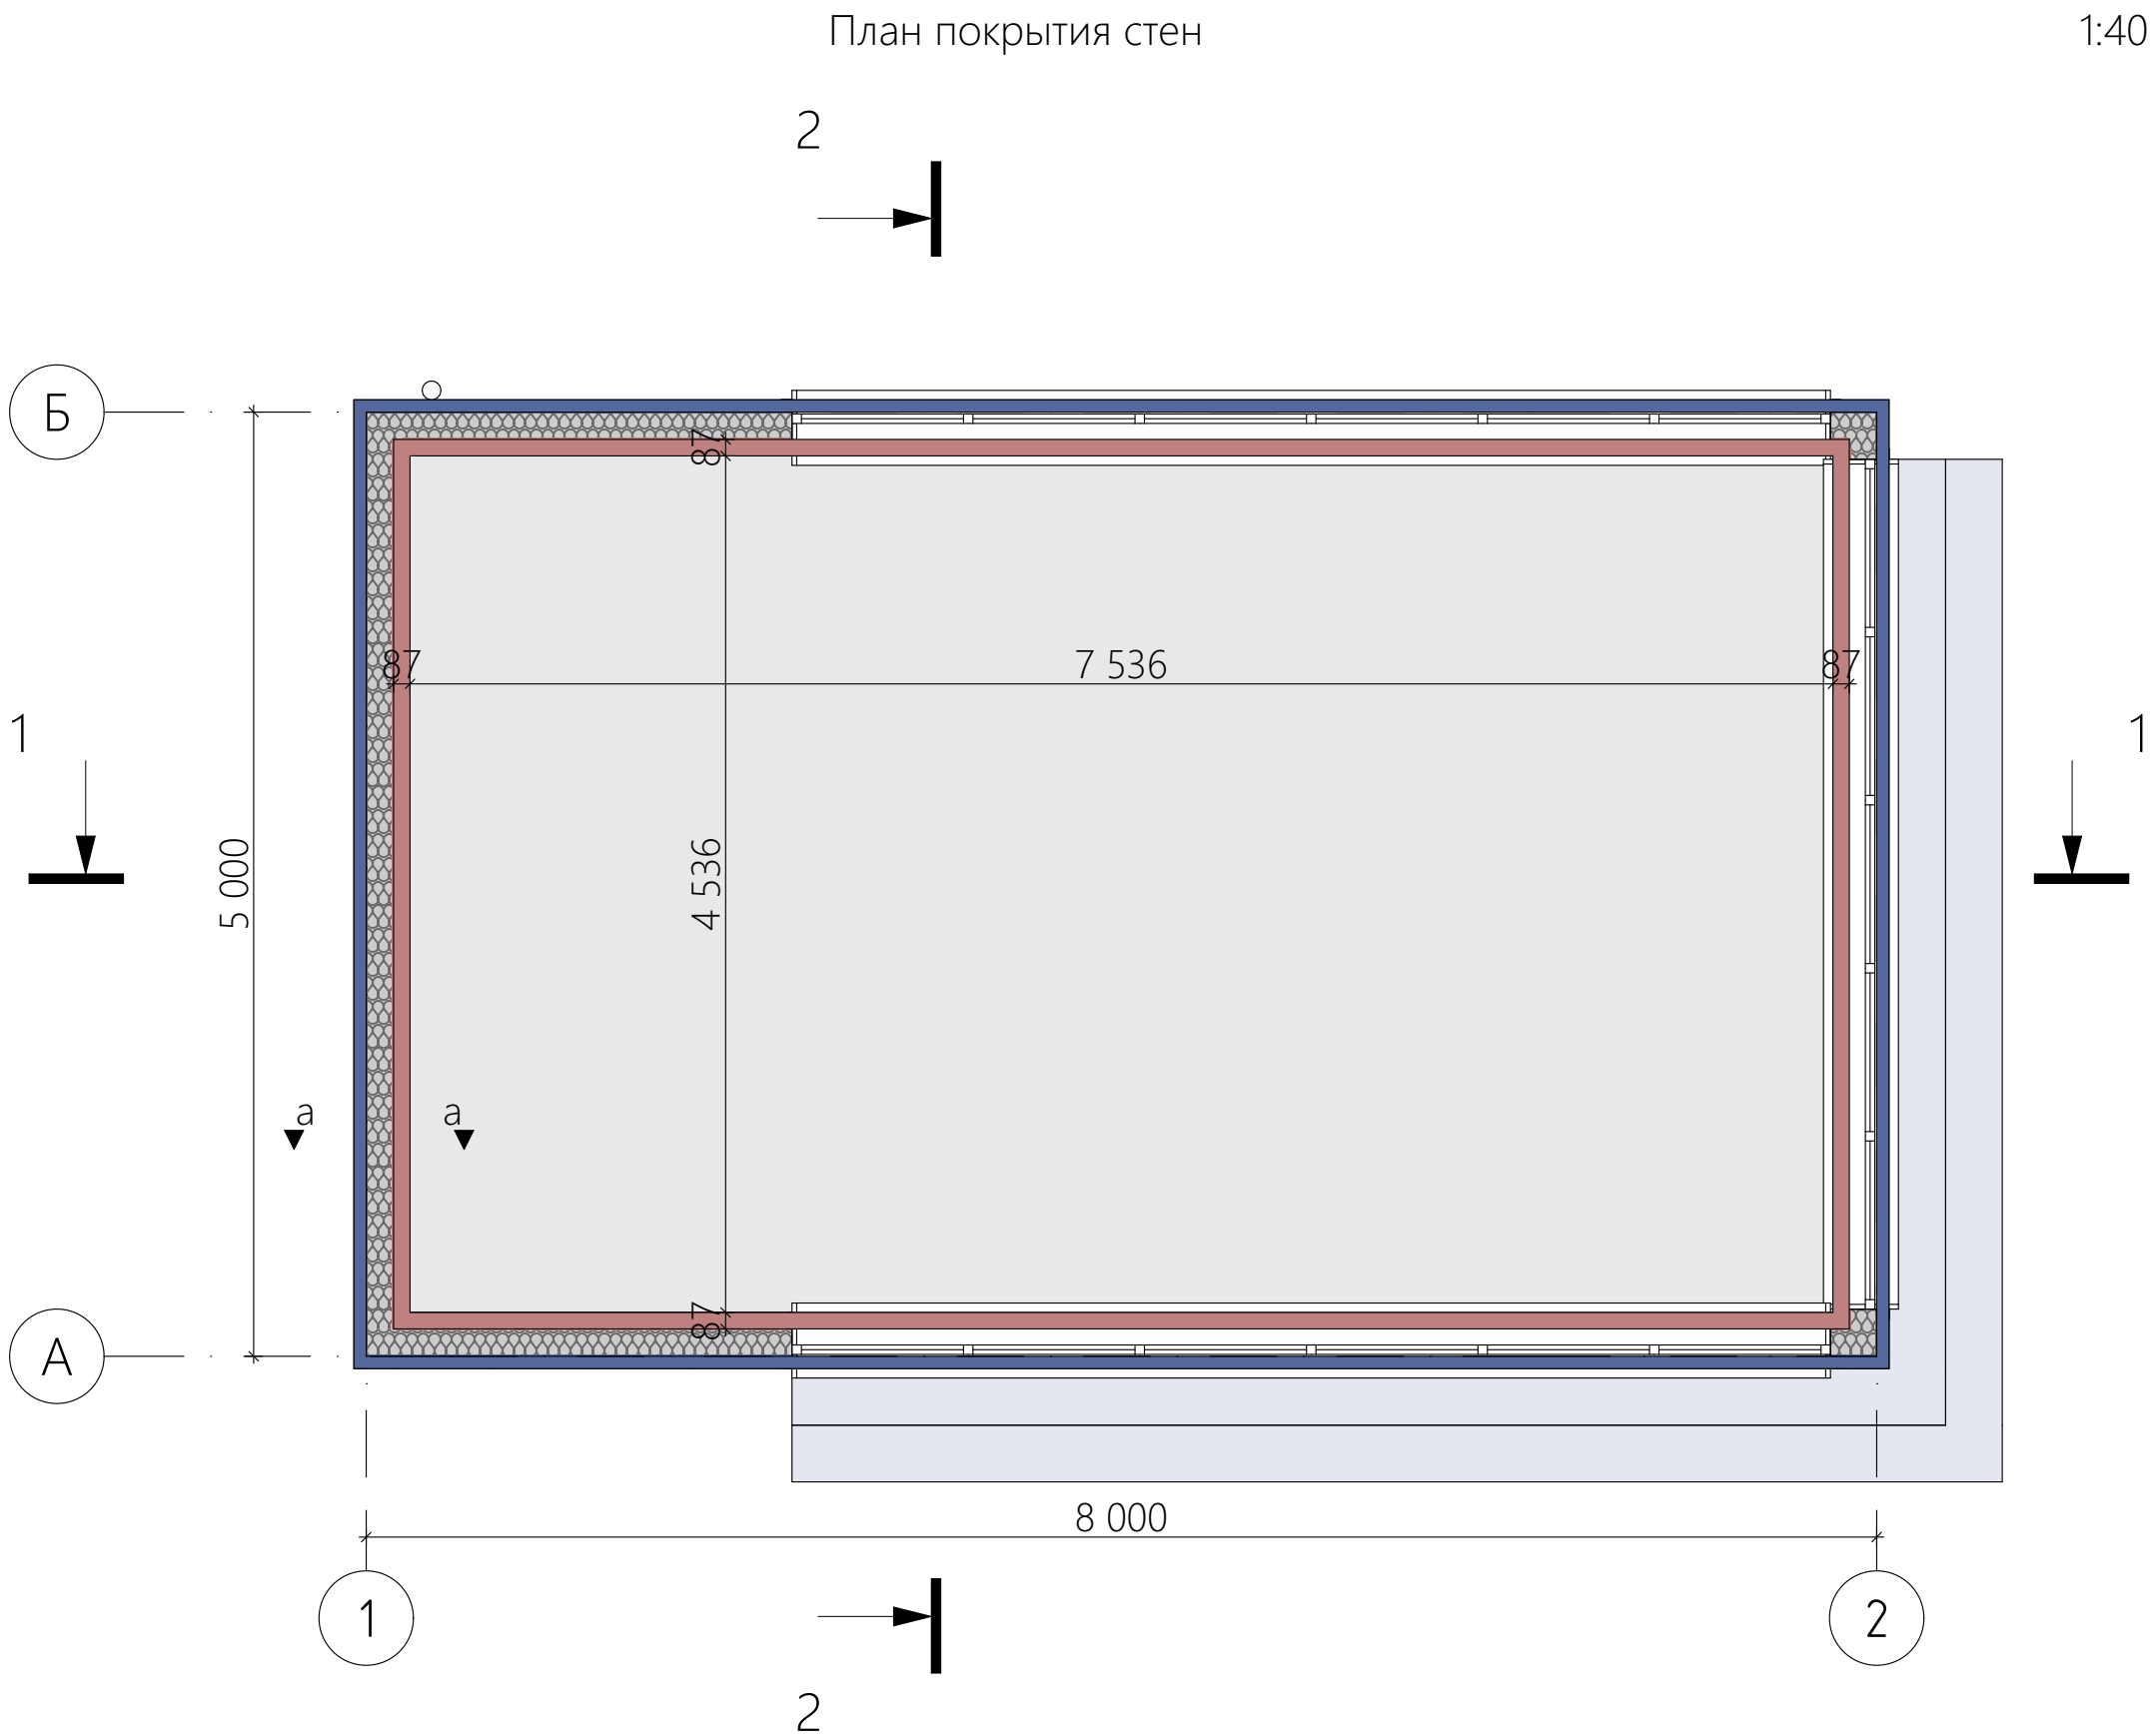

Экспликация покрытий стен		
№	Наименование	Условное обозначение
1	Фиброцементные панели (20мм)	
2	Керамогранит (10мм)	


Пироги стен

№ разреза

Сечение

Состав

а-а

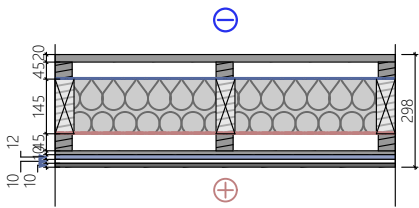


-Фиброцементные панели	20мм
-Вентбрусок (вертикально)	45мм
-Гидро-ветрозащитная мембрана	-
-Стойка каркаса (утепленная)	145мм
-Пароизоляционная мембрана	-
-Вентбрусок (вертикально)	45мм
-ОСБ	10мм
-ЦСП	12мм
-Клей	10мм
-Керамогранит	10мм

Согласовано					
Инв. № подл.	Подп. и дата	Взам. инв. №			

Лист	Изм.	№ Докум.	Подп.	Дата	Пироги стен		Лист
							11

Экспликация розеток		
Наименование	2д-вид	Кол-во
Розетка 220v (рамка 1 секции)		4
Розетка 220v (рамка 2 секции)		2
Эл. вывод		2
		8
Примечание:		
1. Схема размещения розеток является рекомендательной и требует согласования с заказчиком по месту. 2. Все высоты даны от чистового пола. 3. Все указанные размеры даются до центра позиций. 4. Отметки розеток, выключателей, выводов и др. оборудования, являются предварительными и уточняются после выбора финишных материалов и мебели. 5. Размеры уточняются дополнительно		
		Лист
		12

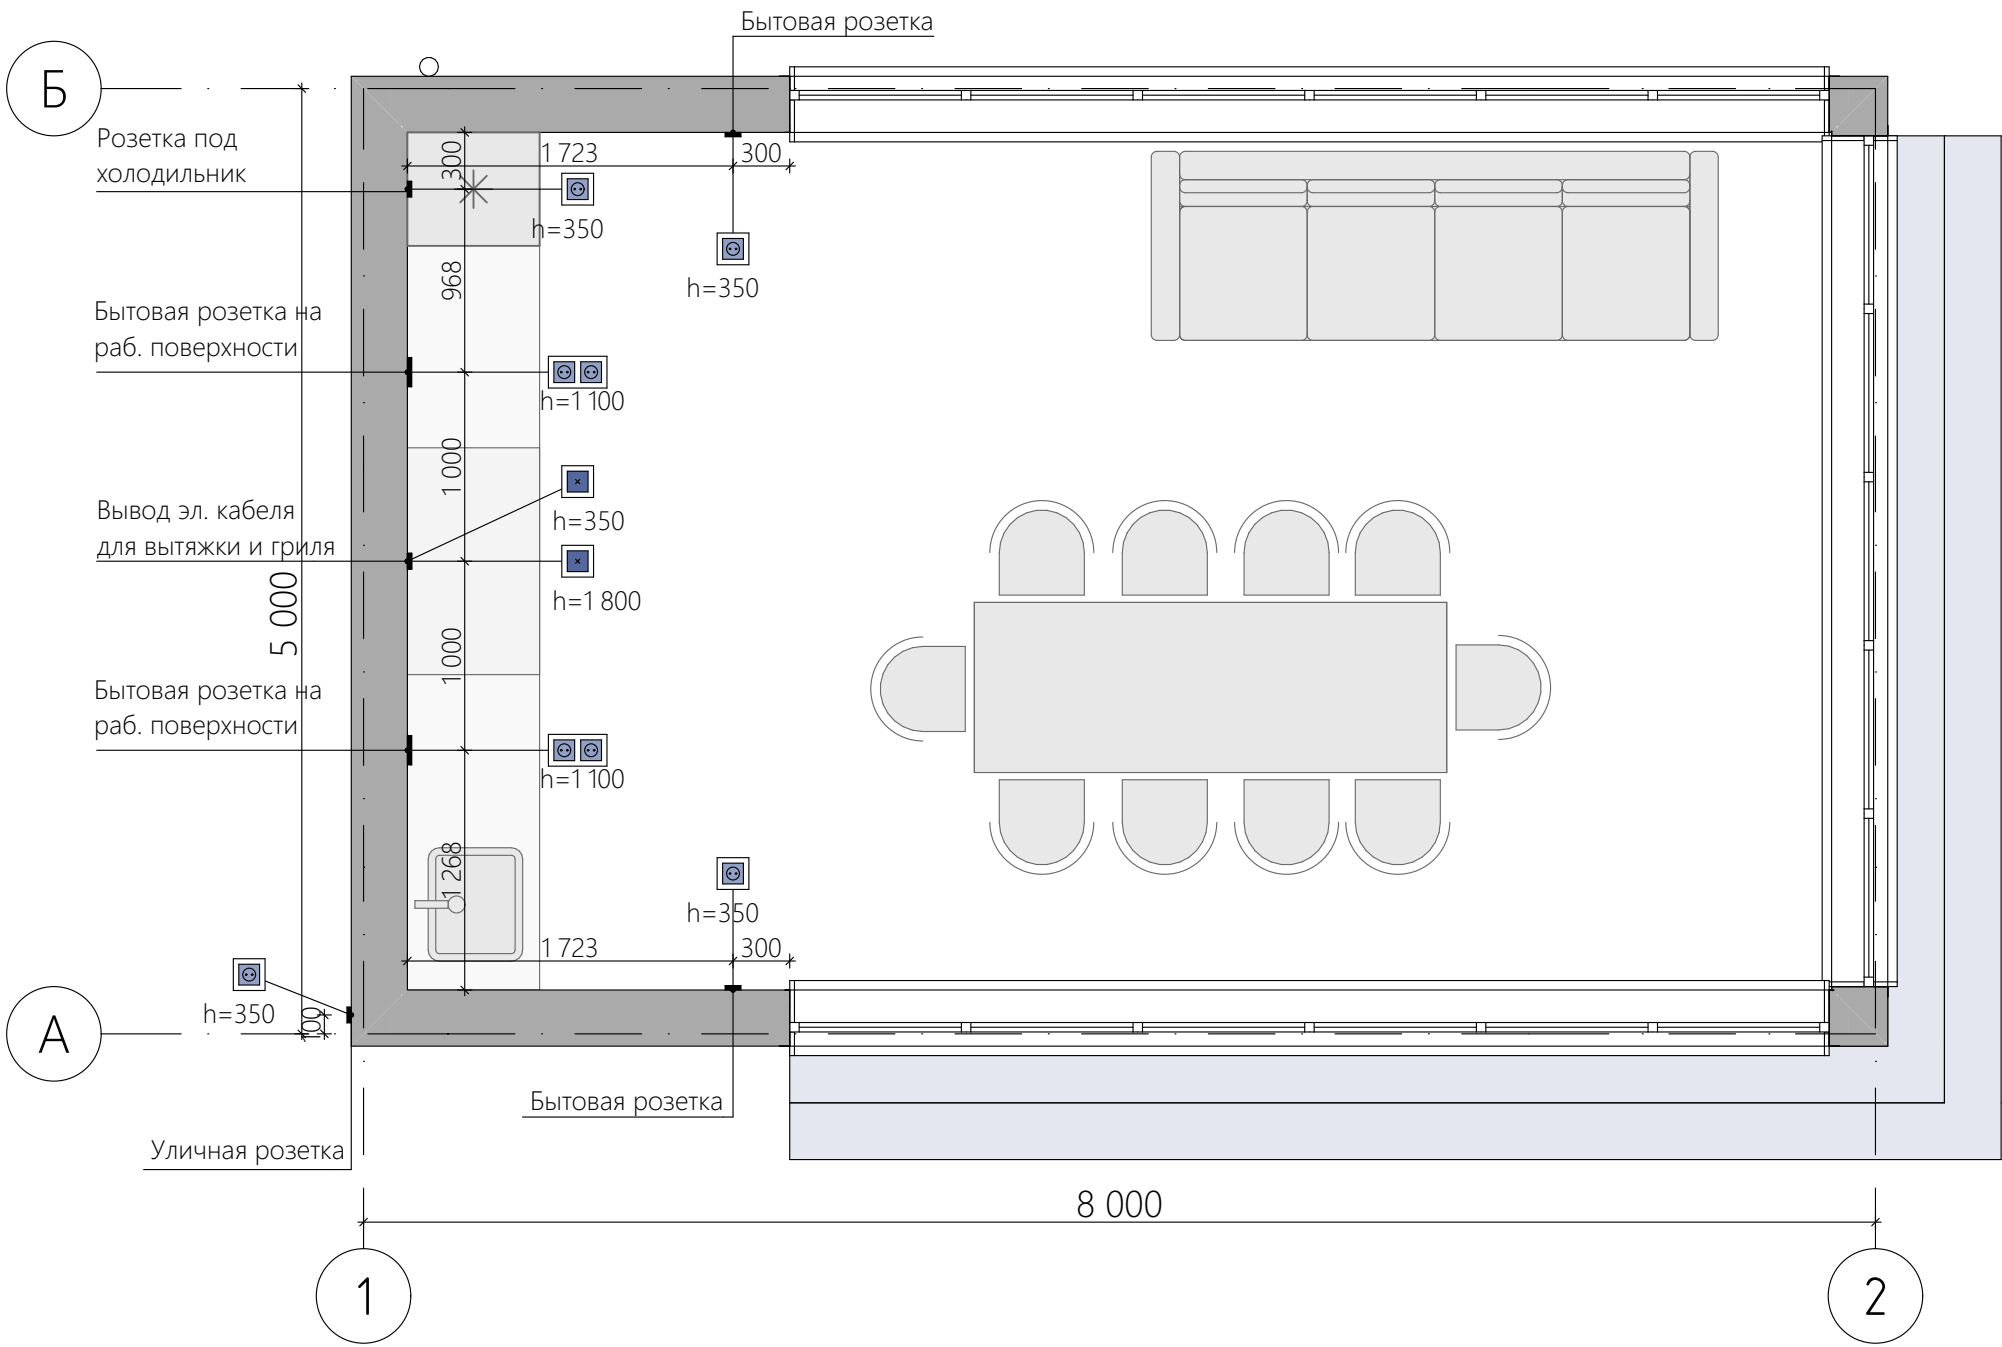

Согласовано				
Инов. № подл.	Подп. и дата	Взам. инв. №		

Лист	Изм.	№ Докум.	Подп.	Дата

План размещения светильников и выключателей 1 этажа

1:40

Экспликация светильников и выключателей

Наименование	2д-вид	Кол-во
Выключатель одно- и двухклавишный (рамка 2 секции)		1
Светильник точечный		8
Уличный светильник		1
		10

Примечание:


1. Схема размещения розеток является рекомендательной и требует согласования с заказчиком по месту.

2. Все высоты даны от чистового пола.

3. Все указанные размеры даются до центра позиций.

4. Отметки розеток, выключателей, выводов и др. оборудования, являются предварительными и уточняются после выбора финишных материалов и мебели.

5. Размеры уточняются дополнительно

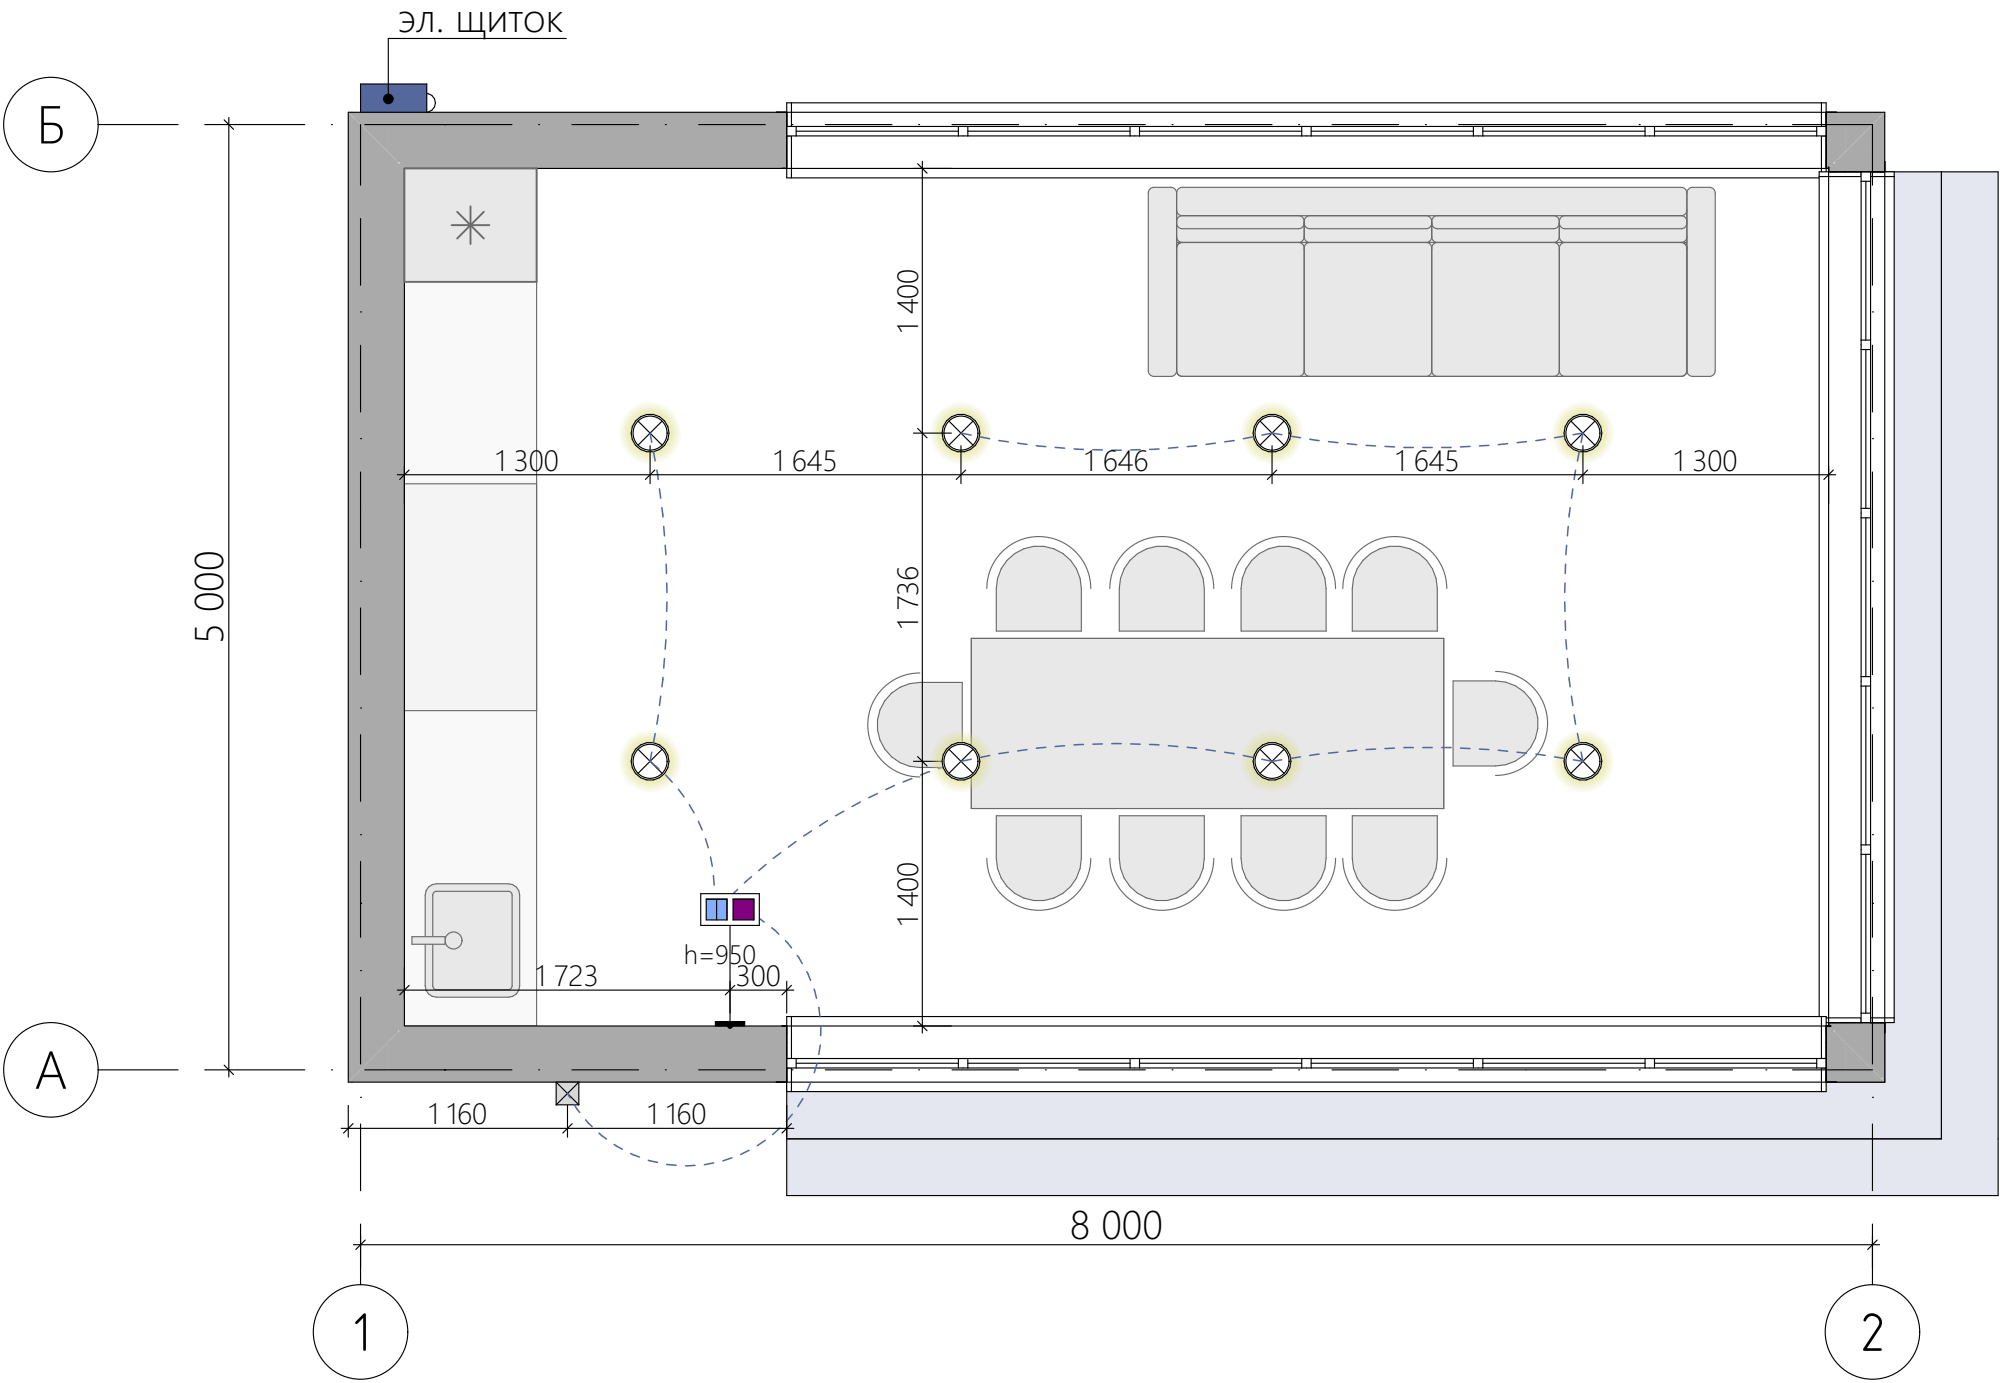

Согласовано				
Взам. инв. №				
Подп. и дата				
Инв. № подл.				

Лист	Изм.	№ Докум.	Подп.	Дата

Обл. Московская, г.о. Мытищи, дер. Чиверёво, ул. Парусная, дом 12

План размещения светильников и выключателей 1 этажа

	Лист
	13

План теплого пола


1:40

Условные обозначения:



- зона теплого пола

Площадь эл. теплого пола (S , m^2) = 27,85 m^2

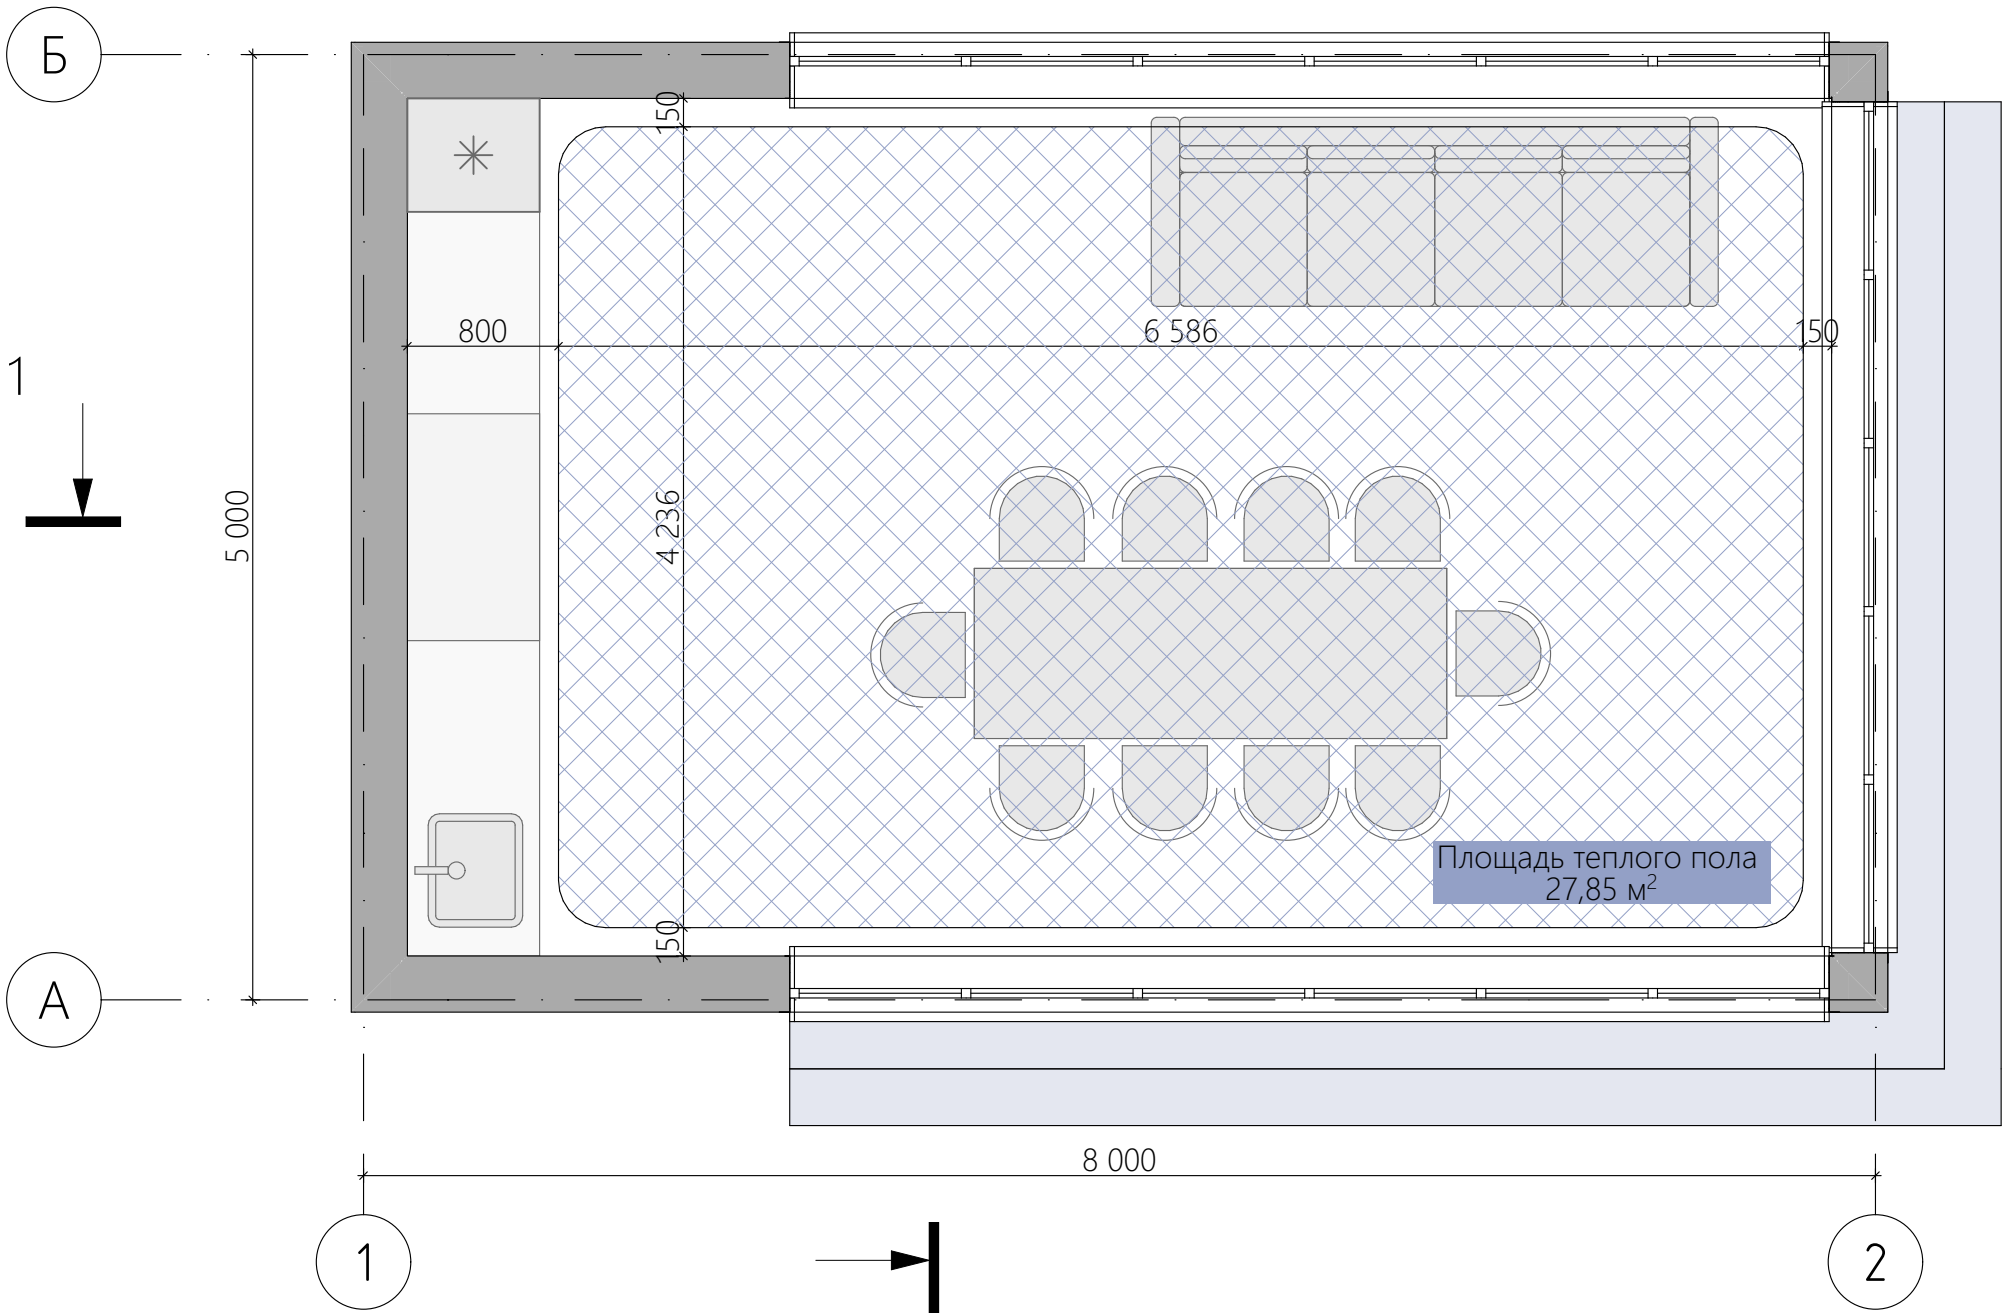

Согласовано					
Инов. № подл.	Подп. и дата		Взам. инв. №		

Лист	Изм.	№ Докум.	Подп.	Дата

Обл. Московская, г.о. Мытищи, дер. Чиверёво, ул. Парусная,
дом 12


План теплого пола

Согласовано					
Инв. № подл.	Подп. и дата	Взам. инв. №			

Лист	Изм.	№ Докум.	Подп.	Дата

Обл. Московская, г.о. Мытицы, дер. Чиверёво, ул. Парусная,
дом 12

План крыши

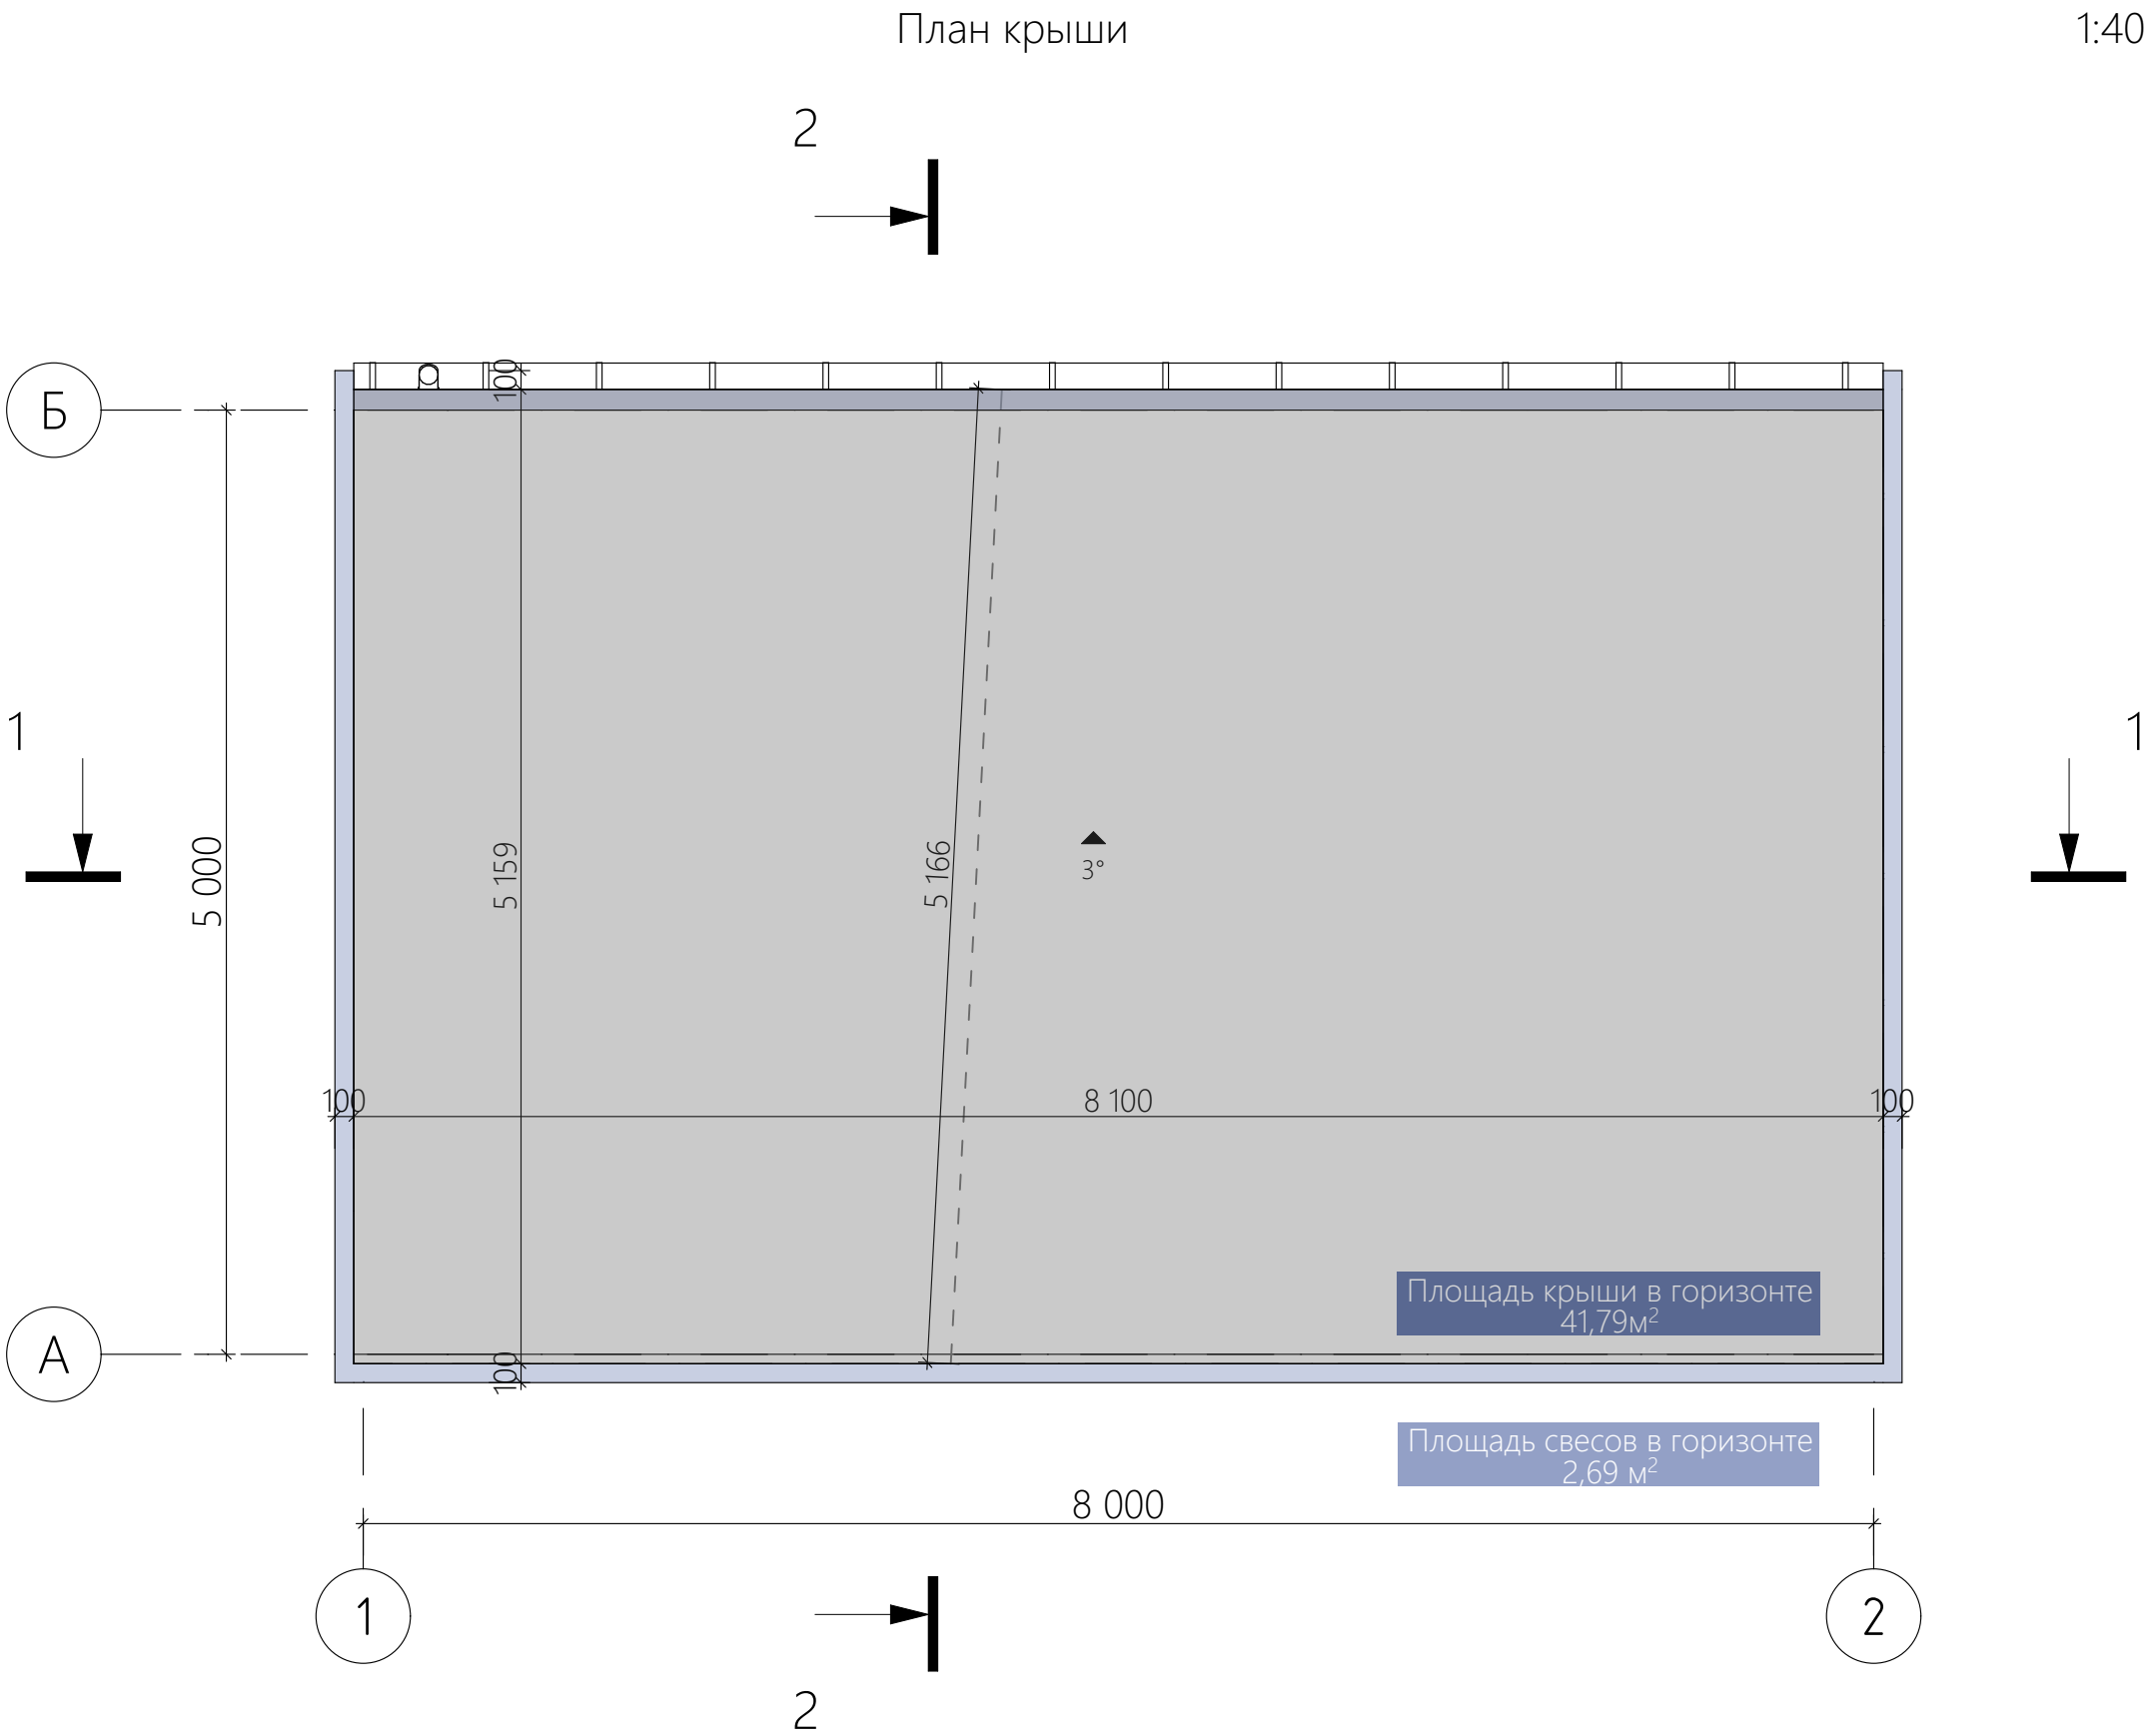


Условные обозначения:

- Крыша (уклон 3°)
- Подшив свесов

Площадь крыши (S, м²) = 41,84м²

Аксонометрия крыши

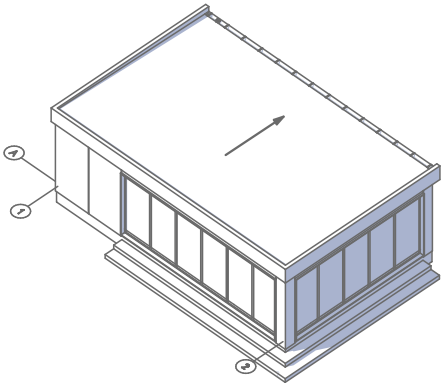


1:1

	38,75 m ²
--	----------------------

Инв. № подл.	Подп. и дата	Взам. инв. №

1. Изготовление окон и дверей определяется заказчиком, допускается изменение открывания окон и дверей;
2. При заказе оконных и дверных блоков необходим обмер по месту от изготовителя;
3. Оконные и дверные изделия изображены со стороны открывания.

Лист	Изм.	№ Докум.	Подп.	Дата	Ведомость оконных проемов		Лист
							16

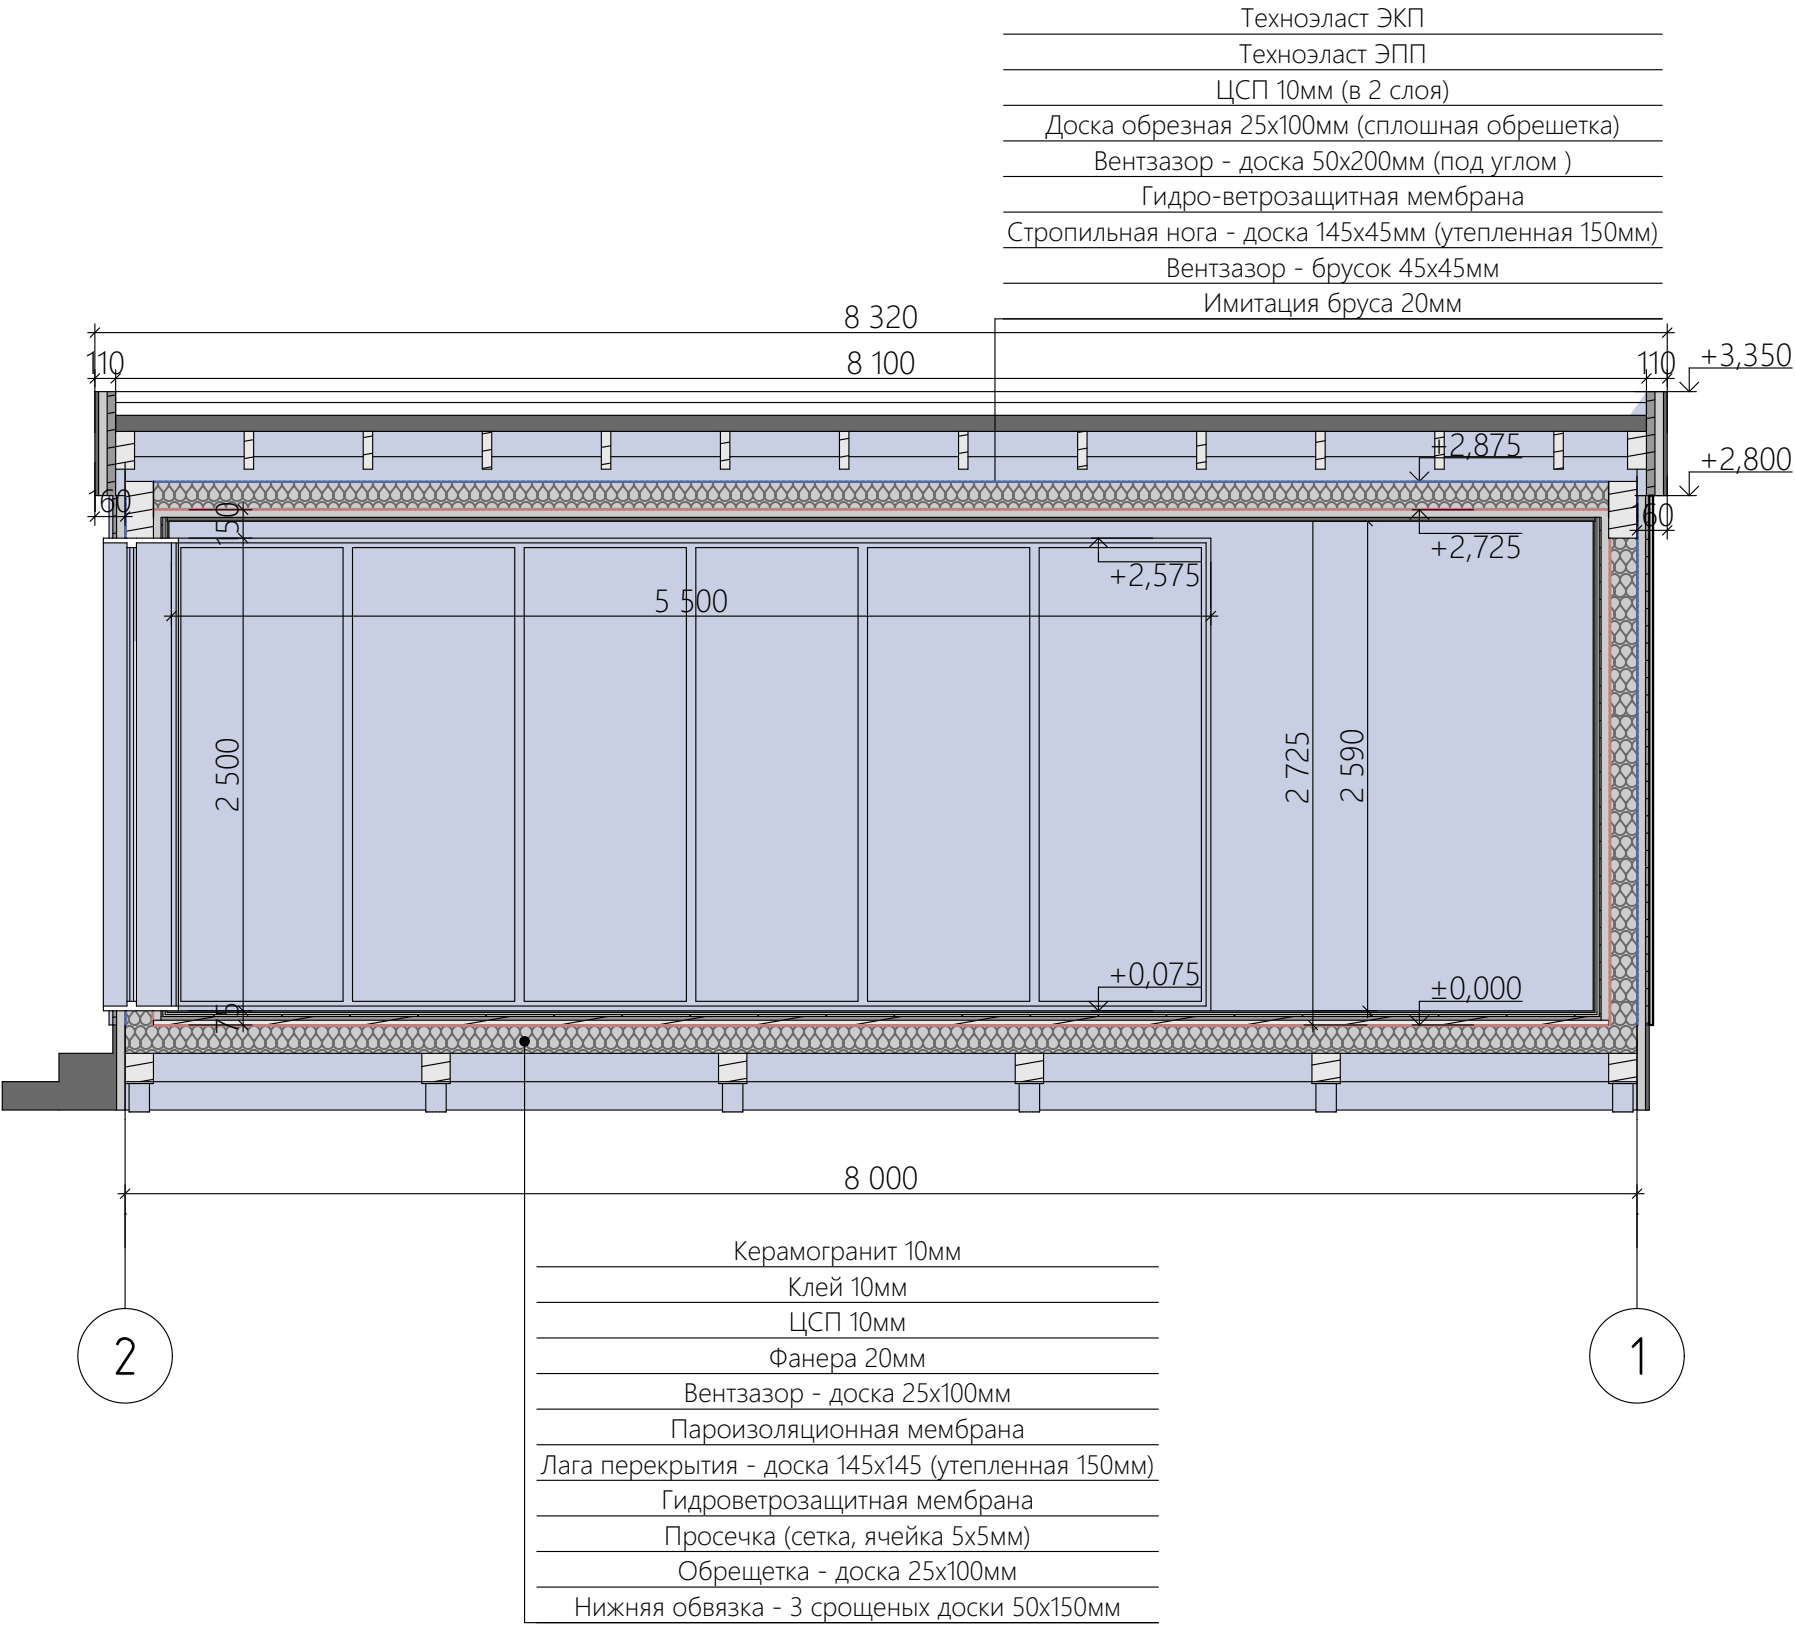

Согласовано				
Инов. № подл.	Взам. инв. №	Подп. и дата		

Лист	Изм.	№ Докум.	Подп.	Дата


Обл. Московская, г.о. Мытищи, дер. Чиверёво, ул. Парусная,
дом 12

Разрез 1-1

Лист
17

Разрез 2-2

1:40

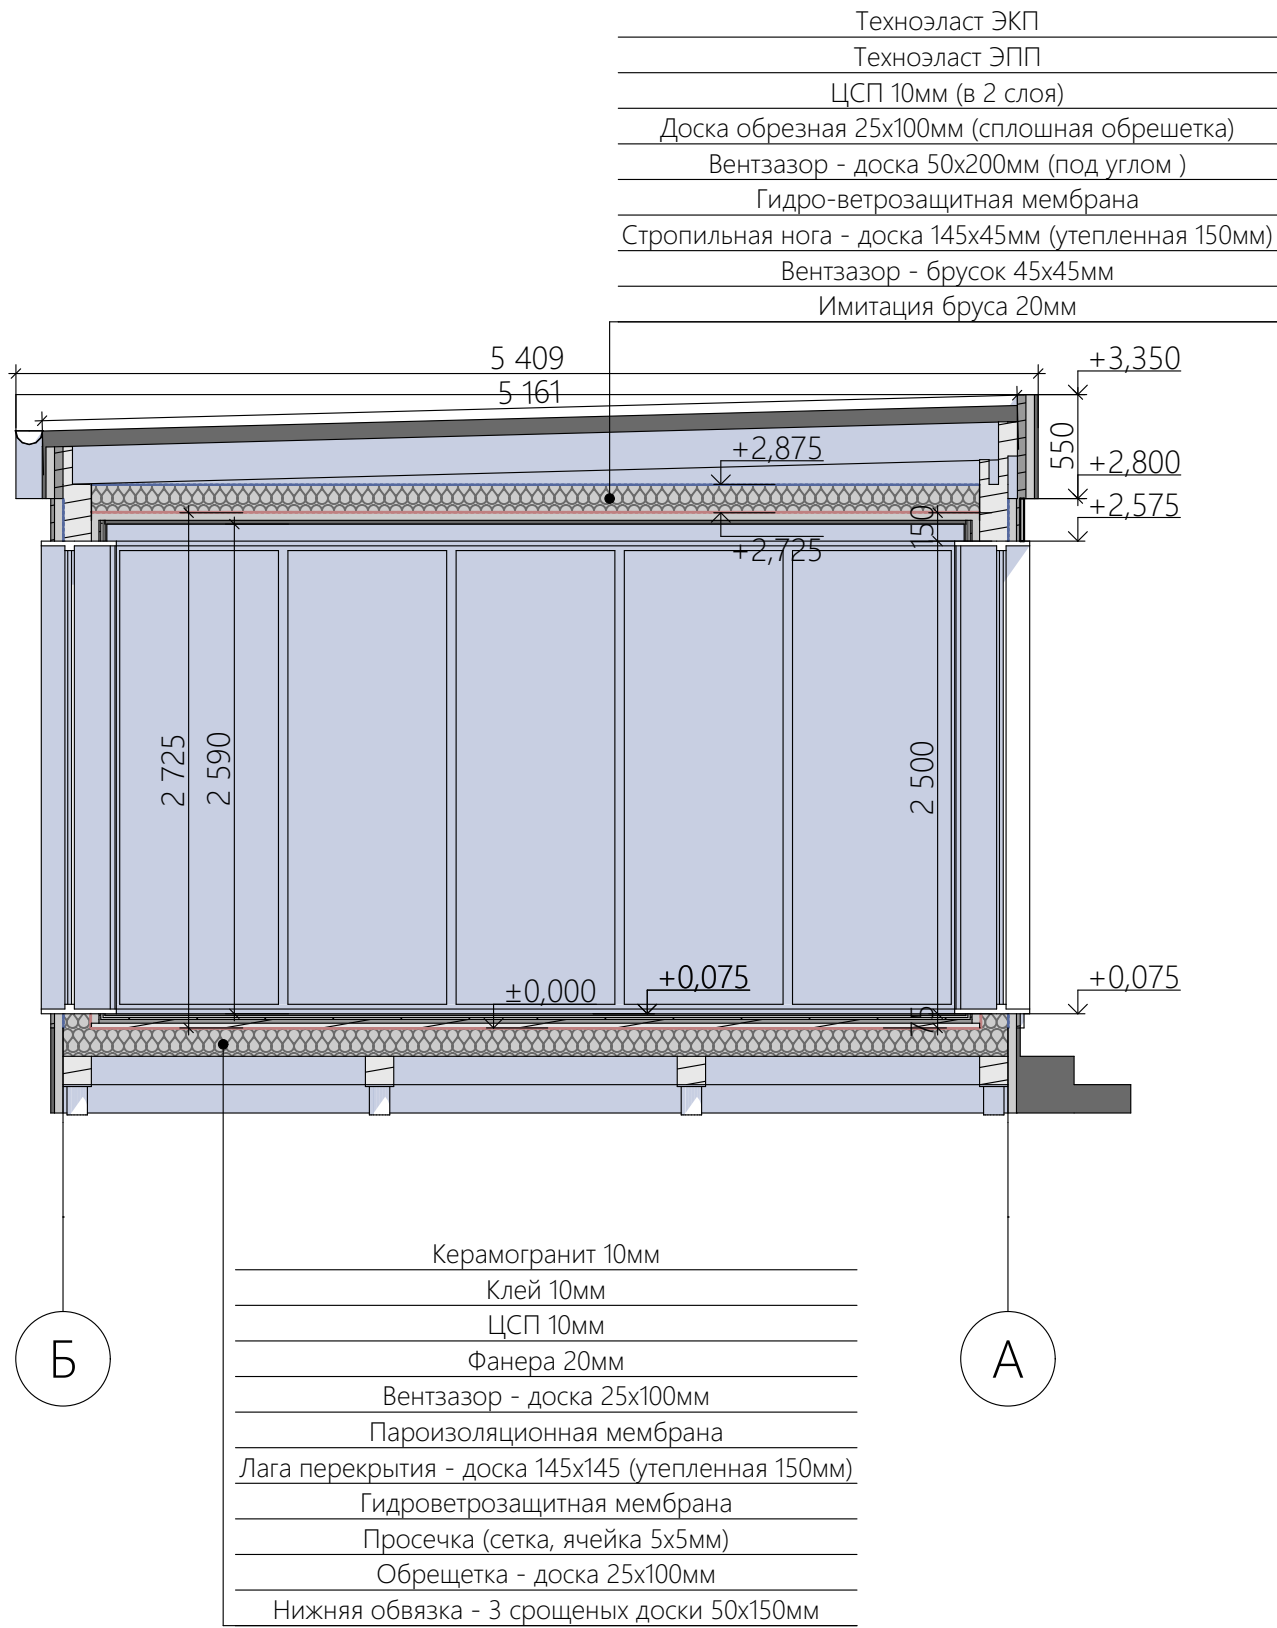

Согласовано				
И.нв. № подл.	Подп. и дата	Взам. инв. №		

Лист	Изм.	№ Докум.	Подп.	Дата

Обл. Московская, г.о. Мытищи, дер. Чиверёво, ул. Парусная,
дом 12

Разрез 2-2


Лист
18

Фасад 1-2

1:40

Условные обозначения:

- Фиброцементные панели (черный)
- ДПК (черный)
- Водосточная система (RAL 9004)
- Наличники, рамы, угловые элементы (RAL 9004)

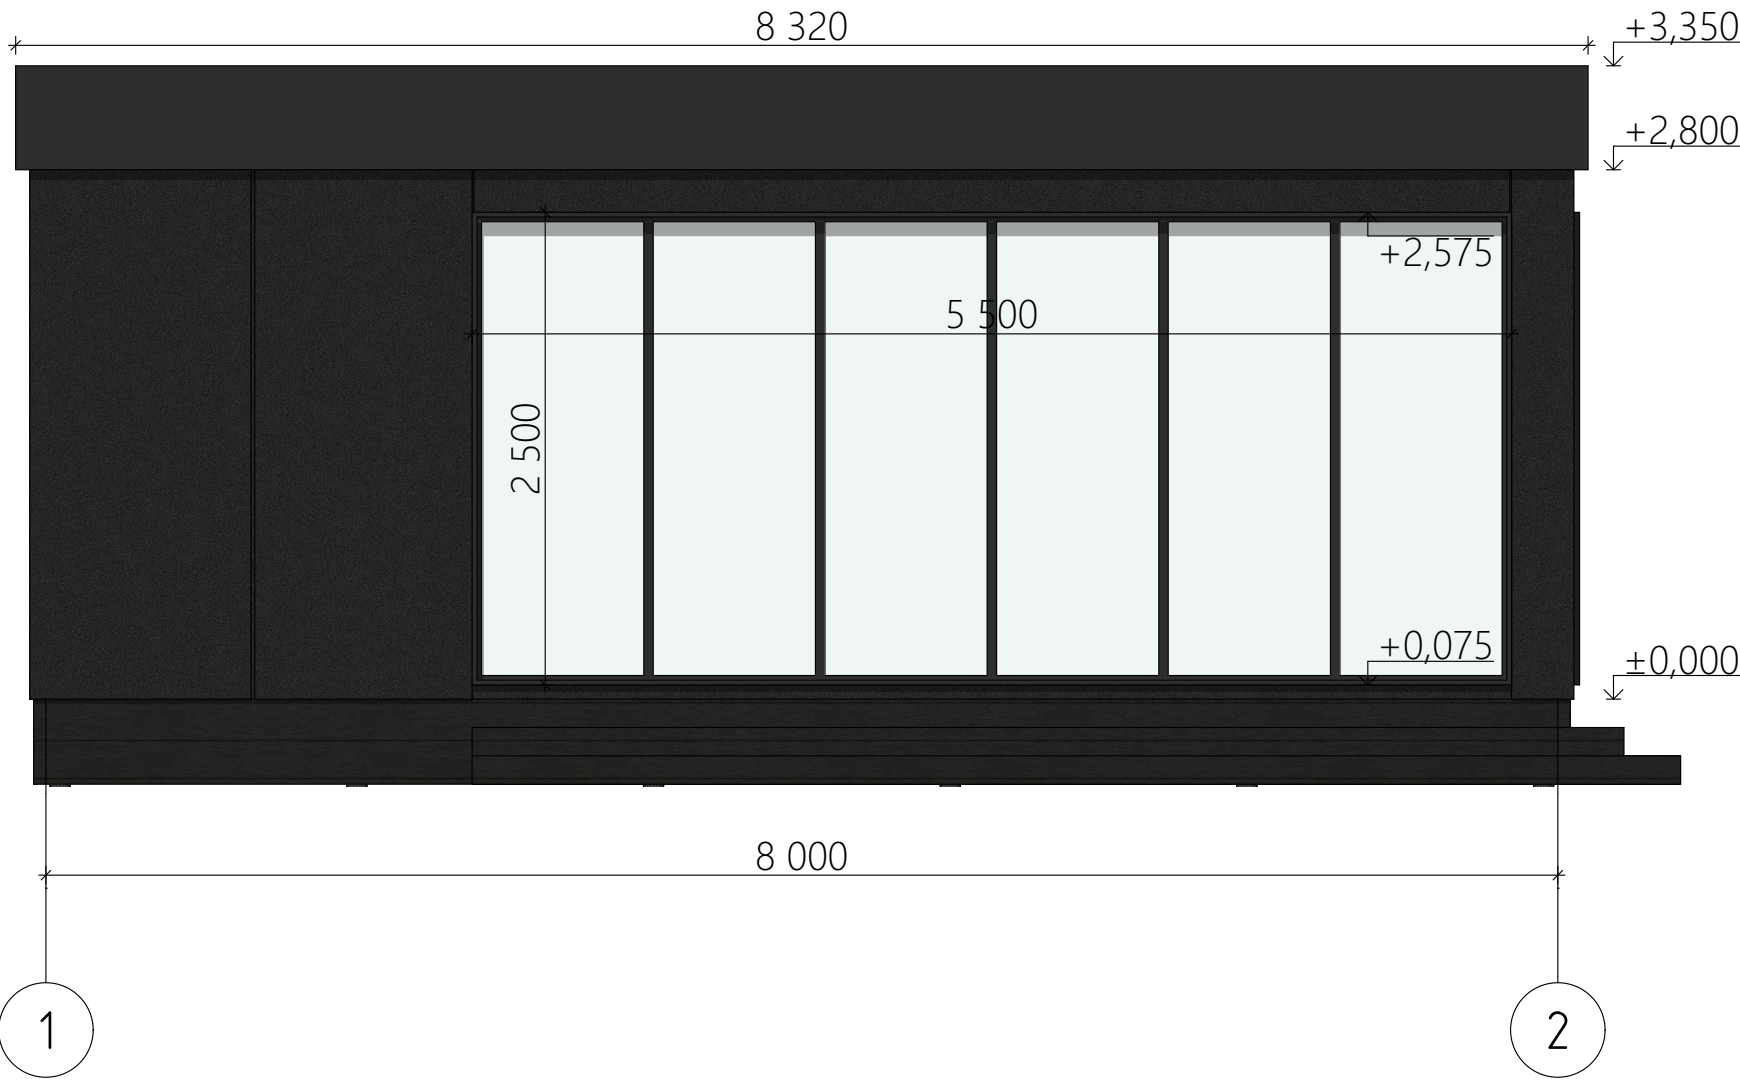

Согласовано				

Инов. № подл.	Подп. и дата	Взам. инв. №	

Лист	Изм.	№ Докум.	Подп.	Дата

Обл. Московская, г.о. Мытищи, дер. Чиверёво, ул. Парусная,
дом 12

Фасад 1-2


Согласовано				
Инва. № подл.	Подп. и дата		Взам. инв. №	

Фасад А-Б

1:40

Условные обозначения:

- Фиброцементные панели
(черный)
- ДПК
(черный)
- Водосточная система
(RAL 9004)
- Наличники, рамы, угловые
элементы (RAL 9004)

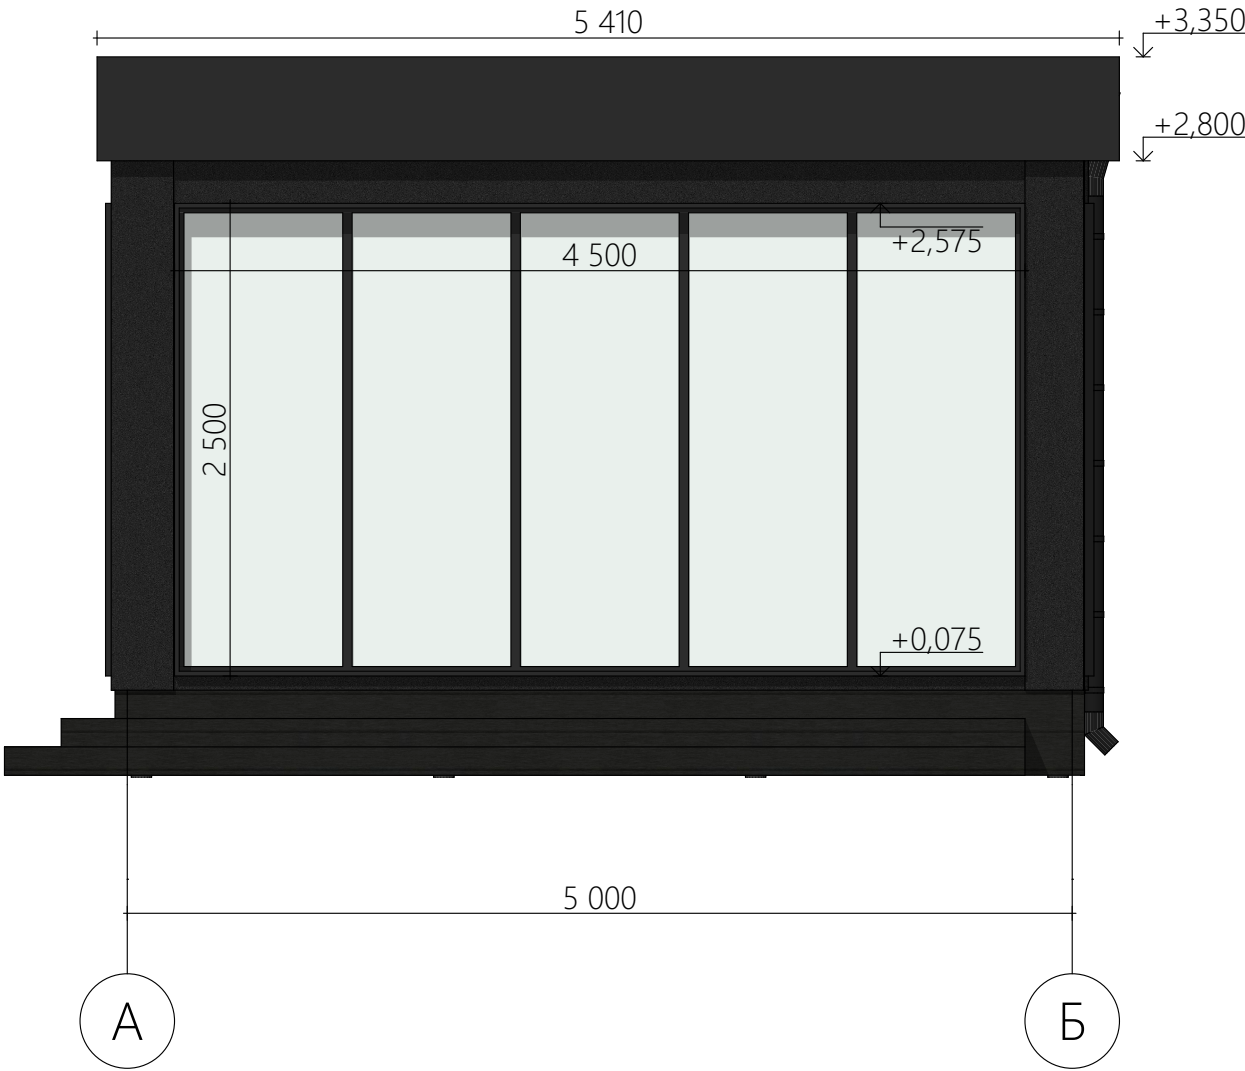

Лист	Изм.	№ Докум.	Подп.	Дата

Обл. Московская, г.о. Мытищи, дер. Чиверёво, ул. Парусная,
дом 12

Фасад А-Б


Согласовано			

Инва. № подл.	Подп. и дата	Взам. инв. №	

Лист	Изм.	№ Докум.	Подп.	Дата

Обл. Московская, г.о. Мытищи, дер. Чиверёво, ул. Парусная,
дом 12

Аксонометрия №1

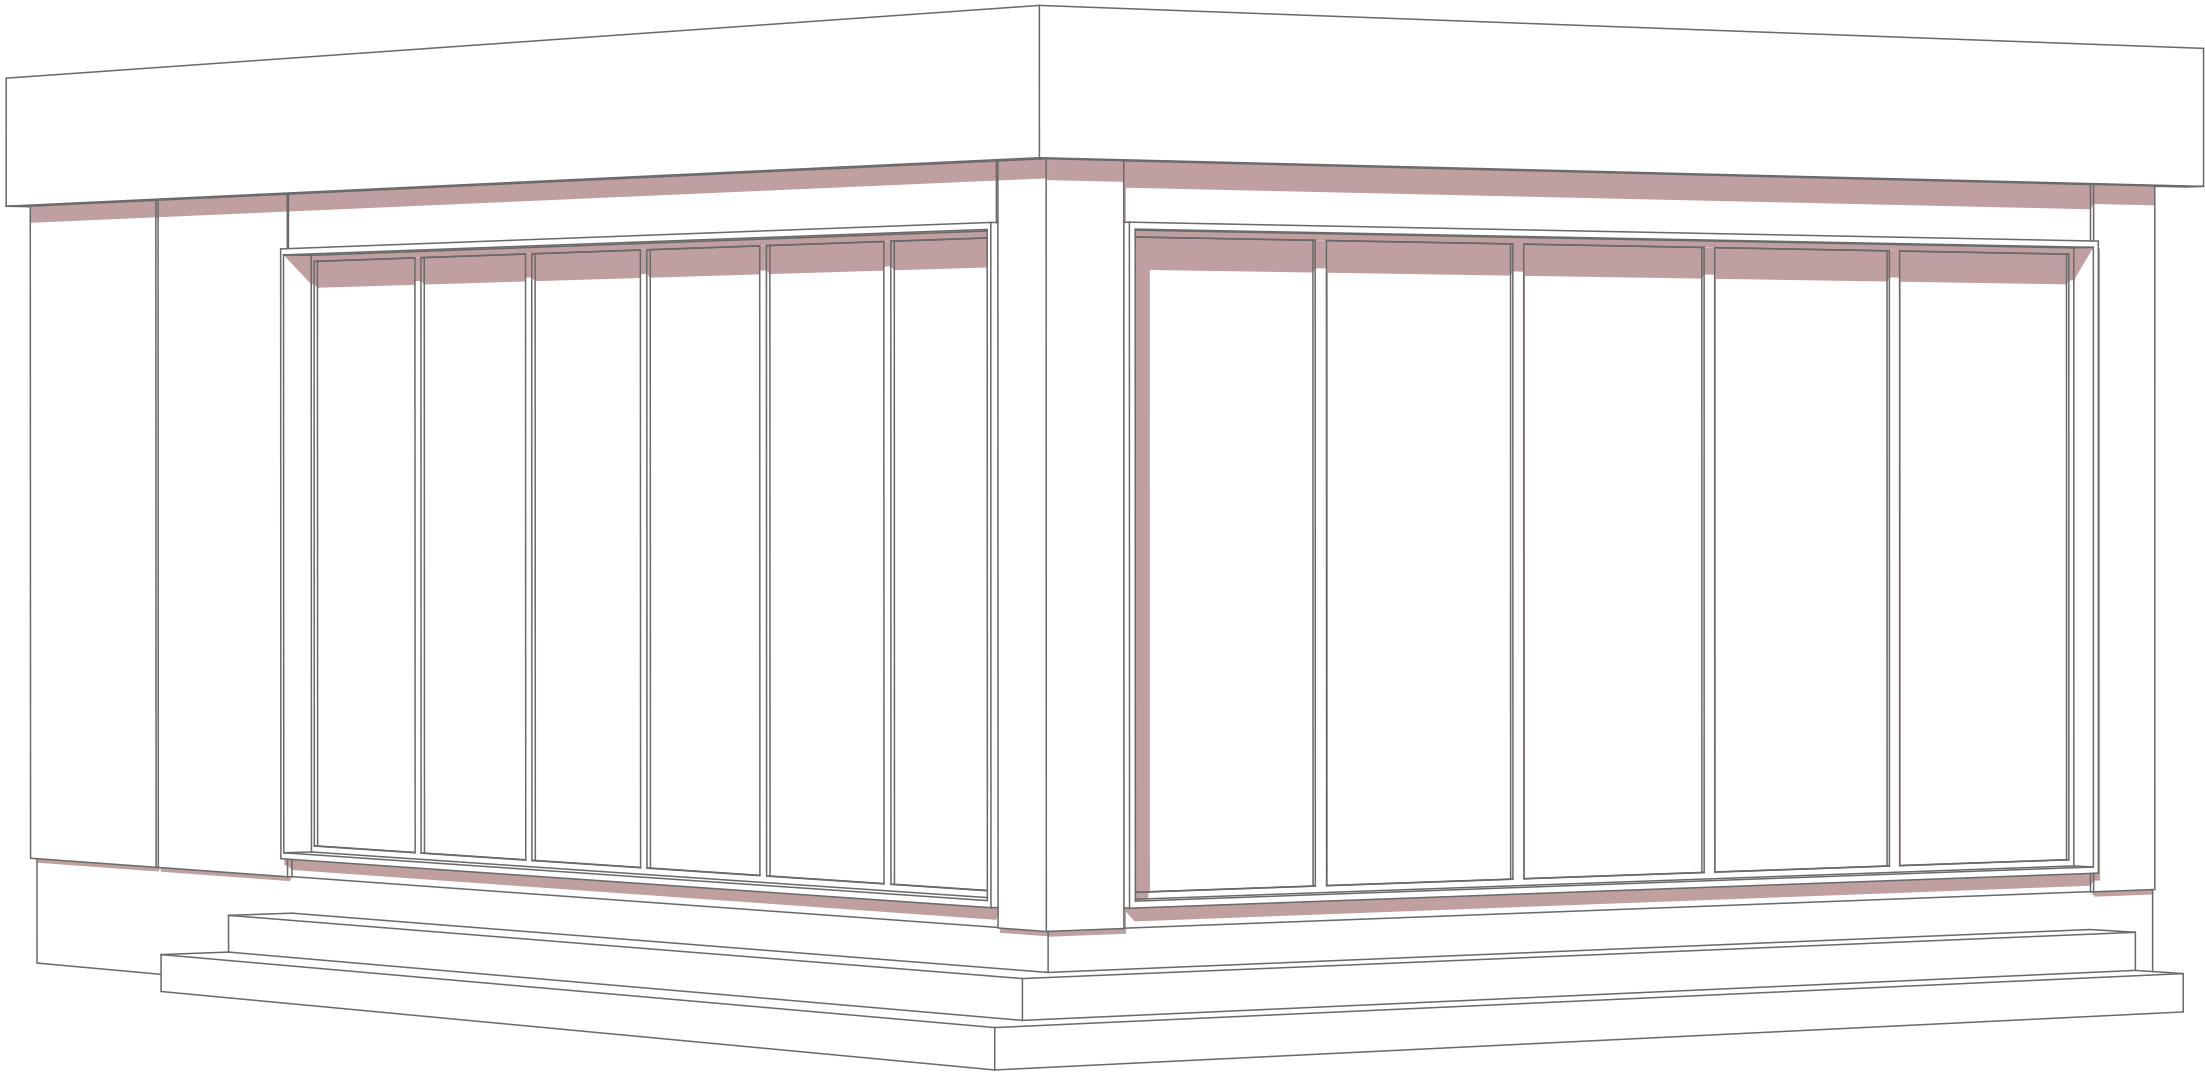


Согласовано				
Инва. № подл.	Взам. инв. №			
	Подп. и дата			

Фасад Б-А

1:40

Условные обозначения:

- Фиброцементные панели
(черный)
- ДПК
(черный)
- Водосточная система
(RAL 9004)
- Наличники, рамы, угловые
элементы (RAL 9004)

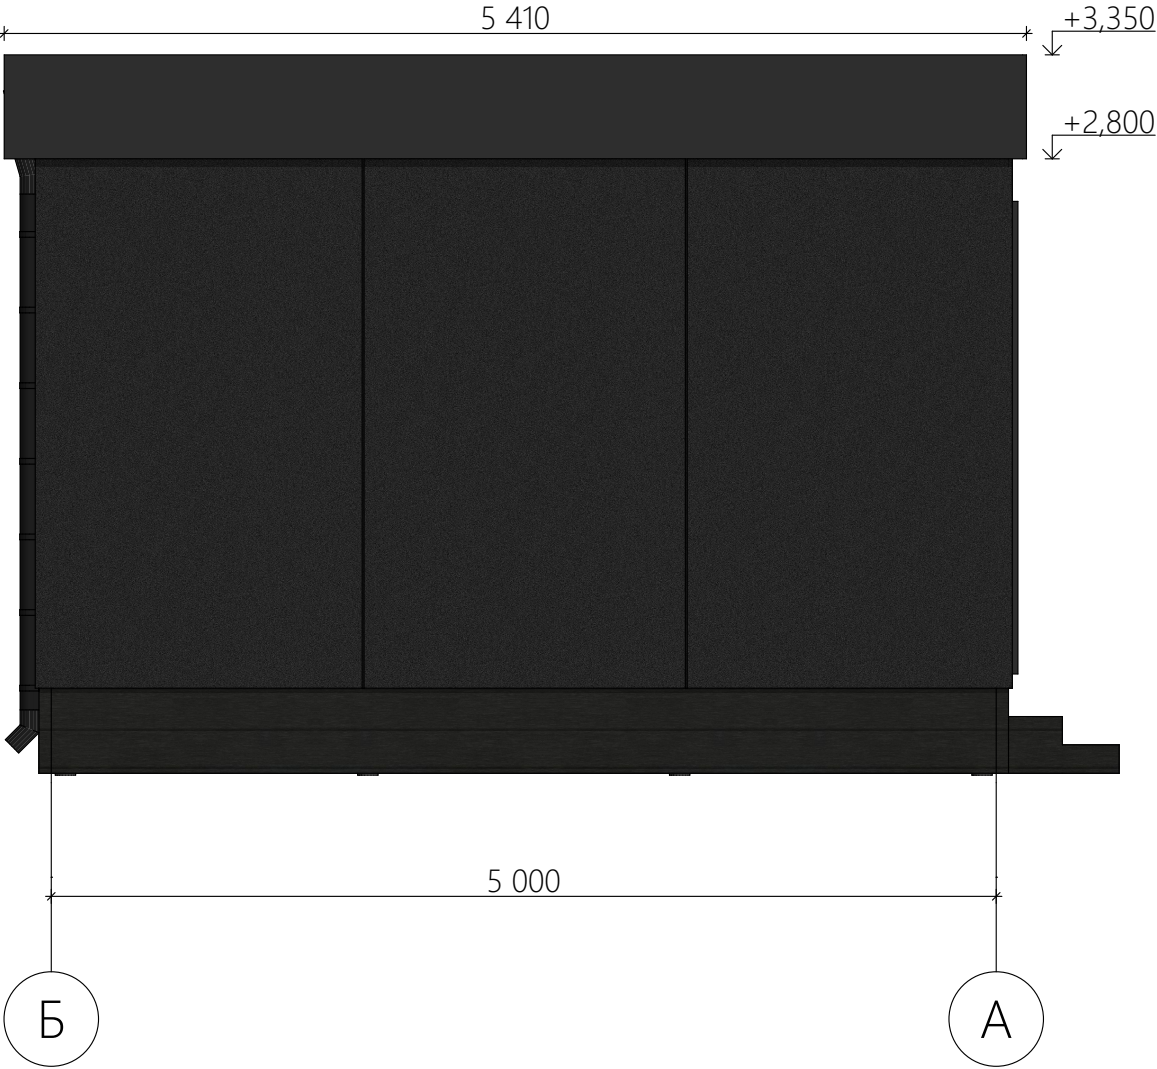

Лист	Изм.	№ Докум.	Подп.	Дата

Обл. Московская, г.о. Мытищи, дер. Чиверёво, ул. Парусная,
дом 12


Фасад Б-А

Фасад 2-1

1:40

Условные обозначения:

- Фиброцементные панели (черный)
- ДПК (черный)
- Водосточная система (RAL 9004)
- Наличники, рамы, угловые элементы (RAL 9004)

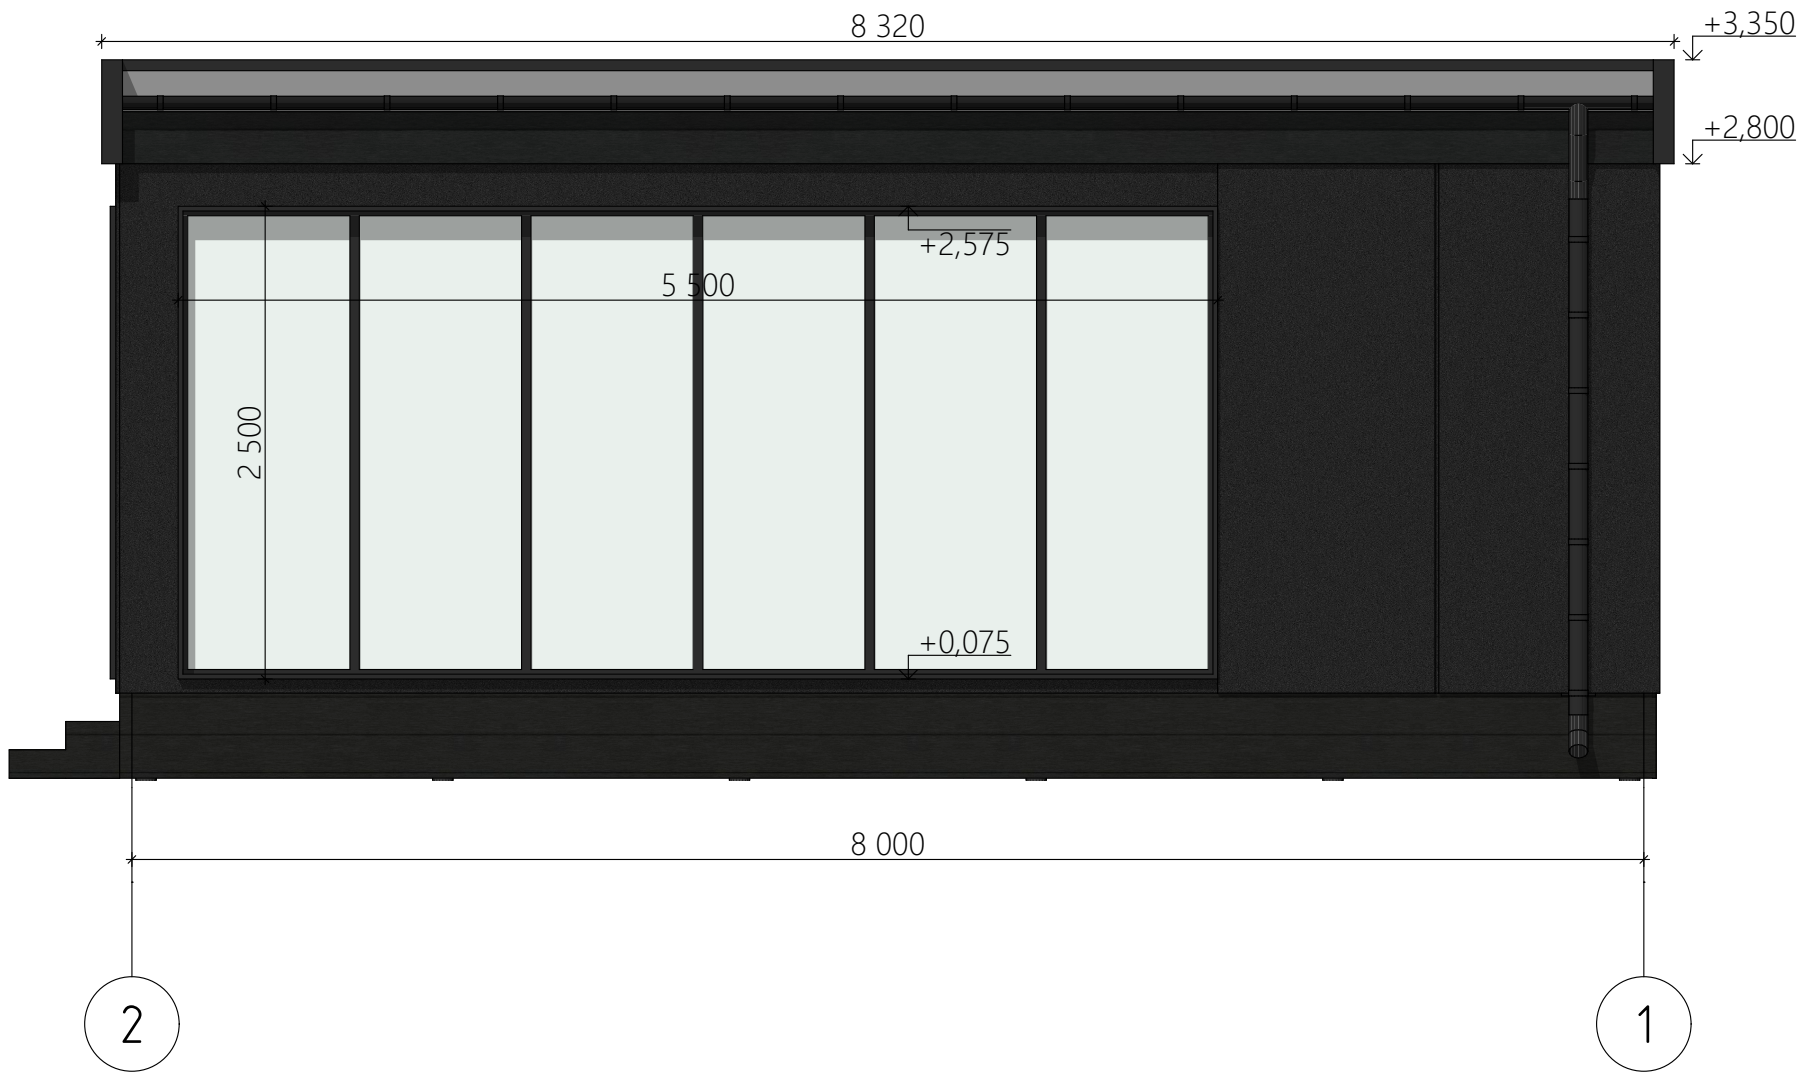

Согласовано				


Инов. № подл.	Подп. и дата		Взам. инв. №	

Лист	Изм.	№ Докум.	Подп.	Дата

Обл. Московская, г.о. Мытищи, дер. Чиверёво, ул. Парусная,
дом 12

Фасад 2-1

Согласовано			

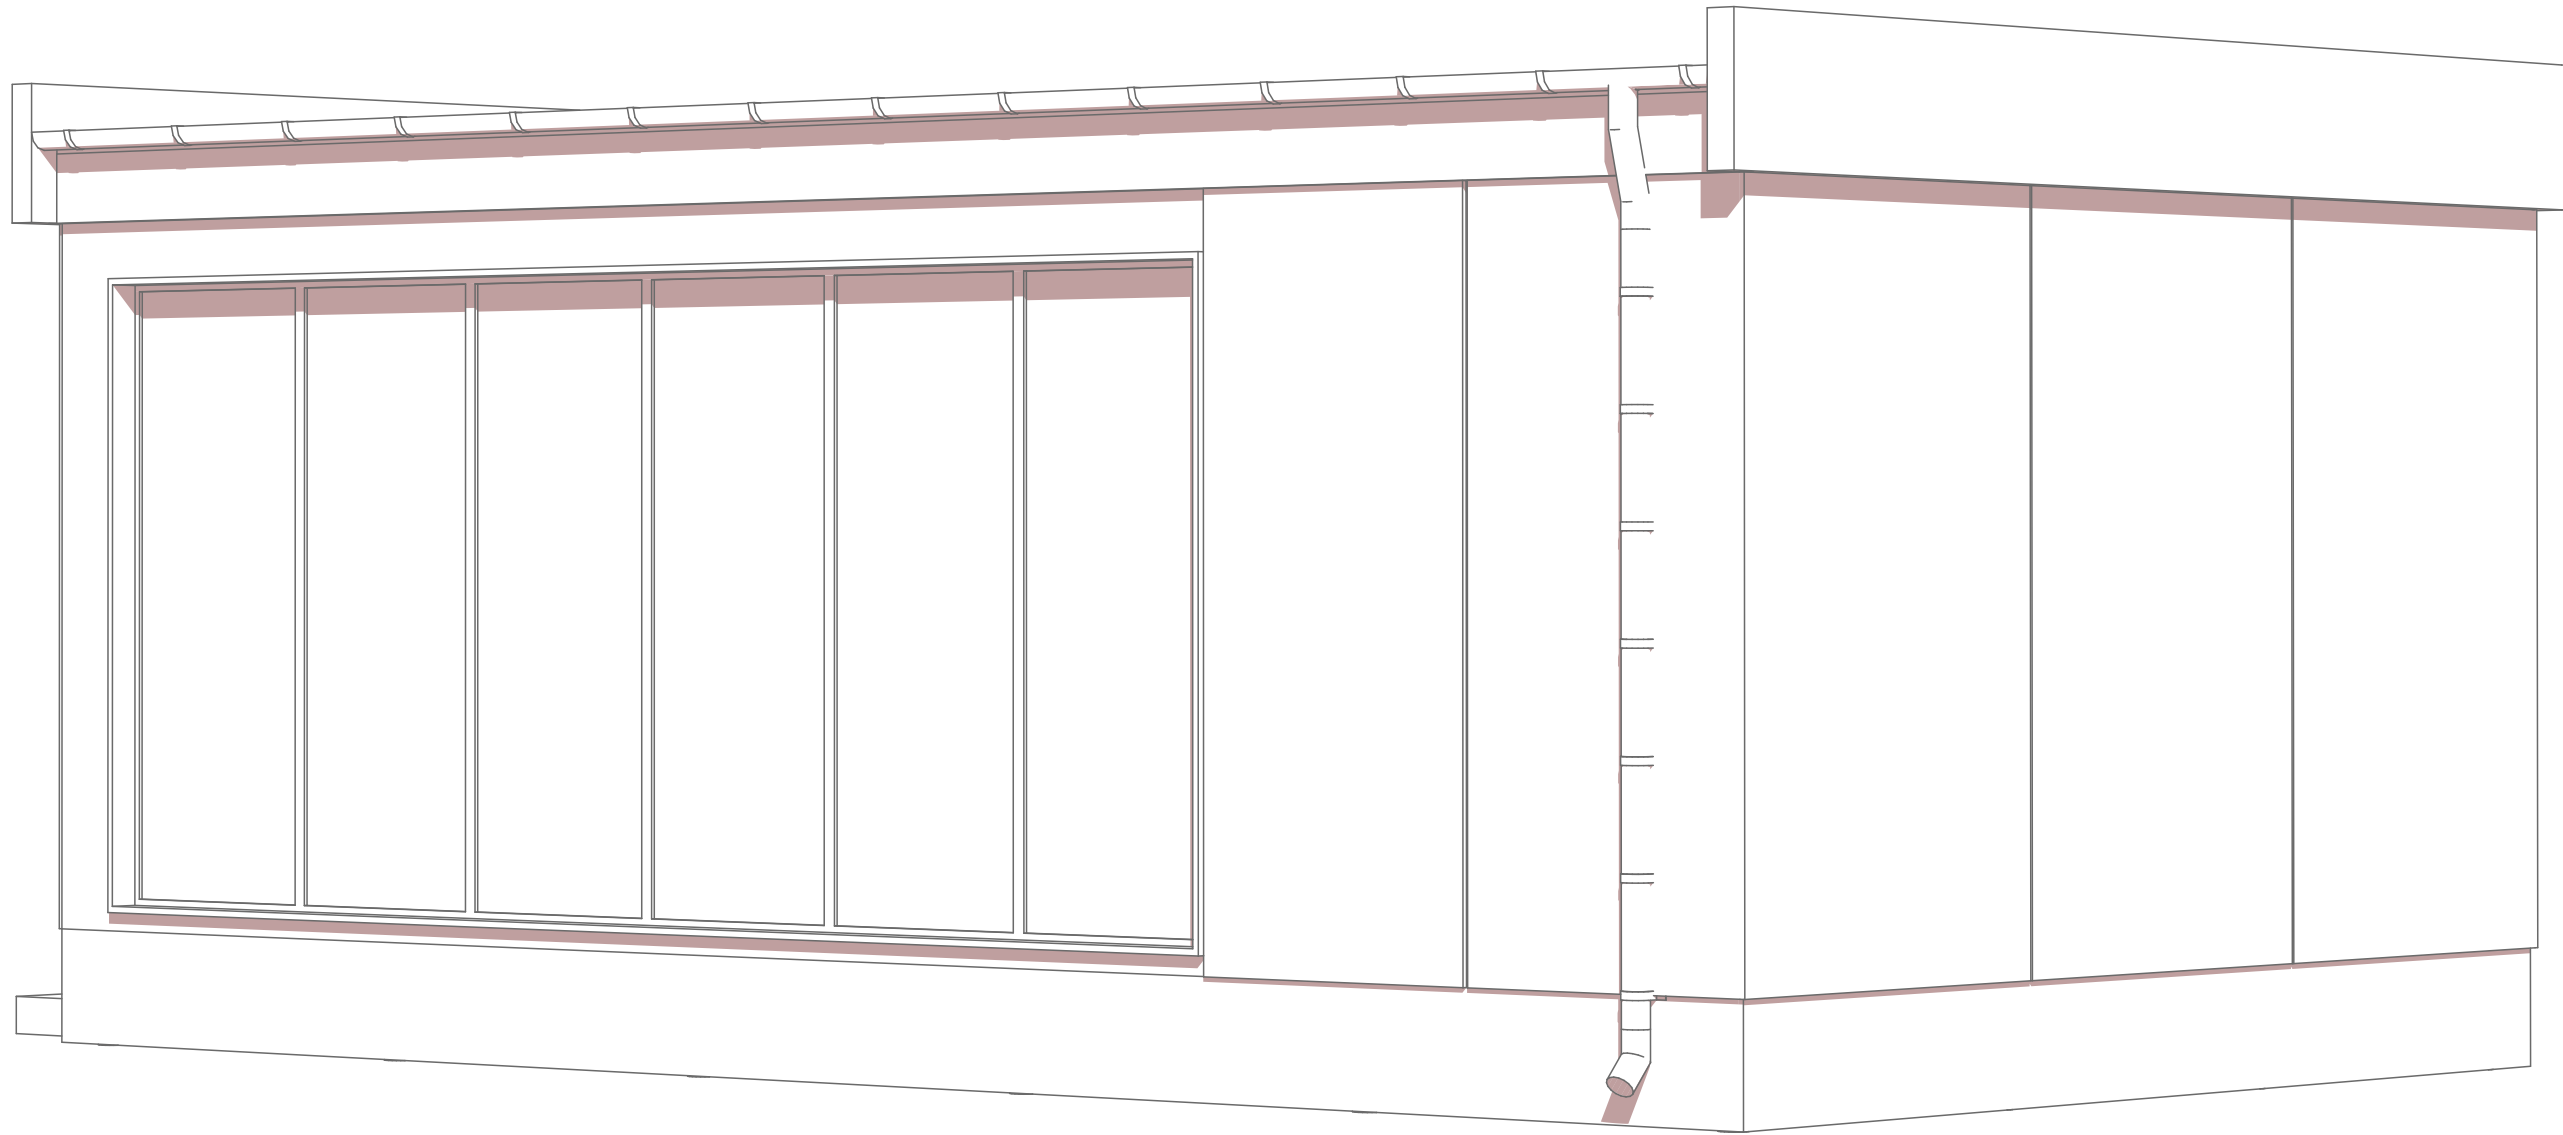

Инов. № подл.	Подп. и дата	Взам. инв. №

Лист	Изм.	№ Докум.	Подп.	Дата

Обл. Московская, г.о. Мытищи, дер. Чиверёво, ул. Парусная,
дом 12

Аксонометрия №2

Лист	
24	

Согласовано			

Инов. № подл.	Подп. и дата	Взам. инв. №	



Лист	Изм.	№ Докум.	Подп.	Дата

Обл. Московская, г.о. Мытищи, дер. Чиверёво, ул. Парусная,
дом 12

Визуализация

Лист
25

Согласовано

Взам. инв. №

Подп. и дата

Инв. № подл.

Лист	Изм.	№ Докум.	Подп.	Дата

Обл. Московская, г.о. Мытищи, дер. Чиверёво, ул. Парусная,
дом 12

Визуализация

Согласовано					
Инва. № подл.	Подп. и дата		Взам. инв. №		



Лист	Изм.	№ Докум.	Подп.	Дата

Обл. Московская, г.о. Мытищи, дер. Чиверёво, ул. Парусная,
дом 12

Визуализация

Лист
27

Согласовано					
Изм. № подл.	Подп. и дата	Взам. инв. №			



Лист	Изм.	№ Докум.	Подп.	Дата

Обл. Московская, г.о. Мытищи, дер. Чиверёво, ул. Парусная,
дом 12

Визуализация

Лист
28

Согласовано

Взам. инв. №

Подп. и дата

Инв. № подл.



Лист	Изм.	№ Докум.	Подп.	Дата

Обл. Московская, г.о. Мытищи, дер. Чиверёво, ул. Парусная,
дом 12

Визуализация